


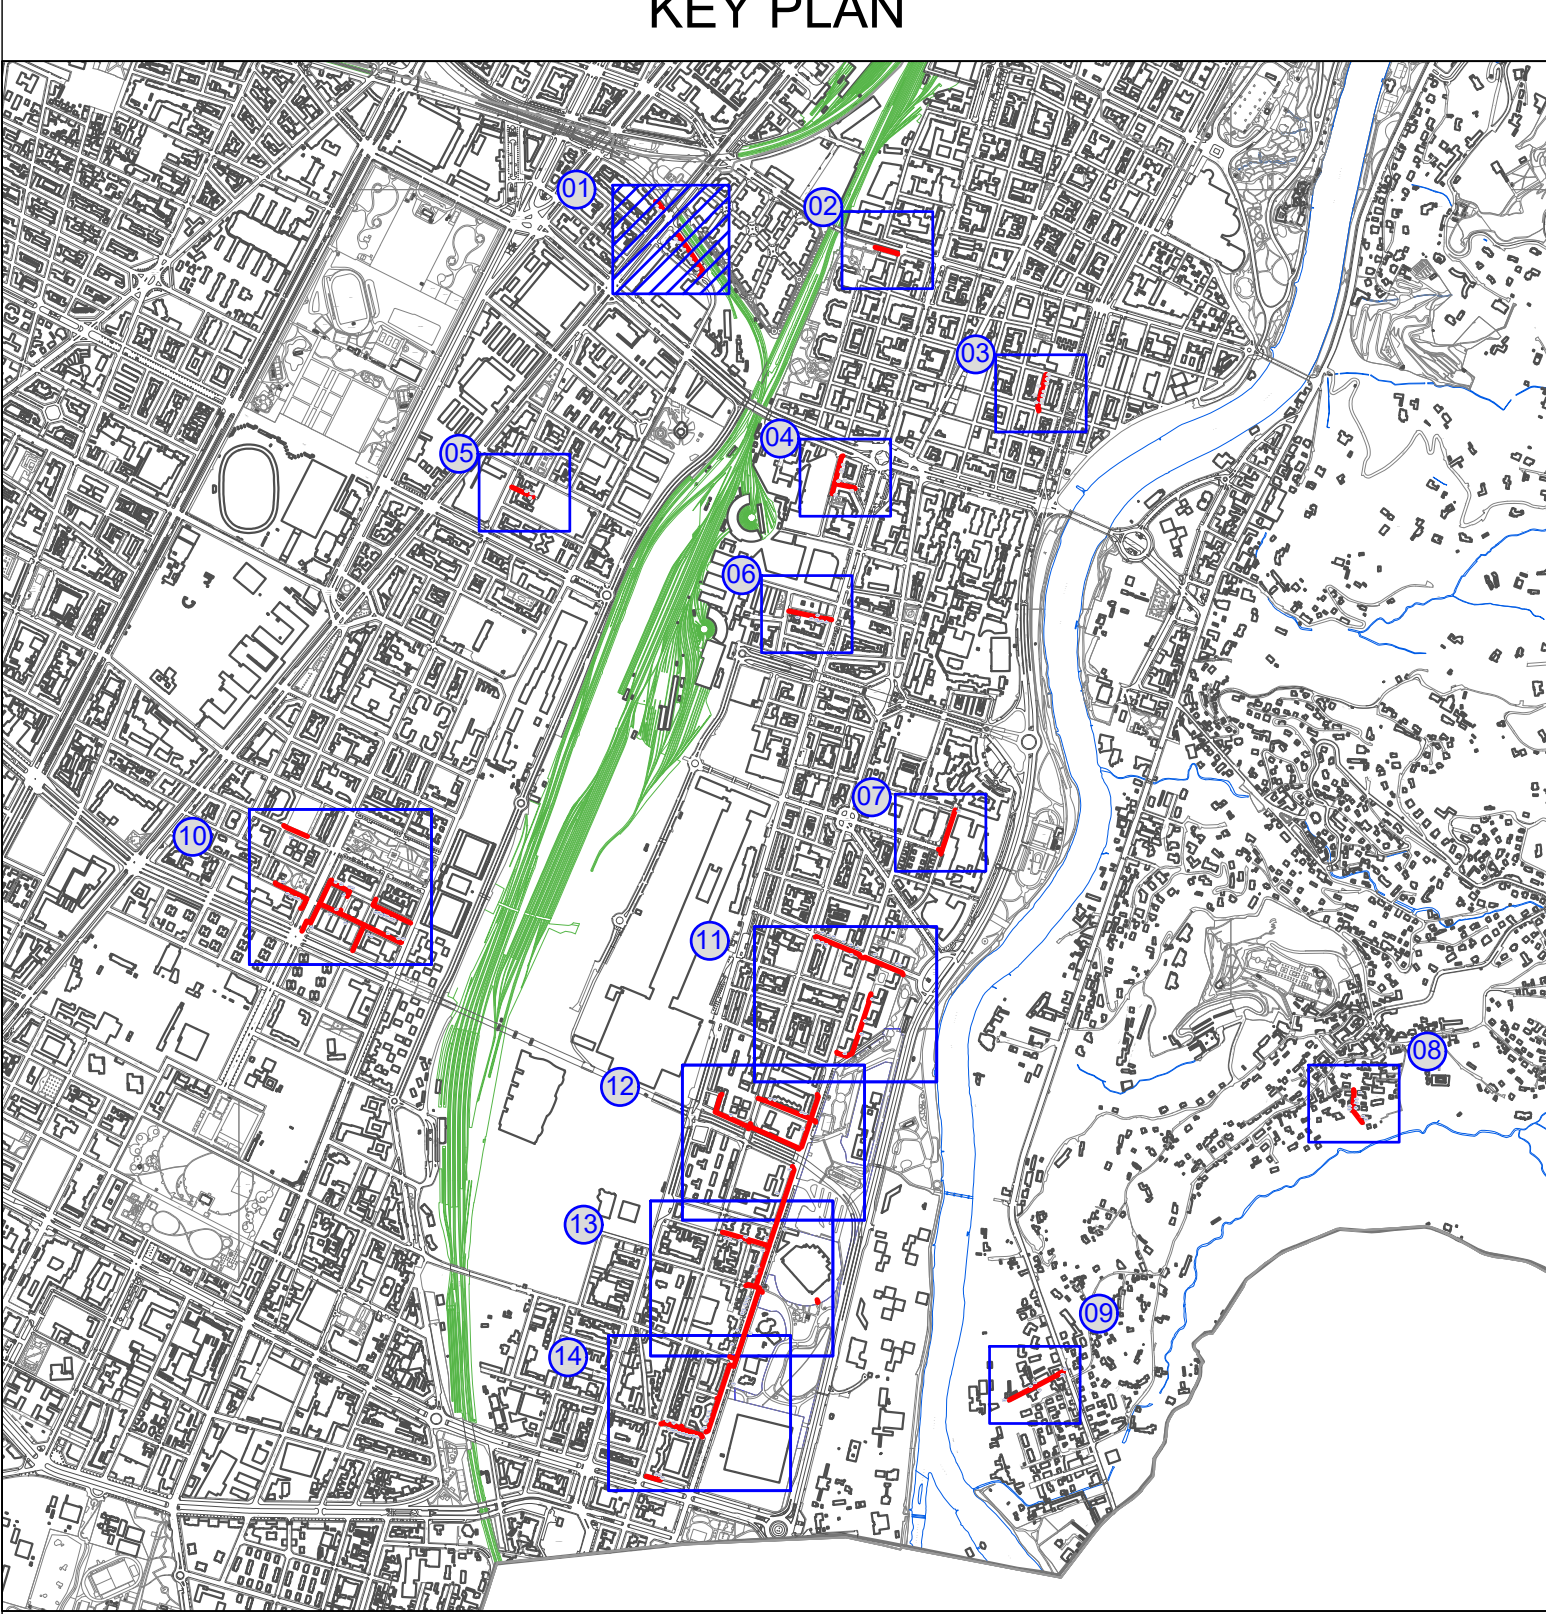

LEGENDA

- Rete in progetto BP
- Tubazione I.D.U. esistente
- Rete da rimuovere
- Tubazione I.D.U. in progetto
- Organo di presa
- Numero I.D.U. in progetto

| Riepilogo allacciamenti |                                    |            |                    |       |                      |       |                   |       |                   |
|-------------------------|------------------------------------|------------|--------------------|-------|----------------------|-------|-------------------|-------|-------------------|
| n.                      | Posizione                          | Tipologico | diametro esistente |       | diametro di progetto |       | lunghezza (L) [m] | ΔH[m] | Lprivata >12m [m] |
|                         |                                    |            | Acc DN             | Pe De | Acc DN               | Pe De |                   |       |                   |
| 001                     | Via Camogli snc                    |            |                    |       |                      | 50    | 5,50              |       |                   |
| 002                     | Via Camogli snc                    |            |                    |       |                      | 50    | 5,50              |       |                   |
| 003                     | C.so Turati civ. 63 da via Camogli | 3          | 25                 | -     | -                    | 32    | 8,50              |       |                   |
| 004                     | C.so Turati civ. 63 da via Camogli | 3          | 40                 | -     | -                    | 50    | 8,50              |       |                   |
| 005                     | Via Camogli civ. 6                 | 3          | 40                 | -     | -                    | 50    | 8,50              |       |                   |
| 006                     | Via Camogli civ. 8                 | 3          | 25                 | -     | -                    | 32    | 8,00              |       |                   |
| 007                     | Via Camogli civ. 10                | 3          | 40                 | -     | -                    | 50    | 9,00              |       |                   |
| 008                     | Via Camogli civ. 12                | 3          | 40                 | -     | -                    | 50    | 7,50              |       |                   |
| 009                     | Via Camogli civ. 14                | 3          | 40                 | -     | -                    | 50    | 7,00              |       |                   |

tratto di condotta da posare a maggiore profondità per presenza teleriscaldamento

001 002 003 004 005 006 007 008 009

004

geopavia

Progettista: Ing. Claudio Gatti  
Ordine degli Ingegneri di Pavia  
Albo n. 3197

Unità Responsabile della Progettazione  
INGERAL-INGE-PROGRE

Progetto n°: 21-0564-3E-00-001272  
WBS: SI.20.I0300.02.1109  
Codice elaborato: 25.1  
Tavola:


Nome file: AI.25.dwg  
Descrizione: Emissione per progetto esecutivo  
Formato: A1  
Scale: 1:500  
Comm.: 2464

00 28 01 26  
A. Ingardi  
L. Domingo  
C. Gatti

Rev. G. M. A. Redatto Controllato Approvato

Comune di Torino (TO) - Vie Varie  
PROGETTO ESECUTIVO  
SOSTITUZIONE RETE BP (2.745,39 m) - GARA TO1  
Intervento n° SI-036213-001272-TSS-TORIN008  
Planimetria di localizzazione IDU - Tavola 1



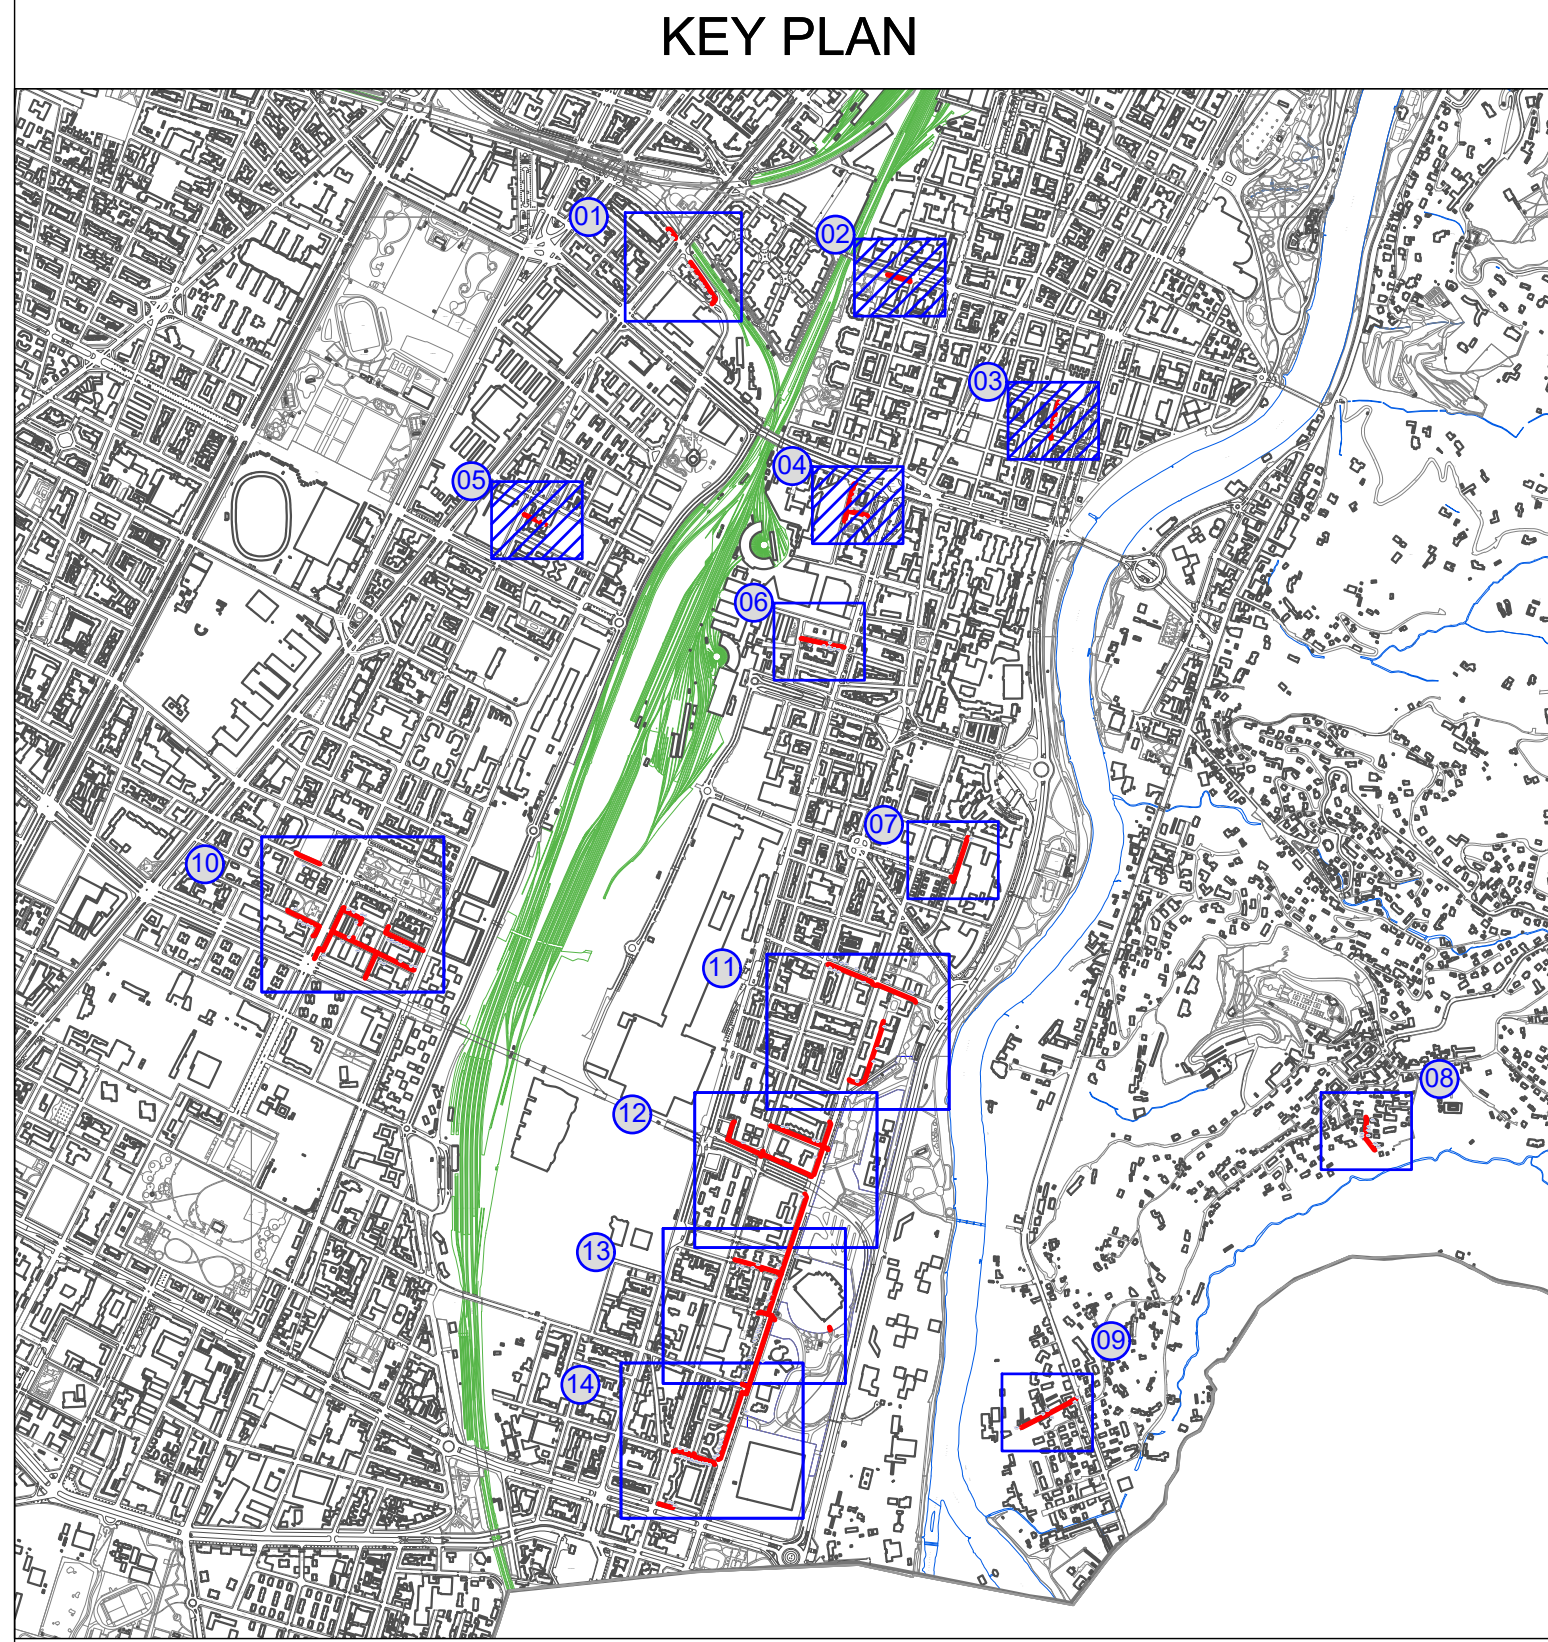

LEGENDA

- Rete in progetto BP
- Tubazione I.D.U. esistente
- Rete da rimuovere
- Tubazione I.D.U. in progetto
- Organo di presa
- Numero I.D.U. in progetto




| Riepilogo allacciamenti |                              |            |                    |       |                      |       |                   |       |                   |
|-------------------------|------------------------------|------------|--------------------|-------|----------------------|-------|-------------------|-------|-------------------|
| n.                      | Posizione                    | Tipologico | diametro esistente |       | diametro di progetto |       | lunghezza (L) [m] | ΔH[m] | Lprivata >12m [m] |
|                         |                              |            | Acc DN             | Pe De | Acc DN               | Pe De |                   |       |                   |
| 010                     | Corso Alghieri Dante civ. 42 | 3          | 100                | -     | -                    | 125   | 7.00              |       |                   |
| 011                     | Corso Alghieri Dante civ. 46 | 3          | 100                | -     | -                    | 125   | 7.00              |       |                   |
| 012                     | Via Foà Pio snc              | 1          | -                  | 50    | -                    | 50    | 2.00              |       |                   |
| 013                     | Via Foà Pio civ. 59          | 3          | 75                 | -     | -                    | 90    | 3.50              |       |                   |
| 014                     | Via Foà Pio civ. 61          | 3          | 25                 | -     | -                    | 32    | 4.00              |       |                   |
| 015                     | Via Foà Pio civ. 68          | 4          | 80                 | -     | -                    | 90    | 7.50              |       |                   |
| 016                     | Via Foà Pio civ. 63          | 1          | -                  | 90    | -                    | 90    | 2.50              |       |                   |
| 017                     | Via Foà Pio civ. 65          | 1          | -                  | 90    | -                    | 90    | 5.50              |       |                   |
| 018                     | Via Foà Pio civ. 74          | 3          | 75                 | -     | -                    | 90    | 7.50              |       |                   |
| 019                     | Via Foà Pio civ. 65          | 3          | 75                 | -     | -                    | 90    | 4.50              |       |                   |
| 020                     | Via Foà Pio civ. 65          | 3          | 25                 | -     | -                    | 32    | 4.50              |       |                   |
| 021                     | Via Foà Pio civ. 76          | 2          | -                  | 63    | -                    | 63    | 1.00              |       |                   |
| 022                     | Via Pagliani Luigi civ. 1    | 3          | 50                 | -     | -                    | 63    | 6.00              |       |                   |
| 023                     | Via Pagliani Luigi civ. 3    | 3          | 25                 | -     | -                    | 32    | 6.00              |       |                   |
| 024                     | Via Pagliani Luigi civ. 3    | 3          | 32                 | -     | -                    | 32    | 6.50              |       |                   |
| 025                     | Via Pagliani Luigi civ. 5    | 3          | 40                 | -     | -                    | 50    | 6.00              |       |                   |
| 026                     | Via Gavello Giuseppe civ. 4  | 4          | 40                 | -     | -                    | 50    | 11.00             |       |                   |
| 027                     | Via Gavello Giuseppe civ. 3  | 3          | -                  | 90    | -                    | 90    | 8.00              |       |                   |
| 028                     | Via Pagliani Luigi civ. 11   | 1          | -                  | 63    | -                    | 63    | 5.50              |       |                   |
| 029                     | Via Tunisi civ. 45 mt. 3     | 1          | -                  | 50    | -                    | 50    | 2.50              |       |                   |
| 030                     | Via Tunisi civ. 45 mt. 5     | 3          | 50                 | -     | -                    | 63    | 3.00              |       |                   |
| 031                     | Via Tunisi civ. 45 mt. 6     | 4          | 40                 | -     | -                    | 50    | 2.50              |       |                   |

geopavia




Progetto n°: 21-0564-3E-00-001272  
WBS: SI-20-0300-02-1109  
Codice elettronico: 25.2

Unità Responsabile della Progettazione  
INGEGNERIA-INCE-PROGIE

Comune di Torino (TO) - Vie Varie  
PROGETTO ESECUTIVO  
SOSTITUZIONE RETE BP (2.745,39 m) - GARA TO1  
Intervento n° SK036213-001272-TSS-TORIN008  
Planimetria di localizzazione IDU - Tavola 2

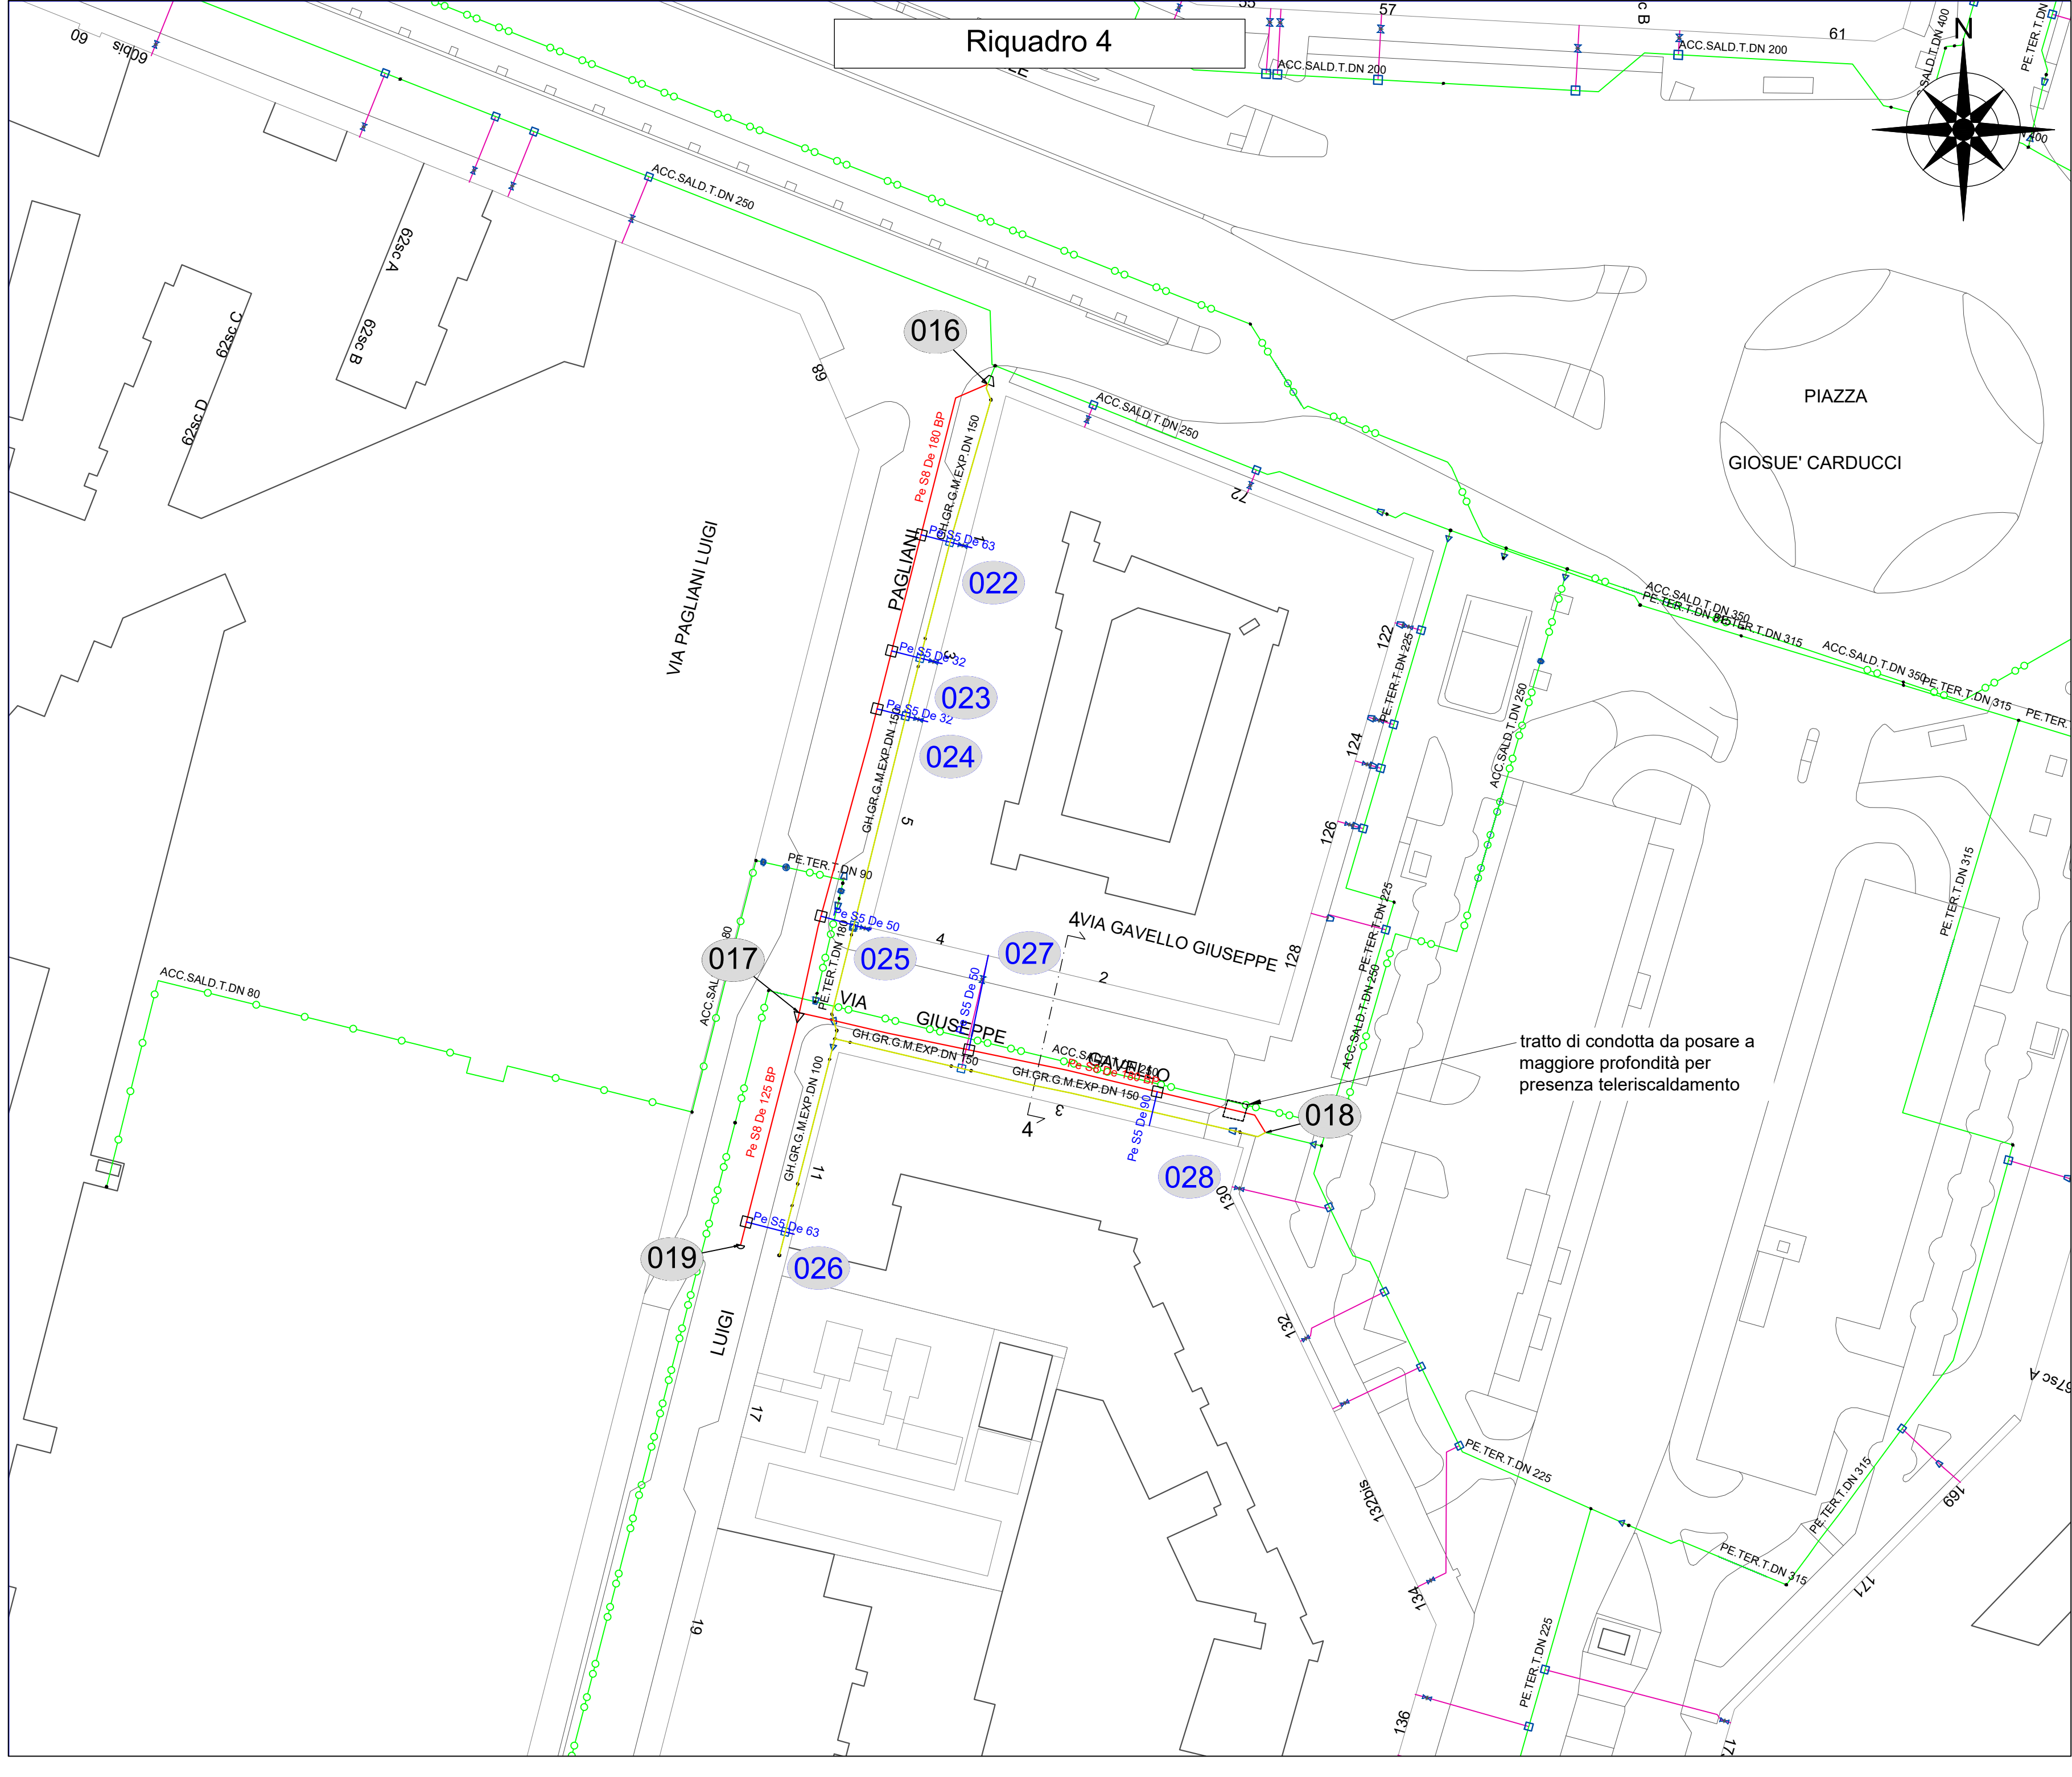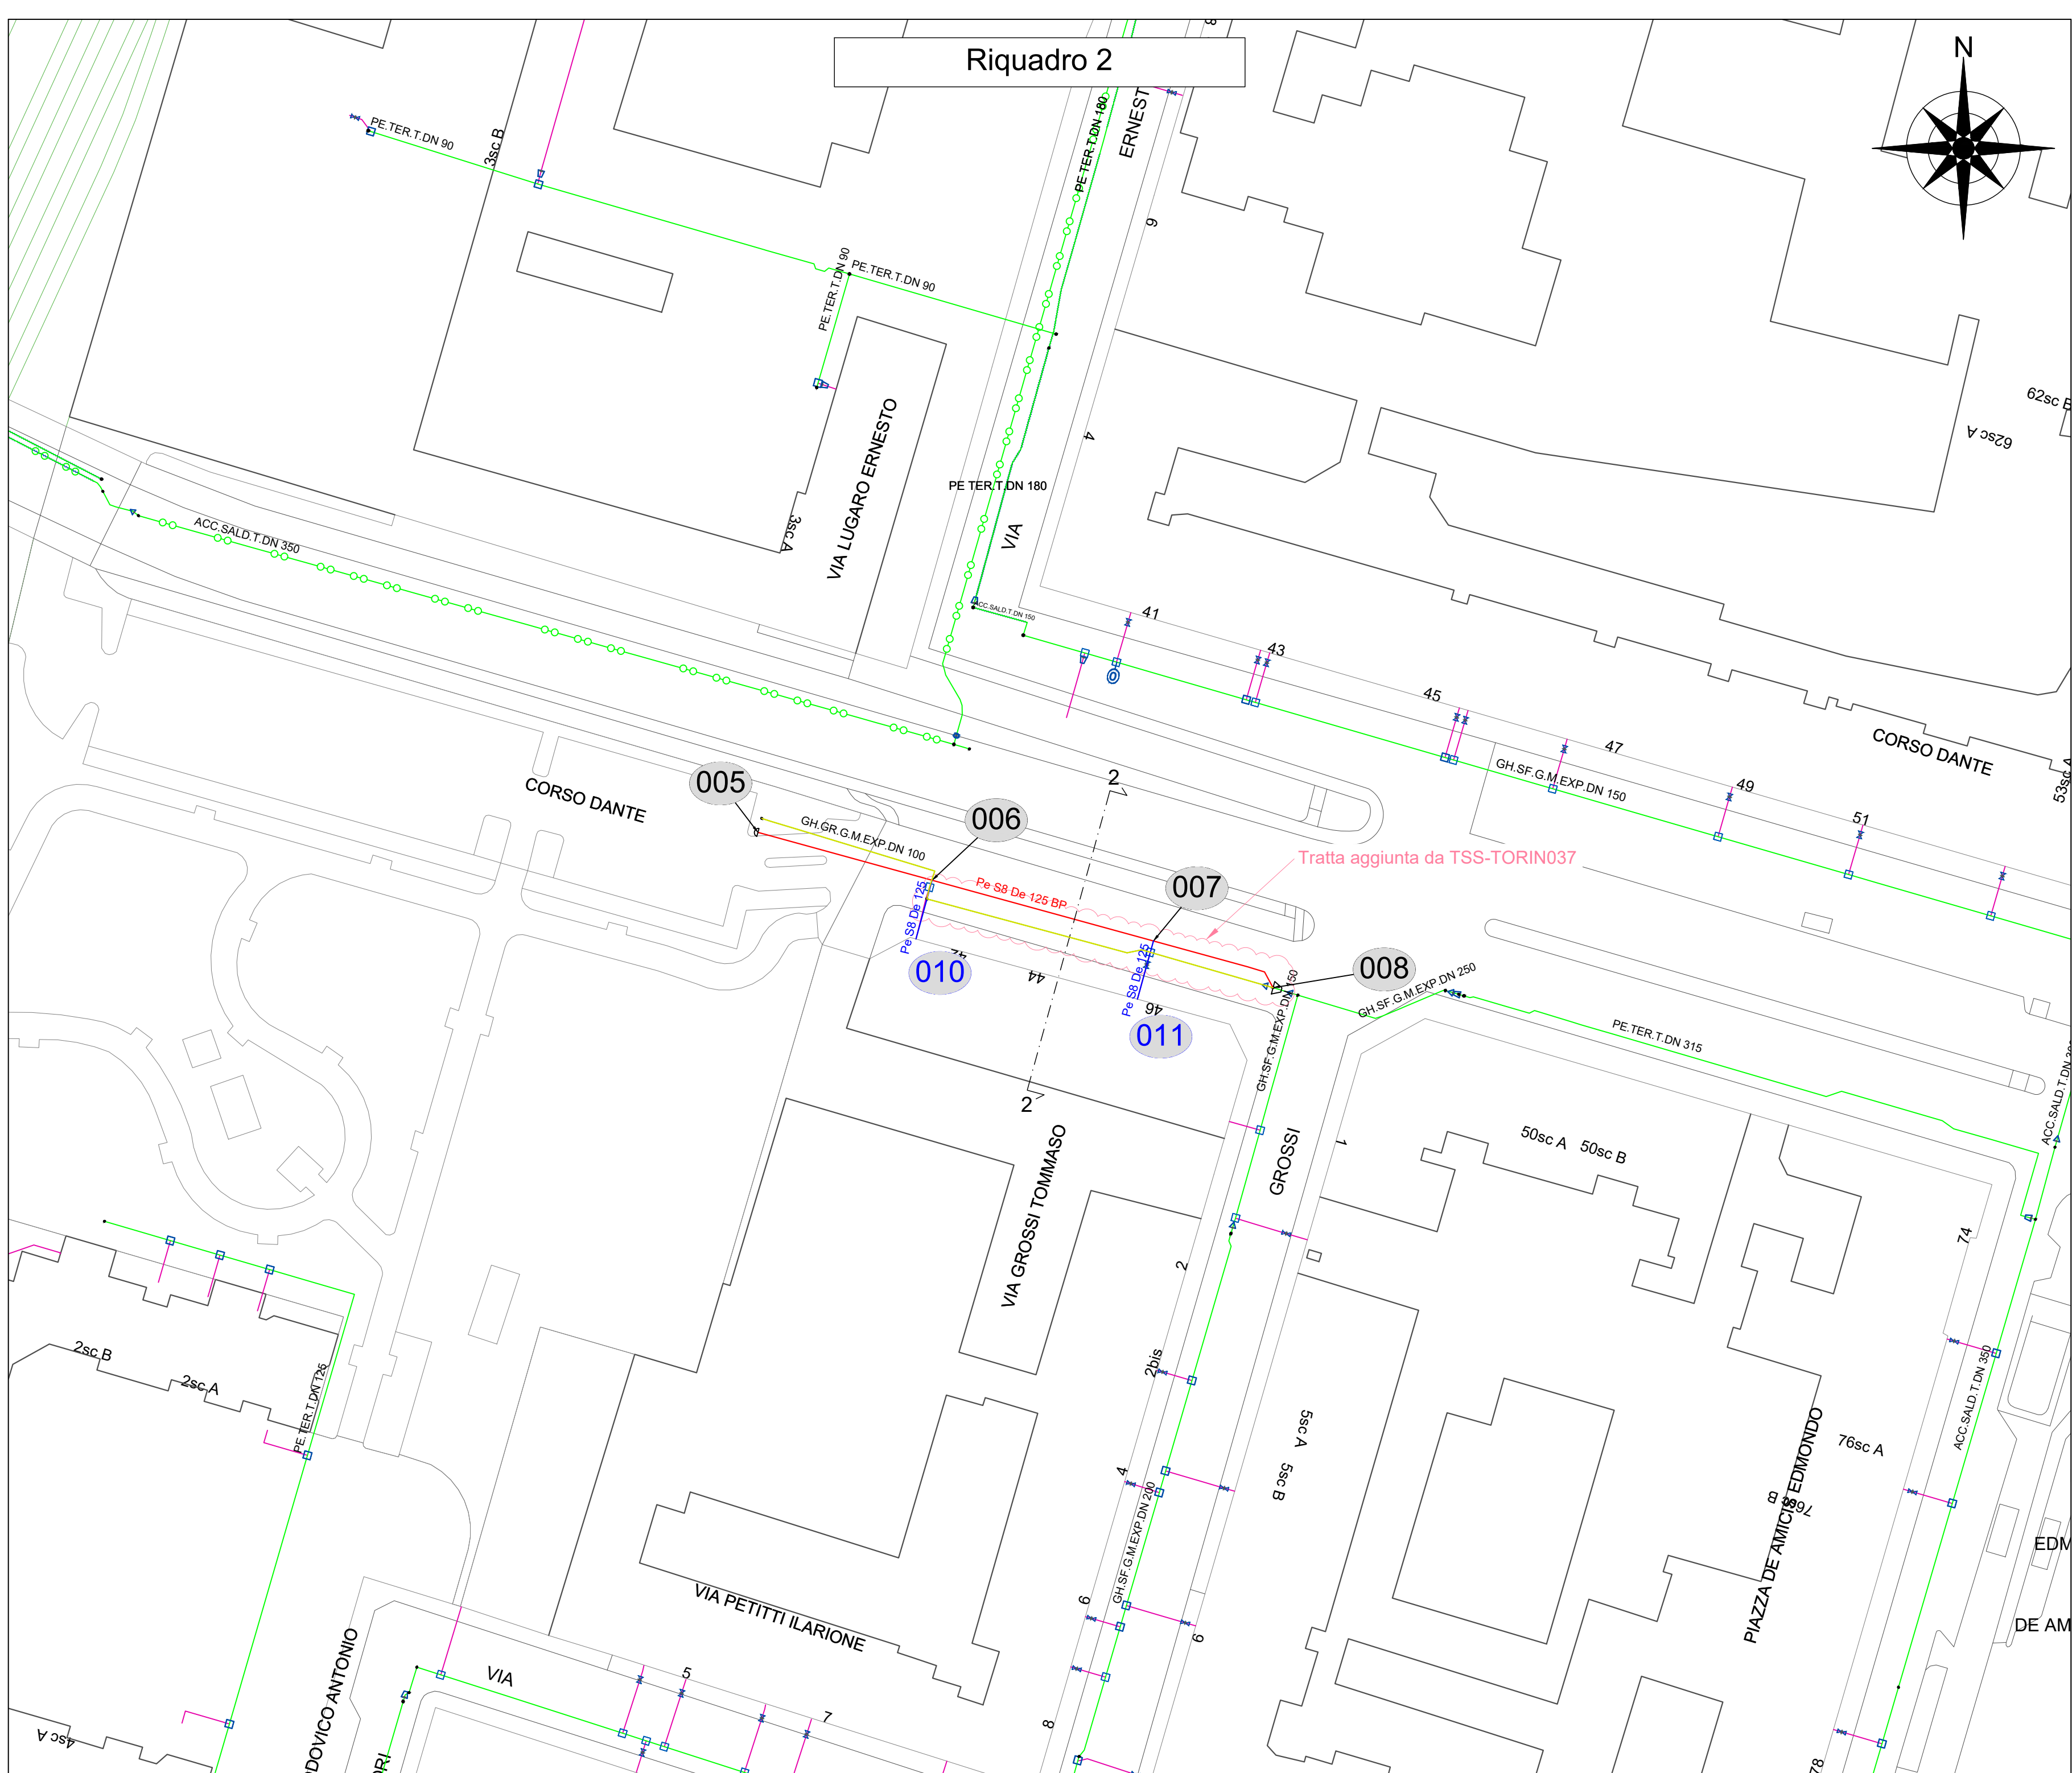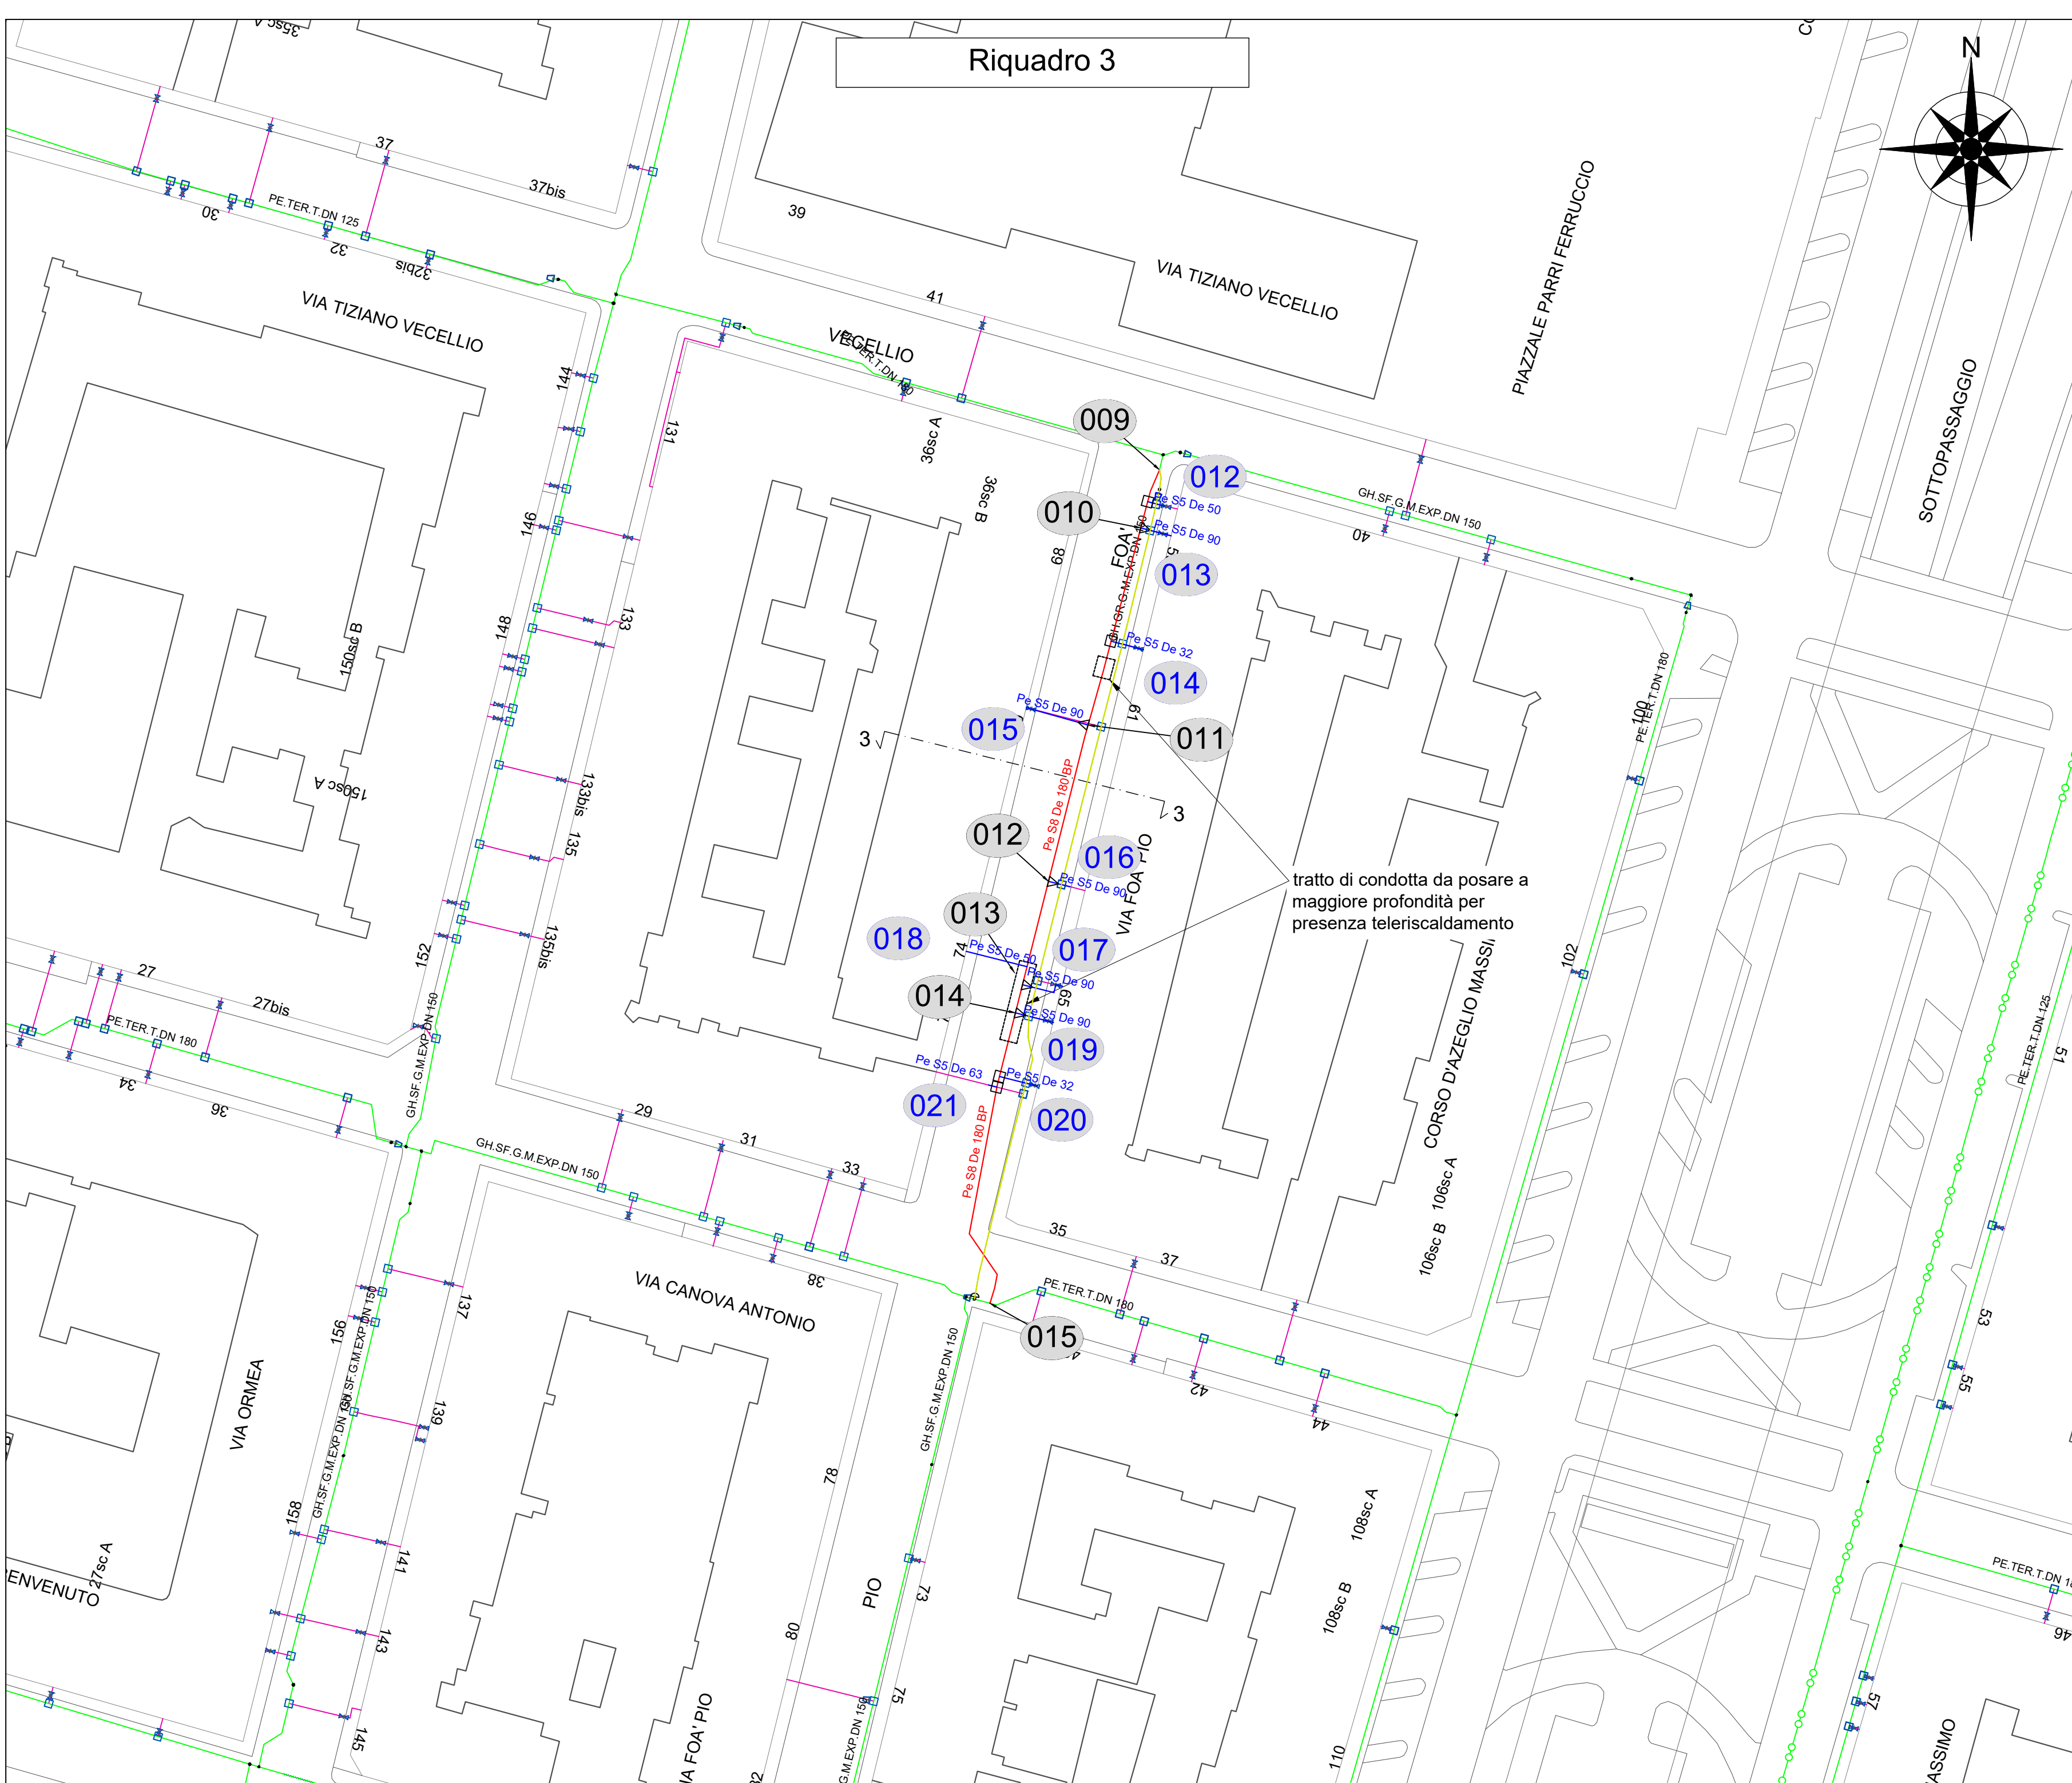



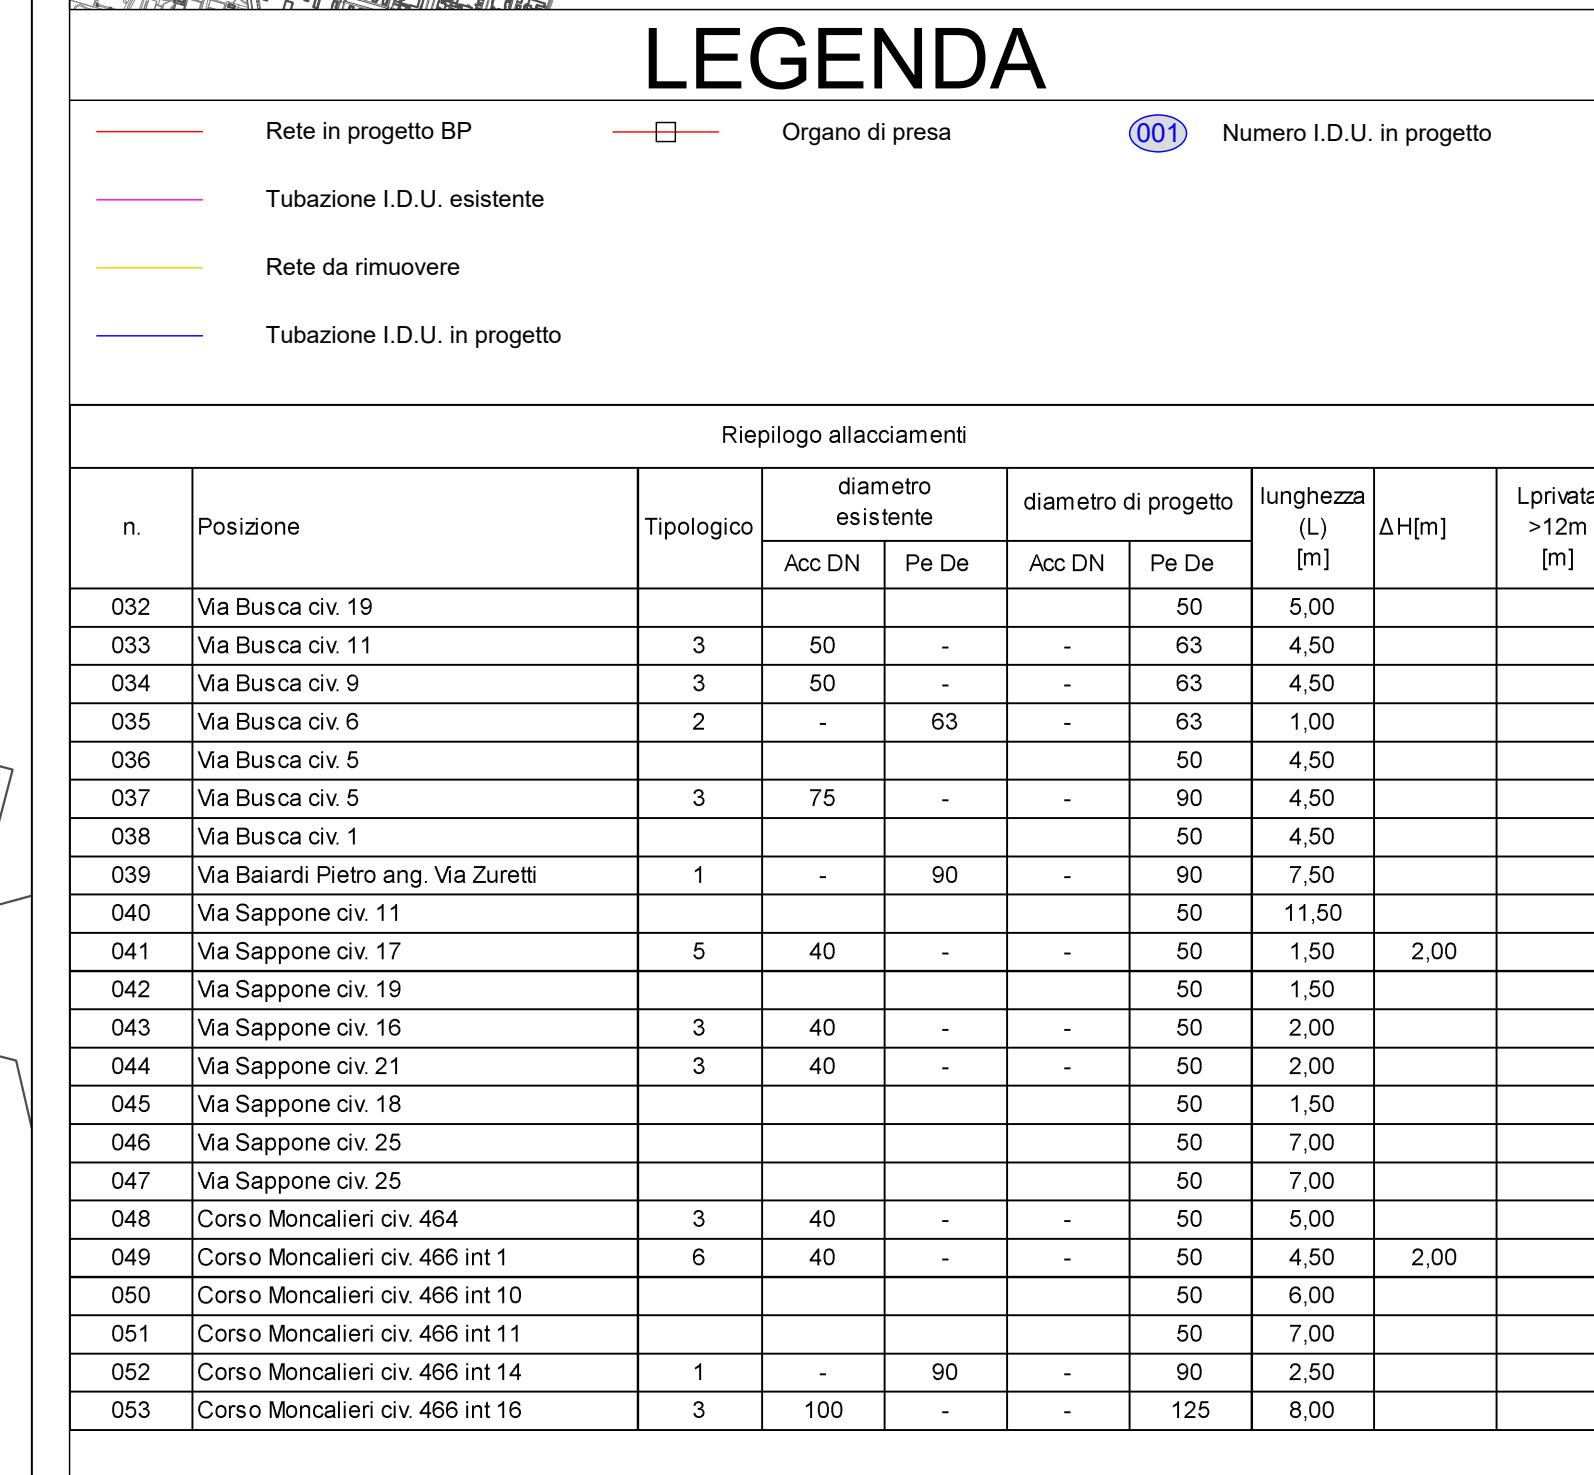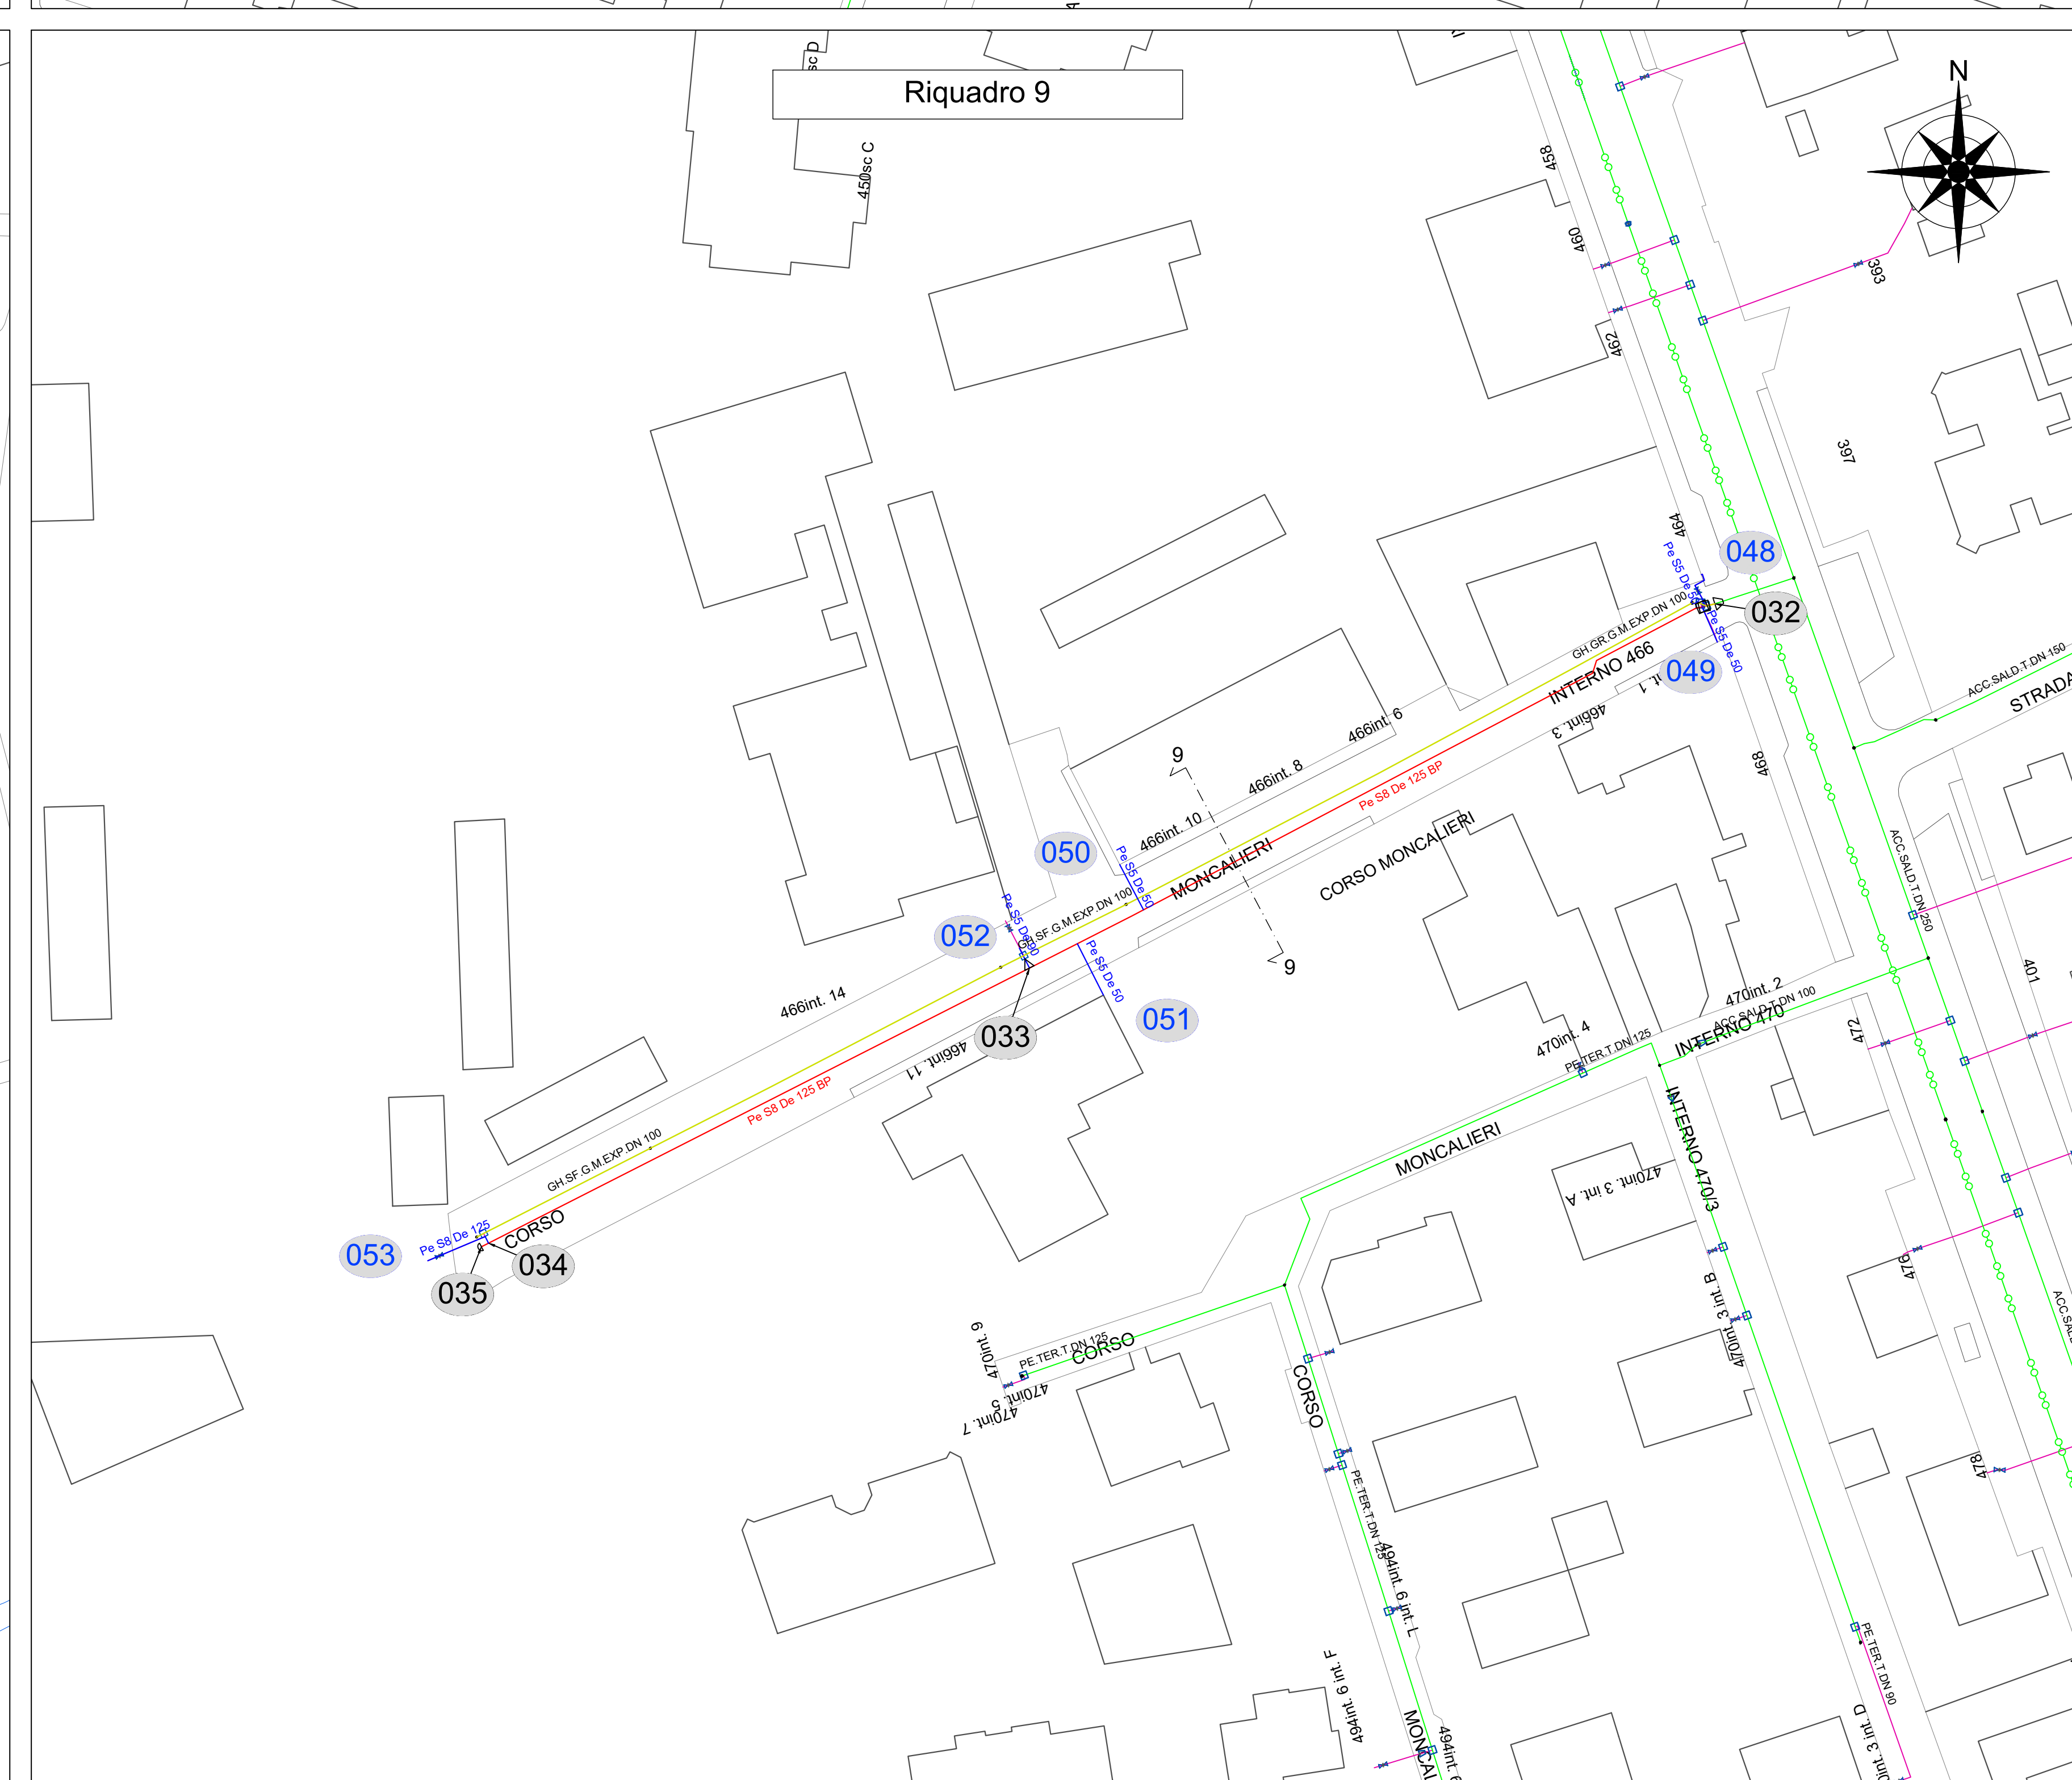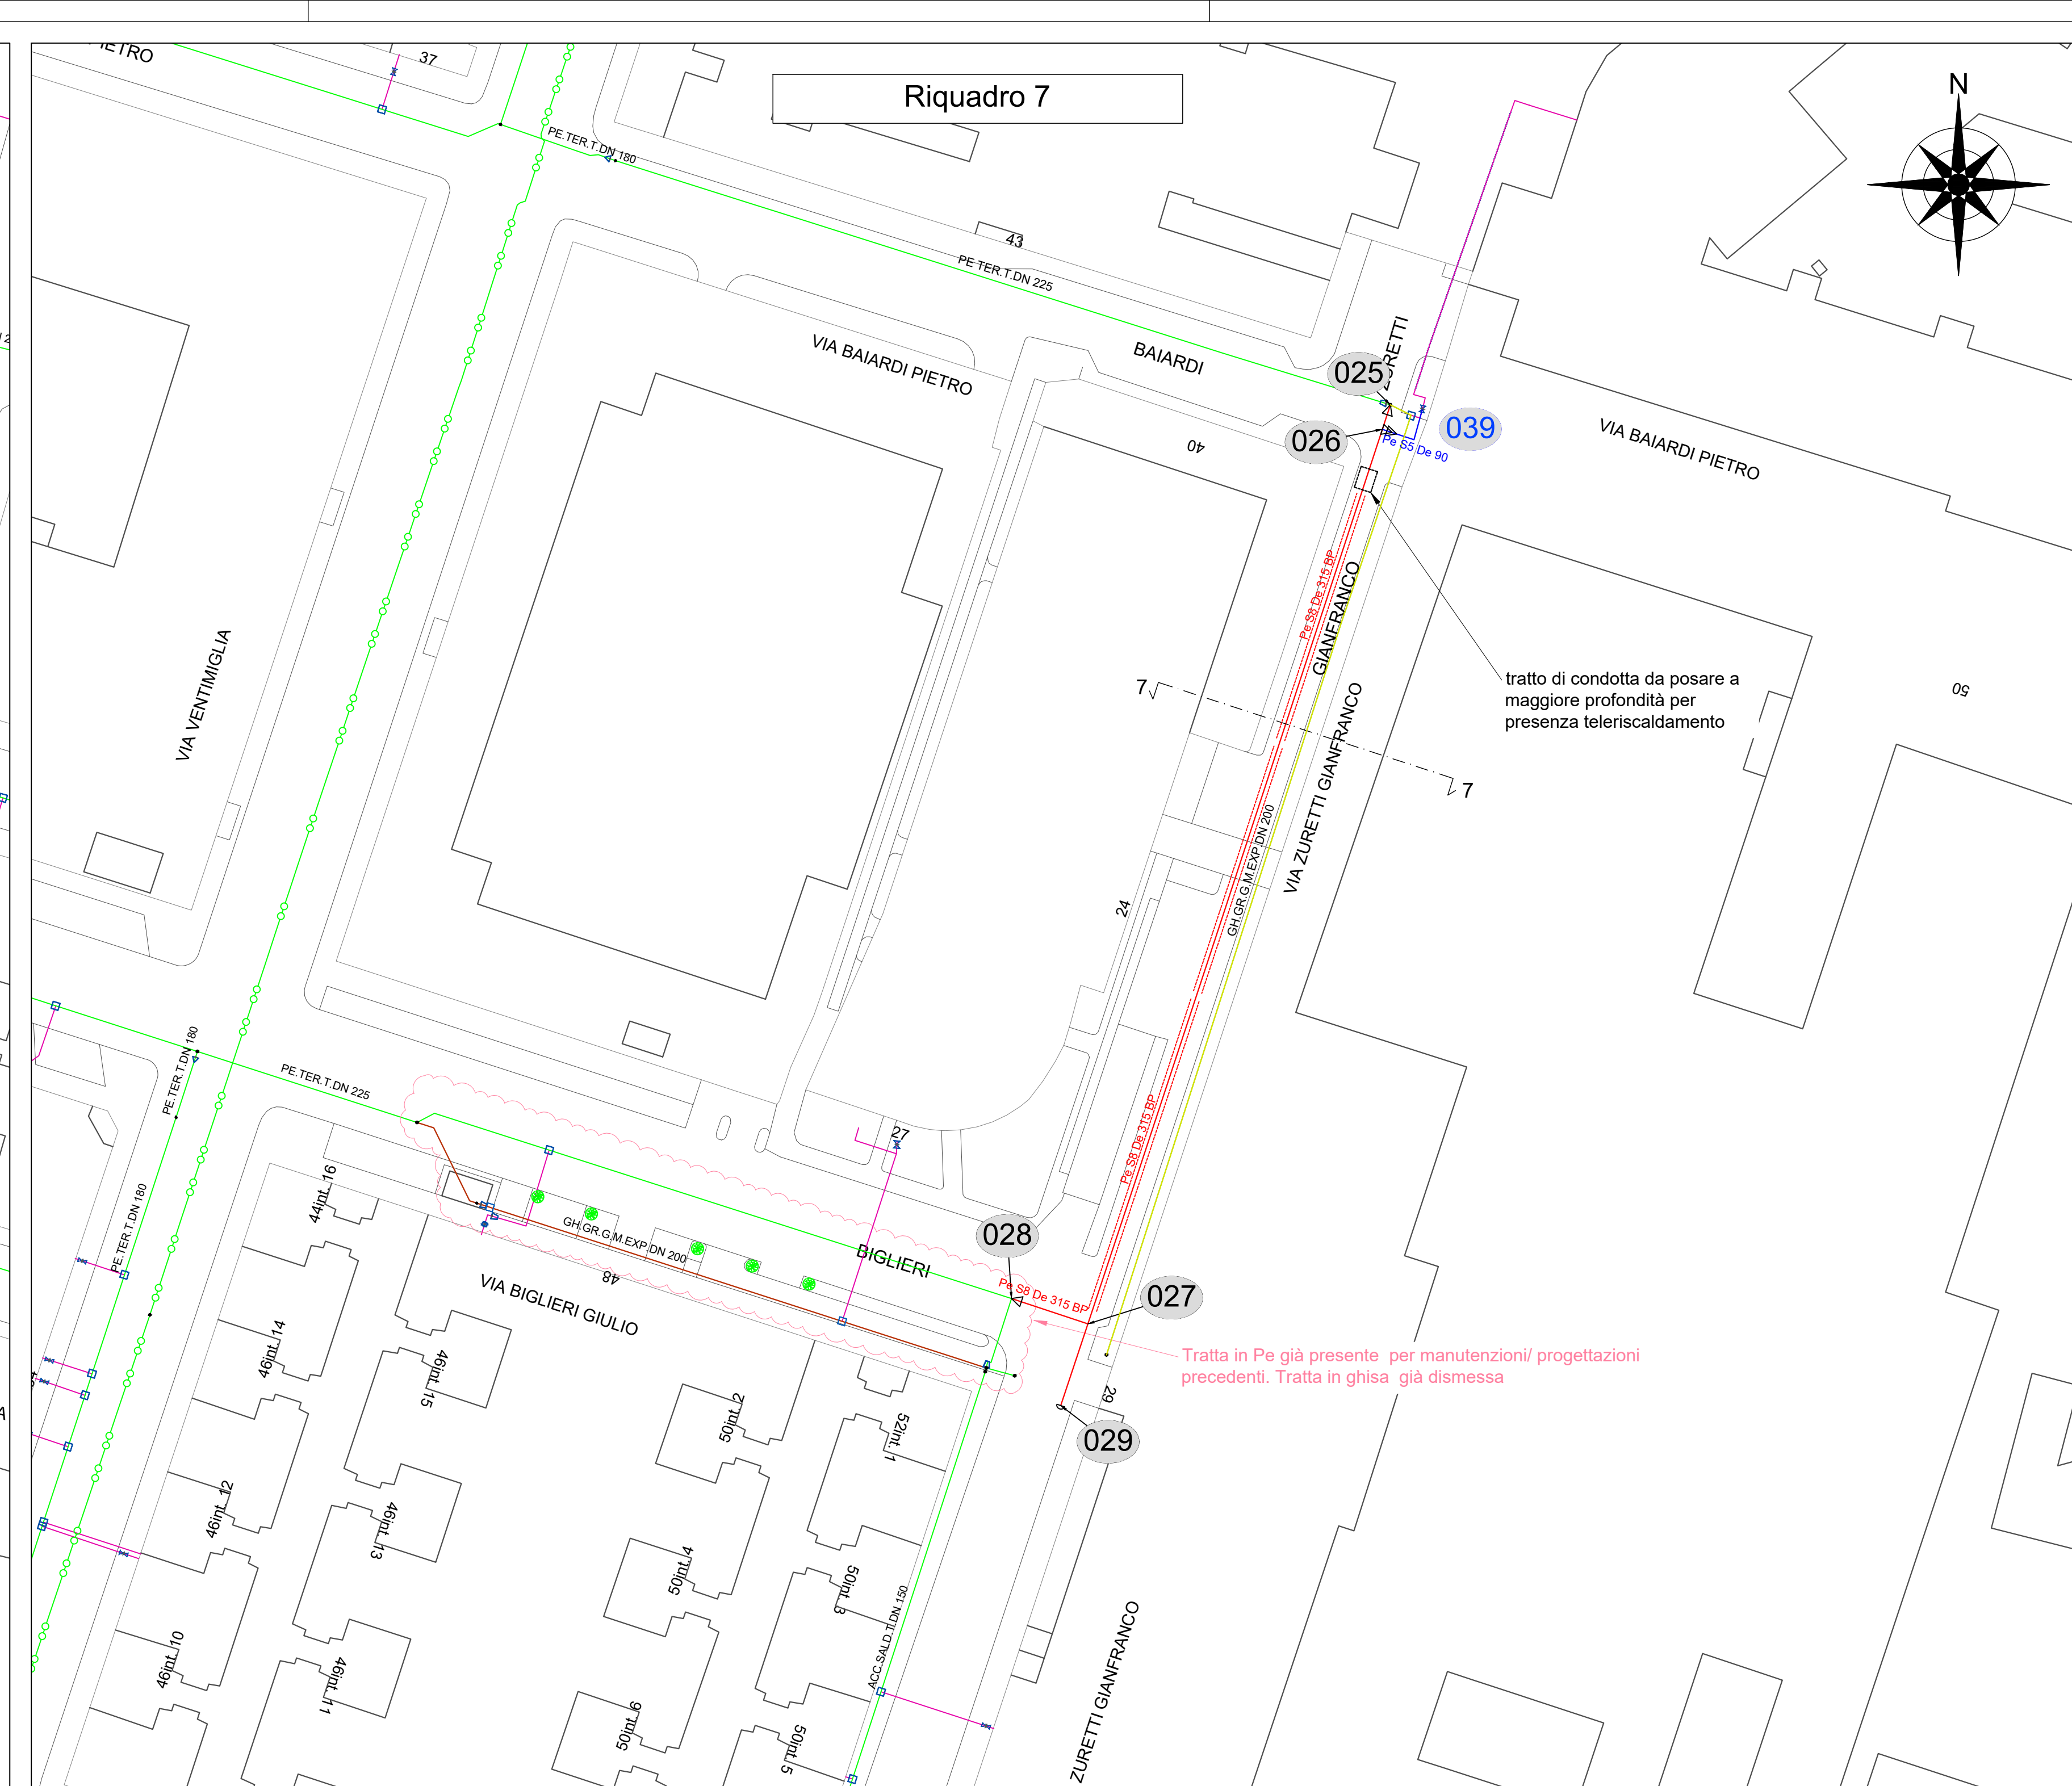
















|                                                                                     |                              |                                                                                     |                 |                                                                                     |                           |
|-------------------------------------------------------------------------------------|------------------------------|-------------------------------------------------------------------------------------|-----------------|-------------------------------------------------------------------------------------|---------------------------|
|  | Rete in progetto BP          |  | Organo di presa |  | Numero I.D.U. in progetto |
|  | Tubazione I.D.U. esistente   |                                                                                     |                 |                                                                                     |                           |
|  | Rete da rimuovere            |                                                                                     |                 |                                                                                     |                           |
|  | Tubazione I.D.U. in progetto |                                                                                     |                 |                                                                                     |                           |

| Riepilogo allacciamenti |                                        |            |                    |       |                      |       |               |       |                   |
|-------------------------|----------------------------------------|------------|--------------------|-------|----------------------|-------|---------------|-------|-------------------|
| n.                      | Posizione                              | Tipologico | diametro esistente |       | diametro di progetto |       | lunghezza (L) | ΔH[m] | Lportata >15m [m] |
|                         |                                        |            | Acc DN             | Pe De | Acc DN               | Pe De |               |       |                   |
| 106                     | Via Genovè civ. 171 da Via Caramagna   | 4          | 40                 | -     | -                    | 50    | 11,60         |       |                   |
| 107                     | Via Caramagna civ. 28                  | 4          | 40                 | -     | -                    | 50    | 11,50         |       |                   |
| 108                     | Via Caramagna civ. 21                  | 2          | 2                  | 63    | -                    | 63    | 6,3           | 2,00  |                   |
| 109                     | Via Caramagna civ. 21                  | 3          | 75                 | -     | -                    | 90    | 3,50          |       |                   |
| 110                     | Via Valenza civ. 71 da Ventimiglia     | 3          | 40                 | -     | -                    | 50    | 8,00          |       |                   |
| 111                     | Via Ventimiglia civ. 145               | 6          | 40                 | -     | -                    | 50    | 21,50         |       |                   |
| 112                     | Via Ventimiglia civ. 146               | 3          | 80                 | -     | -                    | 90    | 8,00          |       |                   |
| 113                     | Via Caramagna civ. 34 da Ventimiglia   | 3          | 3                  | 60    | -                    | 60    | 6,3           | 8,00  |                   |
| 114                     | Via Ventimiglia civ. 156               | 3          | 50                 | -     | -                    | 63    | 8,50          |       |                   |
| 115                     | Via Ventimiglia civ. 160               | 3          | 75                 | -     | -                    | 90    | 8,50          |       |                   |
| 116                     | Via Ventimiglia civ. 166               | 3          | 75                 | -     | -                    | 90    | 19,50         |       |                   |
| 117                     | Via Ventimiglia civ. 166               | 3          | 3                  | 75    | -                    | 90    | 9,50          |       |                   |
| 118                     | Via Ventimiglia civ. 168               | 3          | 50                 | -     | -                    | 63    | 19,50         |       |                   |
| 119                     | Via Ventimiglia civ. 170               | 3          | 50                 | -     | -                    | 63    | 19,50         |       |                   |
| 120                     | Via Ventimiglia civ. 172               | 1          | -                  | 63    | -                    | 63    | 19,50         |       |                   |
| 121                     | Via Ventimiglia civ. 174               | 3          | 80                 | -     | -                    | 90    | 19,50         |       |                   |
| 122                     | Via Ventimiglia civ. 165 alt. civ. 174 | 4          | 4                  | 80    | -                    | 80    | 11,50         |       |                   |
| 123                     | Via Ventimiglia civ. 176               | 3          | 80                 | -     | -                    | 90    | 19,50         |       |                   |

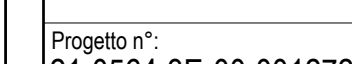

Progetto n°:  
21-0564-3E-00-001272  
WBS: SI.20.03300.02.1109

Codice elaborato: 25.7

|                      |       |
|----------------------|-------|
| None for: All 25 deg |       |
| Format: A1           | Score |

Committee:



Reti

|                                    |                                        |
|------------------------------------|----------------------------------------|
| Progettista:<br>Ing. Claudio Gatti | Unità Responsabile della Progettazione |
|------------------------------------|----------------------------------------|

Ordine degli Ingegneri di Pavia  
Albo n. 3197

[illegible]

|  |  |  |  |  |  |  |  |  |
|--|--|--|--|--|--|--|--|--|
|  |  |  |  |  |  |  |  |  |
|--|--|--|--|--|--|--|--|--|

|  |  |  |  |  |  |  |  |
|--|--|--|--|--|--|--|--|
|  |  |  |  |  |  |  |  |
|--|--|--|--|--|--|--|--|

|                                  |      |    |    |    |             |             |           |
|----------------------------------|------|----|----|----|-------------|-------------|-----------|
| Descrizione:                     | 00   | 28 | 01 | 26 | A. Inglerdi | L. Domingo  | C. Gatti  |
| Emissione per progetto esecutivo |      |    |    |    |             |             |           |
| Comm. - MCM                      | Dir. | C. | M. | I. | Redatto     | Controllato | Approvato |

|                                   |      |    |    |    |         |            |           |
|-----------------------------------|------|----|----|----|---------|------------|-----------|
| Comit. 2464                       | Rev. | Q. | M. | A. | Redatto | Confermato | Approvato |
| Comune di Torino (TO) - Vie Varie |      |    |    |    |         |            |           |

PROGETTO ESECUTIVO  
SOSTITUZIONE RETE RR (2.745,39 m) - GARA TO1

Intervento n° SI-036213-001272-TSS-TORIN008

Planimetria di localizzazione IDU - Tavola 7



