

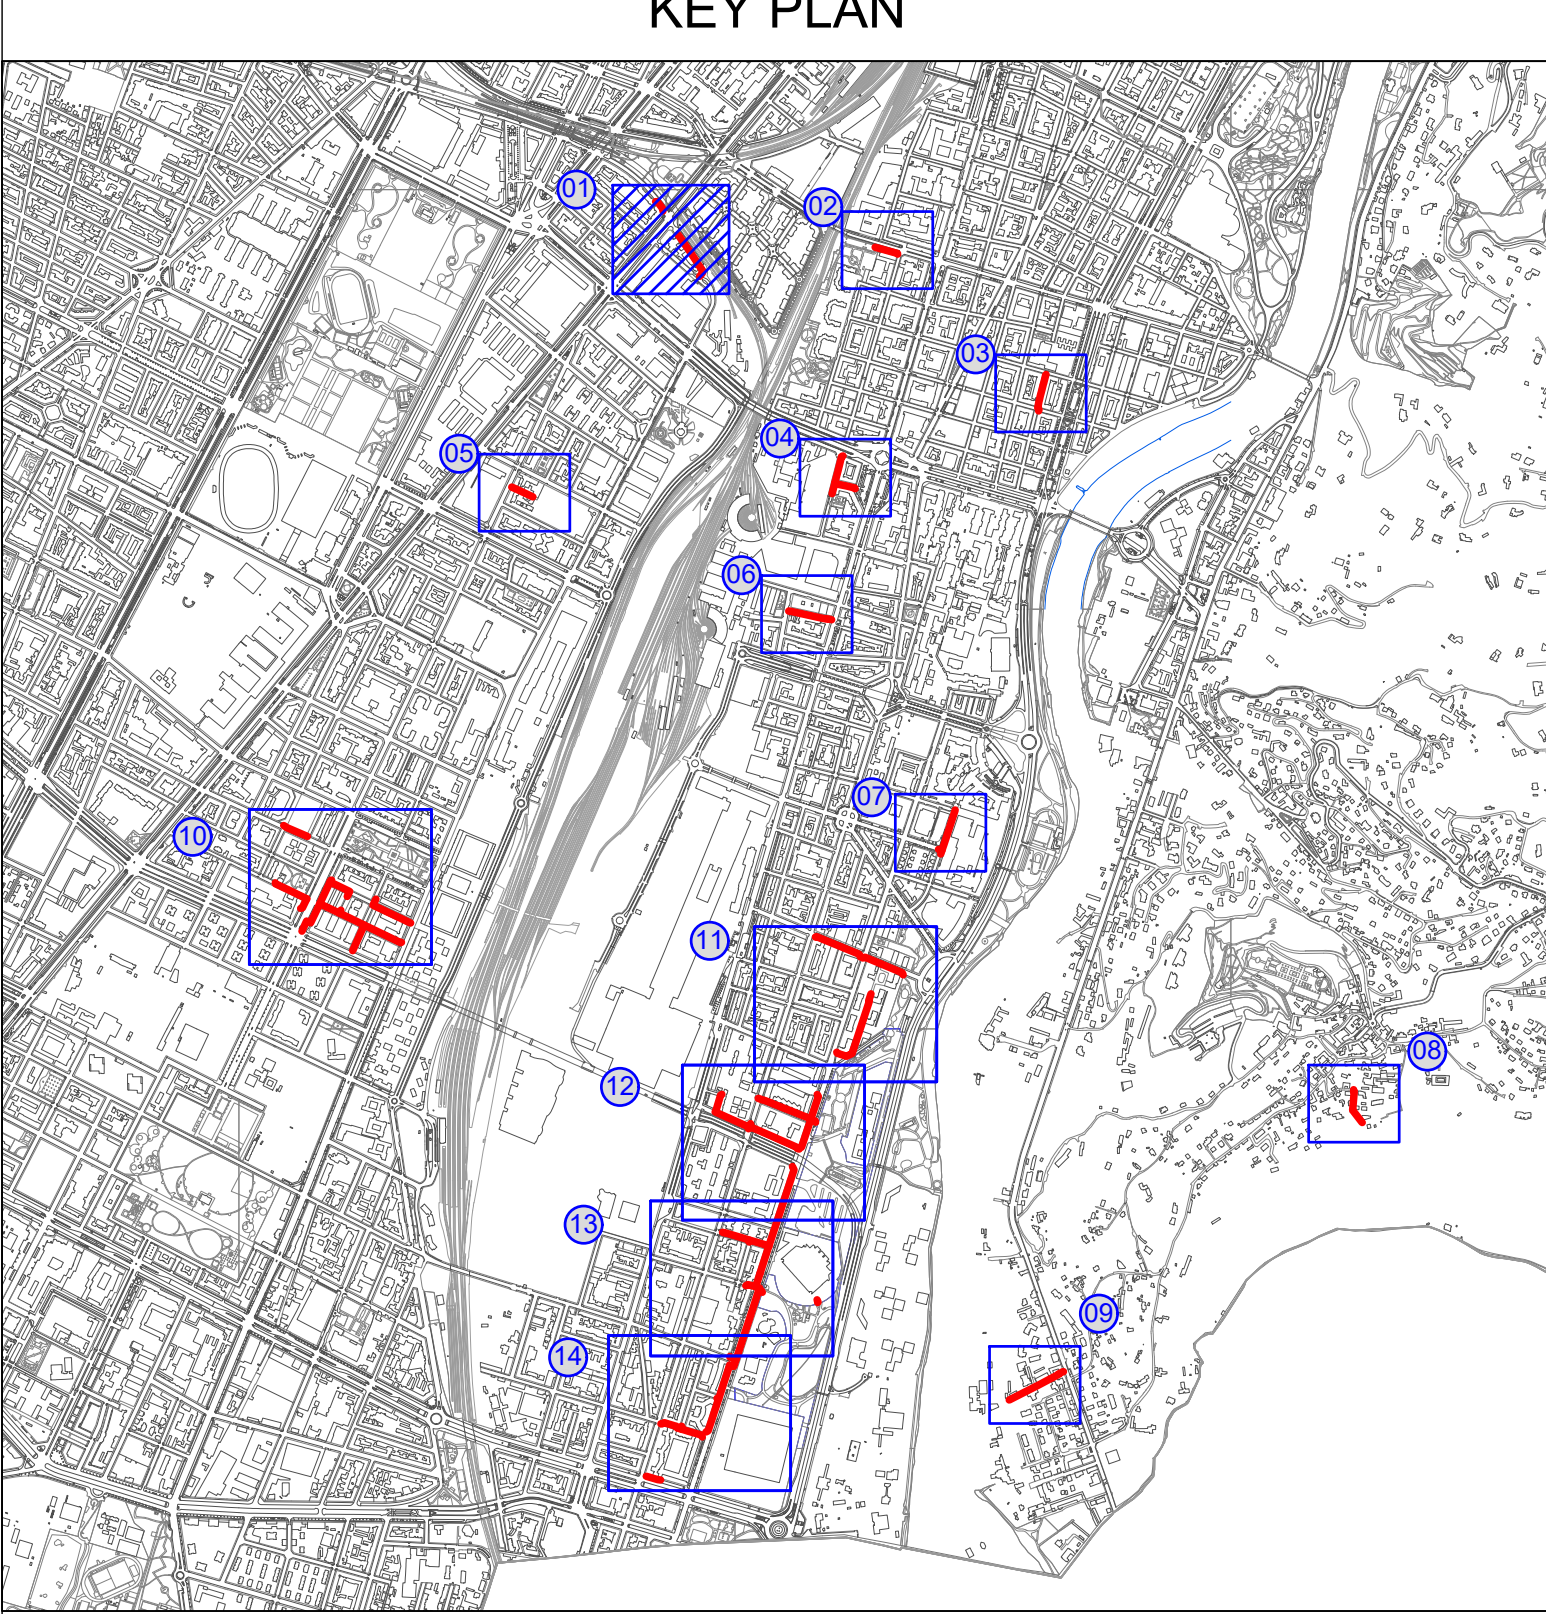


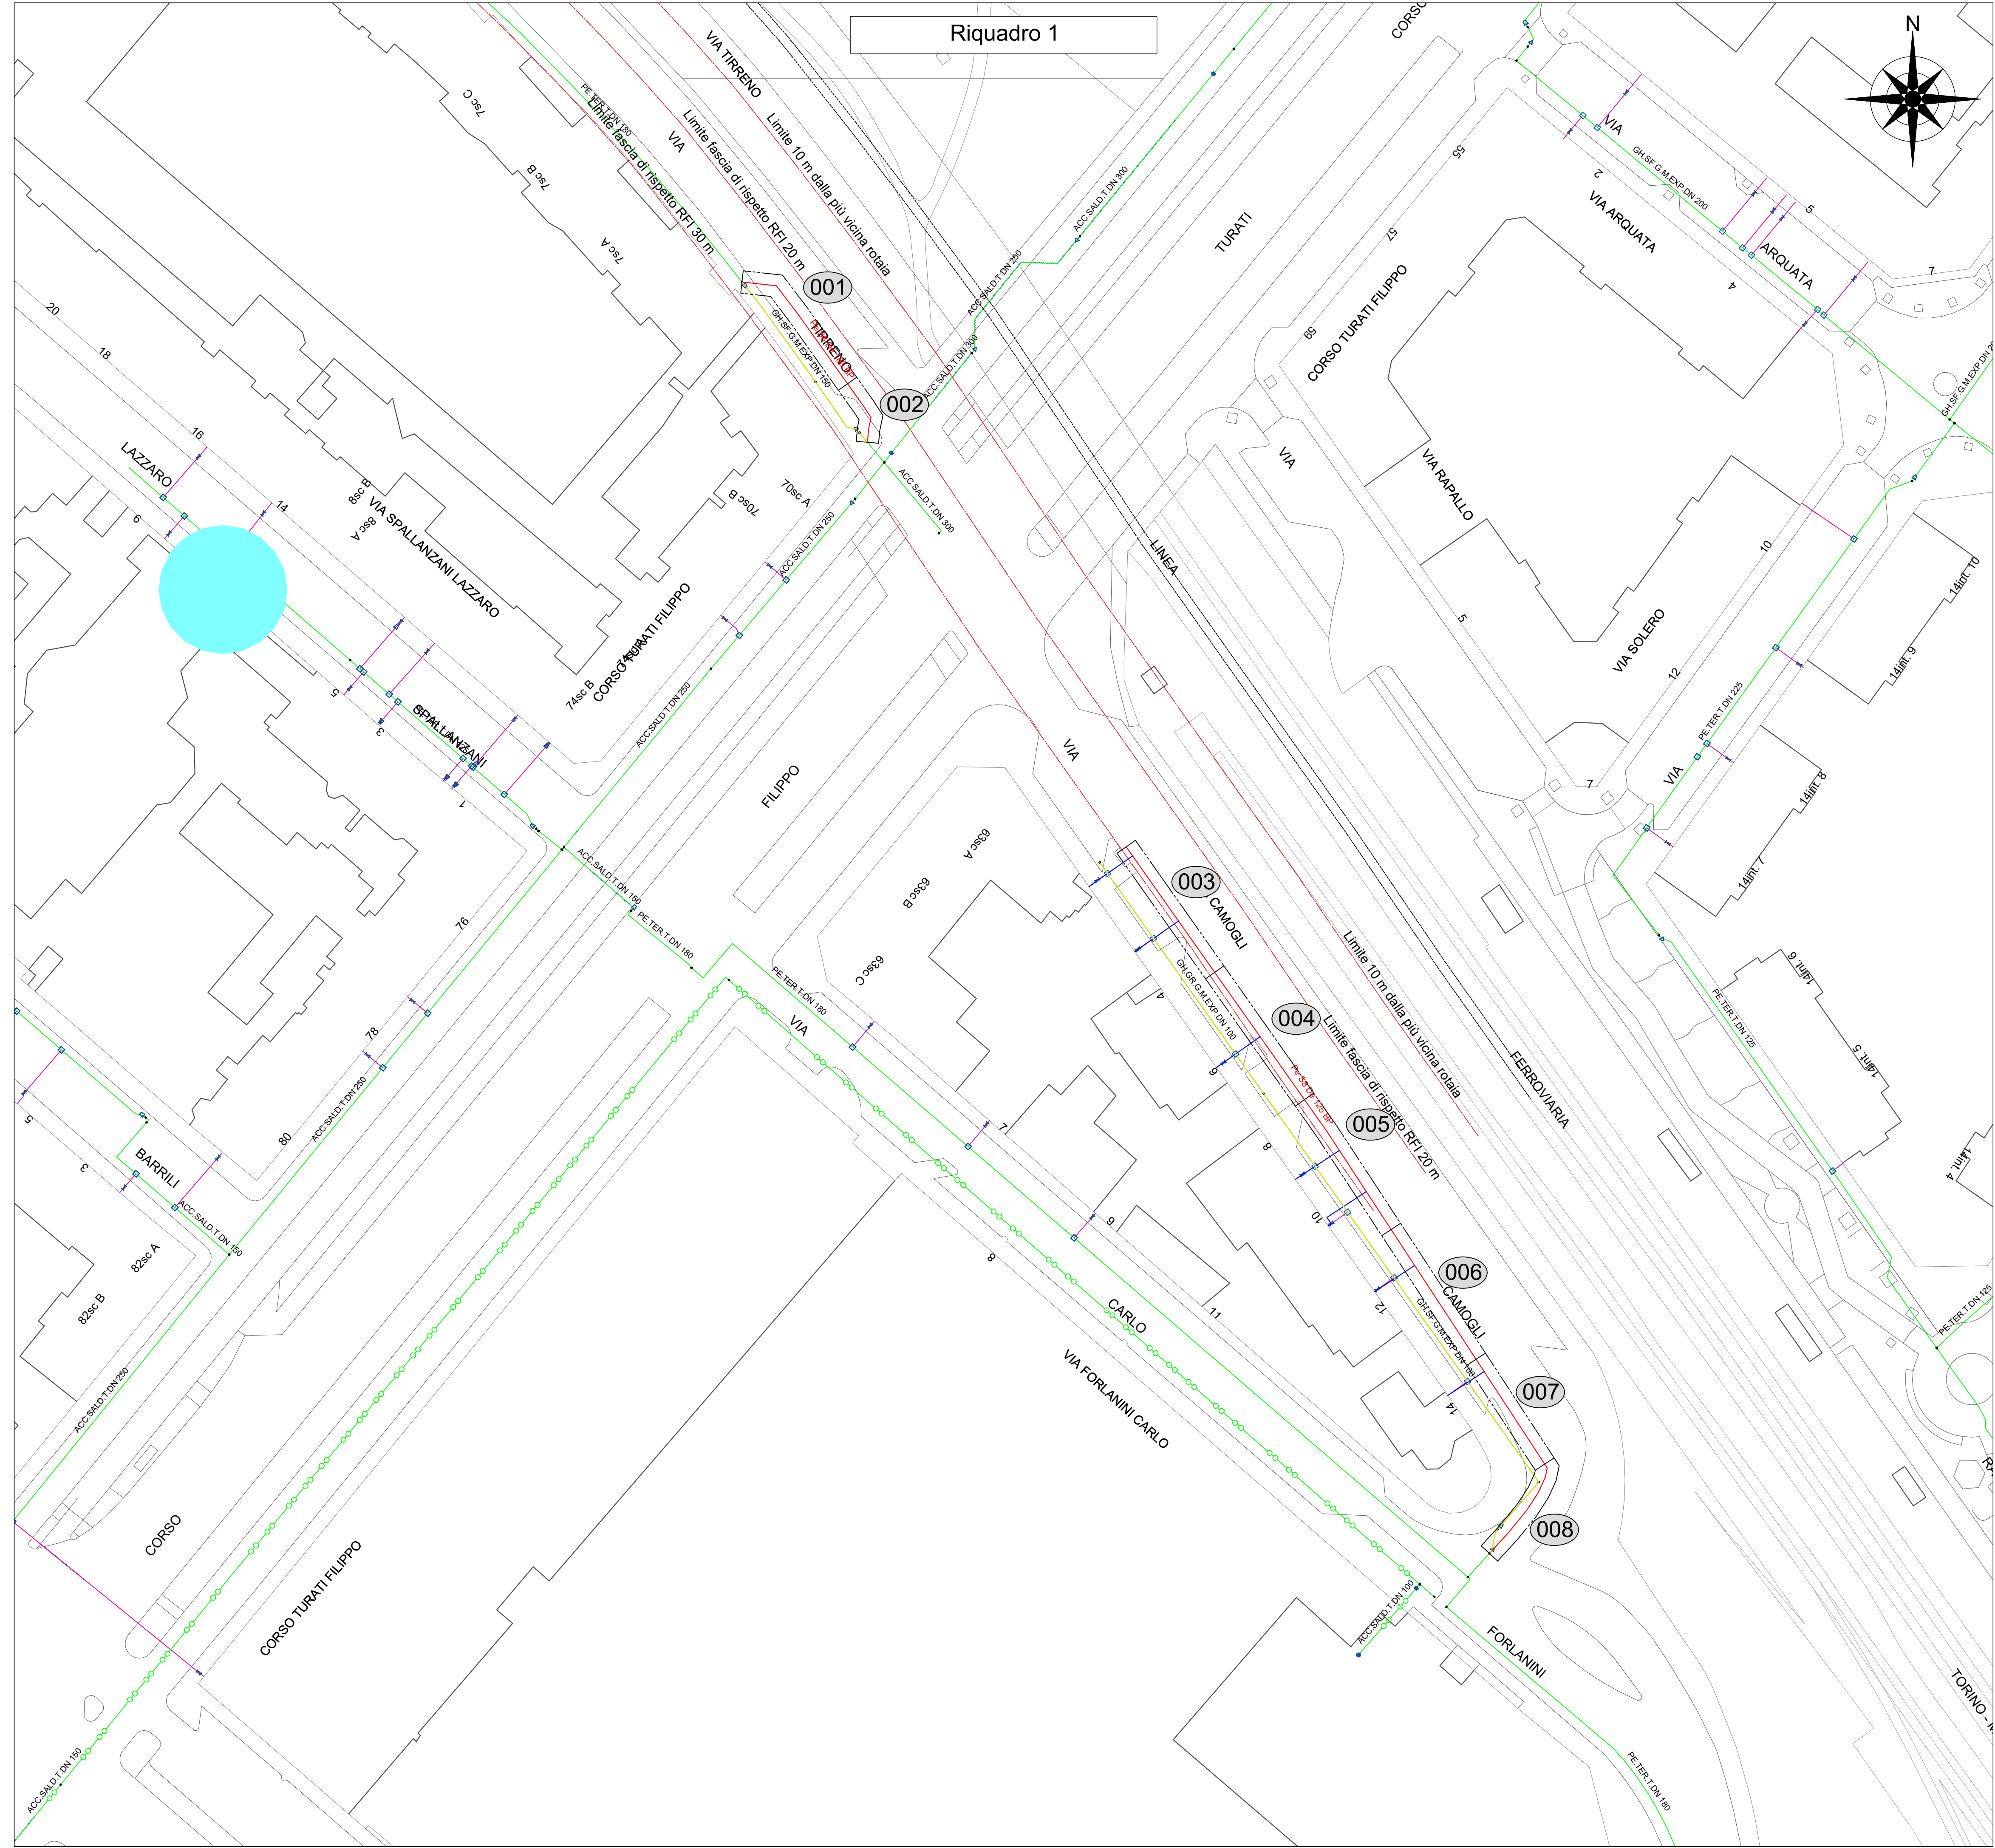

LEGENDA

	Rete nuova		Chiese
	Rete da rimuovere		Carabinieri
	Metro		Vigili del fuoco
	Scuole		Cimiteri
	GTT stop		Polizia municipale
	Musei		Ospedali
	Università		Stazioni ferroviarie
	Biblioteche		Altri luoghi di culto
	Uffici postali		Zona sensibile
	Impianti Sportivi		Aree di lavoro

	Progettista: ORDINE INGEGNERI PROV. ALESSANDRIA ALESSANDRO LEARDI Ordine degli ingegneri di Alessandria matr. n° 614/101 Firma	Unità Responsabile della Progettazione						
		INGEREAL-INGE-PROGRE						
Progetto n°: 21-0564-3E-00-001272 WBS: SI.20.10300.02.1109 ALLEGATO n°: 30.1								
Nome File: 01_01_01.mxd	Descrizione:	0	30	11	22	L.Olm	L.Cartasegna	A.Leardi
Formato: A1	Scala 1 : 500	Emissione per commenti		Rev.		G.	M.	A.
Committente	Com. : 2464							
		Comune di TORINO (TO) Vie Varie Progetto Esecutivo SOSTITUZIONE RETE BP (L=2745.39 M) - GARA TO 1 Intervento n° SI-036213-001272-TSS-TORIN008 Planimetria zone sensibili - Tavola 1						

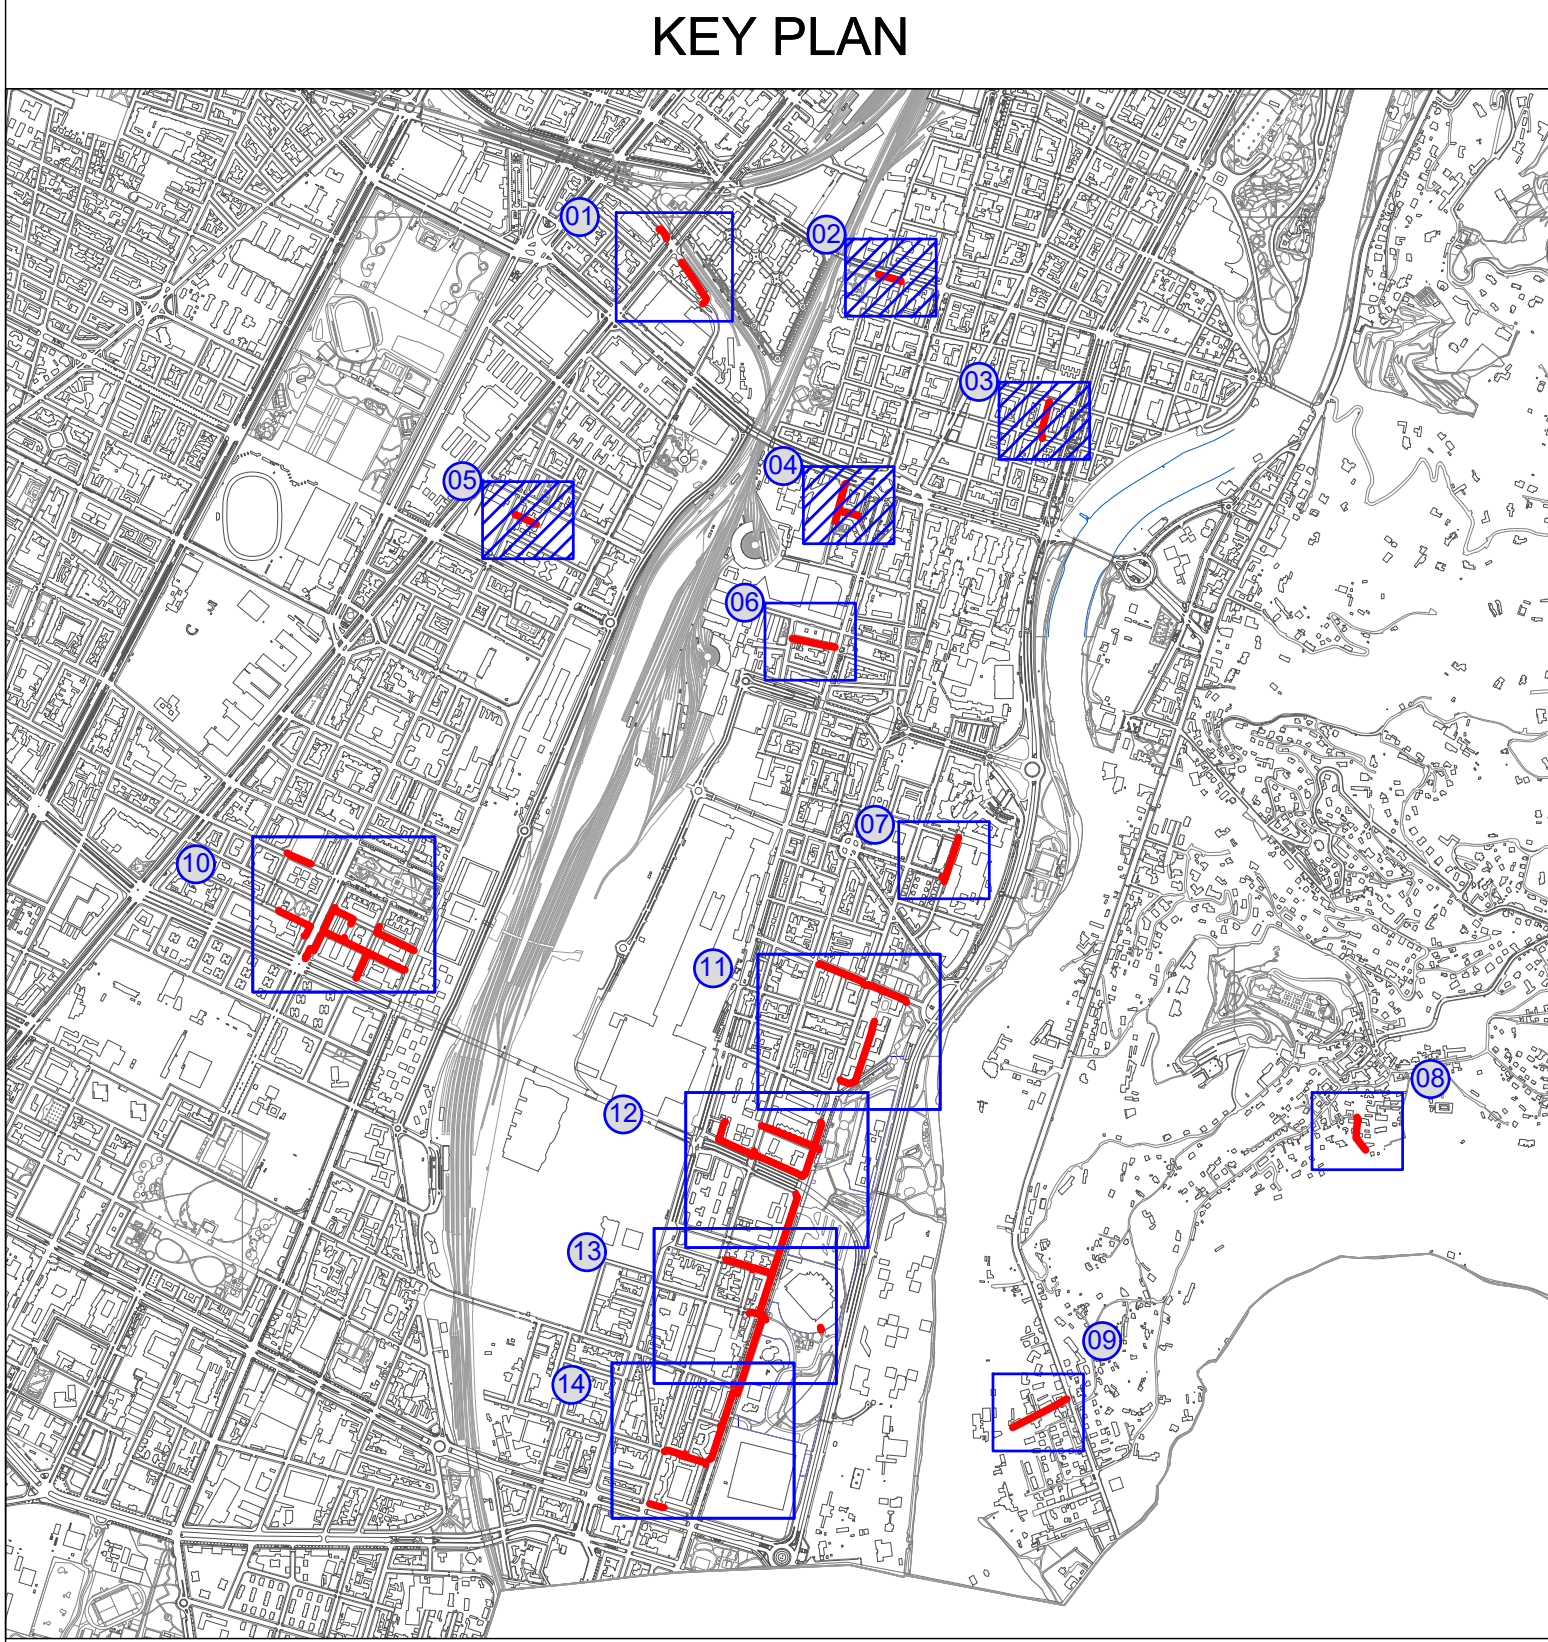




Comune di TORINO (TO)
Via Vane
Progetto Esecutivo
SOSTITUZIONE RETE BP (L=2745,39 M) - GARA TO 1
Intervento n° SI-026213-001272-TSS-TORINO08
Planimetria zone sensibili - Tavola 2

Progetto n°:
21-0564-3E-00-001272
WBS:
SI.20.10300.02.1109
ALLEGATO n°: 30.2
Formato: A0
Scale: 1:500

Comitente:
IG Italgas
Rei

Unità Responsabile della Progettazione:
INGENER-INGE-PROGRE



Revisione	0	1	2	
-----------	---	---	---	---	---	---	---	---	---	---	----	----	-----	-----	------	------	

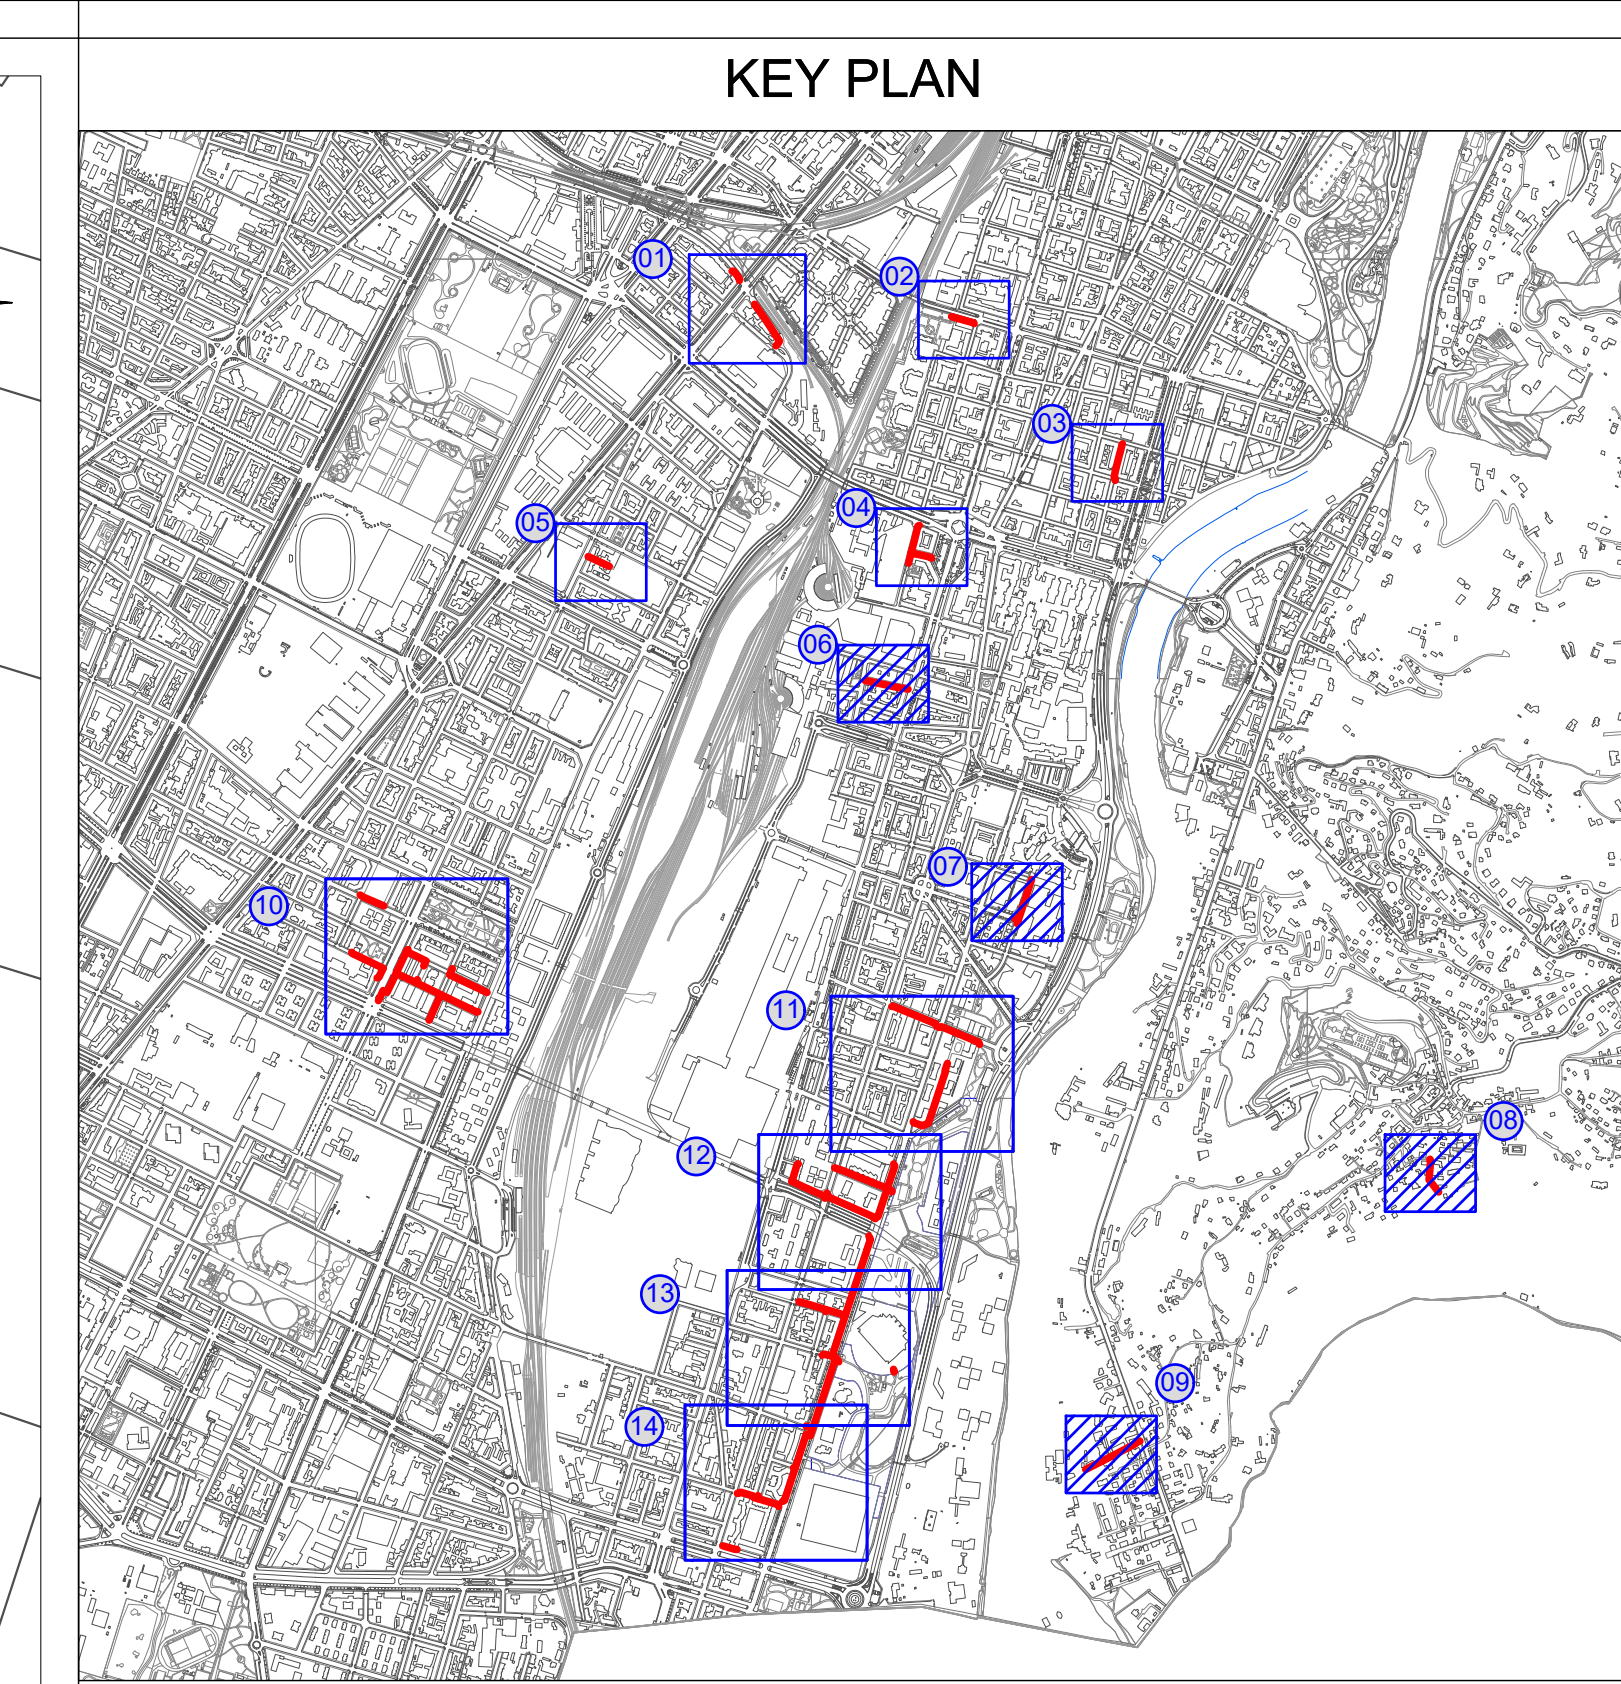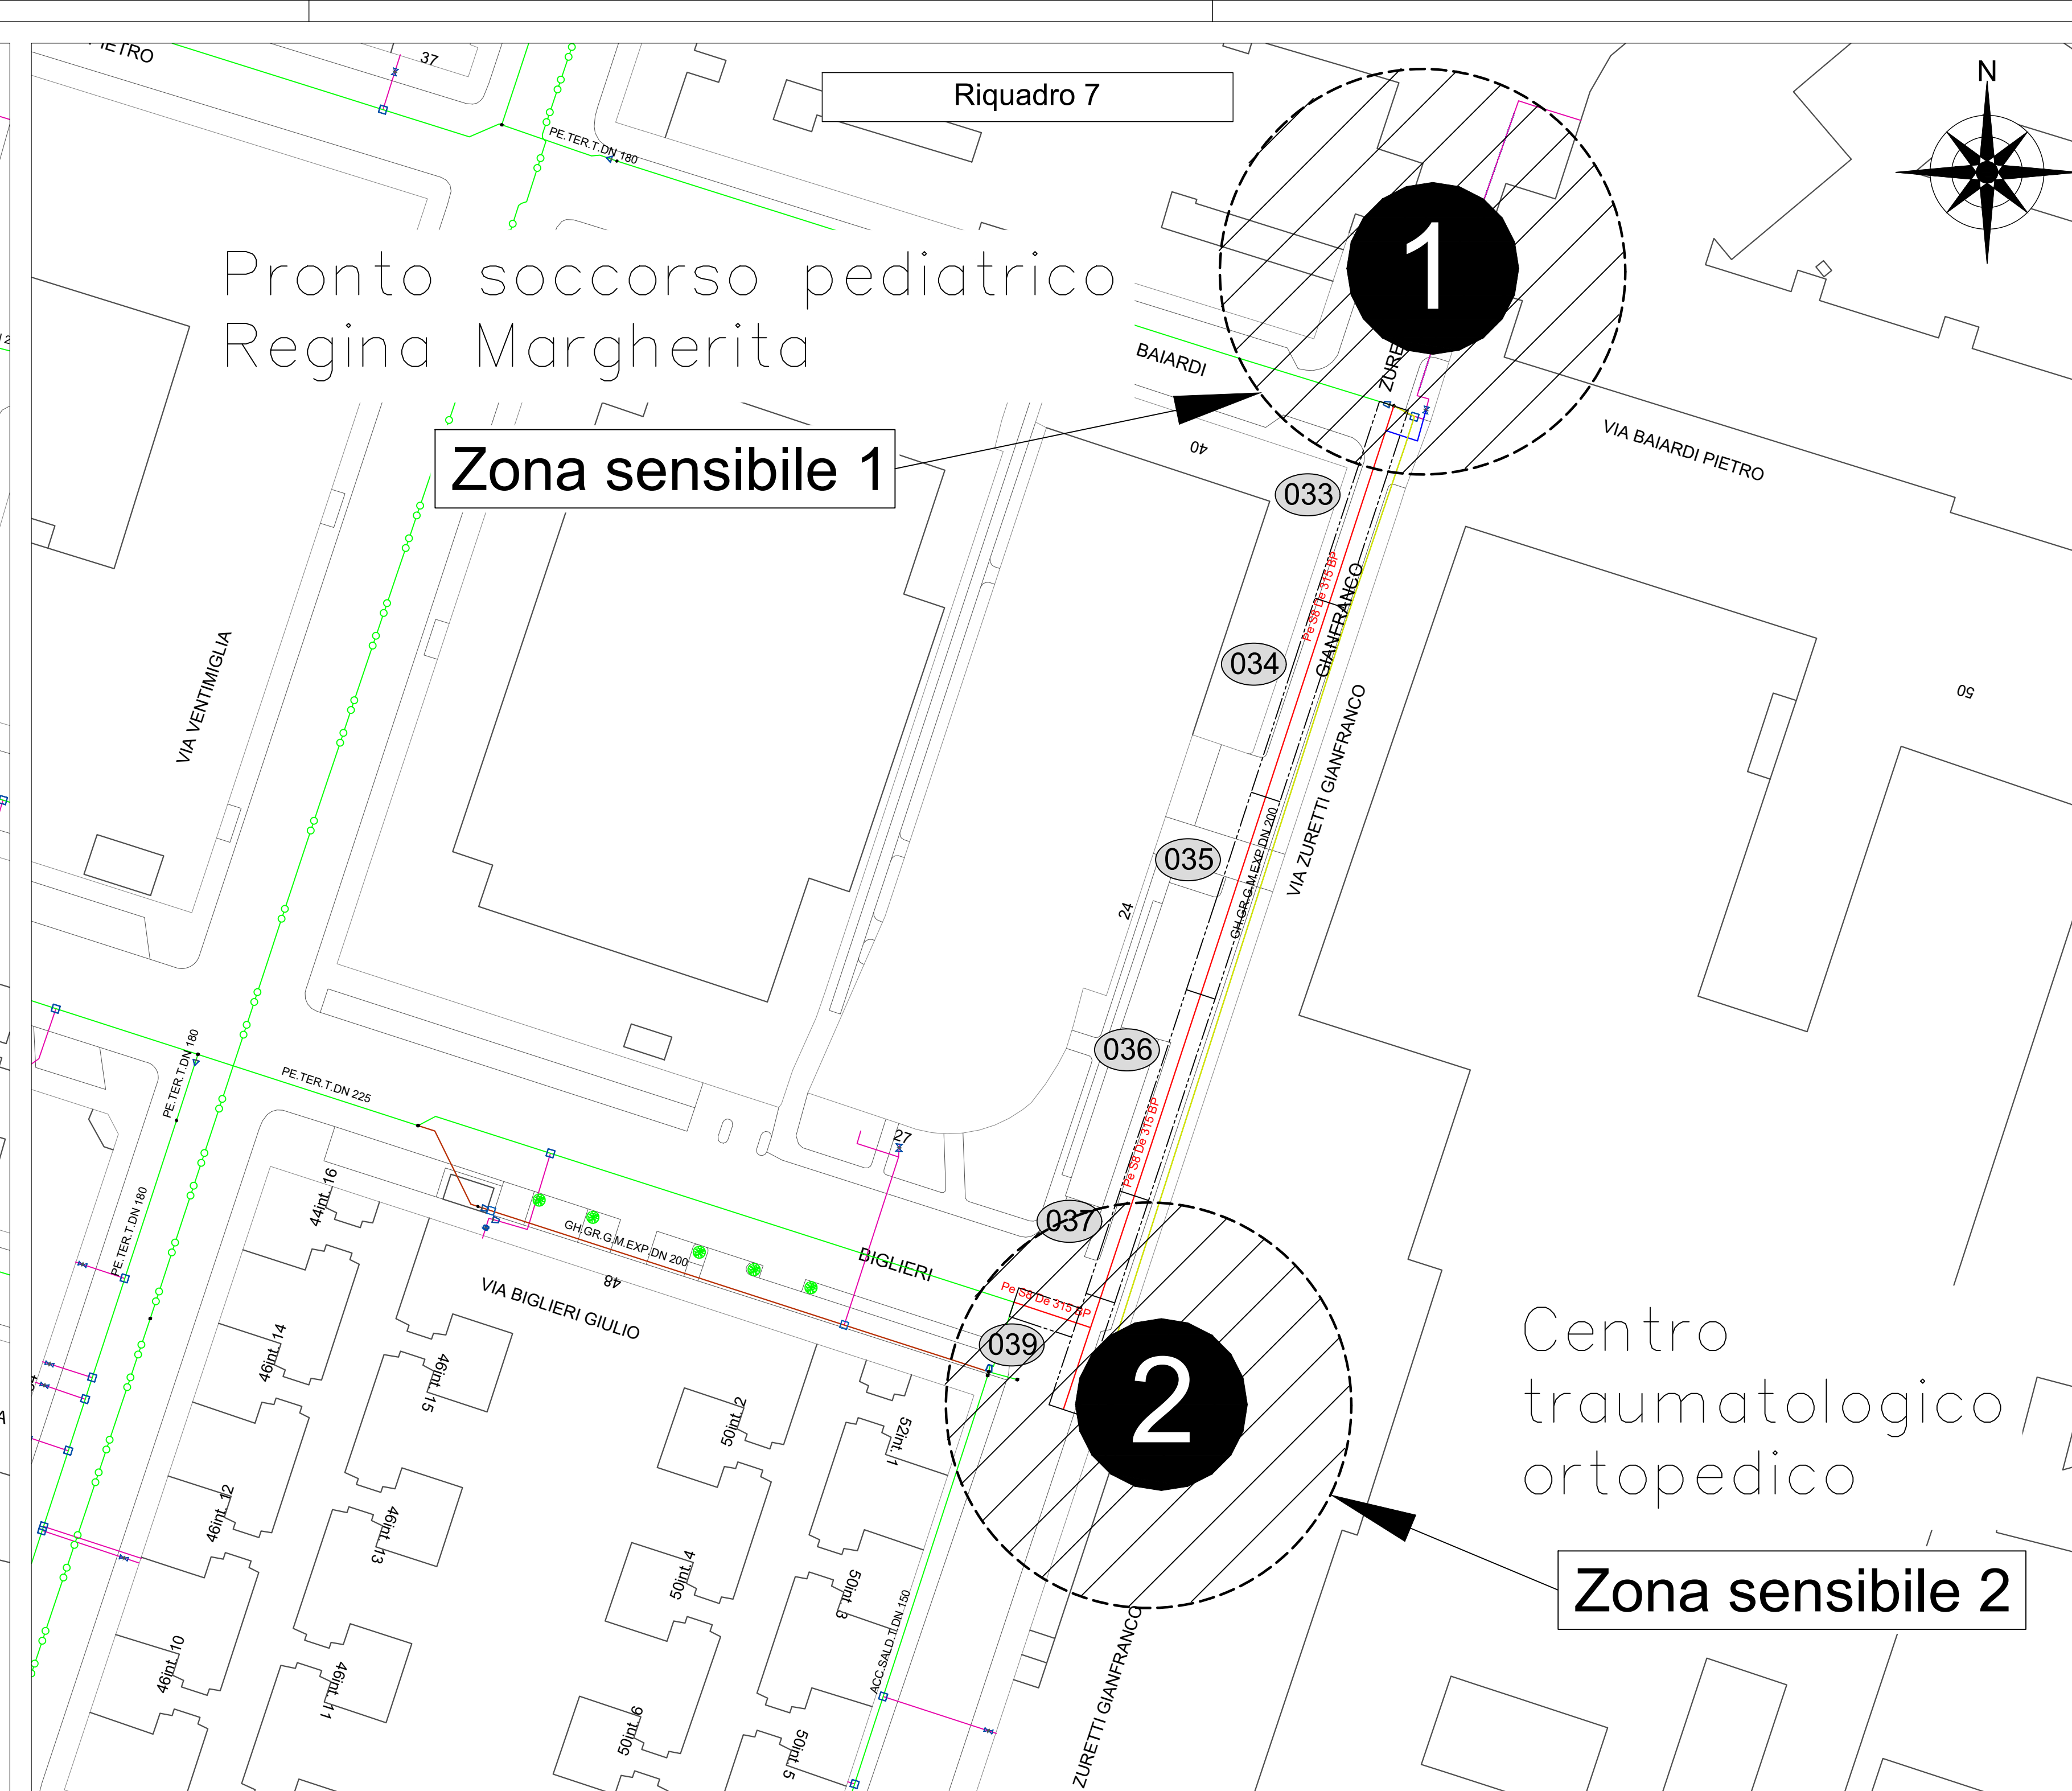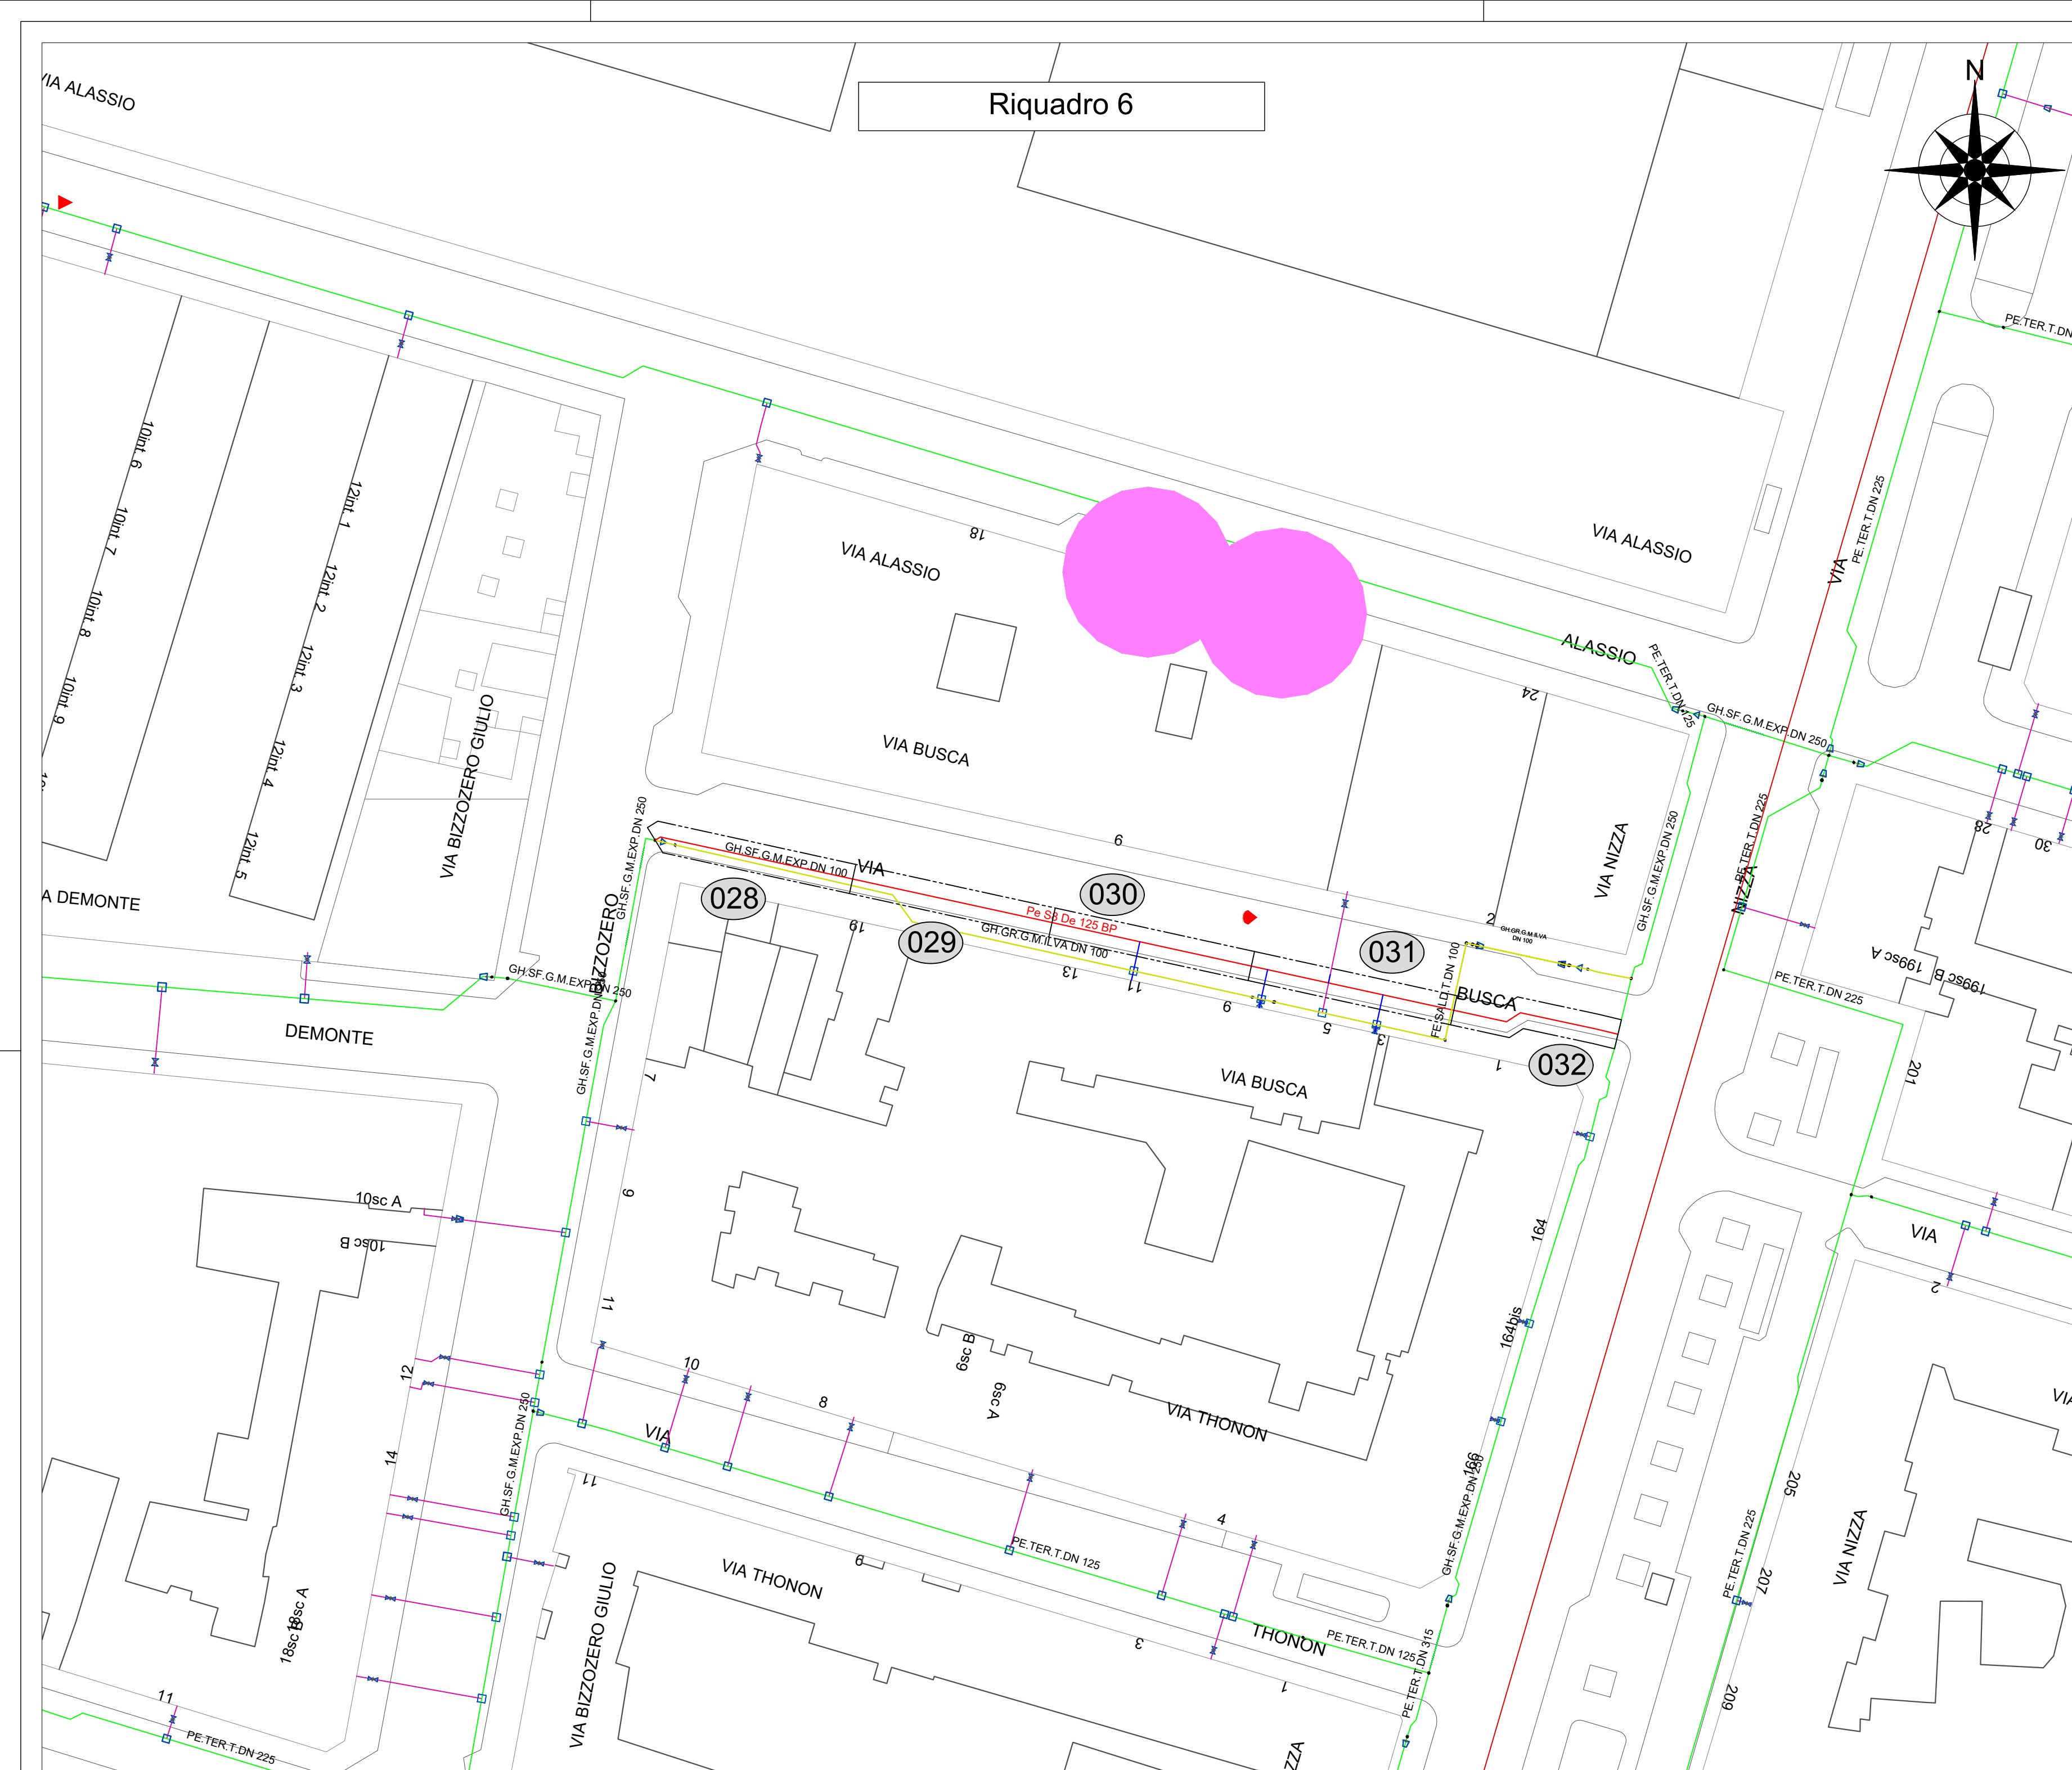

LEGENDA

— Rete nuova	Chiese
— Rete da rimuovere	Carabinieri
— Metro	Vigili del fuoco
— Scuole	Cimiteri
— GTT stop	Polizia municipale
— Musei	Ospedali
— Università	Stazioni ferroviarie
— Biblioteche	Altri luoghi di culto
— Uffici postali	Zona sensibile
— Impianti Sportivi	Aree di lavoro

Zona di lavoro		Zona sensibile	Via/Strada/Spazio	Dettaglio	Nota
033	1	Via Gianfranco Zuretti	Pronto soccorso pediatrico Regina Margherita		Garantire la visibilità alle ambulanze
037-038-039	2	Via Gianfranco Zuretti	Centro traumatologico ortopedico		Garantire la visibilità alle ambulanze
030	3	Corso Moncalieri	Club Sportivo Ronchiverdi		Pianificare le attività di cantiere fuori dall'orario degli eventi

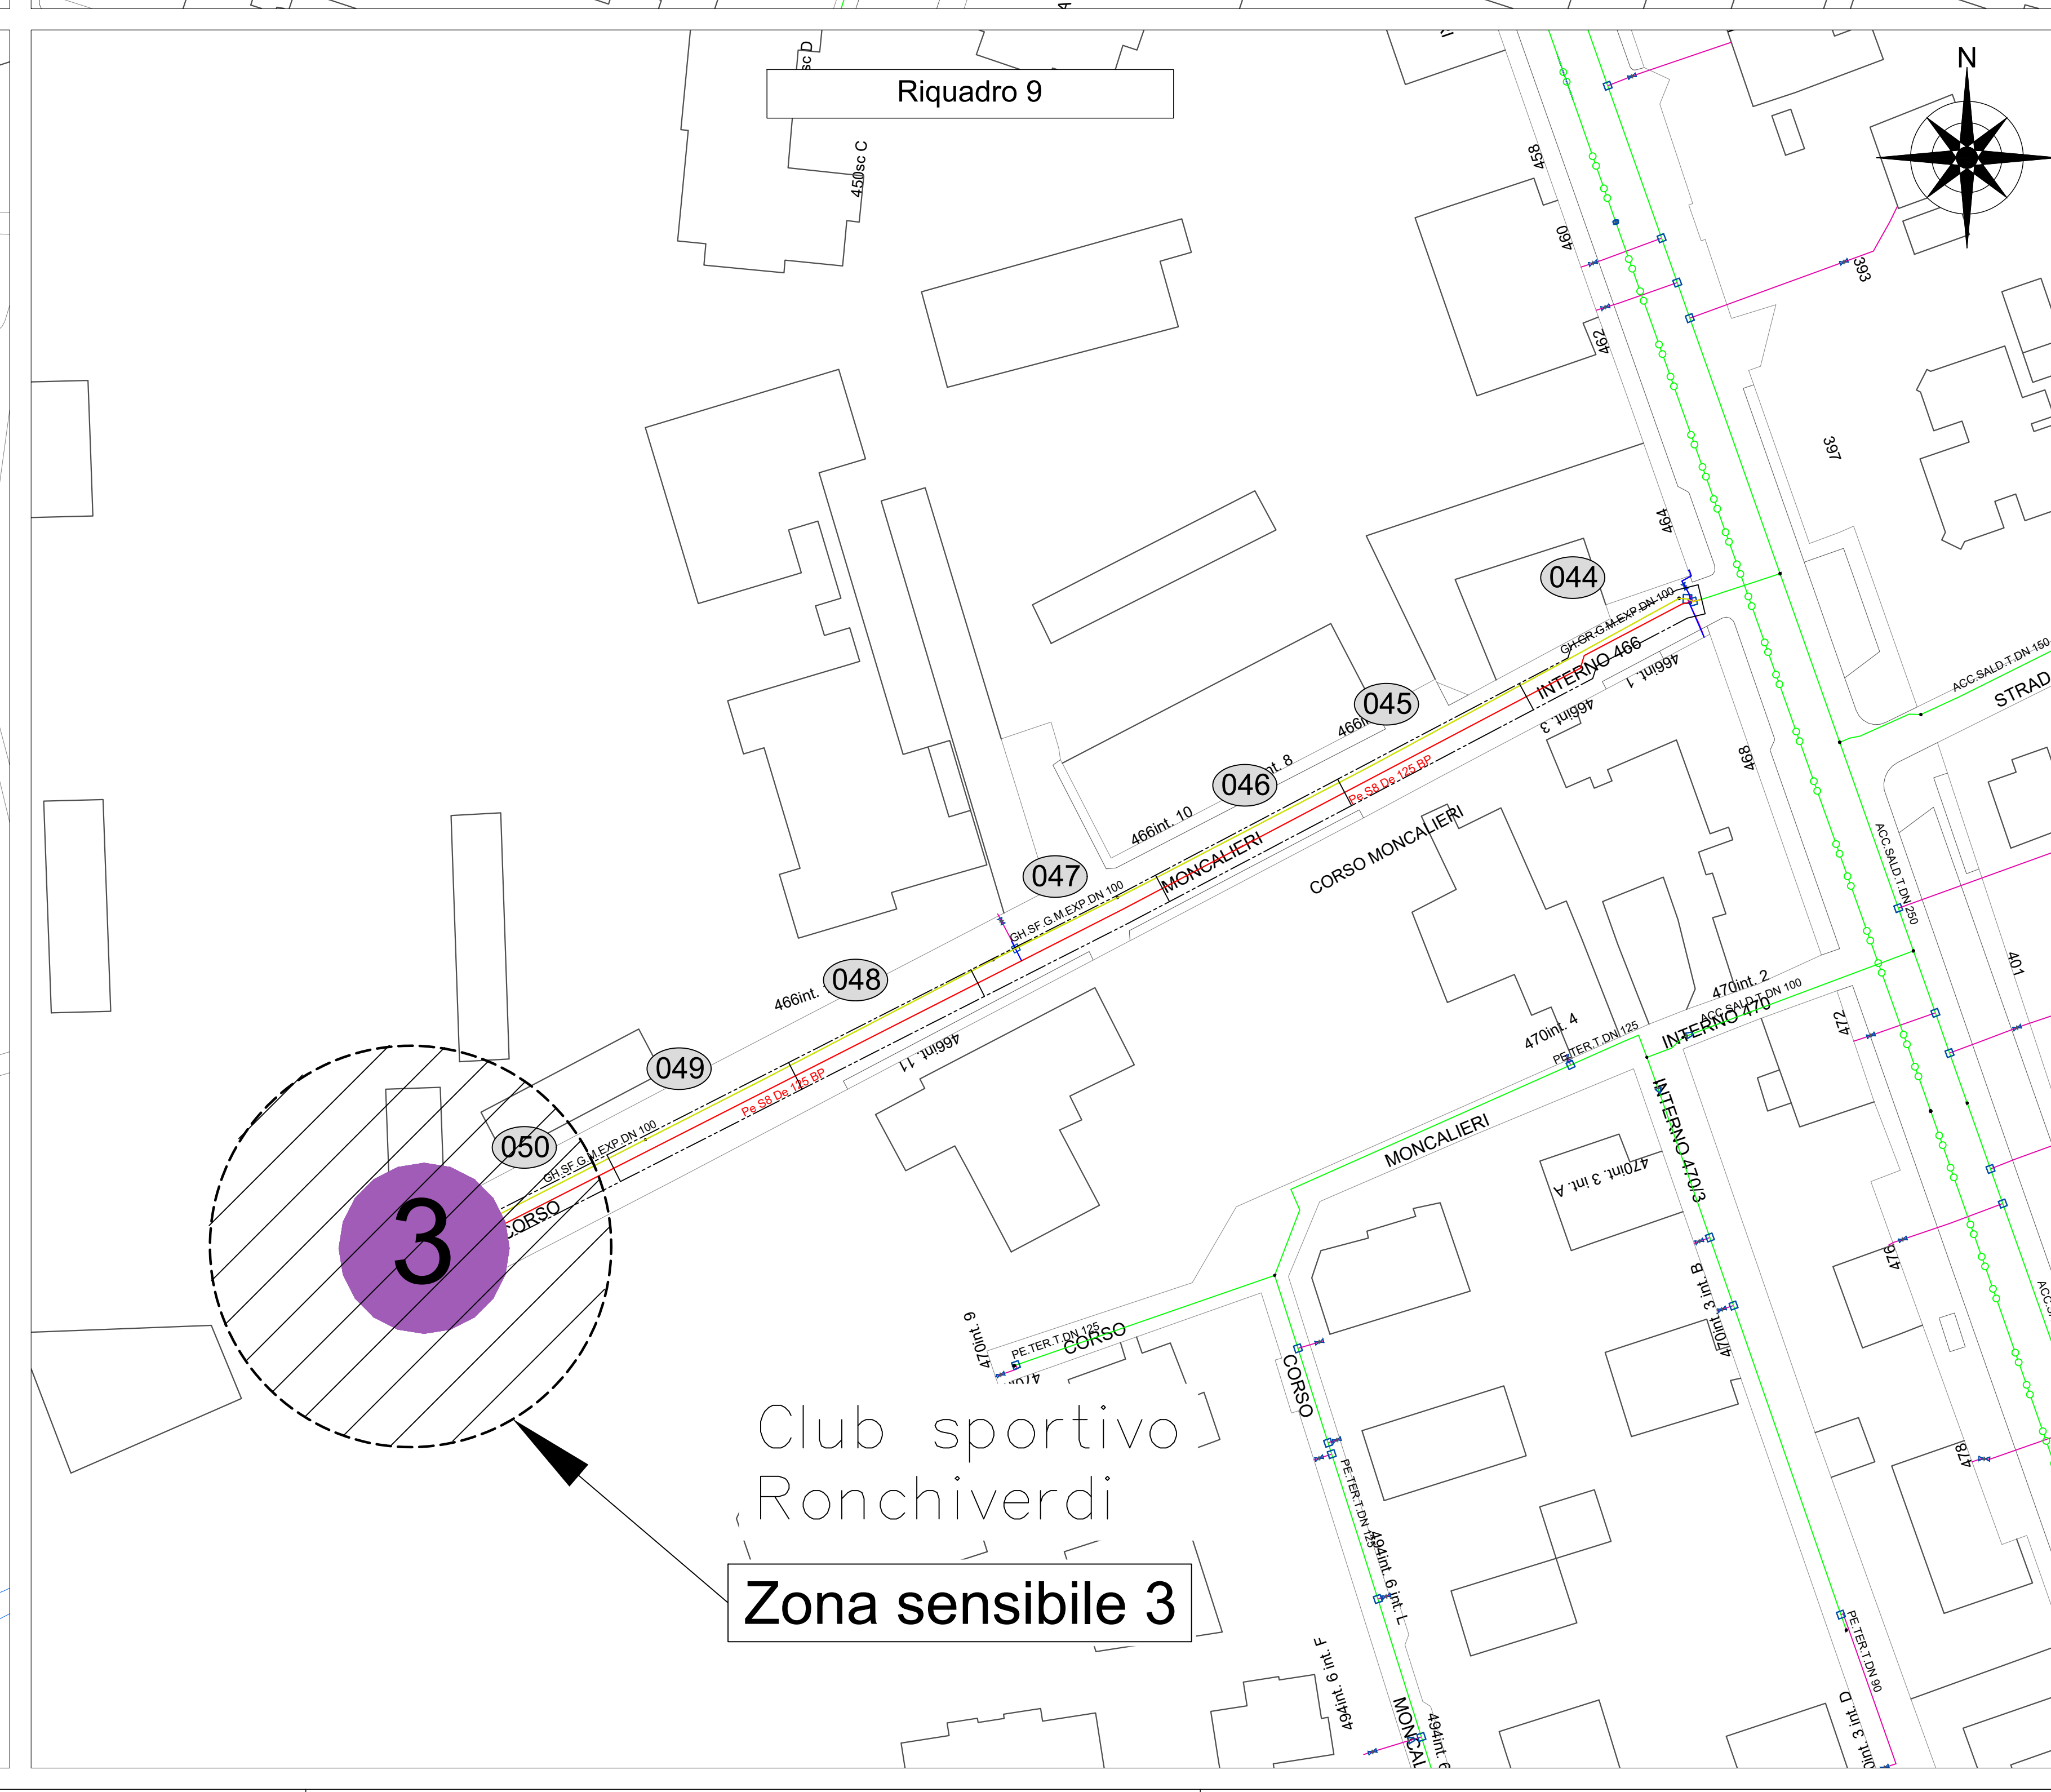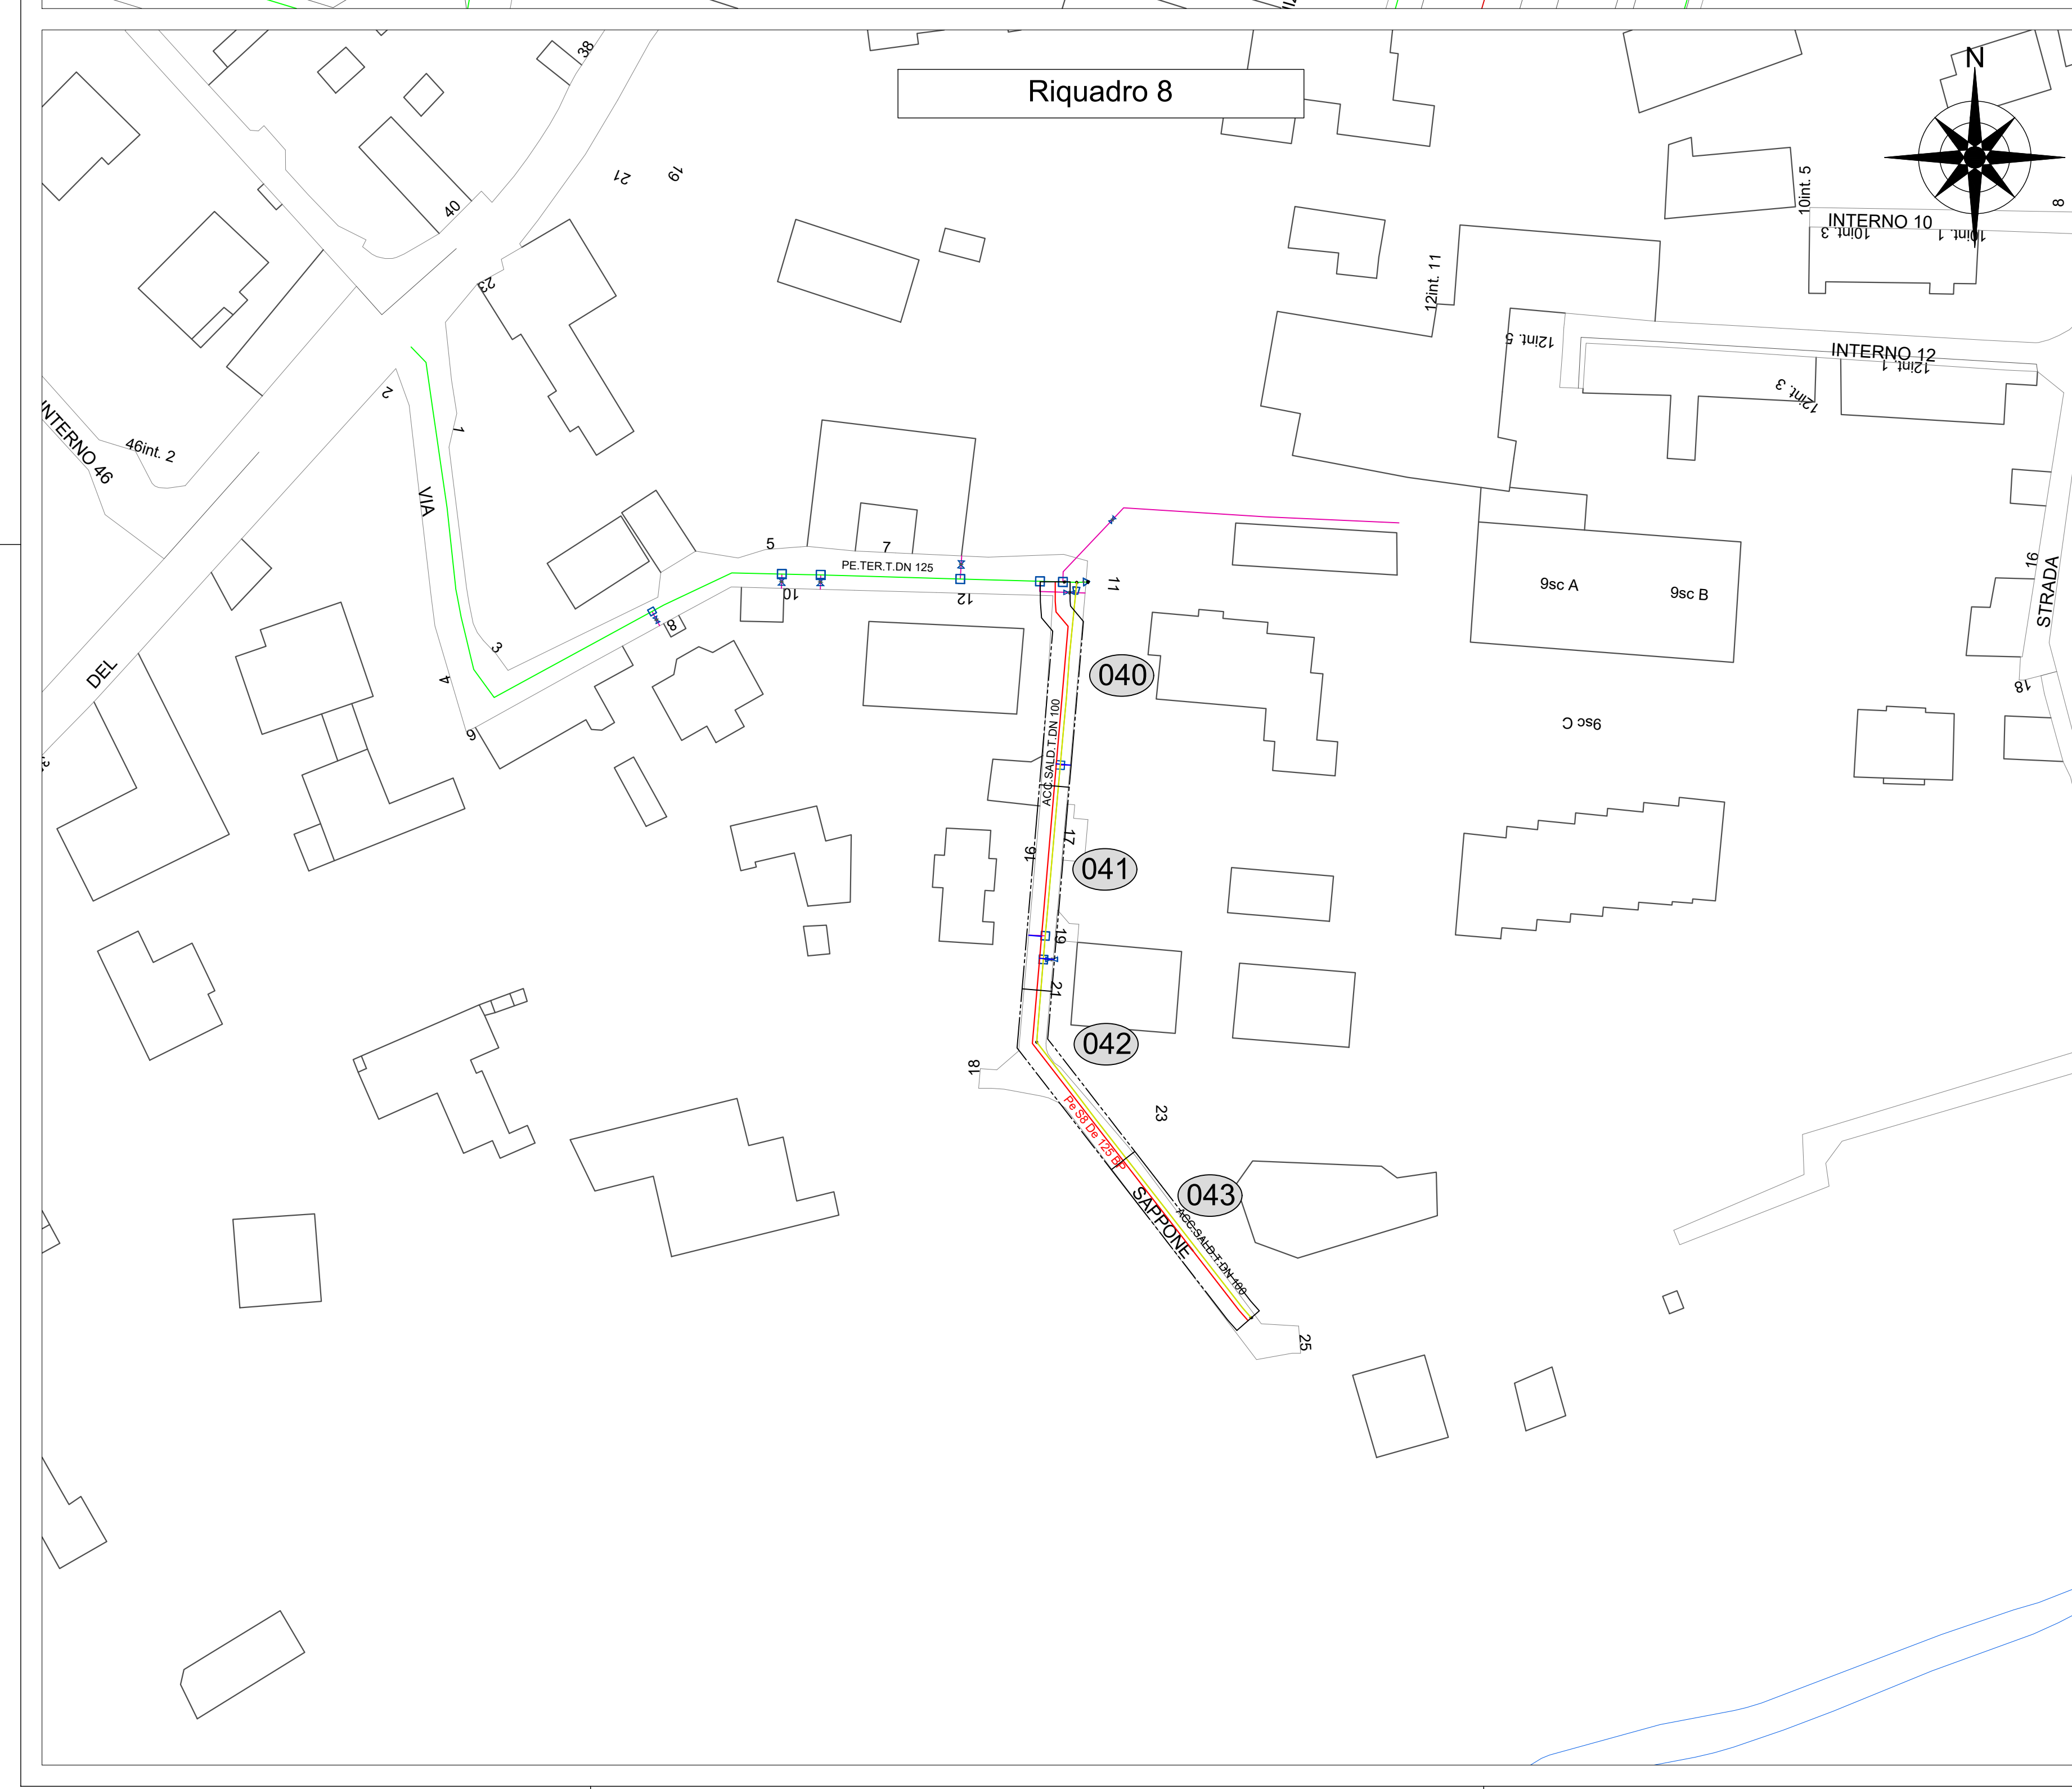

LEARDI

Progettista: Ordine degli Ingegneri di Alessandria

Unità Responsabile della Progettazione: INGEGNERE INGE-PROGRE

Progetto n°: 21-0584-3E-00-001272

WBS: SI.20.10300.02.1109

ALLEGATO n°: 30.3

Formato: A0 Scale 1: 500

Comune di TORINO (TO)




Via Vane

Progetto Esecutivo

SOSTITUZIONE RETE BP (L=2745,39 M) - GARA TO 1

Intervento n° SI-026213-001272-TSS-TORINO08

Planimetria zone sensibili - Tavola 3

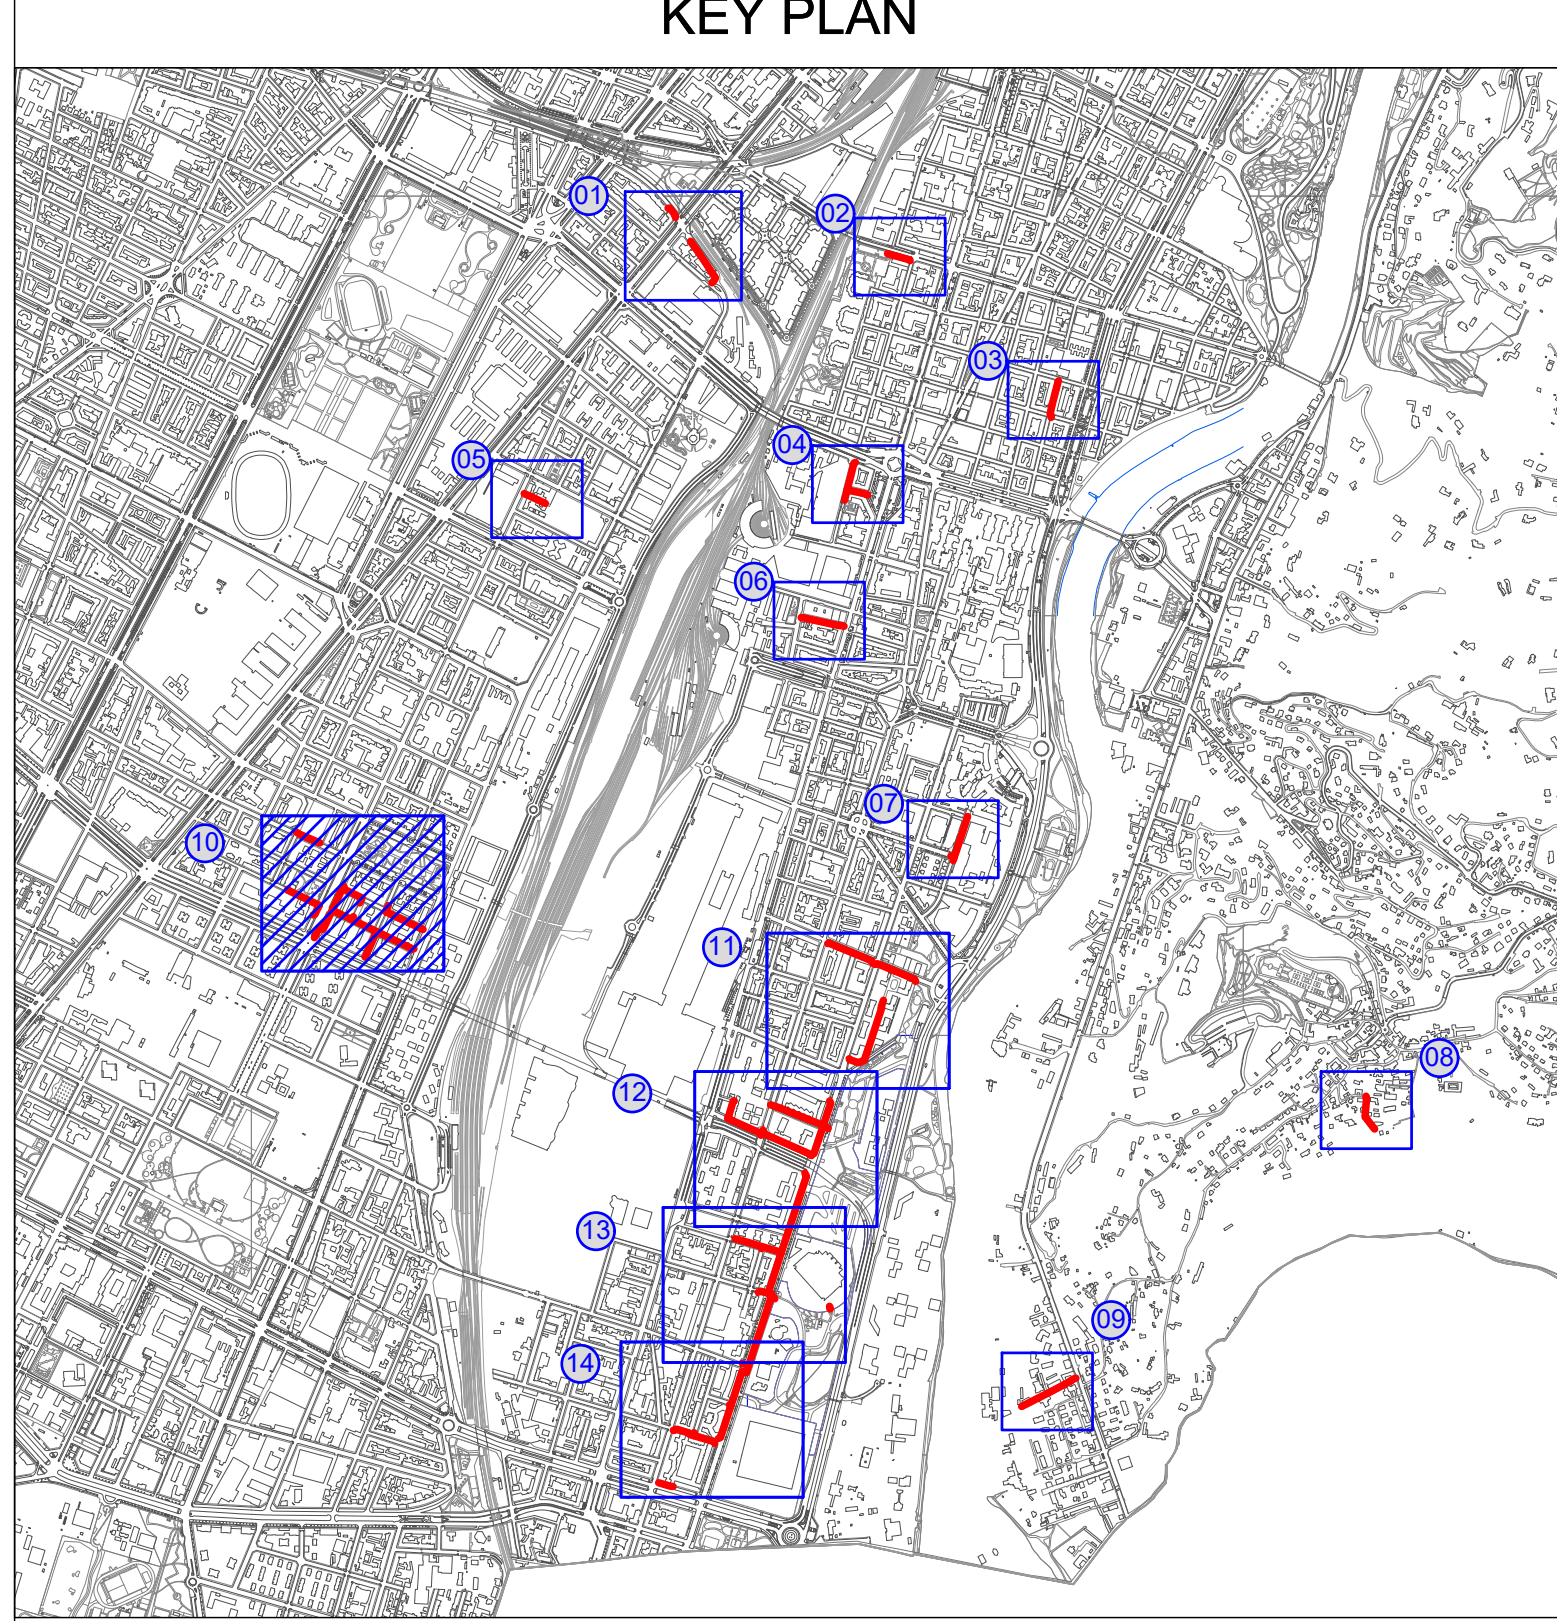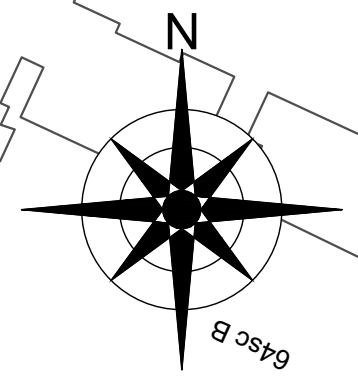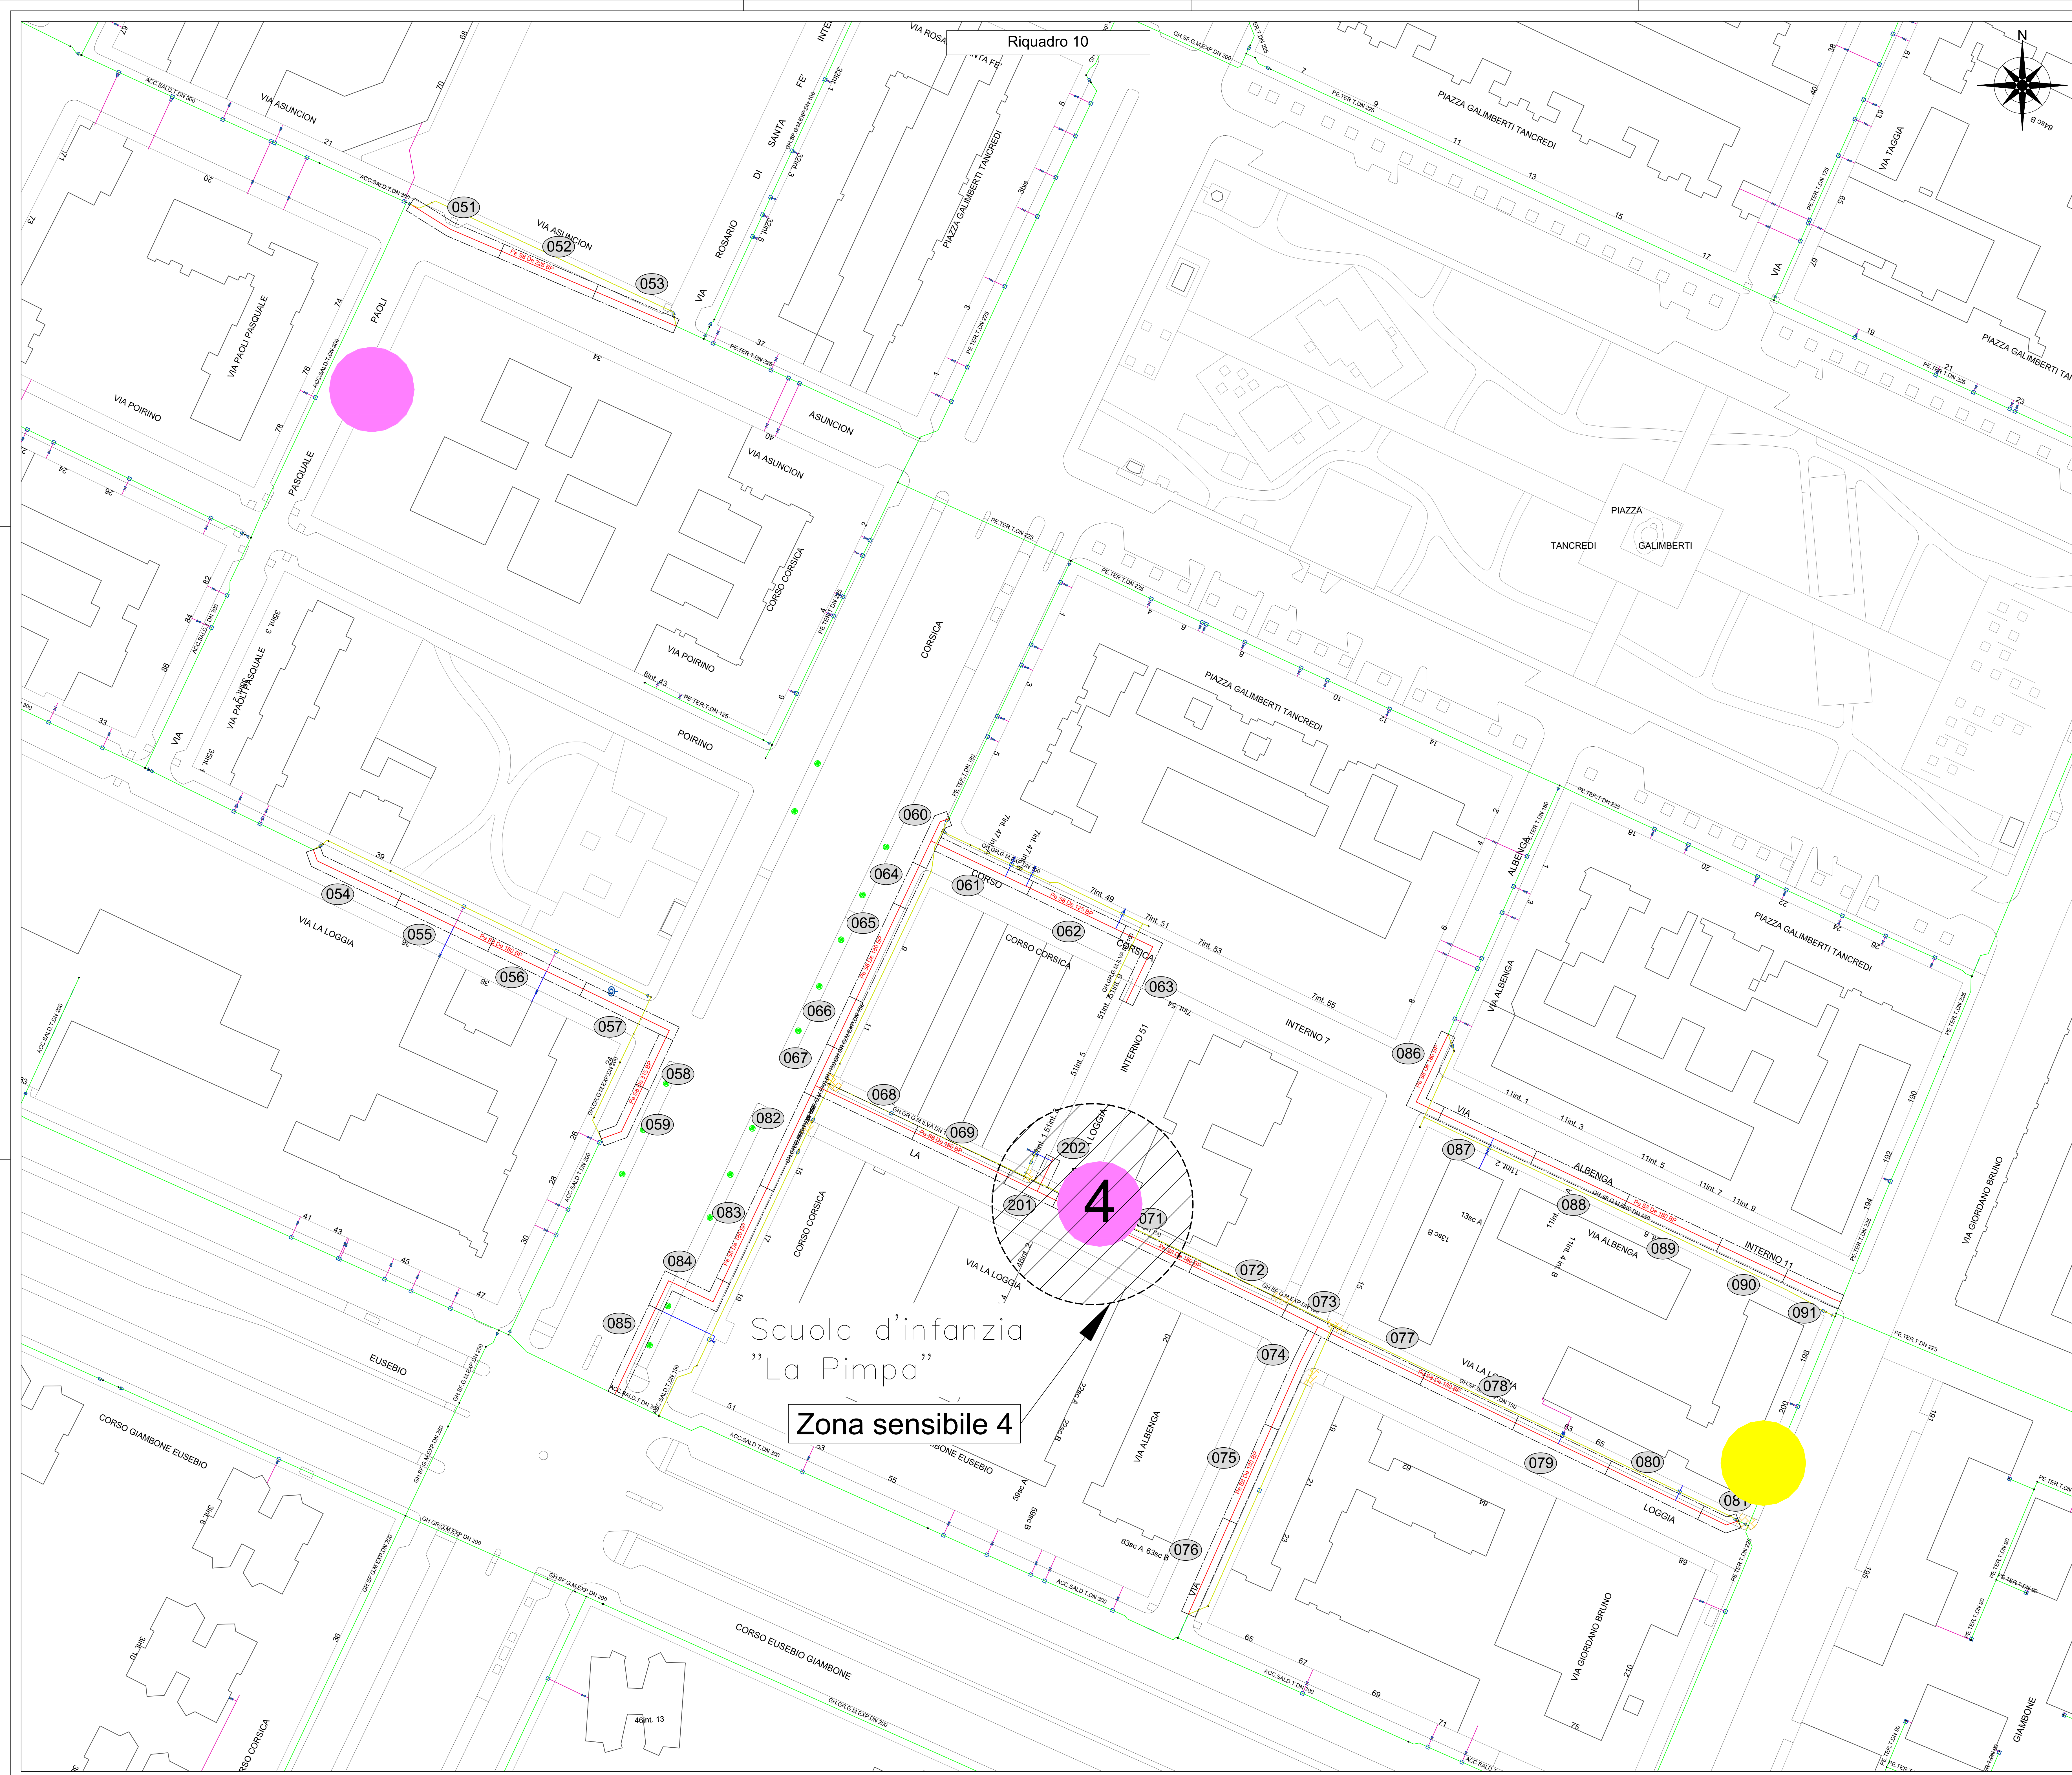

LEGENDA

- Rete nuova

Rete da rimuovere

Metro

Scuole

GTT stop

Musei

Università

Biblioteche

Uffici postali

Impianti Sportivi
- Chiese

Carabinieri

Vigili del fuoco

Cimiteri

Polizia municipale

Ospedali

Stazioni ferroviarie

Altri luoghi di culto

Zona sensibile

Aree di lavoro

Zone sensibili			
Zona di lavoro	Zona sensibile	Definizione	Nota
019-071-020-022	4	Via La Loggia	Strada d'incrocio "La Pimpa"

Planificare le attività di cantiere fuori dall'orario scolastico

LEARDI

Progetto n°:
21-0564-3E-00-00/1272
WBS:
SI.20.10300.02.1109
ALLEGATO n°:
30.4

Formato: A0
Scale: 1:500

Comune di
TORINO (TO)
Via Vane
Progetto Esecutivo
SOSTITUZIONE RETE BP (L=2745,39 M) - GARA TO 1
Intervento n° SI-026213-001272-TSS-TORINO08
Planimetria zone sensibili - Tavola 4

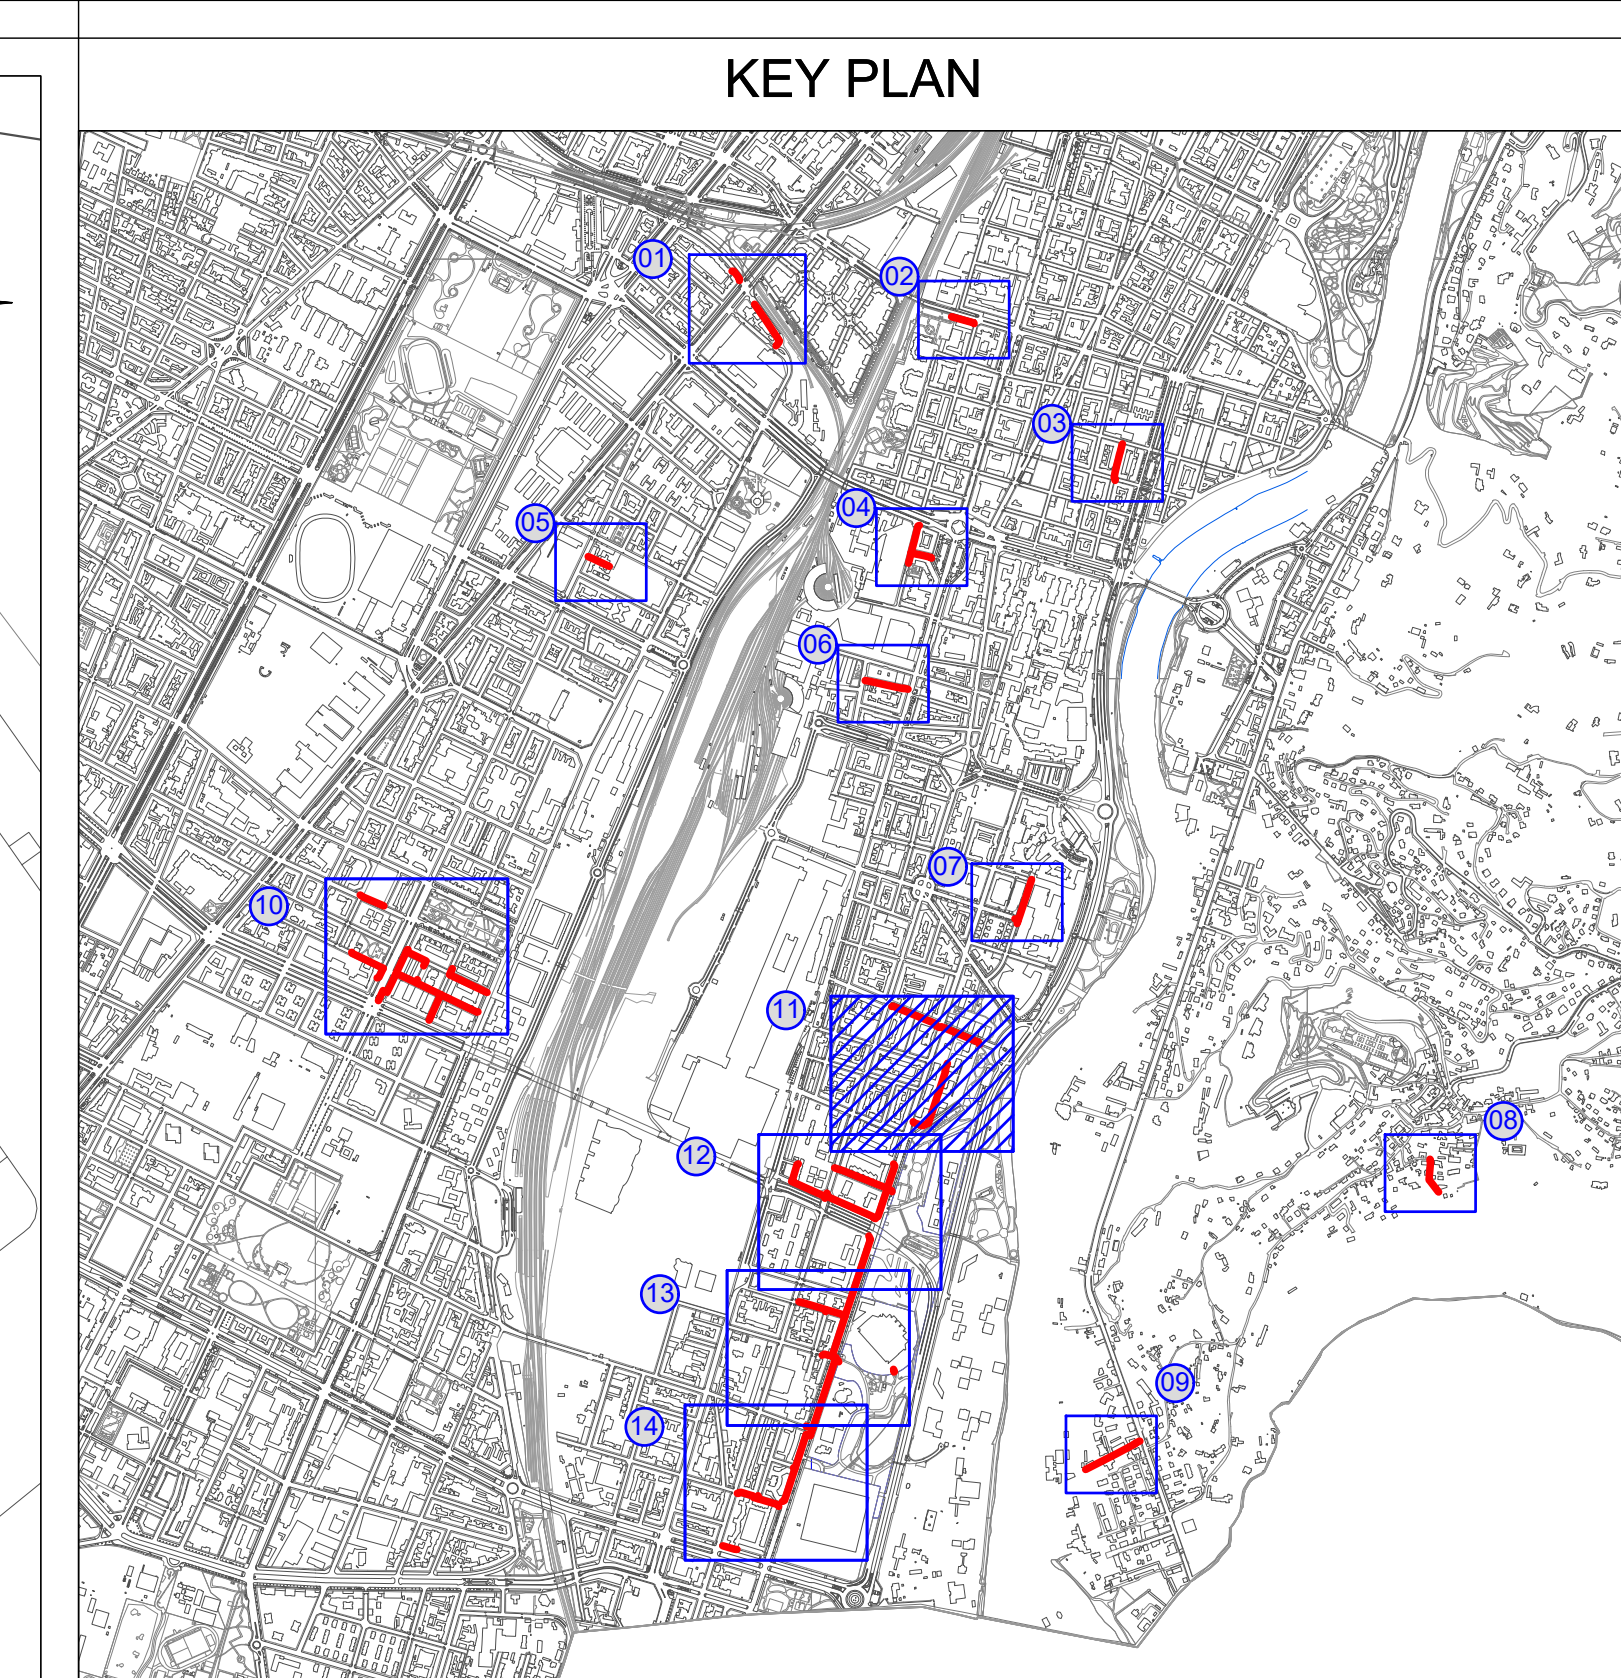

LEGENDA

- | | | | |
|---|-------------------|---|-----------------------|
| | Rete nuova | | Chiese |
| | Rete da rimuovere | | Carabinieri |
| | Metro | | Vigili del fuoco |
| | Scuole | | Cimiteri |
| | GTT stop | | Polizia municipale |
| | Musei | | Ospedali |
| | Università | | Stazioni ferroviarie |
| | Biblioteche | | Altri luoghi di culto |
| | Uffici postali | | Zona sensibile |
| | Impianti Sportivi | | Aree di lavoro |

	Proprietà Ordine n° _____ Indirizzo _____ CAP _____ Città _____ Prov. _____		Unità Responsabile della Progettazione INGEGNERE-INGE-PROGRE														
	Progetto n° _____ 21-06564-3E-00-001272 WBS: SI 00 I0300.02 I109 ALLEGATO n°: 30.5 Nome file cartaceo _____ Formato: A0 Scala 1 : 500 Committente _____																
Descrizione Emisione per commenti Contatti: 2484		<table border="1"> <tr> <td>0</td> <td>30</td> <td>11</td> <td>22</td> <td>L.Offr.</td> <td>L. Caricagna</td> <td>A. Leardi</td> </tr> <tr> <td>Rev.</td> <td>G.</td> <td>M.</td> <td>A.</td> <td>Redatto</td> <td>Controllato</td> <td>Approvato</td> </tr> </table>		0	30	11	22	L.Offr.	L. Caricagna	A. Leardi	Rev.	G.	M.	A.	Redatto	Controllato	Approvato
0	30	11	22	L.Offr.	L. Caricagna	A. Leardi											
Rev.	G.	M.	A.	Redatto	Controllato	Approvato											
		Comune di TORINO (TO) Via Varie Progetto Esecutivo SOSTITUZIONE RETE RP (L-2745, 30 ML - GARA TO 1 Intervento n° SI-0362-03-001272-ISS-TORIN008 Pianimetria zona sensibile - Tavola 5															

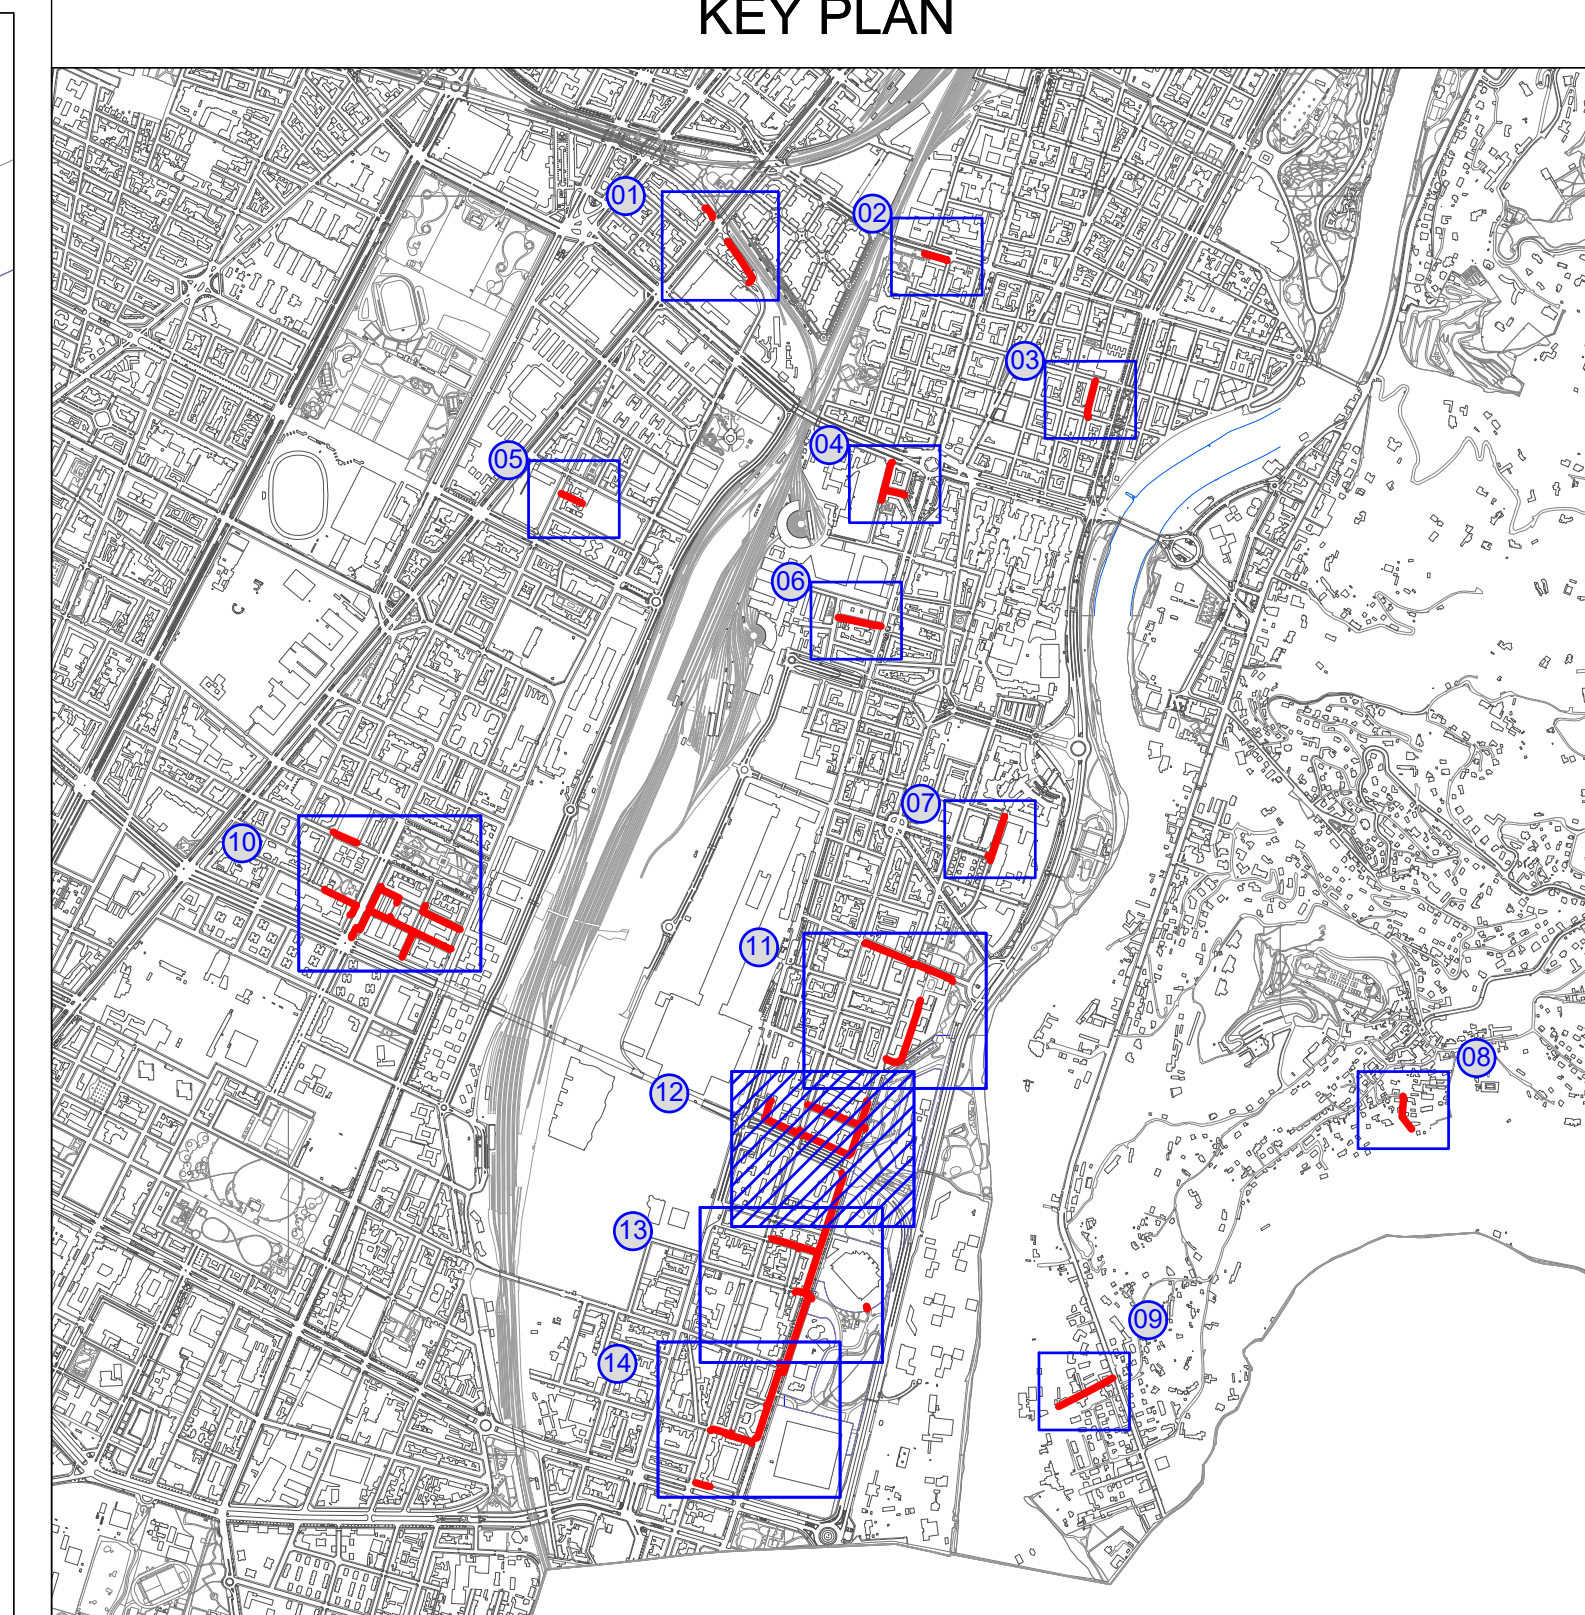

	Rete nuova		Chiese
	Rete da rimuovere		Carabinieri
	Metro		Vigili del fuoco
	Scuole		Cimiteri
	GTT stop		Polizia municipale
	Musei		Ospedali
	Università		Stazioni ferroviarie
	Biblioteche		Altri luoghi di culto
	Uffici postali		Zona sensibile
	Impianti Sportivi		Aree di lavoro

Zone sensibili				
Zona di lavoro	Zona sensibile	Via/Strada/Piazza	Dettaglio	Nota
136-137-138	5	Corso Caduti sul Lavoro	Scuola Materna Municipale	Pianificare le attività di cantiere i fuori dall'orario scolastico
130-131-132	6	Corso Caduti sul Lavoro	Liceo delle Scienze e Umane Regina Margherita	Pianificare le attività di cantiere i fuori dall'orario scolastico
124-125	7	Via Ventimiglia	GTT Stop 2254	Richiedere lo spostamento della fermata prima o dopo il punto di interferenza
142-143-144	8	Via Ventimiglia	I.C. Rignon-Re Umberto I	Pianificare le attività di cantiere i fuori dall'orario scolastico

Scuola Materna
Municipale

Liceo delle
Scienze Umane
Regina Margherita

I.C. Peyron-Re Umberto I

GTT Stop 2254

	Rete nuova		Chiese
	Rete da rimuovere		Carabinieri
	Metro		Vigili del fuoco
	Scuole		Cimiteri
	GTT stop		Polizia municipale
	Musei		Ospedali
	Università		Stazioni ferroviarie
	Biblioteche		Altri luoghi di culto
	Uffici postali		Zona sensibile
	Impianti Sportivi		Aree di lavoro

LEARDI

Progettista

ALTEA

Ordine degli Ingegneri e Architetti

numero 1101

Pavia

Unità Responsabile della Progettazione

INGENER-INGE-PROGRE

Progetto n°:

21-0584-3E-00-001272

WBS:

SI-20-03000-02-1109

ALLEGATO n°:

30.7

Nome FIR: ALTEA

Formato: A0

Scala 1 : 500

Committenza

0

30

11

22

L.Olivri

L.Cattaneo

A.Leardi

Comm.: 2484

Rev. G. M. A.

Redatto

Controllato

Approvato

Comune di

TORINO (TO)



Via Vire

Progetto Esecutivo

SOSTITUZIONE RETE BP (L-2745-39 M) - GARA TO 1

Intervento n° SI-0300-15-001272-15S-TORIN008

Pianimetria zone sensibili - Tavola 7

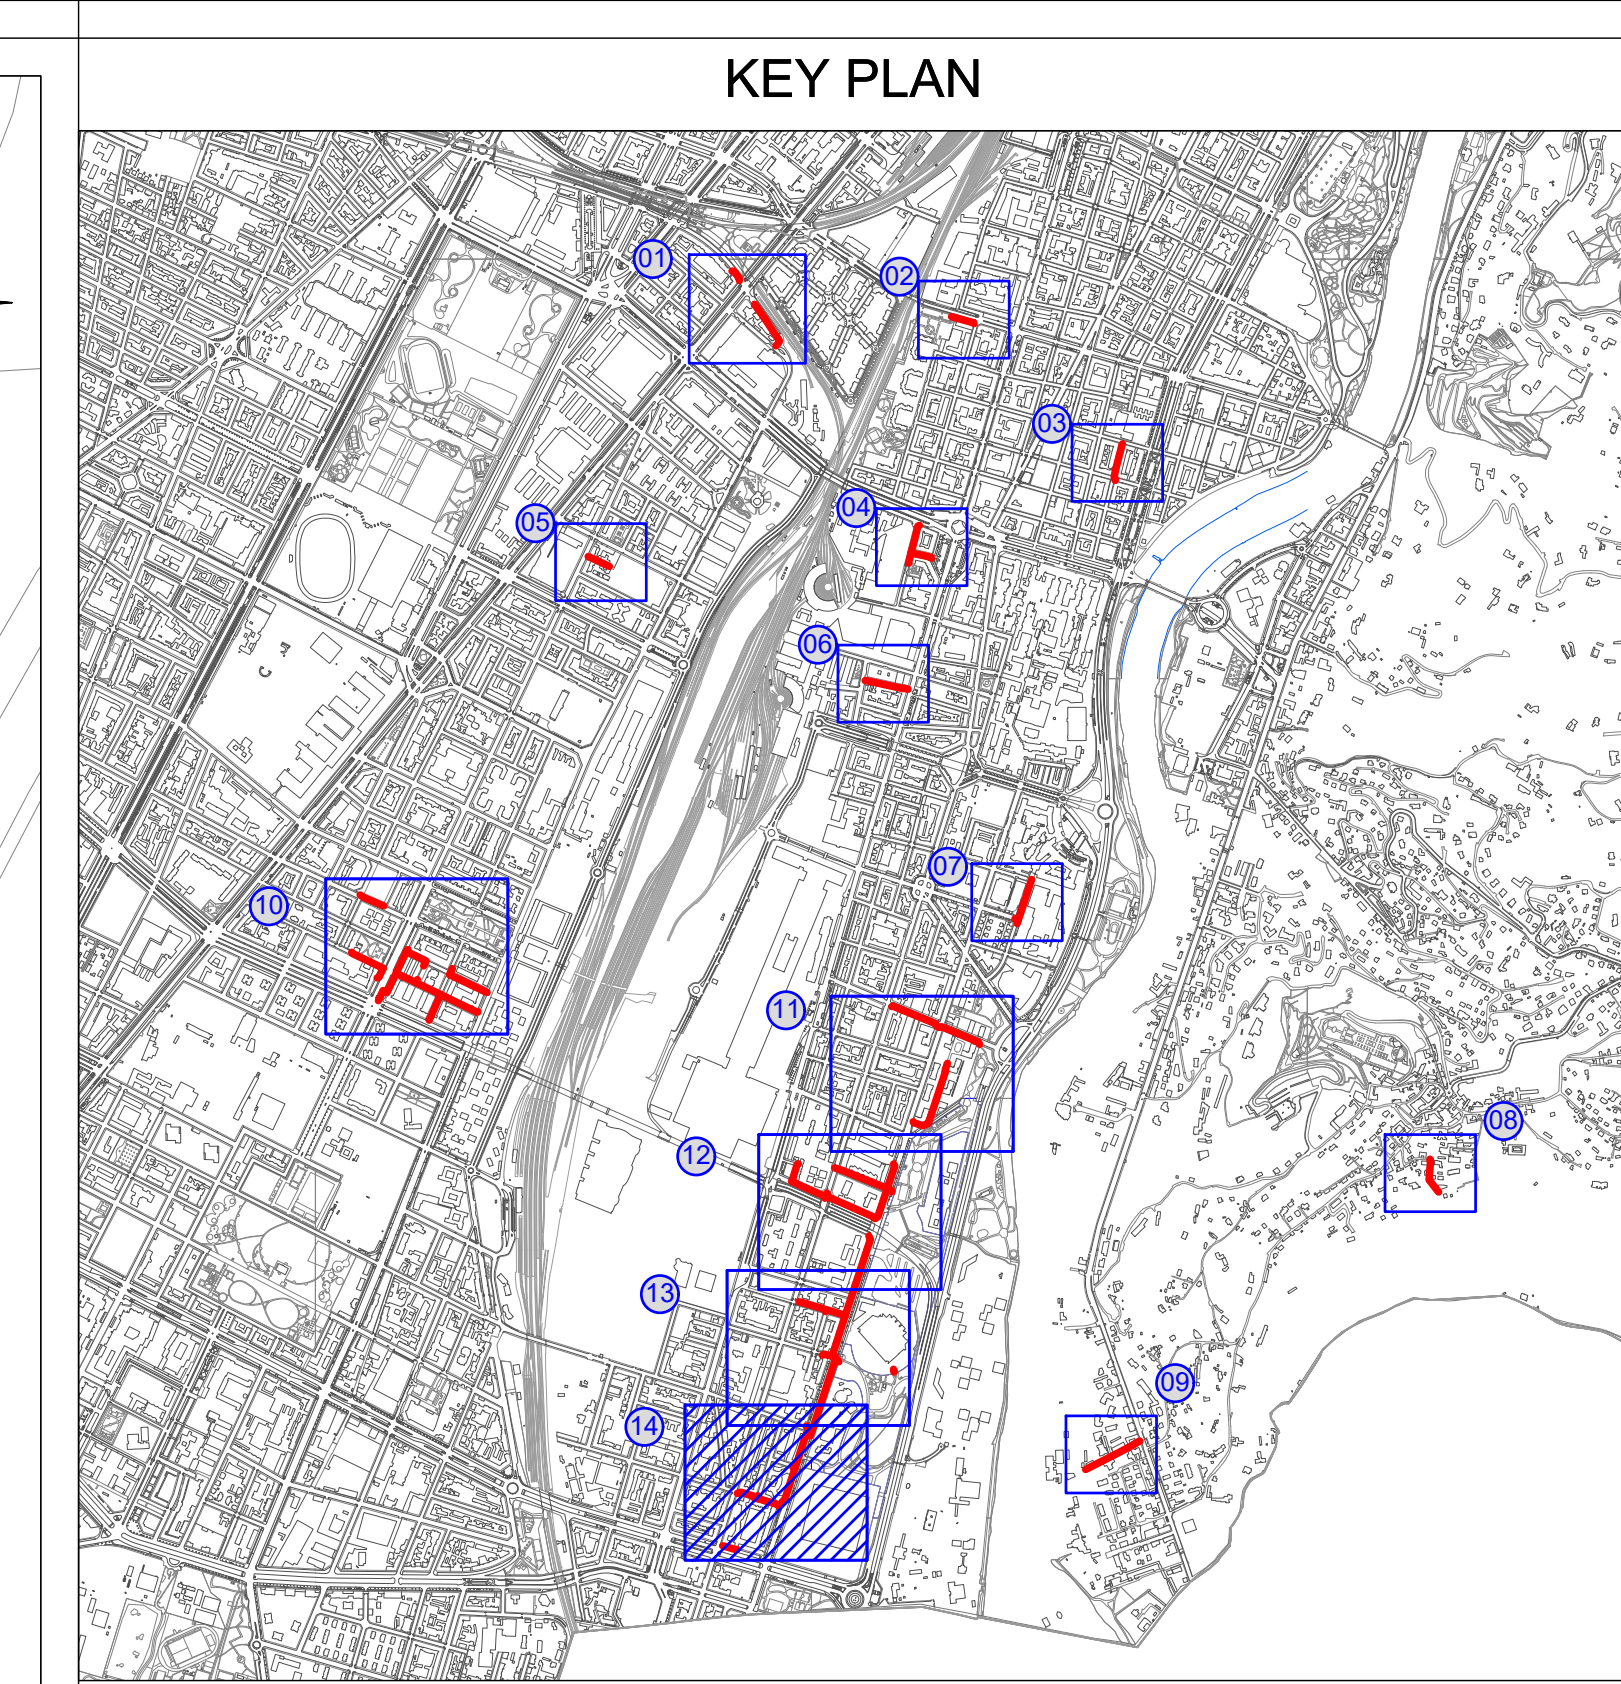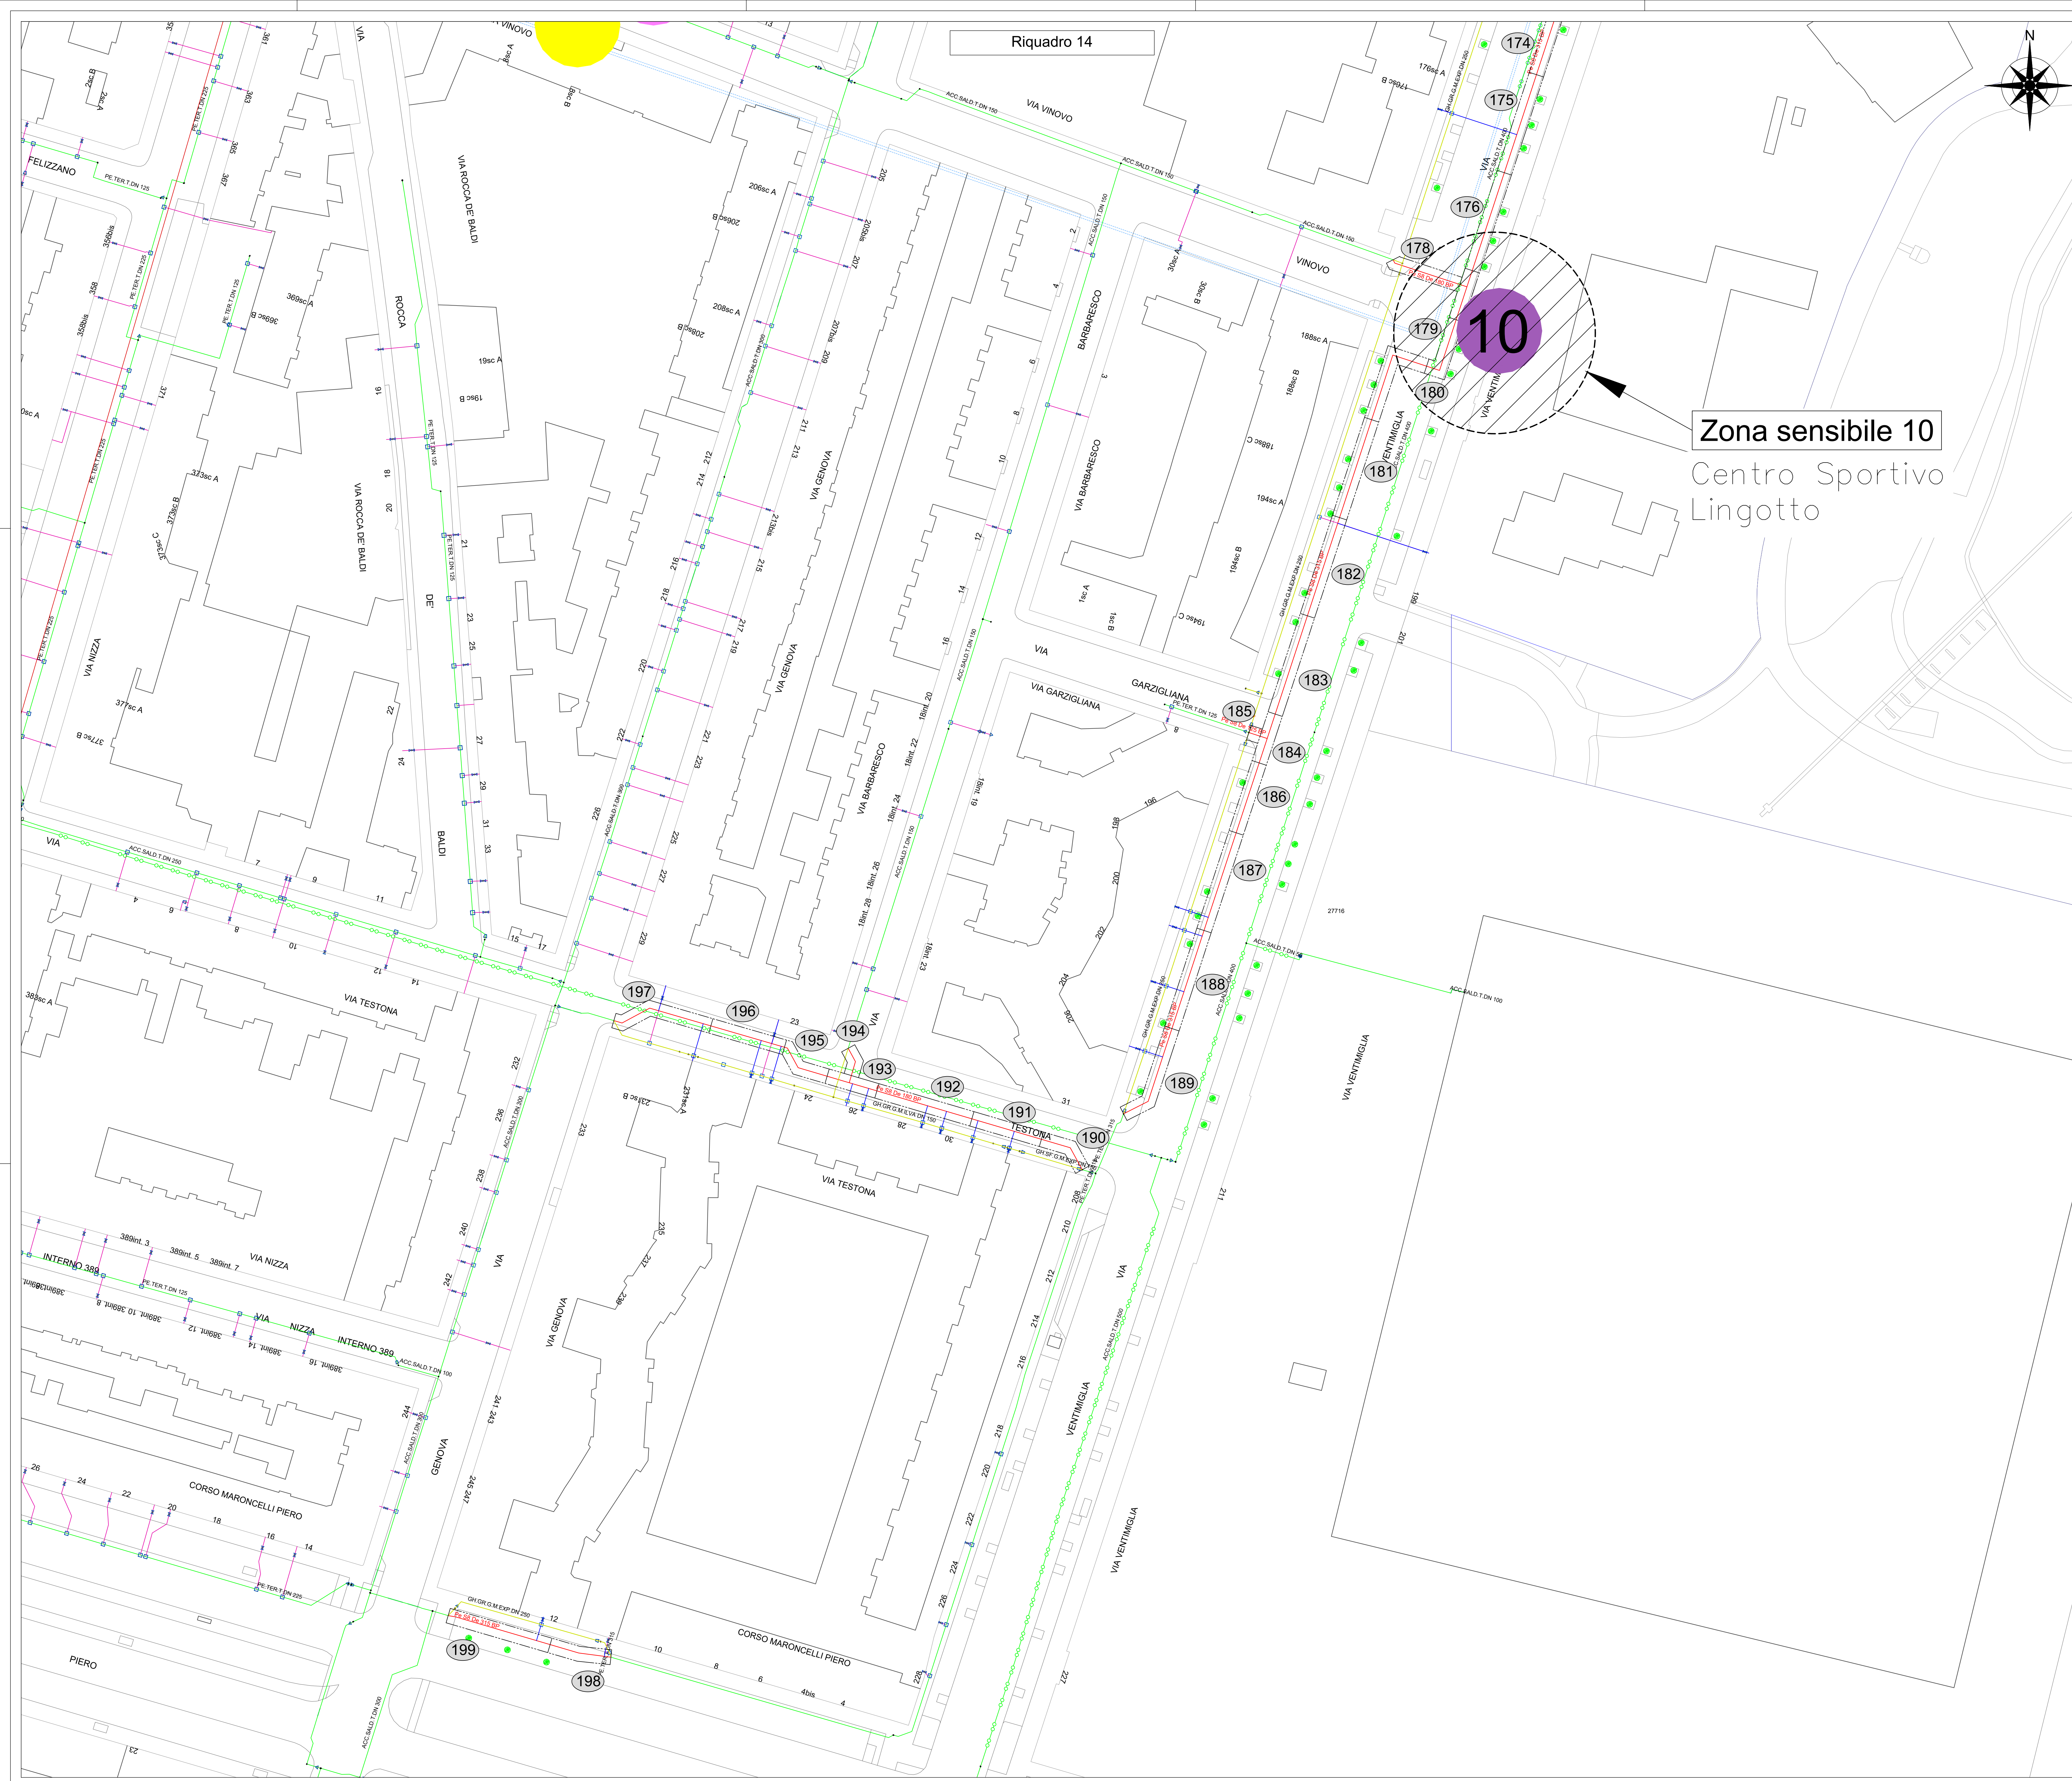

Zona sensibile			
Zona di lavoro	Zona sensibile	Dettaglio	Nota
176-177-178-179-180	10	Via Ventrone	Centro Sportivo Lingotto

Planificare le attività di cantiere fuori dall'orario degli eventi

LEARDI

Progetto n°:
21-0584-3E-00-001272
WBS:
SI.20.10300.02.1109
ALLEGATO n°: 30.8
Formato: A0
Comm: 2484

Comune di TORINO (TO)
Via Vane
Progetto Esecutivo
SOSTITUZIONE RETE BP (L=2745,39 M) - GARA TO 1
Intervento n° SI-026213-001272-TSS-TORIN008
Planimetria zone sensibili - Tavola 8

INGEGNERI PROV. ALBA
ING. G. M. A.
ING. G. M. A.
ING. G. M. A.
ING. G. M. A.

Unità Responsabile della Progettazione
INGREAL-INGE-PROGRE

Progetto n°:
21-0584-3E-00-001272
WBS:
SI.20.10300.02.1109
ALLEGATO n°: 30.8
Formato: A0
Comm: 2484

Comune di TORINO (TO)
Via Vane
Progetto Esecutivo
SOSTITUZIONE RETE BP (L=2745,39 M) - GARA TO 1
Intervento n° SI-026213-001272-TSS-TORIN008
Planimetria zone sensibili - Tavola 8

Il presente elaborato è di proprietà aziendale - La società tutela i propri diritti a termini di legge.