


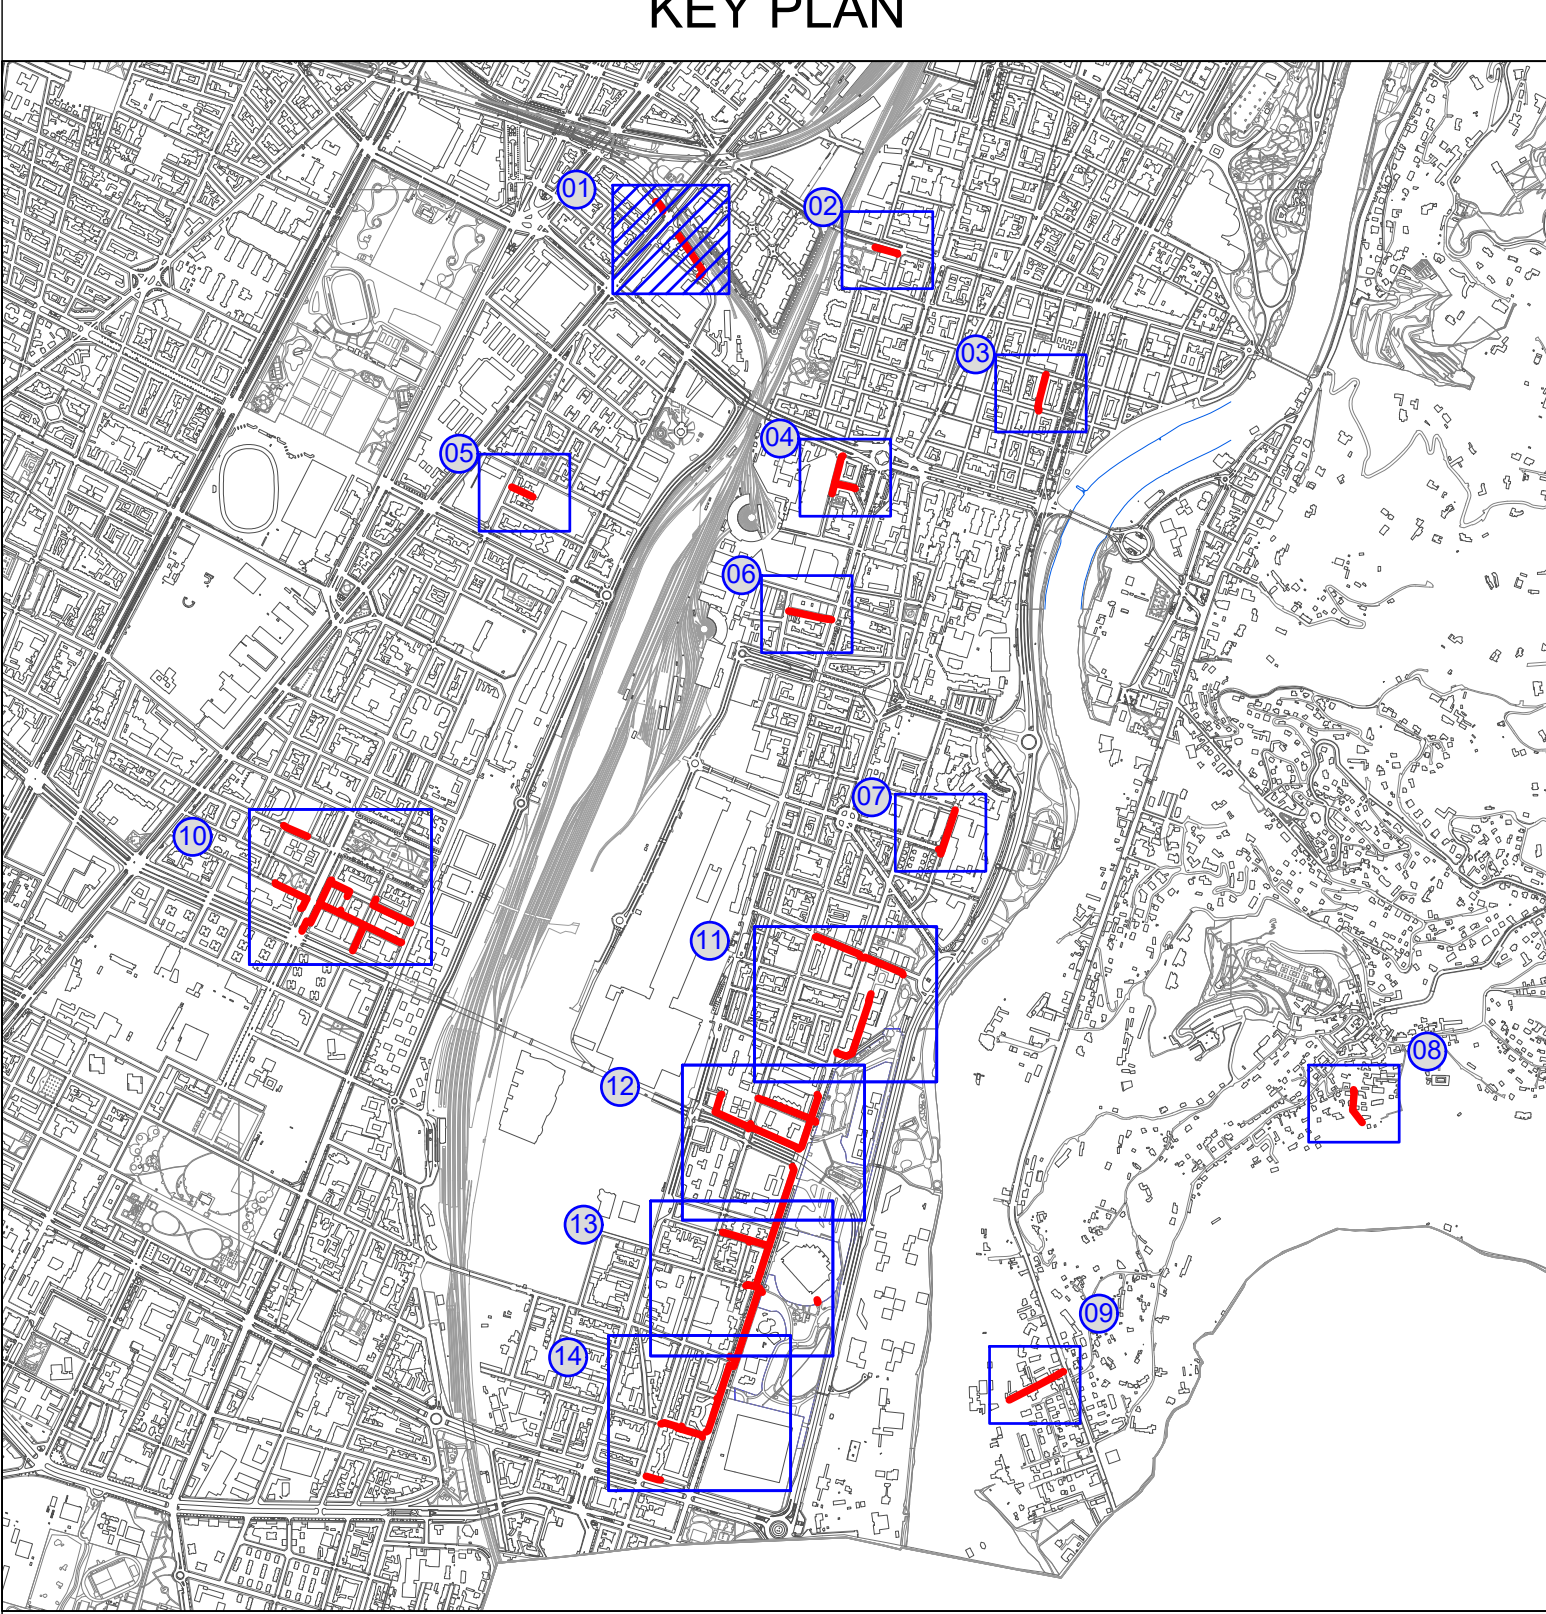

LEGENDA

	Rete in progetto BP		n° Zona di lavoro
	Rete in dismissione BP		Asfalto
	Zona di lavoro		Sterrato/area verde
			Autobloccanti/ammattionato

Zone di lavoro e pavimentazioni				
n.	dati condotta	quantità [m]	lato strada	tipo di pavimentazione
1	Pe De 180	24	Sinistra	Asfalto
2	Pe De 180	4	Sinistra	Autobloccanti
2	Pe De 180	5	Attraversamento	Asfalto
3	Pe De 125	24	Destra	Asfalto
4	Pe De 125	24	Destra	Asfalto
5	Pe De 125	24	Destra	Asfalto
6	Pe De 125	24	Destra	Asfalto
7	Pe De 125	20	Destra	Asfalto
8	Pe De 125	17	Destra	Asfalto

tratto di condotta da posare a maggiore profondità per presenza teleriscaldamento

LEARDI

Progettista:

Unità Responsabile della Progettazione

INGEREAL-INGE-PROGRE

Progetto n°: 21-0564-3E-00-001272
WBS: SI.20.10300.02.1109
ALLEGATO n°: 4.1

Descrizione:

Nome File: 04.1.png



Formato: A1 Scala 1 : 500

Committente:

Comune di TORINO (TO)
Vie Varie
Progetto Esecutivo
SOSTITUZIONE RETE BP (L=2745.39 M) - GARA TO 1
Intervento n° SI-036213-001272-TSS-TORIN008
Planimetria pavimentazioni e zone di lavoro - Tavola 1

0	30	11	22	A.Saronni	L.Cartasegna	A.Leardi
Rev.	G.	M.	A.	Redatto	Controllato	Approvato

Il presente elaborato è di proprietà aziendale - La società tutelerà i propri diritti a termini di legge.

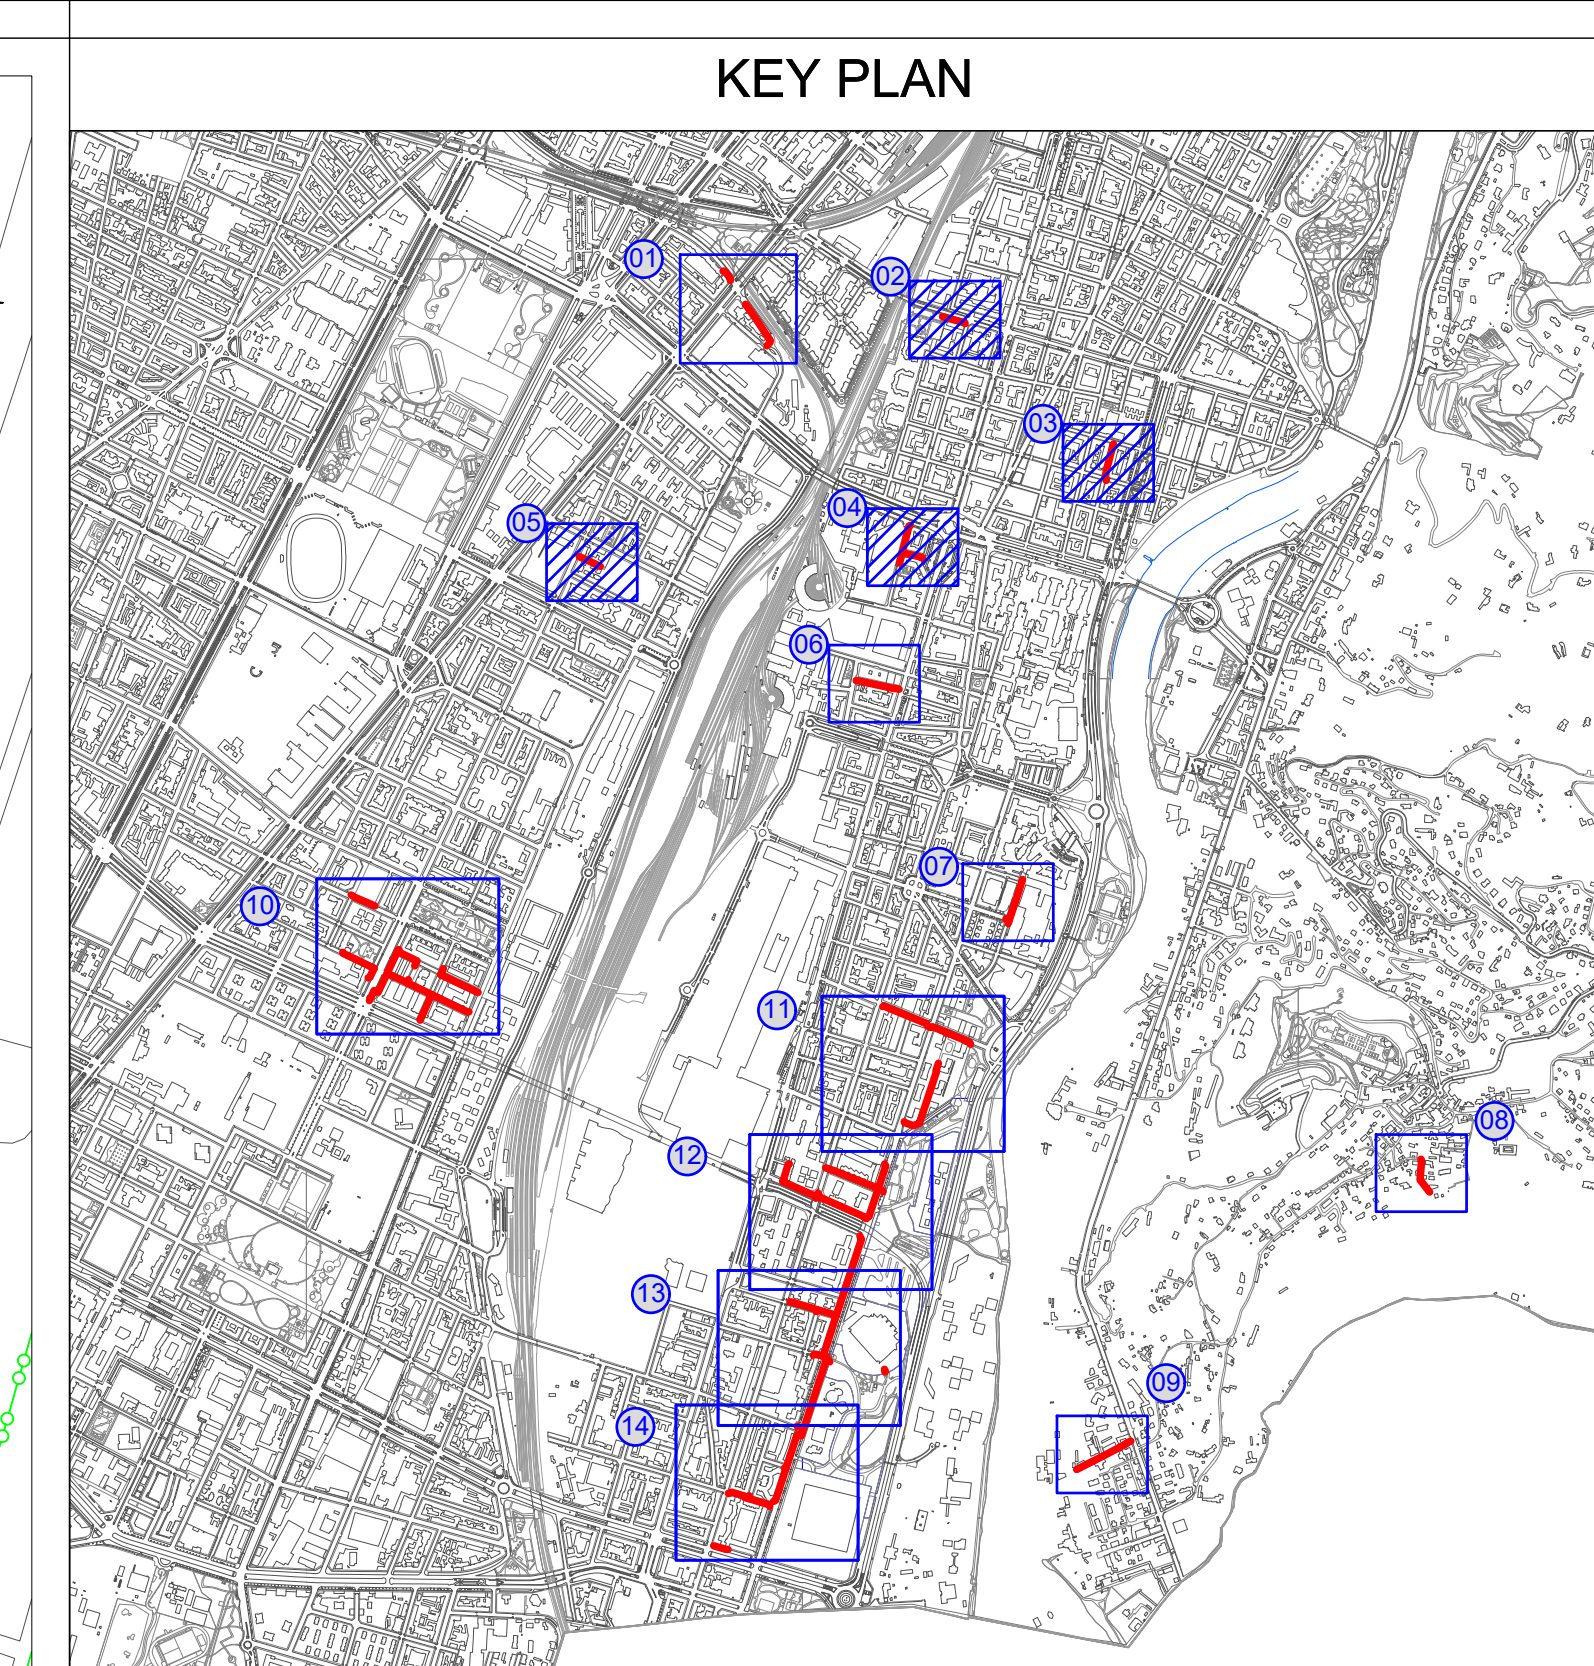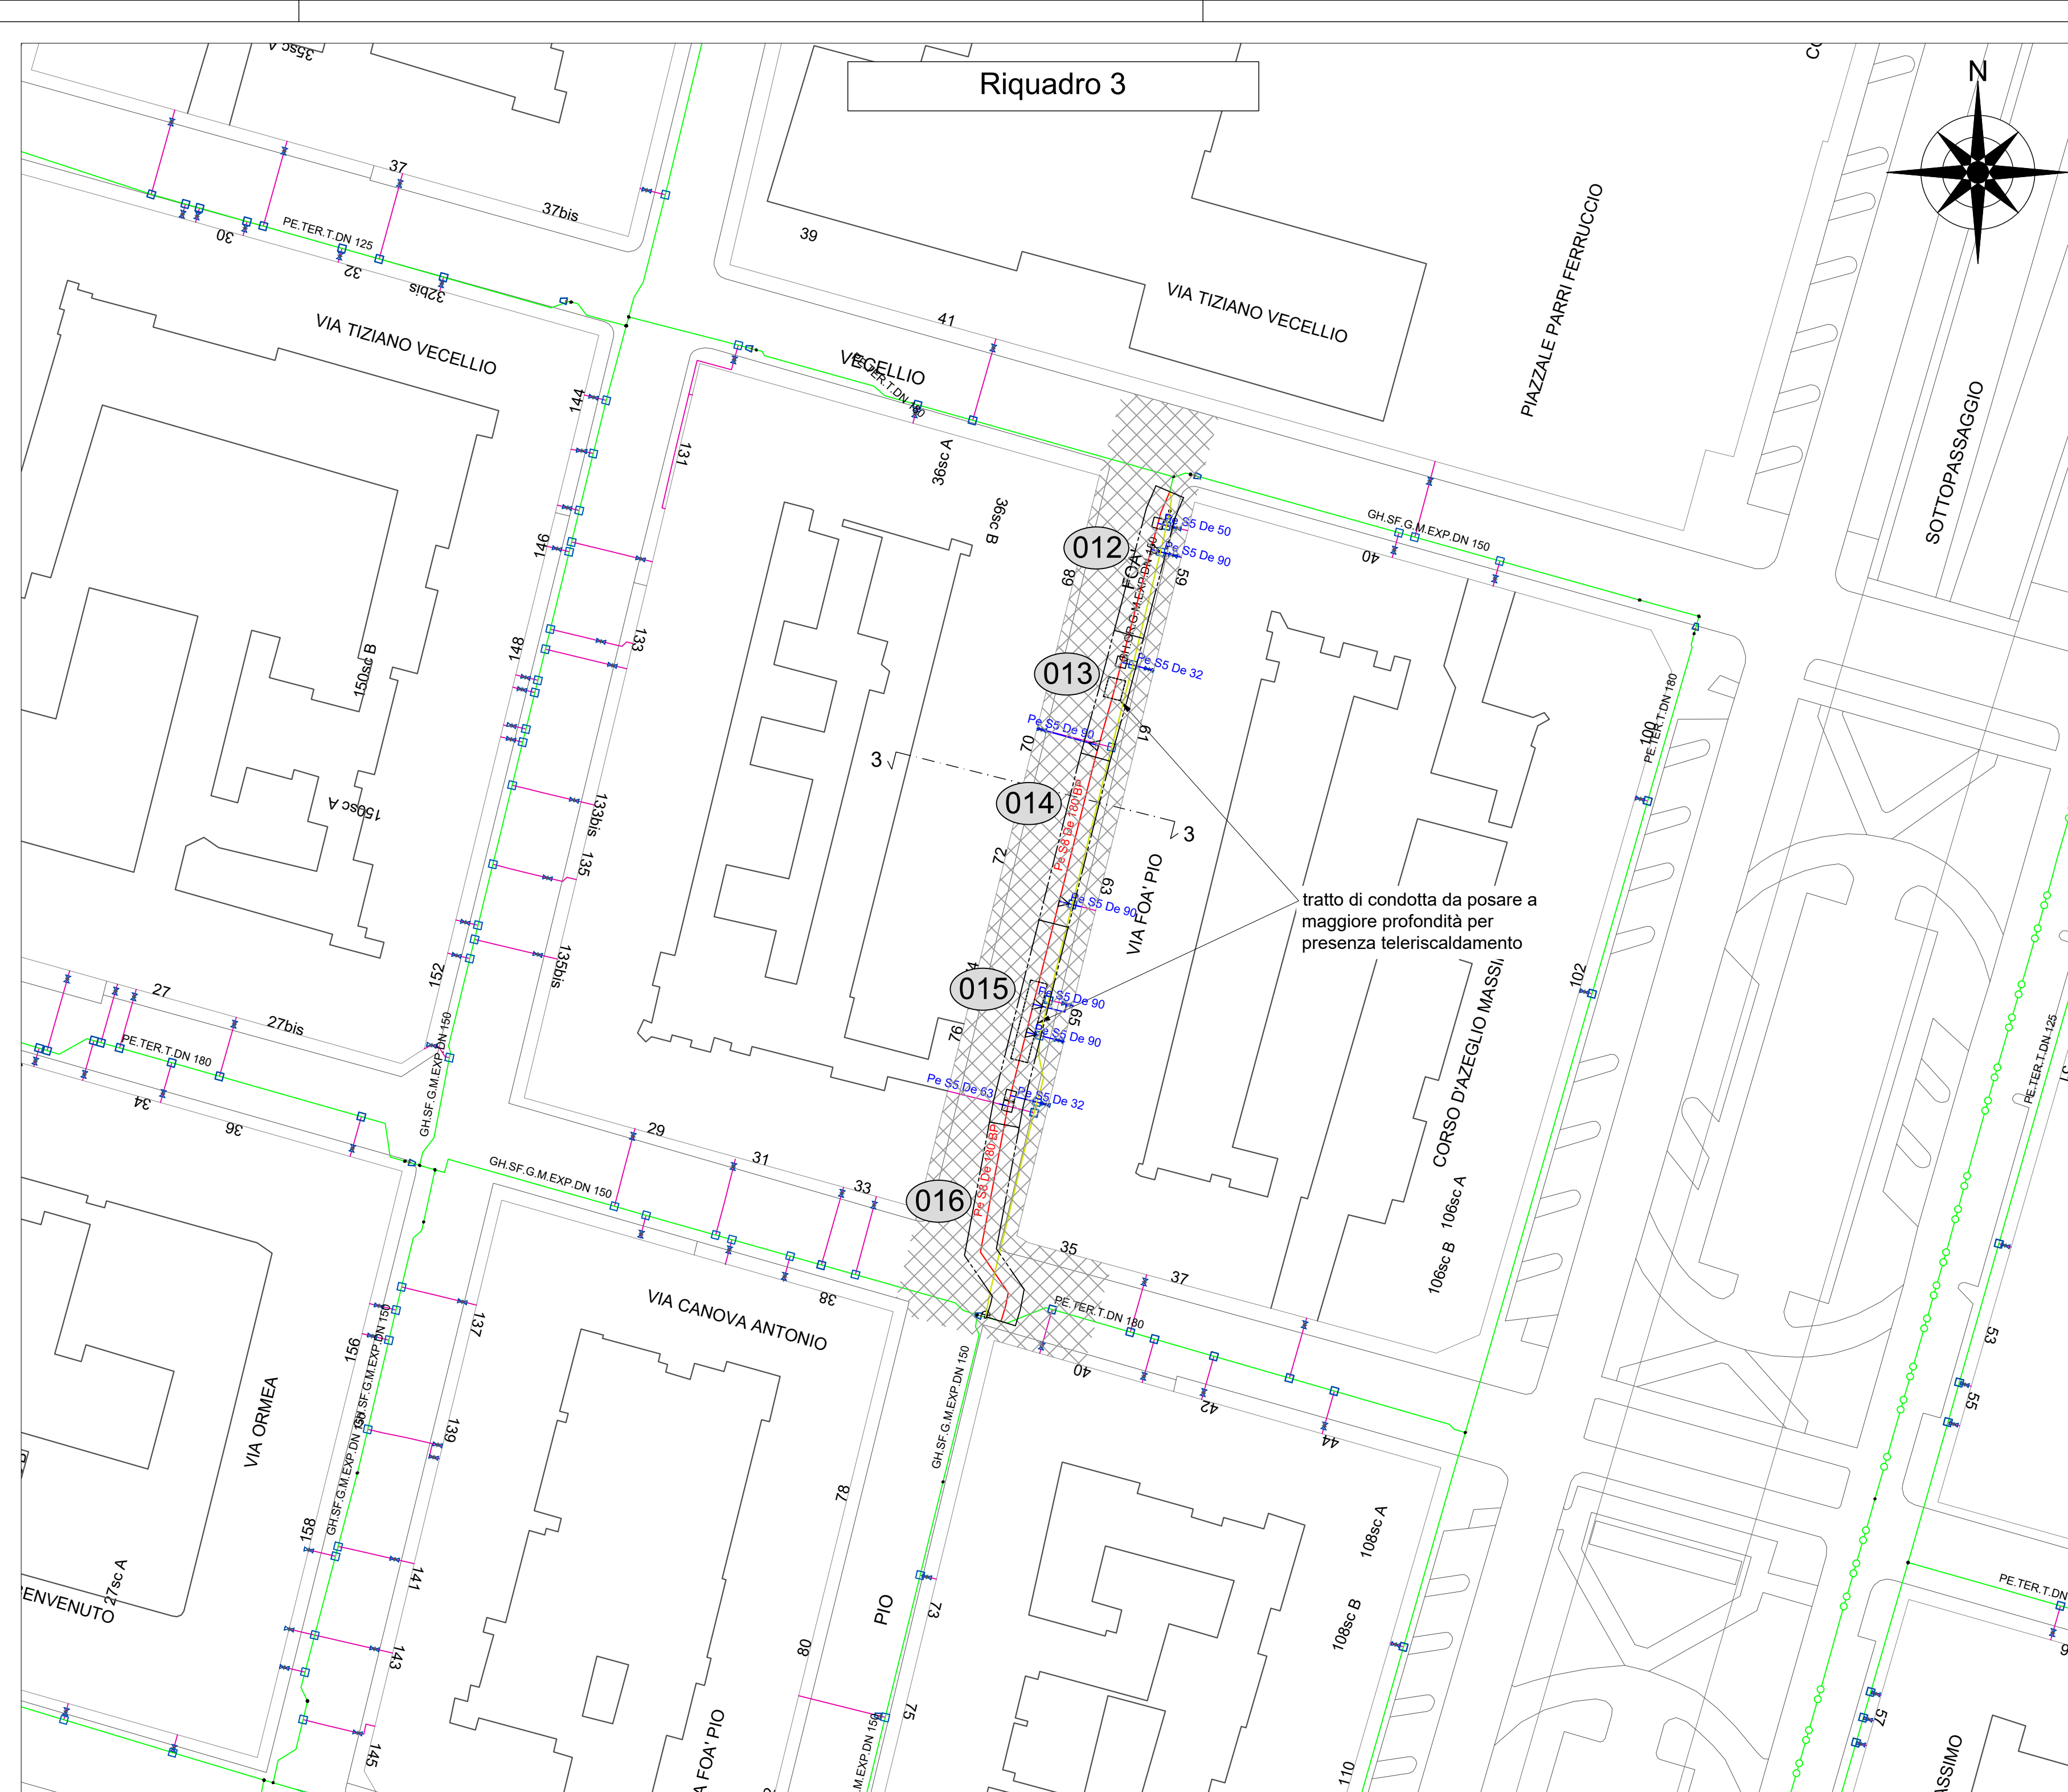

LEGENDA





	Rete in progetto BP		n° Zona di lavoro
	Rete in dismissione BP		Asfalto
	Zona di lavoro		Sterrato/area verde
			Autobloccanti/ammattonato

Zone di lavoro e pavimentazioni (Riquadro 2)				
n.	dati condotta	quantità [m]	lato strada	tipo di pavimentazione
9	Pe De 125	24	Destra	Asfalto
10	Pe De 125	24	Destra	Asfalto
11	Pe De 125	15	Destra	Asfalto

Zone di lavoro e pavimentazioni (Riquadro 3)				
n	dati condotta	quantità [m]	lato strada	tipo di pavimentazione
12	Pe De 180	18	Sinistra	Asfalto
13	Pe De 180	14	Sinistra	Asfalto
14	Pe De 180	20	Sinistra	Asfalto
15	Pe De 180	24	Sinistra	Asfalto
16	Pe De 180	15	Sinistra	Asfalto
16	Pe De 180	9	Attraversamento	Asfalto

Zone di lavoro e pavimentazioni (Riquadro 4)				
n	dati condotta	quantità [m]	lato strada	tipo di pavimentazione
17	Pe De 180	18	Sinistra	Asfalto
18	Pe De 180	24	Sinistra	Asfalto
19	Pe De 180	24	Sinistra	Asfalto
20	Pe De 180	2	Attraversamento	Asfalto
20	Pe De 125	4		Asfalto
20	Pe De 180	10	Sinistra	Asfalto
21	Pe De 180	24	Destra	Asfalto
22	Pe De 180	12	Destra	Asfalto
23	Pe De 180	18	Destra	Asfalto
24	Pe De 125	24	Sinistra	Asfalto

Zone di lavoro e pavimentazioni (Riquadro 5)				
n.	dal condotta	quantità [m]	lato strada	tipo di pavimentazione
25	Pe De 125	24	Destra	Asfalto
26	Pe De 125	24	Destra	Asfalto
27	Pe De 125	14	Destra	Asfalto

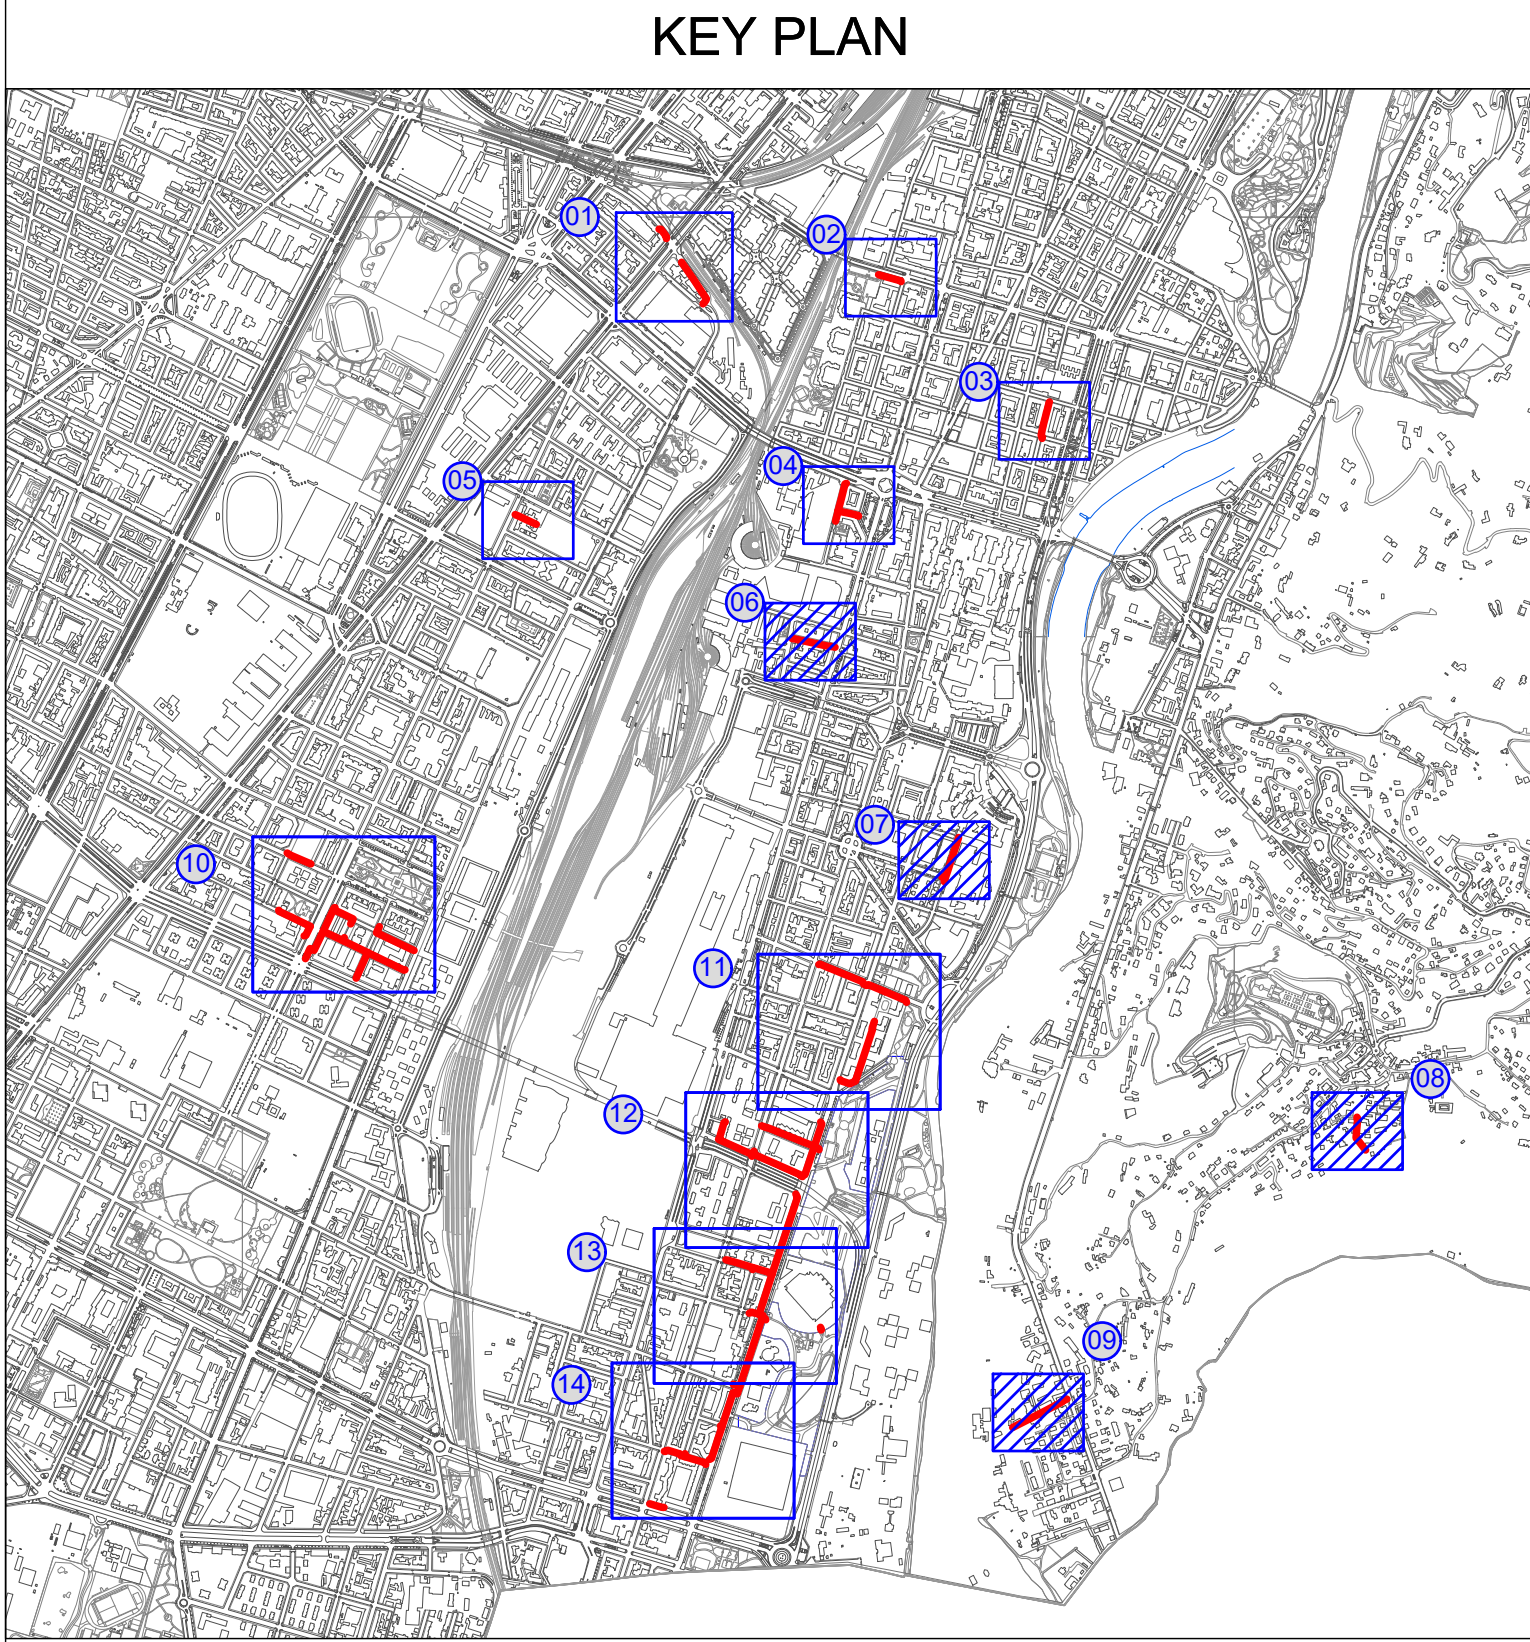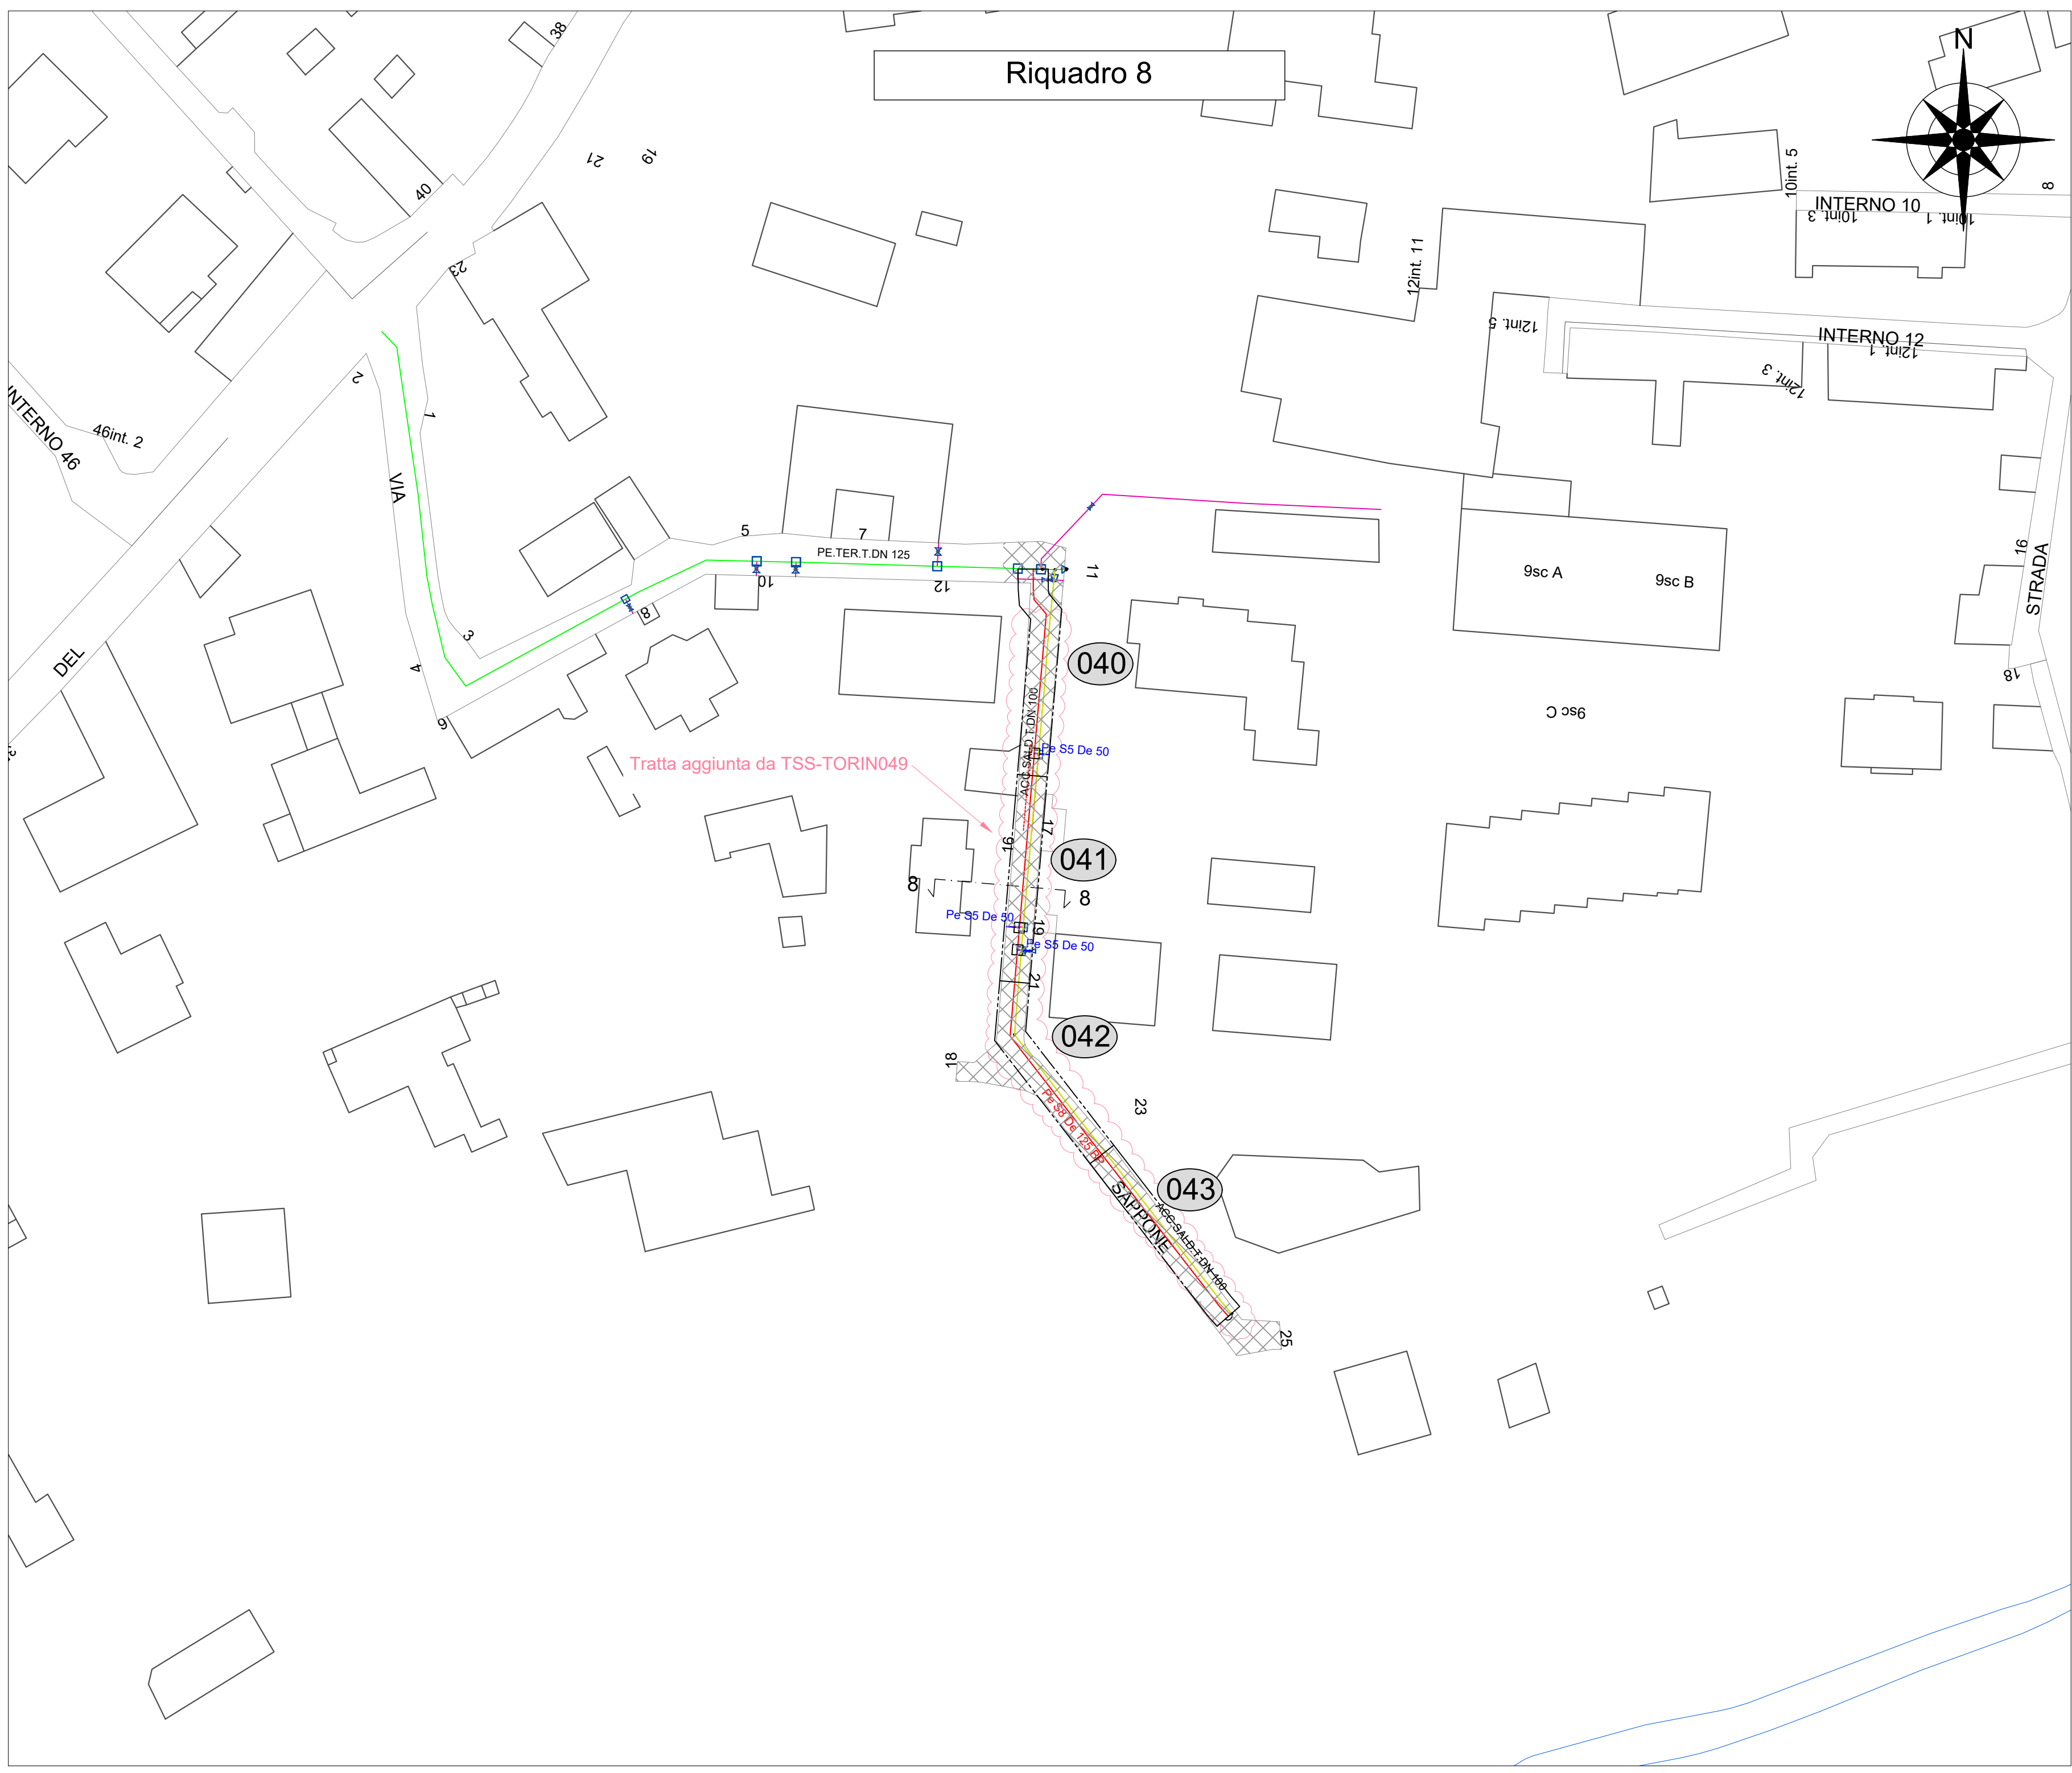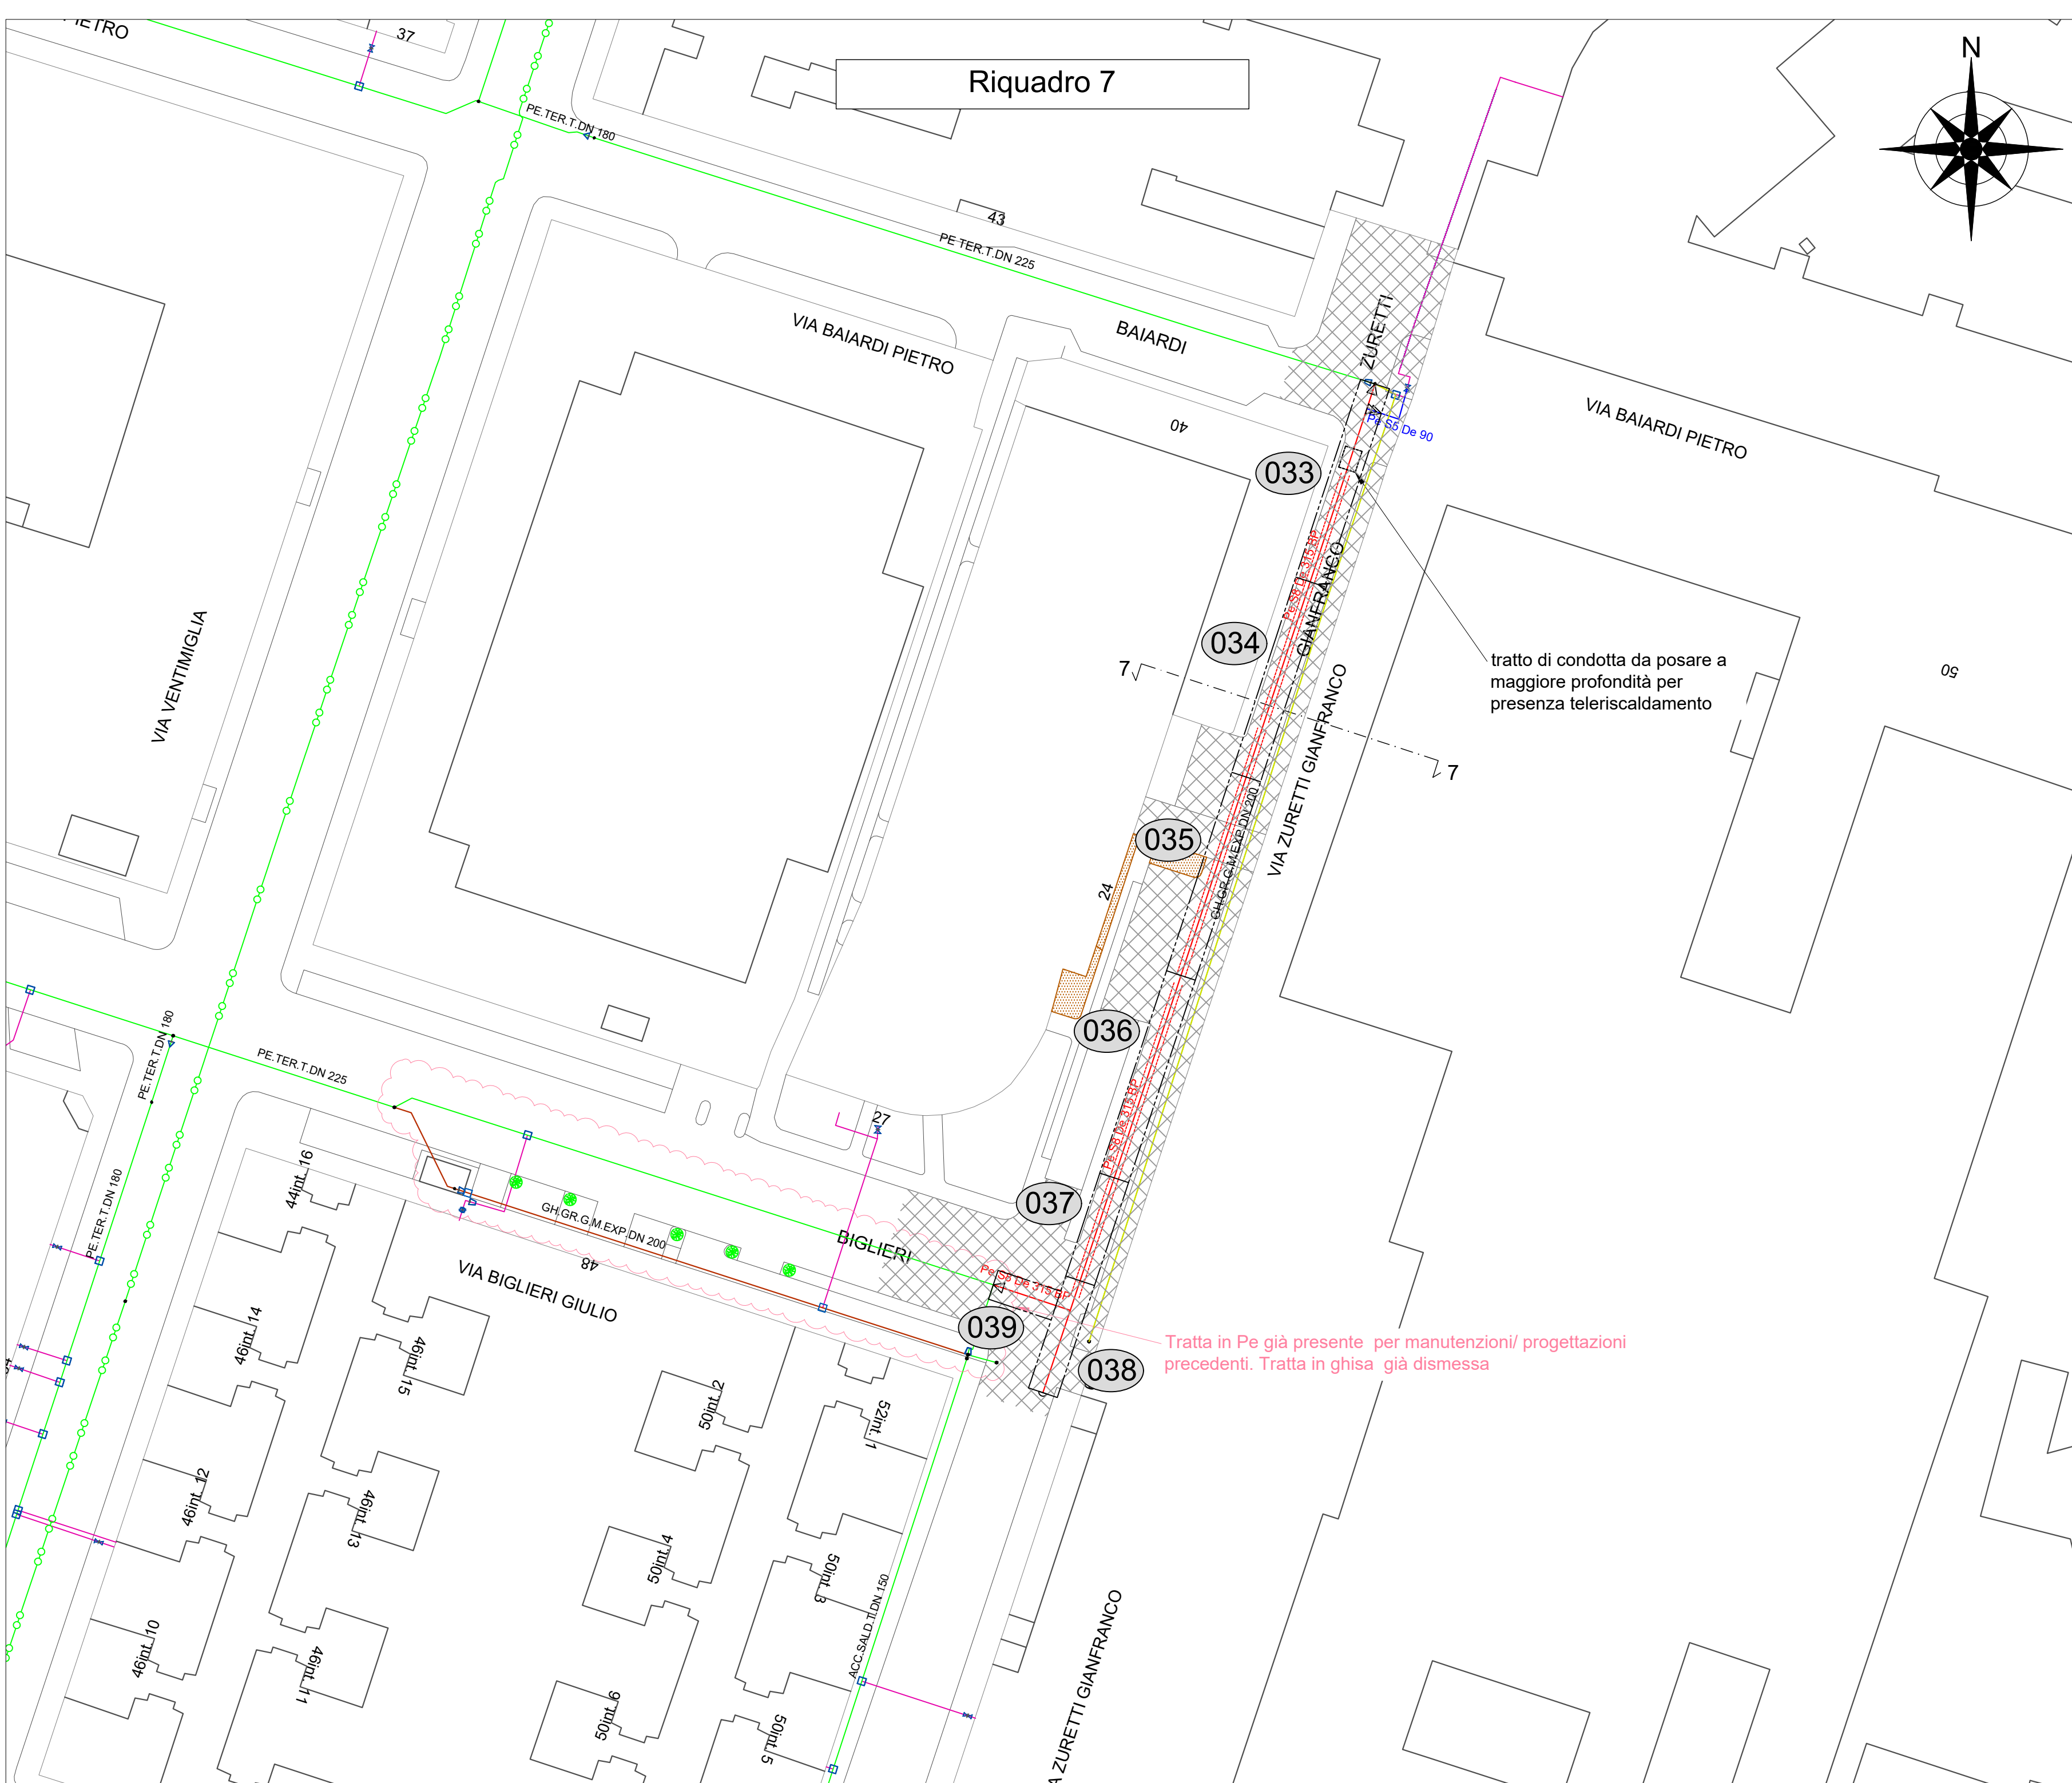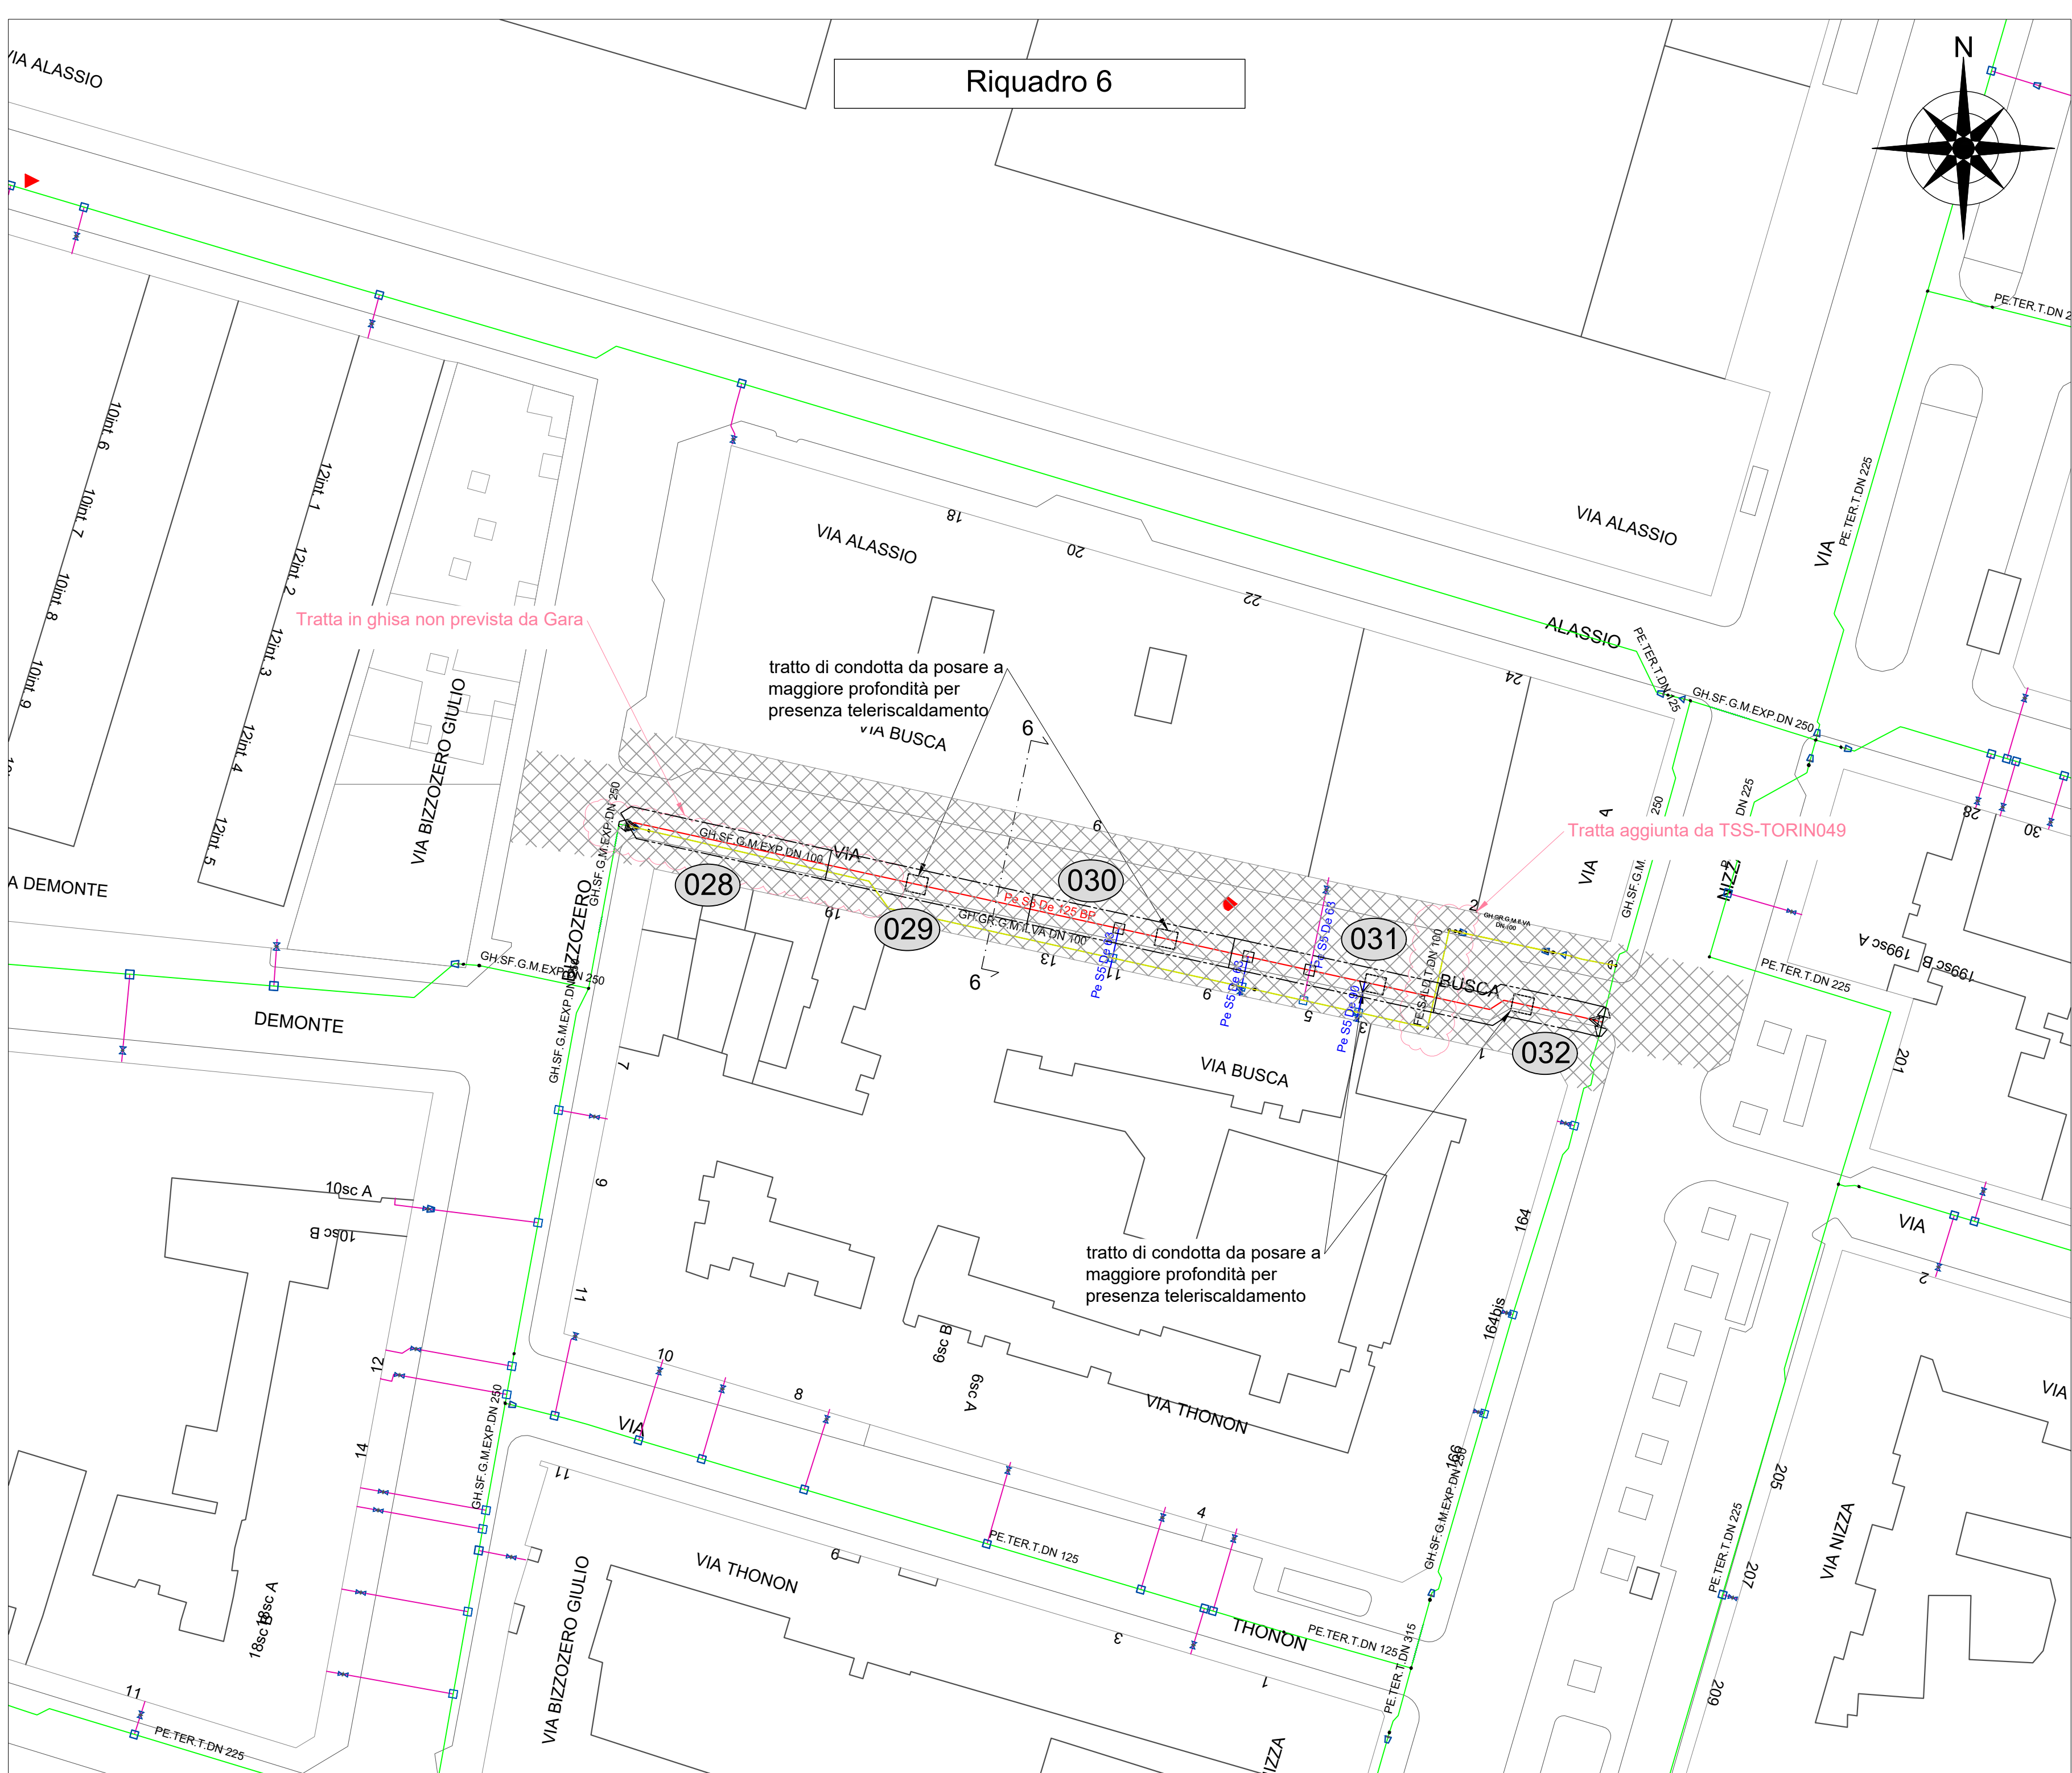

LEGENDA

	Reti in progetto BP
	Reti in dismissione BP
	Zona di lavoro
	n° Zona di lavoro
	Asfalto
	Sternatore/area verde
	Autobloccanti/ammattionato

Zone di lavoro e pavimentazioni (Riquadro 6)

n.	dati condotta	quantità [m]	lato strada	tipo di pavimentazione
28	Pe De 125	24	Destra	Asfalto
29	Pe De 125	24	Destra	Asfalto
30	Pe De 125	24	Destra	Asfalto
31	Pe De 125	24	Destra	Asfalto
32	Pe De 125	20	Destra	Asfalto

Zone di lavoro e pavimentazioni (Riquadro 7)

n.	dati condotta	quantità [m]	lato strada	tipo di pavimentazione
33	Pe De 315	19	Destra	Asfalto
33	Pe De 315	5	Attraversamento	Asfalto
34	Pe De 315	24	Destra	Asfalto
35	Pe De 315	24	Destra	Asfalto
36	Pe De 315	24	Destra	Asfalto
37	Pe De 315	13	Destra	Asfalto
38	Pe De 315	2	Attraversamento	Asfalto
38	Pe De 315	12	Destra	Asfalto
39	Pe De 315	9	Centro	Asfalto

Zone di lavoro e pavimentazioni (Riquadro 8)

n.	dati condotta	quantità [m]	lato strada	tipo di pavimentazione
40	Pe De 125	7	Attraversamento	Asfalto
40	Pe De 125	17	Centro	Asfalto
41	Pe De 125	24	Centro	Asfalto
42	Pe De 125	24	Centro	Asfalto
43	Pe De 125	24	Sinistra	Asfalto

Zone di lavoro e pavimentazioni (Riquadro 9)

n.	dati condotta	quantità [m]	lato strada	tipo di pavimentazione
44	Pe De 125	24	Destra	Asfalto
45	Pe De 125	24	Centro	Asfalto
46	Pe De 125	24	Centro	Asfalto
47	Pe De 125	24	Centro	Asfalto
48	Pe De 125	24	Centro	Asfalto
49	Pe De 125	24	Centro	Asfalto
50	Pe De 125	18	Centro	Asfalto

LEARDI


Progetto:

Unità Responsabile della Progettazione: INGEGREAL-INGE-PROGRE

Progetto n°: 21-0584-3E-00-001272
WBS: SI20.I0300.02.1109
ALLEGATO n°: 4.3

Formato: A0 Scale: 1:500

Comune di TORINO (TO)
Viale Varie
Progetto Esecutivo
SOSTITUZIONE RETE BP (L=2745,39 M) - GARA TO 1
Intervento n° SI-036213-001272-TSS-TORIN008
Planimetria pavimentazioni e zone di lavoro - Tavola 3

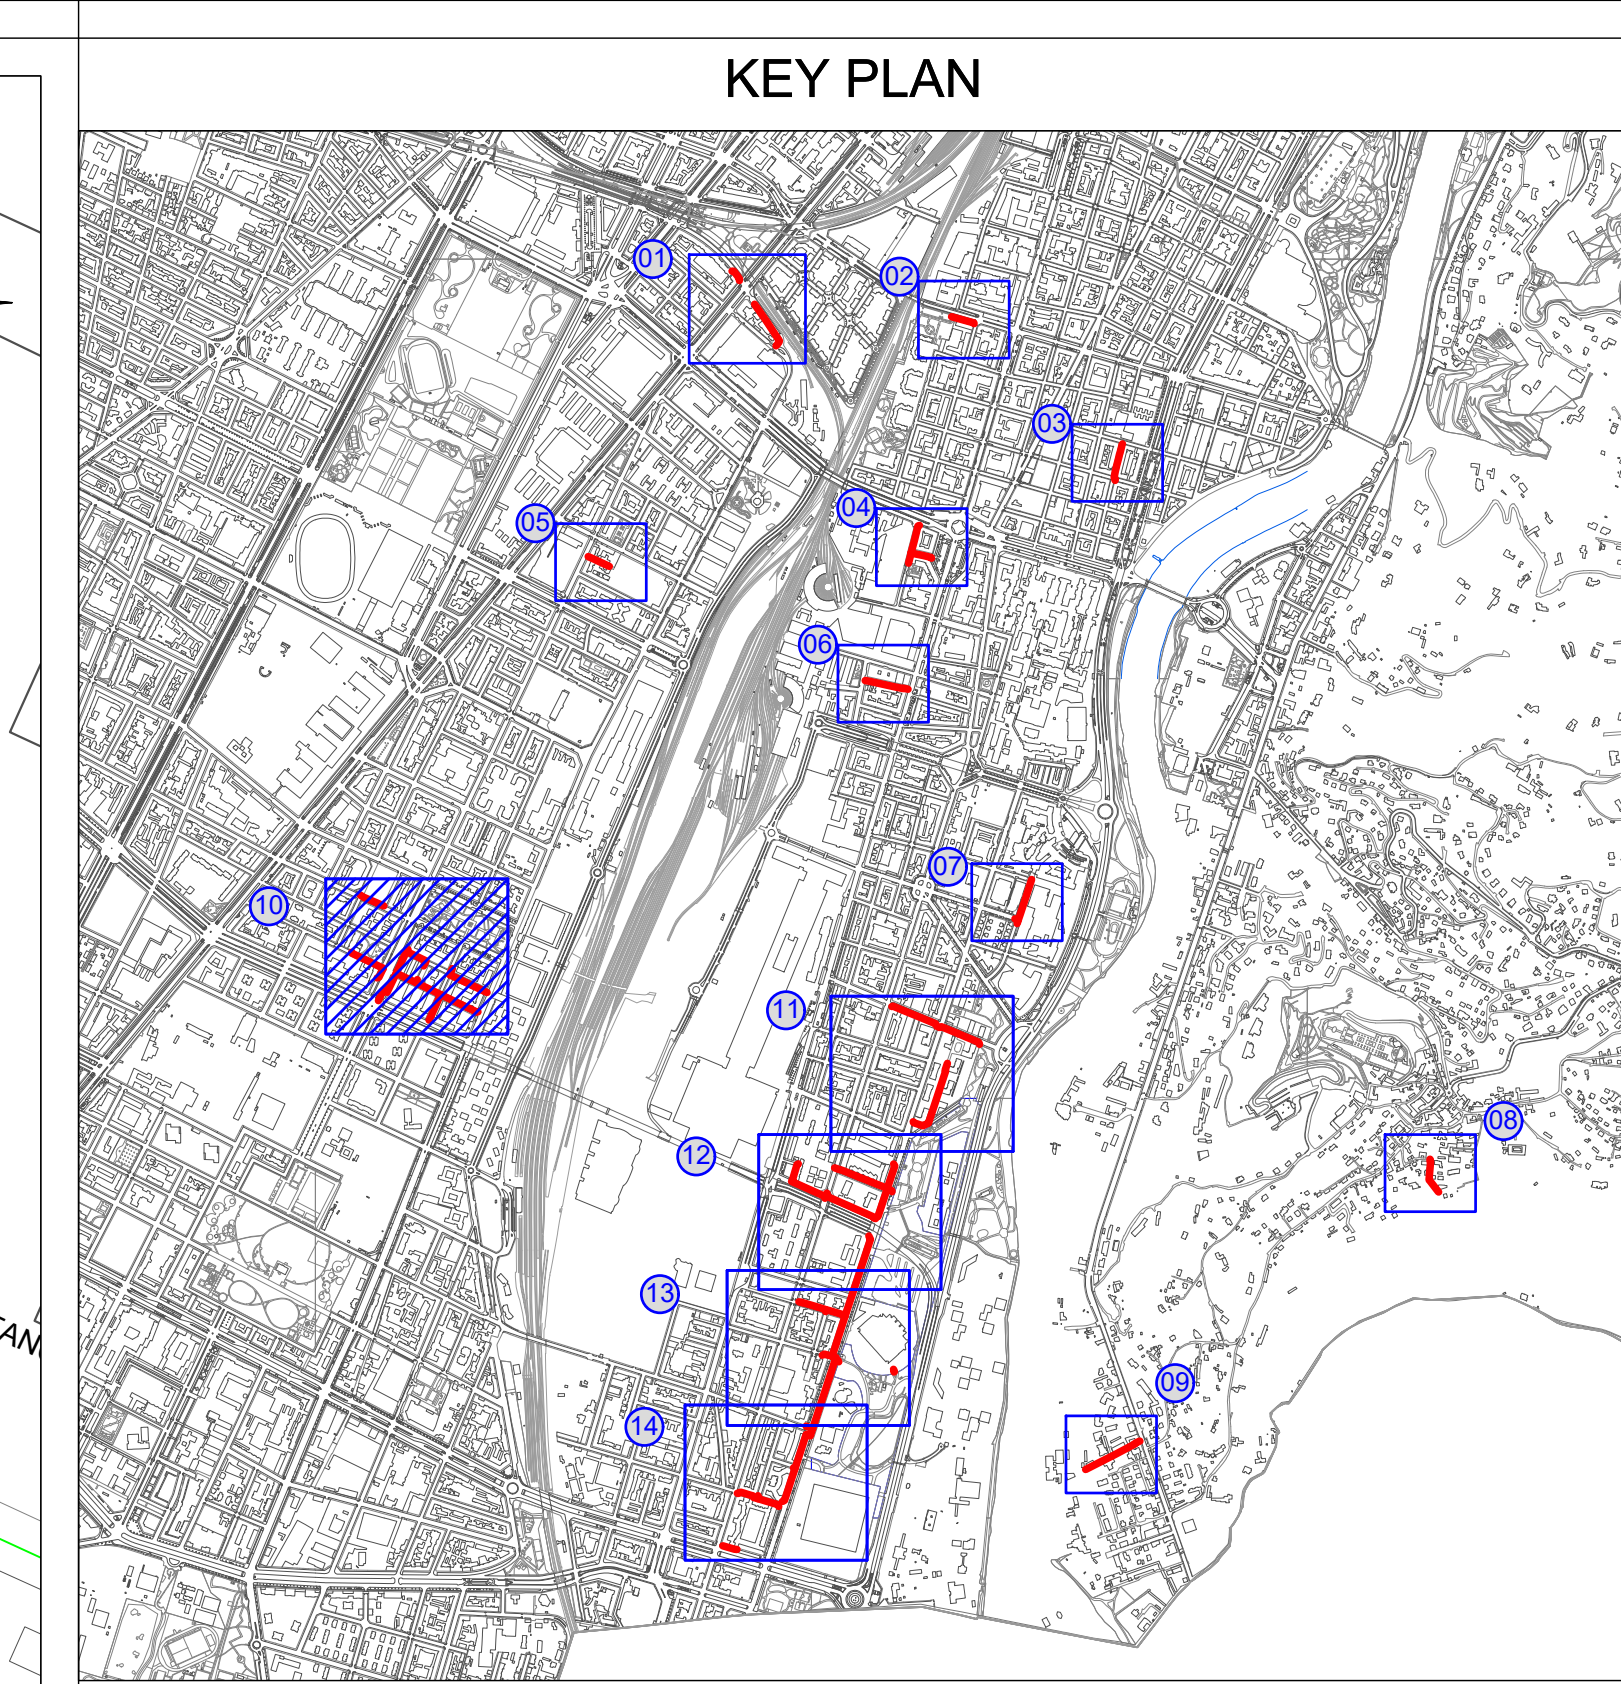

LEGENDA				
	Reti in progetto BP		n° Zona di lavoro	
	Reti in dismissione BP		Asfalto	
	Zona di lavoro		Sterzo/area verde	
			Autobloccanti/ammattonato	

Zone di lavoro e pavimentazioni				
n.	dati condotta	quantità [m]	lato strada	tipo di pavimentazione
51	Fe De 225	8	Attraversamento	Asfalto
51	Fe De 225	16	Sinistra	Asfalto
52	Fe De 225	24	Sinistra	Asfalto
53	Fe De 225	21	Sinistra	Asfalto
54	Fe De 180	2	Attraversamento	Asfalto
54	Fe De 180	22	Destra	Asfalto
55	Fe De 180	24	Destra	Asfalto
56	Fe De 180	24	Destra	Asfalto
57	Fe De 180	7	Attraversamento	Asfalto
57	Fe De 315	3	Sinistra	Asfalto
57	Fe De 180	16	Destra	Asfalto
58	Fe De 315	13	Sinistra	Asfalto
59	Fe De 315	11	Sinistra	Asfalto
59	Fe De 315	6	Attraversamento	Asfalto
60	Fe De 125	2	Attraversamento	Asfalto
60	Fe De 180	12	Sinistra	Asfalto
61	Fe De 125	24	Sinistra	Asfalto
62	Fe De 125	24	Sinistra	Asfalto
63	Fe De 125	15	Attraversamento	Asfalto
63	Fe De 125	9	Sinistra	Asfalto
64	Fe De 180	12	Sinistra	Asfalto
65	Fe De 180	24	Sinistra	Asfalto
66	Fe De 180	12	Sinistra	Asfalto
67	Fe De 180	2	Attraversamento	Asfalto
67	Fe De 180	12	Sinistra	Asfalto
68	Fe De 180	24	Sinistra	Asfalto
69	Fe De 180	24	Sinistra	Asfalto
70	Fe De 180	11	Sinistra	Asfalto
71	Fe De 180	24	Sinistra	Asfalto
72	Fe De 180	24	Sinistra	Asfalto
73	Fe De 180	2	Attraversamento	Asfalto
73	Fe De 180	12	Sinistra	Asfalto
74	Fe De 180	7	Attraversamento	Asfalto
74	Fe De 180	17	Sinistra	Asfalto
75	Fe De 180	24	Sinistra	Asfalto
76	Fe De 180	24	Sinistra	Asfalto
77	Fe De 180	24	Sinistra	Asfalto
78	Fe De 180	24	Sinistra	Asfalto
79	Fe De 180	24	Sinistra	Asfalto
80	Fe De 180	24	Sinistra	Asfalto
81	Fe De 180	9,5	Sinistra	Asfalto
81	Fe De 180	0,5	Sinistra	Autobloccanti
82	Fe De 180	24	Destra	Asfalto
83	Fe De 180	24	Destra	Asfalto
84	Fe De 180	9	Attraversamento	Asfalto
84	Fe De 180	3	Attraversamento	Sterzo
84	Fe De 180	7	Destra	Asfalto
84	Fe De 180	6	Sinistra	Asfalto
85	Fe De 180	23	Destra	Asfalto
85	Fe De 180	18	Sinistra	Asfalto
85	Fe De 180	7	Attraversamento	Asfalto
87	Fe De 180	24	Destra	Asfalto
88	Fe De 180	24	Destra	Asfalto
88	Fe De 180	24	Destra	Asfalto
90	Fe De 180	17	Destra	Asfalto
91	Fe De 180	15	Destra	Asfalto
201	Fe De 125	2	Attraversamento	Asfalto
201	Fe De 180	12	Destra	Asfalto
202	Fe De 125	7	Sinistra	Asfalto

Progetto: **ORDINE DEI GEOMETRI DELLA PROV. DI TORINO**

Progetto n°: 21-0564-3E-00-00/1272
VBS: SI.20.10300.02.1109
ALLEGATO n°: 4.4

Formato: A0 Scale 1 : 500


Unità Responsabile della Progettazione

INGENER-ANGE-PROGRE

Disegnato	0	30	11	22	A. Saroni	L. Contagna	A. Leardi
Revisione							
Com. : 2484							

Comune di TORINO (TO)
Via Vane
Progetto Esecutivo
SOSTITUZIONE RETE BP (L=2745,39 M) - GARA TO 1
Intervento n° SI-0262-13-01/1272-TSS-TORIN008
Planimetria pavimentazioni e zone di lavoro - Tavola 4

Il presente elaborato è di proprietà aziendale - La società tutela i propri diritti a termini di legge.

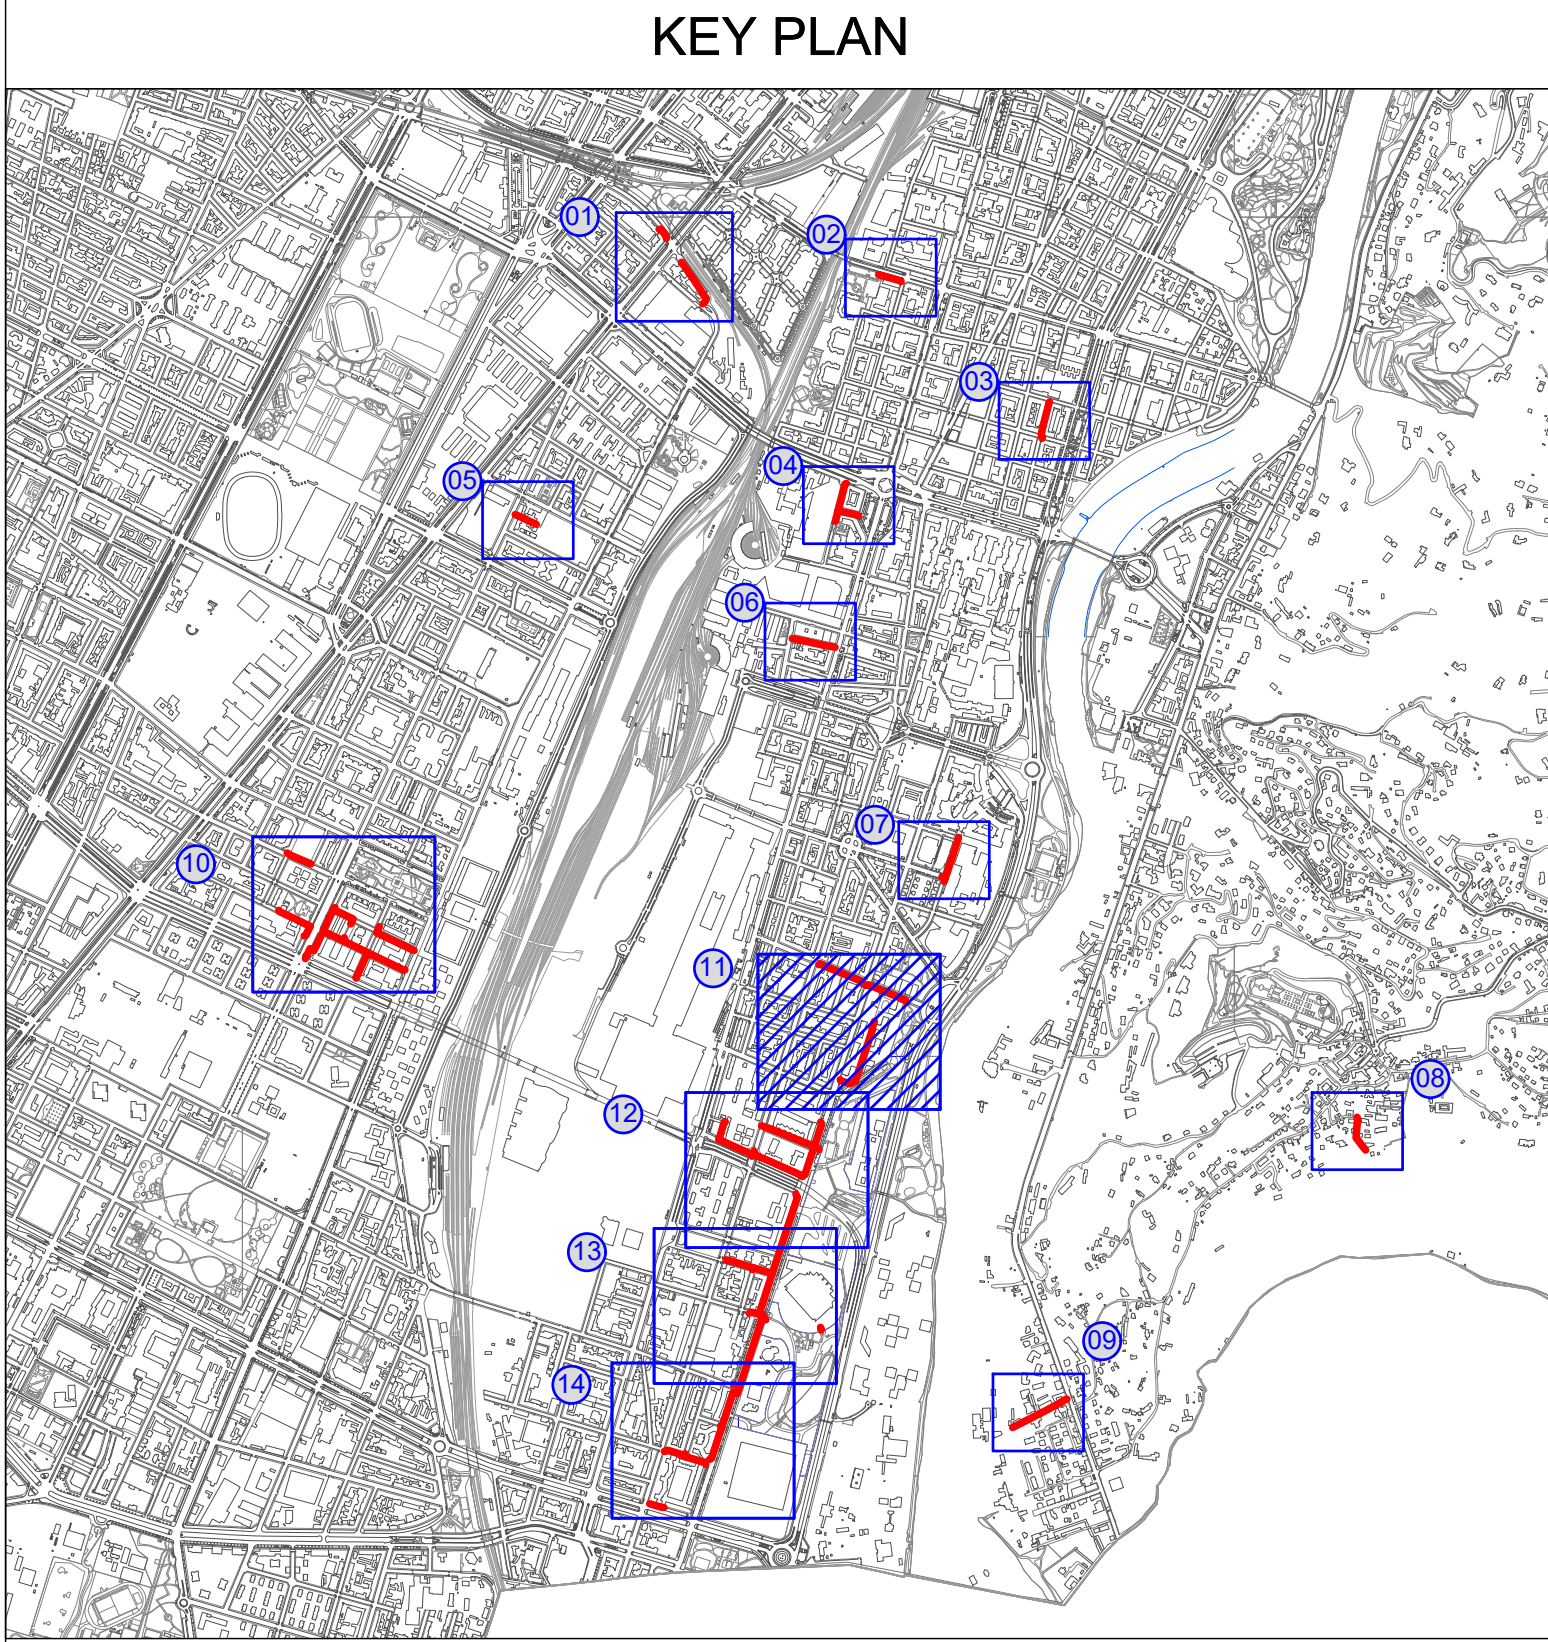

LEGENDA

	Rete in progetto BP
	Rete in dismissione BP
	Zona di lavoro
	n° Zona di lavoro
	Asfalto
	Sterratore/area verde
	Autobloccanti/ammattionato

Zone di lavoro e pavimentazioni				
n.	dati condotta	quantità [m]	lato strada	tipo di pavimentazione
92	Pe De 180	24	Destra	Asfalto
93	Pe De 180	24	Destra	Asfalto
94	Pe De 180	24	Destra	Asfalto
95	Pe De 180	24	Destra	Asfalto
96	Pe De 180	24	Destra	Asfalto
97	Pe De 180	12	Destra	Asfalto
98	Pe De 180	9	Attraversamento	Asfalto
99	Pe De 180	16	Destra	Asfalto
100	Pe De 180	24	Destra	Asfalto
101	Pe De 125	5	Destra	Asfalto
102	Pe De 125	24	Destra	Asfalto
103	Pe De 125	16	Destra	Asfalto
104	Pe De 125	8	Attraversamento	Asfalto
105	Pe De 180	17	Centro	Asfalto
106	Pe De 180	3	Attraversamento	Asfalto
107	Pe De 180	1	Sinistra	Asfalto
108	Pe De 180	20	Sinistra	Asfalto
109	Pe De 180	24	Sinistra	Asfalto
110	Pe De 180	24	Sinistra	Asfalto
111	Pe De 180	24	Sinistra	Asfalto
112	Pe De 180	24	Sinistra	Asfalto
113	Pe De 180	16	Attraversamento	Asfalto
114	Pe De 180	5	Sinistra	Sterrato
115	Pe De 180	23	Destra	Sterrato
116	Pe De 180	1	Attraversamento	Asfalto

Progetto n°: 21-0584-3E-00-00/1272
WBS: SI.20.10300.02.1109
ALLEGATO n°: 4.5

Progettato da:
Ordine degli Ingegneri di Alessandria
matr. n° 1061

Unità Responsabile della Progettazione
INGREAL-INGE-PROGRE


Comune di TORINO (TO)
Via Vane
Progetto Esecutivo
SOSTITUZIONE RETE BP (L=2745,39 M) - GARA TO 1
Intervento n° SI-0362-13-001272-TSS-TORINO08
Planimetria pavimentazioni e zone di lavoro - Tavola 5

Formato: A0
Scale: 1:500

Comittente:

Revisione	0	30	11	22	A. Saroni	L. Contagna	A. Leardi
Elaborazione per commenti	Rev.	G.	M.	A.	Redatto	Controllato	Approvato

Il presente elaborato è di proprietà aziendale - La società tutela i propri diritti a termini di legge.

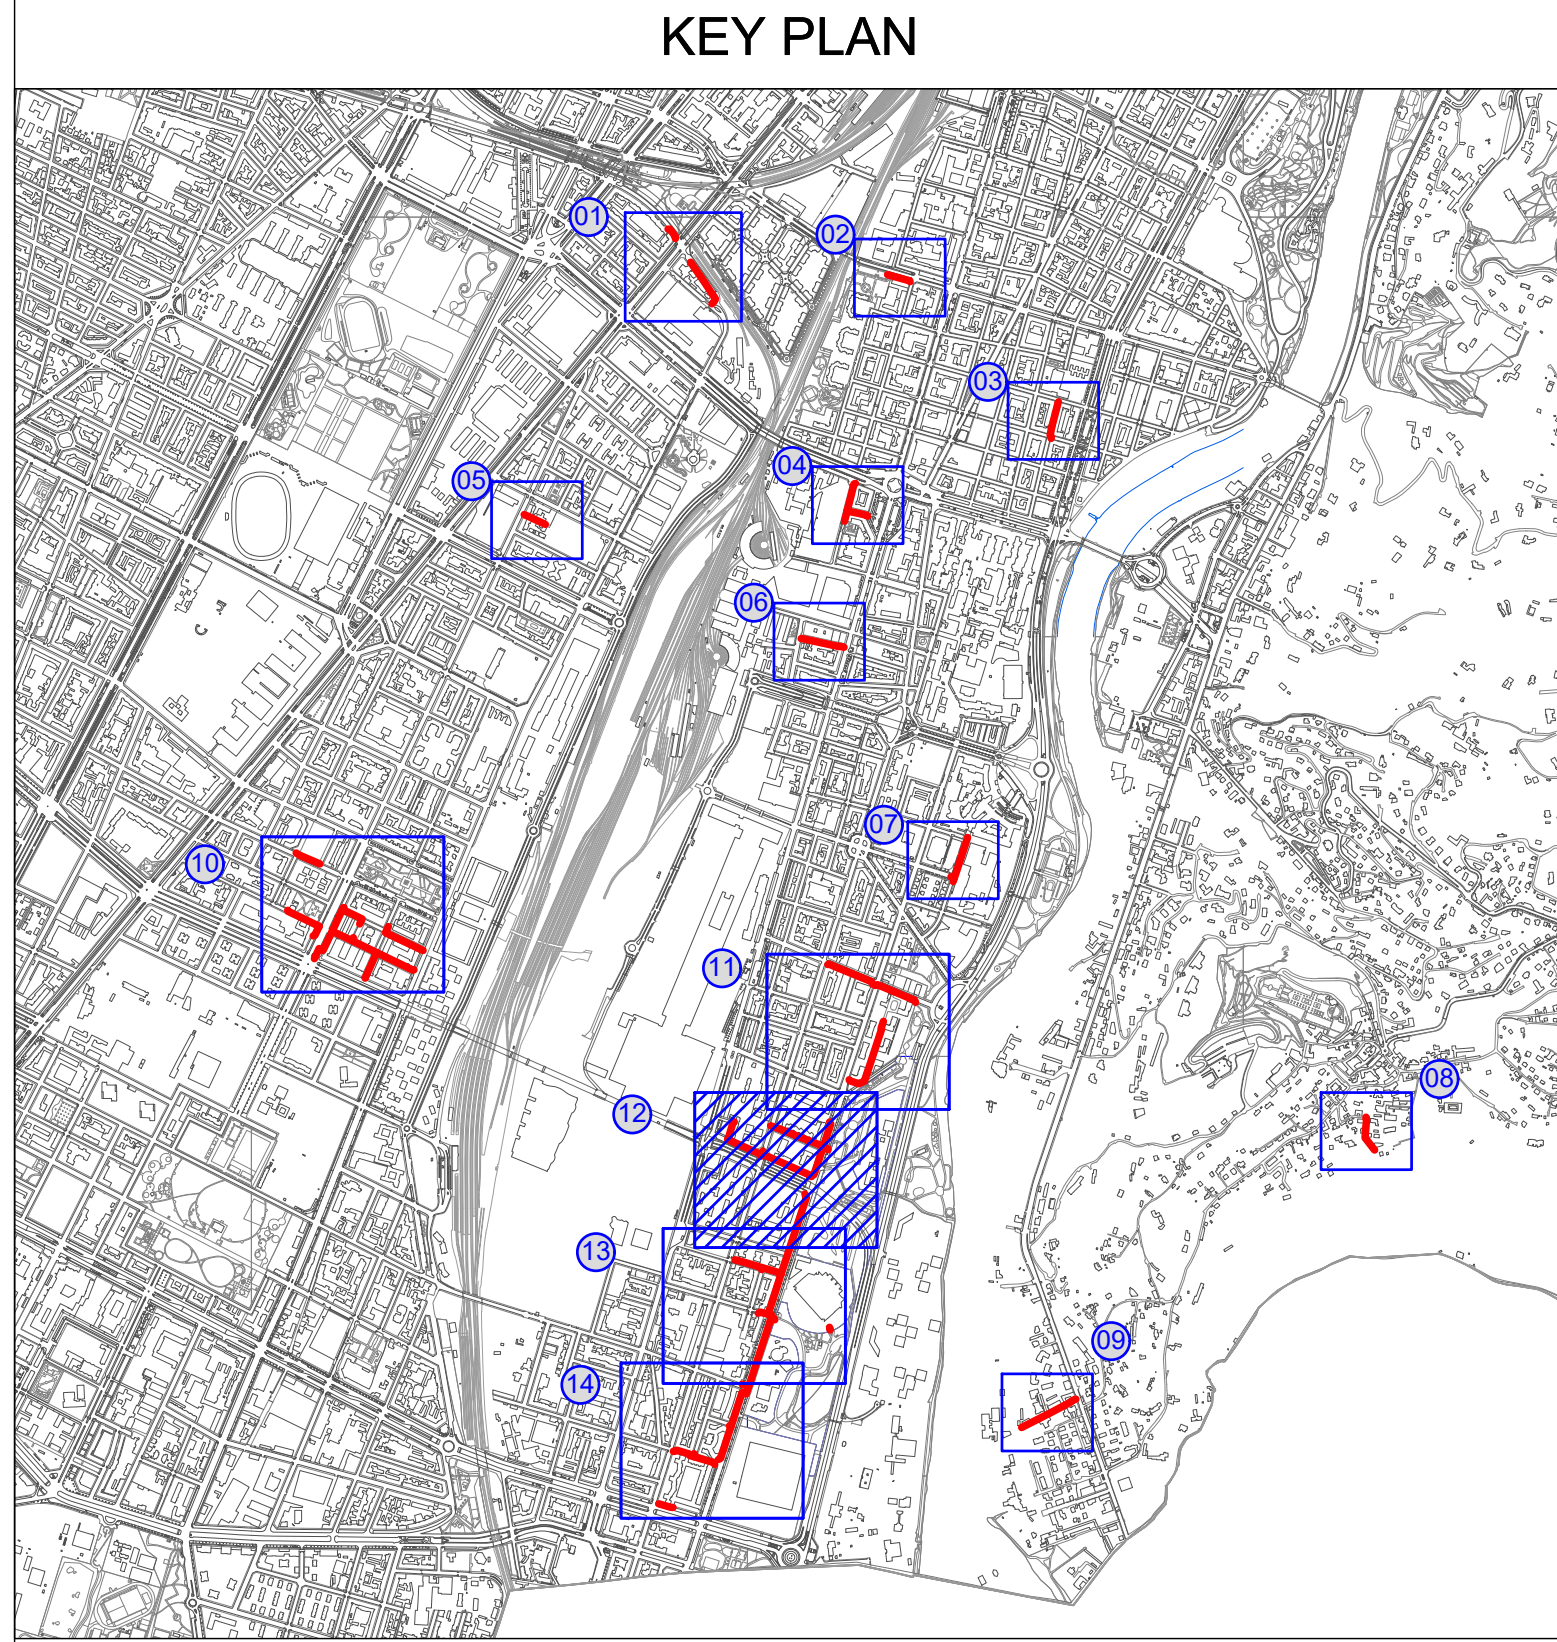

LEGENDA

- Rele in progetto BP
- Rele in dismissione BP
- Zona di lavoro
- n° Zona di lavoro
- Asfalto
- Smeraldo/area verde
- Autobloccanti/ammattionato

Zone di lavoro e pavimentazioni				
n.	dati condotta	quantità [m]	lato strada	tipo di pavimentazione
112	Pe De 315	3	Attraversamento	Asfalto
112	Pe De 315	1	Attraversamento	Asfalto
112	Pe De 315	20	Destra	Asfalto
113	Pe De 315	24	Destra	Asfalto
114	Pe De 315	15	Attraversamento	Asfalto
115	Pe De 315	2	Destra	Asfalto
115	Pe De 315	3	Attraversamento	Asfalto
116	Pe De 225	24	Destra	Asfalto
117	Pe De 225	24	Destra	Asfalto
118	Pe De 225	24	Destra	Asfalto
119	Pe De 225	24	Destra	Asfalto
120	Pe De 225	24	Destra	Asfalto
121	Pe De 225	14	Destra	Asfalto
122	Pe De 225	13	Destra	Asfalto
123	Pe De 180	14	Attraversamento	Asfalto
124	Pe De 315	24	Destra	Asfalto
125	Pe De 315	24	Destra	Asfalto
126	Pe De 315	24	Destra	Asfalto
127	Pe De 315	24	Destra	Asfalto
128	Pe De 315	24	Destra	Asfalto
129	Pe De 315	24	Destra	Asfalto
130	Pe De 315	24	Destra	Asfalto
131	Pe De 315	24	Destra	Asfalto
132	Pe De 315	15	Destra	Asfalto
132	Pe De 315	3	Attraversamento	Asfalto
133	Pe De 315	2	Attraversamento	Asfalto
133	Pe De 315	8	Destra	Asfalto
133	Pe De 315	2	Attraversamento	Asfalto
133	Pe De 180	5	Destra	Asfalto
134	Pe De 315	6	Sinistra	Asfalto
134	Pe De 315	4	Attraversamento	Asfalto
135	Pe De 315	4	Attraversamento	Asfalto
136	Pe De 180	24	Destra	Asfalto
137	Pe De 180	24	Destra	Asfalto
138	Pe De 180	24	Destra	Asfalto
139	Pe De 180	20	Destra	Asfalto
139	Pe De 180	4	Attraversamento	Asfalto
140	Pe De 180	24	Destra	Asfalto
141	Pe De 180	20	Destra	Asfalto
141	Pe De 180	2	Attraversamento	Asfalto
142	Pe De 180	8	Attraversamento	Asfalto
142	Pe De 315	16	Destra	Asfalto
143	Pe De 315	24	Destra	Asfalto
144	Pe De 315	24	Destra	Asfalto
145	Pe De 315	24	Destra	Asfalto
146	Pe De 315	24	Destra	Asfalto
147	Pe De 315	24	Destra	Asfalto

Comune di TORINO (TO)
Via Vane
Progetto Esecutivo
SOSTITUZIONE RETE BP (L=2745,39 M) - GARA TO 1
Intervento n° SI-036213-001272-TSS-TORIN006
Planimetria pavimentazioni e zone di lavoro - Tavola 6

Progetto n°: 21-0584-3E-00-001272
WBS: SI20.I0300.02.1109
ALLEGATO n°: 4.6

Formato: A0 Scale 1 : 500

Comittente: IG Italgas Reti


Unità Responsabile della Progettazione: INGEGRA-INGE-PROG


Progettazione: LEARDI

Disegnato: G. M. A. Redatto: A. Leardi

Verificato: G. M. A. Controllato: A. Leardi

Approvato: A. Leardi

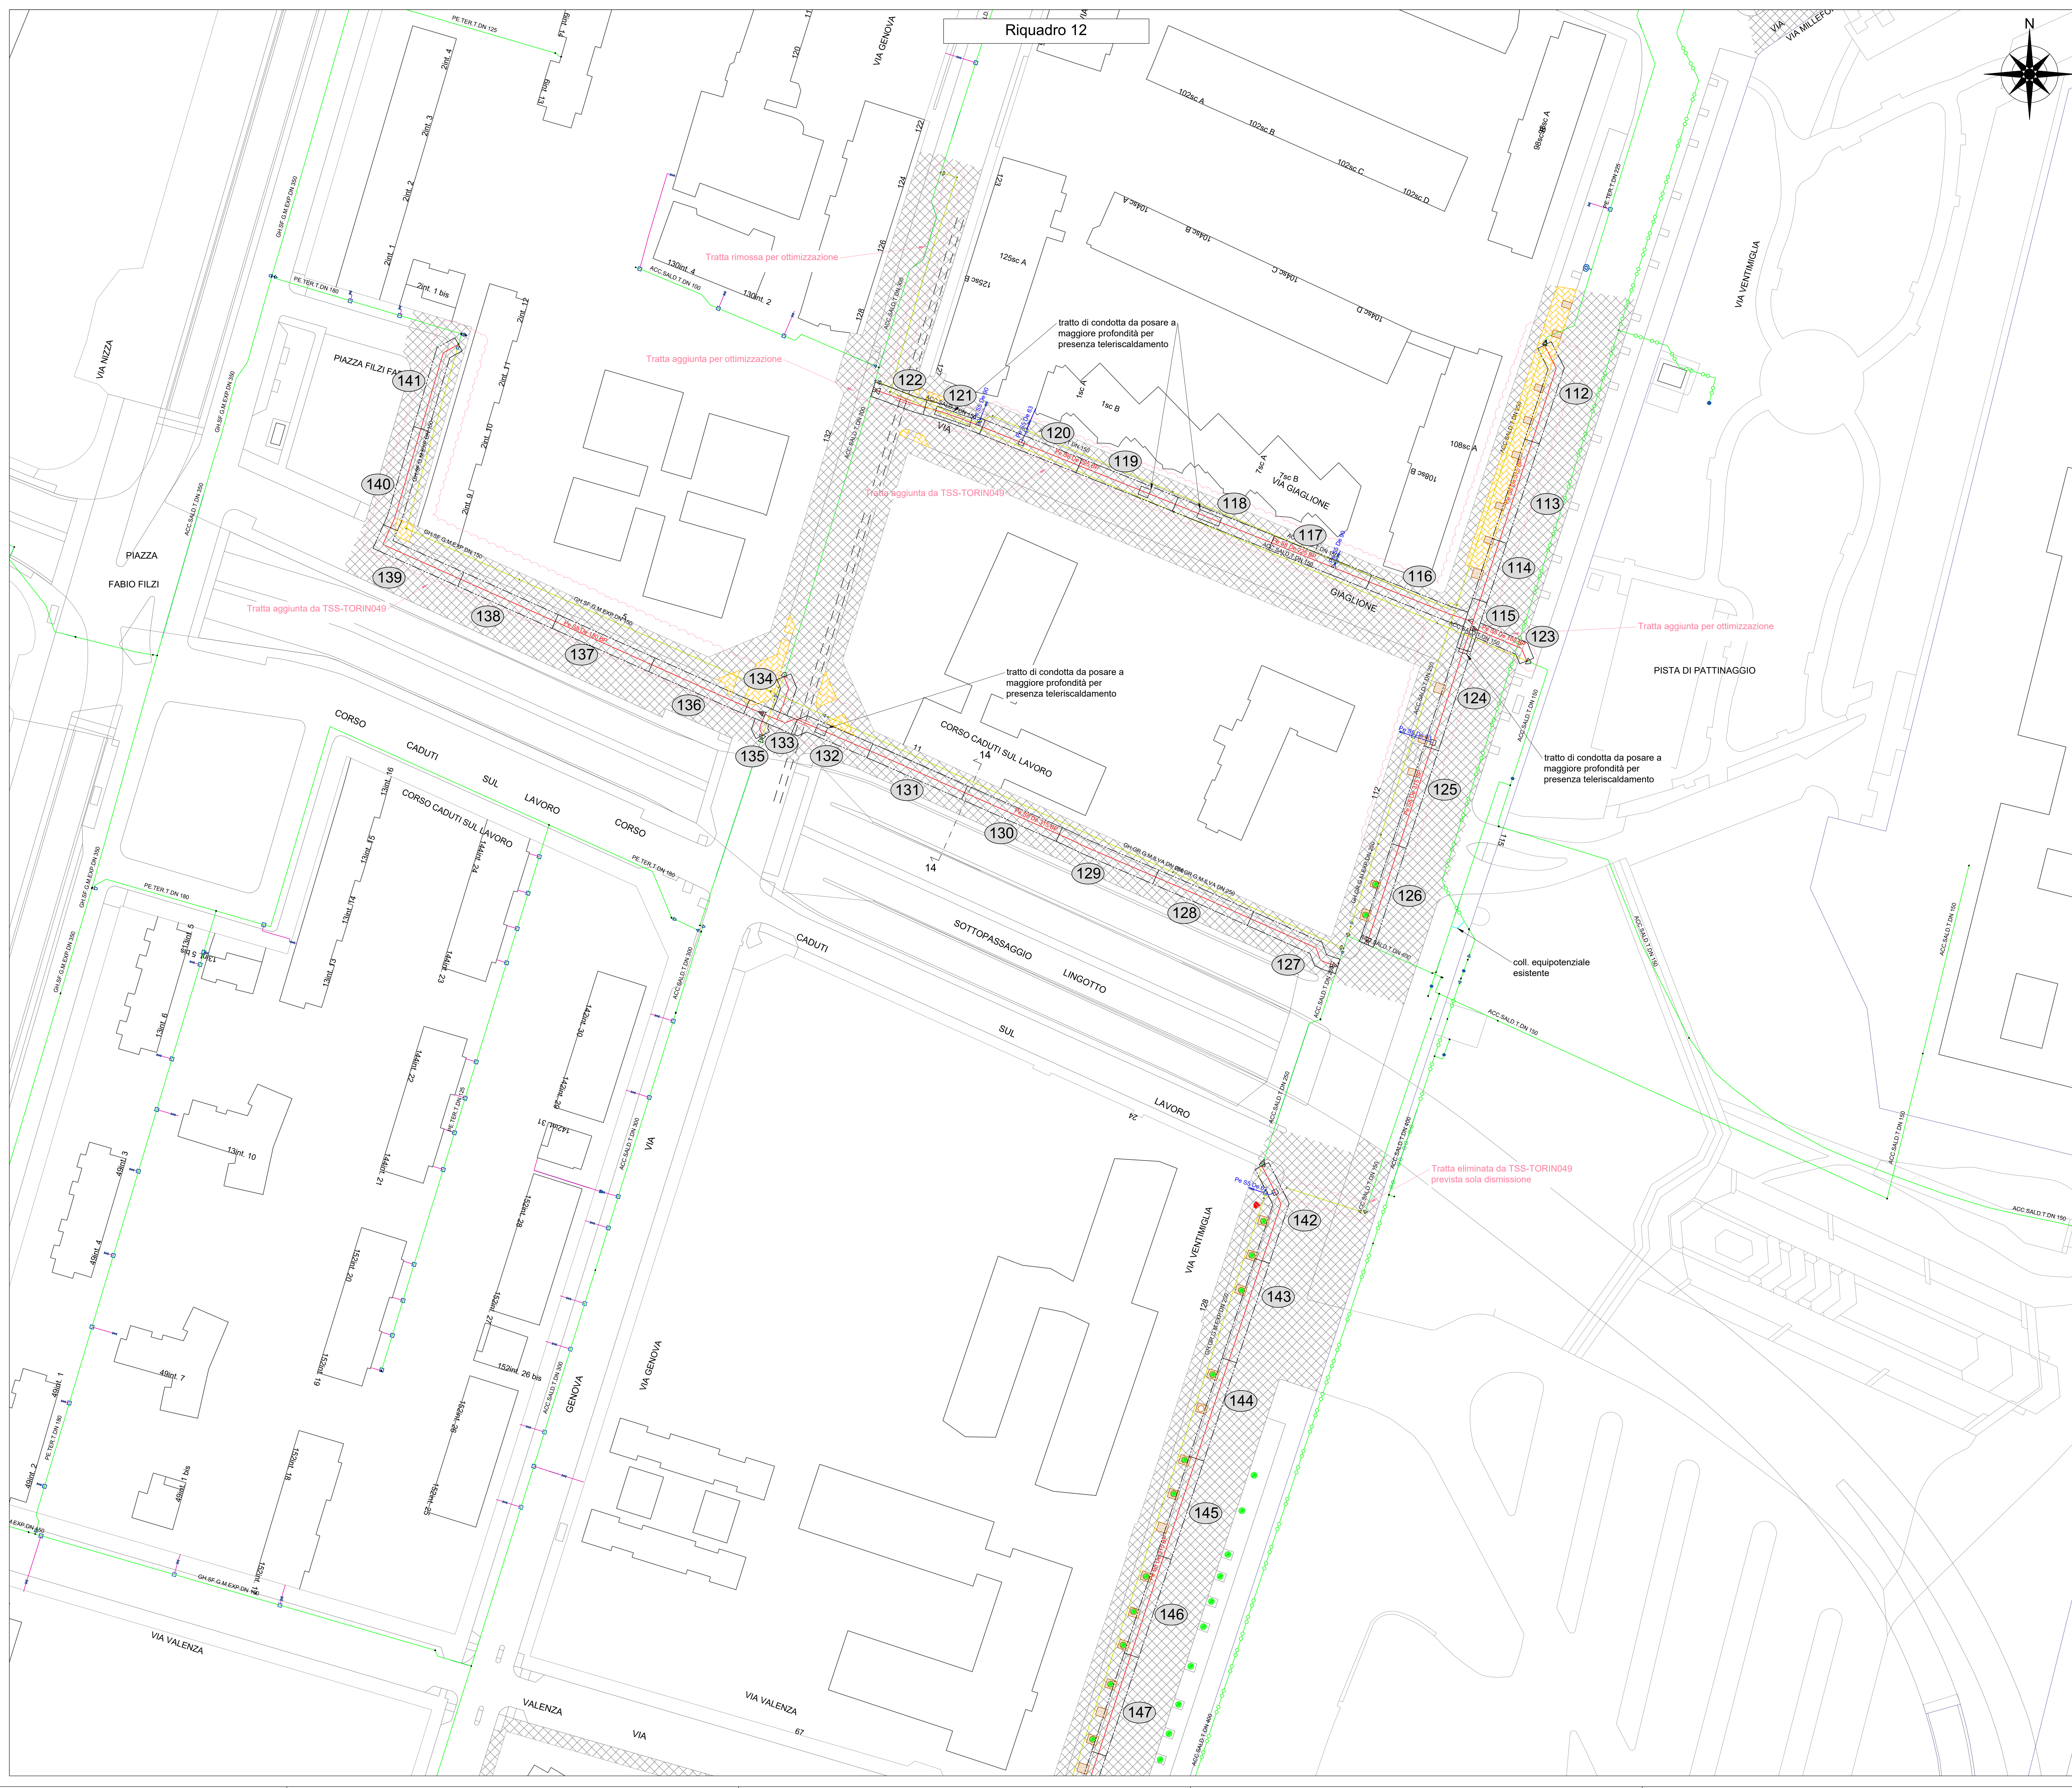

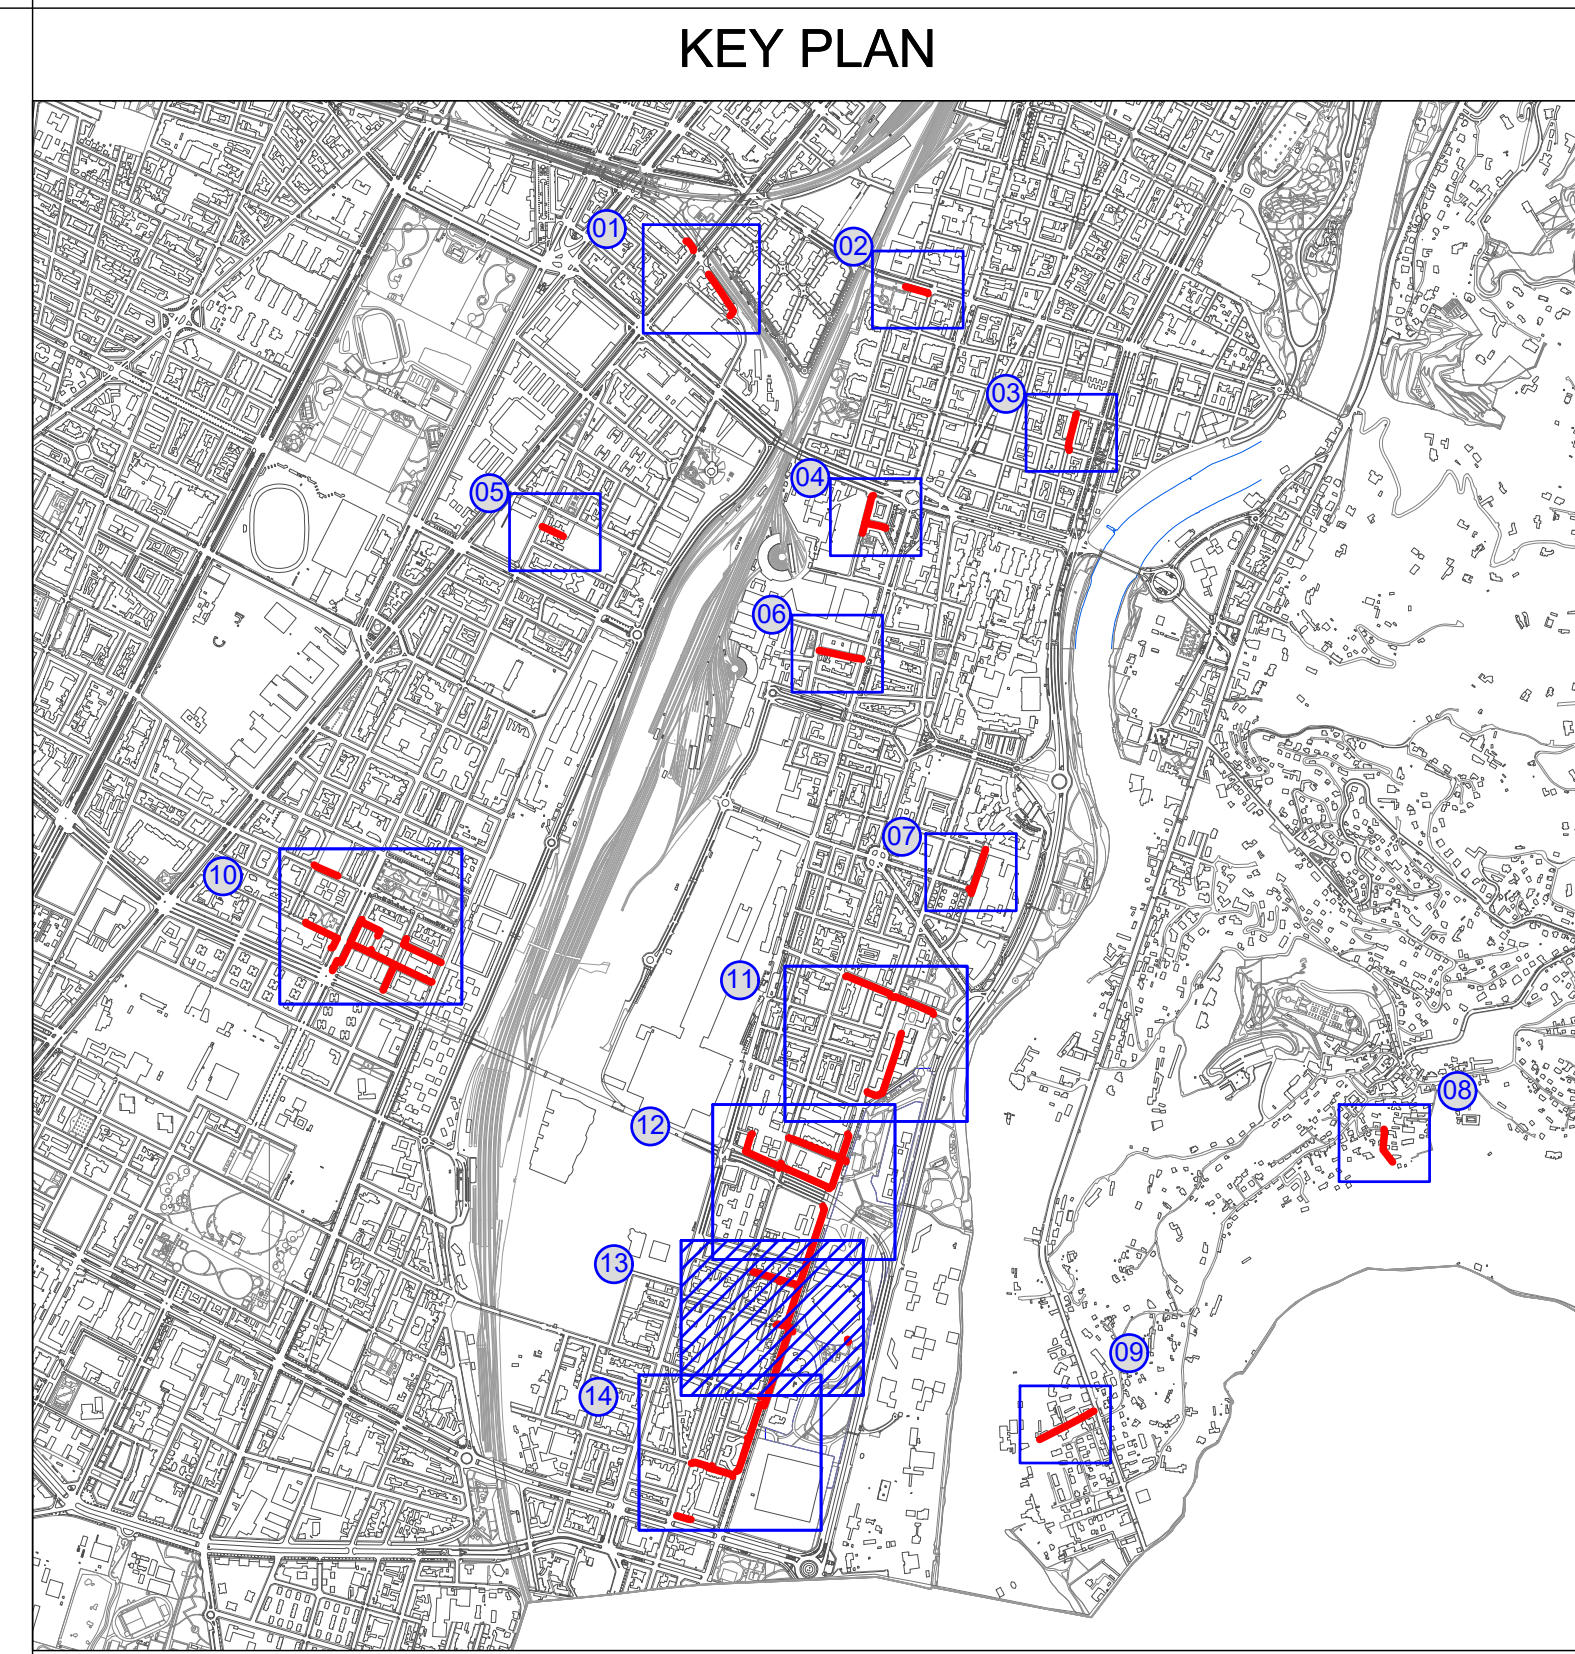

Zona di lavoro e pavimentazioni				
n.	dati condotta	quantità [m]	lato strada	tipo di pavimentazione
148	Fe De 315	24	Destra	Asfalto
149	Fe De 315	24	Destra	Asfalto
150	Fe De 315	24	Destra	Asfalto
151	Fe De 315	12	Destra	Asfalto
152	Fe De 180	2	Attraversamento	Asfalto
153	Fe De 180	1	Attraversamento	Asfalto
154	Fe De 180	23	Destra	Asfalto
155	Fe De 180	24	Destra	Asfalto
156	Fe De 125	2	Attraversamento	Asfalto
157	Fe De 180	12	Destra	Asfalto
158	Fe De 125	4	Attraversamento	Asfalto
159	Fe De 180	24	Destra	Asfalto
160	Fe De 315	24	Destra	Asfalto
161	Fe De 315	24	Destra	Asfalto
162	Fe De 315	24	Destra	Asfalto
163	Fe De 315	8	Destra	Asfalto
164	Fe De 315	2	Destra	Asfalto
165	Fe De 180	4	Attraversamento	Asfalto
166	Fe De 315	9	Attraversamento	Asfalto
167	Fe De 180	12	Destra	Asfalto
168	Fe De 180	6	Destra	Asfalto
169	Fe De 180	6	Attraversamento	Asfalto
170	Fe De 315	2	Attraversamento	Asfalto
171	Fe De 180	2	Attraversamento	Asfalto
172	Fe De 315	12	Sinistra	Asfalto
173	Fe De 180	9	Attraversamento	Asfalto
174	Fe De 315	13	Sinistra	Asfalto
175	Fe De 315	24	Sinistra	Asfalto
176	Fe De 315	24	Sinistra	Asfalto
177	Fe De 315	24	Sinistra	Asfalto
178	Fe De 315	24	Sinistra	Asfalto
200	Fe De 125	8	Centro	Sterrato

Progetto n°:
21-0584-3E-00-00/1272
VBS:
SI.20.10300.02.1109
ALLEGATO n°: 4.7


Comune di TORINO (TO)
Via Vane
Progetto Esecutivo
SOSTITUZIONE RETE BP (L=2745,39 M) - GARA TO 1
Intervento n° SI-0362-13-00/1272-TSS-TORIN008
Planimetria pavimentazioni e zone di lavoro - Tavola 7

Progettista:
Ordine degli Ingegneri di Alessandria
marco.rossi@ing.it

Unità Responsabile della Progettazione
INGENER-INGE-PROGRE

Disegnato	0	30	11	22	A. Saroni	L. Contagna	A. Leardi		
Verificato									
Formato: A0	Scale: 1:500	Com: 2484	Rev:	G.	M.	A.	Redatto	Controllato	Approvato

Comune di TORINO (TO)
Via Vane
Progetto Esecutivo
SOSTITUZIONE RETE BP (L=2745,39 M) - GARA TO 1
Intervento n° SI-0362-13-00/1272-TSS-TORIN008
Planimetria pavimentazioni e zone di lavoro - Tavola 7

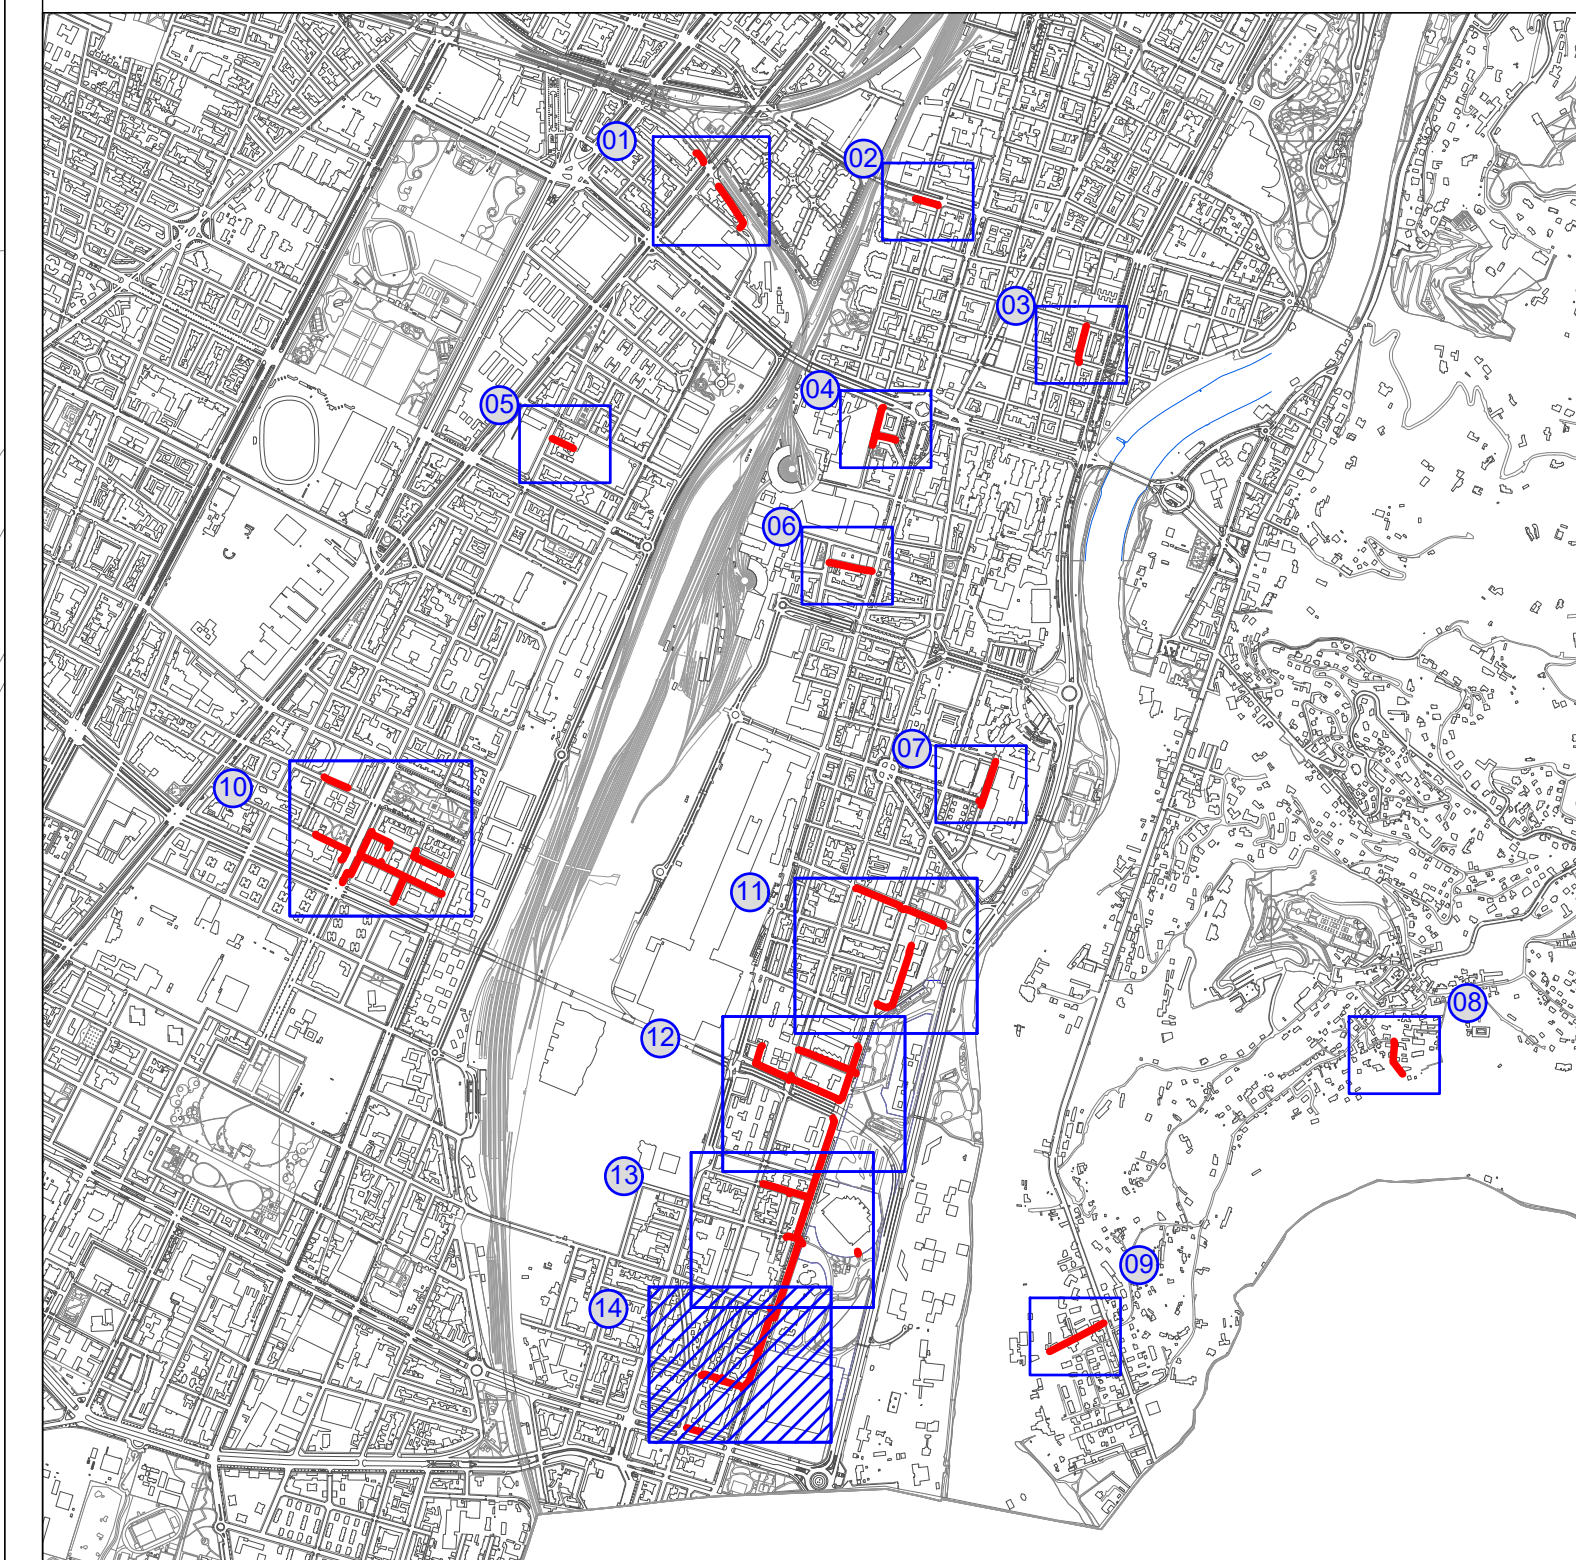

 Rete in progetto BP
 Rete in dismissione BP
 Zona di lavoro

Zone di lavoro e pavimentazioni				
n.	dati condotta	quantità [m]	lato strada	tipo di pavimentazione
177	Pe Di 315	13	Sinistra	Asfalto
177	Pe Di 180	2	Attraversamento	Asfalto
178	Pe Di 180	17	Attraversamento	Asfalto
179	Pe Di 315	12	Sinistra	Asfalto
180	Pe Di 315	12	Attraversamento	Asfalto
180	Pe Di 315	2	Sinistra	Asfalto
180	Pe Di 315	18	Destra	Asfalto
181	Pe Di 315	24	Destra	Asfalto
182	Pe Di 315	24	Destra	Asfalto
183	Pe Di 315	24	Destra	Asfalto
184	Pe Di 315	13	Destra	Asfalto
184	Pe Di 125	2	Attraversamento	Asfalto
185	Pe Di 125	3	Attraversamento	Asfalto
186	Pe Di 315	18	Destra	Asfalto
187	Pe Di 315	24	Destra	Asfalto
188	Pe Di 315	24	Destra	Asfalto
189	Pe Di 315	8	Attraversamento	Asfalto
189	Pe Di 315	18	Destra	Asfalto
190	Pe Di 180	6	Attraversamento	Asfalto
190	Pe Di 180	7	Sinistra	Asfalto
191	Pe Di 180	18	Sinistra	Asfalto
192	Pe Di 180	23	Sinistra	Asfalto
193	Pe Di 180	2	Attraversamento	Asfalto
193	Pe Di 180	12	Sinistra	Asfalto
194	Pe Di 180	8	Attraversamento	Asfalto
195	Pe Di 180	5	Attraversamento	Asfalto
195	Pe Di 180	1	Destra	Asfalto
195	Pe Di 180	12	Sinistra	Asfalto
196	Pe Di 180	17	Destra	Asfalto
197	Pe Di 180	16	Destra	Asfalto
197	Pe Di 180	1	Sinistra	Asfalto
197	Pe Di 180	7	Attraversamento	Asfalto
198	Pe Di 315	16	Destra	Asfalto
199	Pe Di 315	24	Destra	Asfalto

Planimetria pavimen

001272-TSS-TORIN008
e zone di lavoro - Tavola 8

Il presente elaborato è di proprietà aziendale - La società tutelera i propri diritti a termini di le