
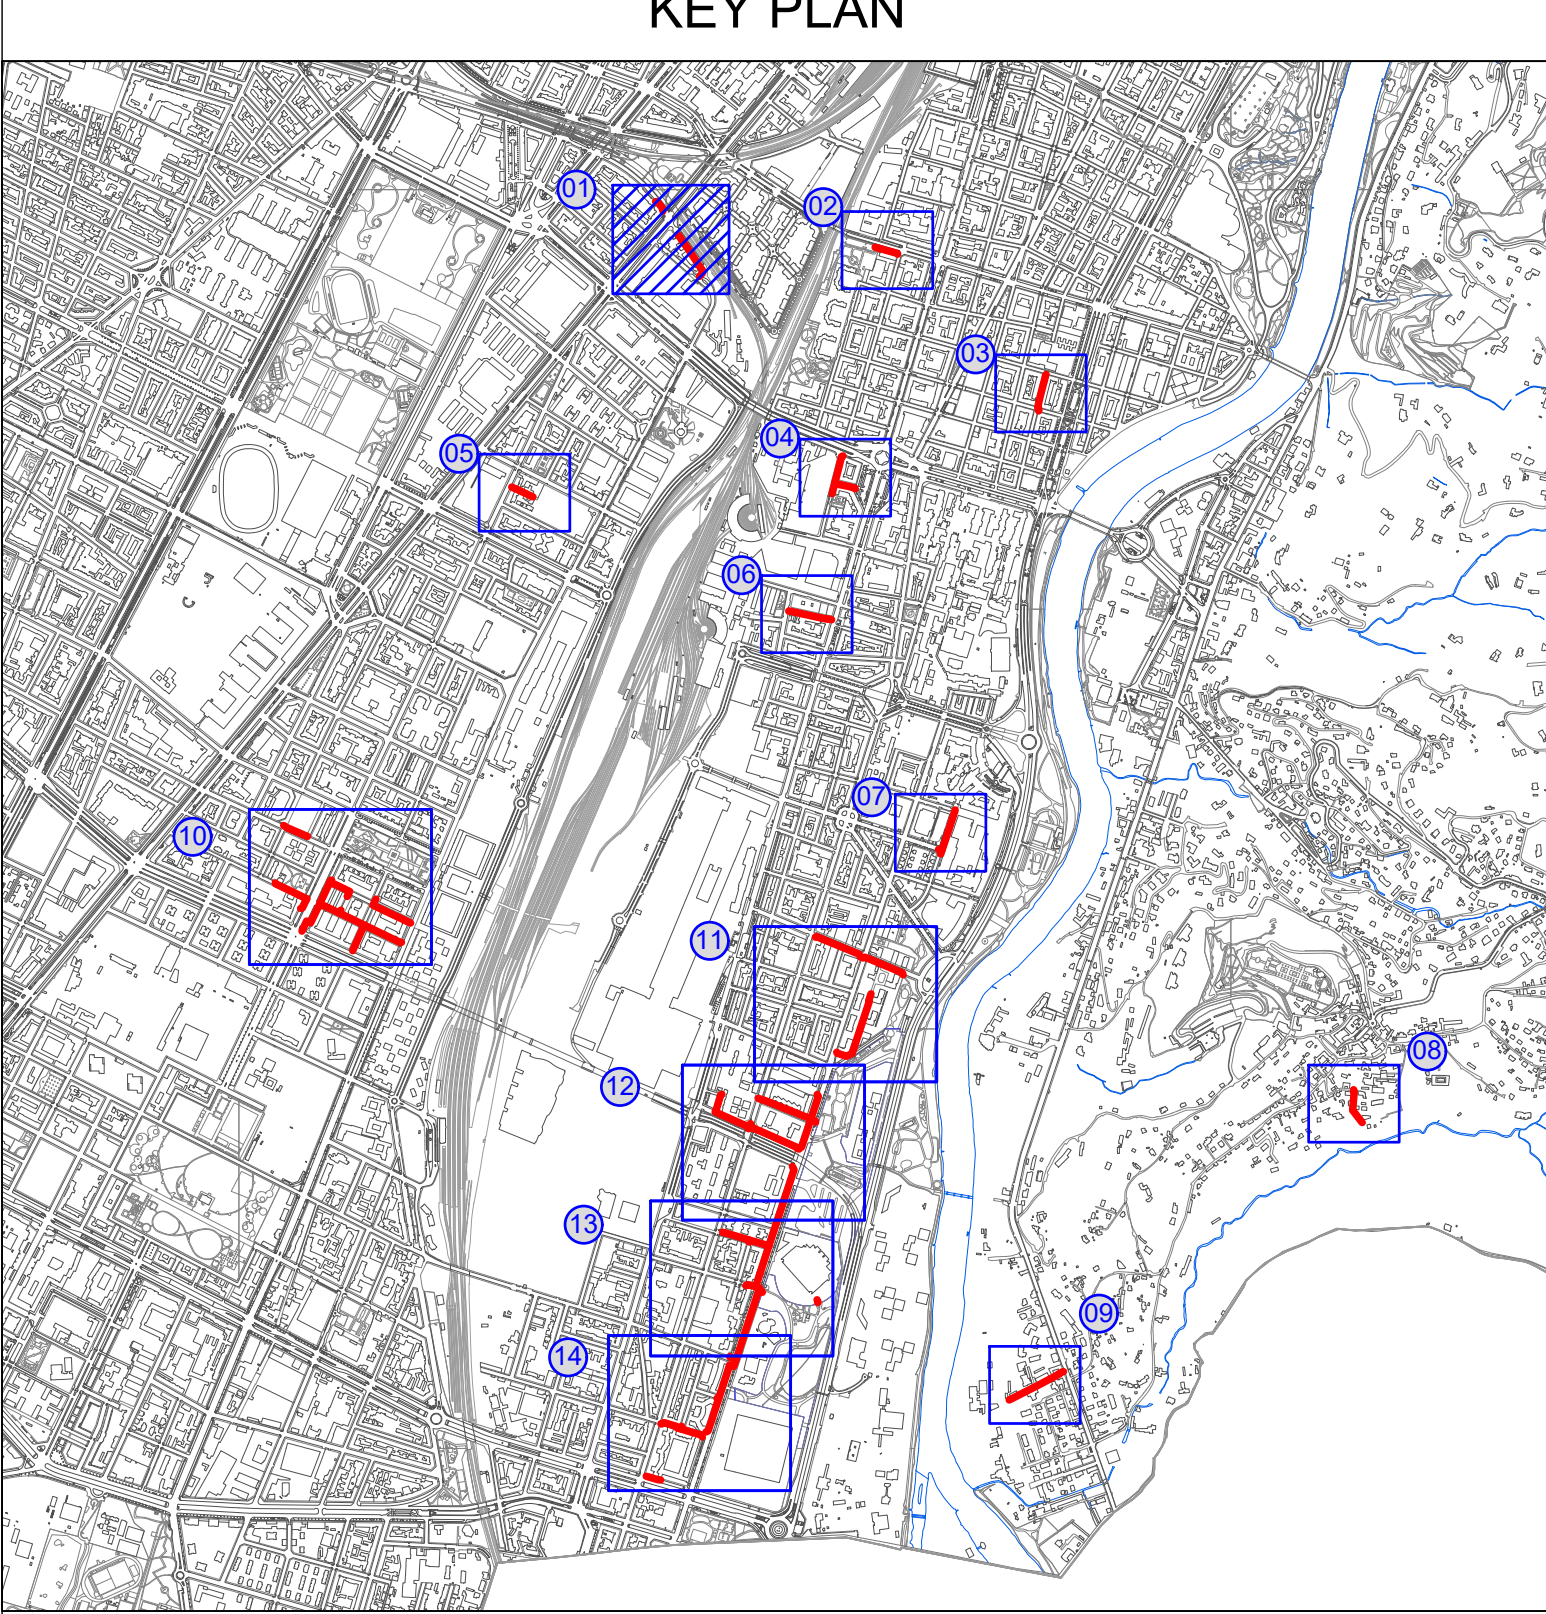


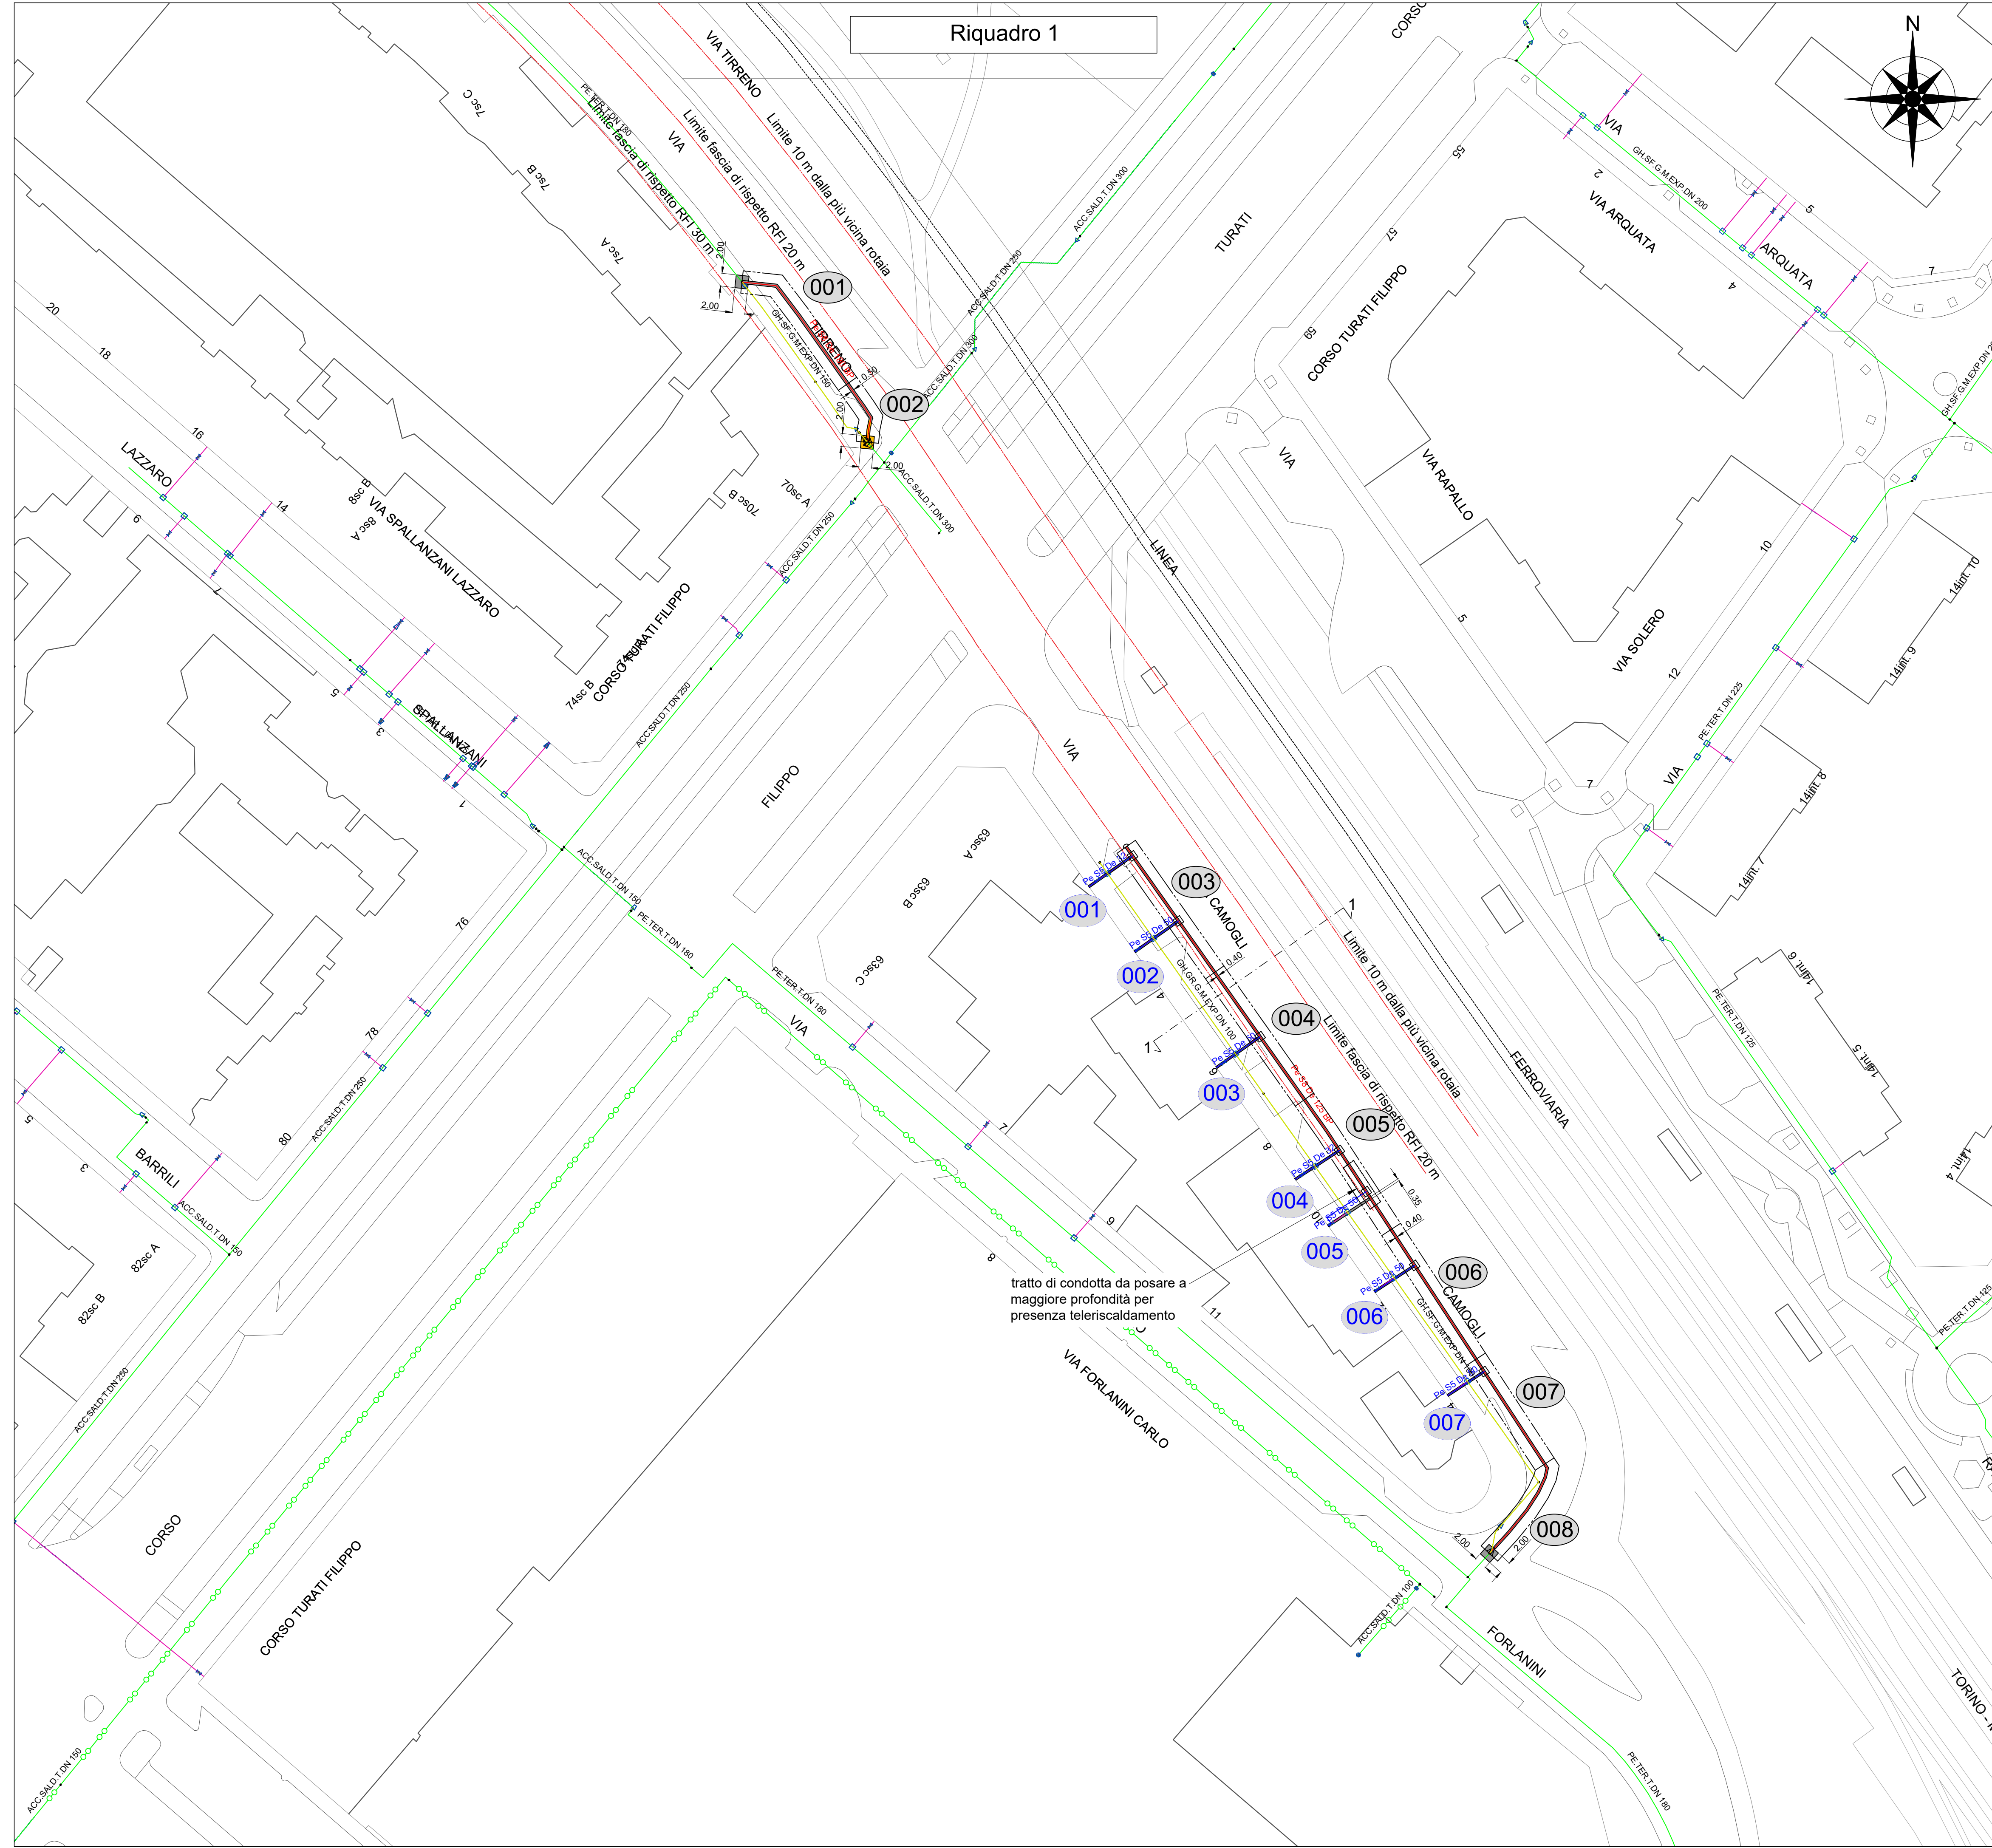

LEGENDA

	Rete in progetto		n° Zona di lavoro
	Rete da rimuovere		n° I.D.U. in progetto
	Zona di lavoro		Area scavi asfalto
	I.D.U. in progetto		Area scavi sterrato
	Tubazione I.D.U. esistente		Area scavi autobloccanti

Riepilogo Scavi									
dati condotta		scavo				tipo superficie	volume rifiuti [mc]	tipo di terreno	volume terre e rocce [mc]
caratteristiche	bar	lung. [m]	largh. [m]	h superf. [m]	h terr. [m]				
Pe S8 De 315	BP	3	0,55	0,1	1,32	Autobloccanti	0,17	di riporto	2,17
Pe S8 De 315	BP	1261	0,55	0,15	1,27	Asfalto	104,03	di riporto	877,34
Pe S8 De 225	BP	218	0,50	0,15	1,18	Asfalto	16,35	di riporto	128,08
Pe S8 De 180	BP	1832,5	0,50	0,15	1,13	Asfalto	137,44	di riporto	1035,36
Pe S8 De 180	BP	31	0,50	0,00	1,28	Sterrato	0,00	di riporto	19,84
Pe S8 De 180	BP	0,5	0,50	0,10	1,18	Autobloccanti	0,03	di riporto	0,30
Pe S8 De 125	BP	8	0,40	0,00	1,23	Sterrato	0,00	di riporto	3,92
Pe S8 De 125	BP	817	0,40	0,15	1,08	Asfalto	49,02	di riporto	351,31
Acc DN 400 (rimozione)		2	0,75	0,15	1,25	Asfalto	0,23	di riporto	1,88
Acc DN 350 (rimozione)		8	0,75	0,15	1,25	Asfalto	0,90	di riporto	7,50
Pe De 315 (rimozione)		8	0,55	0,15	1,25	Asfalto	0,66	di riporto	5,50
GH DN 300 (rimozione)		2	0,55	0,15	1,25	Asfalto	0,17	di riporto	1,38
Acc DN 300 (rimozione)		5	0,55	0,15	1,25	Asfalto	0,41	di riporto	3,44
GH DN 250 (rimozione)		894	0,55	0,15	1,20	Asfalto	73,76	di riporto	590,04
Acc DN 250 (rimozione)		77	0,55	0,15	1,20	Asfalto	6,35	di riporto	50,82
Acc DN 250 (rimozione)		54	0,55	0,10	1,25	Autobloccanti	2,97	di riporto	37,13
GH DN 250 (rimozione)		4	0,55	0,10	1,25	Autobloccanti	0,22	di riporto	2,75
GH DN 250 (rimozione)		19	0,55	0,00	1,35	Sterrato	0,00	di riporto	14,11
Pe De 225 (rimozione)		2	0,50	0,15	1,18	Asfalto	0,15	di riporto	1,18
Acc DN 200 (rimozione)		3	0,50	0,15	1,15	Asfalto	0,23	di riporto	1,73
GH DN 200 (rimozione)		220	0,50	0,15	1,15	Asfalto	16,50	di riporto	126,50
Pe De 180 (rimozione)		41	0,50	0,15	1,13	Asfalto	3,08	di riporto	23,17
GH DN 150 (rimozione)		1634	0,50	0,15	1,10	Asfalto	122,55	di riporto	898,70
GH DN 150 (rimozione)		56	0,50	0,10	1,15	Autobloccanti	2,80	di riporto	32,20
Acc DN 150 (rimozione)		447	0,50	0,15	1,10	Asfalto	33,53	di riporto	245,85
Pe De 125 (rimozione)		25	0,40	0,15	1,08	Asfalto	1,50	di riporto	10,75
GH DN 100 (rimozione)		8	0,40	0,00	1,20	Sterrato	0,00	di riporto	3,84
Acc DN 100 (rimozione)		102	0,40	0,15	1,05	Asfalto	6,12	di riporto	42,84
GH DN 100 (rimozione)		648	0,40	0,15	1,05	Asfalto	38,88	di riporto	272,16
Pe De 90 (rimozione)		8	0,40	0,15	1,04	Asfalto	0,36	di riporto	2,50
GH DN 80 (rimozione)		52	0,40	0,15	1,03	Asfalto	3,12	di riporto	21,42
Parziale							621,65		4815,94
Scarifica aggiuntiva							1988,17		0,00
Scarifica IDU							142,38		284,58
Buche di inserimento							30,60		236,64
Totale							2782,79		5337,16

Progettista: INGEGNERIA PROV. ALESSANDRIA
Ordine degli Ingegneri di Alessandria
matr. n° 2109

Unità Responsabile della Progettazione
INGEAL-INGE-PROGRE


Progetto n°: 21-0584-3E-00-001272
WBS: SI.20.10300.02.1109
ALLEGATO n°: 5.1

Descrizione:
Nome File:
Formato: A1 Scala: 1 : 500
Committente:

Descrizione:
Emissione per commenti:
Comm.: 2464

0	30	11	22	A.Saronni	L.Cartasegna	A.Leardi
Rev.	G.	M.	A.	Redatto	Controllato	Approvato

Comune di TORINO (TO)
Vie Varie
Progetto Esecutivo
SOSTITUZIONE RETE BP (L=2745,39 M) - GARA TO 1
Intervento n° SI-036213-001272-TSS-TORIN008
Planimetria d'insieme con rete - Tavola 1

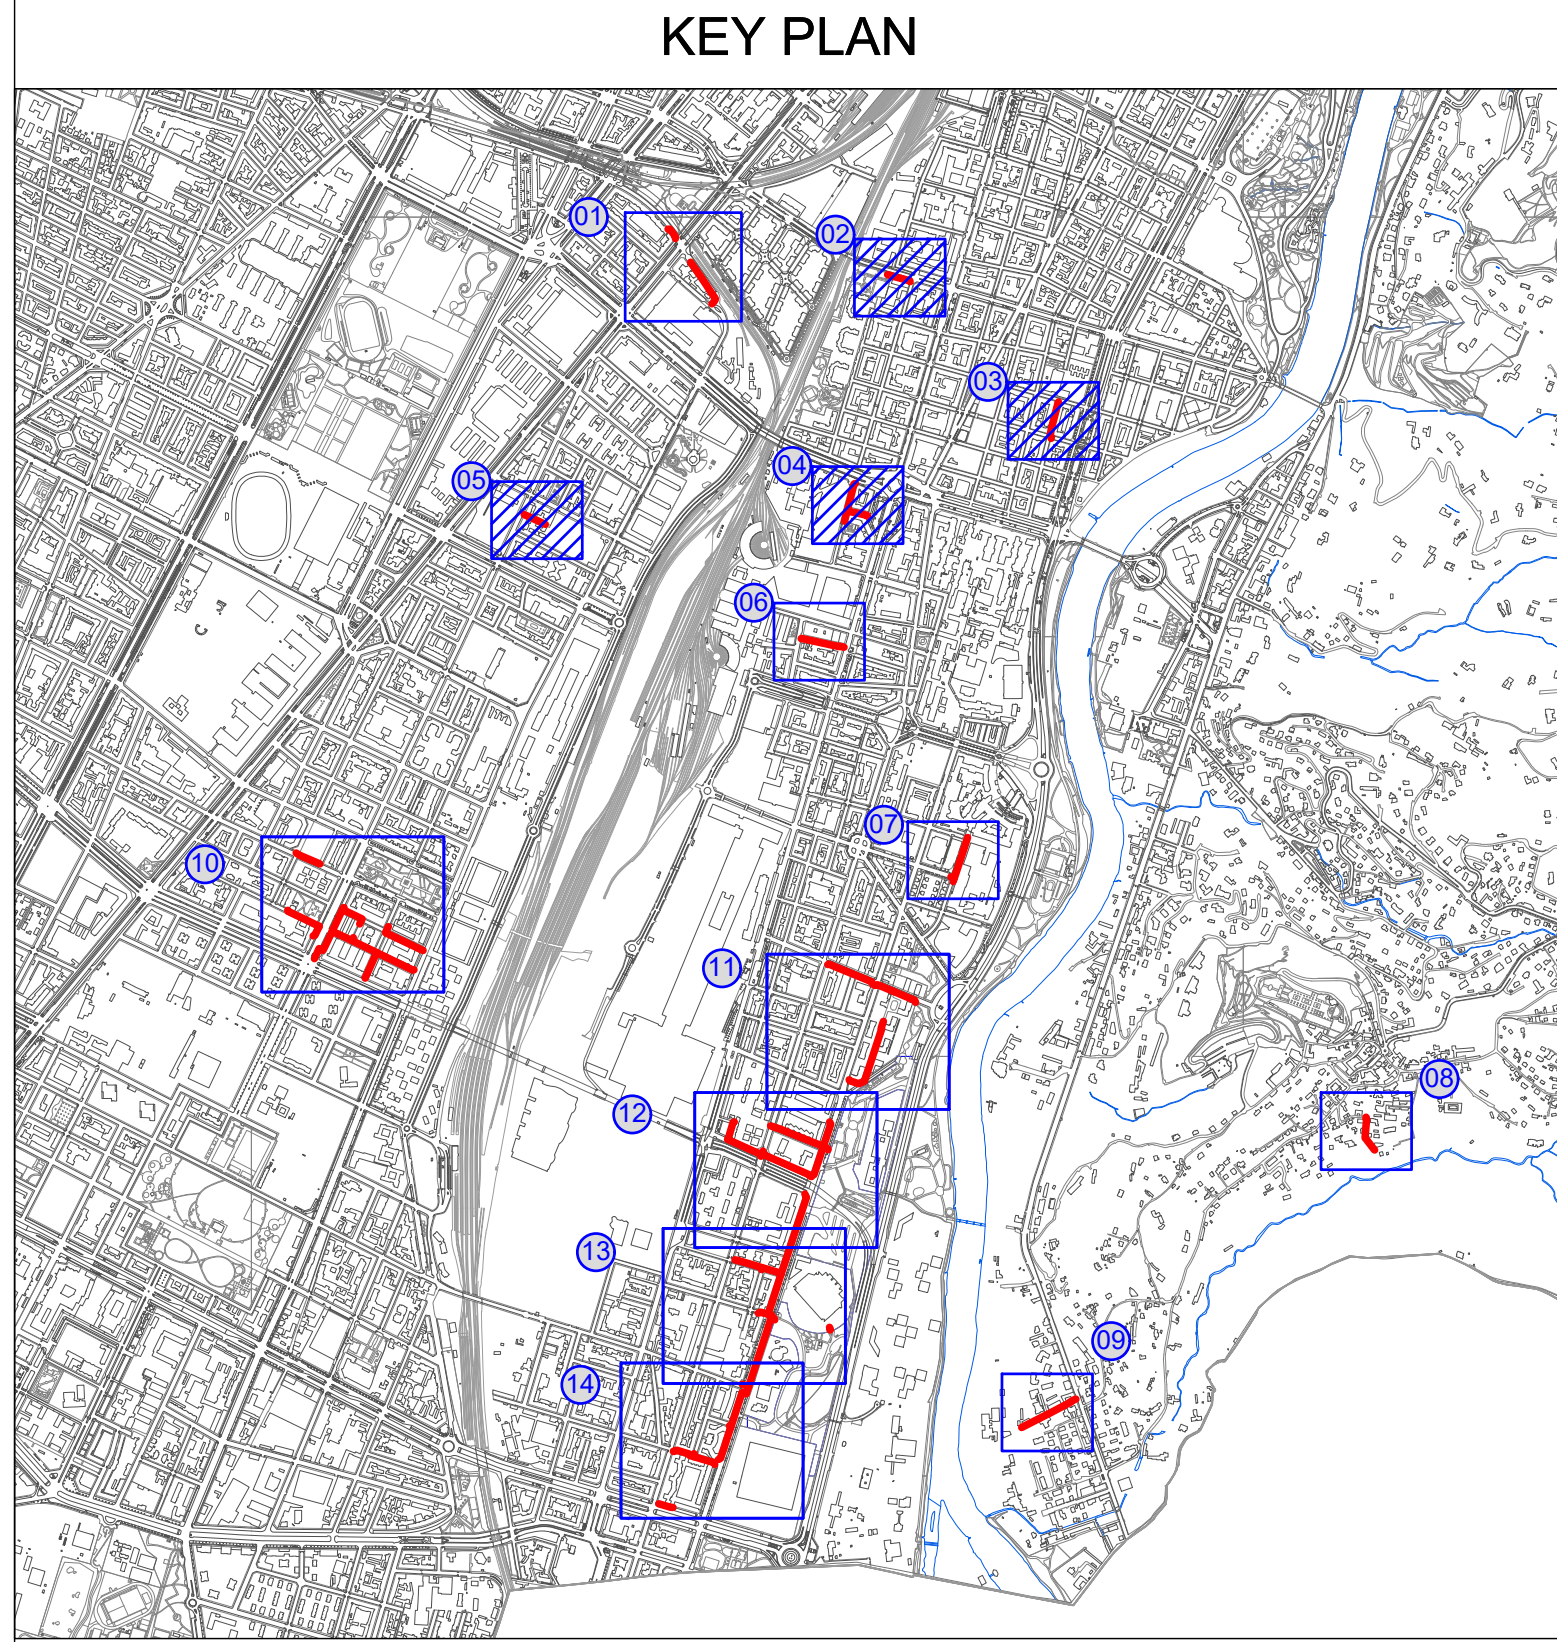

LEGENDA

	Reti in progetto		n° Zona di lavoro
	Reti da rimuovere		n° I.D.U. in progetto
	Zona di lavoro		Area scavi asfalto
	I.D.U. in progetto		Area scavi sinterato
	Tubazione I.D.U. esistente		Area scavi autobloccanti

dati condotta		scavo		Replagio: Scavi		tipo superficie	volume rifili [mc]	tipo di terreno	volume terra e rocce [mc]
caratteristiche	bar	lung. [m]	largh. [m]	h superf. [m]	h terr. [m]				
Re SS De 315	BP	3	0,55	0,1	1,32	Autobloccanti	0,17	di riporto	2,17
Re SS De 315	BP	1261	0,55	0,15	1,27	Asfalto	104,03	di riporto	877,34
Re SS De 225	BP	219	0,50	0,15	1,18	Asfalto	15,35	di riporto	120,08
Re SS De 180	BP	1632,5	0,50	0,15	1,13	Asfalto	137,44	di riporto	1035,36
Re SS De 180	BP	31	0,50	0,00	1,28	Sterrato	0,00	di riporto	19,84
Re SS De 180	BP	0,5	0,50	0,10	1,18	Autobloccanti	0,03	di riporto	0,30
Re SS De 125	BP	8	0,40	0,00	1,23	Sterrato	0,00	di riporto	3,92
Re SS De 125	BP	817	0,40	0,15	1,08	Asfalto	49,02	di riporto	351,31
Acc DN 400 (rimozione)		2	0,75	0,15	1,25	Asfalto	0,23	di riporto	1,88
Acc DN 350 (rimozione)		8	0,75	0,15	1,25	Asfalto	0,80	di riporto	7,50
Re De 315 (rimozione)		8	0,55	0,15	1,25	Asfalto	0,66	di riporto	5,50
GH DN 300 (rimozione)		2	0,55	0,15	1,25	Asfalto	0,17	di riporto	1,38
Acc DN 300 (rimozione)		5	0,55	0,15	1,25	Asfalto	0,41	di riporto	3,44
GH DN 250 (rimozione)		884	0,55	0,15	1,20	Asfalto	73,76	di riporto	590,04
Acc DN 250 (rimozione)		77	0,55	0,15	1,20	Asfalto	6,35	di riporto	50,82
Acc DN 250 (rimozione)		54	0,55	0,10	1,25	Autobloccanti	2,97	di riporto	37,13
GH DN 250 (rimozione)		4	0,55	0,10	1,25	Autobloccanti	0,22	di riporto	2,75
GH DN 250 (rimozione)		19	0,55	0,00	1,35	Sterrato	0,00	di riporto	14,11
Re De 225 (rimozione)		2	0,50	0,15	1,18	Asfalto	0,15	di riporto	1,18
Acc DN 200 (rimozione)		3	0,50	0,15	1,15	Asfalto	0,23	di riporto	1,73
GH DN 200 (rimozione)		220	0,50	0,15	1,15	Asfalto	16,50	di riporto	128,50
Re De 180 (rimozione)		41	0,50	0,15	1,13	Asfalto	3,08	di riporto	23,17
GH DN 150 (rimozione)		1634	0,50	0,15	1,10	Asfalto	122,55	di riporto	898,70
GH DN 150 (rimozione)		58	0,50	0,10	1,15	Autobloccanti	1,90	di riporto	22,38
Acc DN 150 (rimozione)		447	0,50	0,15	1,10	Asfalto	33,53	di riporto	245,85
Re De 125 (rimozione)		25	0,40	0,15	1,08	Asfalto	1,50	di riporto	10,75
GH DN 100 (rimozione)		8	0,40	0,00	1,20	Sterrato	0,00	di riporto	3,84
Acc DN 100 (rimozione)		102	0,40	0,15	1,05	Asfalto	6,12	di riporto	42,84
GH DN 80 (rimozione)		648	0,40	0,15	1,05	Asfalto	36,88	di riporto	272,18
Re De 80 (rimozione)		8	0,40	0,15	1,04	Asfalto	0,36	di riporto	2,50
GH DN 80 (rimozione)		52	0,40	0,15	1,03	Asfalto	3,12	di riporto	21,42
Scarifica aggiuntiva							651,80		4915,94
Scarifica di riporto							1968,17		0,00
Buone di riporto							142,38		284,58
Buone di riporto							30,60		236,04
Totale							2762,79		5337,16

LEARDI



Progetto n°: 21-0584-3E-00-001272
VBS: SI.20.10300.02.1109
ALLEGATO n°: 5.2






Formato: A0 Scale 1: 500

Comune di TORINO (TO)
Via Vane
Progetto Esecutivo
SOSTITUZIONE RETE BP (L=2745,38 M) - GARA TO 1
Intervento n° SI-036213-001272-TSS-TORINO08
Planimetria d'insieme con rete - Tavola 2

Unità Responsabile della Progettazione
INGENER-ANGE-PROGRE

Completato: 0 30 11 20
Revisioni: 0 30 11 20
Redatto: 0 30 11 20
Controllato: 0 30 11 20
Approvato: 0 30 11 20

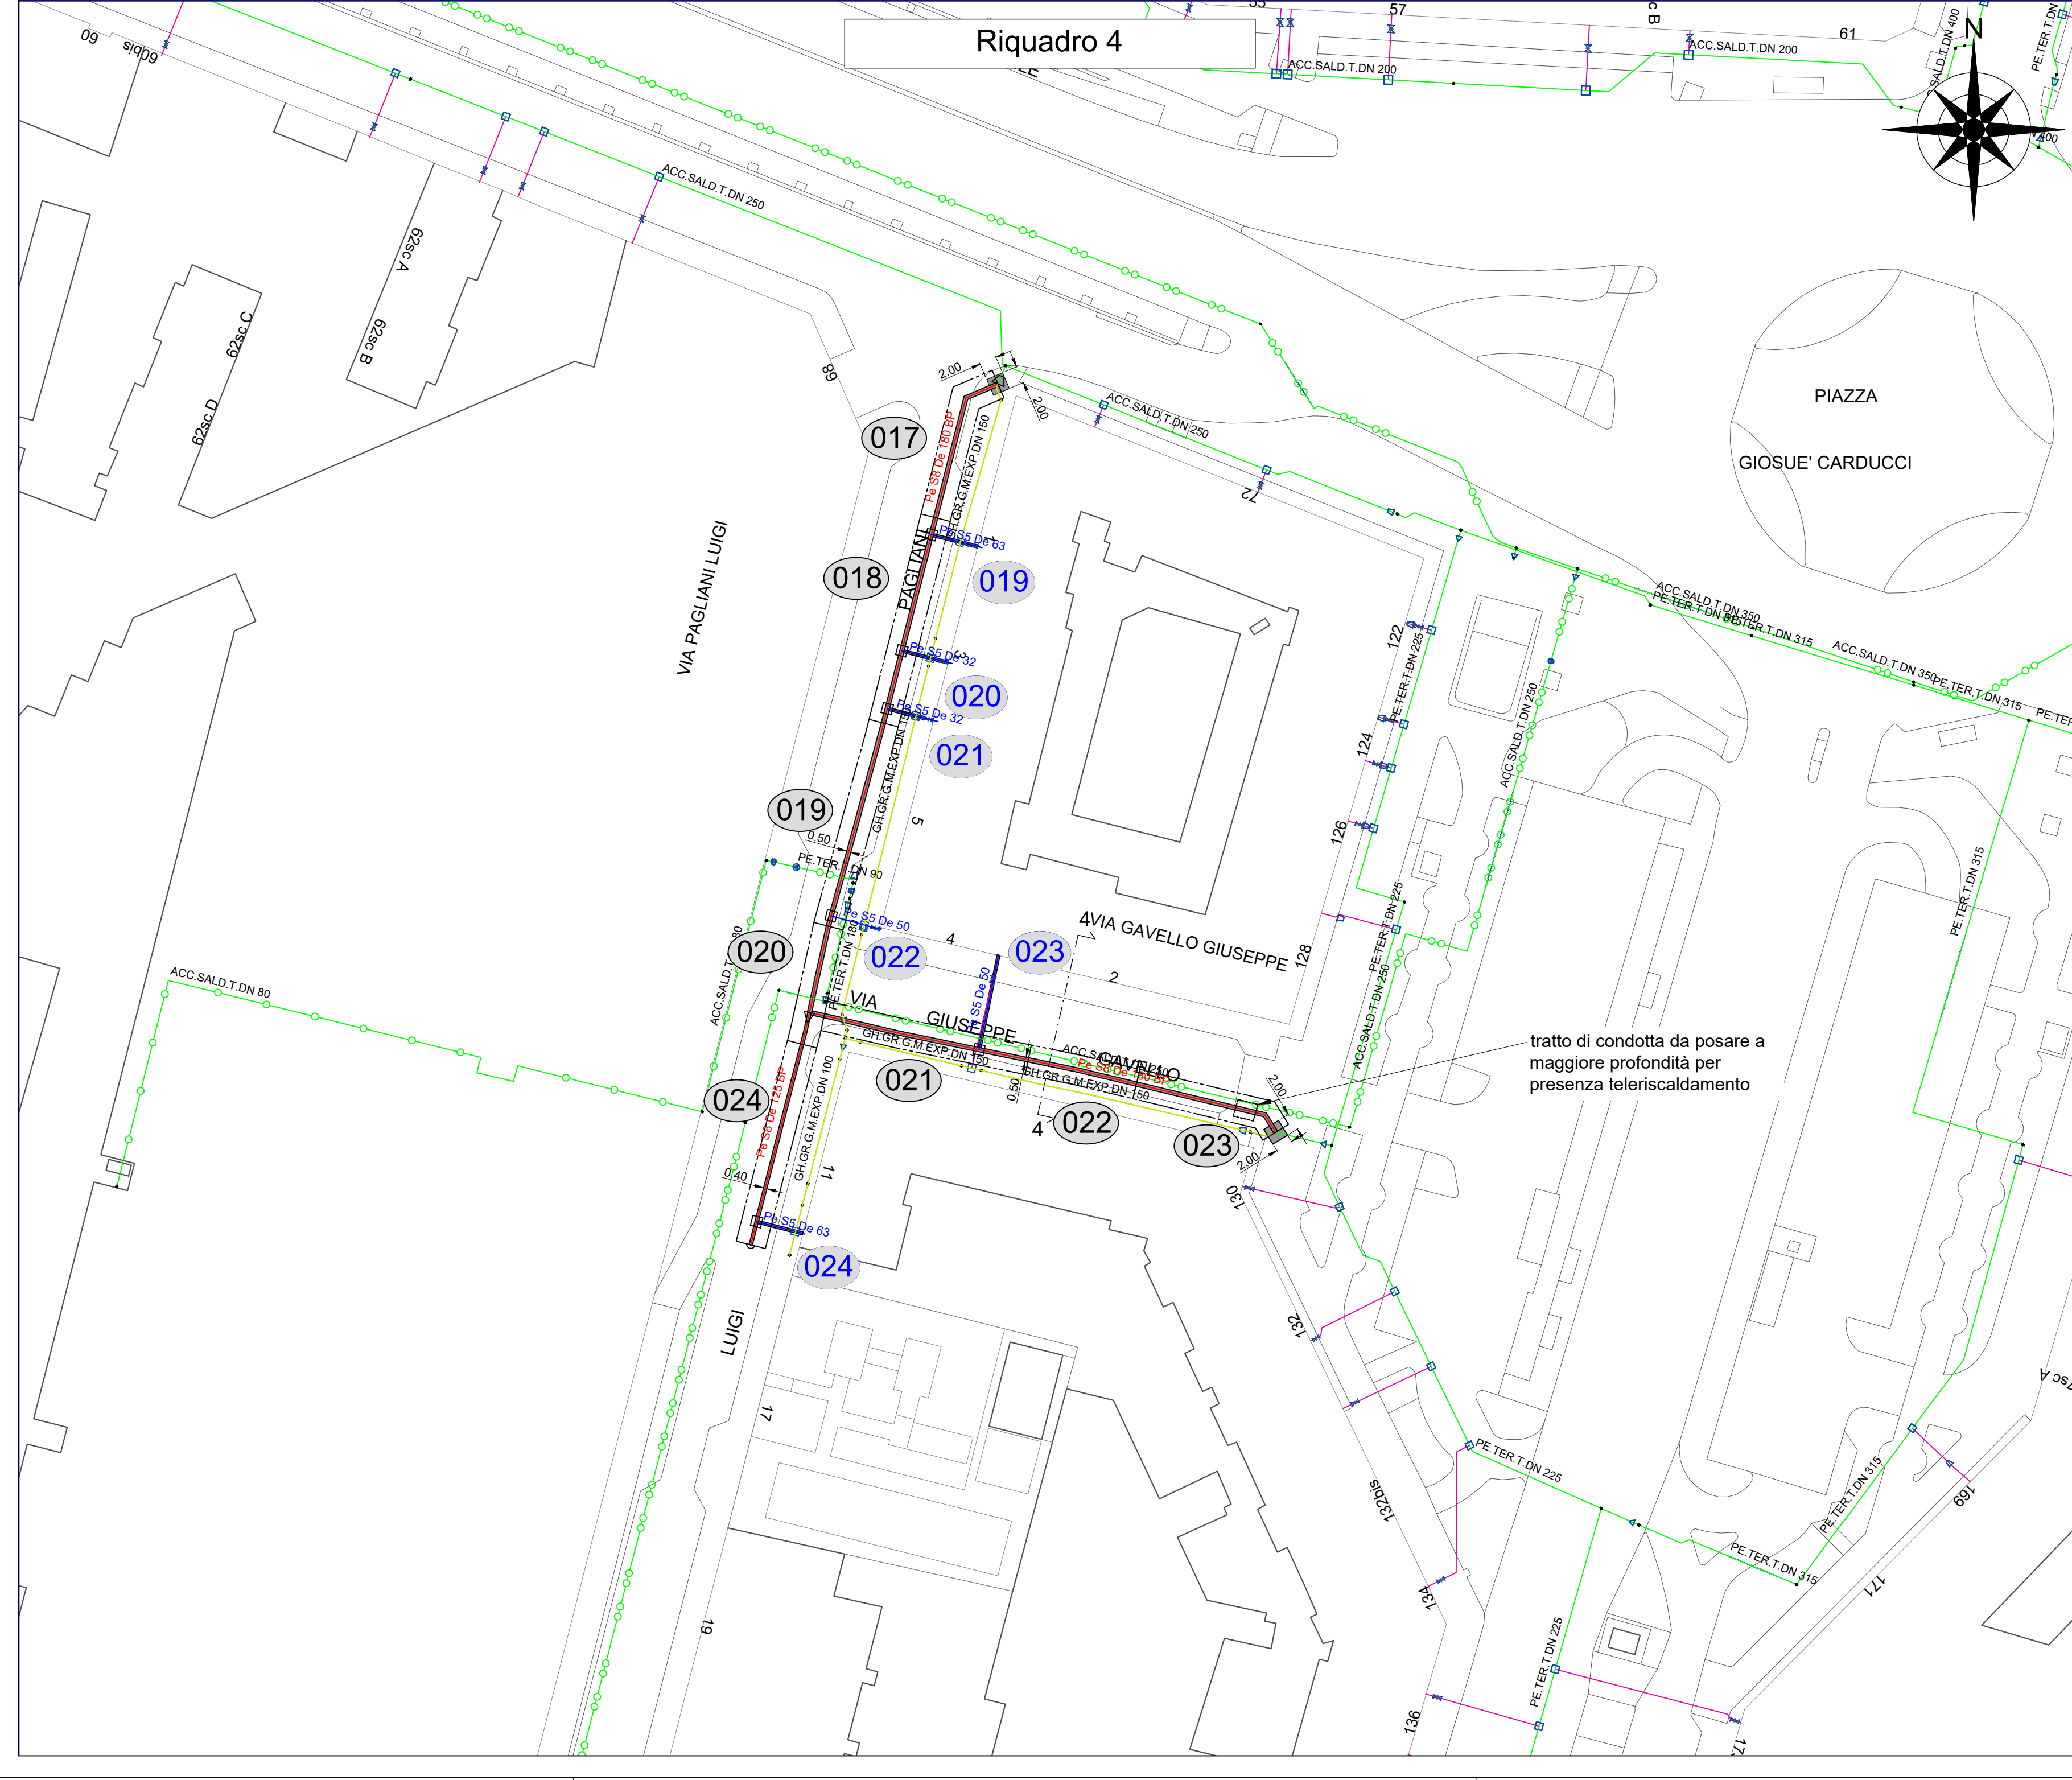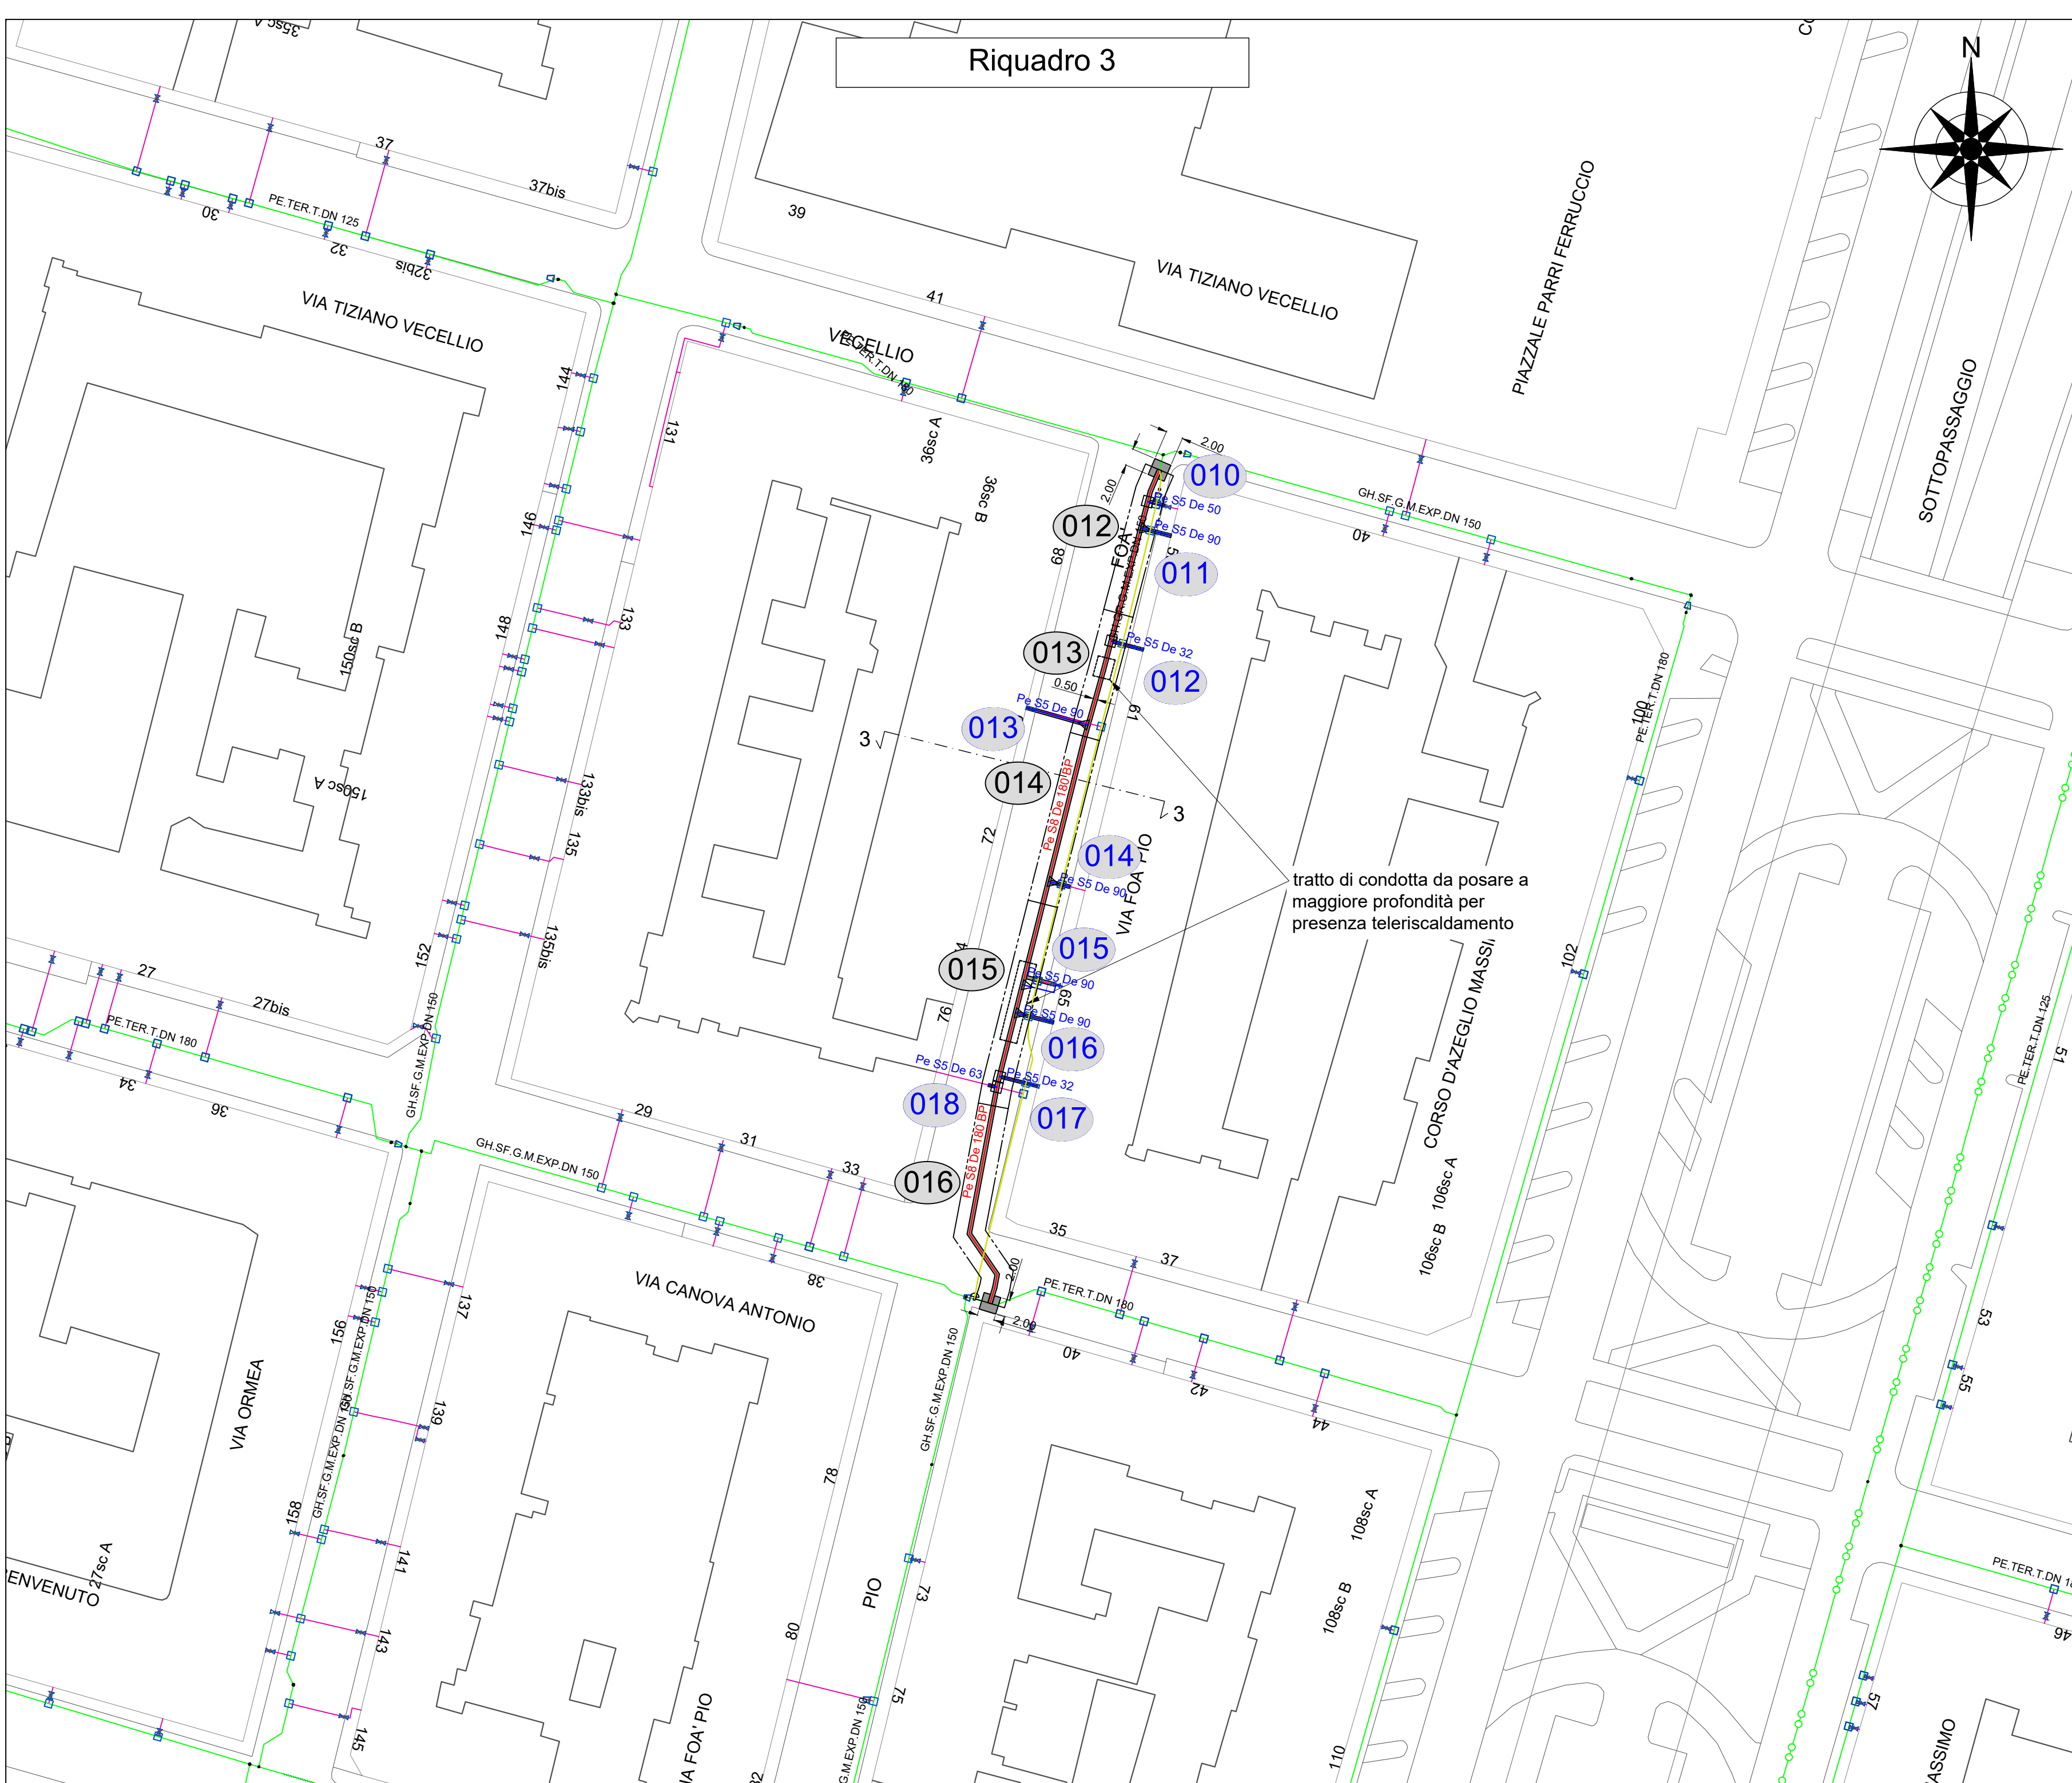

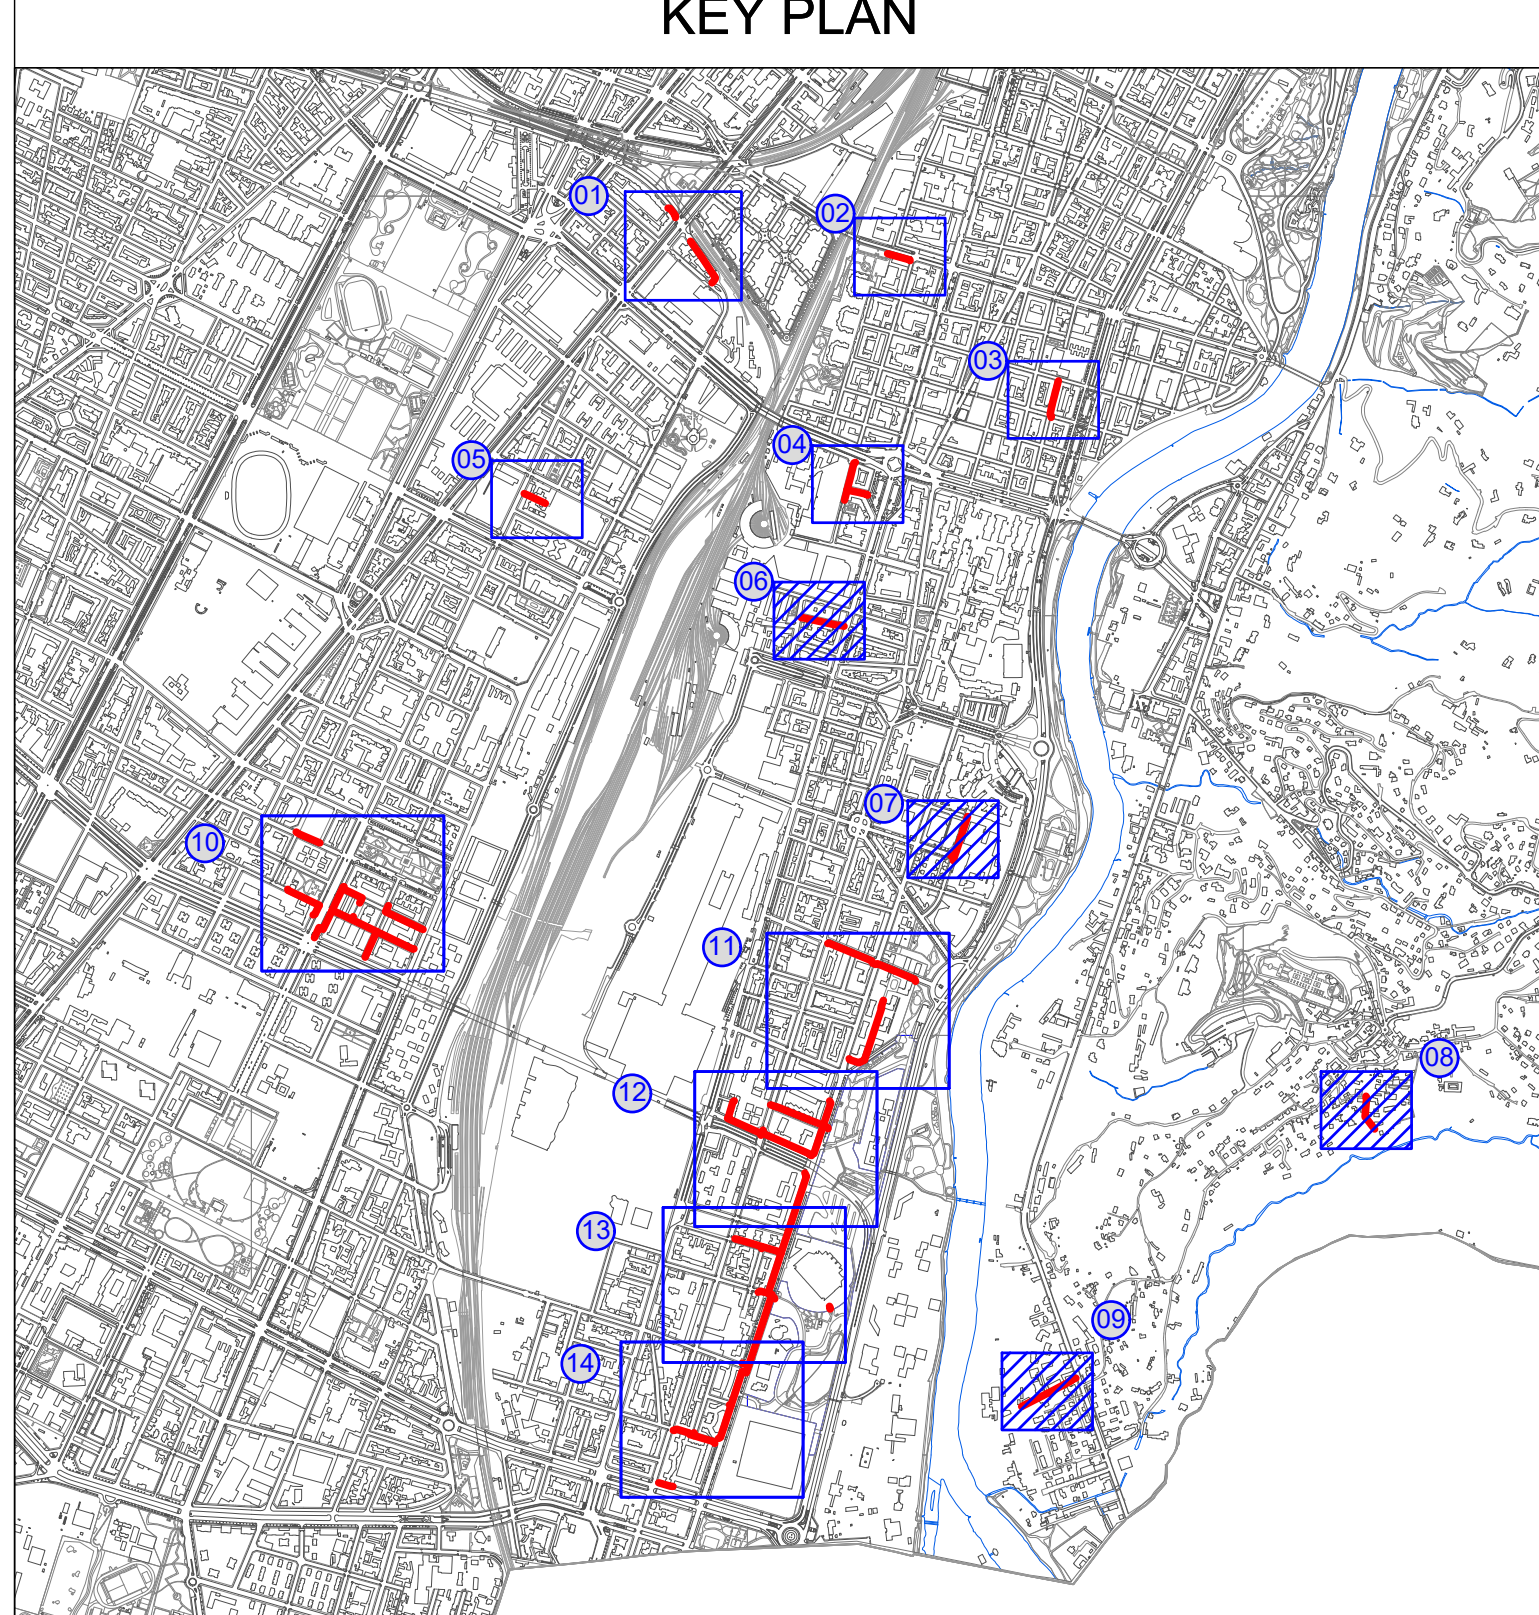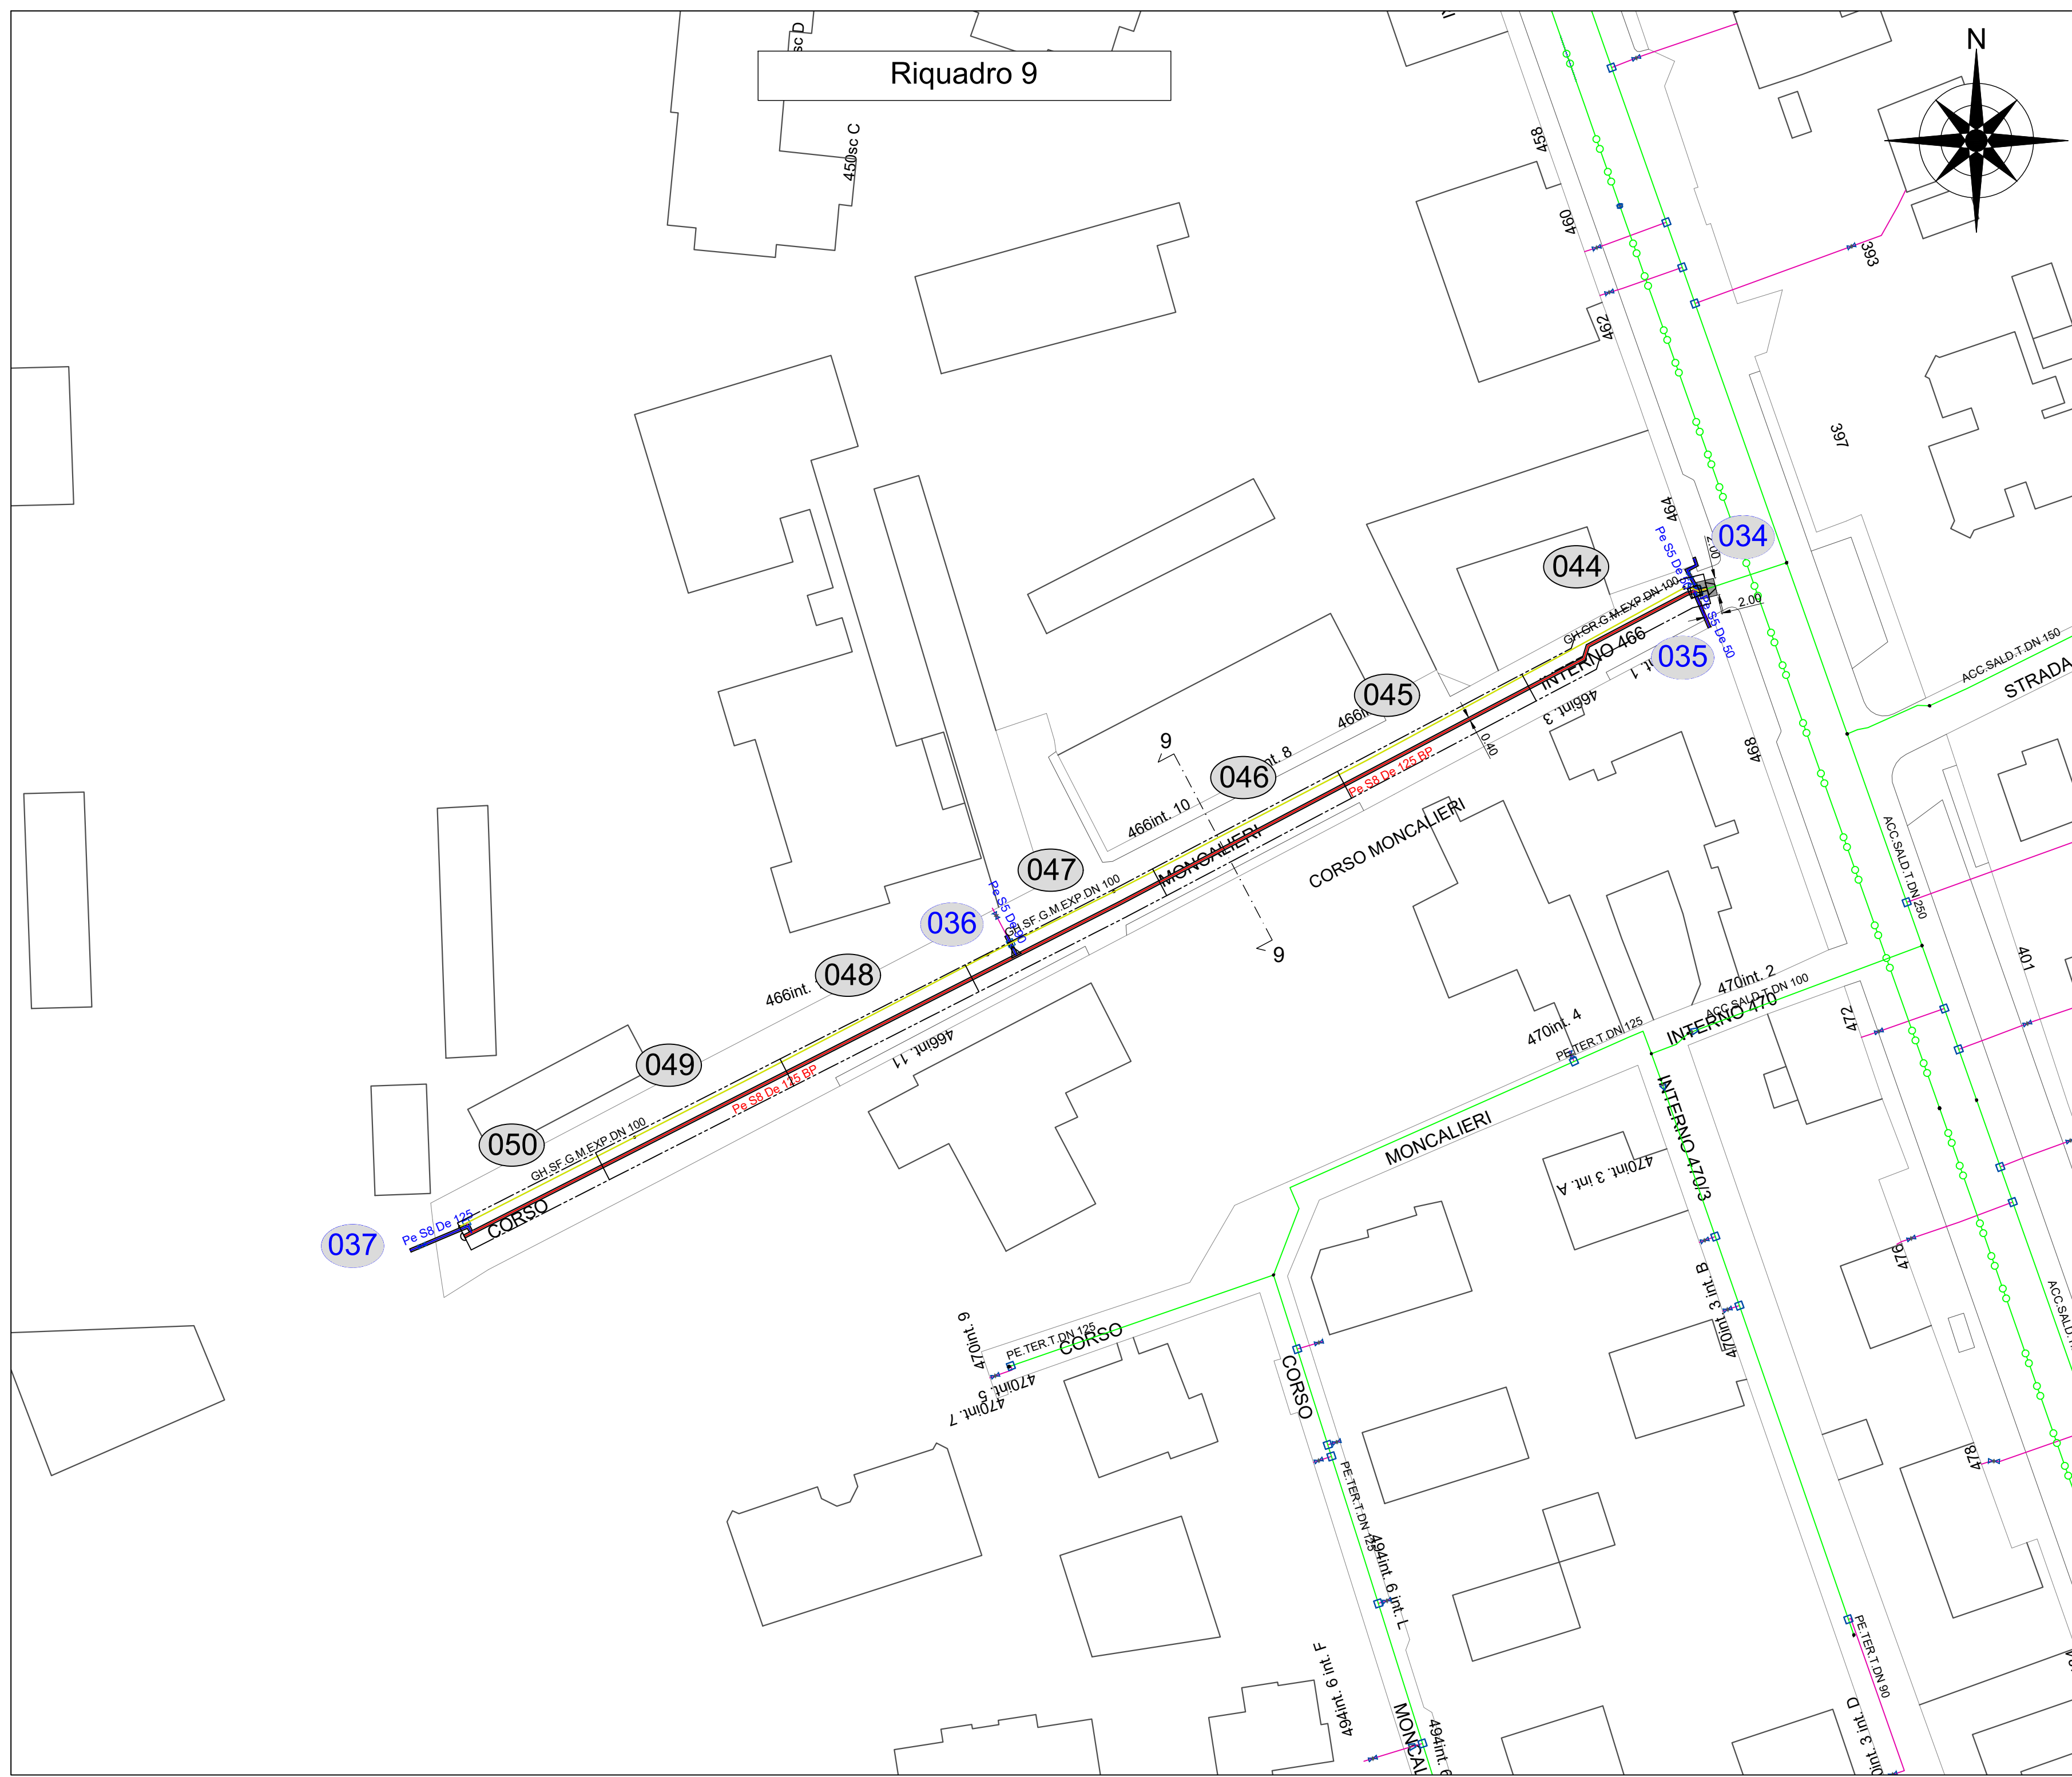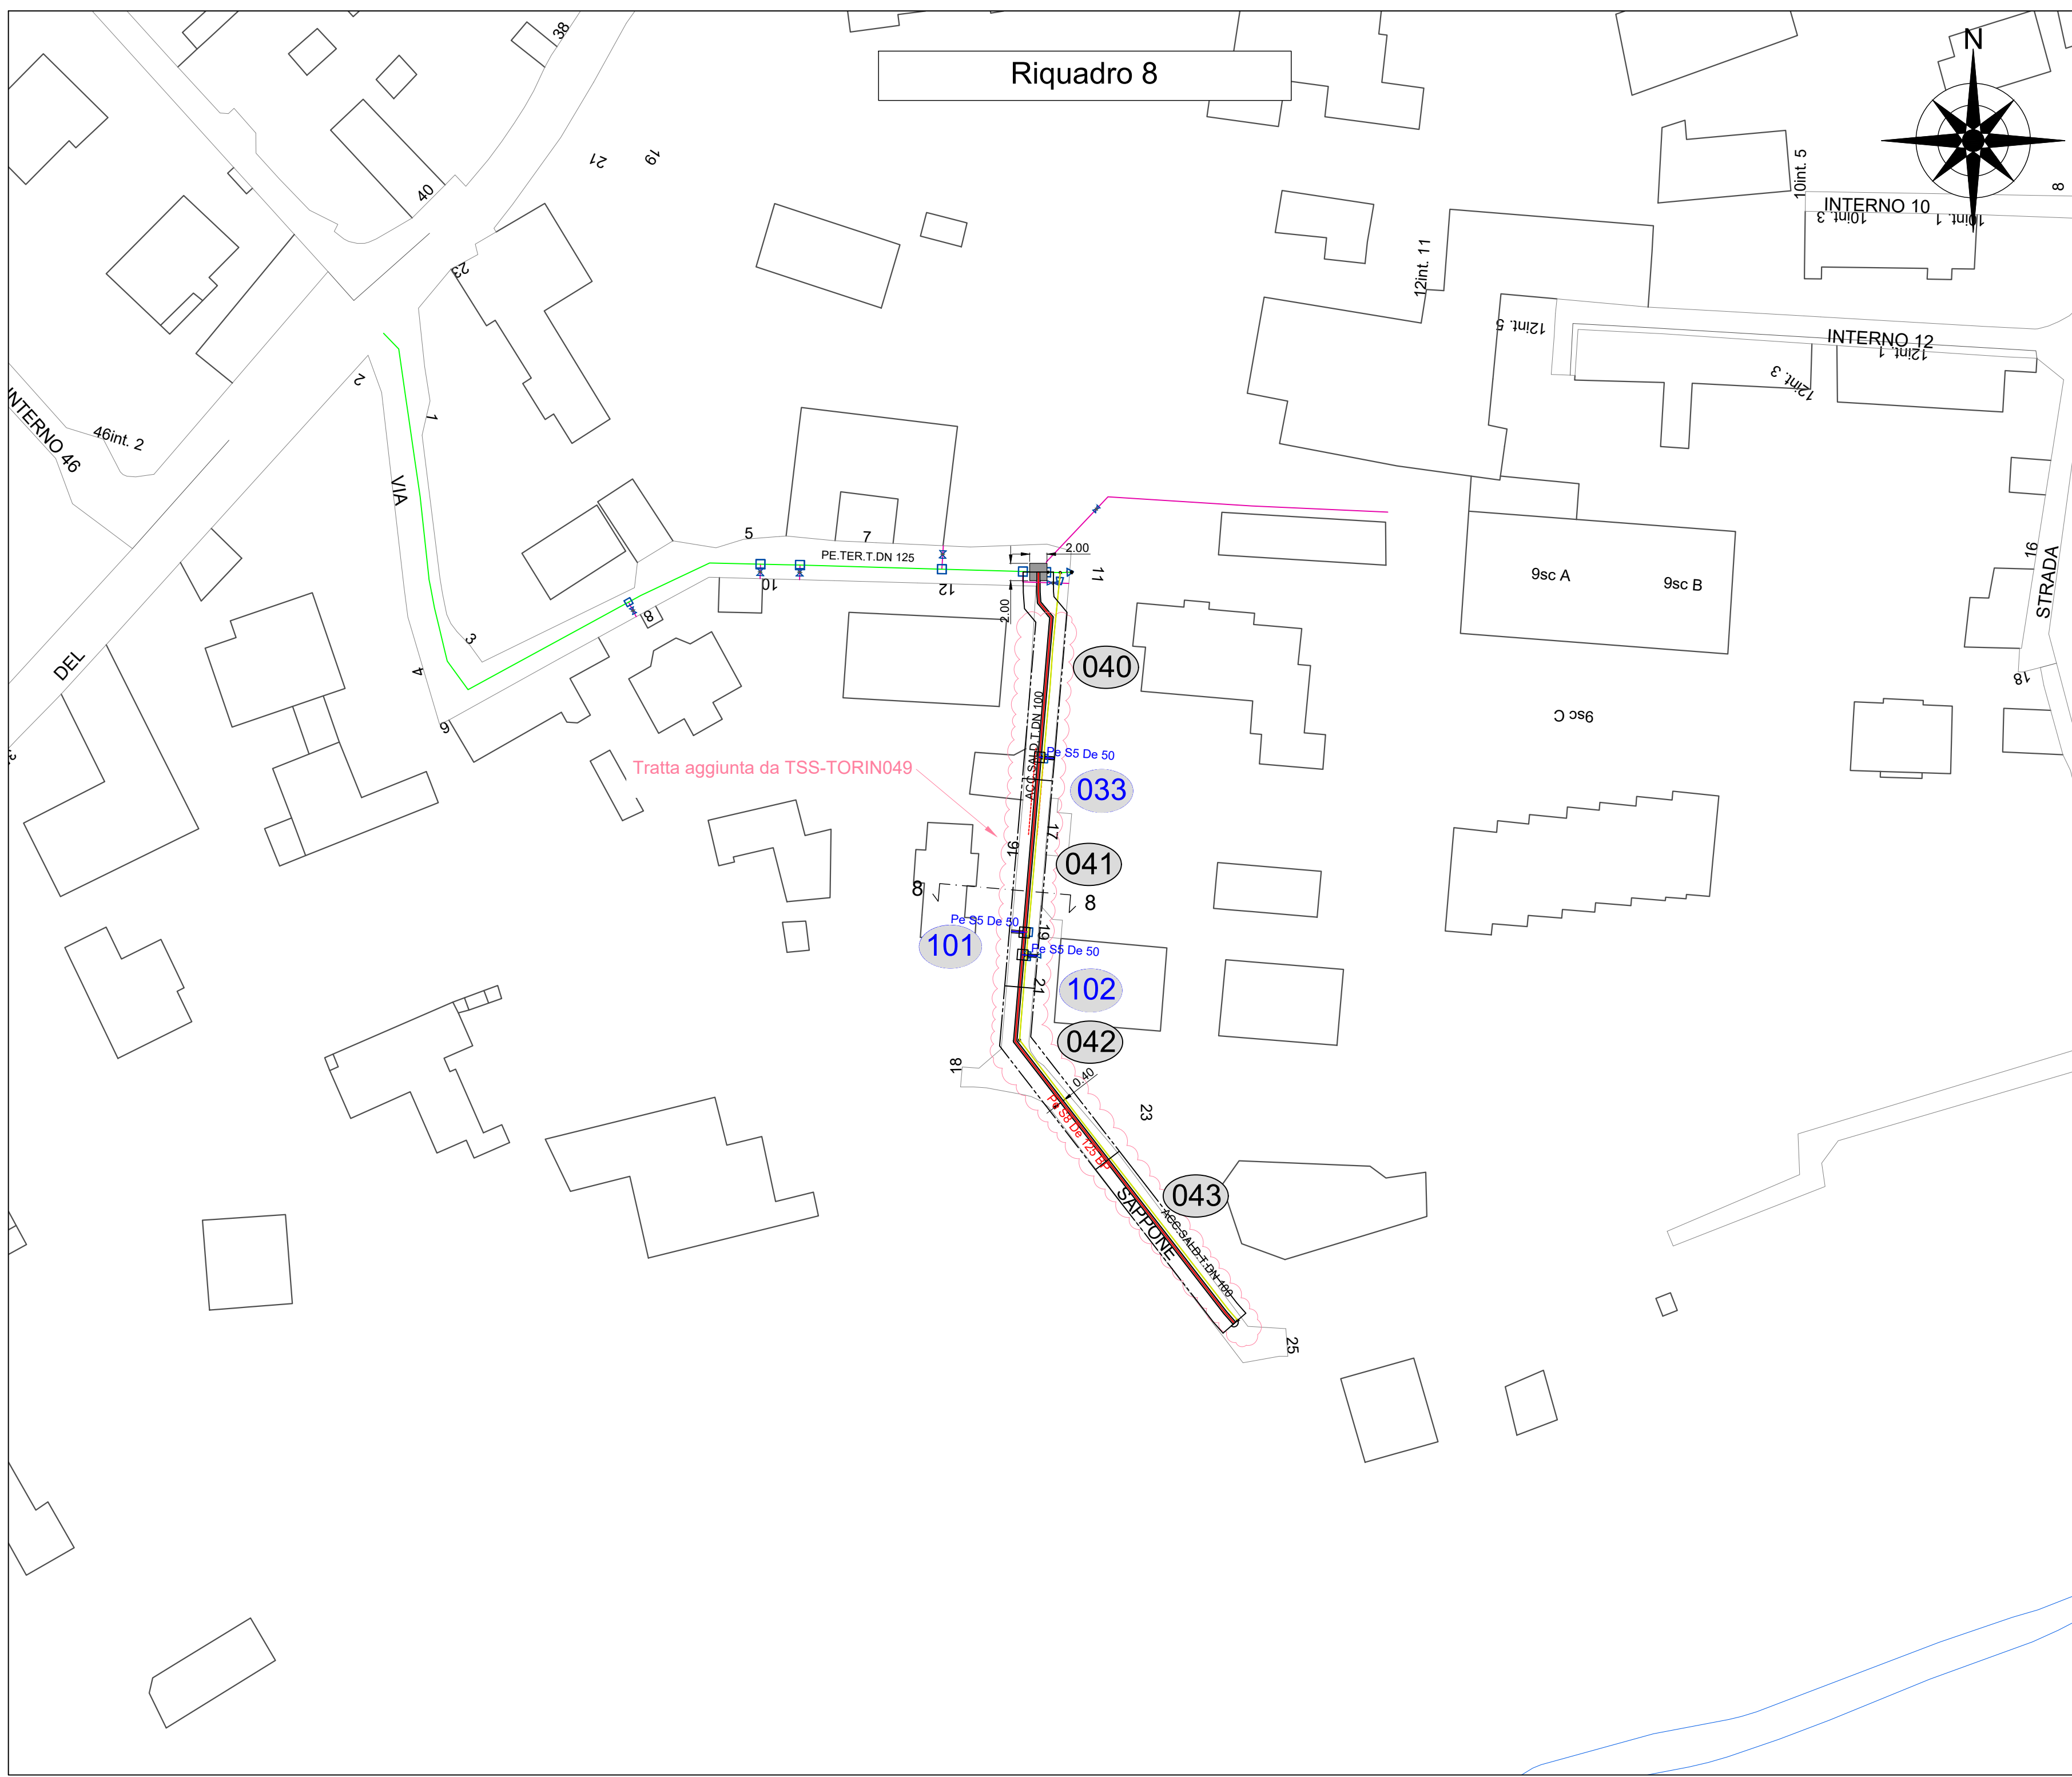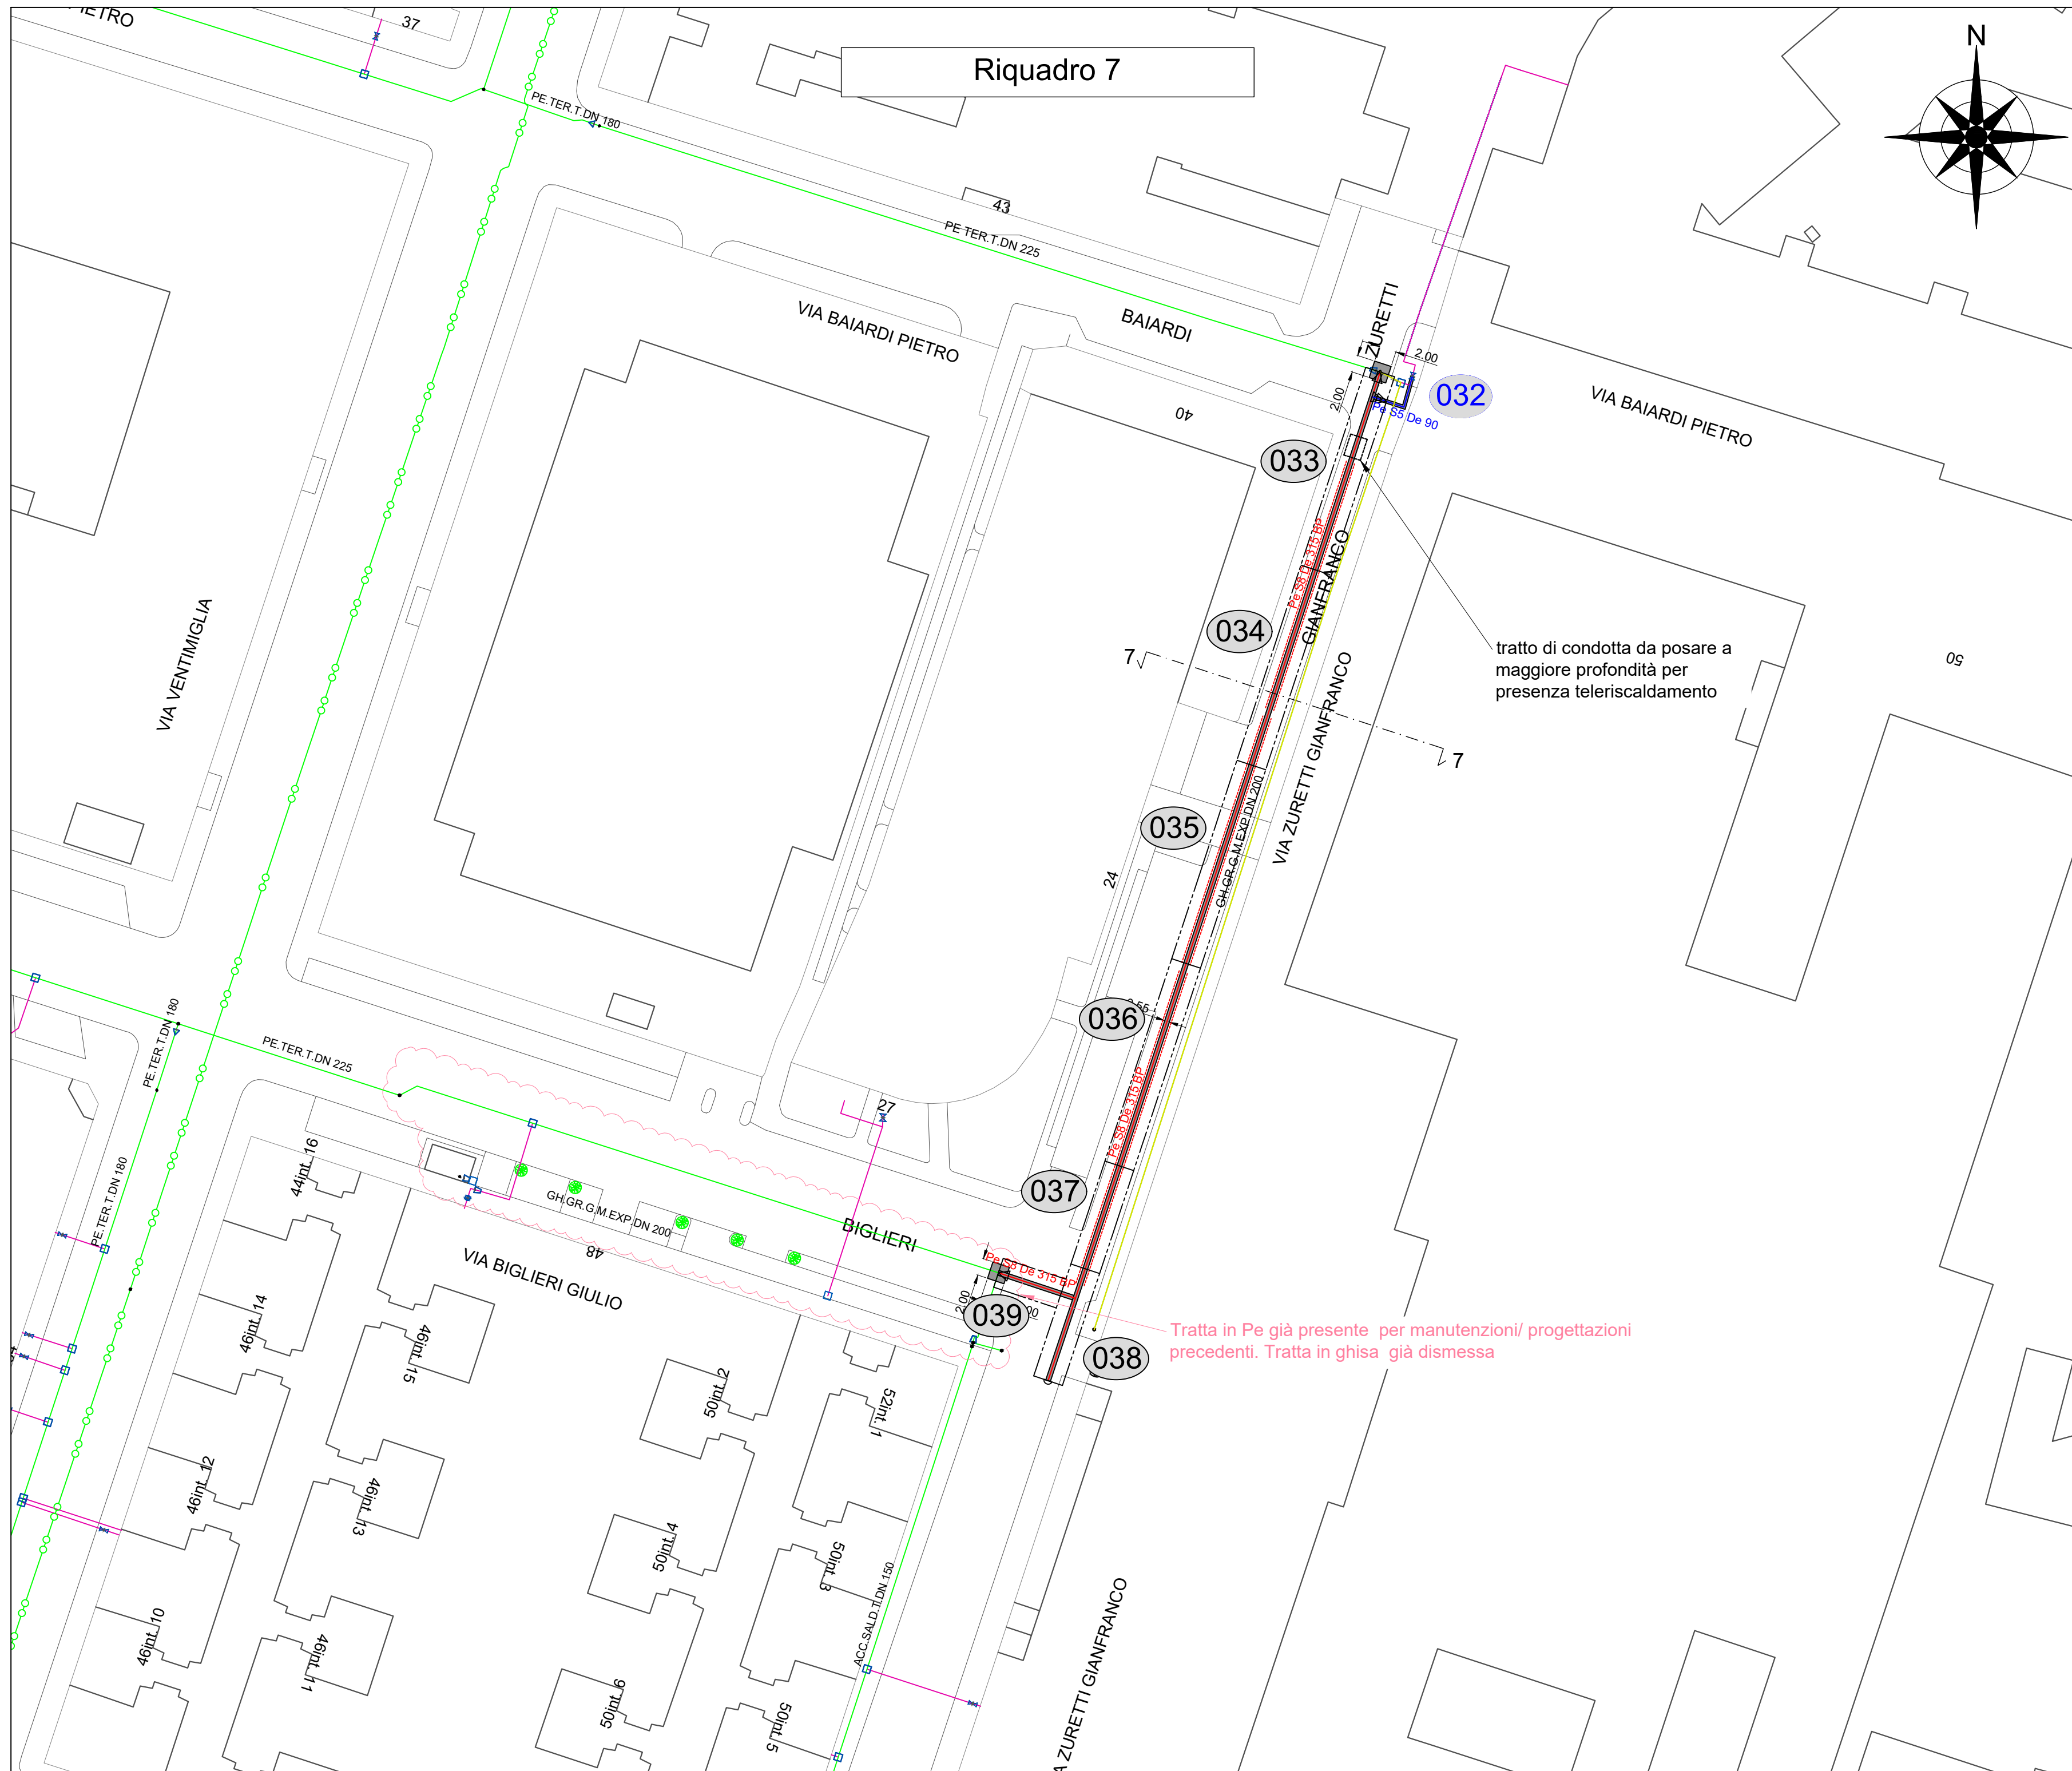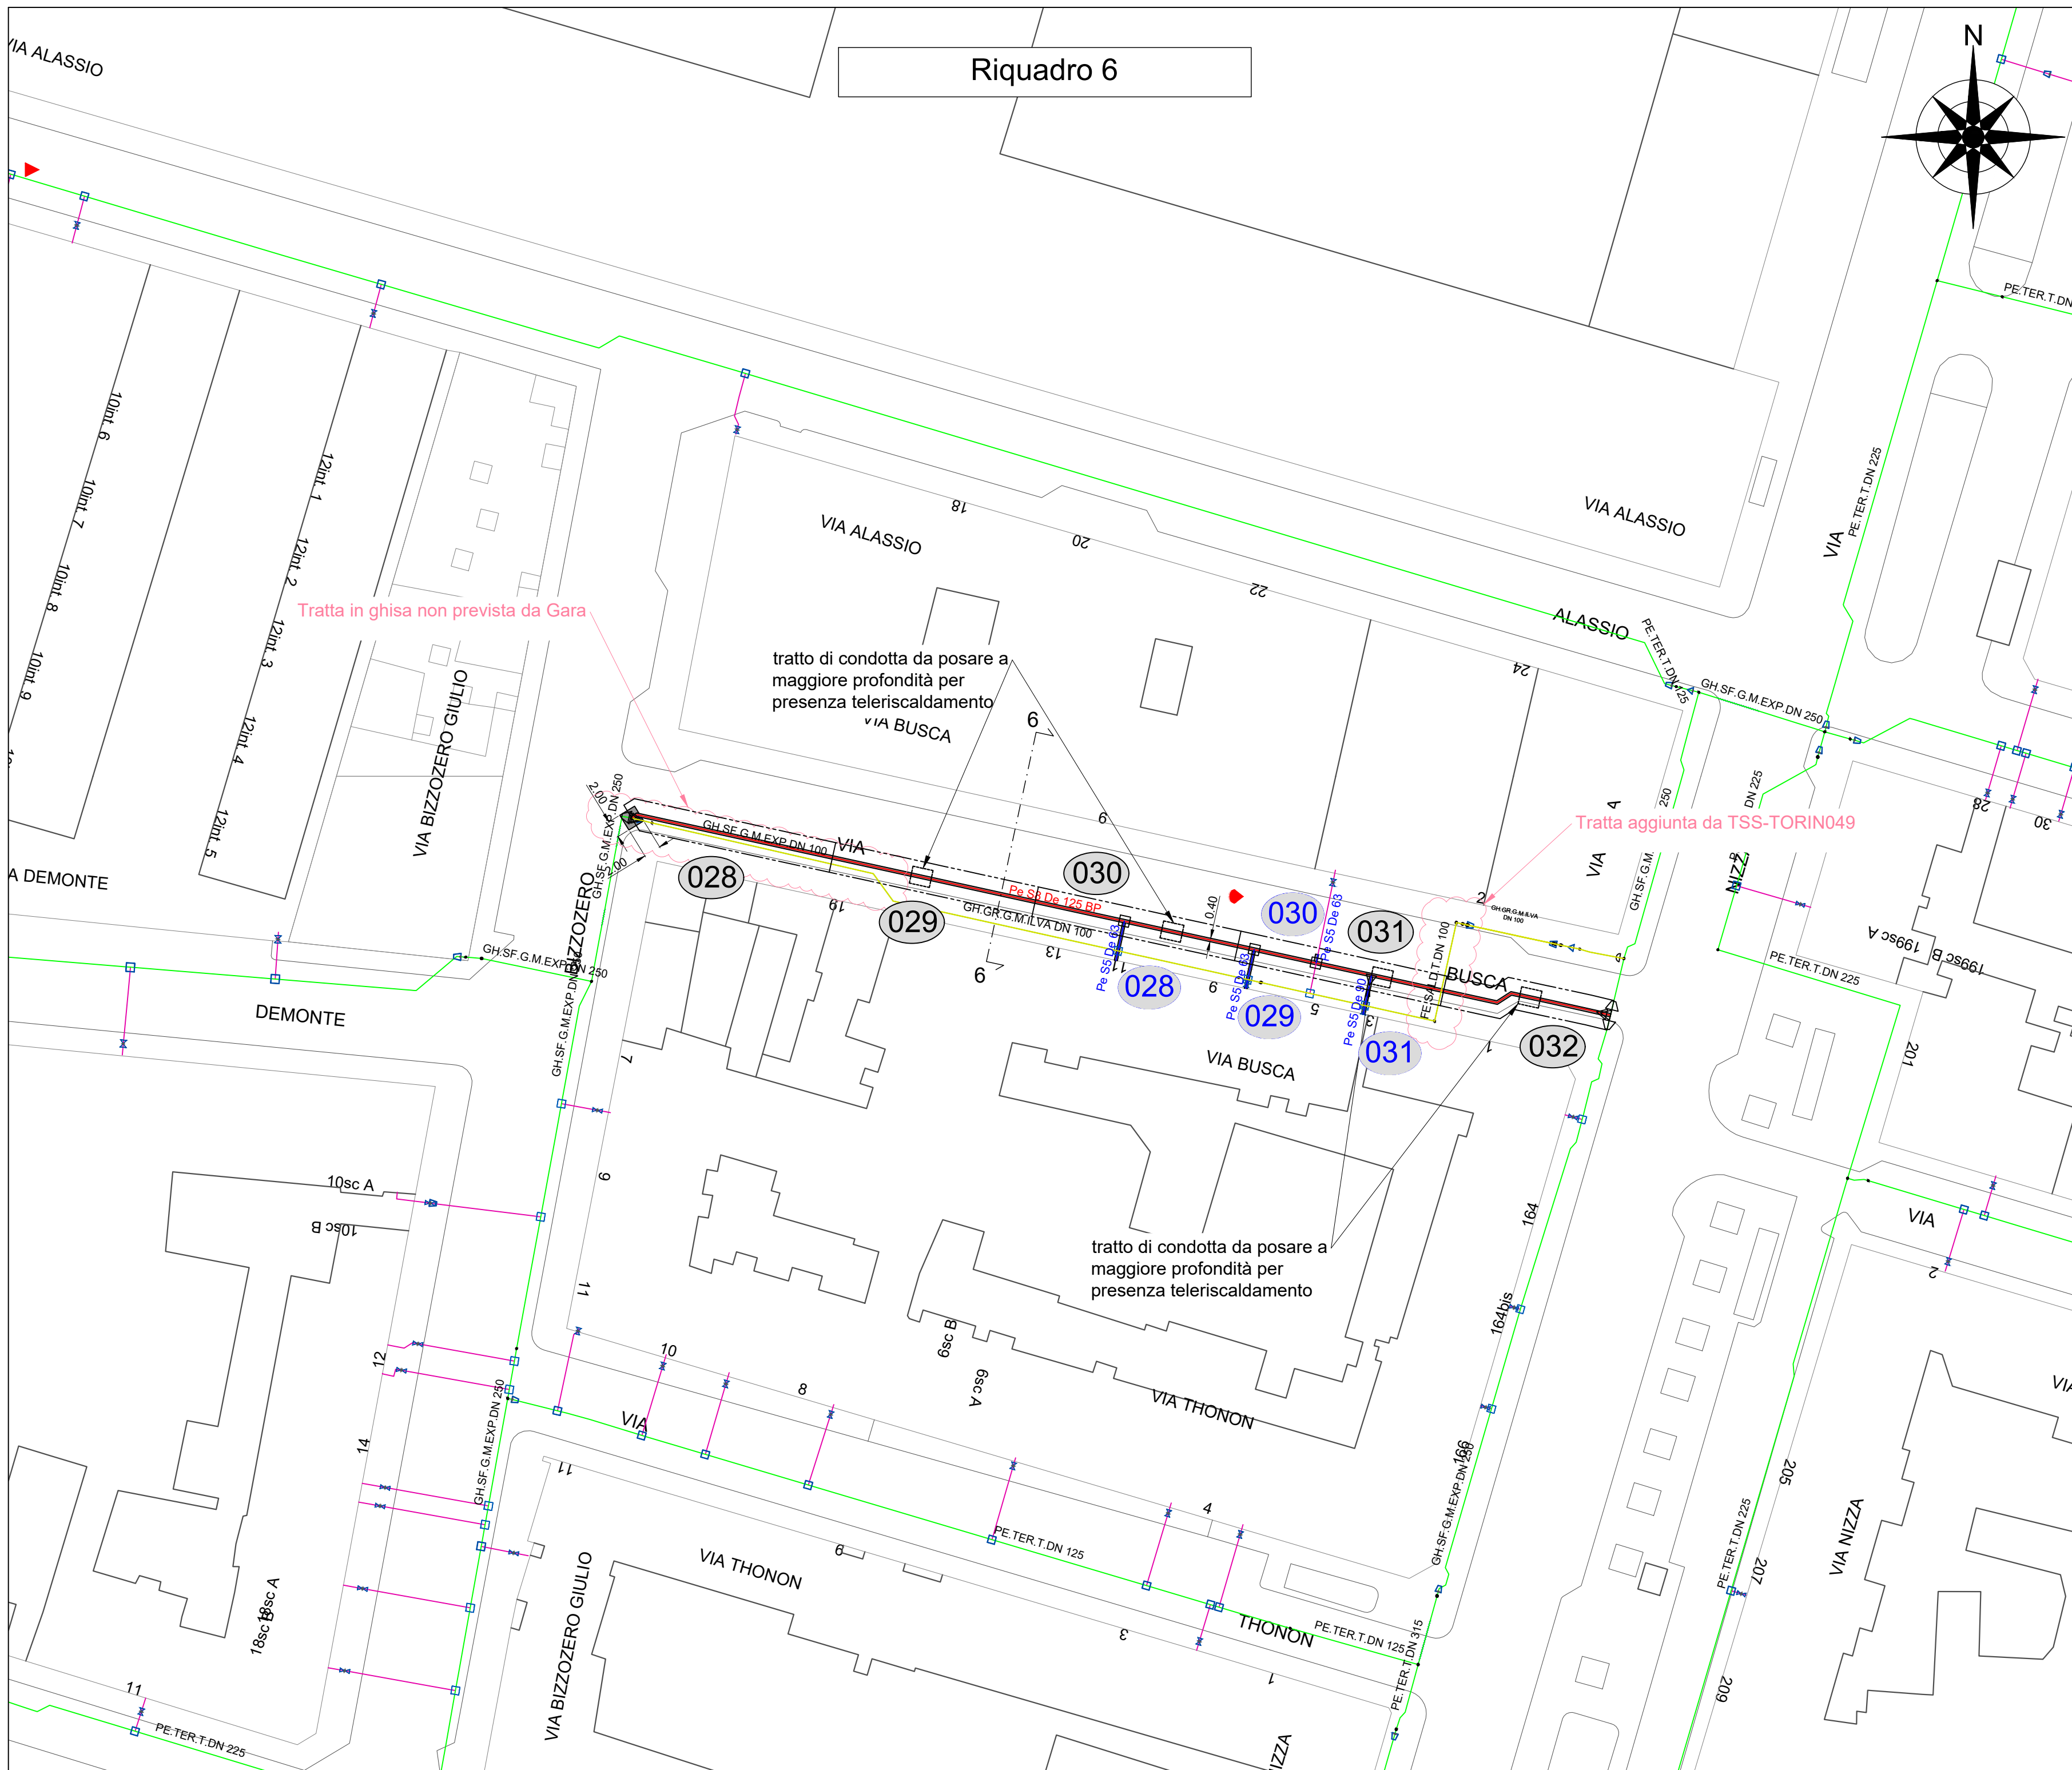

LEGENDA

— Rete in progetto	— Rete da rimuovere	— Zona di lavoro	— I.D.U. in progetto	— Tubazione I.D.U. esistente	— n° Zona di lavoro	— n° I.D.U. in progetto	— Area scavi asfalto	— Area scavi sterrato	— Area scavi autobloccanti
--------------------	---------------------	------------------	----------------------	------------------------------	---------------------	-------------------------	----------------------	-----------------------	----------------------------

dati condotta		scavo		Regolo: Scavi		tipo superficie		volume (rif.)		tipo di terreno		volume (ref.)	
caratteristiche	bar	lung. [m]	largh. [m]	h superf. [m]	h terr. [m]								
Re S8 De 315	BP	3	0,55	0,1	1,32	Asfalto	0,17	di riporto	2,17				
Re S8 De 315	BP	1201	0,55	0,15	1,27	Asfalto	104,03	di riporto	877,34				
Re S8 De 225	BP	239	0,50	0,15	1,18	Asfalto	15,35	di riporto	120,08				
Re S8 De 180	BP	1632,5	0,50	0,15	1,13	Asfalto	137,44	di riporto	1035,38				
Re S8 De 180	BP	31	0,50	0,00	1,28	Sterrato	0,00	di riporto	19,84				
Re S8 De 180	BP	0,5	0,50	0,10	1,18	Asfalto	0,03	di riporto	0,30				
Re S8 De 125	BP	8	0,40	0,00	1,23	Sterrato	0,00	di riporto	3,92				
Re S8 De 125	BP	817	0,40	0,15	1,08	Asfalto	49,02	di riporto	351,31				
Acc DN 400 (rimozione)		2	0,75	0,15	1,25	Asfalto	0,23	di riporto	1,88				
Acc DN 350 (rimozione)		8	0,75	0,15	1,25	Asfalto	0,80	di riporto	7,50				
Re De 315 (rimozione)		8	0,55	0,15	1,25	Asfalto	0,66	di riporto	5,50				
GH DN 300 (rimozione)		2	0,55	0,15	1,25	Asfalto	0,17	di riporto	1,38				
Acc DN 300 (rimozione)		5	0,55	0,15	1,25	Asfalto	0,41	di riporto	3,44				
GH DN 250 (rimozione)		894	0,55	0,15	1,20	Asfalto	73,76	di riporto	590,04				
Acc DN 250 (rimozione)		77	0,55	0,15	1,20	Asfalto	6,35	di riporto	50,82				
Acc DN 250 (rimozione)		54	0,55	0,10	1,25	Asfalto	2,97	di riporto	37,13				
GH DN 250 (rimozione)		4	0,55	0,10	1,25	Asfalto	0,22	di riporto	2,75				
GH DN 250 (rimozione)		19	0,55	0,00	1,35	Sterrato	0,00	di riporto	14,11				
Re De 225 (rimozione)		2	0,50	0,15	1,18	Asfalto	0,15	di riporto	1,18				
Acc DN 200 (rimozione)		3	0,50	0,15	1,15	Asfalto	0,23	di riporto	1,73				
GH DN 200 (rimozione)		220	0,50	0,15	1,15	Asfalto	16,50	di riporto	128,50				
Re De 180 (rimozione)		41	0,50	0,15	1,13	Asfalto	3,08	di riporto	23,17				
GH DN 150 (rimozione)		1634	0,50	0,15	1,10	Asfalto	122,55	di riporto	898,70				
GH DN 150 (rimozione)		58	0,50	0,10	1,15	Asfalto	3,99	di riporto	32,38				
Acc DN 150 (rimozione)		447	0,50	0,15	1,10	Asfalto	33,53	di riporto	245,85				
Re De 125 (rimozione)		25	0,40	0,15	1,08	Asfalto	1,50	di riporto	10,75				
GH DN 100 (rimozione)		8	0,40	0,00	1,20	Sterrato	0,00	di riporto	3,84				
Acc DN 100 (rimozione)		102	0,40	0,15	1,05	Asfalto	6,12	di riporto	42,84				
GH DN 100 (rimozione)		648	0,40	0,15	1,05	Asfalto	36,88	di riporto	272,16				
Re De 80 (rimozione)		8	0,40	0,15	1,04	Asfalto	0,36	di riporto	2,50				
GH DN 80 (rimozione)		52	0,40	0,15	1,03	Asfalto	3,12	di riporto	21,42				
Scavatura aggiuntiva									651,54				
Scavatura aggiuntiva									1968,17				
Buone di riporto									142,38				
Buone di riporto									30,60				
Totale									2762,79				


Progetto n°: 21-0584-3E-00-001272
VBS: SI.20.10300.02.1109
ALLEGATO n°: 5.3

Formato: A0 Scale: 1:500

Comune di TORINO (TO)
Via Vane
Progetto Esecutivo
SOSTITUZIONE RETE BP (L=2745,38 M) - GARA TO 1
Intervento n° SI-036213-011272-TSS-TORIN008
Planimetria d'insieme con rete - Tavola 3

Unità Responsabile della Progettazione
INGENERAL-INGE-PROGRE

Comune di TORINO (TO)
Via Vane
Progetto Esecutivo
SOSTITUZIONE RETE BP (L=2745,38 M) - GARA TO 1
Intervento n° SI-036213-011272-TSS-TORIN008
Planimetria d'insieme con rete - Tavola 3

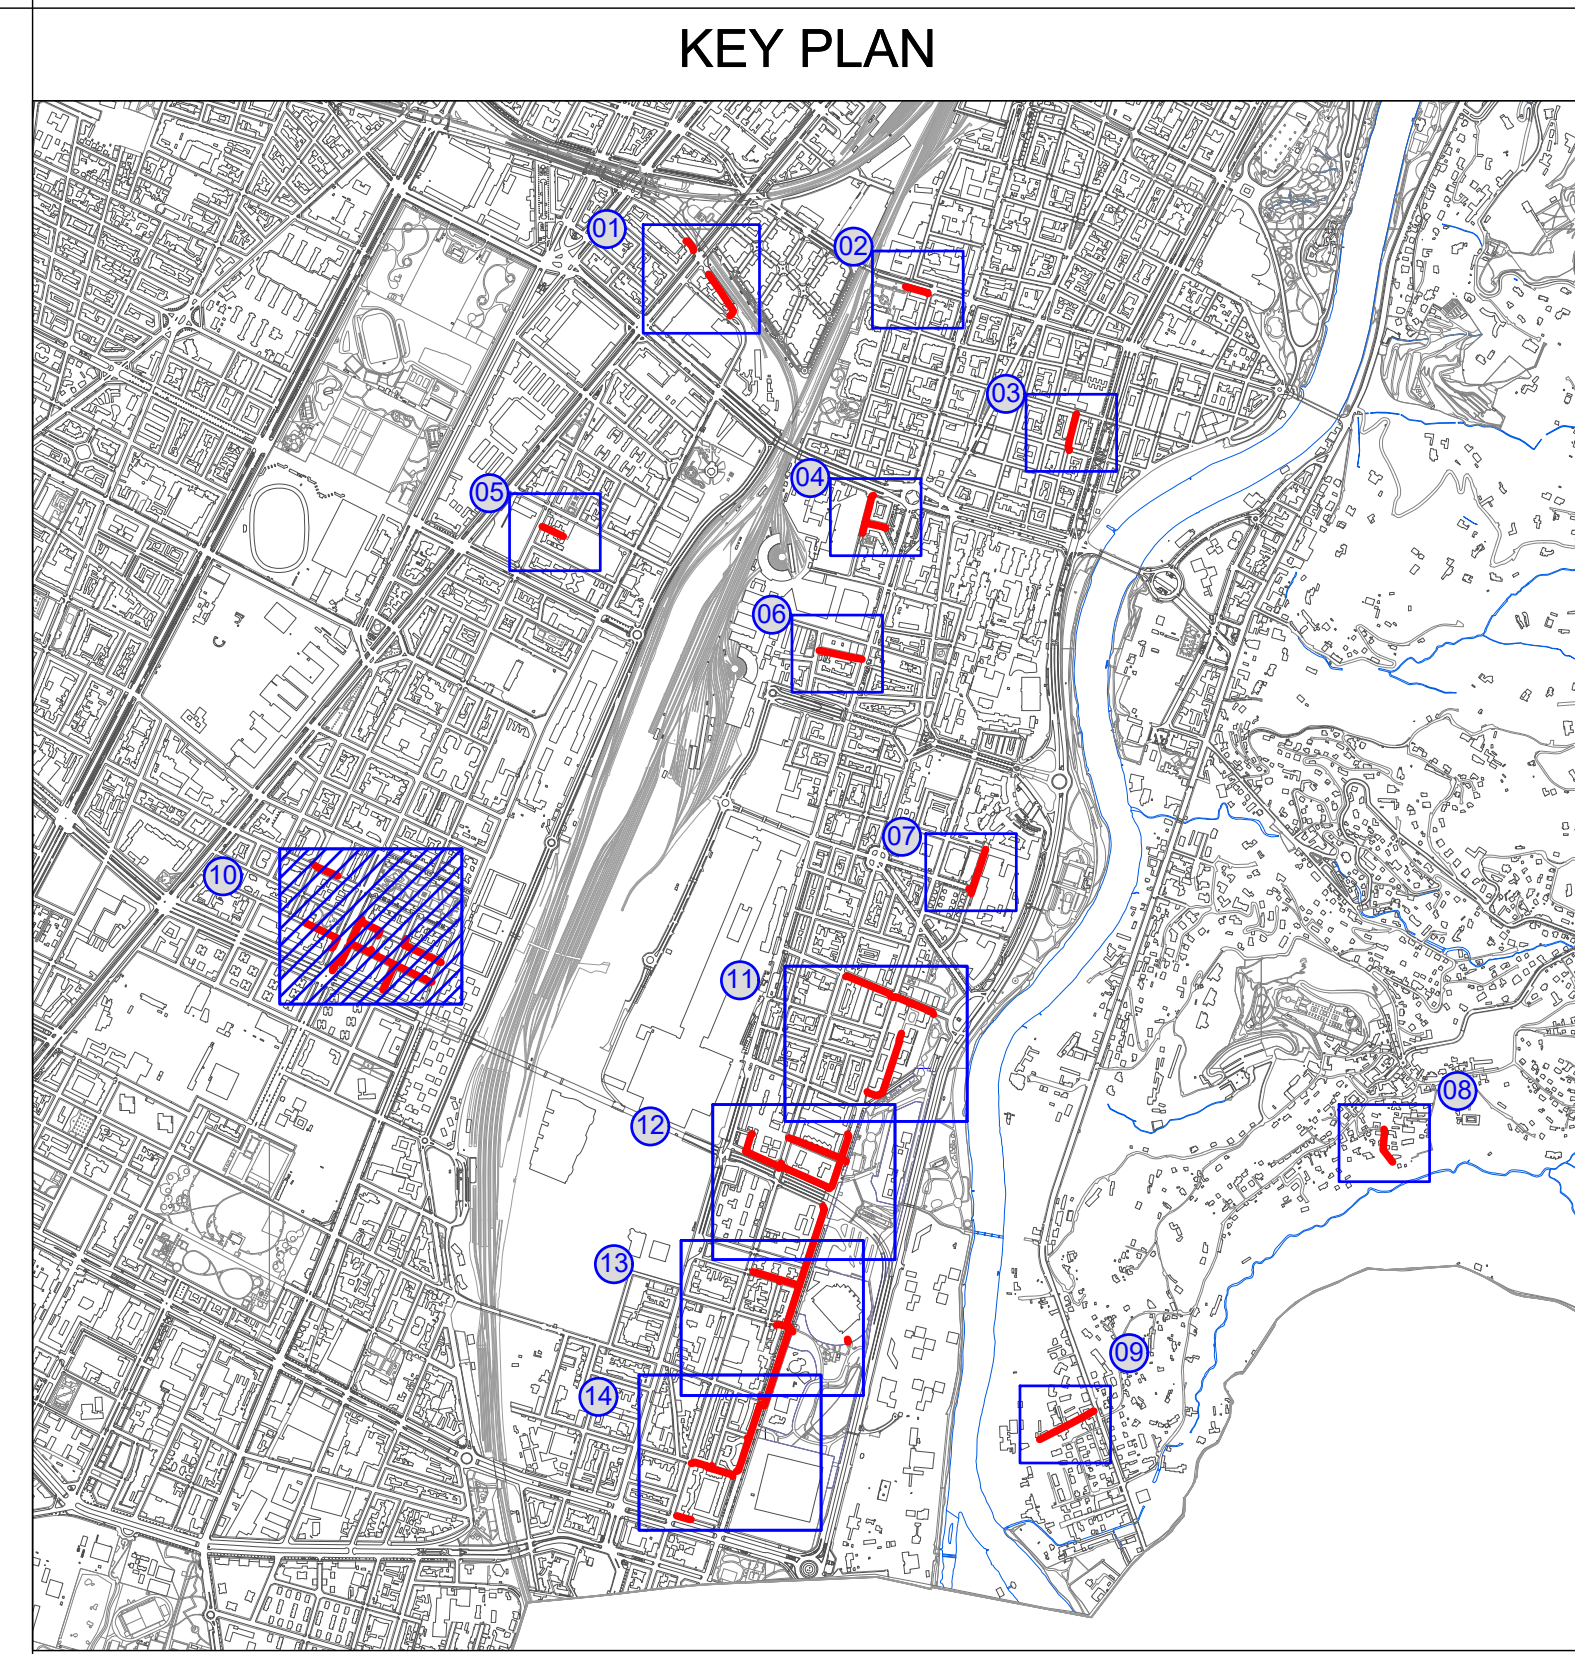

LEGENDA

— Rete in progetto

— Rete da rimuovere

— Zona di lavoro

— I.D.U. in progetto

— Tubazione I.D.U. esistente

001

002

n° Zona di lavoro

n° I.D.U. in progetto

Area scavi asfalto

Area scavi sterrato

Area scavi autobloccanti

dati condotta		scavo		Replage Scavi		tipo superficie		volume (m³)		tipo di terreno		volume terra e rocce (m³)	
caratteristiche	bar	lung. [m]	largh. [m]	h. sup. [m]	h. terr. [m]								
Pe 58 De 315	BP	3	0.55	0.1	1.32		Autobloccanti	0.17	di riporto		2.17		
Pe 58 De 315	BP	1281	0.55	0.15	1.27		Asfalto	104.03	di riporto		877.34		
Pe 58 De 225	BP	218	0.50	0.15	1.18		Asfalto	16.35	di riporto		128.08		
Pe 58 De 180	BP	1632.5	0.50	0.15	1.13		Asfalto	137.44	di riporto		1035.36		
Pe 58 De 180	BP	31	0.50	0.00	1.25		Sterrato	0.00	di riporto		19.84		
Pe 58 De 180	BP	0.5	0.50	0.10	1.18		Autobloccanti	0.03	di riporto		0.30		
Pe 58 De 125	BP	8	0.40	0.00	1.23		Sterrato	0.00	di riporto		3.92		
Pe 58 De 125	BP	817	0.40	0.15	1.08		Asfalto	40.02	di riporto		351.31		
Acc DN 400 (rimozione)		2	0.75	0.15	1.25		Asfalto	0.23	di riporto		1.88		
Acc DN 350 (rimozione)		6	0.75	0.15	1.25		Asfalto	0.90	di riporto		7.50		
Pe De 315 (rimozione)		8	0.55	0.15	1.25		Asfalto	0.68	di riporto		5.50		
GH DN 300 (rimozione)		2	0.55	0.15	1.25		Asfalto	0.17	di riporto		1.38		
Acc DN 300 (rimozione)		5	0.55	0.15	1.25		Asfalto	0.41	di riporto		3.44		
GH DN 250 (rimozione)		894	0.55	0.15	1.20		Asfalto	73.76	di riporto		590.04		
Acc DN 250 (rimozione)		77	0.55	0.15	1.20		Asfalto	6.36	di riporto		50.82		
Acc DN 250 (rimozione)		54	0.55	0.10	1.25		Autobloccanti	2.97	di riporto		37.13		
GH DN 250 (rimozione)		4	0.55	0.10	1.25		Autobloccanti	0.22	di riporto		2.75		
GH DN 250 (rimozione)		19	0.55	0.00	1.25		Sterrato	0.00	di riporto		14.11		
Pe De 225 (rimozione)		2	0.50	0.15	1.18		Asfalto	0.15	di riporto		1.18		
Acc DN 200 (rimozione)		3	0.50	0.15	1.15		Asfalto	0.23	di riporto		1.73		
GH DN 200 (rimozione)		220	0.50	0.15	1.15		Asfalto	16.50	di riporto		126.50		
Pe De 180 (rimozione)		41	0.50	0.15	1.13		Asfalto	3.08	di riporto		23.17		
GH DN 150 (rimozione)		1634	0.50	0.15	1.10		Asfalto	122.55	di riporto		988.70		
GH DN 150 (rimozione)		38	0.50	0.10	1.15		Autobloccanti	2.80	di riporto		22.40		
Acc DN 150 (rimozione)		447	0.50	0.15	1.10		Asfalto	33.53	di riporto		245.85		
Pe De 125 (rimozione)		25	0.40	0.15	1.08		Asfalto	1.50	di riporto		10.75		
GH DN 150 (rimozione)		8	0.40	0.00	1.20		Sterrato	0.00	di riporto		3.84		
Acc DN 100 (rimozione)		102	0.40	0.15	1.05		Asfalto	6.12	di riporto		42.84		
GH DN 100 (rimozione)		648	0.40	0.15	1.05		Asfalto	36.68	di riporto		272.16		
Pe De 90 (rimozione)		5	0.40	0.15	1.04		Asfalto	0.36	di riporto		2.50		
GH DN 80 (rimozione)		52	0.40	0.15	1.03		Asfalto	3.12	di riporto		21.42		
Scarifica aggiuntiva								651.60			4815.94		
Scarifica aggiuntiva								1968.17			0.00		
Scarifica RVI								142.38			284.58		
Buche di inasamento								30.60			236.04		
Totale								2762.79			5337.16		

Progetto n°:
21-0584-3E-00-00/1272
VBS:
SI20.I0300.02.1109
ALLEGATO n°: 5.4

Progettista
Ing. Alessandro Leardi
Assistente
Ing. Alessandra Leardi
Progettista
Ing. Alessandro Leardi


Comune di TORINO (TO)
Via Vane
Progetto Esecutivo
SOSTITUZIONE RETE BP (L=2745.38 M) - GARA TO 1
Intervento n° SI-06213-001272-TSS-TORIN008
Planimetria d'insieme con rete - Tavola 4

Unità Responsabile della Progettazione
INGENER-INGE-PROGRE

Disegnato	0	30	11	22	A.Salerno	L.Cantagna	A.Leardi
Revisione							
Com. 1: 2484							

Comune di TORINO (TO)
Via Vane
Progetto Esecutivo
SOSTITUZIONE RETE BP (L=2745.38 M) - GARA TO 1
Intervento n° SI-06213-001272-TSS-TORIN008
Planimetria d'insieme con rete - Tavola 4

Il presente elaborato è di proprietà aziendale - La società tutela i propri diritti a termini di legge.

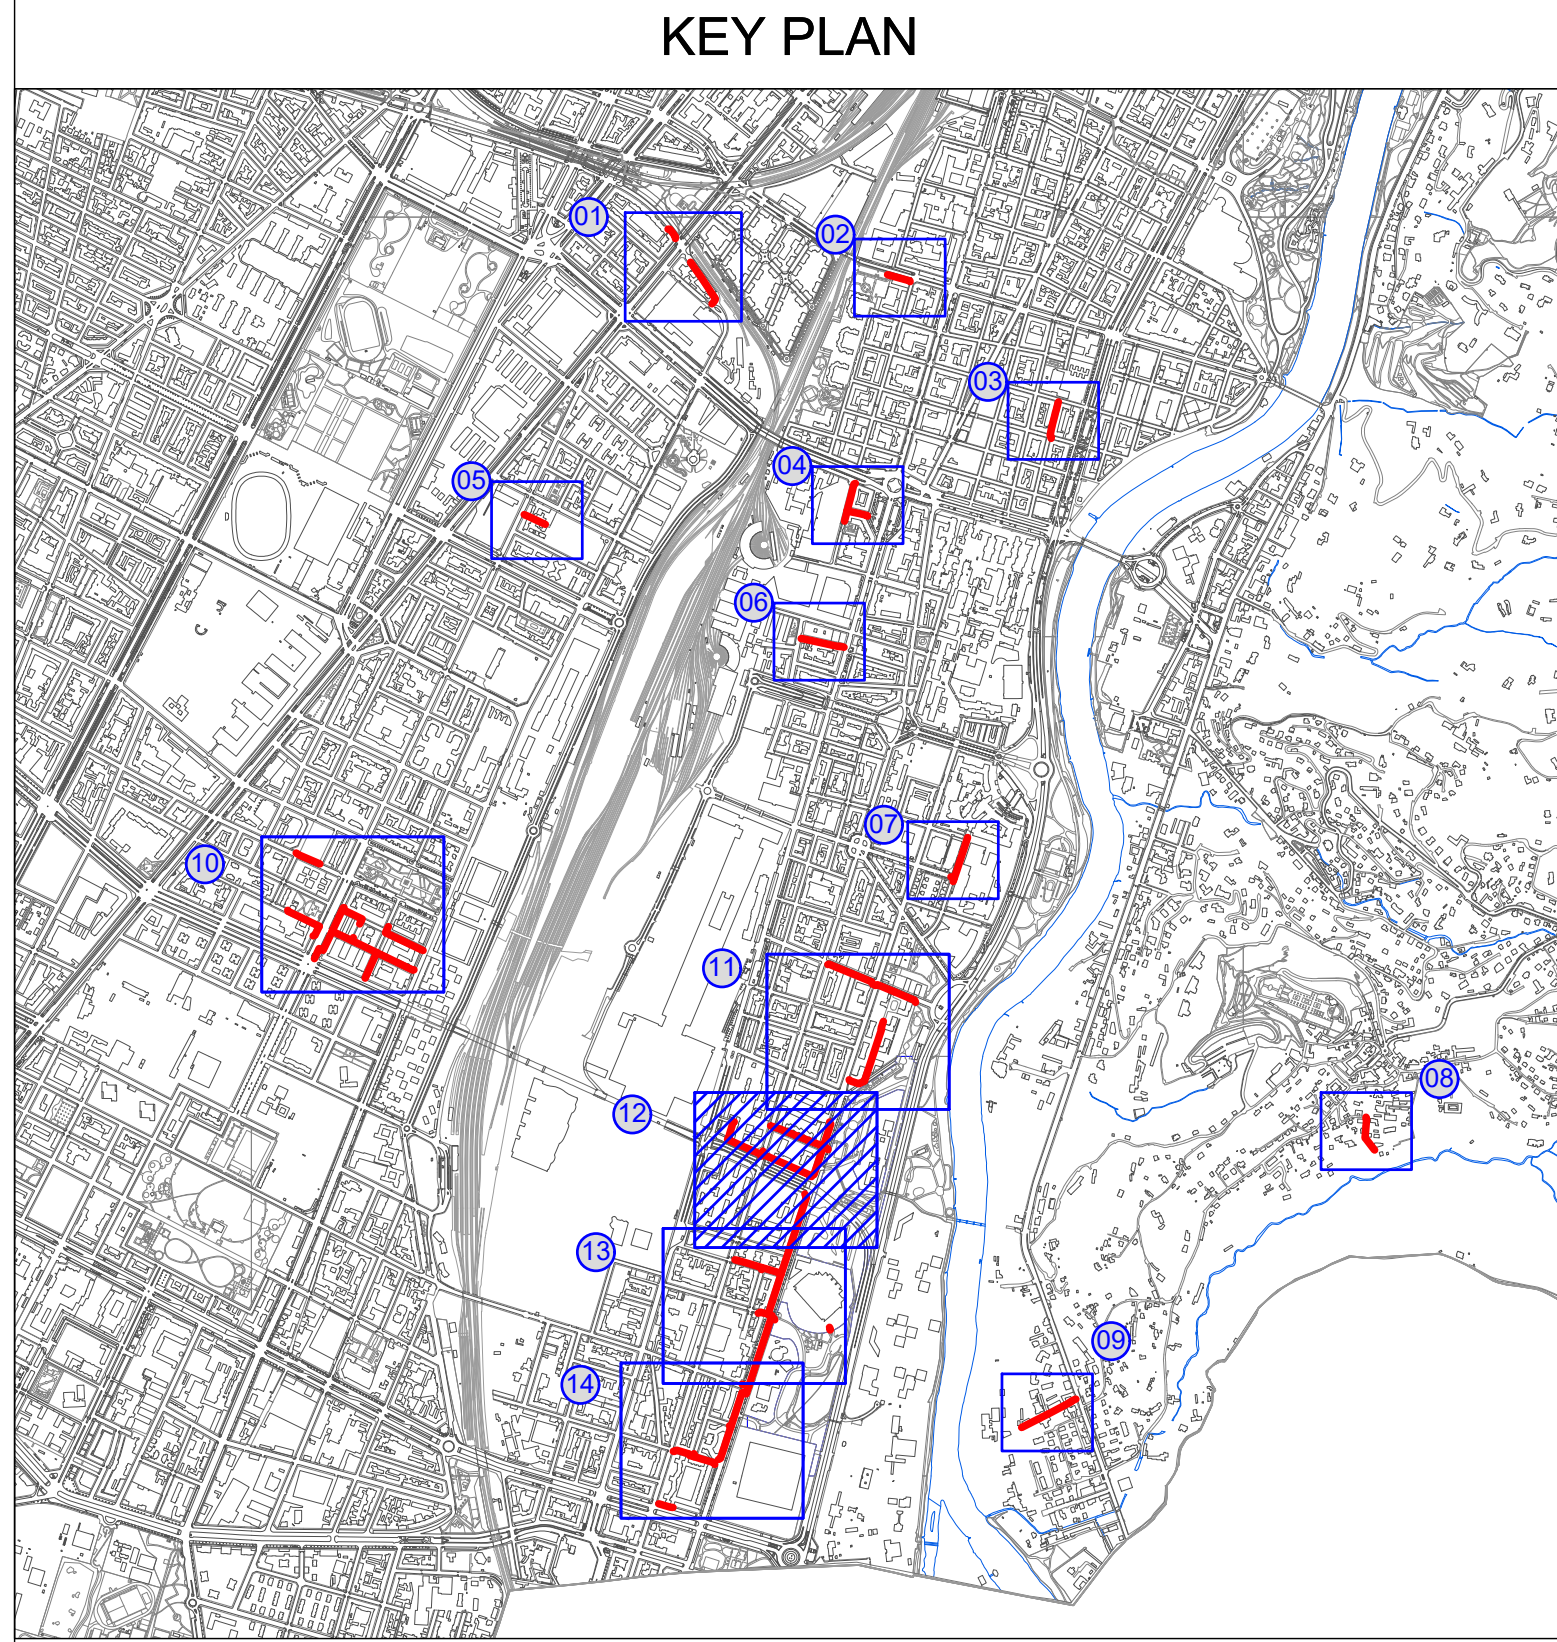

LEGENDA

- Rete in progetto
- Rete da rimuovere
- Zona di lavoro
- I.D.U. in progetto
- Tubazione I.D.U. esistente
- n° Zona di lavoro
- n° I.D.U. in progetto
- Area scavi asfalto
- Area scavi sterrato
- Area scavi autobloccanti

Reperto: Scavi									
dati condotta	scavo								
caratteristiche	bar	lung [m]	largh. [m]	h superf. [m]	h terr. [m]	tipo superficie	volume (m³)	tipo di terreno	volume terra e roccia (m³)
Ri 50 Da 315	BP	3	0,55	0,1	1,32	Autobloccanti	0,17	di riporto	2,17
Ri 50 Da 315	BP	1281	0,55	0,15	1,27	Asfalto	104,03	di riporto	677,34
Ri 50 Da 225	BP	219	0,50	0,15	1,18	Asfalto	15,35	di riporto	128,08
Ri 50 Da 180	BP	1832,5	0,50	0,15	1,13	Asfalto	137,44	di riporto	1035,38
Ri 50 Da 160	BP	31	0,50	0,20	1,28	Sterrato	0,09	di riporto	19,84
Ri 50 Da 100	BP	0,5	0,50	0,10	1,18	Autobloccanti	0,03	di riporto	0,30
Ri 50 Da 125	BP	5	0,40	0,00	1,23	Sterrato	0,00	di riporto	3,92
Ri 50 Da 125	BP	817	0,40	0,15	1,08	Asfalto	46,02	di riporto	351,31
Acc DN 400 (rimozione)		2	0,75	0,15	1,25	Asfalto	0,23	di riporto	1,88
Acc DN 350 (rimozione)		5	0,75	0,15	1,25	Asfalto	0,80	di riporto	7,50
Ri Da 315 (rimozione)		6	0,55	0,15	1,25	Asfalto	0,66	di riporto	5,50
GH DN 300 (rimozione)		2	0,55	0,15	1,25	Asfalto	0,17	di riporto	1,38
Acc DN 300 (rimozione)		5	0,55	0,15	1,25	Asfalto	0,41	di riporto	3,44
GH DN 250 (rimozione)		894	0,55	0,15	1,20	Asfalto	73,76	di riporto	590,04
Acc DN 250 (rimozione)		77	0,55	0,15	1,20	Asfalto	6,35	di riporto	50,62
Acc DN 250 (rimozione)		54	0,55	0,10	1,25	Autobloccanti	2,97	di riporto	37,13
GH DN 250 (rimozione)		4	0,55	0,10	1,25	Autobloccanti	0,22	di riporto	2,75
GH DN 250 (rimozione)		19	0,55	0,00	1,35	Sterrato	0,00	di riporto	14,11
Ri Da 225 (rimozione)		2	0,50	0,15	1,18	Asfalto	0,15	di riporto	1,18
Acc DN 200 (rimozione)		3	0,50	0,15	1,15	Asfalto	0,23	di riporto	1,73
GH DN 200 (rimozione)		220	0,50	0,15	1,15	Asfalto	16,50	di riporto	126,50
Ri Da 180 (rimozione)		41	0,50	0,15	1,13	Asfalto	3,08	di riporto	23,17
GH DN 150 (rimozione)		1634	0,50	0,15	1,10	Asfalto	122,85	di riporto	966,70
GH DN 150 (rimozione)		58	0,50	0,10	1,15	Autobloccanti	2,80	di riporto	32,30
Acc DN 150 (rimozione)		447	0,50	0,15	1,10	Asfalto	33,53	di riporto	246,85
Ri Da 125 (rimozione)		25	0,40	0,15	1,08	Asfalto	1,50	di riporto	10,75
GH DN 100 (rimozione)		5	0,40	0,00	1,20	Sterrato	0,00	di riporto	3,84
Acc DN 100 (rimozione)		102	0,40	0,15	1,05	Asfalto	6,12	di riporto	42,84
GH DN 100 (rimozione)		646	0,40	0,15	1,05	Asfalto	36,36	di riporto	272,18
Ri Da 90 (rimozione)		5	0,40	0,15	1,04	Asfalto	0,36	di riporto	2,50
GH DN 80 (rimozione)		52	0,40	0,15	1,03	Asfalto	3,12	di riporto	21,42
Scarifica aggiuntiva							621,63		4613,94
Scarifica da							1968,17		0,00
Buco di inasamento							30,60		284,58
Totale							2762,79		5337,16

Progetto n°: 21-0564-3E-00-001272
WBS: SI20.I0300.02.1109
ALLEGATO n°: 5.6


Progettato da: LEARDI
Ordinatore: Ing. Alessandria
Verificato: Ing. Alessandria

Unità Responsabile della Progettazione

INGENER-INGE-PROGRE

Comune di TORINO (TO)
Via Vane
Progetto Esecutivo
SOSTITUZIONE RETE BP (L=2745,38 M) - GARA TO 1
Intervento n° SI-0362-13-001272-TSS-TORINO08
Planimetria d'insieme con rete - Tavola 6

Il presente elaborato è di proprietà aziendale - La società tutelata i propri diritti a termini di legge.

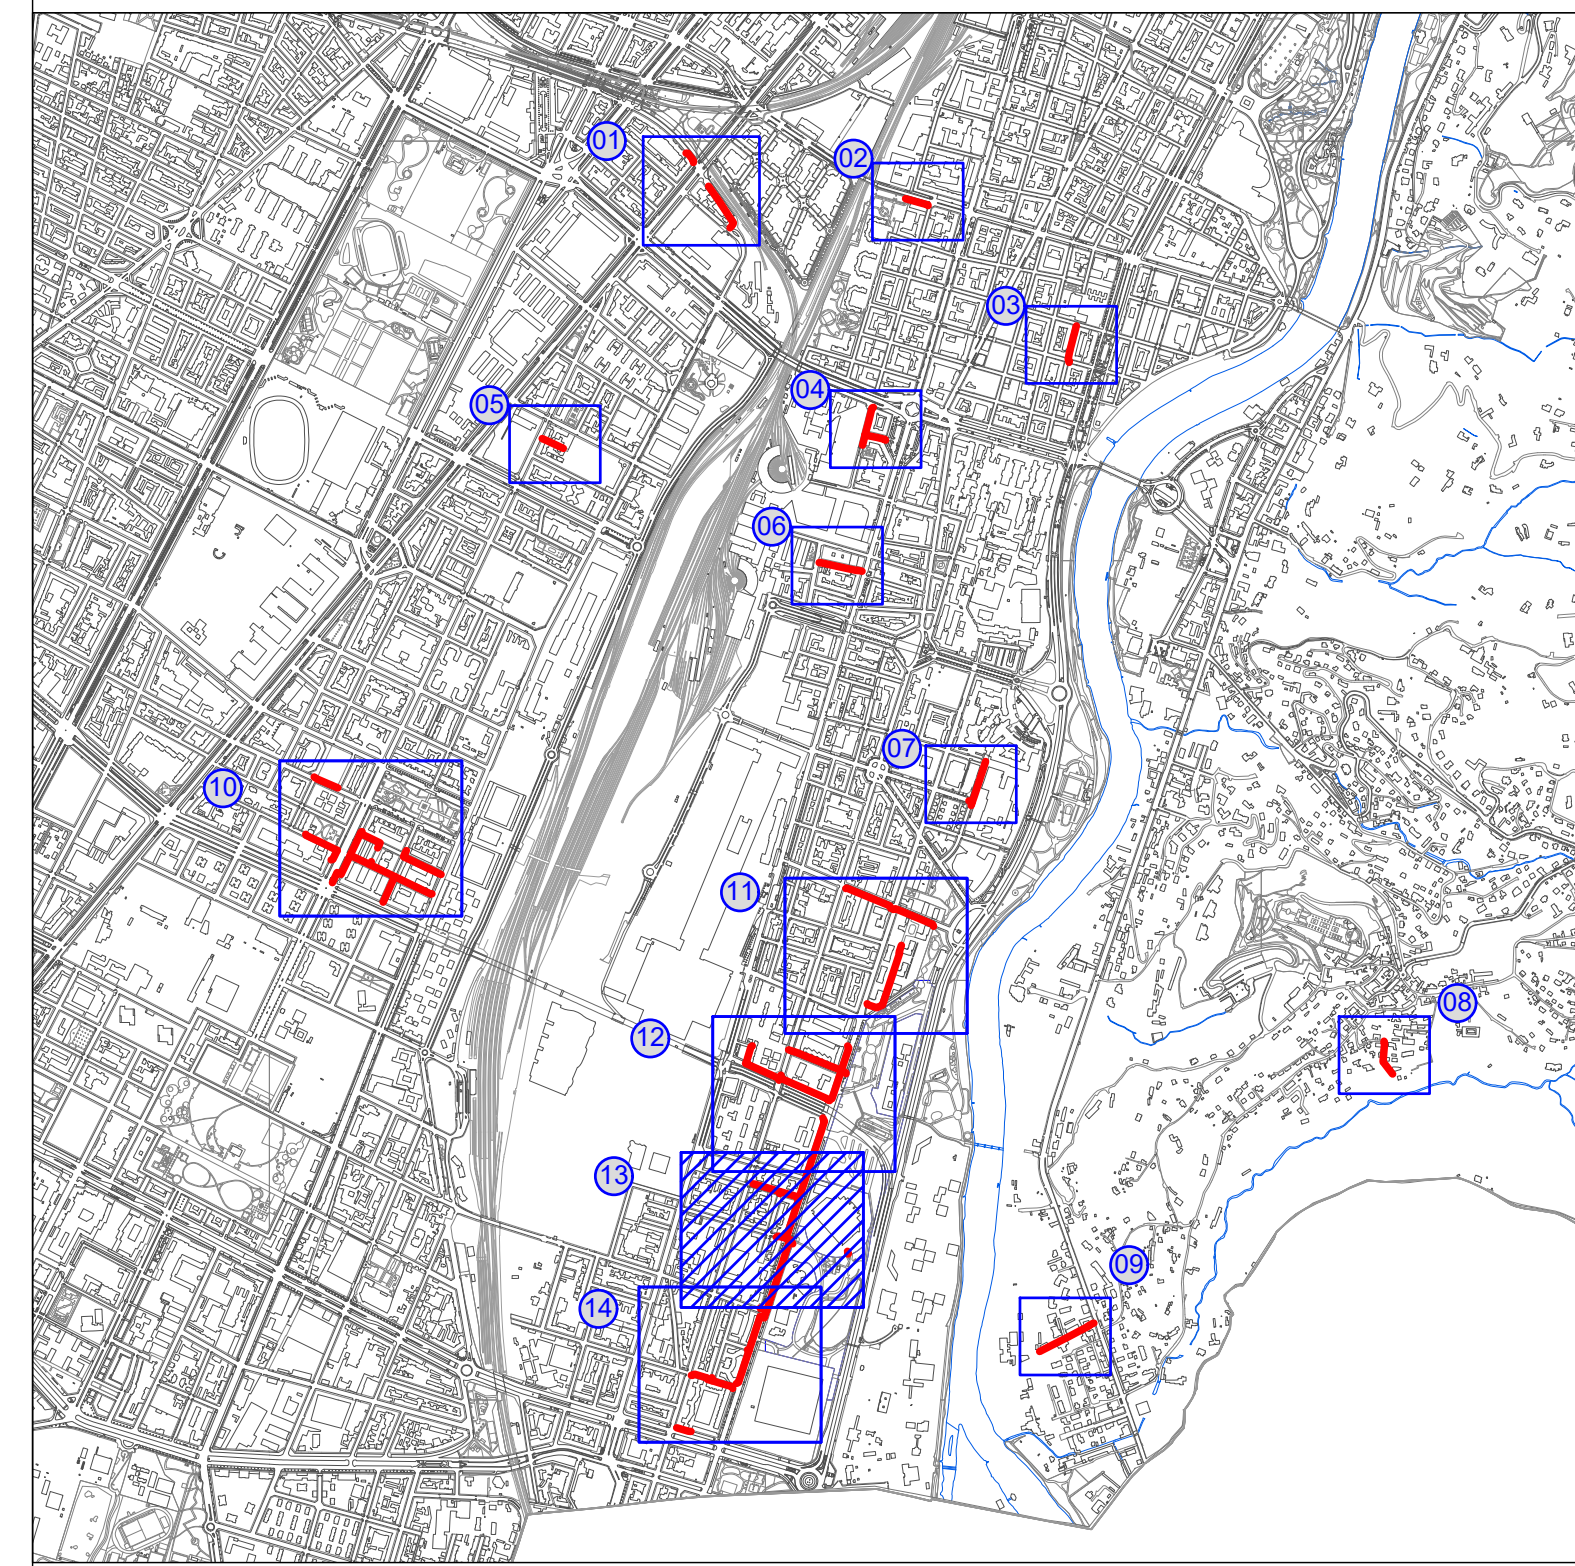

LEGENDA

	Rete in progetto		n° Zona di lavoro
	Rete da rimuovere		n° I.D.U. in progetto
	Zona di lavoro		Area scavi asfalto
	I.D.U. in progetto		Area scavi sterzato
	Tubazione I.D.U. esistente		Area scavi autobloccanti

dati condotta		scavo		Replogo Scavi		tipo superficie	volume (m³)	tipo di terreno	volume terra e rocce (m³)
caratteristiche	bar	lung. [m]	largh. [m]	h superf. [m]	h terr. [m]				
Re SS Da 315	BP	3	0,55	0,1	1,32	Autobloccanti	0,17	di riporto	2,17
Re SS Da 315	BP	1261	0,55	0,15	1,27	Asfalto	104,03	di riporto	877,34
Re SS Da 225	BP	219	0,50	0,15	1,18	Asfalto	15,35	di riporto	129,08
Re SS Da 180	BP	1632,5	0,50	0,15	1,13	Asfalto	137,44	di riporto	1035,36
Re SS Da 180	BP	31	0,50	0,00	1,28	Sterzato	0,00	di riporto	19,84
Re SS Da 180	BP	0,5	0,50	0,10	1,18	Autobloccanti	0,03	di riporto	0,30
Re SS Da 125	BP	8	0,40	0,00	1,23	Sterzato	0,00	di riporto	3,92
Re SS Da 125	BP	817	0,40	0,15	1,08	Asfalto	49,02	di riporto	351,31
Acc DN 400 (rimozione)		2	0,75	0,15	1,25	Asfalto	0,23	di riporto	1,88
Acc DN 350 (rimozione)		8	0,75	0,15	1,25	Asfalto	0,90	di riporto	7,50
Re Da 315 (rimozione)		8	0,55	0,15	1,25	Asfalto	0,68	di riporto	5,50
GH DN 300 (rimozione)		2	0,55	0,15	1,25	Asfalto	0,17	di riporto	1,38
Acc DN 300 (rimozione)		5	0,55	0,15	1,25	Asfalto	0,41	di riporto	3,44
GH DN 250 (rimozione)		894	0,55	0,15	1,20	Asfalto	73,76	di riporto	590,04
Acc DN 250 (rimozione)		77	0,55	0,15	1,20	Asfalto	6,35	di riporto	50,82
Acc DN 250 (rimozione)		54	0,55	0,10	1,25	Autobloccanti	2,97	di riporto	37,13
GH DN 250 (rimozione)		4	0,55	0,10	1,25	Autobloccanti	0,22	di riporto	2,75
GH DN 250 (rimozione)		19	0,55	0,00	1,35	Sterzato	0,00	di riporto	14,11
Re Da 225 (rimozione)		2	0,50	0,15	1,18	Asfalto	0,15	di riporto	1,18
Acc DN 200 (rimozione)		3	0,50	0,15	1,15	Asfalto	0,23	di riporto	1,73
GH DN 200 (rimozione)		220	0,50	0,15	1,15	Asfalto	16,50	di riporto	128,50
Re Da 180 (rimozione)		41	0,50	0,15	1,13	Asfalto	3,08	di riporto	23,17
GH DN 150 (rimozione)		1634	0,50	0,15	1,10	Asfalto	122,55	di riporto	898,70
GH DN 150 (rimozione)		56	0,50	0,10	1,15	Autobloccanti	2,80	di riporto	32,39
Acc DN 150 (rimozione)		447	0,50	0,15	1,10	Asfalto	33,53	di riporto	245,85
Re Da 125 (rimozione)		25	0,40	0,15	1,08	Asfalto	1,50	di riporto	10,75
GH DN 100 (rimozione)		8	0,40	0,00	1,20	Sterzato	0,00	di riporto	5,84
Acc DN 100 (rimozione)		102	0,40	0,15	1,05	Asfalto	6,12	di riporto	42,84
GH DN 100 (rimozione)		646	0,40	0,15	1,05	Asfalto	39,58	di riporto	272,16
Re Da 90 (rimozione)		5	0,40	0,15	1,04	Asfalto	0,36	di riporto	2,50
GH DN 80 (rimozione)		52	0,40	0,15	1,03	Asfalto	3,12	di riporto	21,42
Scarifica aggiuntiva							601,65		4819,94
Scarifica aggiuntiva							1968,17		0,00
Buche di manovra							140,35		264,58
Totale							30,60		238,04
							2762,79		6337,16

Progetto n°: 21-0584-3E-00-00/1272
VBS: SI.20.10300.02.1109
ALLEGATO n°: 5.7
Formato: A0 Scale 1: 500

Progettazione
Ordine degli Ingegneri di Alessandria
n° 1101
Firma

Unità Responsabile della Progettazione
INGENERAL-INGE-PROGRE

Disegnata	0	30	11	22	A. Sironi	L. Contagna	A. Leardi
Revisione per commenti							
Com: 2484							

Comittente
Comune di TORINO (TO)
Via Vane
Progetto Esecutivo
SOSTITUZIONE RETE BP (L=2745,39 M) - GARA TO 1
Intervento n° SI-026213-001272-TSS-TORIN008
Planimetria d'insieme con rete - Tavola 7

	Rete in progetto		n° Zona di lavoro
	Rete da rimuovere		n° I.D.U. in progetto
	Zona di lavoro		Area scavi asfalto
	I.D.U. in progetto		Area scavi sterrato
	Tubazione I.D.U. esistente		Area scavi autobloccanti

Replogio Scavi								
dati condotta caratteristiche		scavo			tipo superficie	volume rifuti [m ³]	tipo di terreno	volume terre e rocce iniettate
bar	lung [m]	largh. [m]	h superf. [m]	h metr. [m]				
Rp SB De 315	BP	3	0,55	0,1	1,32	Autobloccanti	0,17	dipinto 2,17
Rp SB De 315	BP	1261	0,55	0,15	1,27	Astafalo	104,03	dipinto 877,34
Rp SB De 325	BP	218	0,50	0,15	1,18	Astafalo	19,35	dipinto 128,8
Rp SB De 180	BP	163	0,55	0,1	1,13	Sterato	137,44	dipinto 130,3
Rp SB De 180	BP	31	0,50	0,00	1,20	Sterato	0	dipinto 19,84
Rp SB De 180	BP	0,5	0,50	0,15	1,18	Autobloccanti	0,03	dipinto 0,30
Rp SB De 125	BP	52	0,40	0,15	1,23	Sterato	0,06	dipinto 0,35
Rp SB De 125	BP	817	0,40	0,15	1,08	Astafalo	49,02	dipinto 351,31
Acc DN 400 (rimozione)		2	0,75	0,15	1,25	Astafalo	0,23	dipinto 1,68
Acc DN 350 (rimozione)		8	0,75	0,15	1,25	Astafalo	0,90	dipinto 7,50
Rp De 315 (rimozione)		8	0,55	0,15	1,25	Astafalo	0,86	dipinto 5,50
GHI DN 200 (rimozione)		2	0,15	0,15	1,25	Astafalo	0,17	dipinto 1,35
Acc DN 300 (rimozione)		5	0,55	0,15	1,25	Astafalo	0,41	dipinto 3,44
GHI DN 250 (rimozione)		694	0,55	0,15	1,20	Astafalo	73,76	dipinto 590,04
Acc DN 250 (rimozione)		77	0,55	0,10	1,20	Astafalo	6,36	dipinto 50,82
Acc DN 250 (rimozione)		54	0,55	0,10	1,25	Autobloccanti	2,97	dipinto 27,13
Acc DN 250 (rimozione)		4	0,55	0,1	1,25	Autobloccanti	0,31	dipinto 2,7
GHI DN 200 (rimozione)		19	0,55	0,00	1,30	Sterato	0	dipinto 14,11
Rp De 205 (rimozione)		2	0,50	0,15	1,18	Astafalo	0,15	dipinto 1,18
Acc DN 200 (rimozione)		3	0,50	0,15	1,15	Astafalo	0,23	dipinto 1,73
GHI DN 200 (rimozione)		220	0,50	0,15	1,15	Astafalo	16,50	dipinto 126,50
Rp De 180 (rimozione)		41	0,50	0,15	1,13	Astafalo	3,30	dipinto 23,17
GHI DN 150 (rimozione)		1634	0,50	0,15	1,10	Astafalo	122,55	dipinto 886,70
GHI DN 150 (rimozione)		5	0,40	0,15	1,15	Autobloccanti	2,18	dipinto 32,4
Acc DN 150 (rimozione)		447	0,50	0,15	1,10	Astafalo	33,53	dipinto 245,85
Rp De 125 (rimozione)		25	0,40	0,15	1,08	Astafalo	1,50	dipinto 10,75
GHI DN 100 (rimozione)		6	0,40	0,15	1,20	Sterato	0,20	dipinto 3,4
Acc DN 100 (rimozione)		102	0,40	0,15	1,05	Astafalo	6,12	dipinto 42,84
GHI DN 100 (rimozione)		648	0,40	0,15	1,05	Astafalo	38,88	dipinto 272,18
Rp De 50 (rimozione)		52	0,40	0,15	1,04	Astafalo	3,36	dipinto 2,9
GHI DN 80 (rimozione)		52	0,40	0,15	0,93	Astafalo	3,12	dipinto 21,42
							621,65	4615,94
Scantaria aggrigata							1905,17	
Scantaria DOL							142,39	284,58
Buche di riserimento							206,80	
Totale							2767,98	5337,16

				Unità Responsabile della Progettazione		
		Progettista Ordine degli Ingegneri di Alessandria Maresca 1101 Firma				
Progetto n°: 21-0564-36-00-001272 WBS SI-20-03000-02-1109 ALLEGATO n° 5_8		INGENER-INGE-PROGRE				
Numero						
Descrizione Emissione per commento		0	30	11	22	A.Saroni L.Cantegna A.Leardi
Formato: A4 Scale 1 : 500		Rev.	G.	M.	A.	Redatto Controllato Approvato
Commento		Comune di TORINO (TO) Via Vares Progetto Esecutivo SOSTITUZIONE RETE BP L=2745,39 M) - GARA TO 1 Intervento n° SI-03000-02-1272-TSS-TORINO006 Planimetria d'insieme con rete - Tavola 8				