


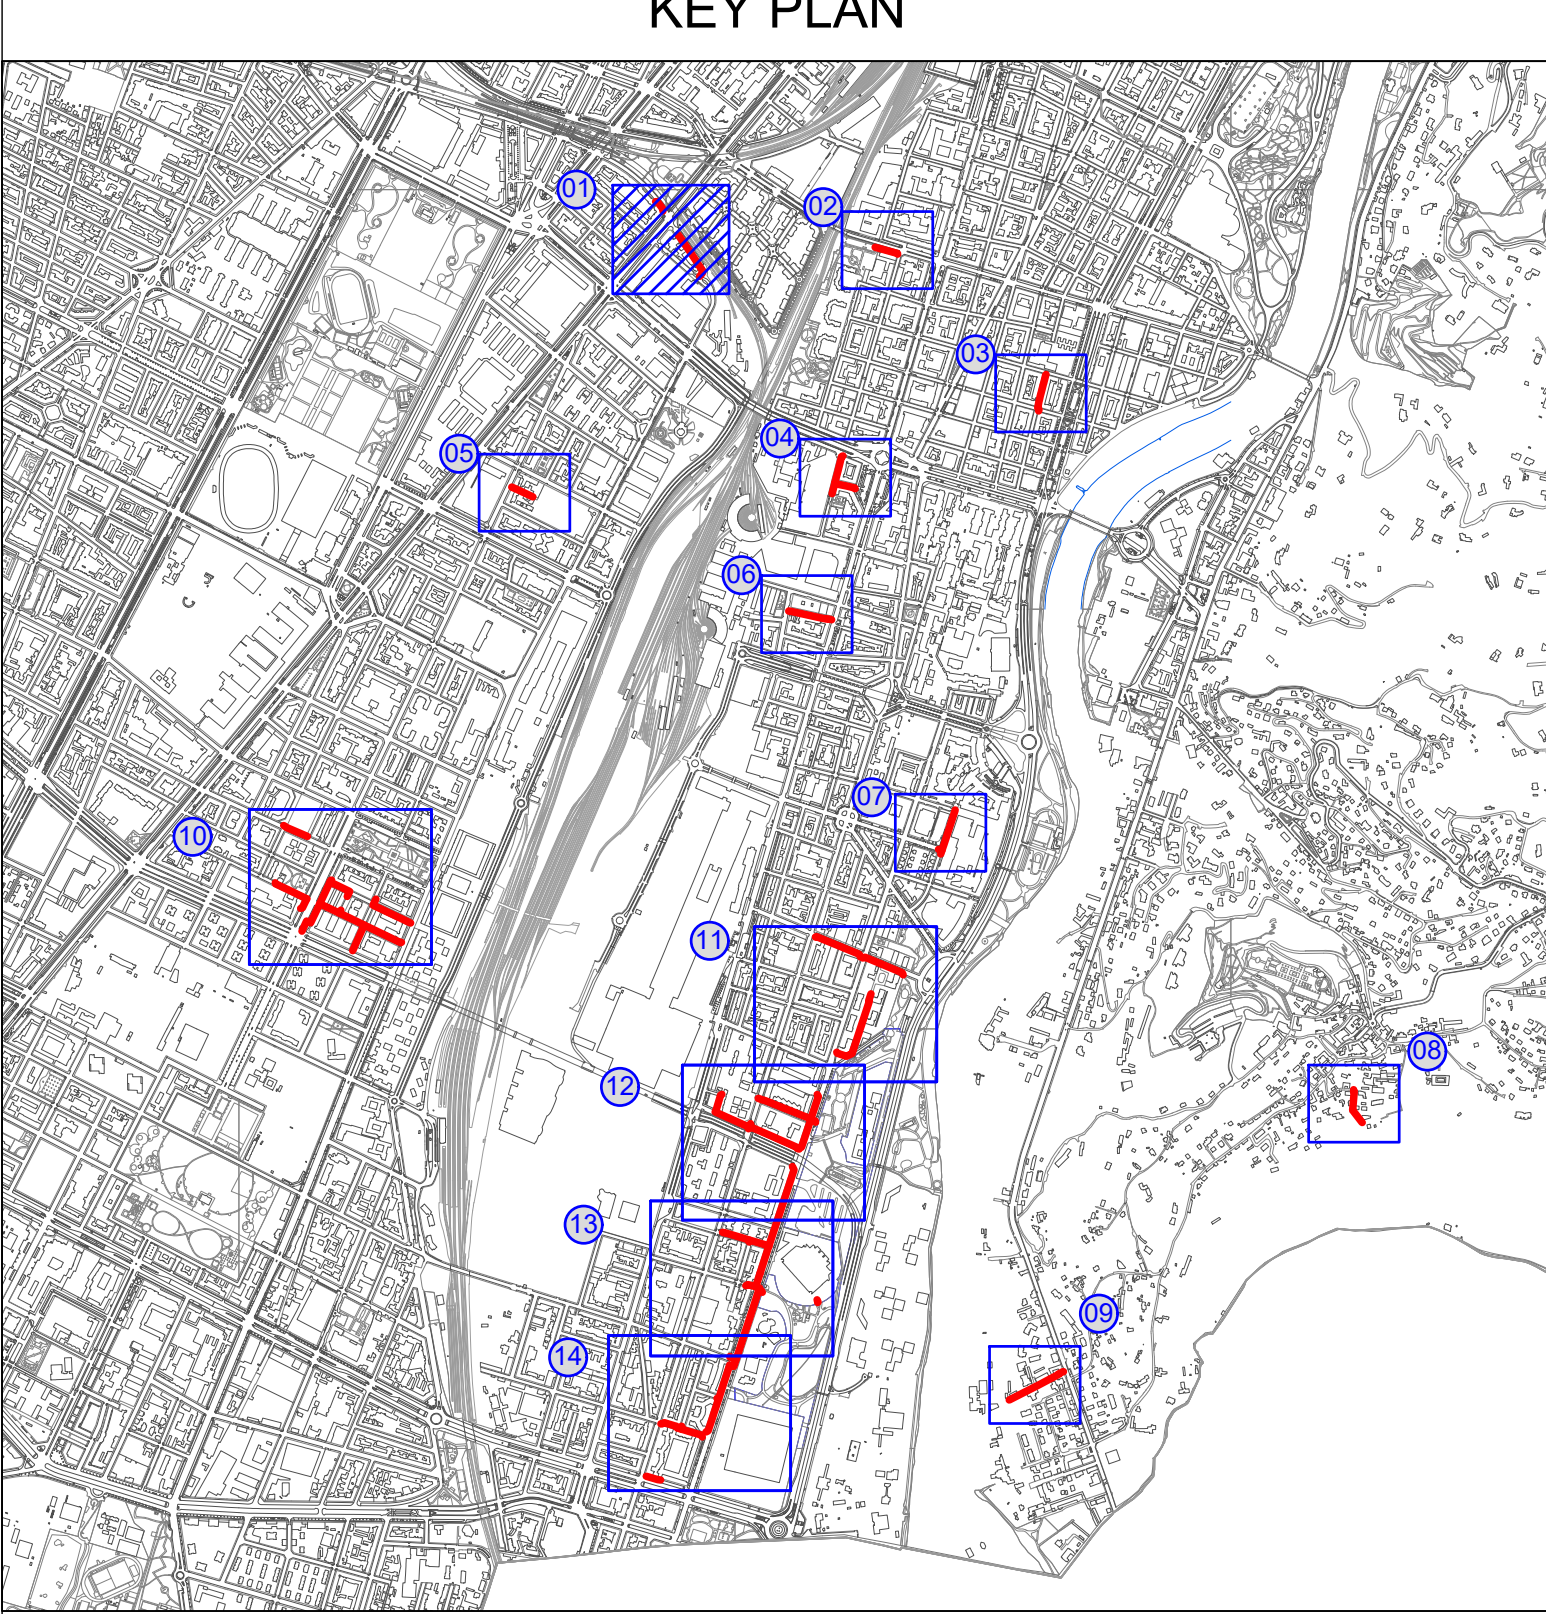

LEGENDA

Rete in progetto BP

Rete in dismissione BP

Zona di lavoro

001

n° Zona di lavoro

Asfalto

Sterrato/area verde

Autobloccanti/ammattionato

Zone di lavoro e pavimentazioni					
n.	dati condotta	tipo superficie	lato strada	Tipo strada	Segnaletica
1	Pe De 180 BP	Asfalto	Sinistra	Comunale	
1	Pe De 180 BP	Asfalto	Sinistra	Comunale	
2	Pe De 180 BP	Autobloccanti	Sinistra	Comunale	
2	Pe De 180 BP	Asfalto	Attraversamento	Comunale	segnaletica di arresto, strisce pedonali
3	Pe De 125 BP	Asfalto	Destra	Comunale	segnaletica parcheggio blu, striscia laterale tratteggiata
4	Pe De 125 BP	Asfalto	Destra	Comunale	segnaletica parcheggio blu, striscia laterale tratteggiata, segnaletica orizzontale freccia
5	Pe De 125 BP	Asfalto	Destra	Comunale	segnaletica parcheggio blu, striscia laterale tratteggiata
6	Pe De 125 BP	Asfalto	Destra	Comunale	segnaletica parcheggio blu, striscia laterale tratteggiata
7	Pe De 125 BP	Asfalto	Destra	Comunale	segnaletica parcheggio blu, strisce pedonali
8	Pe De 125 BP	Asfalto	Destra	Comunale	

LEARDI

Progettista:
Ordine degli Ingegneri di Alessandria
Matteo C. 1701
F. Rina

Unità Responsabile della Progettazione

INGEREAL-INGE-PROGRE

Progetto n°:
21-0584-3E-00-001272
WBS:
SI.20.10300.02.1109
ALLEGATO n°: 6.1

Descrizione:

Nome File: 001.png

Formato: A1 Scala 1 : 500

Committente


Descrizione:

Emissione per commenti

Comm. : 2464

Rev. G. M. A. Redatto Controllato Approvato

Comune di
TORINO (TO)
Vie Varie
Progetto Esecutivo
SOSTITUZIONE RETE BP (L=2745.39 M) - GARA TO 1
Intervento n° SI-038213-001272-TSS-TORIN008
Planimetria pavimentazioni e zone di lavoro - Tavola 1

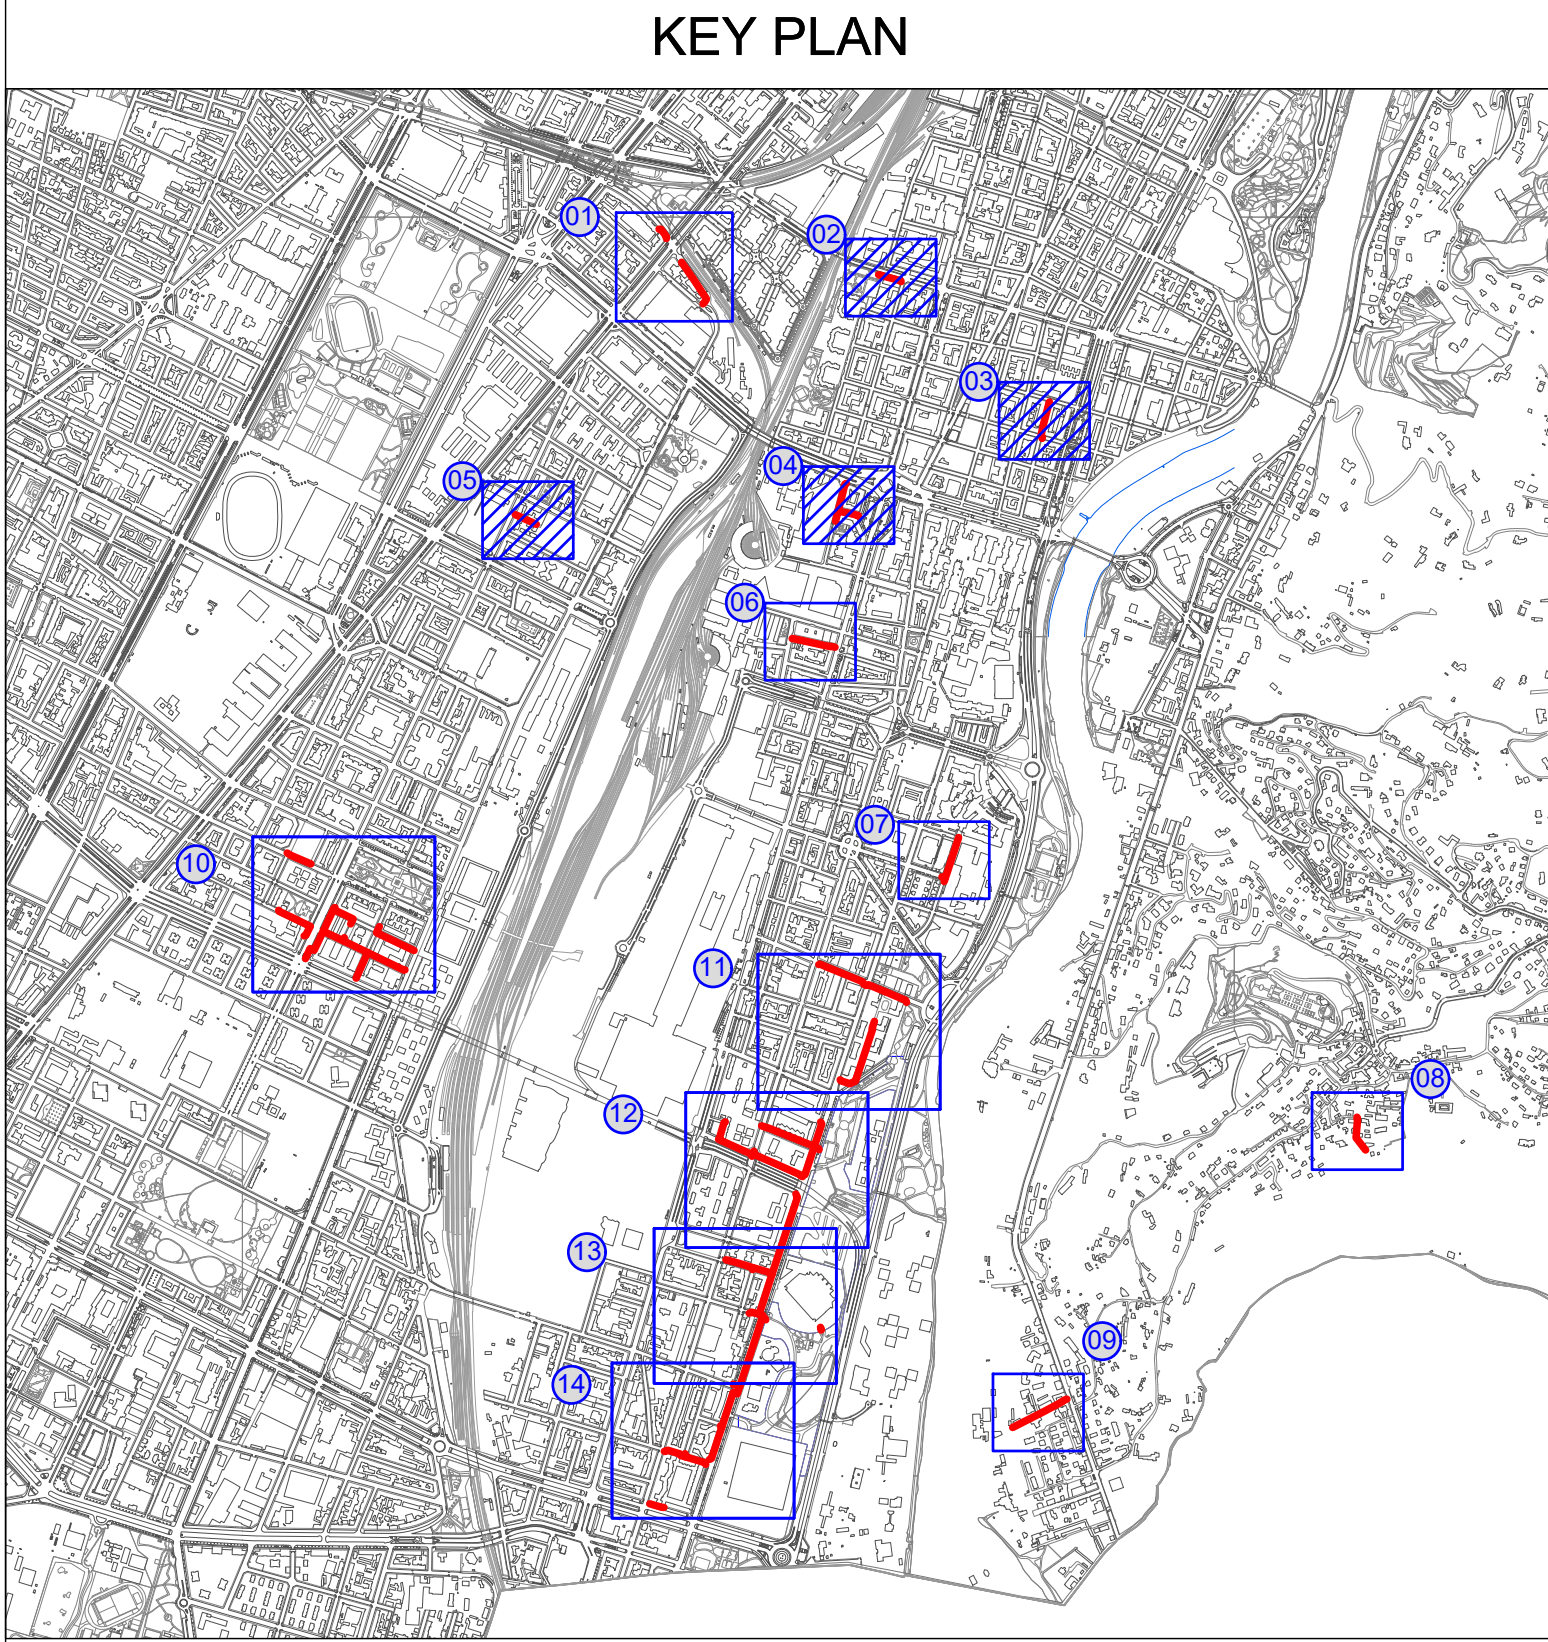

LEGENDA

	Reti in progetto BP		n° Zona di lavoro
	Reti in dismissione BP		Asfalto
	Zona di lavoro		Sternatore/area verde
			Autobloccanti/ammattinato

Zone di lavoro e pavimentazioni (Riquadro 2)

n.	dell'condotta	caratteristiche bar	tipo superficie	lato strada	tipo strada	Segnaletica
9	Pi De 125	BP	Asfalto	Destra	Comunale	segnaletica parcheggio blu
10	Pi De 125	BP	Asfalto	Destra	Comunale	segnaletica parcheggio blu
11	Pi De 125	BP	Asfalto	Destra	Comunale	segnaletica parcheggio blu, segnaletica di arresto

Zone di lavoro e pavimentazioni (Riquadro 3)

n.	dell'condotta	caratteristiche bar	tipo superficie	lato strada	tipo strada	Segnaletica
12	Pi De 150	BP	Asfalto	Sinistra	Comunale	strisce pedonali
13	Pi De 150	BP	Asfalto	Sinistra	Comunale	striscia parcheggio blu
14	Pi De 150	BP	Asfalto	Sinistra	Comunale	striscia parcheggio blu
15	Pi De 150	BP	Asfalto	Sinistra	Comunale	striscia parcheggio blu
16	Pi De 150	BP	Asfalto	Sinistra	Comunale	striscia parcheggio blu, doppia strisce pedonali

Zone di lavoro e pavimentazioni (Riquadro 4)

n.	dell'condotta	caratteristiche bar	tipo superficie	lato strada	tipo strada	Segnaletica
17	Pi De 150	BP	Asfalto	Sinistra	Comunale	strisce pedonali, linea strasversale di dare precedenza
18	Pi De 150	BP	Asfalto	Sinistra	Comunale	
19	Pi De 150	BP	Asfalto	Sinistra	Comunale	strisce pedonali
20	Pi De 150	BP	Asfalto	Attraversamento	Comunale	
21	Pi De 150	BP	Asfalto	Sinistra	Comunale	strisce pedonali
22	Pi De 150	BP	Asfalto	Sinistra	Comunale	
23	Pi De 150	BP	Asfalto	Destra	Comunale	
24	Pi De 150	BP	Asfalto	Destra	Comunale	linea parcheggio gialla disabili

Zone di lavoro e pavimentazioni (Riquadro 5)

n.	dell'condotta	caratteristiche bar	tipo superficie	lato strada	tipo strada	Segnaletica
25	Pi De 125	BP	Asfalto	Destra	Privata	
26	Pi De 125	BP	Asfalto	Destra	Privata	
27	Pi De 125	BP	Asfalto	Destra	Privata	

LEARDI

Progetto n°: 21-0584-3E-00-001272
VBS: SI.20.10300.02.1109
ALLEGATO n°: 6.2


Formato: A0 Scale 1: 500



Comune di TORINO (TO)
Via Vane
Progetto Esecutivo
SOSTITUZIONE RETE BP (L=2745,39 M) - GARA TO 1
Intervento n° SI-036213-001272-TSS-TORINO06
Planimetria pavimentazioni e zone di lavoro - Tavola 2

Unità Responsabile della Progettazione
INGENERAL-INGE-PROGRE

Comitato di Progetto
Direttore: [Nome]
Vice Direttore: [Nome]
Relatore: [Nome]
Redatto: [Nome]
Controllato: [Nome]
Approvato: [Nome]

Il presente elaborato è di proprietà aziendale - La società tutela i propri diritti a termini di legge.

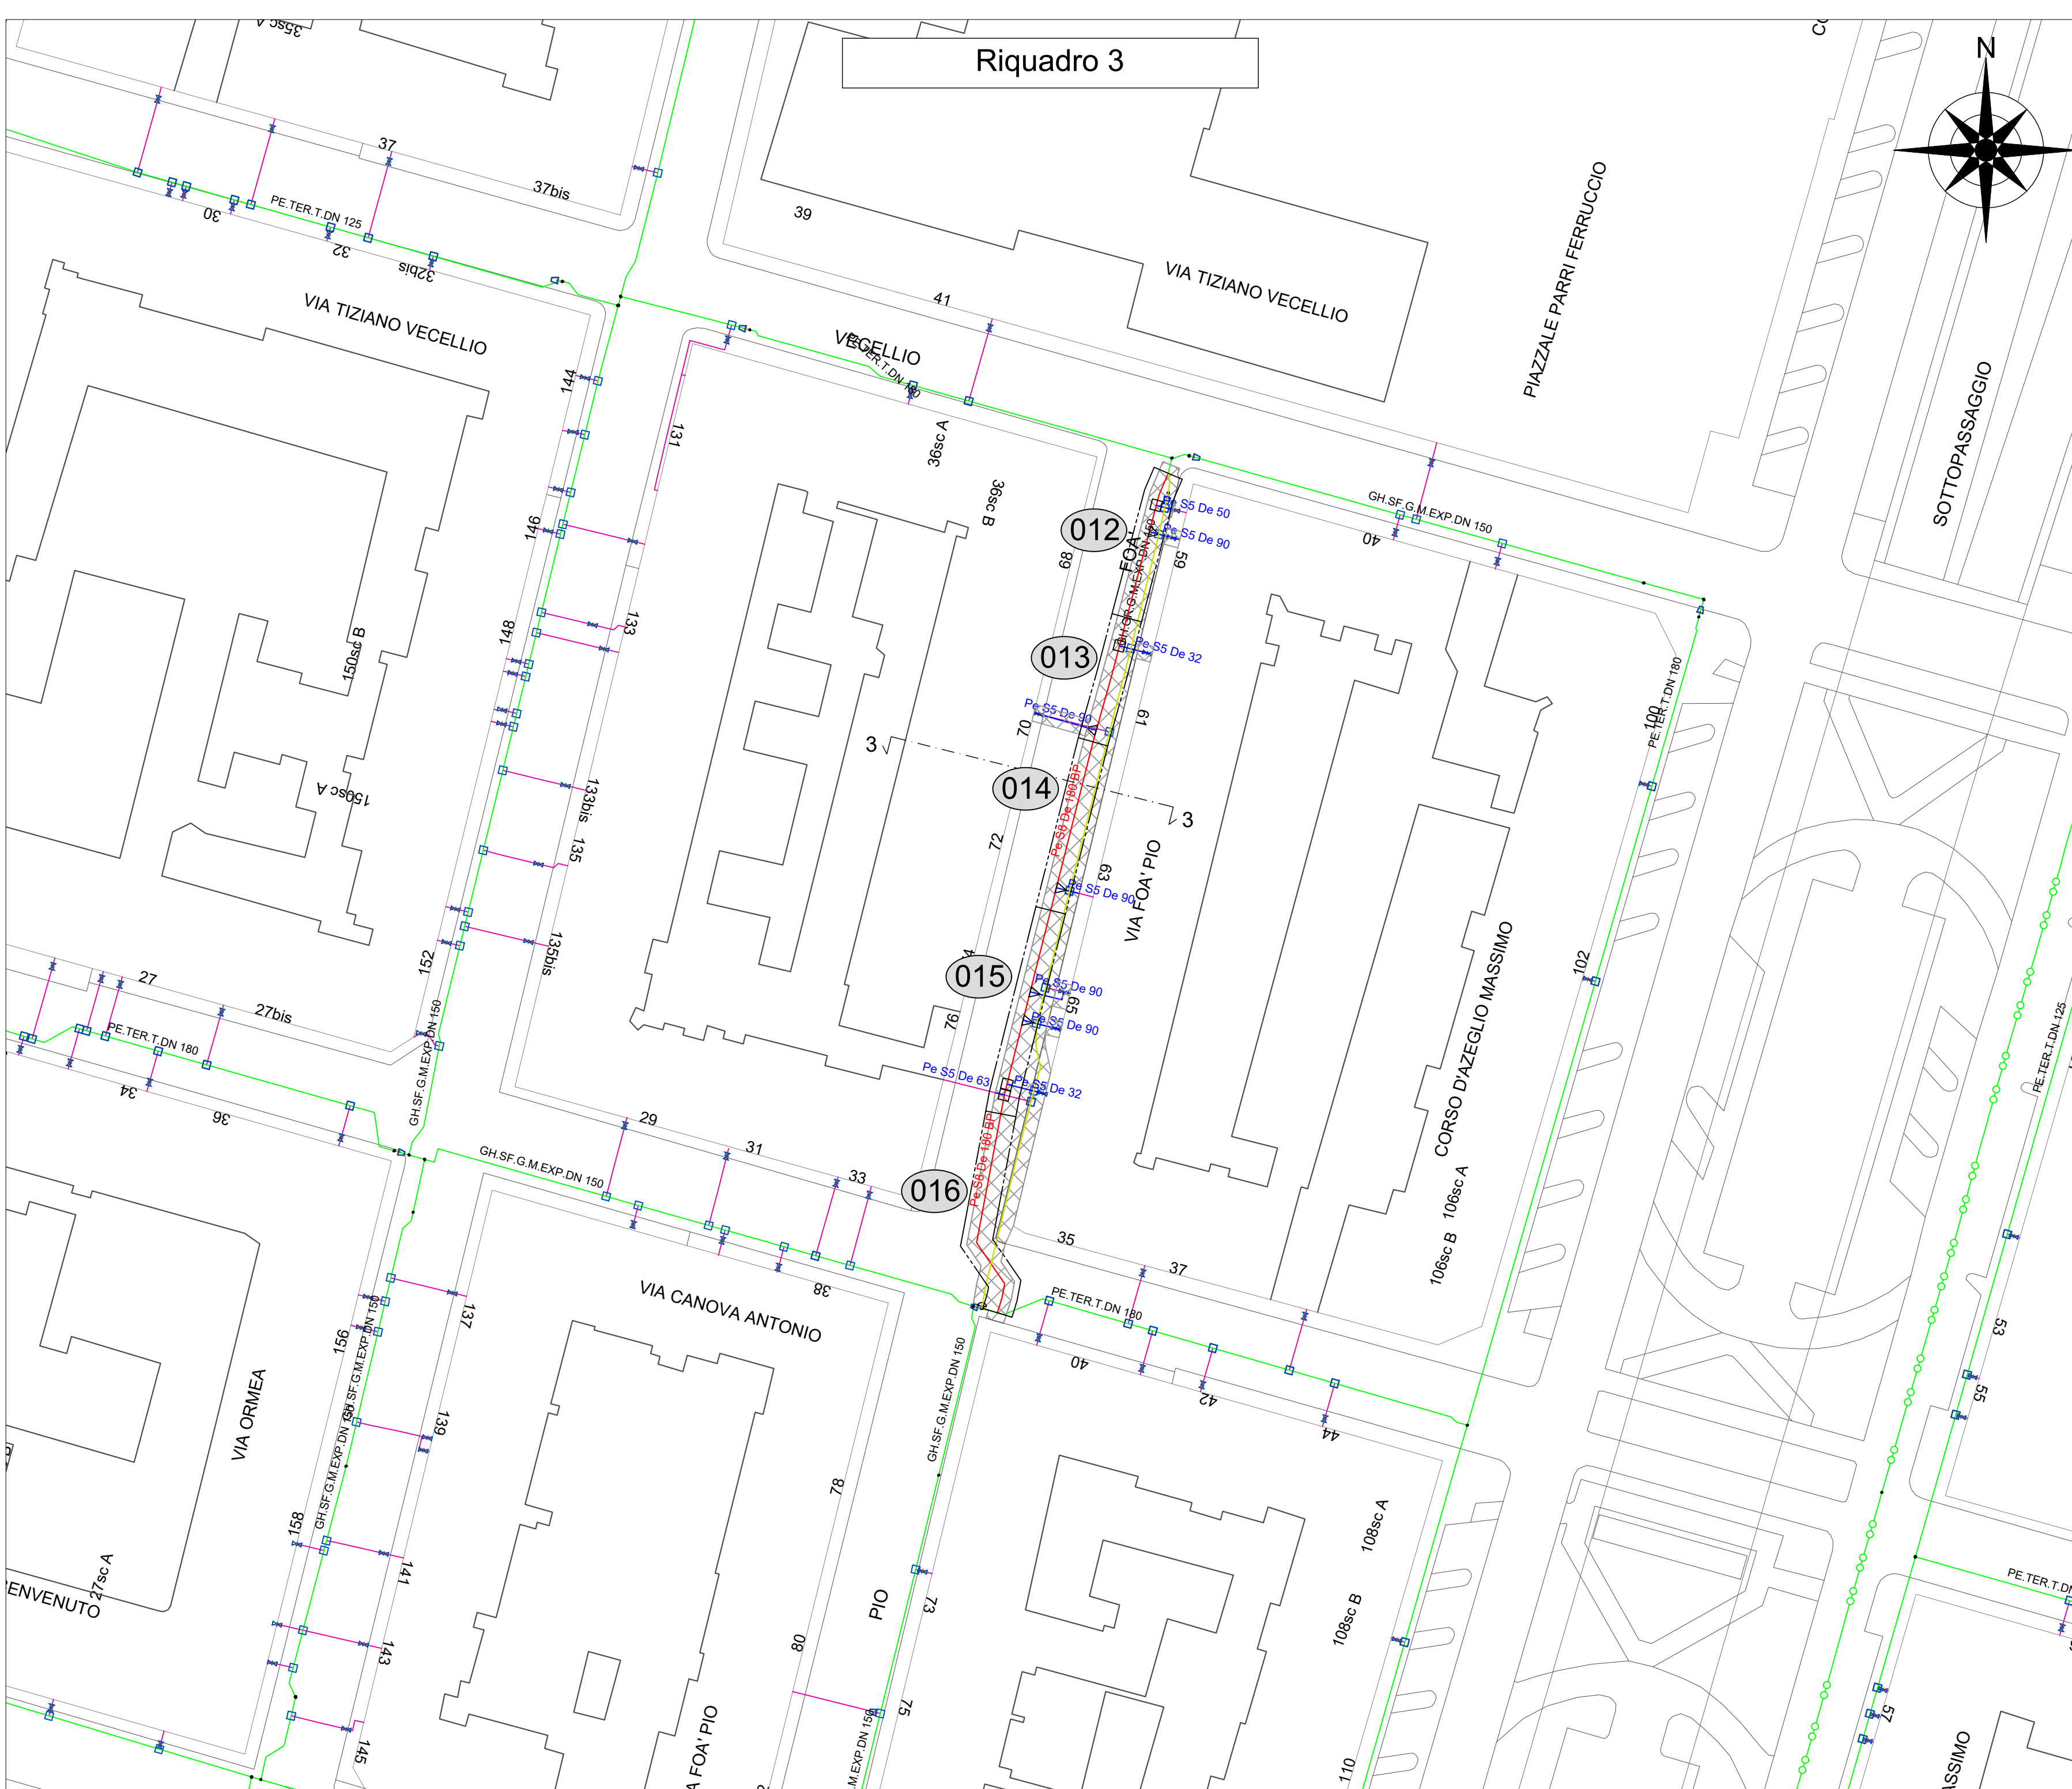

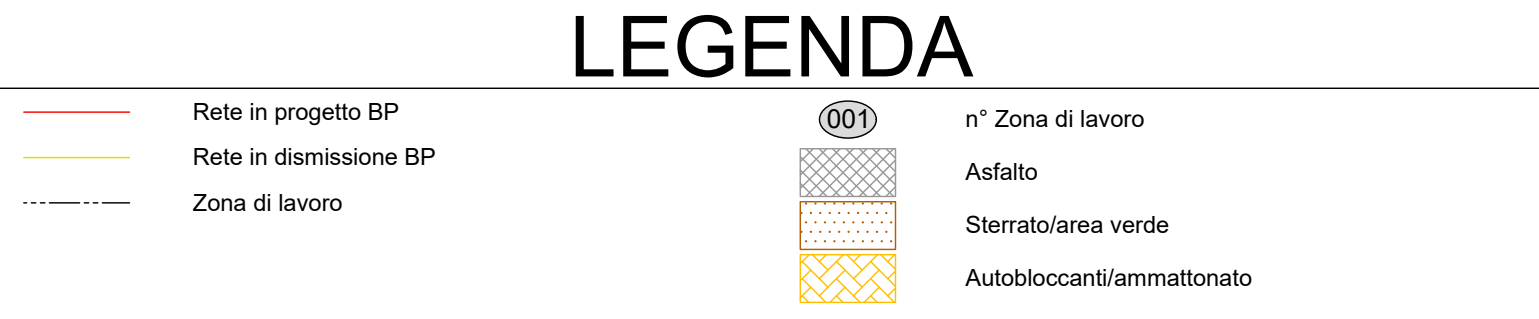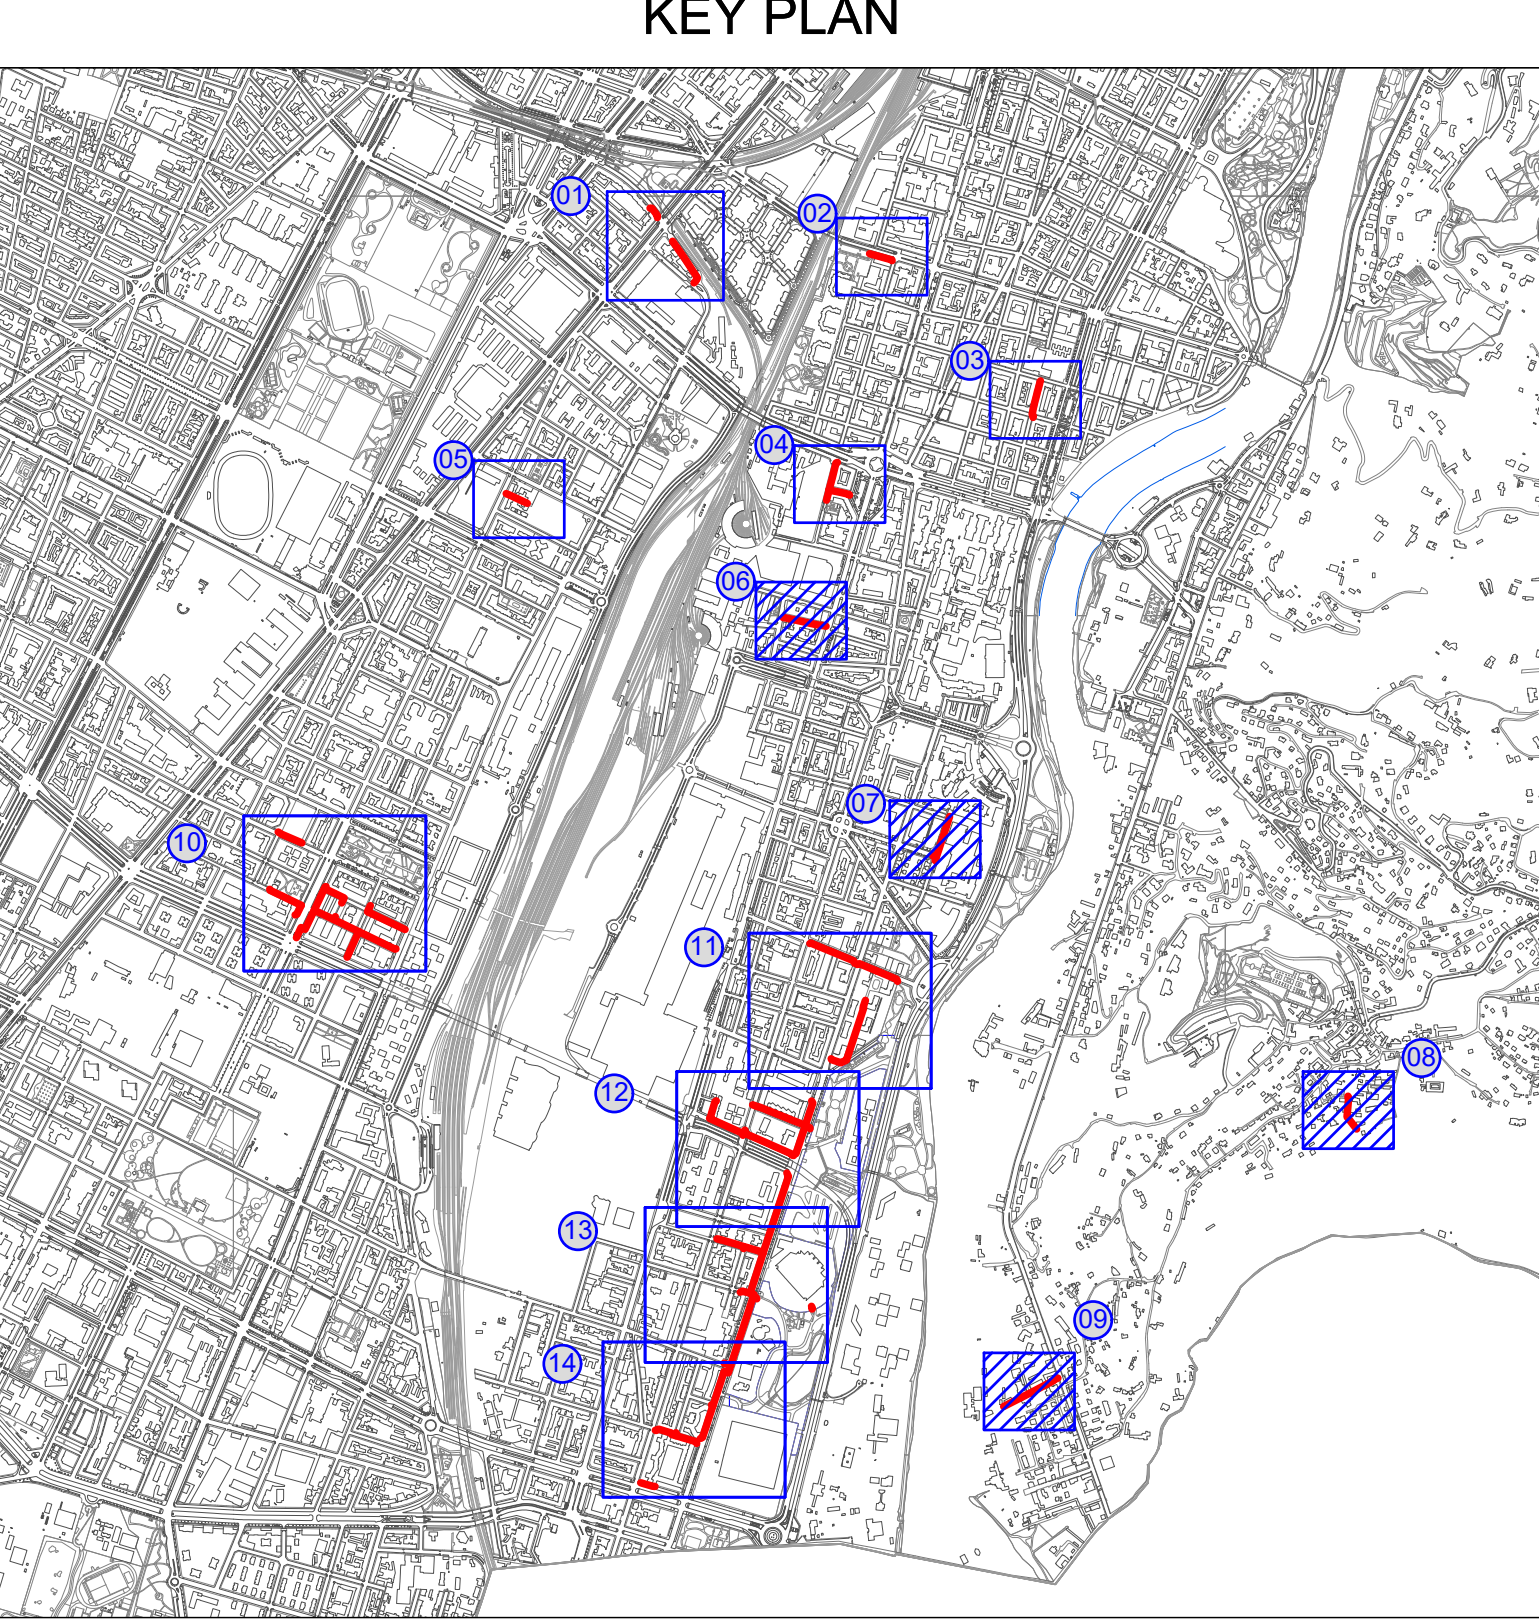

Zone di lavoro e pavimentazioni (Riquadro 6)

n.	dell' condotta	caratteristiche	tipo superficie	lato strada	Tipo strada	Segnaletica
28	Pi De 125	BP	Asfalto	Destra	Comunale	strisce pedonali, linee di parcheggio
29	Pi De 125	BP	Asfalto	Destra	Comunale	linea galleria carico e scarico
30	Pi De 125	BP	Asfalto	Destra	Comunale	
31	Pi De 125	BP	Asfalto	Destra	Comunale	strisce pedonali
32	Pi De 125	BP	Asfalto	Destra	Comunale	strisce pedonali

Zone di lavoro e pavimentazioni (Riquadro 7)

n.	dell' condotta	caratteristiche	tipo superficie	lato strada	Tipo strada	Segnaletica
33	Pi De 315	BP	Asfalto	Destra	Comunale	strisce pedonali, striscia longitudinale continua laterale
33	Pi De 315	BP	Asfalto	Attraversamento	Comunale	
34	Pi De 315	BP	Asfalto	Destra	Comunale	striscia longitudinale continua laterale
35	Pi De 315	BP	Asfalto	Destra	Comunale	striscia longitudinale tratteggiata laterale, striscia pedonale linee di parcheggio, linea di parcheggio, linea di parcheggio, linea di parcheggio
36	Pi De 315	BP	Asfalto	Destra	Comunale	striscia tratteggiata laterale, linee di parcheggio, linea di parcheggio
37	Pi De 315	BP	Asfalto	Destra	Comunale	linea continua laterale
38	Pi De 315	BP	Asfalto	Attraversamento	Comunale	
39	Pi De 315	BP	Asfalto	Destra	Comunale	
39	Pi De 315	BP	Asfalto	Centro	Comunale	strisce pedonali

Zone di lavoro e pavimentazioni (Riquadro 8)

n.	dell' condotta	caratteristiche	tipo superficie	lato strada	Tipo strada	Segnaletica
40	Pi De 125	BP	Asfalto	Attraversamento	Comunale	
40	Pi De 125	BP	Asfalto	Centro	Comunale	
41	Pi De 125	BP	Asfalto	Centro	Comunale	
42	Pi De 125	BP	Asfalto	Centro	Comunale	
43	Pi De 125	BP	Asfalto	Sinistra	Comunale	

Zone di lavoro e pavimentazioni (Riquadro 9)

n.	dell' condotta	caratteristiche	tipo superficie	lato strada	Tipo strada	Segnaletica
44	Pi De 125	BP	Asfalto	Destra	Comunale	strisce pedonali
45	Pi De 125	BP	Asfalto	Centro	Comunale	
46	Pi De 125	BP	Asfalto	Centro	Comunale	
47	Pi De 125	BP	Asfalto	Centro	Comunale	
48	Pi De 125	BP	Asfalto	Centro	Comunale	
49	Pi De 125	BP	Asfalto	Centro	Comunale	
50	Pi De 125	BP	Asfalto	Centro	Comunale	

Progetto n°: 21-0584-3E-00-001272
WBS: SI20.I0300.02.1109
ALLEGATO n°: 6.3


Progettista: Ordine degli Ingegneri Alessandria
Ingegnere: Ing. Alessandria
Ingegnere: Ing. Alessandria


Unità Responsabile della Progettazione
INGENERAL-INGE-PROGRE

Comune di TORINO (TO)
Via Vane
Progetto Esecutivo
SOSTITUZIONE RETE BP (L=2745,39 M) - GARA TO 1
Intervento n° SI-036213-001272-TSS-TORIN008
Planimetria pavimentazioni e zone di lavoro - Tavola 3

Formato: A0
Scale: 1:500

Comune di TORINO (TO)
Via Vane
Progetto Esecutivo
SOSTITUZIONE RETE BP (L=2745,39 M) - GARA TO 1
Intervento n° SI-036213-001272-TSS-TORIN008
Planimetria pavimentazioni e zone di lavoro - Tavola 3

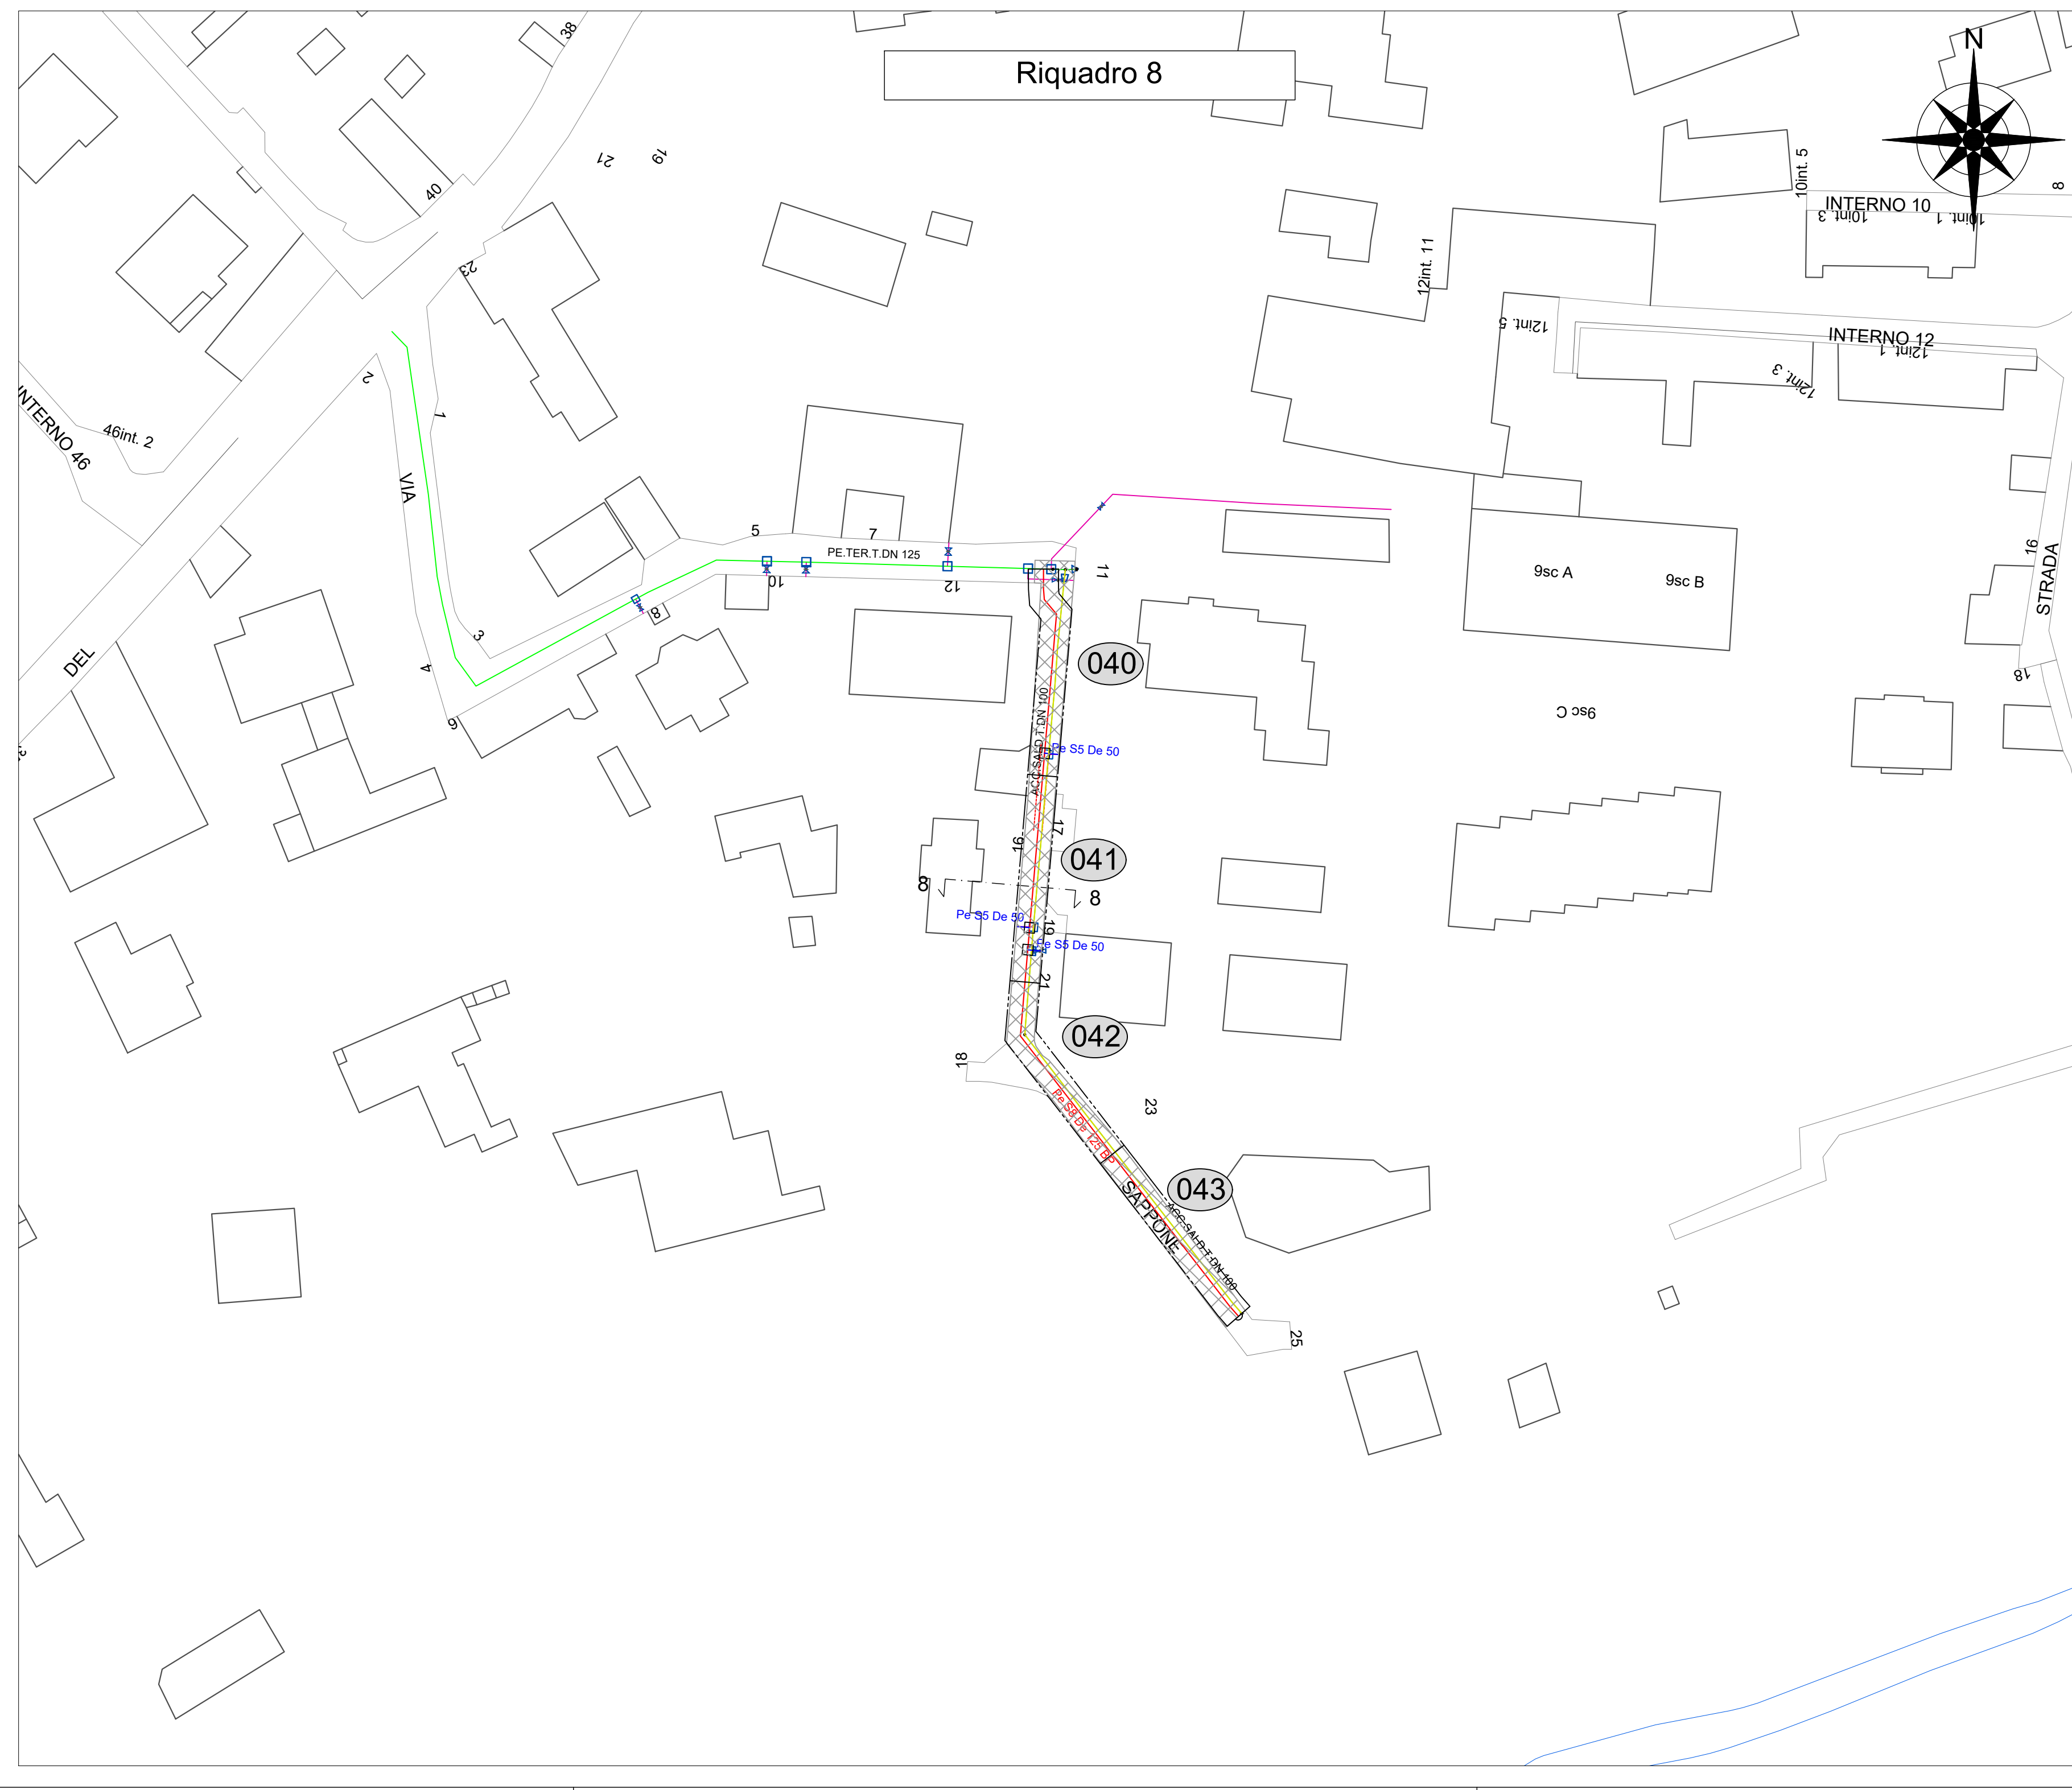

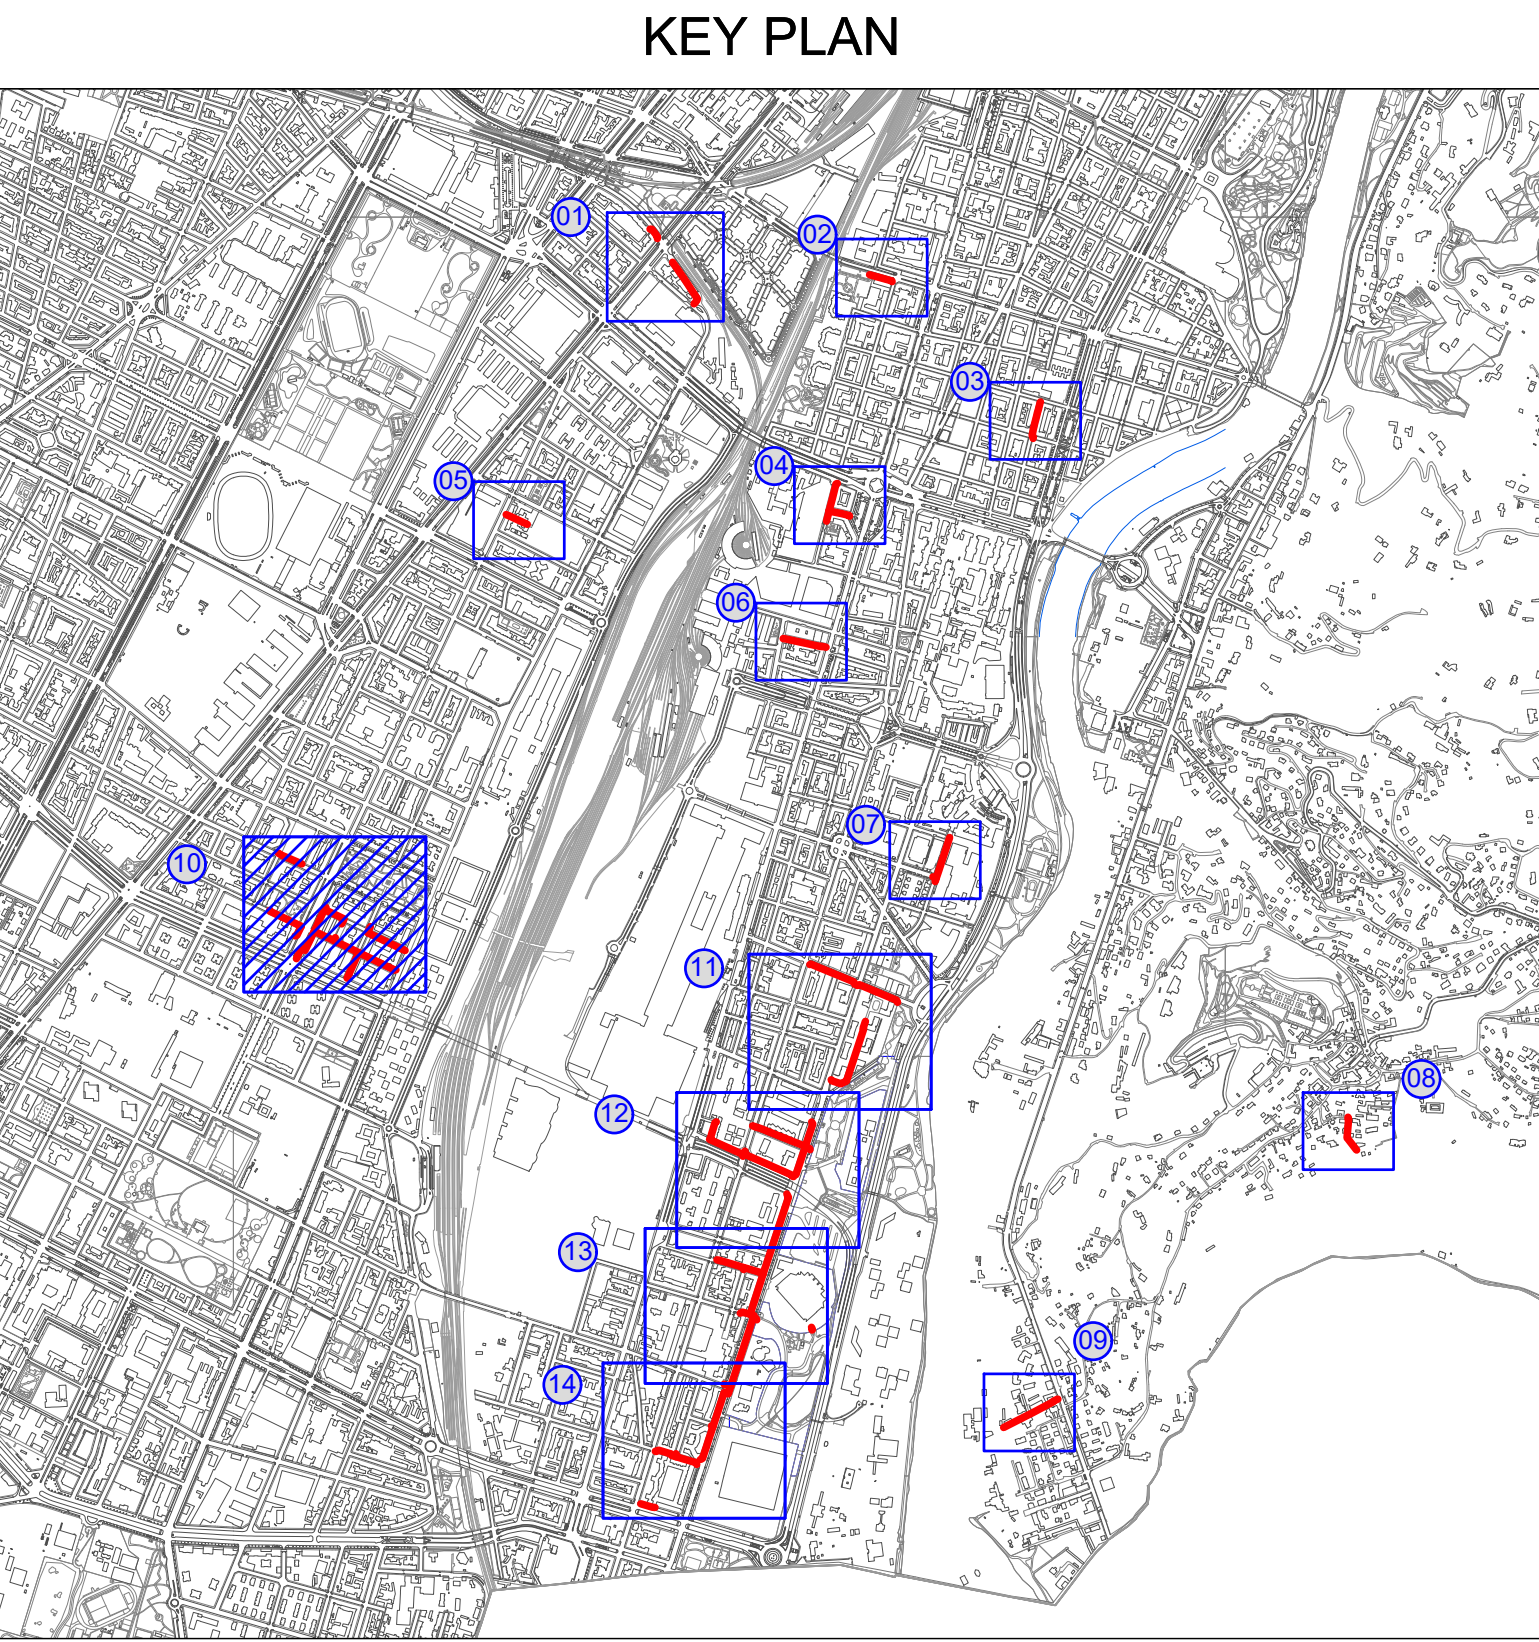

LEGENDA

Rete in progetto BP

Rete in dismissione BP

Zona di lavoro

n° Zona di lavoro

Asfalto

Sterzo/area verde

Autobloccanti/ammattionato

Zone di lavoro e pavimentazioni				
n.	del condotto	caratteristica	tipo superficie	Segnaletica
51	Pe De 225	BP	Asfalto	Attraversamento Comune
51	Pe De 225	BP	Asfalto	Sinistra Comune
53	Pe De 225	BP	Asfalto	Sinistra Comune
53	Pe De 225	BP	Asfalto	Sinistra Comune
54	Pe De 180	BP	Asfalto	Attraversamento Comune
54	Pe De 180	BP	Asfalto	Destra Comune
55	Pe De 180	BP	Asfalto	Destra Comune
56	Pe De 180	BP	Asfalto	Attraversamento Comune
57	Pe De 315	BP	Asfalto	Sinistra Comune
57	Pe De 180	BP	Asfalto	Destra Comune
58	Pe De 315	BP	Asfalto	Sinistra Comune
59	Pe De 315	BP	Asfalto	Sinistra Comune
59	Pe De 315	BP	Asfalto	Attraversamento Comune
60	Pe De 125	BP	Asfalto	Attraversamento Comune
60	Pe De 180	BP	Asfalto	Sinistra Comune
61	Pe De 125	BP	Asfalto	Sinistra Comune
62	Pe De 125	BP	Asfalto	Sinistra Comune
63	Pe De 125	BP	Asfalto	Attraversamento Comune
63	Pe De 125	BP	Asfalto	Sinistra Comune
64	Pe De 180	BP	Asfalto	Sinistra Comune
65	Pe De 180	BP	Asfalto	Sinistra Comune
66	Pe De 180	BP	Asfalto	Sinistra Comune
67	Pe De 180	BP	Asfalto	Attraversamento Comune
67	Pe De 180	BP	Asfalto	Sinistra Comune
68	Pe De 180	BP	Asfalto	Sinistra Comune
69	Pe De 180	BP	Asfalto	Sinistra Comune
70	Pe De 180	BP	Asfalto	Sinistra Comune
71	Pe De 180	BP	Asfalto	Sinistra Comune
72	Pe De 180	BP	Asfalto	Sinistra Comune
73	Pe De 180	BP	Asfalto	Attraversamento Comune
73	Pe De 180	BP	Asfalto	Sinistra Comune
74	Pe De 180	BP	Asfalto	Attraversamento Comune
74	Pe De 180	BP	Asfalto	Sinistra Comune
75	Pe De 180	BP	Asfalto	Sinistra Comune
76	Pe De 180	BP	Asfalto	Sinistra Comune
77	Pe De 180	BP	Asfalto	Sinistra Comune
78	Pe De 180	BP	Asfalto	Sinistra Comune
79	Pe De 180	BP	Asfalto	Sinistra Comune
80	Pe De 180	BP	Asfalto	Sinistra Comune
81	Pe De 180	BP	Asfalto	Sinistra Comune
81	Pe De 180	BP	Autobloccanti	Sinistra Comune
82	Pe De 180	BP	Asfalto	Destra Comune
83	Pe De 180	BP	Asfalto	Destra Comune
84	Pe De 180	BP	Asfalto	Attraversamento Comune
84	Pe De 180	BP	Sterzo	Attraversamento Comune
84	Pe De 180	BP	Asfalto	Destra Comune
84	Pe De 180	BP	Asfalto	Sinistra Comune
85	Pe De 180	BP	Asfalto	Destra Comune
86	Pe De 180	BP	Asfalto	Attraversamento Comune
87	Pe De 180	BP	Asfalto	Destra Comune
88	Pe De 180	BP	Asfalto	Destra Comune
89	Pe De 180	BP	Asfalto	Destra Comune
90	Pe De 180	BP	Asfalto	Destra Comune
91	Pe De 180	BP	Asfalto	Destra Comune
201	Pe De 125	BP	Asfalto	Attraversamento Comune
201	Pe De 180	BP	Asfalto	Destra Comune
202	Pe De 125	BP	Asfalto	Sinistra Comune

LEARDI

Progetto n°: 21-0864-3E-00-00/1272
S120.10300.02.1109
ALLEGATO n°: 6.4

Revisione

Emissione per commenti

Formattato: A0

Scale: 1 : 500

Comittente

Comune di TORINO (TO)
Via Vane
Progetto Esecutivo
SOSTITUZIONE RETE BP (L=2745,39 M) - GARA TO 1
Intervento n° SI-0362-13-001272-TSS-TORINO08
Planimetria pavimentazioni e zone di lavoro - Tavola 4

Progetto:

Ordine degli ingegneri di Alessandria
matteo.rossi@ing.it

Unità Responsabile della Progettazione

INGENERAL-INGE-PROGRE

Progetto n°: 21-0864-3E-00-00/1272
S120.10300.02.1109
ALLEGATO n°: 6.4

Revisione

Emissione per commenti


Formattato: A0

Scale: 1 : 500

Comittente

Comune di TORINO (TO)
Via Vane
Progetto Esecutivo
SOSTITUZIONE RETE BP (L=2745,39 M) - GARA TO 1
Intervento n° SI-0362-13-001272-TSS-TORINO08
Planimetria pavimentazioni e zone di lavoro - Tavola 4

Il presente elaborato è di proprietà aziendale - La società tutela i propri diritti a termini di legge.

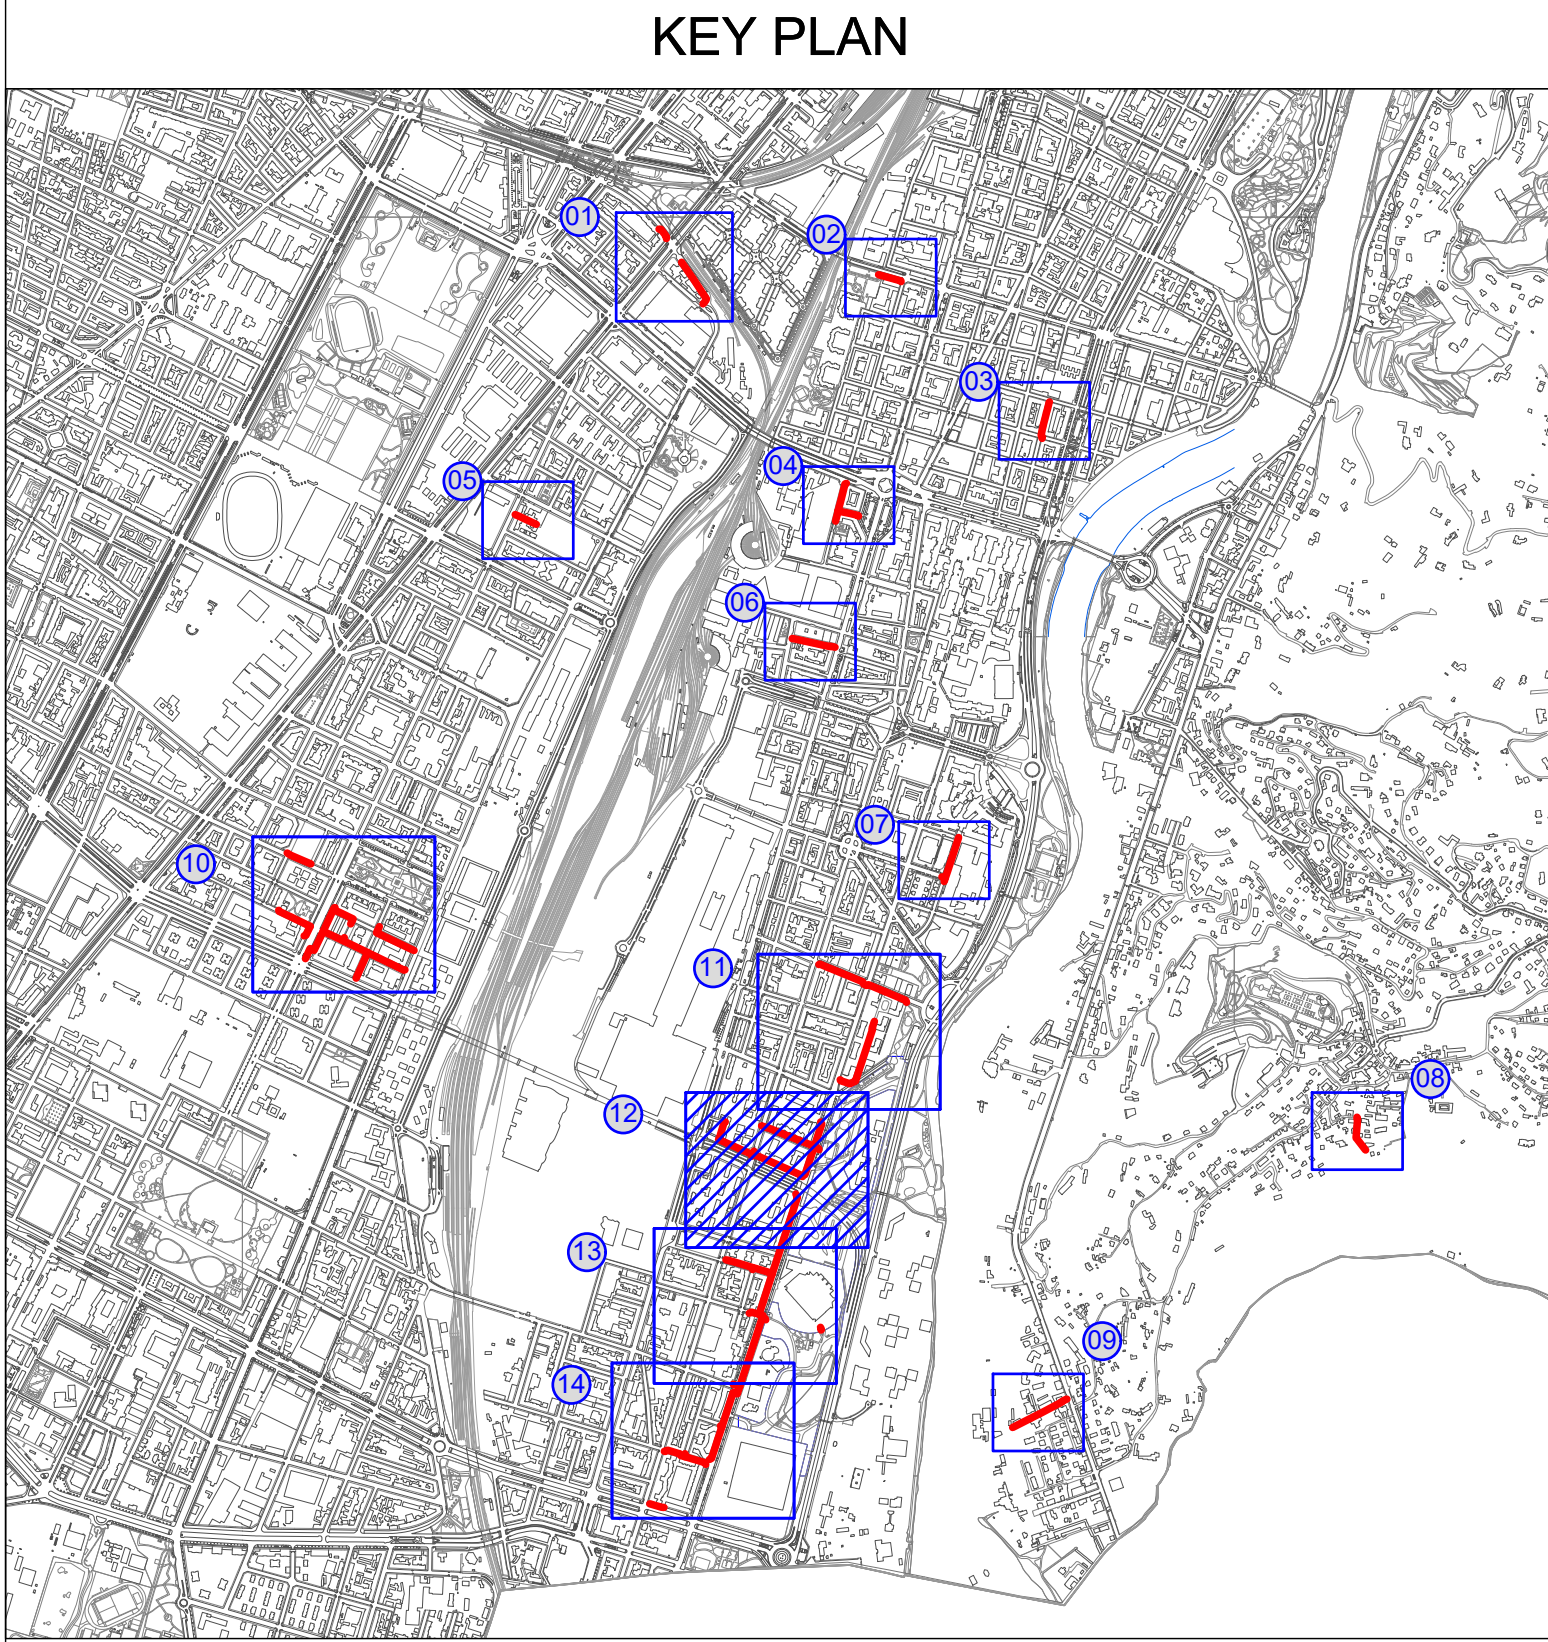

LEGENDA

	Rete in progetto BP
	Rete in dismissione BP
	Zona di lavoro
	n° Zona di lavoro
	Asfalto
	Sternatore/area verde
	Autobloccanti/ammattinato

Zone di lavoro e pavimentazioni					
n.	dati condotta caratteristiche bar	tipo superficie	lato strada	Tipologia strada	Segnaletica
112	Pe De 315 BP	Autobloccanti	Attraversamento	Comunale	linee parcheggio disabili
112	Pe De 315 BP	Asfalto	Attraversamento	Comunale	
112	Pe De 315 BP	Asfalto	Destra	Comunale	
113	Pe De 315 BP	Asfalto	Destra	Comunale	linea parcheggio, linea tratteggiata di mezzaraja
114	Pe De 315 BP	Asfalto	Destra	Comunale	linea parcheggio, linea tratteggiata di mezzaraja
115	Pe De 180 BP	Asfalto	Attraversamento	Comunale	linea di trasversale di dare precedenza, linea tratteggiata di dare precedenza
115	Pe De 315 BP	Asfalto	Destra	Comunale	
115	Pe De 225 BP	Asfalto	Attraversamento	Comunale	
116	Pe De 225 BP	Asfalto	Destra	Comunale	strisce pedonali
117	Pe De 225 BP	Asfalto	Destra	Comunale	
118	Pe De 225 BP	Asfalto	Destra	Comunale	linea di parcheggio gialla disabili, linea di parcheggio
119	Pe De 225 BP	Asfalto	Destra	Comunale	
120	Pe De 225 BP	Asfalto	Destra	Comunale	linea di parcheggio disabili, linea di parcheggio carico e scarico
121	Pe De 225 BP	Asfalto	Destra	Comunale	strisce pedonali
122	Pe De 225 BP	Asfalto	Destra	Comunale	
123	Pe De 180 BP	Asfalto	Attraversamento	Comunale	doppia striscia continua di mezzaraja, strisce tratteggiate, striscia gialla fermata autobus
124	Pe De 315 BP	Asfalto	Destra	Comunale	striscia gialla fermata autobus, segnaletica attraversamento barriera, linea tratteggiata di corsia
125	Pe De 315 BP	Asfalto	Destra	Comunale	striscia gialla fermata autobus, linea tratteggiata di corsia
126	Pe De 315 BP	Asfalto	Destra	Comunale	striscia gialla fermata autobus, linea tratteggiata di corsia, segnaletica di arresto
127	Pe De 315 BP	Asfalto	Destra	Comunale	strisce pedonali
128	Pe De 315 BP	Asfalto	Destra	Comunale	
129	Pe De 315 BP	Asfalto	Destra	Comunale	
130	Pe De 315 BP	Asfalto	Destra	Comunale	
131	Pe De 315 BP	Asfalto	Destra	Comunale	linea di parcheggio gialla disabili
132	Pe De 315 BP	Asfalto	Destra	Comunale	linea di parcheggio gialla disabili, segnaletica di arresto, strisce pedonali
132	Pe De 315 BP	Asfalto	Attraversamento	Comunale	
133	Pe De 315 BP	Asfalto	Attraversamento	Comunale	strisce pedonali
133	Pe De 315 BP	Asfalto	Destra	Comunale	
133	Pe De 315 BP	Asfalto	Attraversamento	Comunale	
133	Pe De 180 BP	Asfalto	Destra	Comunale	
134	Pe De 315 BP	Asfalto	Sinistra	Comunale	
134	Pe De 315 BP	Asfalto	Attraversamento	Comunale	
135	Pe De 315 BP	Asfalto	Attraversamento	Comunale	
136	Pe De 180 BP	Asfalto	Destra	Comunale	strisce pedonali
137	Pe De 180 BP	Asfalto	Destra	Comunale	
138	Pe De 180 BP	Asfalto	Destra	Comunale	
139	Pe De 180 BP	Asfalto	Destra	Comunale	
139	Pe De 180 BP	Asfalto	Attraversamento	Comunale	strisce pedonali
140	Pe De 180 BP	Asfalto	Destra	Comunale	
141	Pe De 180 BP	Asfalto	Destra	Comunale	
141	Pe De 180 BP	Asfalto	Attraversamento	Comunale	strisce pedonali
142	Pe De 180 BP	Asfalto	Attraversamento	Comunale	
142	Pe De 315 BP	Asfalto	Destra	Comunale	
143	Pe De 315 BP	Asfalto	Destra	Comunale	striscia continua di corsia, rallentatori ottici
144	Pe De 315 BP	Asfalto	Destra	Comunale	striscia continua di corsia, rallentatori ottici
145	Pe De 315 BP	Asfalto	Destra	Comunale	linea gialla di parcheggio disabili, strisce pedonali, linea continua di corsia
146	Pe De 315 BP	Asfalto	Destra	Comunale	linea tratteggiata di corsia
147	Pe De 315 BP	Asfalto	Destra	Comunale	linea tratteggiata di corsia

Progetto n°: 21-0584-3E-00-001272
VBS: SI.20.10300.02.1109
ALLEGATO n°: 6.6


Progettista:

Unità Responsabile della Progettazione: INGEGNERIA-INGE-PROGRE

Revisione	0	30	11	25	A. Saroni	L. Contarini	A. Leardi
Emendato per commenti							
Formato: A0	Scale: 1:500	Comm: 2484	Redatto	Controllato	Approvato		

Comune di TORINO (TO)
Via Vane
Progetto Esecutivo
SOSTITUZIONE RETE BP (L=2745,39 M) - GARA TO 1
Intervento n° SI-036213-011212-TSS-TORINO08
Planimetria pavimentazioni e zone di lavoro - Tavola 6

Il presente elaborato è di proprietà aziendale - La società tutela i propri diritti a termini di legge.

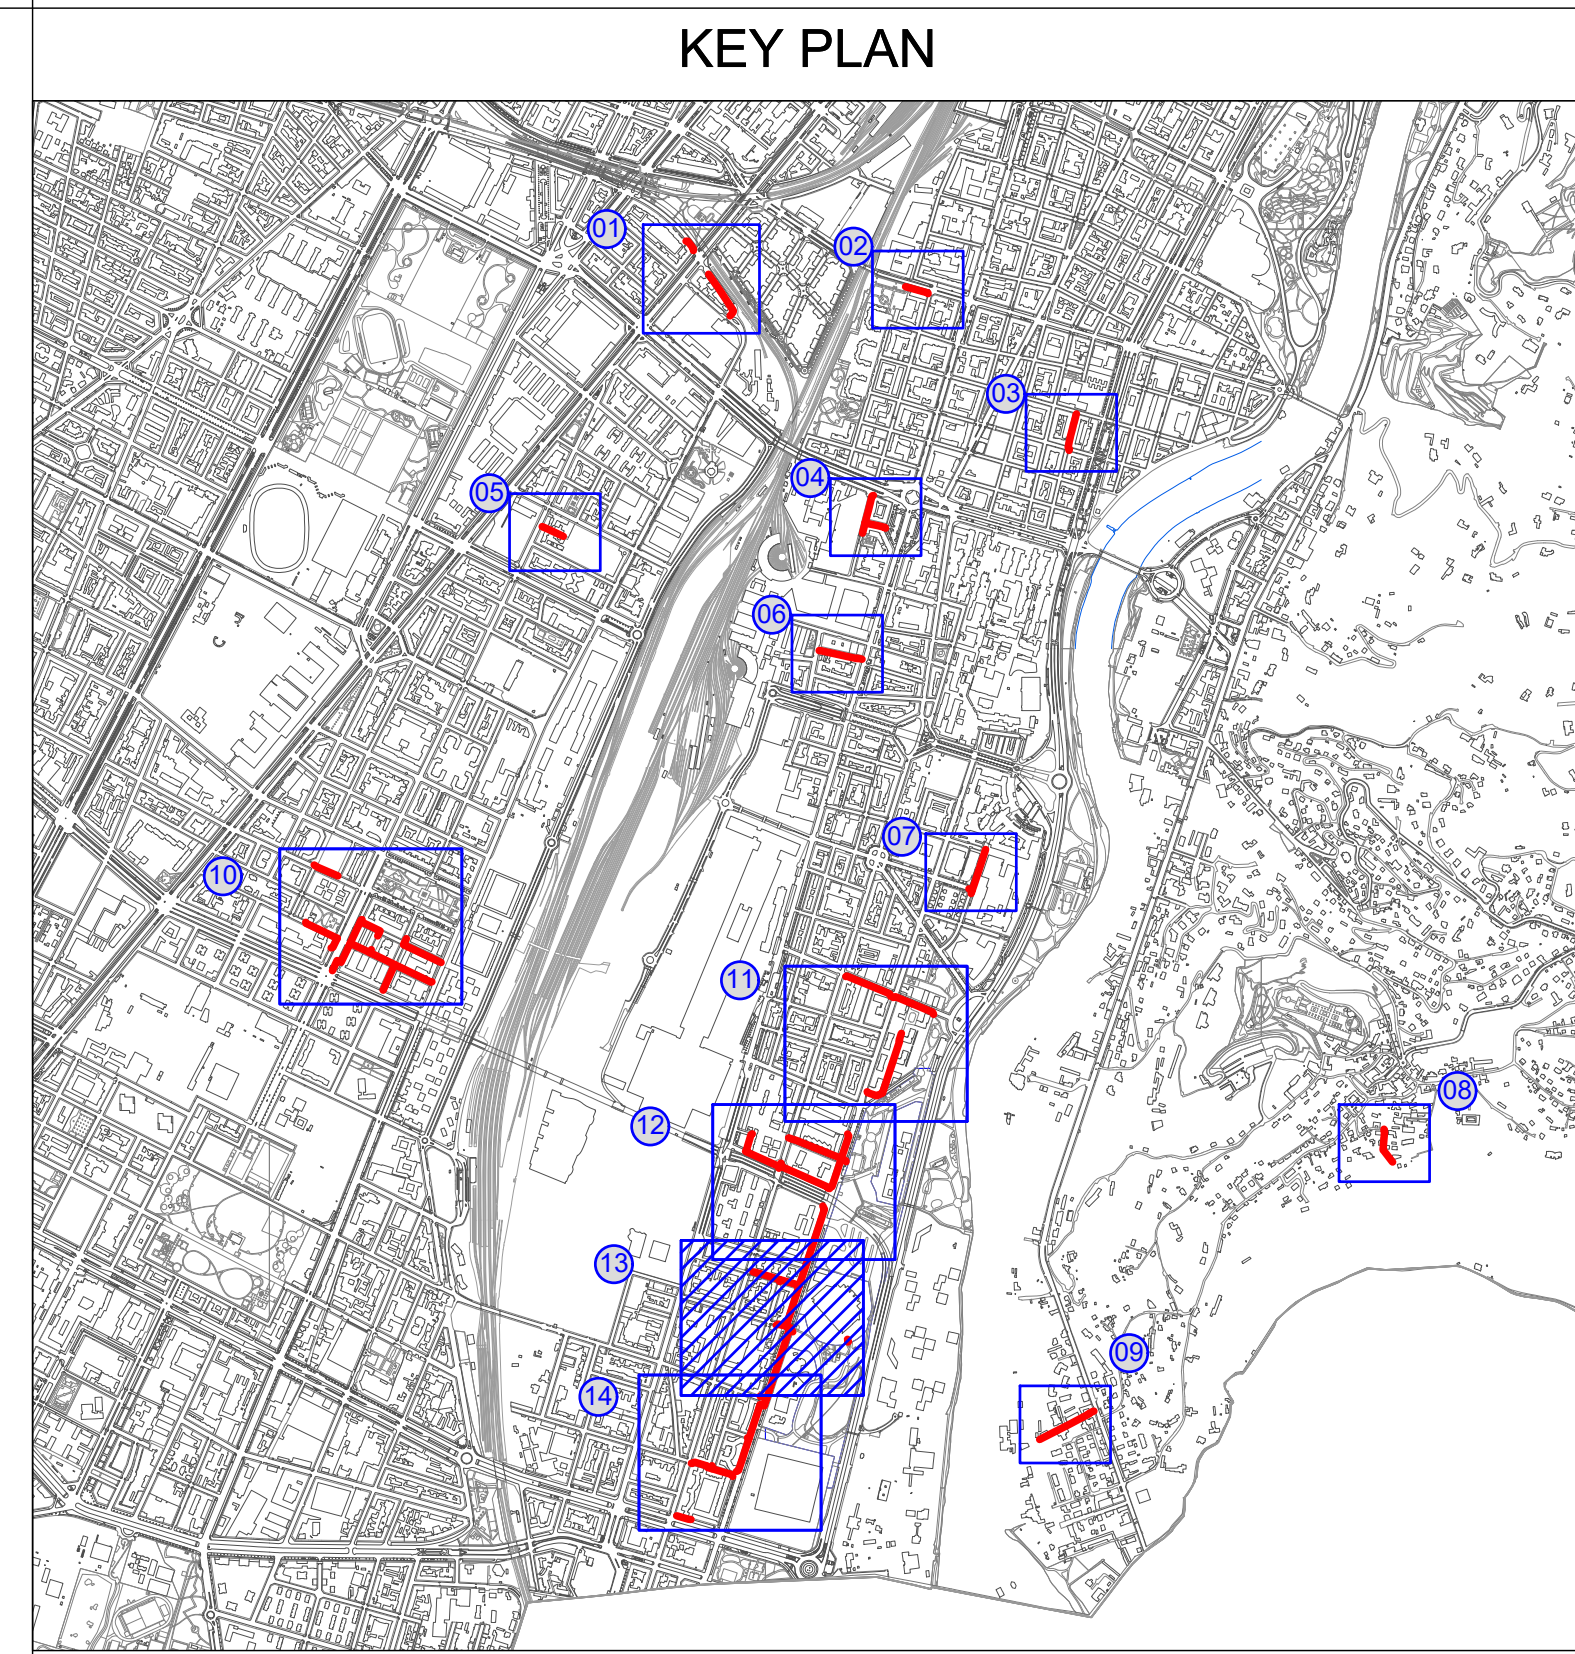

LEGENDA

— Rete in progetto BP
— Rete in dismissione BP
--- Zona di lavoro

001 n° Zona di lavoro
Asfalto
Sterrato/area verde
Autobloccanti/ammattonato

Zone di lavoro e pavimentazioni						
n.	dell'ordato caratteristica	bar	tipo superficie	lato strada	Tipologia strada	Segnaletica
146	Re De 315	BP	Asfalto	Destra	Comunale	linea tratteggiata di corsia
147	Re De 315	BP	Asfalto	Destra	Comunale	linea tratteggiata di corsia
148	Re De 315	BP	Asfalto	Destra	Comunale	linea continua di corsia, rallentatori ottici
149	Re De 315	BP	Asfalto	Destra	Comunale	linea continua di corsia, rallentatori ottici
150	Re De 315	BP	Asfalto	Destra	Comunale	linea continua di corsia, linea di fermata autobus
151	Re De 315	BP	Asfalto	Destra	Comunale	linea tratteggiata di corsia, linea di fermata autobus, linea trasversale di dare precedenza
151	Re De 180	BP	Asfalto	Attraversamento	Comunale	
152	Re De 180	BP	Asfalto	Attraversamento	Comunale	strisce pedonali
152	Re De 180	BP	Asfalto	Destra	Comunale	
153	Re De 180	BP	Asfalto	Destra	Comunale	
154	Re De 125	BP	Asfalto	Attraversamento	Comunale	
154	Re De 180	BP	Asfalto	Destra	Comunale	
155	Re De 125	BP	Asfalto	Attraversamento	Comunale	
156	Re De 180	BP	Asfalto	Destra	Comunale	
157	Re De 180	BP	Asfalto	Destra	Comunale	
158	Re De 180	BP	Asfalto	Attraversamento	Comunale	
158	Re De 180	BP	Asfalto	Destra	Comunale	
159	Re De 315	BP	Asfalto	Destra	Comunale	striscia trasversale di arresto
160	Re De 315	BP	Asfalto	Destra	Comunale	linea tratteggiata di corsia
161	Re De 315	BP	Asfalto	Destra	Comunale	linea tratteggiata di corsia
162	Re De 315	BP	Asfalto	Destra	Comunale	rallentatori ottici/linea continua di corsia
163	Re De 315	BP	Asfalto	Destra	Comunale	strisce pedonali
164	Re De 315	BP	Asfalto	Destra	Comunale	strisce pedonali,doppia striscia trasversale di corsia
164	Re De 180	BP	Asfalto	Attraversamento	Comunale	
164	Re De 315	BP	Asfalto	Attraversamento	Comunale	
165	Re De 180	BP	Asfalto	Destra	Comunale	strisce pedonali
166	Re De 180	BP	Asfalto	Destra	Comunale	
166	Re De 180	BP	Asfalto	Attraversamento	Comunale	
167	Re De 315	BP	Asfalto	Attraversamento	Comunale	striscia continua di corsia, strisce pedonali
167	Re De 180	BP	Asfalto	Attraversamento	Comunale	
167	Re De 315	BP	Asfalto	Sinistra	Comunale	
168	Re De 180	BP	Asfalto	Attraversamento	Comunale	
169	Re De 315	BP	Asfalto	Sinistra	Comunale	strisce pedonali, striscia continua di corsia
170	Re De 315	BP	Asfalto	Sinistra	Comunale	striscia tratteggiata di corsia, rallentatori ottici
171	Re De 315	BP	Asfalto	Sinistra	Comunale	striscia tratteggiata di corsia
172	Re De 315	BP	Asfalto	Sinistra	Comunale	striscia tratteggiata di corsia
173	Re De 315	BP	Asfalto	Sinistra	Comunale	striscia tratteggiata di corsia
174	Re De 315	BP	Asfalto	Sinistra	Comunale	striscia tratteggiata di corsia
175	Re De 315	BP	Asfalto	Sinistra	Comunale	striscia tratteggiata di corsia
176	Re De 315	BP	Asfalto	Sinistra	Comunale	striscia tratteggiata di corsia
177	Re De 315	BP	Asfalto	Sinistra	Comunale	strisce pedonali rossa, striscia continua di corsia
177	Re De 180	BP	Asfalto	Attraversamento	Comunale	
178	Re De 180	BP	Asfalto	Attraversamento	Comunale	striscia pedonale rossa, doppia striscia tratteggiata, striscia tratteggiata corsia
200	Re De 125	BP	Sterrato	Centro	Comunale	

Progetto n°: 21-0584-3E-00-001272
VBS: SI.20.10300.02.1109
ALLEGATO n°: 6.7

Formato: A0 Scale: 1:500


Comittente: **IG Italgas** Reti

Progettista: **LEARDI**

Ordine degli Ingegneri di Alessandria

Unità Responsabile della Progettazione: INGERAL-INGE-PROGRE

Comune di TORINO (TO)
Via Vane
Progetto Esecutivo
SOSTITUZIONE RETE BP (L=2745,39 M) - GARA TO 1
Intervento n° SI-036213-001272-TSS-TORINO09
Planimetria pavimentazioni e zone di lavoro - Tavola 7

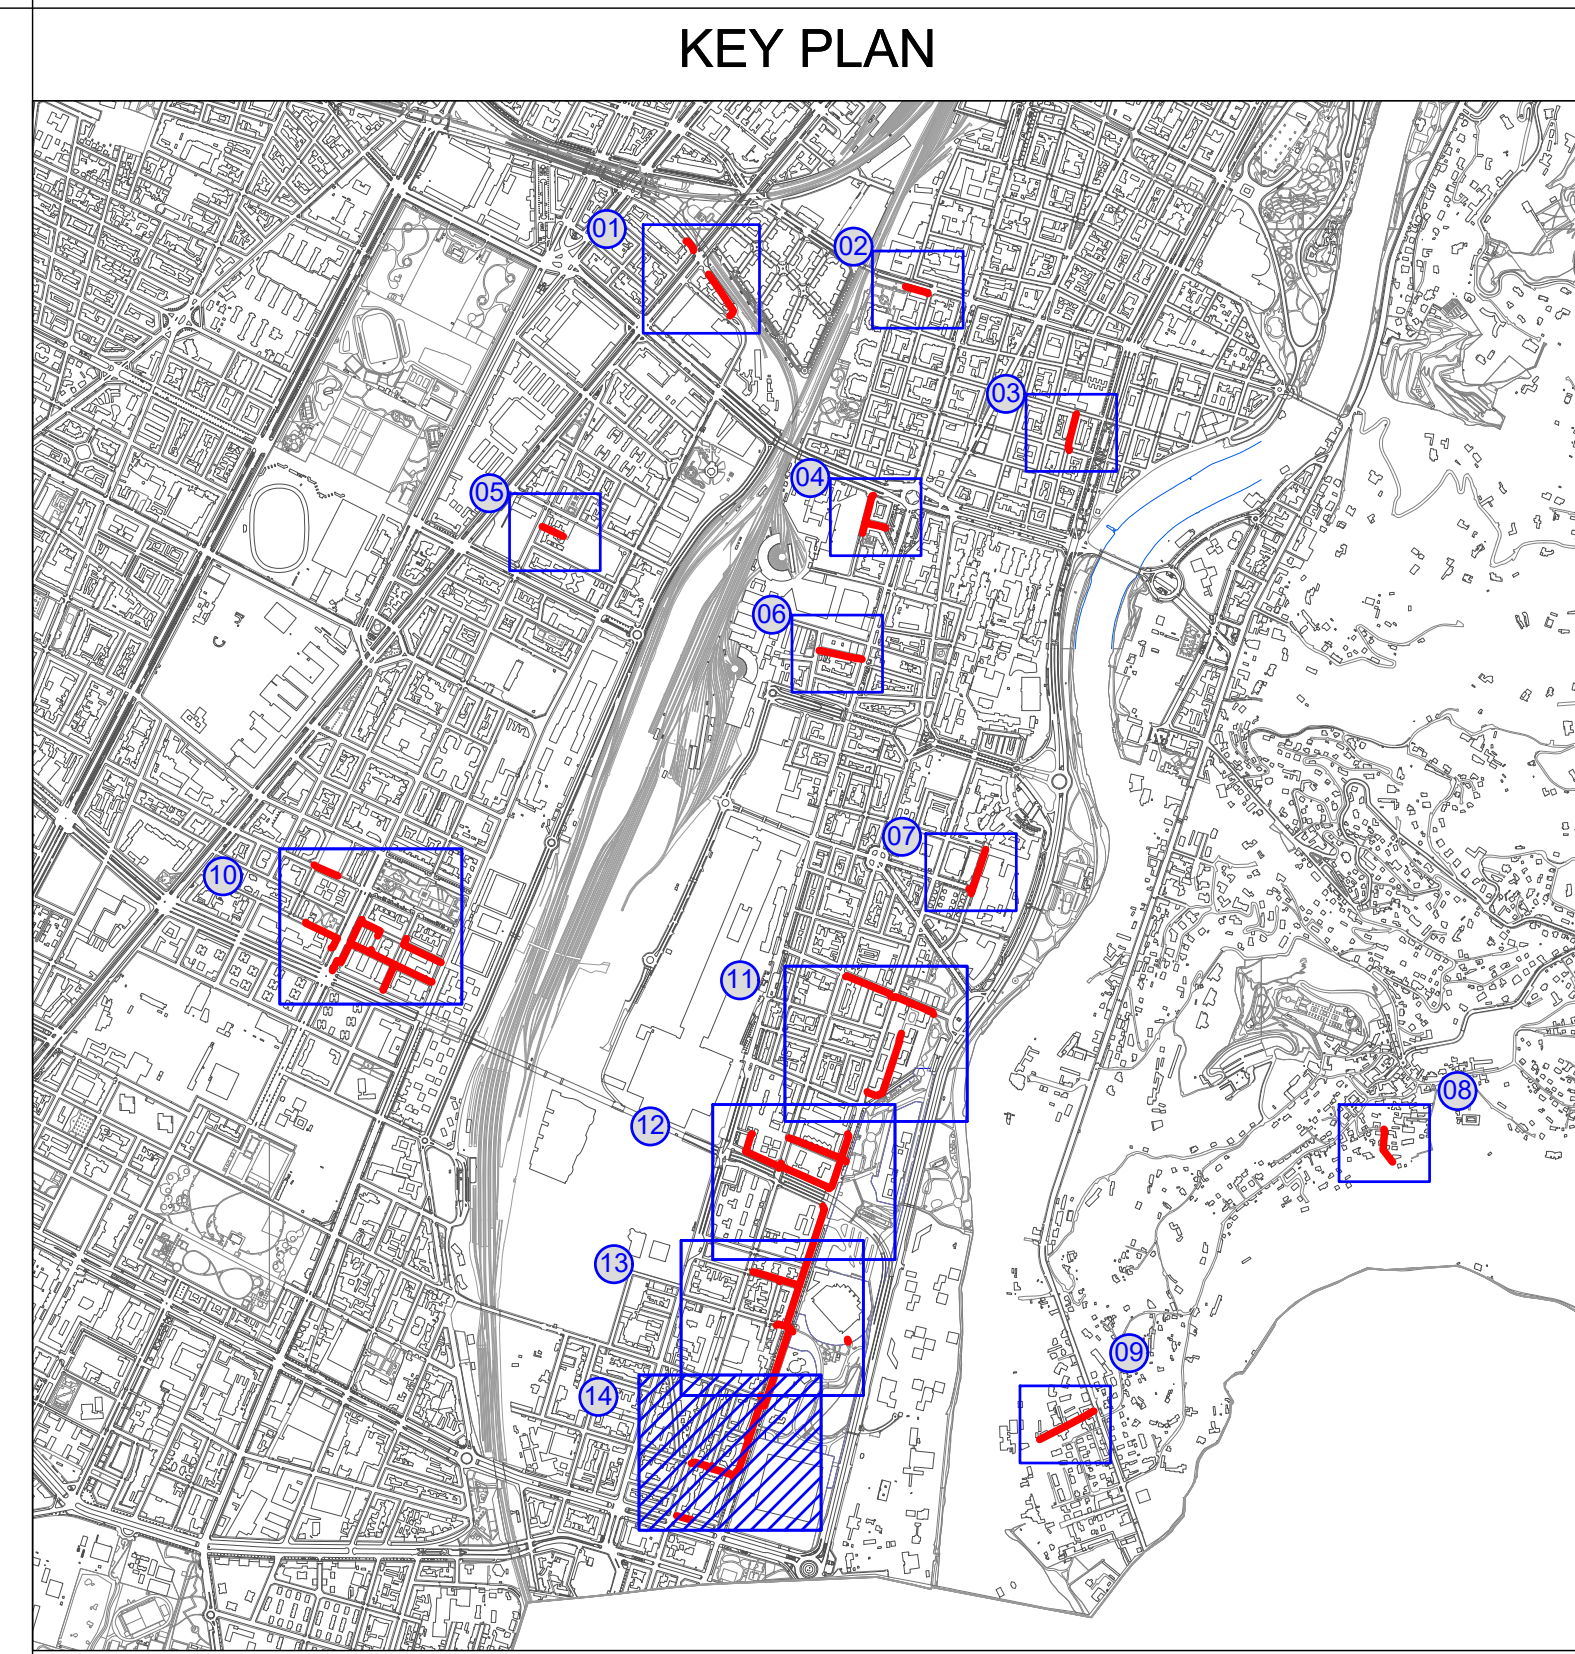

Rete in progetto BP

Rete in dismissione BP

Zona di lavoro

001

n° Zona di lavoro

Asfalto

Sternatore/area verde

Autobloccanti/ammattonato

Zone di lavoro e pavimentazioni

n.	del condotta	caratteristiche	tar	tipo superficie	lato strada	Tipologia strada	Segnaletica
174	Pt De 315	BP		Asfalto	Sinistra	Comunale	striscia tratteggiata di corsia
175	Pt De 315	BP		Asfalto	Sinistra	Comunale	striscia tratteggiata di corsia
176	Pt De 315	BP		Asfalto	Sinistra	Comunale	striscia tratteggiata di corsia
177	Pt De 315	BP		Asfalto	Sinistra	Comunale	strisce pedonali rossa, striscia continua di corsia
178	Pt De 180	BP		Asfalto	Attraversamento	Comunale	striscia pedonale rossa, doppia striscia tratteggiata, striscia tratteggiata di corsia
179	Pt De 315	BP		Asfalto	Sinistra	Comunale	doppia striscia continua di mezzarota, rallentatori ottici, striscia tratteggiata di corsia
180	Pt De 315	BP		Asfalto	Attraversamento	Comunale	striscia tratteggiata di corsia
181	Pt De 315	BP		Asfalto	Sinistra	Comunale	
182	Pt De 315	BP		Asfalto	Destra	Comunale	striscia gialla parcheggio disabili, rallentatori ottici
183	Pt De 315	BP		Asfalto	Destra	Comunale	strisce pedonali, linea tratteggiata di corsia
184	Pt De 315	BP		Asfalto	Destra	Comunale	strisce pedonali, linea tratteggiata di corsia
185	Pt De 125	BP		Asfalto	Attraversamento	Comunale	
186	Pt De 125	BP		Asfalto	Attraversamento	Comunale	
187	Pt De 315	BP		Asfalto	Destra	Comunale	linea tratteggiata di corsia, strisce pedonali
188	Pt De 315	BP		Asfalto	Destra	Comunale	linea tratteggiata di corsia
189	Pt De 315	BP		Asfalto	Destra	Comunale	linea tratteggiata di corsia
190	Pt De 180	BP		Asfalto	Attraversamento	Comunale	
191	Pt De 180	BP		Asfalto	Sinistra	Comunale	
192	Pt De 180	BP		Asfalto	Sinistra	Comunale	
193	Pt De 180	BP		Asfalto	Sinistra	Comunale	
194	Pt De 180	BP		Asfalto	Attraversamento	Comunale	strisce pedonali
195	Pt De 180	BP		Asfalto	Attraversamento	Comunale	strisce pedonali
196	Pt De 180	BP		Asfalto	Destra	Comunale	strisce di parcheggio carico e scarico
197	Pt De 180	BP		Asfalto	Destra	Comunale	strisce pedonali, strisce trasversali di dare precedenza
198	Pt De 315	BP		Asfalto	Sinistra	Comunale	
199	Pt De 315	BP		Asfalto	Destra	Comunale	

Progetto n°:
21-0584-3E-00-001272
VBS:
SI 20.10300.02.1109
ALLEGATO n°: 6.8
Formato: A0
Scale: 1:500

Progetto:
Ordine dei geometri di Alessandria
mancato

Comune di:
TORINO (TO)
Via Vane
Progetto Esecutivo
SOSTITUZIONE RETE BP (L=2745,39 M) - GARA TO 1
Intervento n° SI-036213-001272-TSS-TORINO08
Planimetria pavimentazioni e zone di lavoro - Tavola 8

Unità Responsabile della Progettazione
INGENERAL-INGE-PROGRE

Disegnato	0	30	11	22	A. Saroni	L. Contegna	A. Leardi
Elaborato per commenti							
Comm: 2484	Rev:	G.	M.	A.	Redatto	Controllato	Approvato

Il presente elaborato è di proprietà aziendale - La società tutela i propri diritti a termini di legge.