




Sezione tipo
percorrenza/attraversamento marciapiede
strada comunale asfaltata
Condotta gas in progetto/rimozione Pe De 125

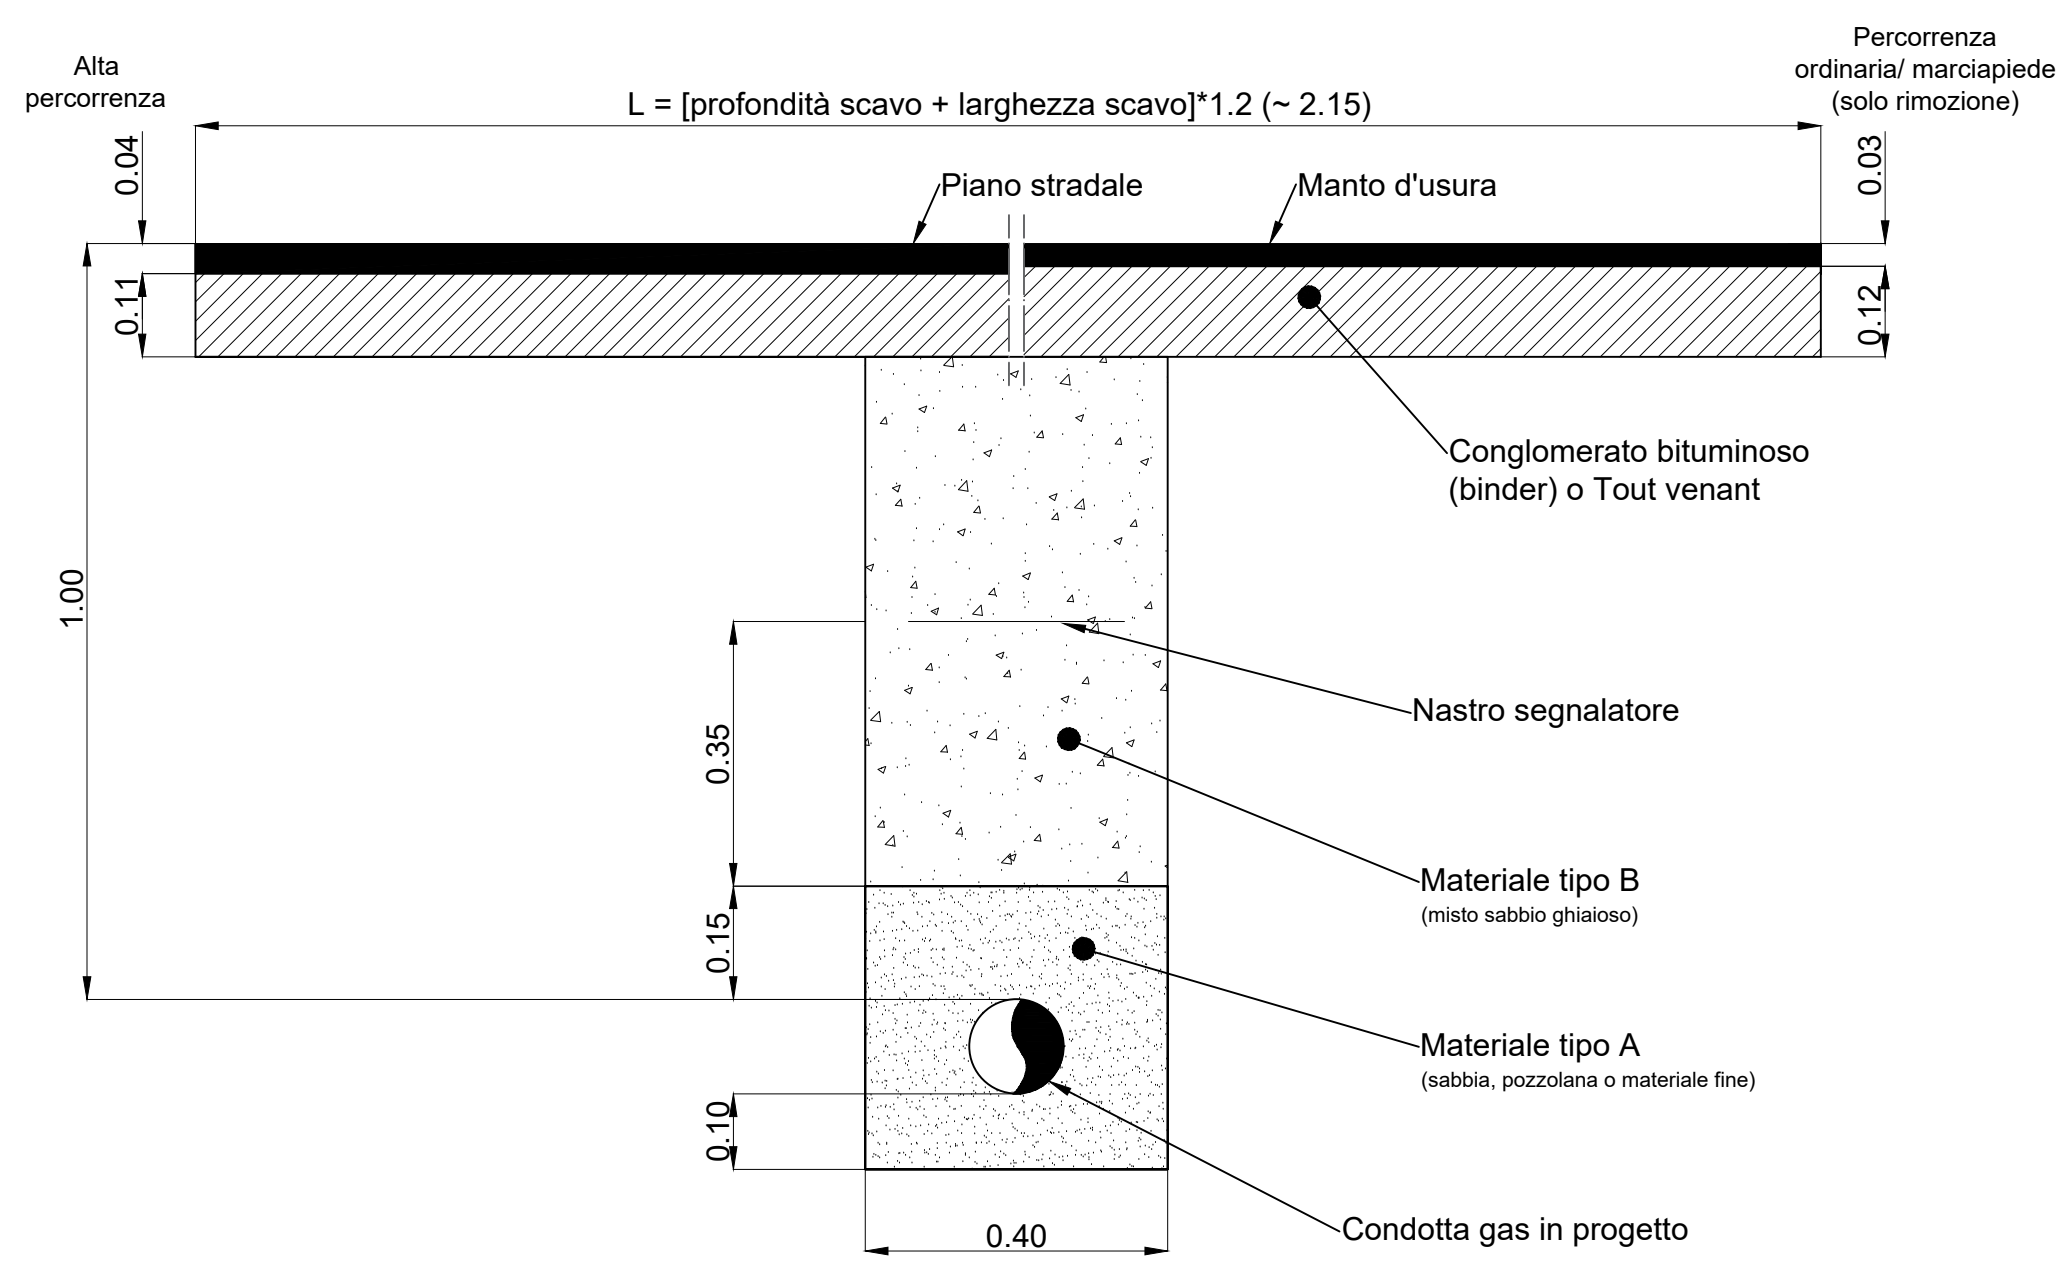


Sezione tipo
percorrenza/attraversamento marciapiede
strada comunale asfaltata
Condotta gas in progetto Pe De 225 - De 180
Condotta gas in rimozione GH DN 150
GH DN 200 - Acc DN 150 - De 180

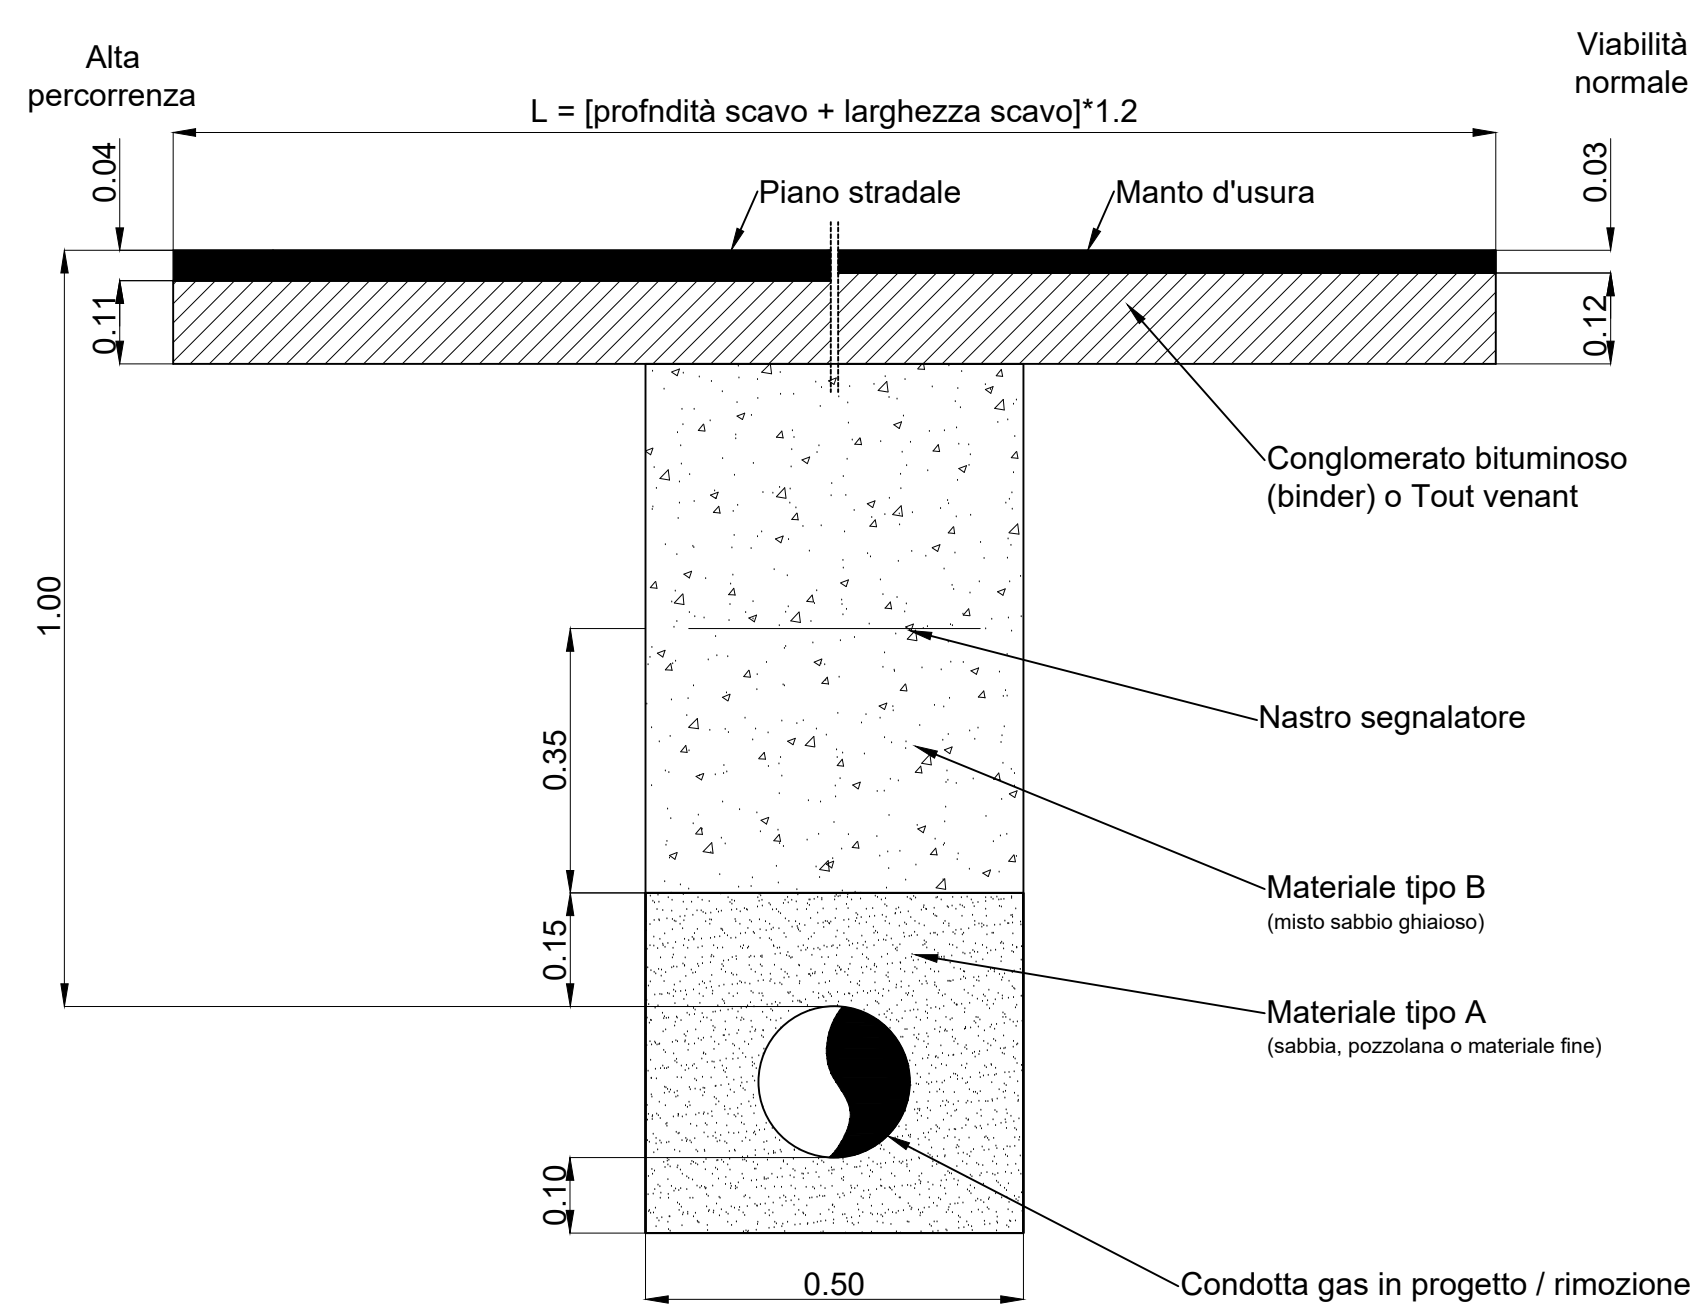


Sezione tipo
percorrenza/attraversamento marciapiede
strada comunale asfaltata
Condotta gas in progetto Pe De 315
Condotta gas in rimozione Acc/GH DN 300/250

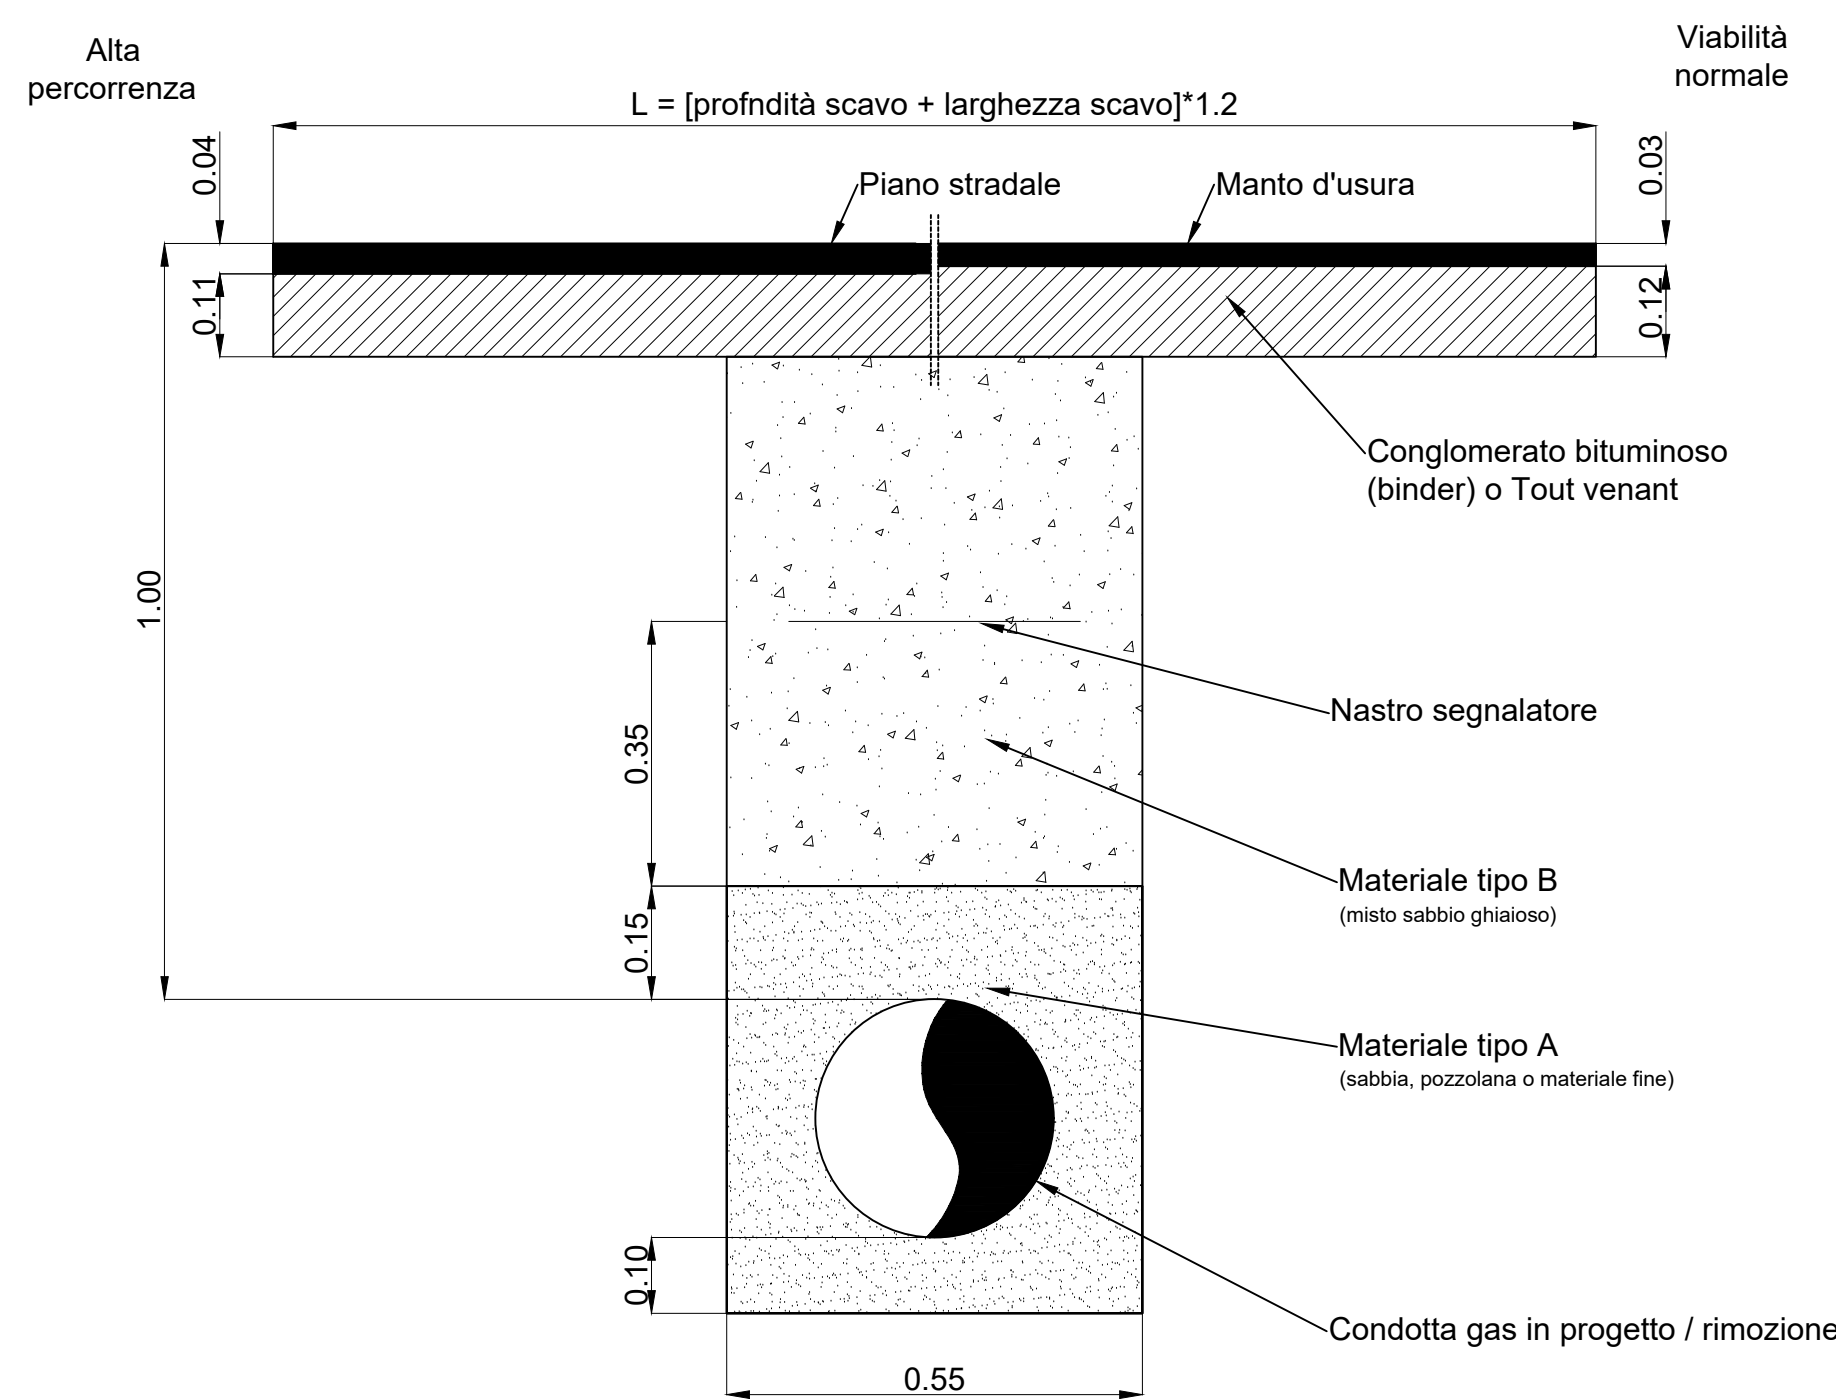


Sezione tipo
Area verde
Condotta gas in progetto Pe De 180

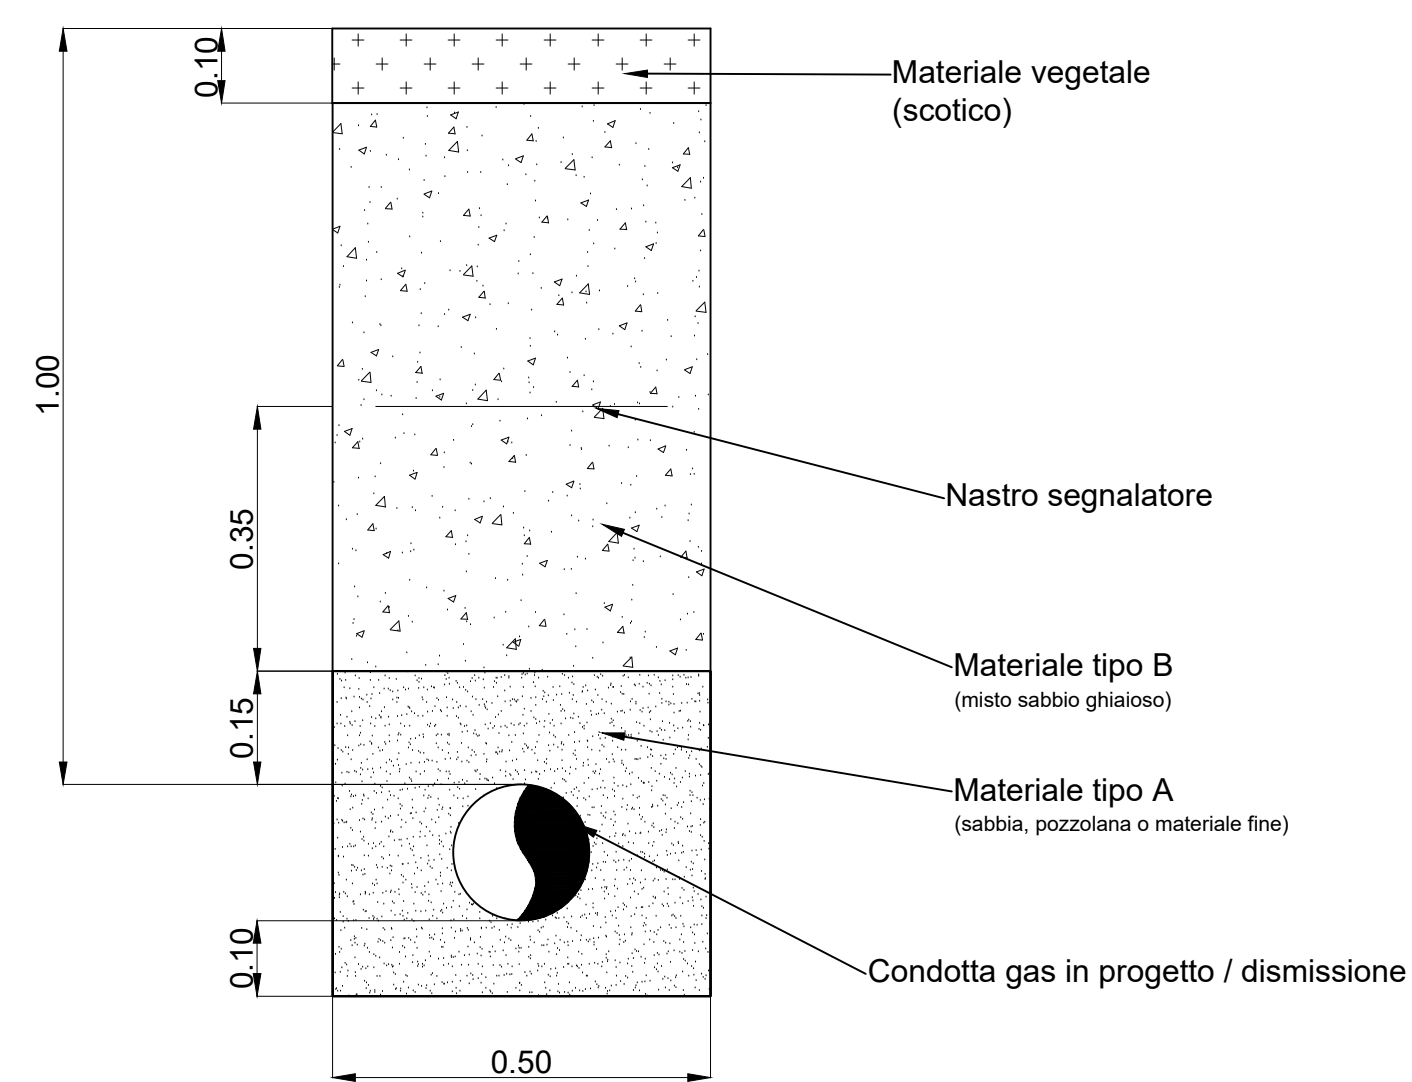


Sezione tipo
pavimentazione autobloccanti
Condotta gas in progetto Pe De 180
Dismissione GH DN 150

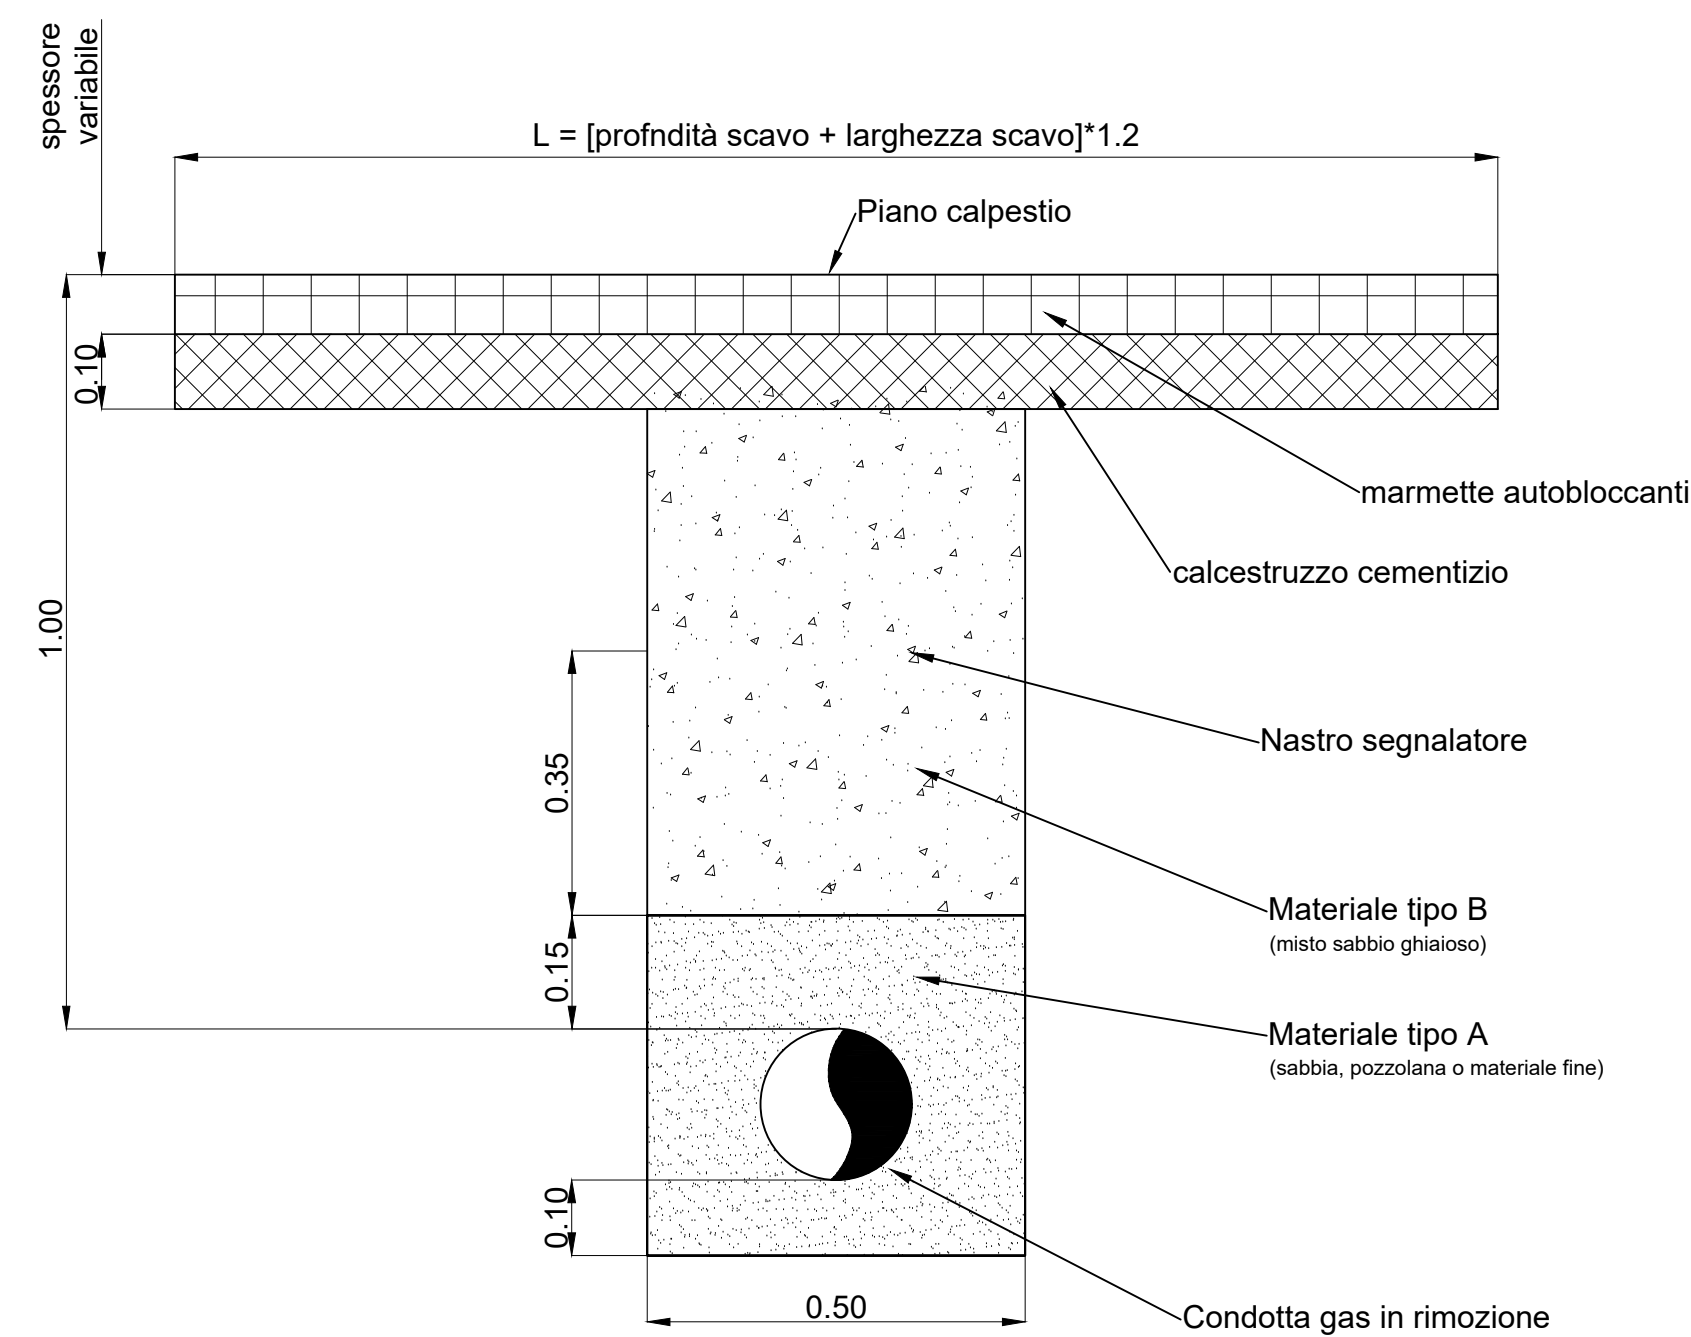


Sezione tipo
pavimentazione autobloccanti
Condotta gas in progetto Pe De 315
Condotta gas in rimozione ACC/GH DN 250

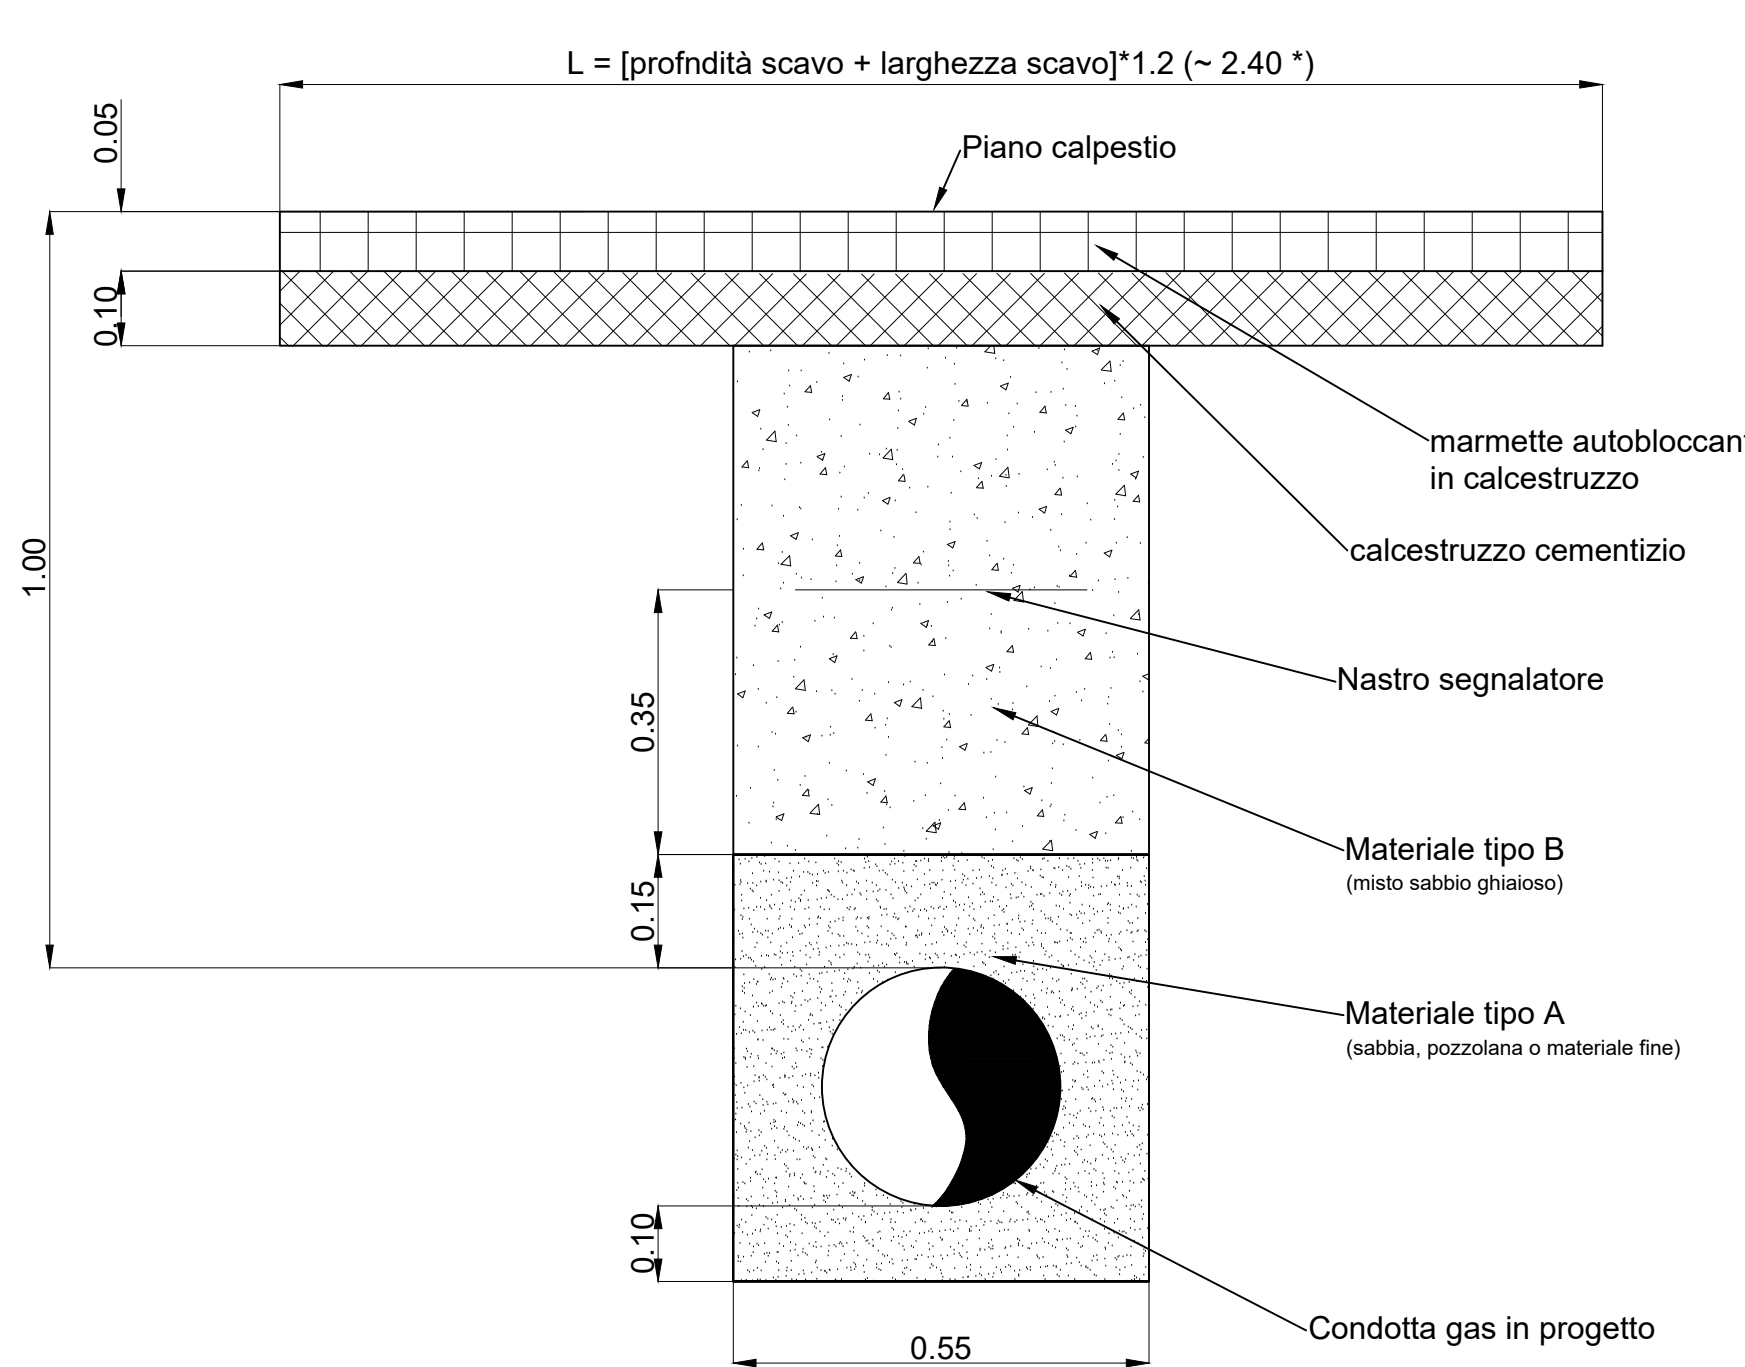


Sezione tipo
percorrenza/attraversamento strada privata asfaltata
Condotta gas in progetto Pe De 125
Condotta gas in dismissione GH DN 80

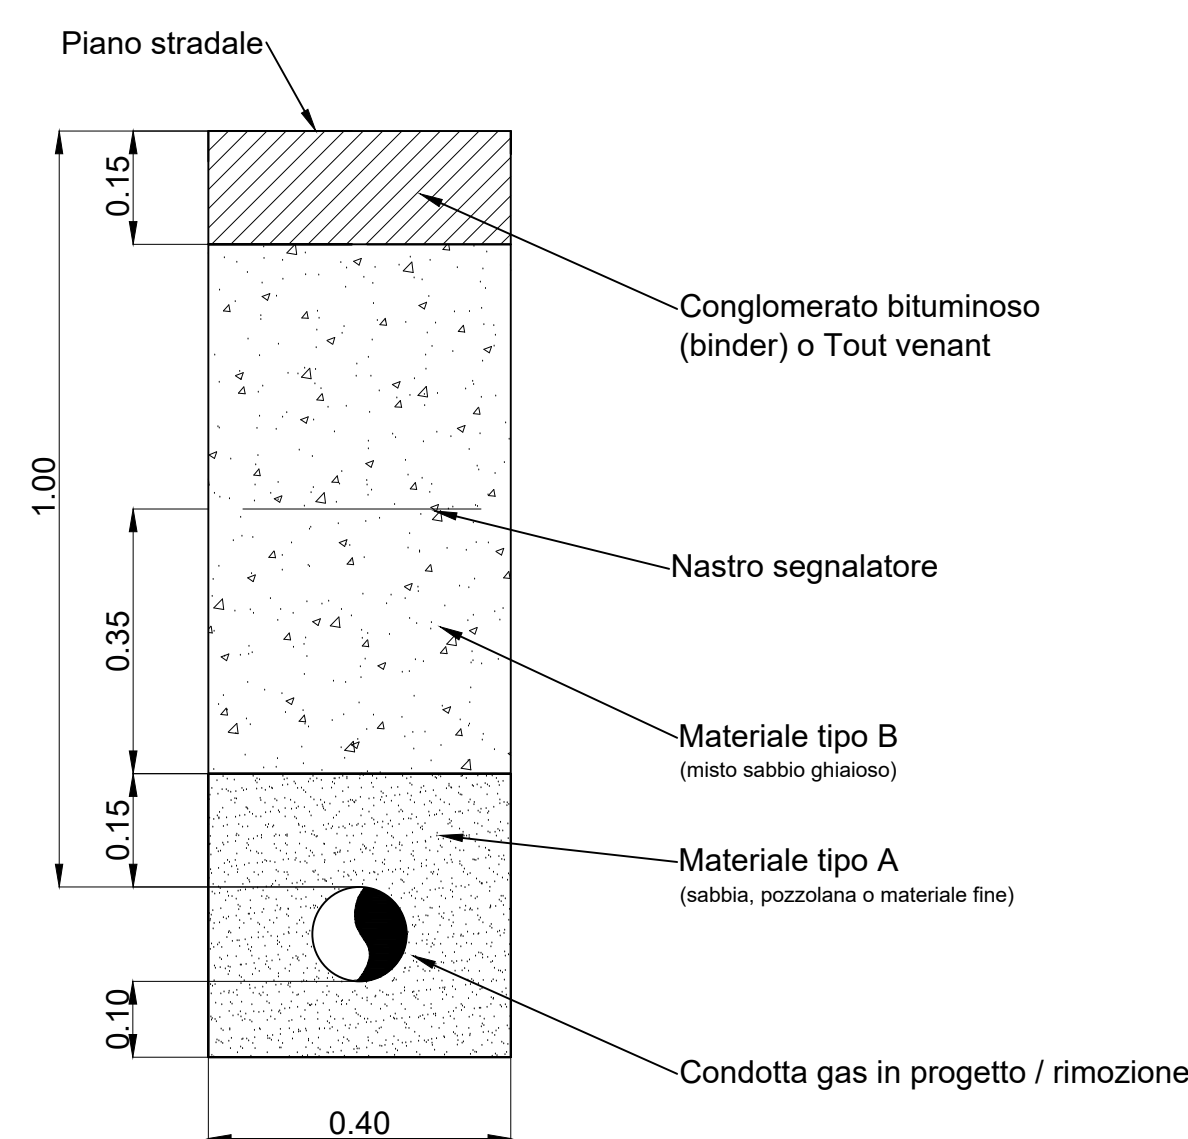


Sezione tipo
percorrenza/attraversamento
strada privata asfaltata
Condotta gas in progetto Pe De 180
Condotta gas in dismissione GH DN 150

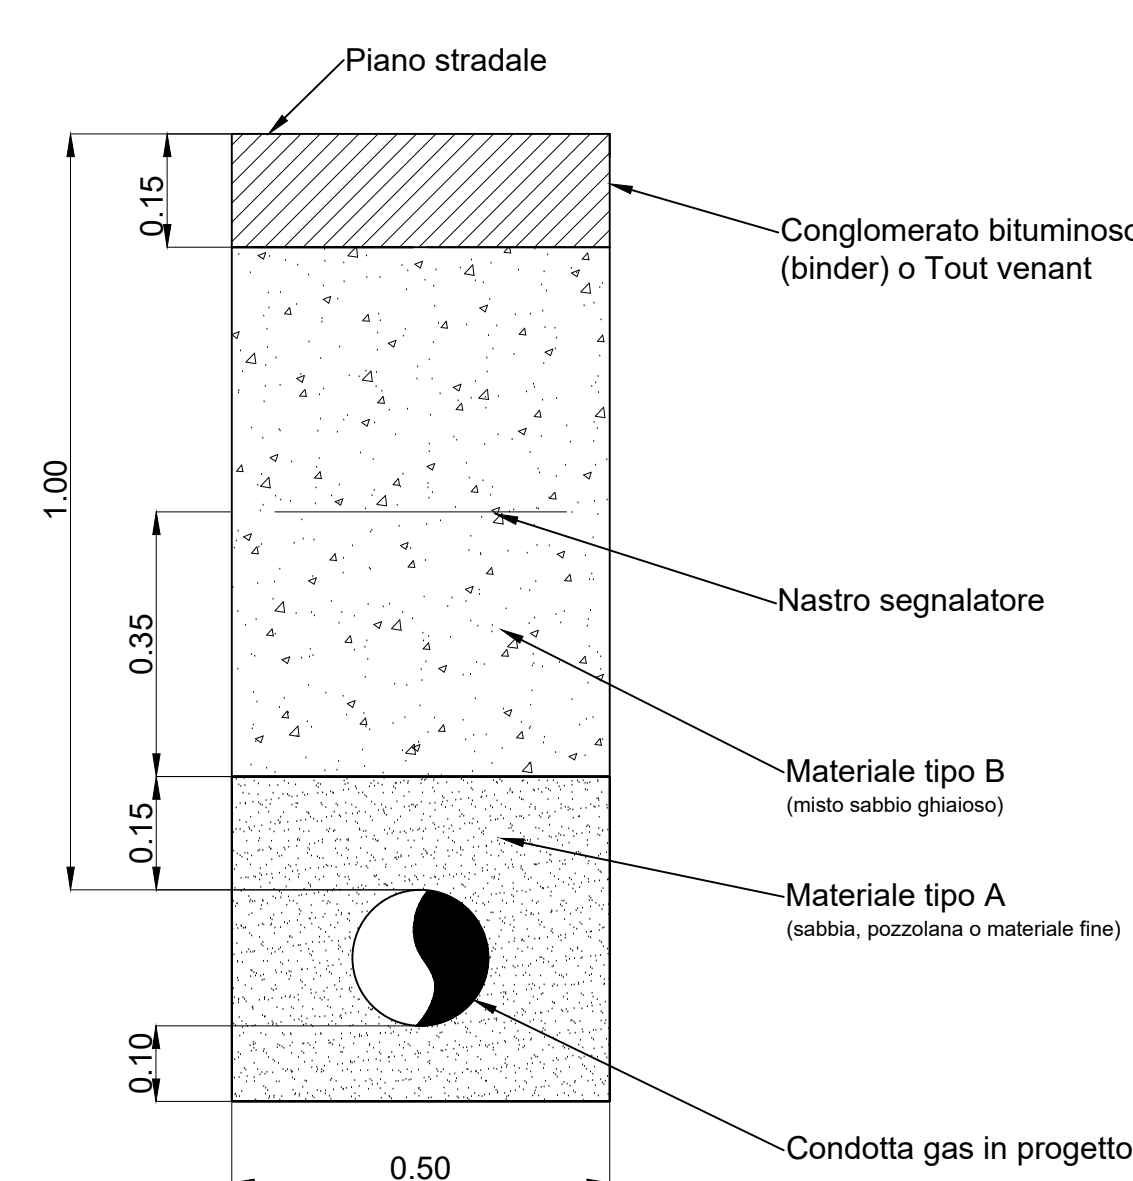


Sezione tipo
percorrenza/attraversamento marciapiede
strada comunale asfaltata
Condotta gas in rimozione ACC DN 400/350

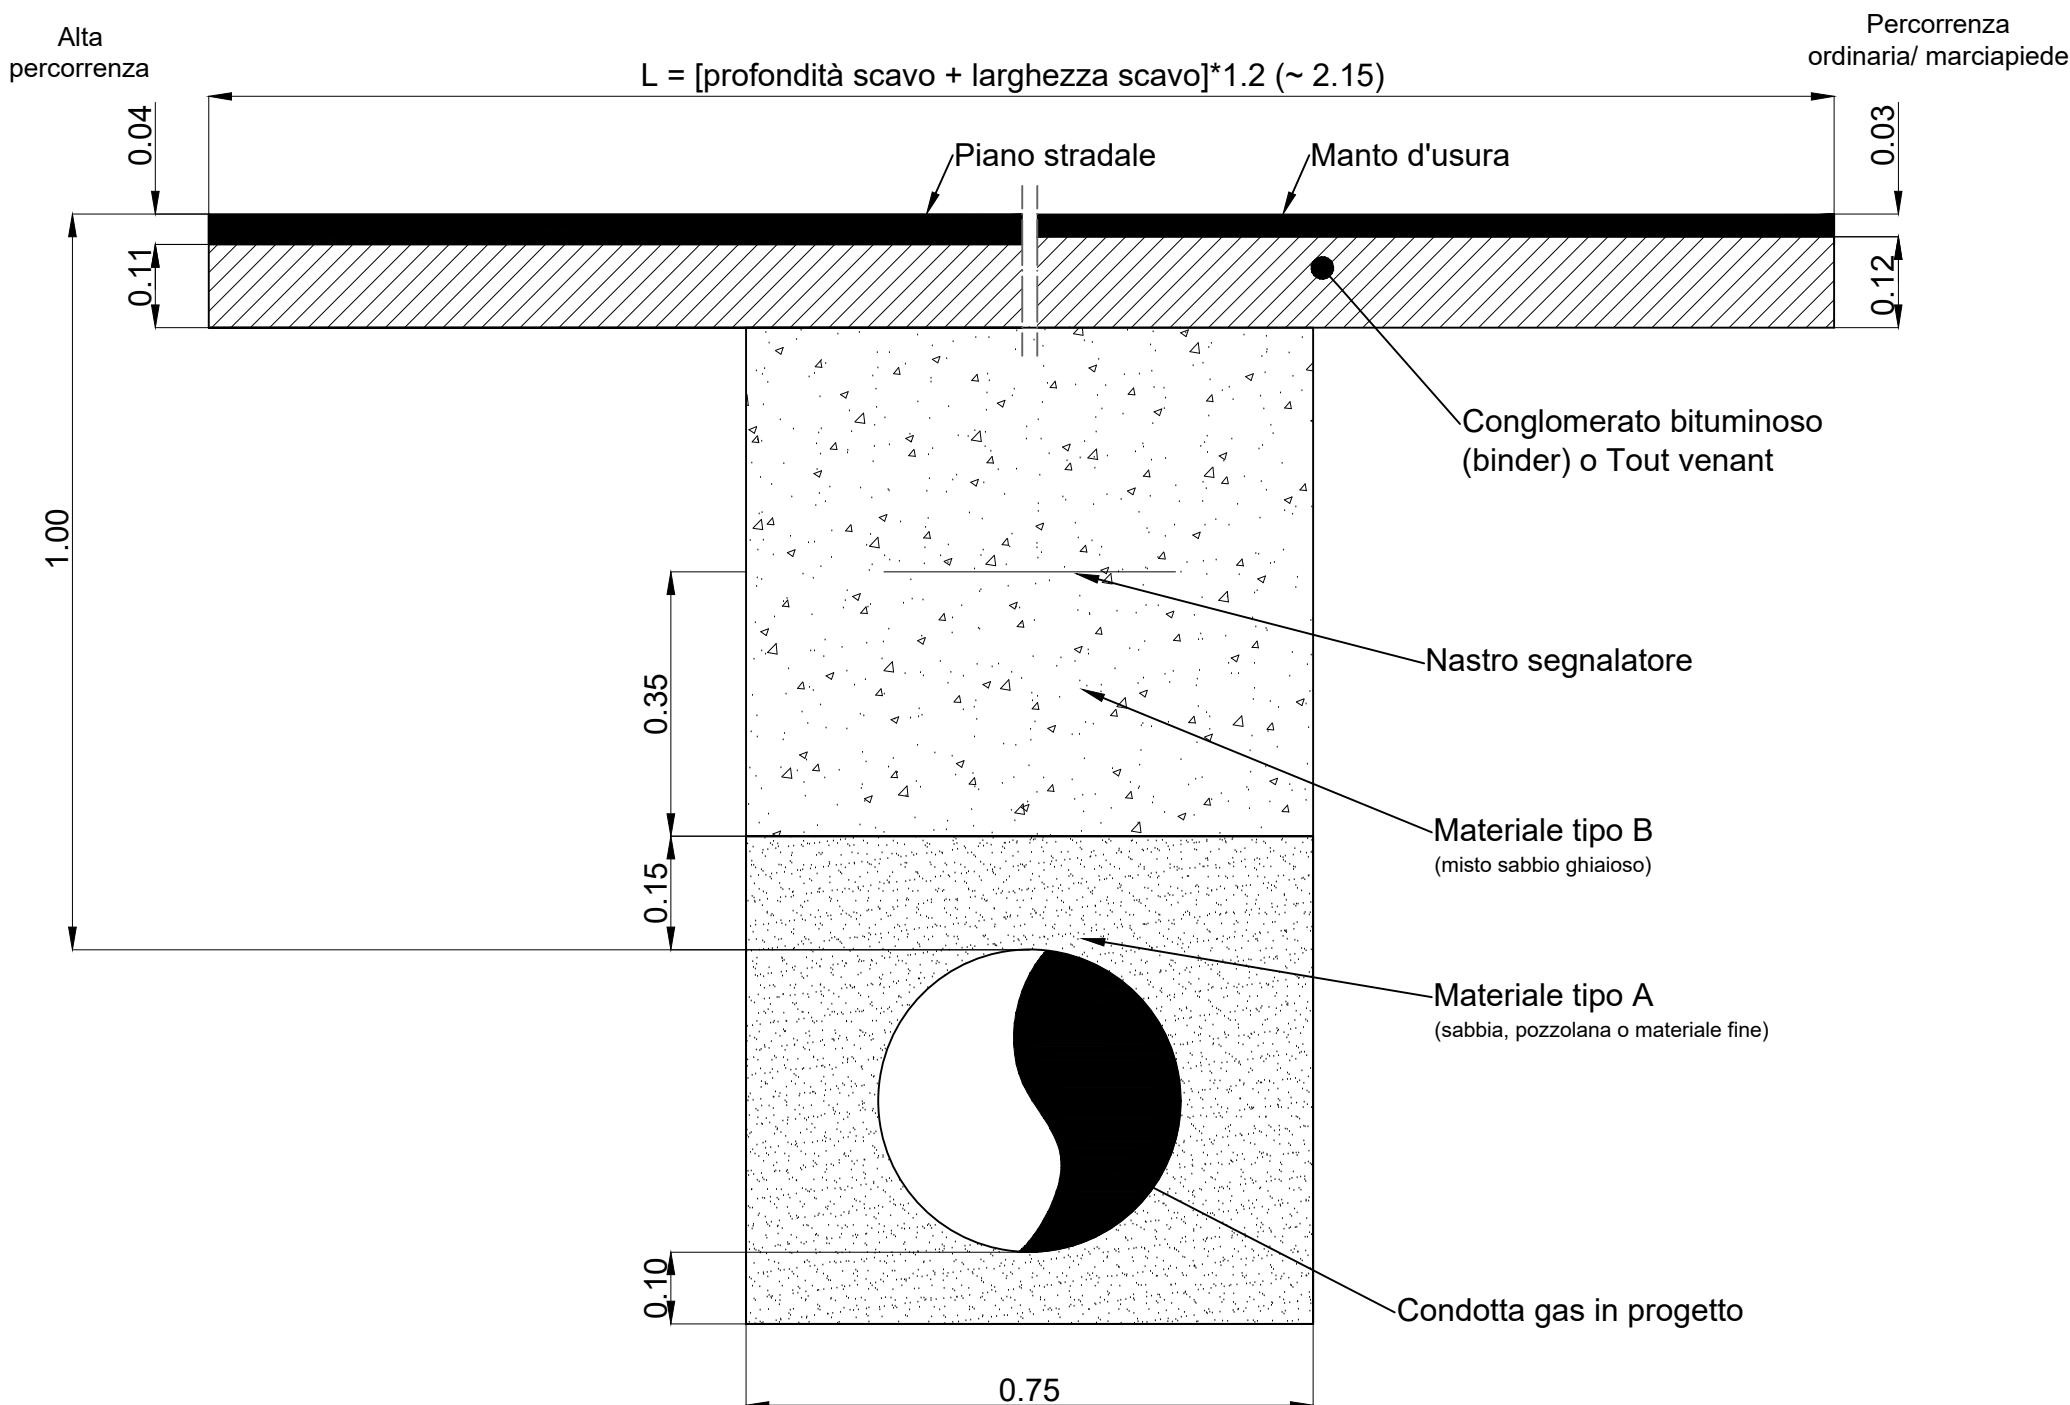

Sezione tipo
Area verde
Condotta gas in progetto Pe De 125
Condotta gas in rimozione GH DN 100

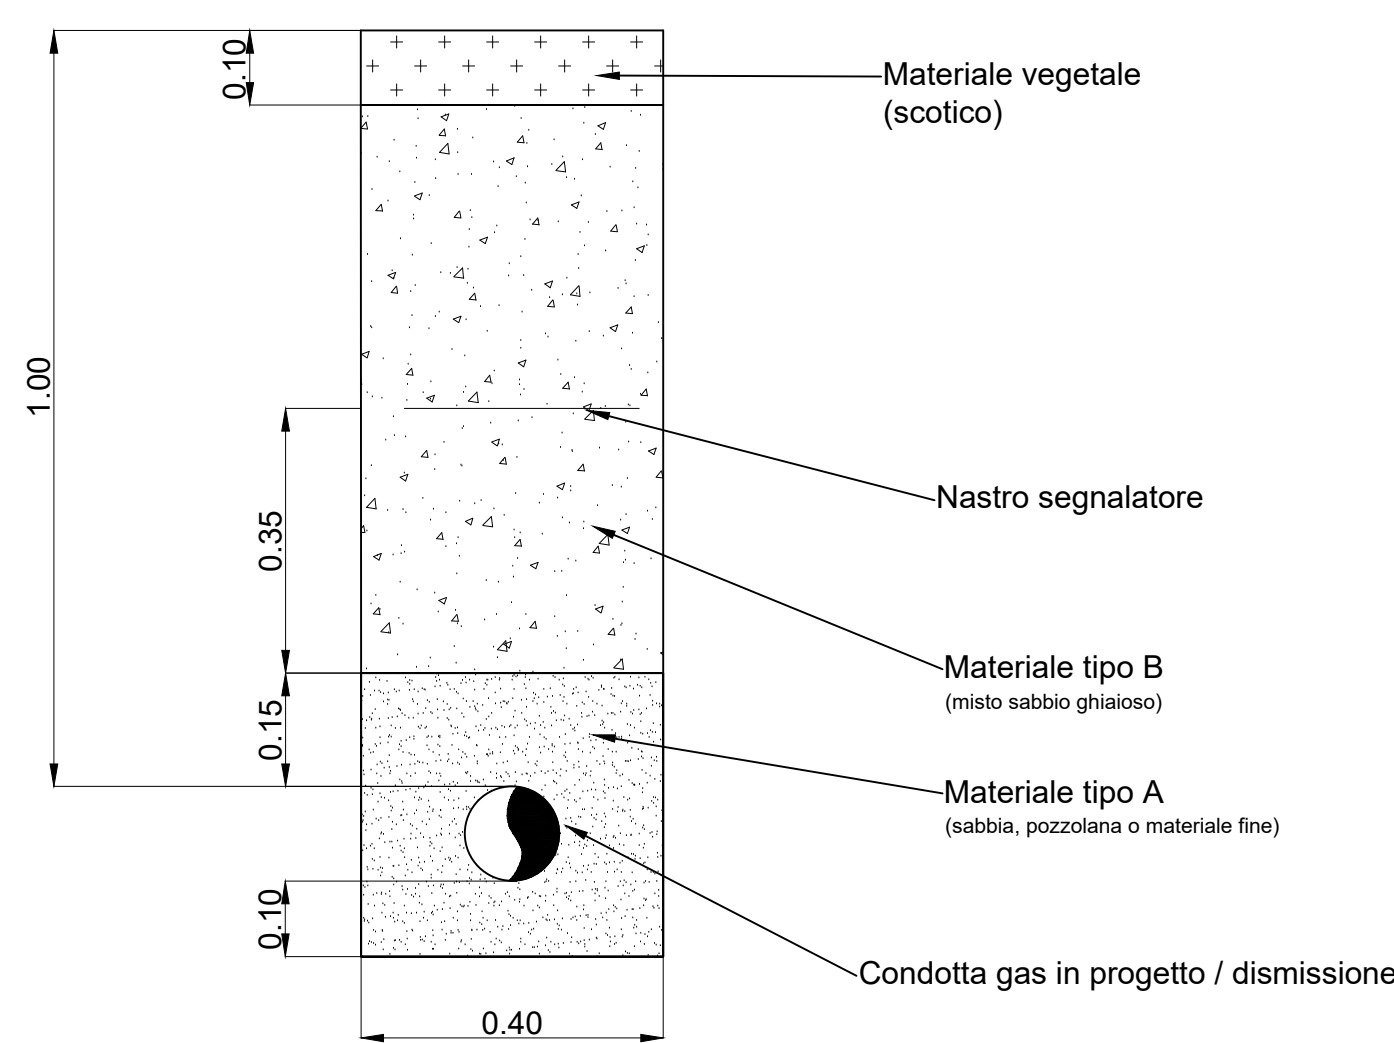

Sezione tipo
Area verde
Condotta gas in rimozione GH DN 250

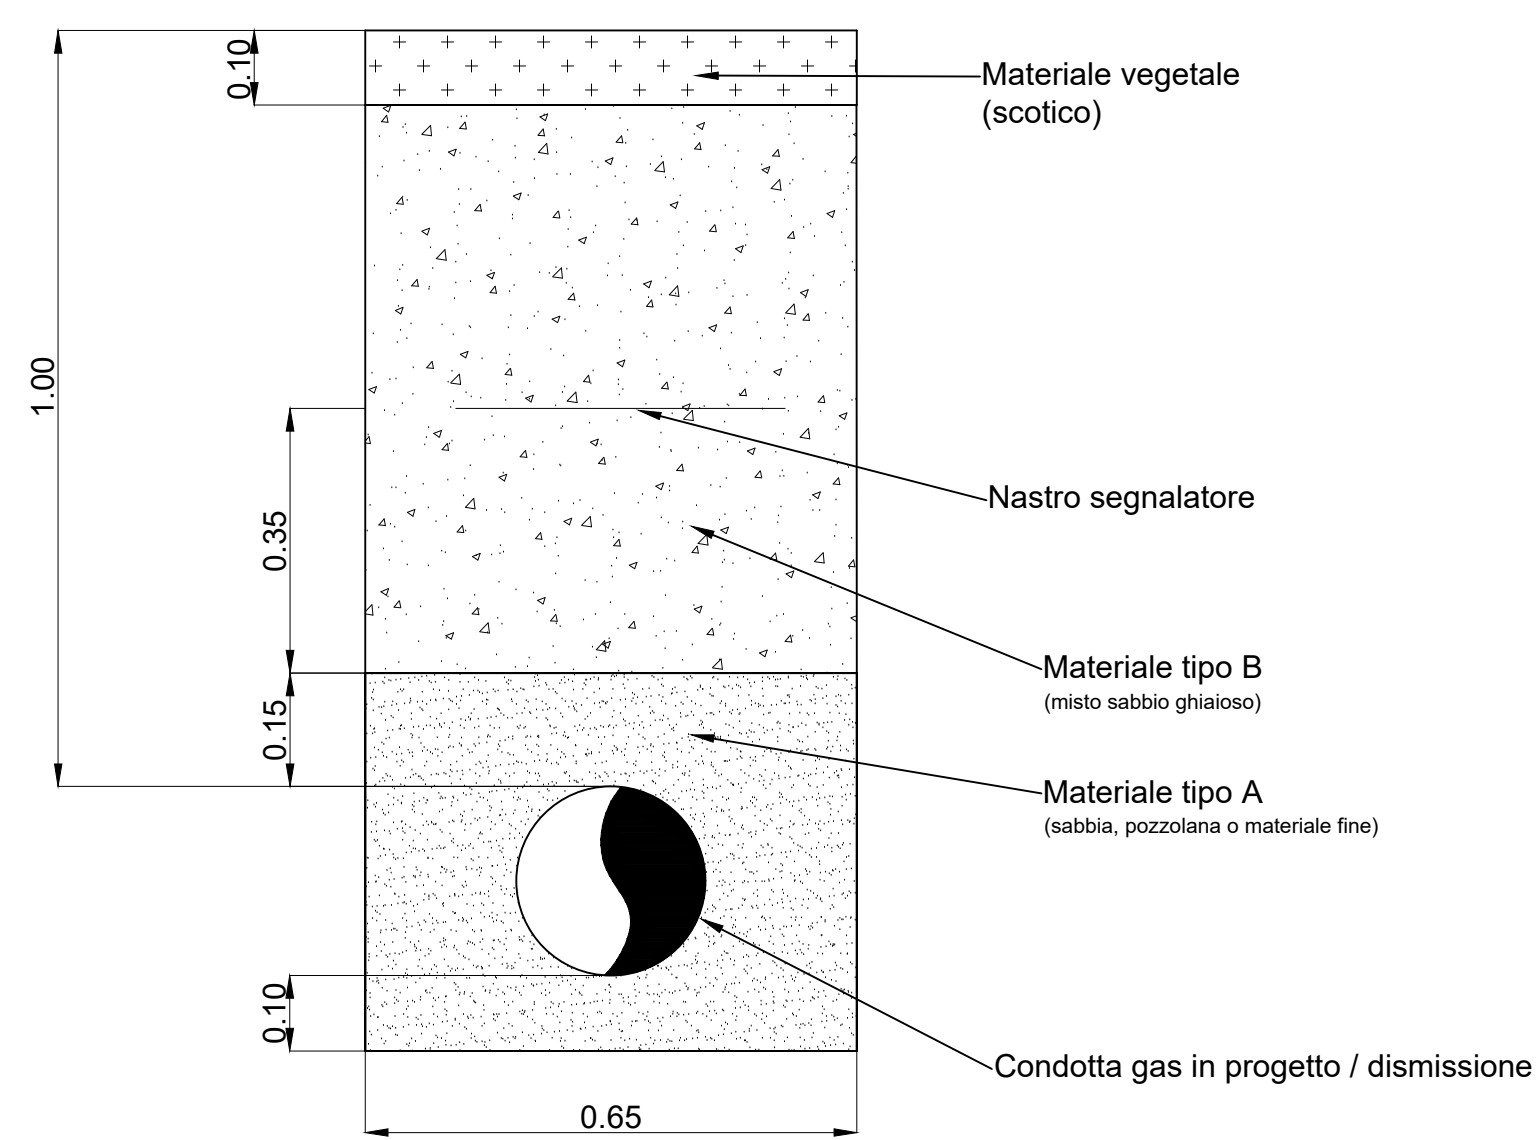

		Progetto n° 21-0584-3E-00-00/1272 WBS: SI20.I0300.02.1109 ALLEGATO n° 7		Unità Responsabile della Progettazione INGREAL-INGE-PROGRE	
Formato: A0		Scale: 1:100		Comune di TORINO (TO) Viale Vares Progetto Esecutivo SOSTITUZIONE RETE BP (L=2745,39 M) - GARA TO 1 Intervento n° SI-036213-001272-TSS-TORINO08 Sezioni Tipologiche	