




Tipologico 16
Riduzione ACC DN 350 - ACC DN 300
Nodi 79

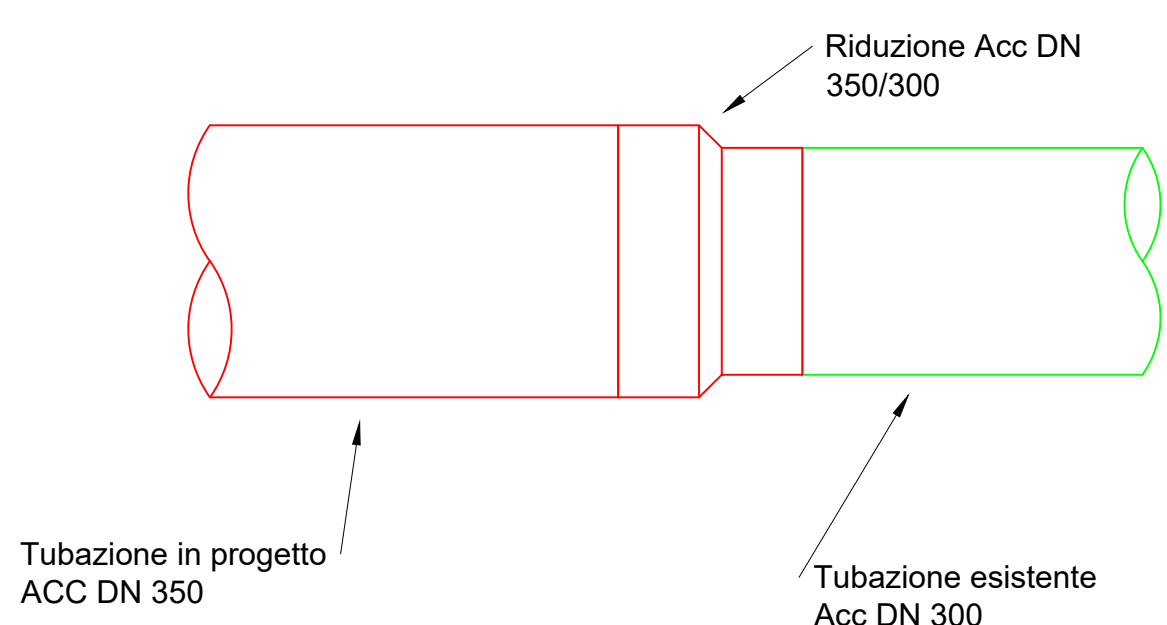


Tipologico 17
Riduzione Pe De 125 - Pe De 90
Nodi 20

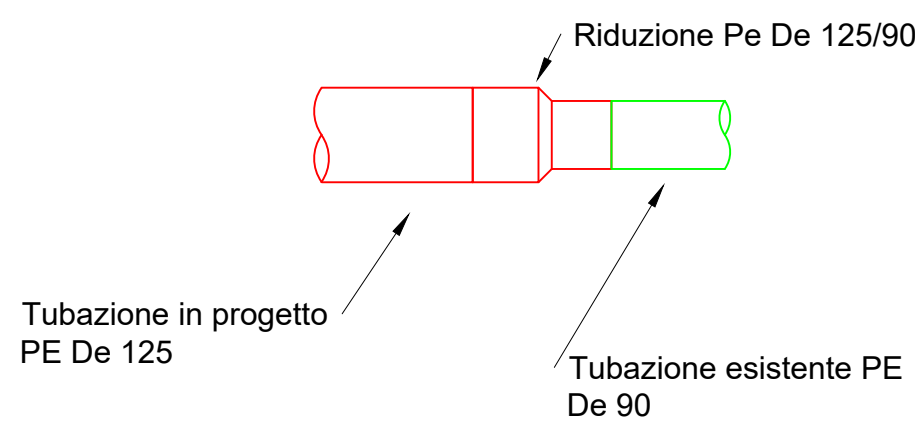


Tipologico 18
Riduzione Pe De 180 - Pe De 125
Nodi 4-65

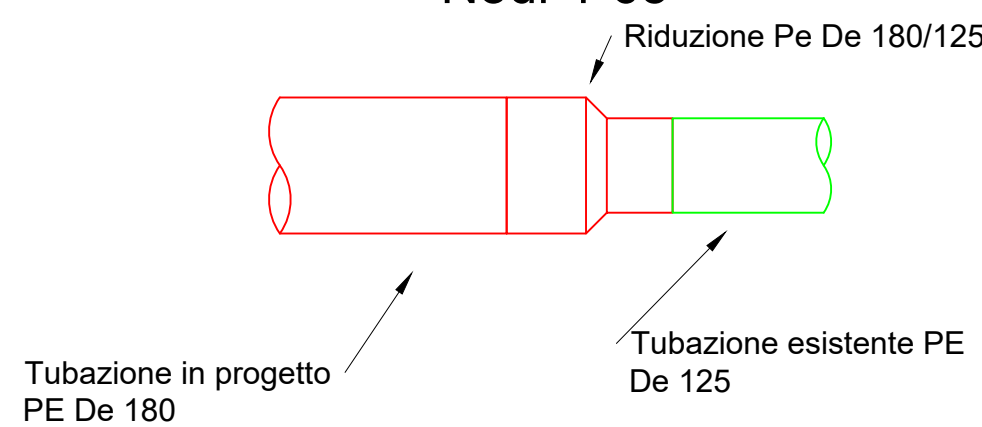


Tipologico 19
Riduzione Pe De 315 - Pe De 225
Nodi 69

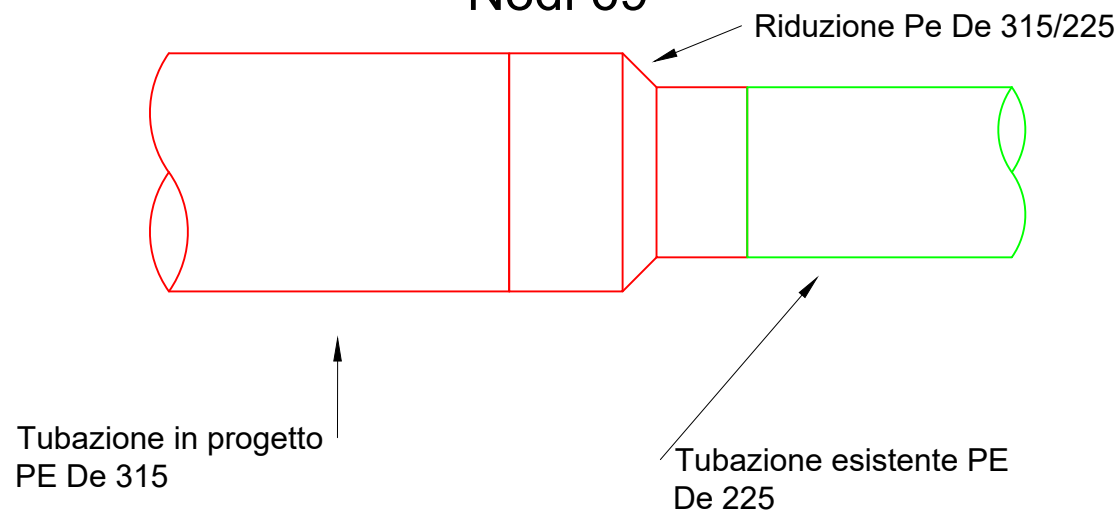


Tipologico 20
Ti di linea ACC DN 250

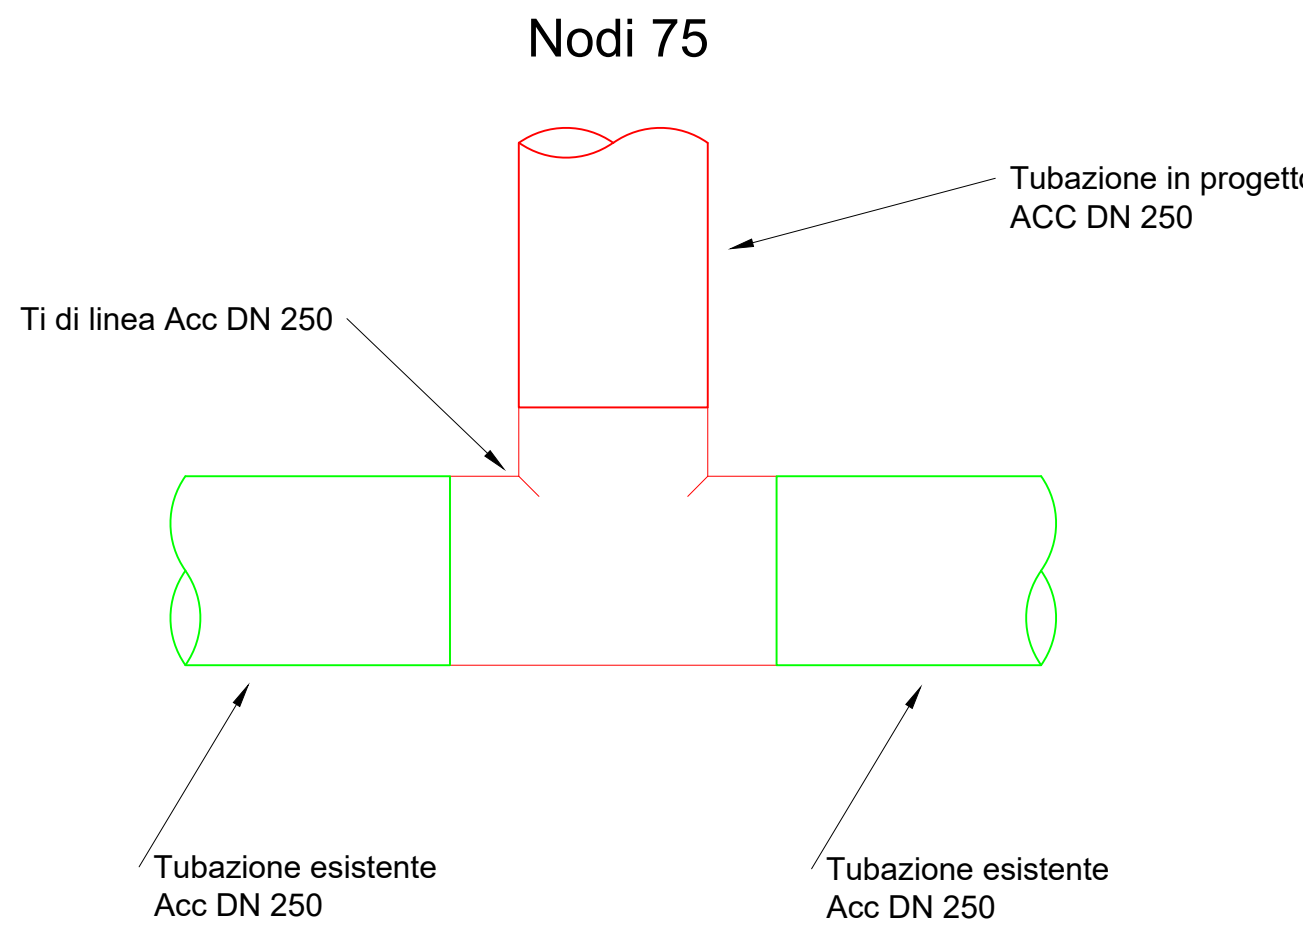


Tipologico 1
Collegamento in linea curva 45° Pe De 125
Nodi 66-85

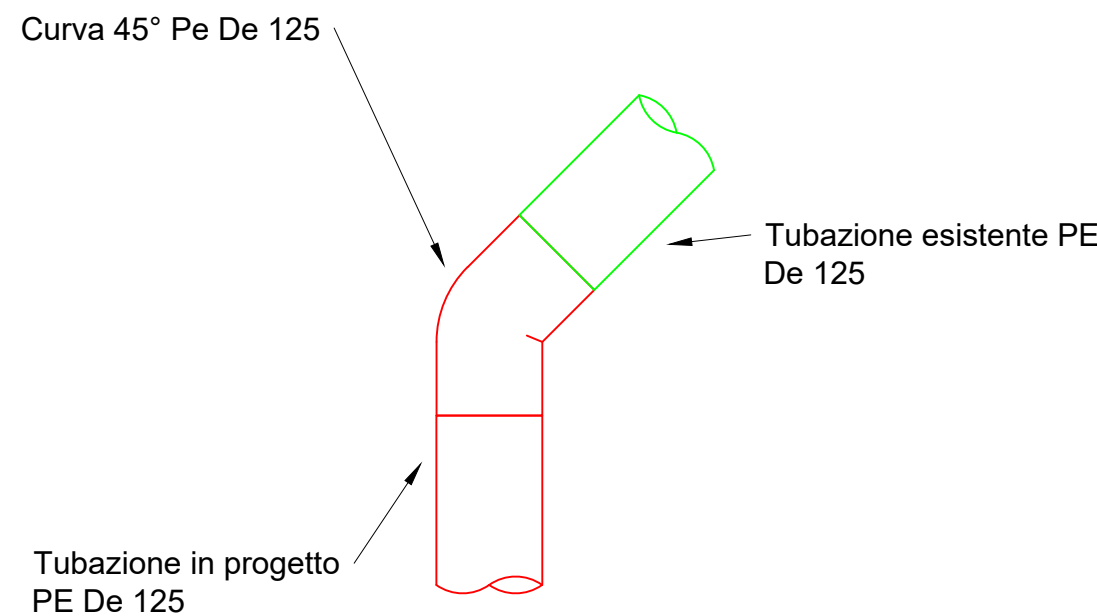


Tipologico 2
Collegamento in linea curva 45° Pe De 180
Nodo
1-18-38-43-54-63-64-68-80-107

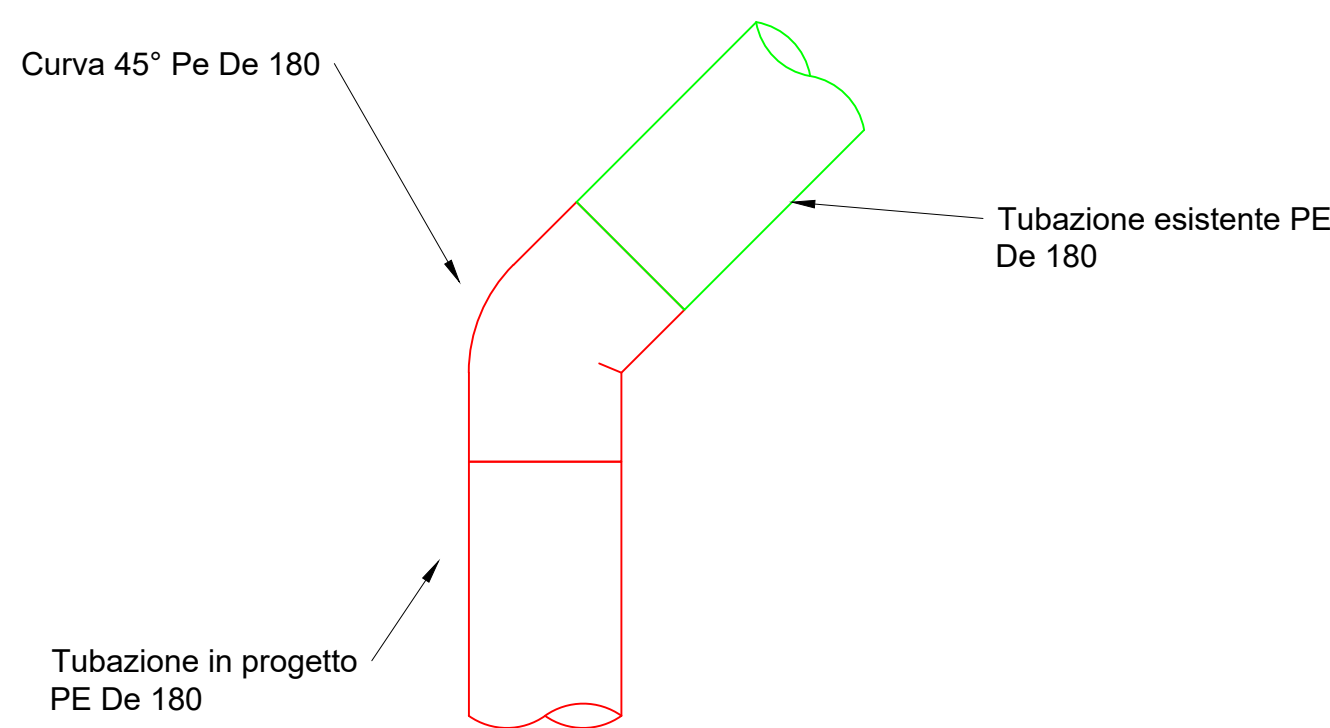

Tipologico 3
Collegamento in linea curva 45° Pe De 315
Nodi 106

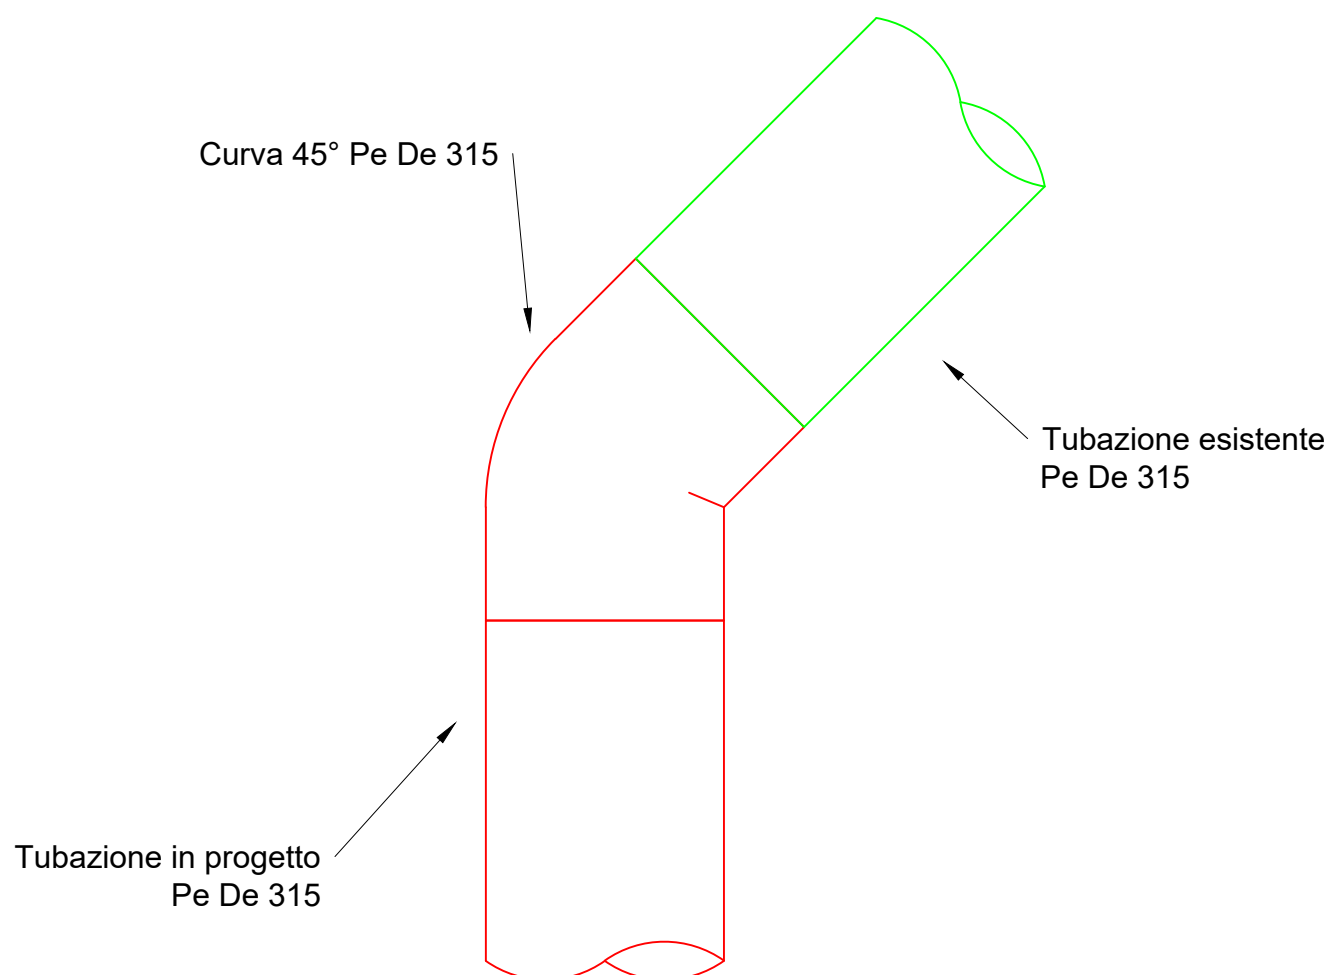


Tipologico 4
Curva 90° Pe De 225
Nodo 25

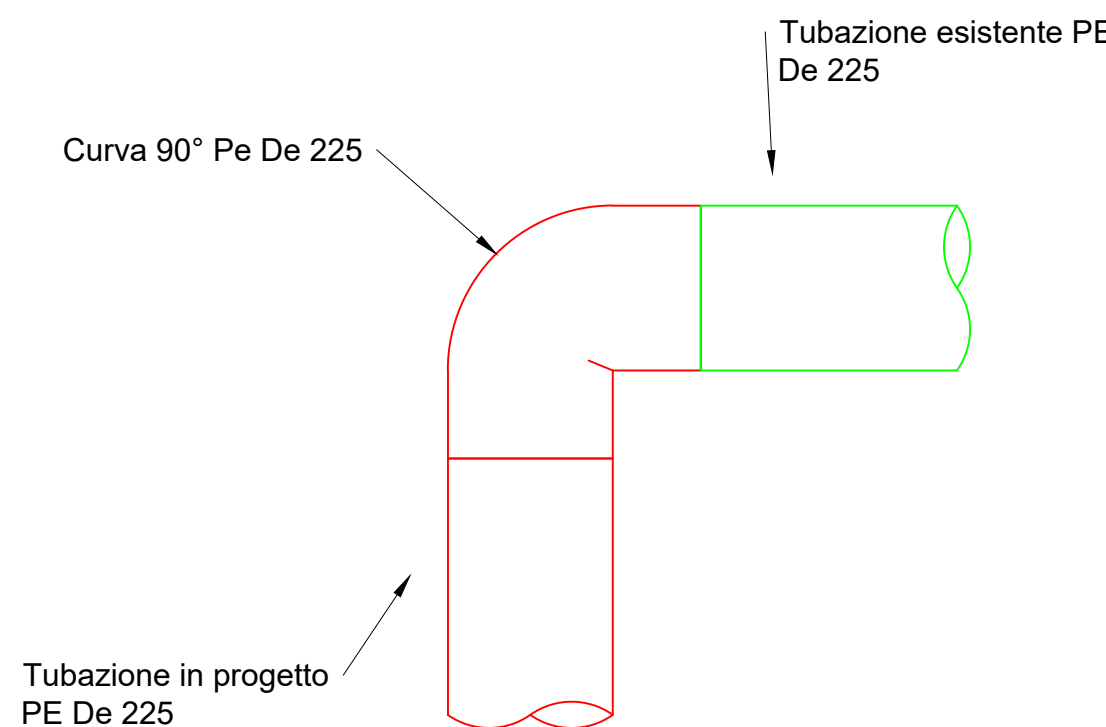


Tipologico 22
Ti di linea Pe De 180


Nodi
15-17-47-48-50-112

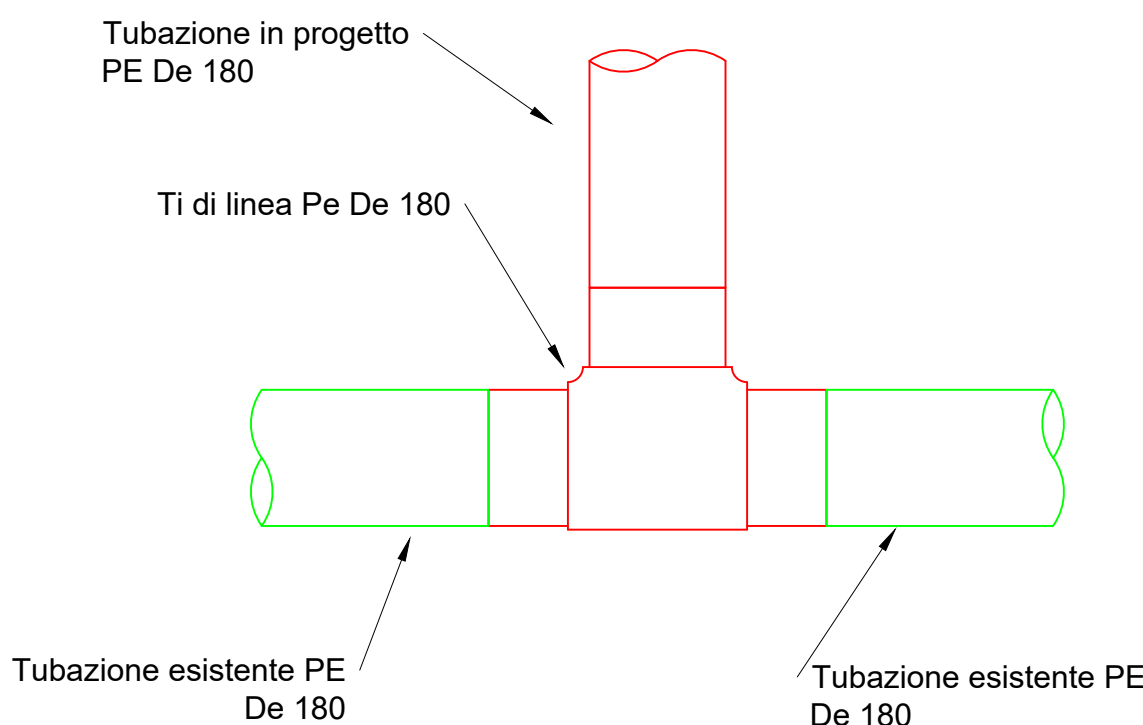


Tipologico 5
Curva 90° Pe De 315
Nodi 41

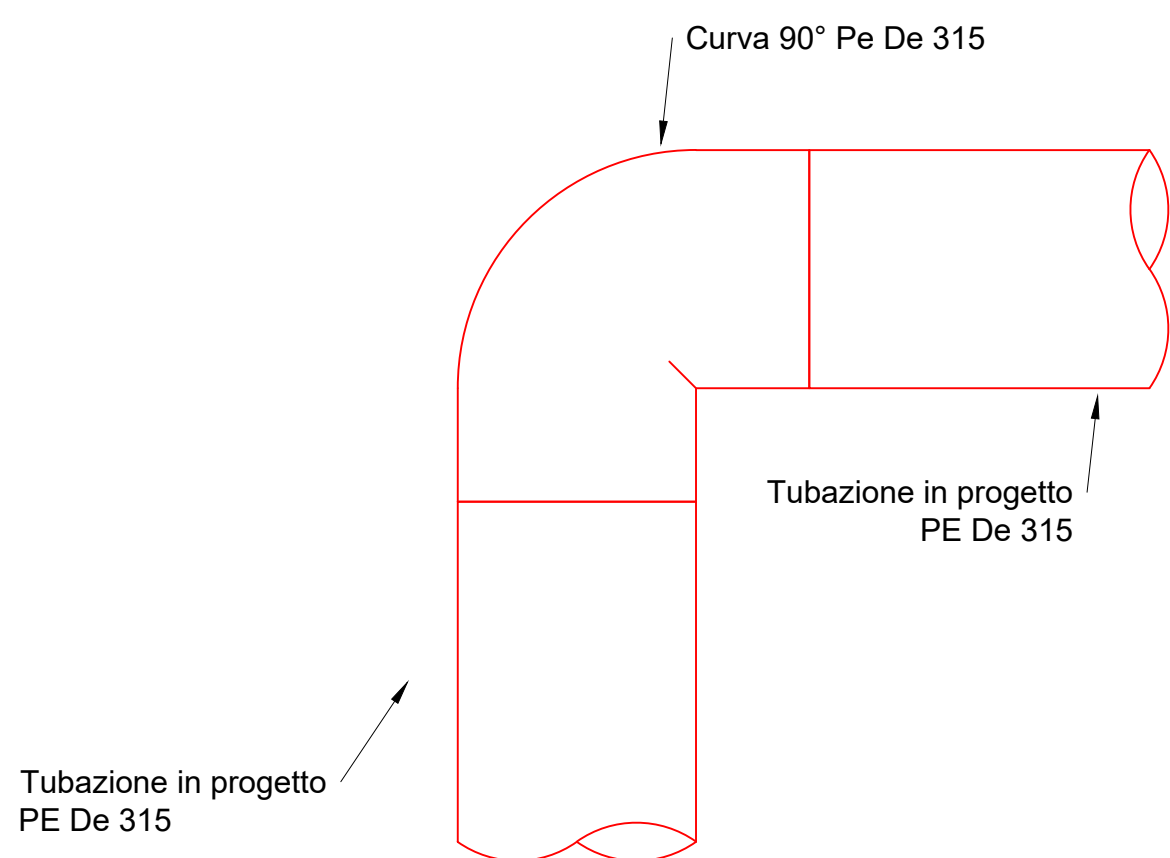


Tipologico 6
Fondello Pe De 125
Nodo
3-5-19-21-31-35-46-120

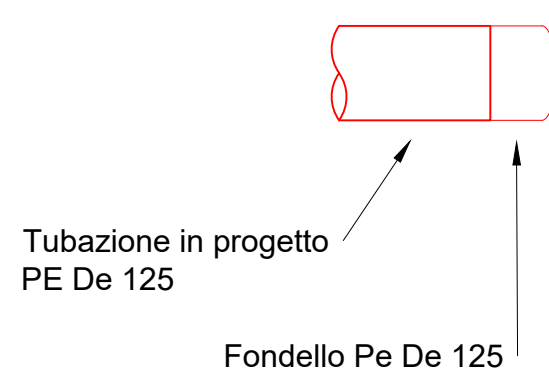


Tipologico 7
Fondello Pe De 180
Nodi 49-67

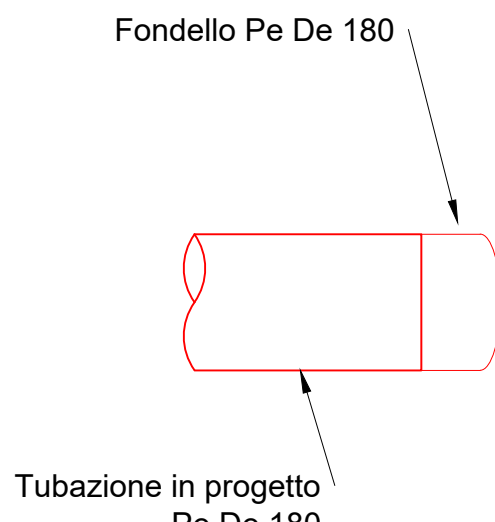


Tipologico 8
Fondello Pe De 315
Nodo 29

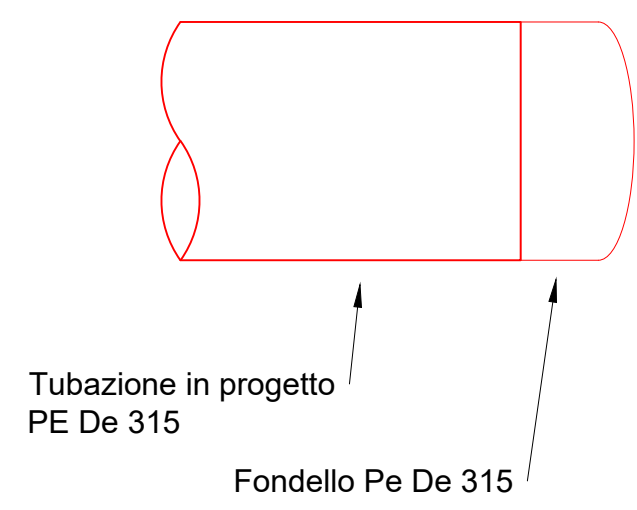


Tipologico 21
Ti di linea Pe De 125
Nodi 6-7-30-34

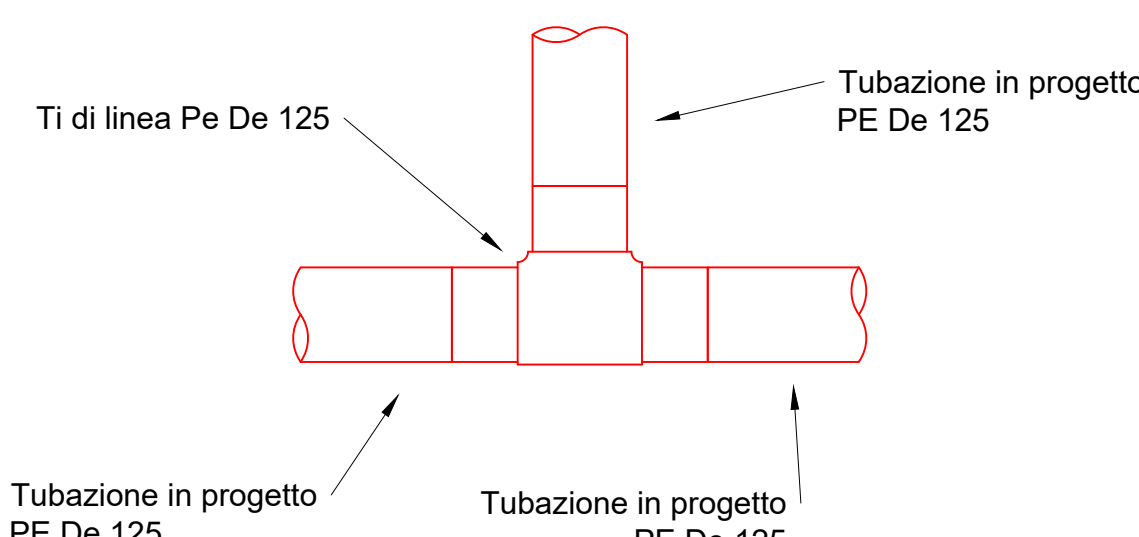


Tipologico 11
Raccordo di Transizione Pe De 180 - Acc DN 150
Nodi 16-51-
59-87-90-92-99-113-116-122

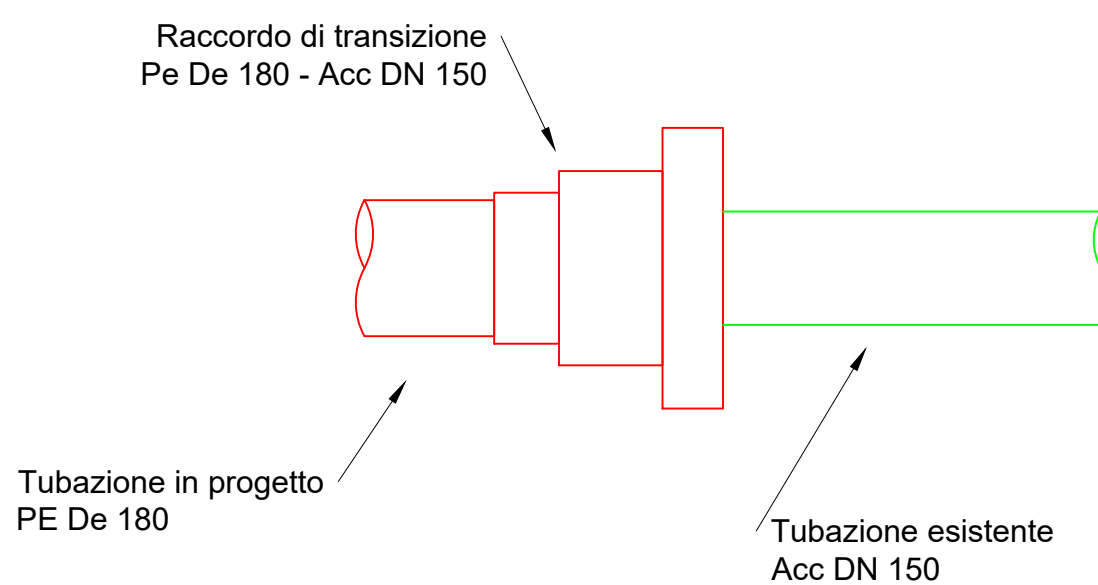


Tipologico 9
Raccordo di Transizione Pe De 125 - Acc DN 100
Nodi 119-32

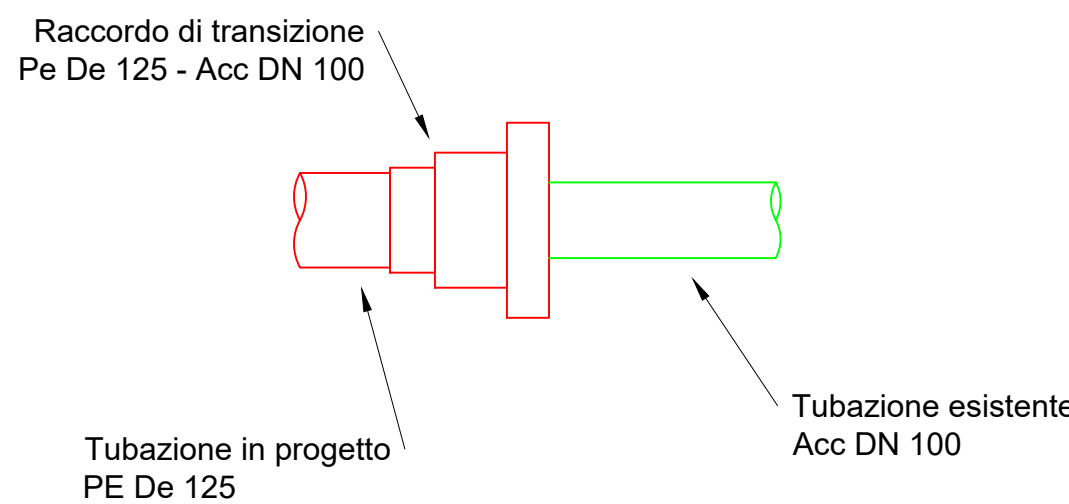






Tipologico 10
Raccordo di Transizione Pe De 125 - GH DN 125
Nodi 8

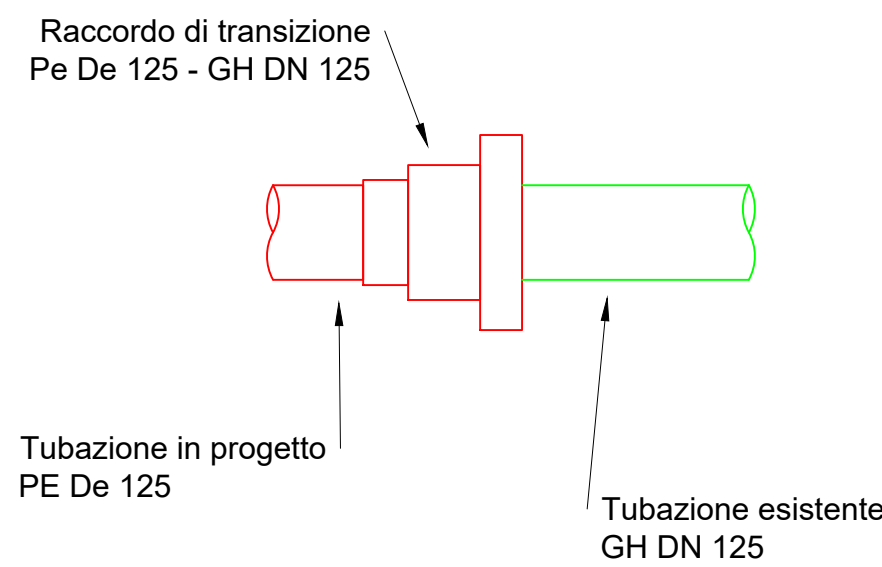


Tipologico 15
Riduzione ACC DN 300 - ACC DN 250
Nodi 81

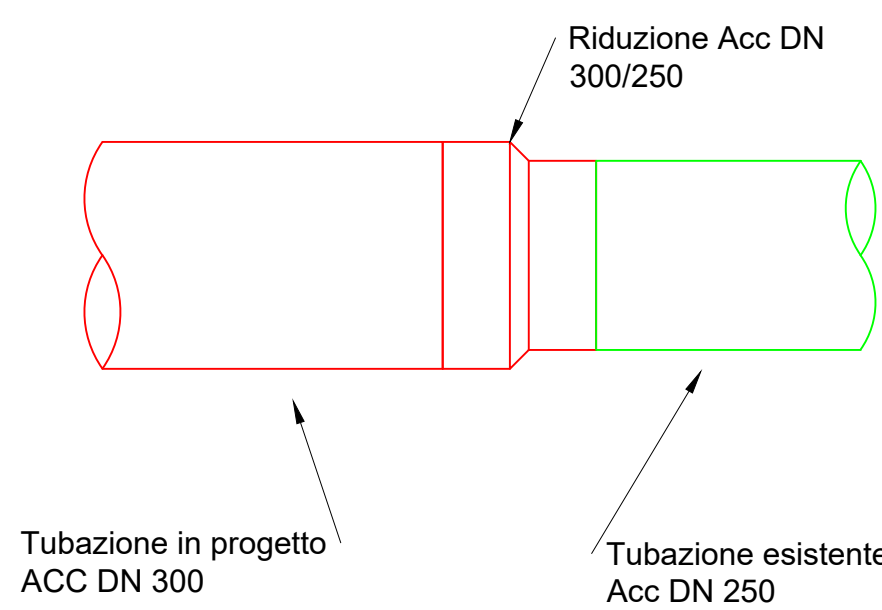


	Progettista: Ordine degli Ingegneri di Alessandria maestro ingegnere ALESSANDRO MAESTRO	Unità Responsabile della Progettazione INGEREAL-INGE-PROGRE
Progetto n°: 21-0584-3E-00-00/1272 WBS: SI.20.I0300.02.1109 ALLEGATO n°: 8.1	Revisione: Emissione per commenti	0 30 11 22 L.Cosentino L.Cantagna A.Leardi
Formato: A0 Scale: 1:10	Comm.: 2484	Rev. G. M. A. Redatto Controllato Approvato
Comitente: 	Comune di TORINO (TO) Via Vane Progetto Esecutivo SOSTITUZIONE RETE BP (L=2745,39 M) - GARA TO 1 Intervento n° SI-036213-001272-TSS-TORIN008 Particolari costruttivi - Tavola 1	

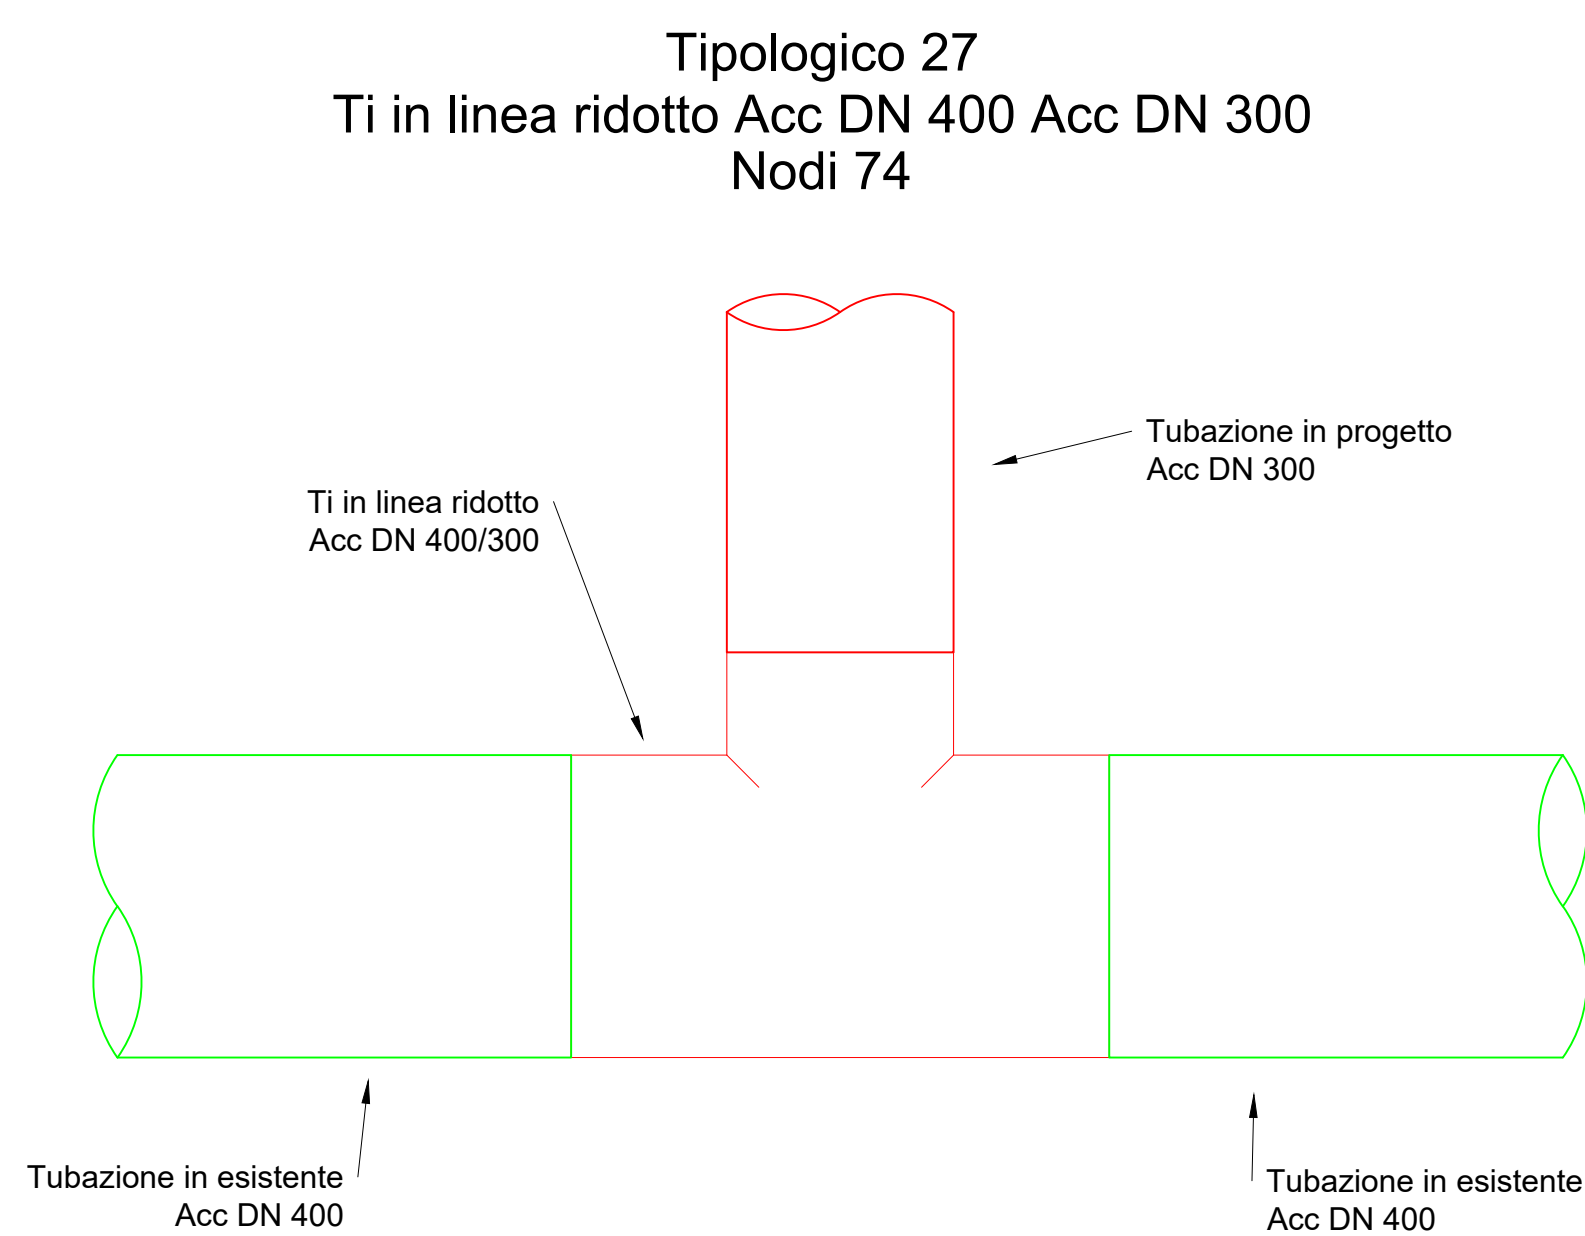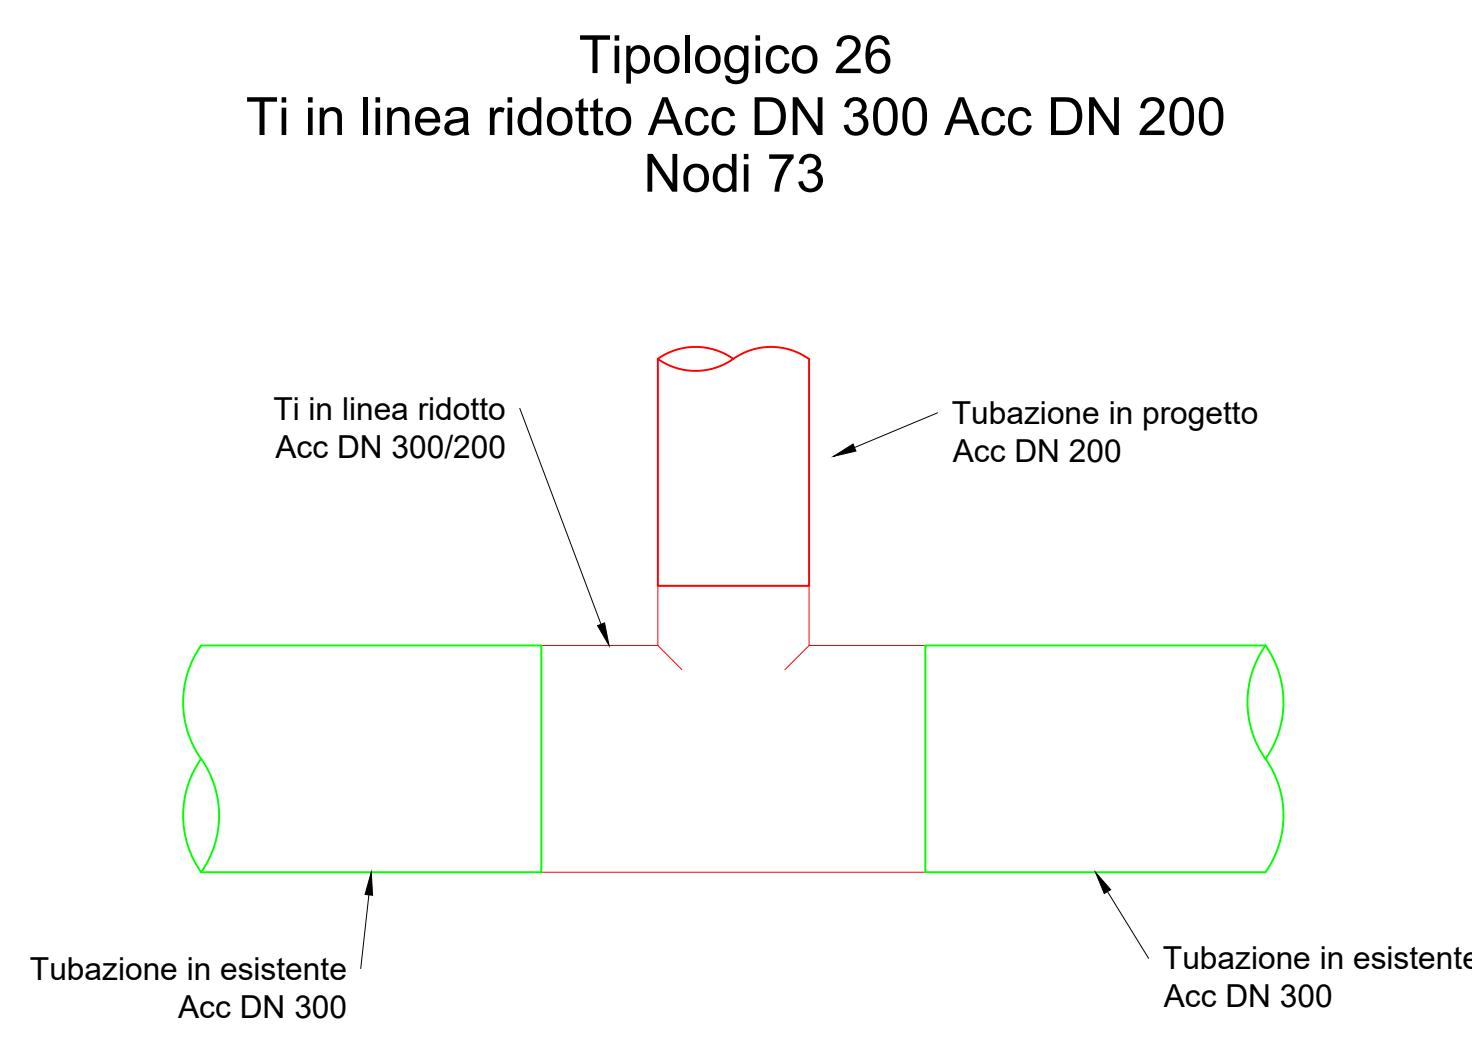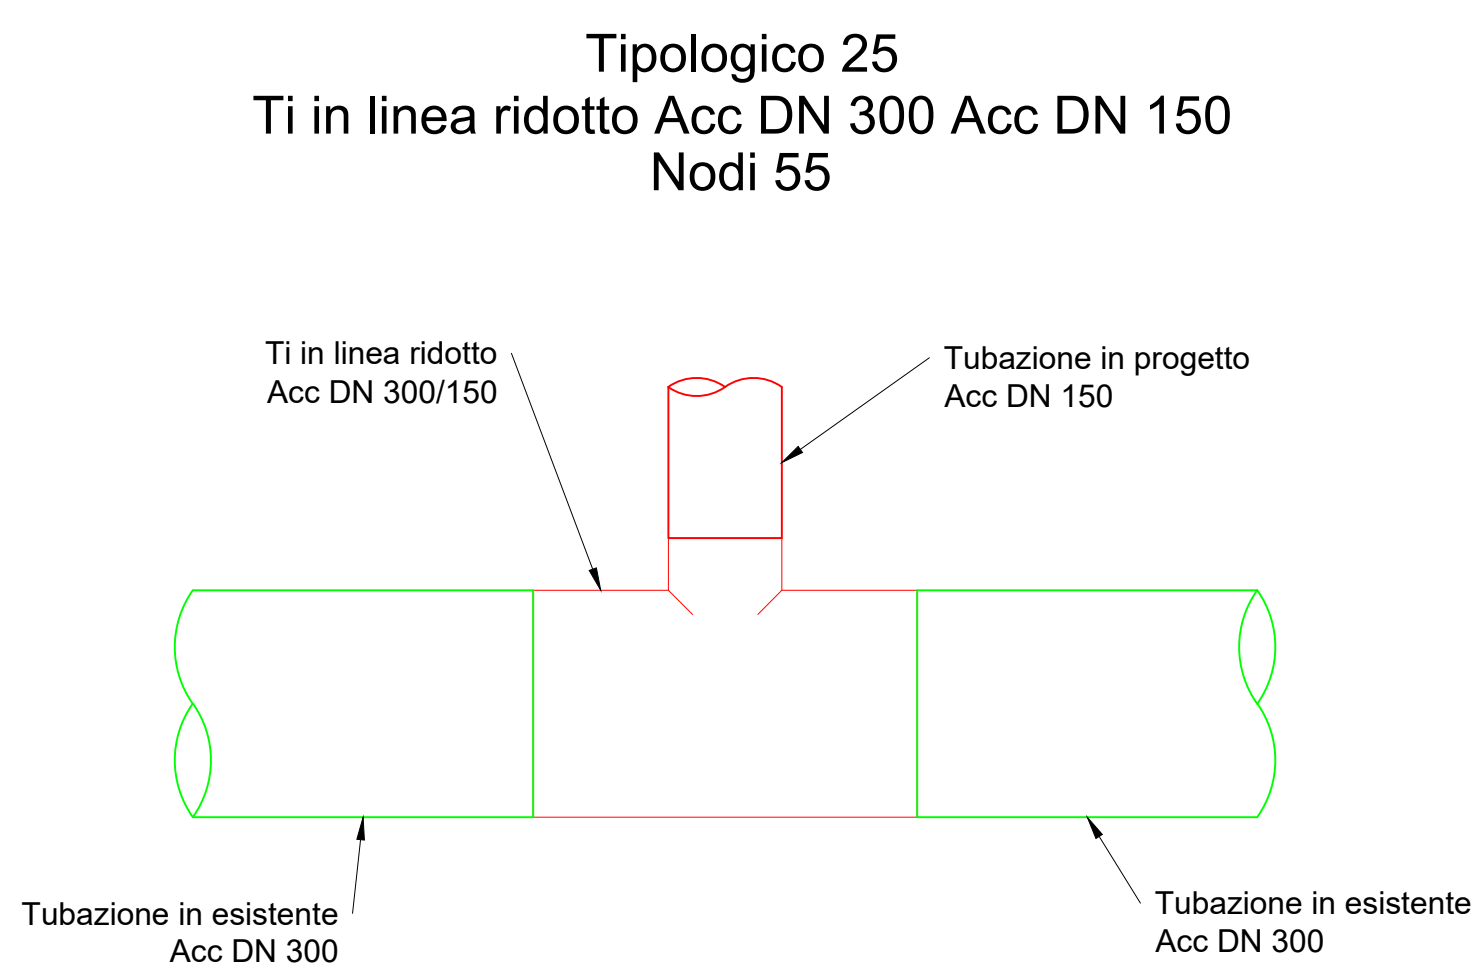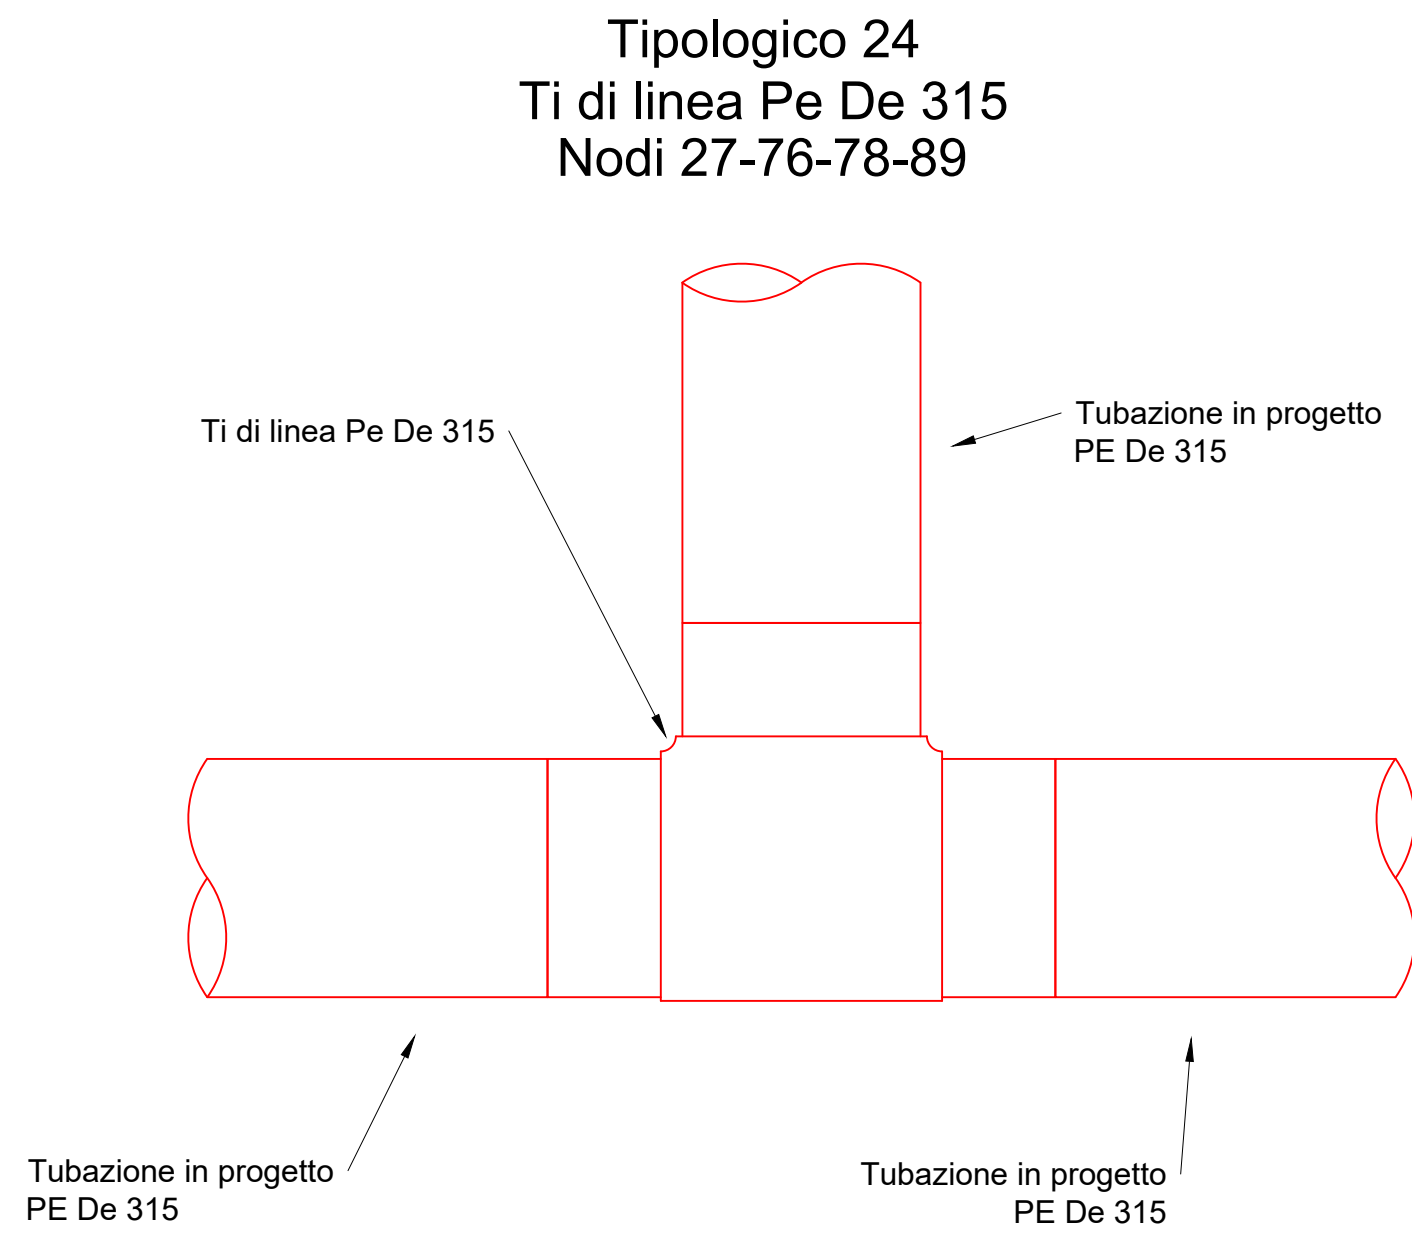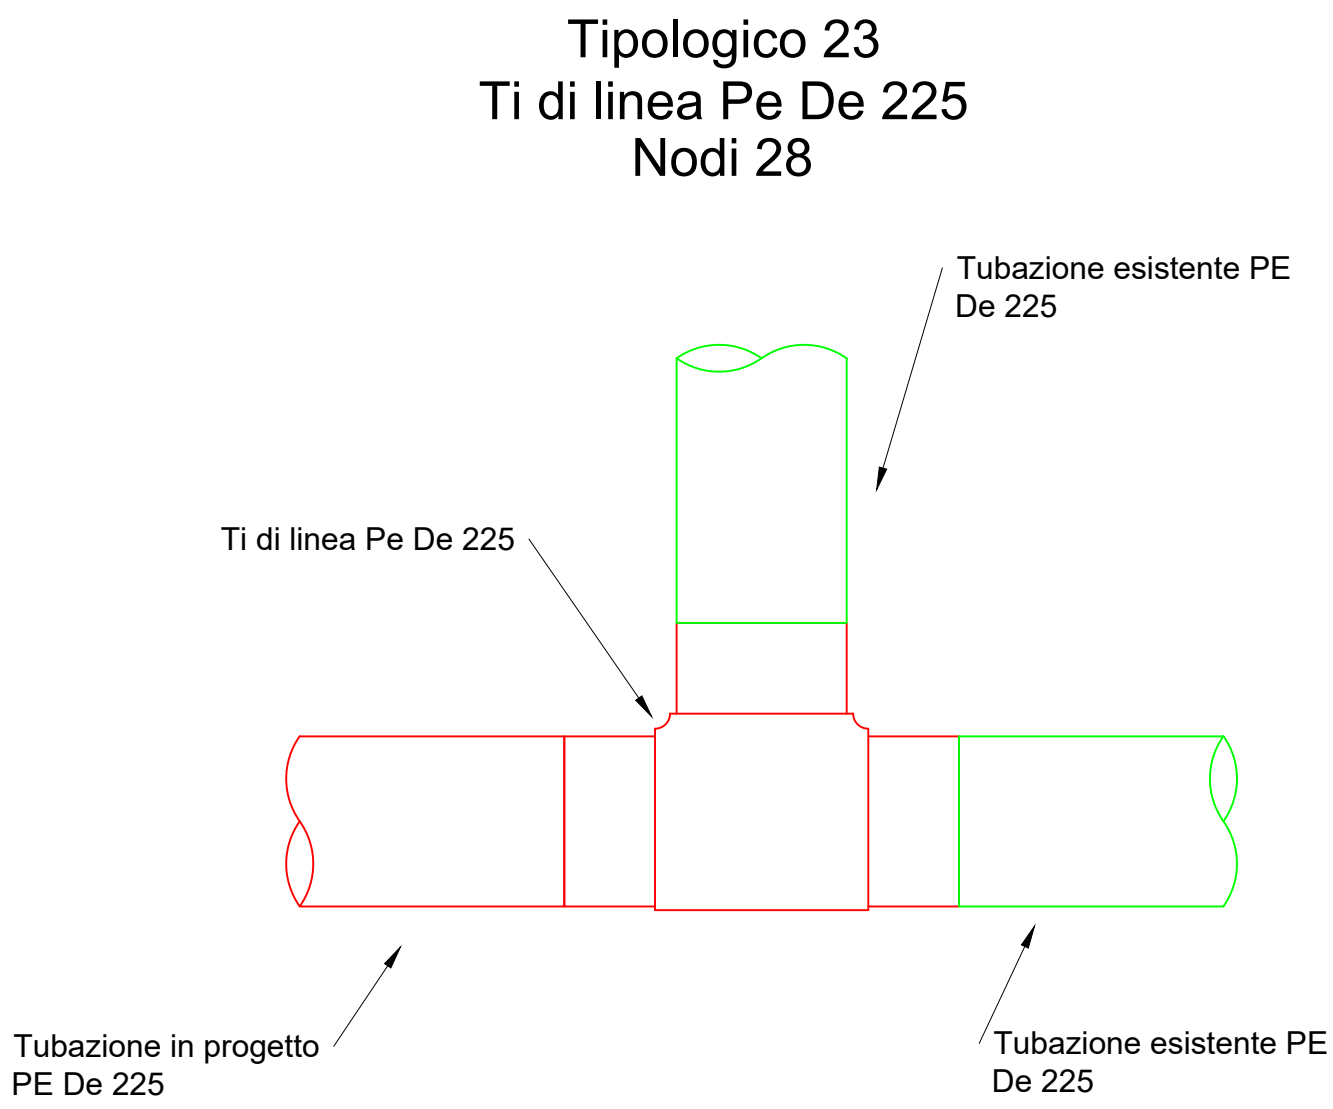


Tipologico 28
Ti in linea ridotto Pe De 125 - Pe De 90
Nodi 23-33-45

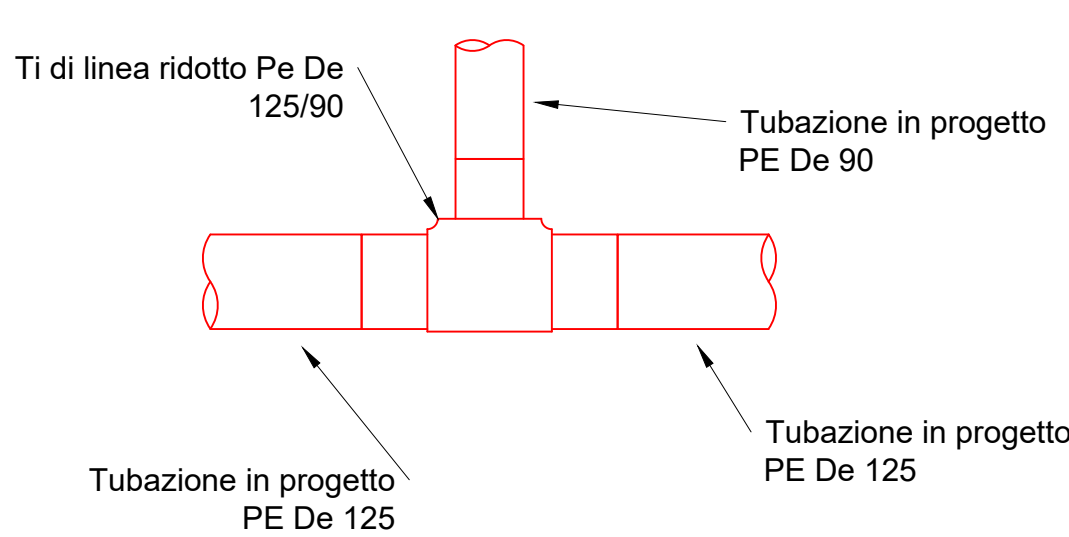


Tipologico 29
Ti in linea ridotto Pe De 180 - Pe De 125
Nodi 44-84

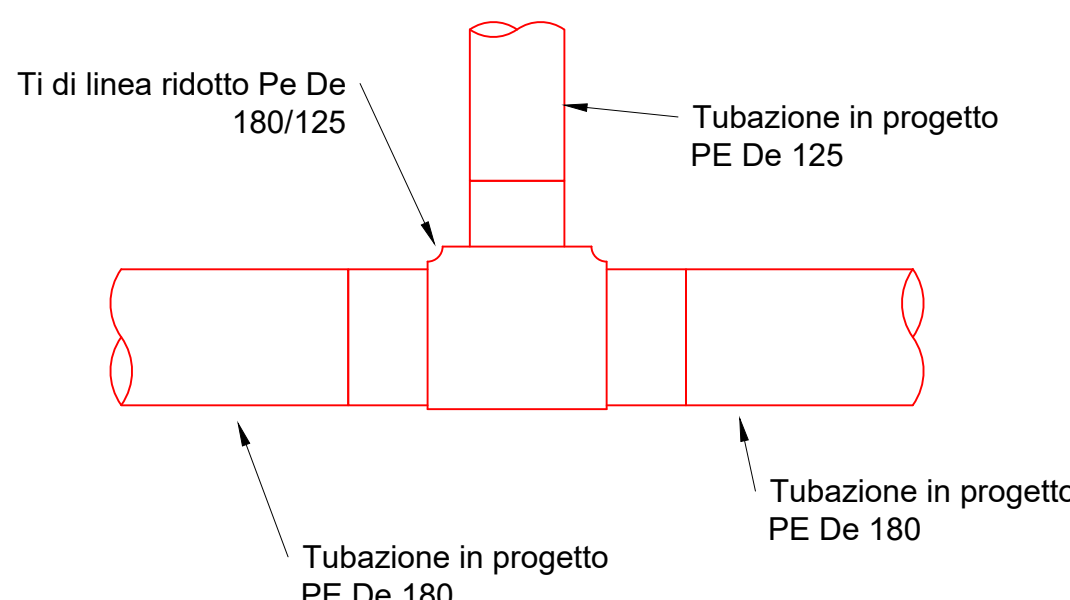


Tipologico 30
Ti in linea ridotto Pe De 180 - Pe De 90
Nodi
10-11-12-13-14-39-40-52-53-57-60-61-
62-86-108-109-110-111-114-115

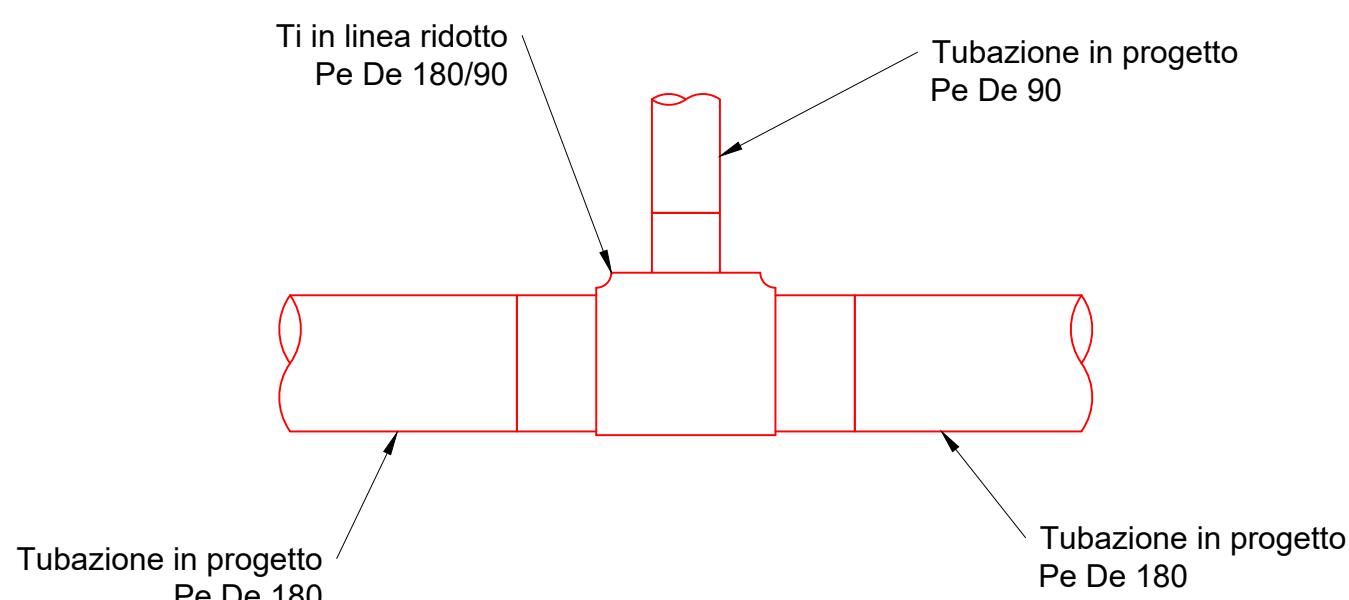


Tipologico 31
Ti in linea ridotto Pe De 225 - Pe De 180
Nodi 58

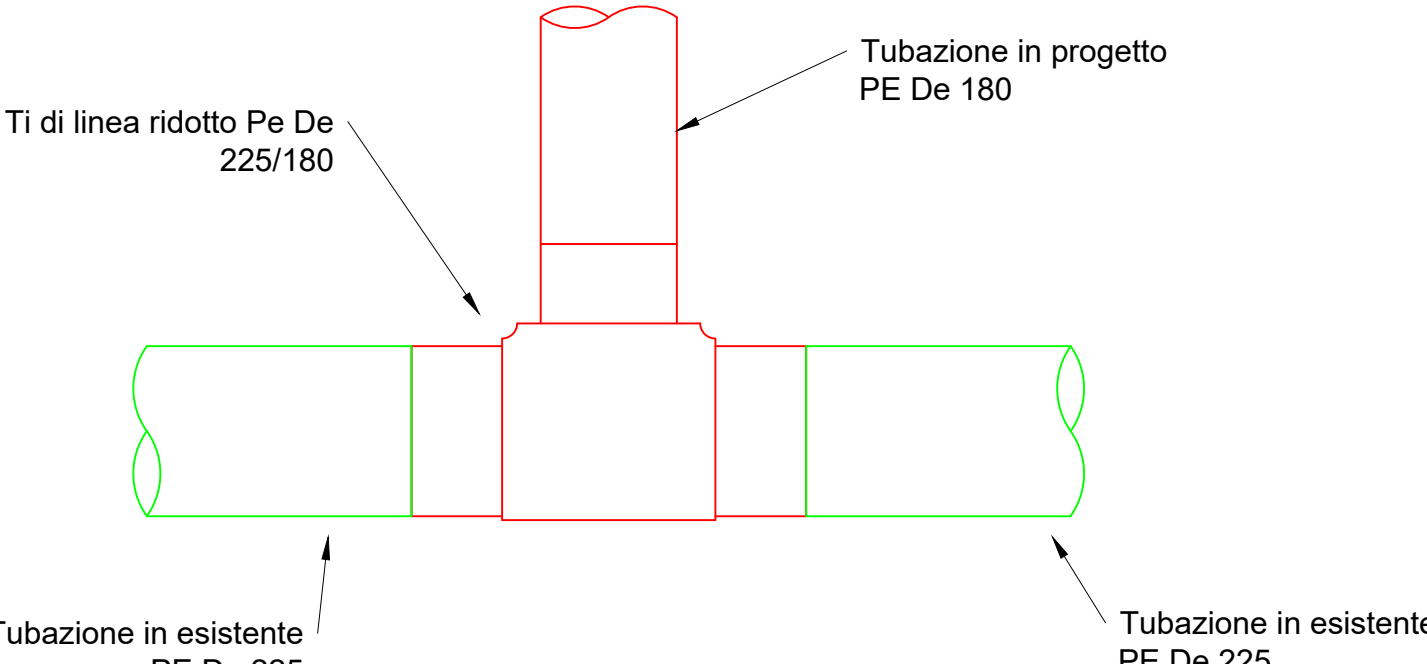


Tipologico 32
Ti in linea ridotto Pe De 225/90
Nodi 71-72

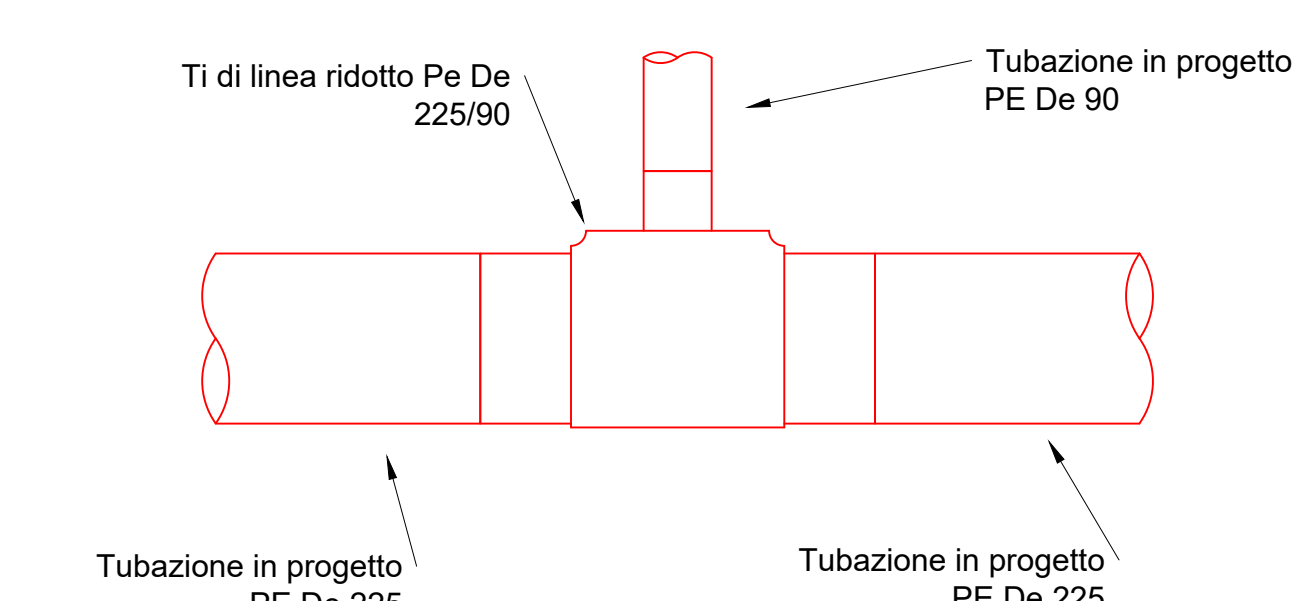


Tipologico 33
Ti in linea ridotto Pe De 315/225
Nodi
24-26-70-82-83-88-91-93-94-95-96-
97-98-100-102-103-104-105-121-123

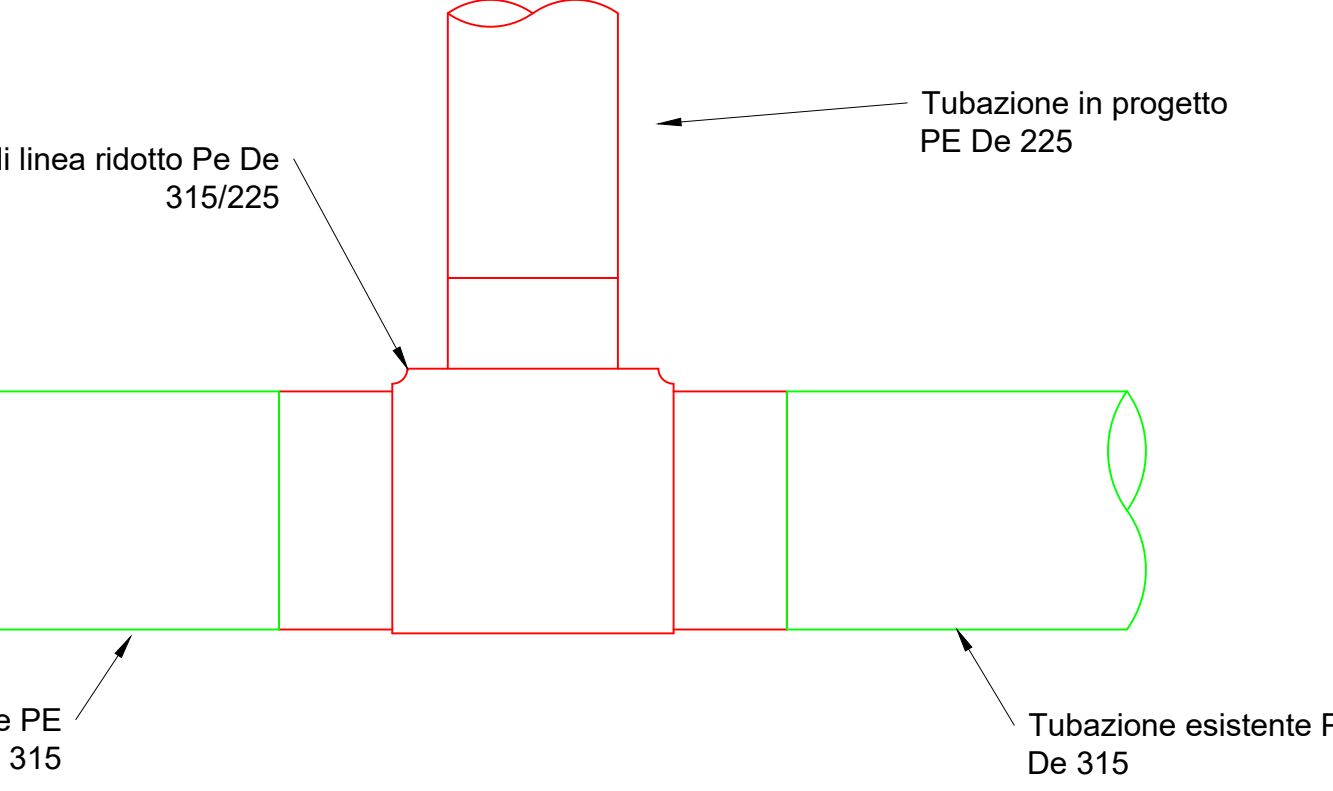


Tipologico 34
Collegamento in linea Pe De 180
Nodi 56

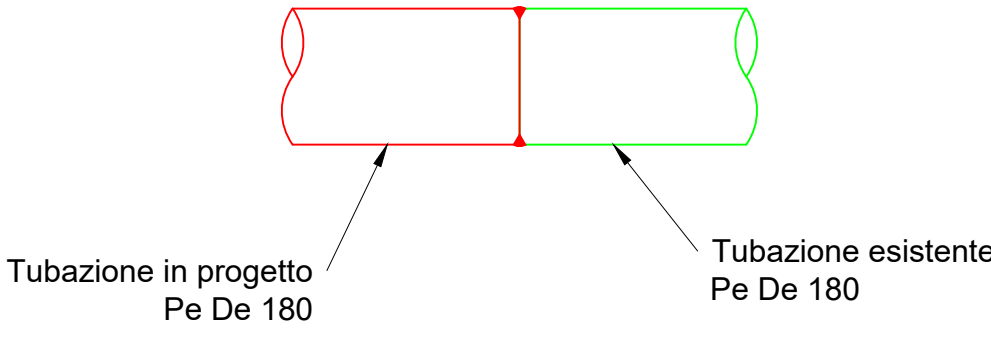


Tipologico 35
Collegamento in linea Pe De 125
Nodi 101

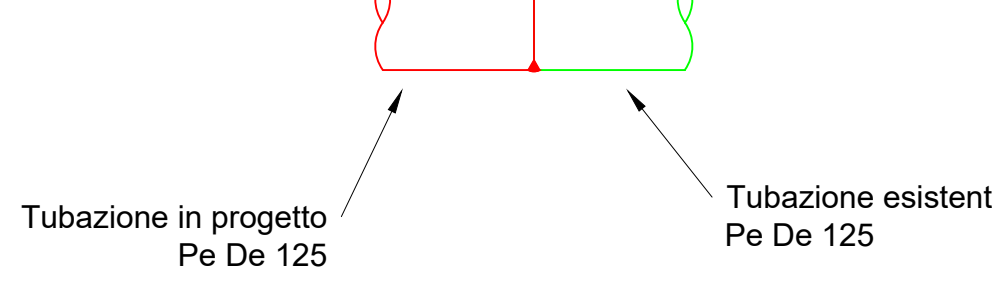


Tipologico 36
Collegamento in linea Pe De 225
Nodi 37

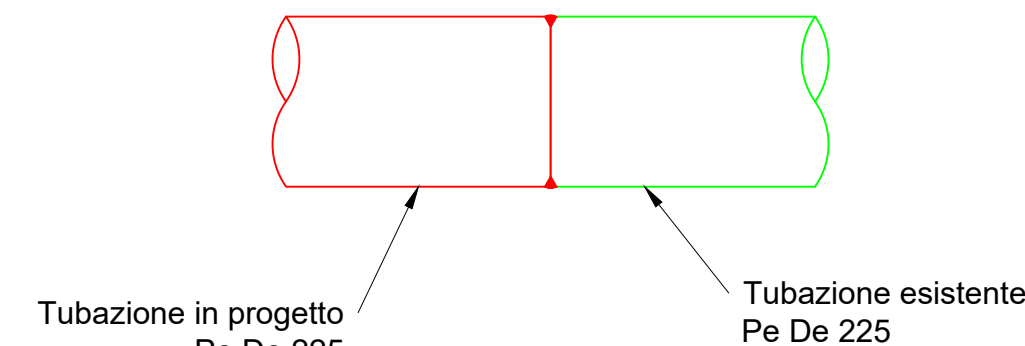


Tipologico 37
Collegamento in linea Pe De 315
Nodi 117

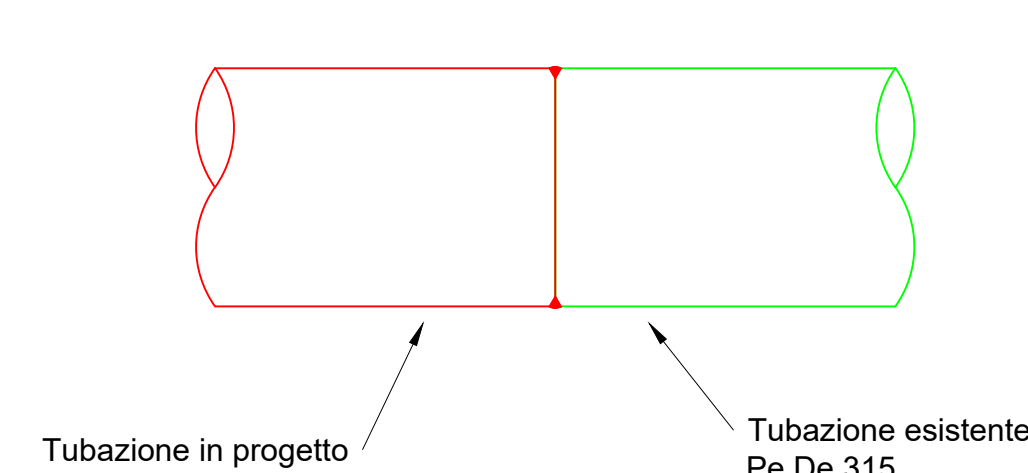

Tipologico 12
Raccordo di Transizione Pe De 225 - Acc DN 200
Nodi 36-42

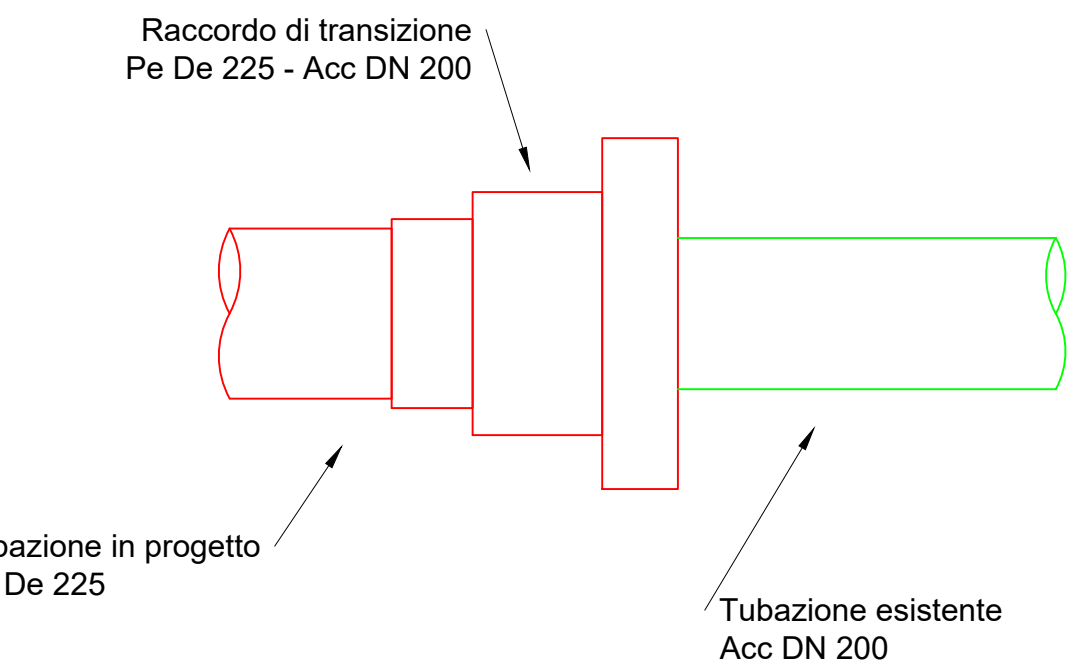

Tipologico 13
Raccordo di Transizione Pe De 315 - Acc DN 300
Nodi 2-77-118

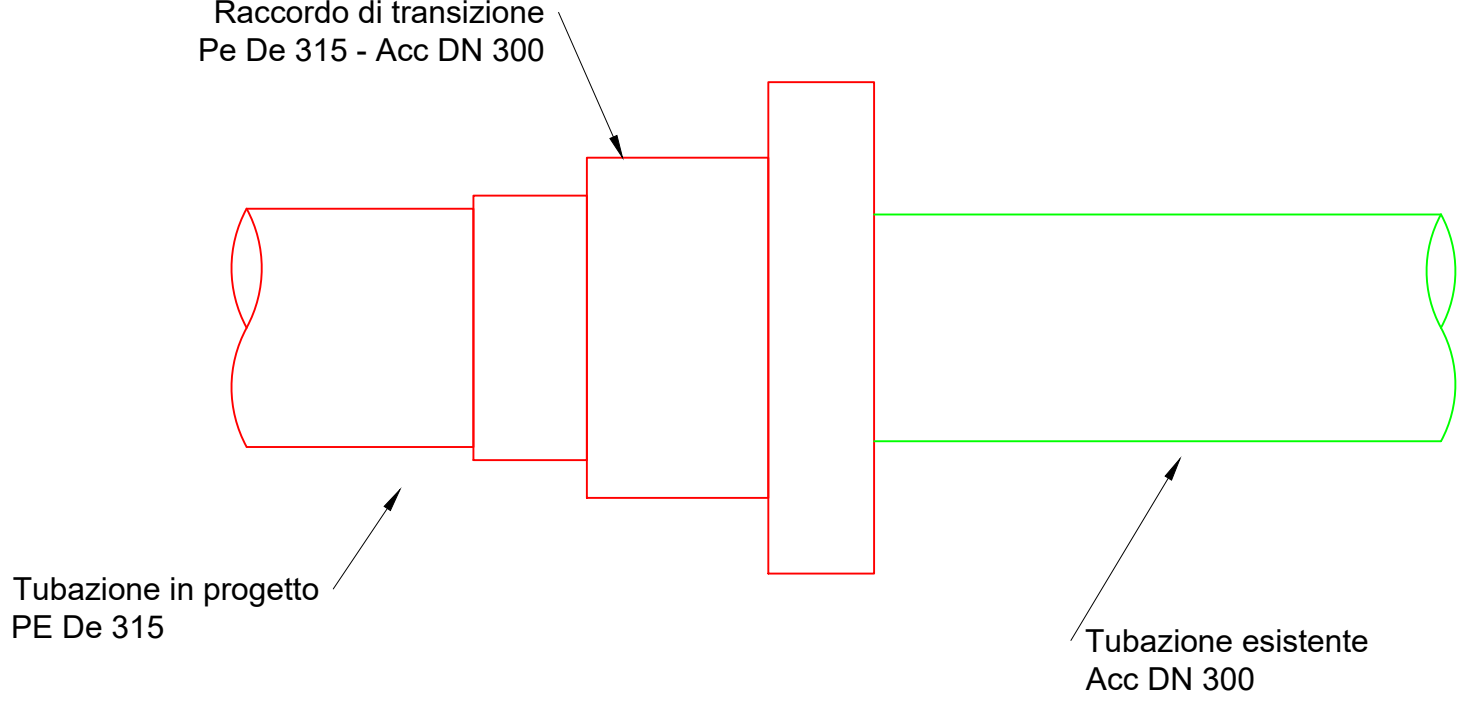

Tipologico 14
Raccordo di Transizione Pe De 315 - GH DN 250
Nodi 22

