


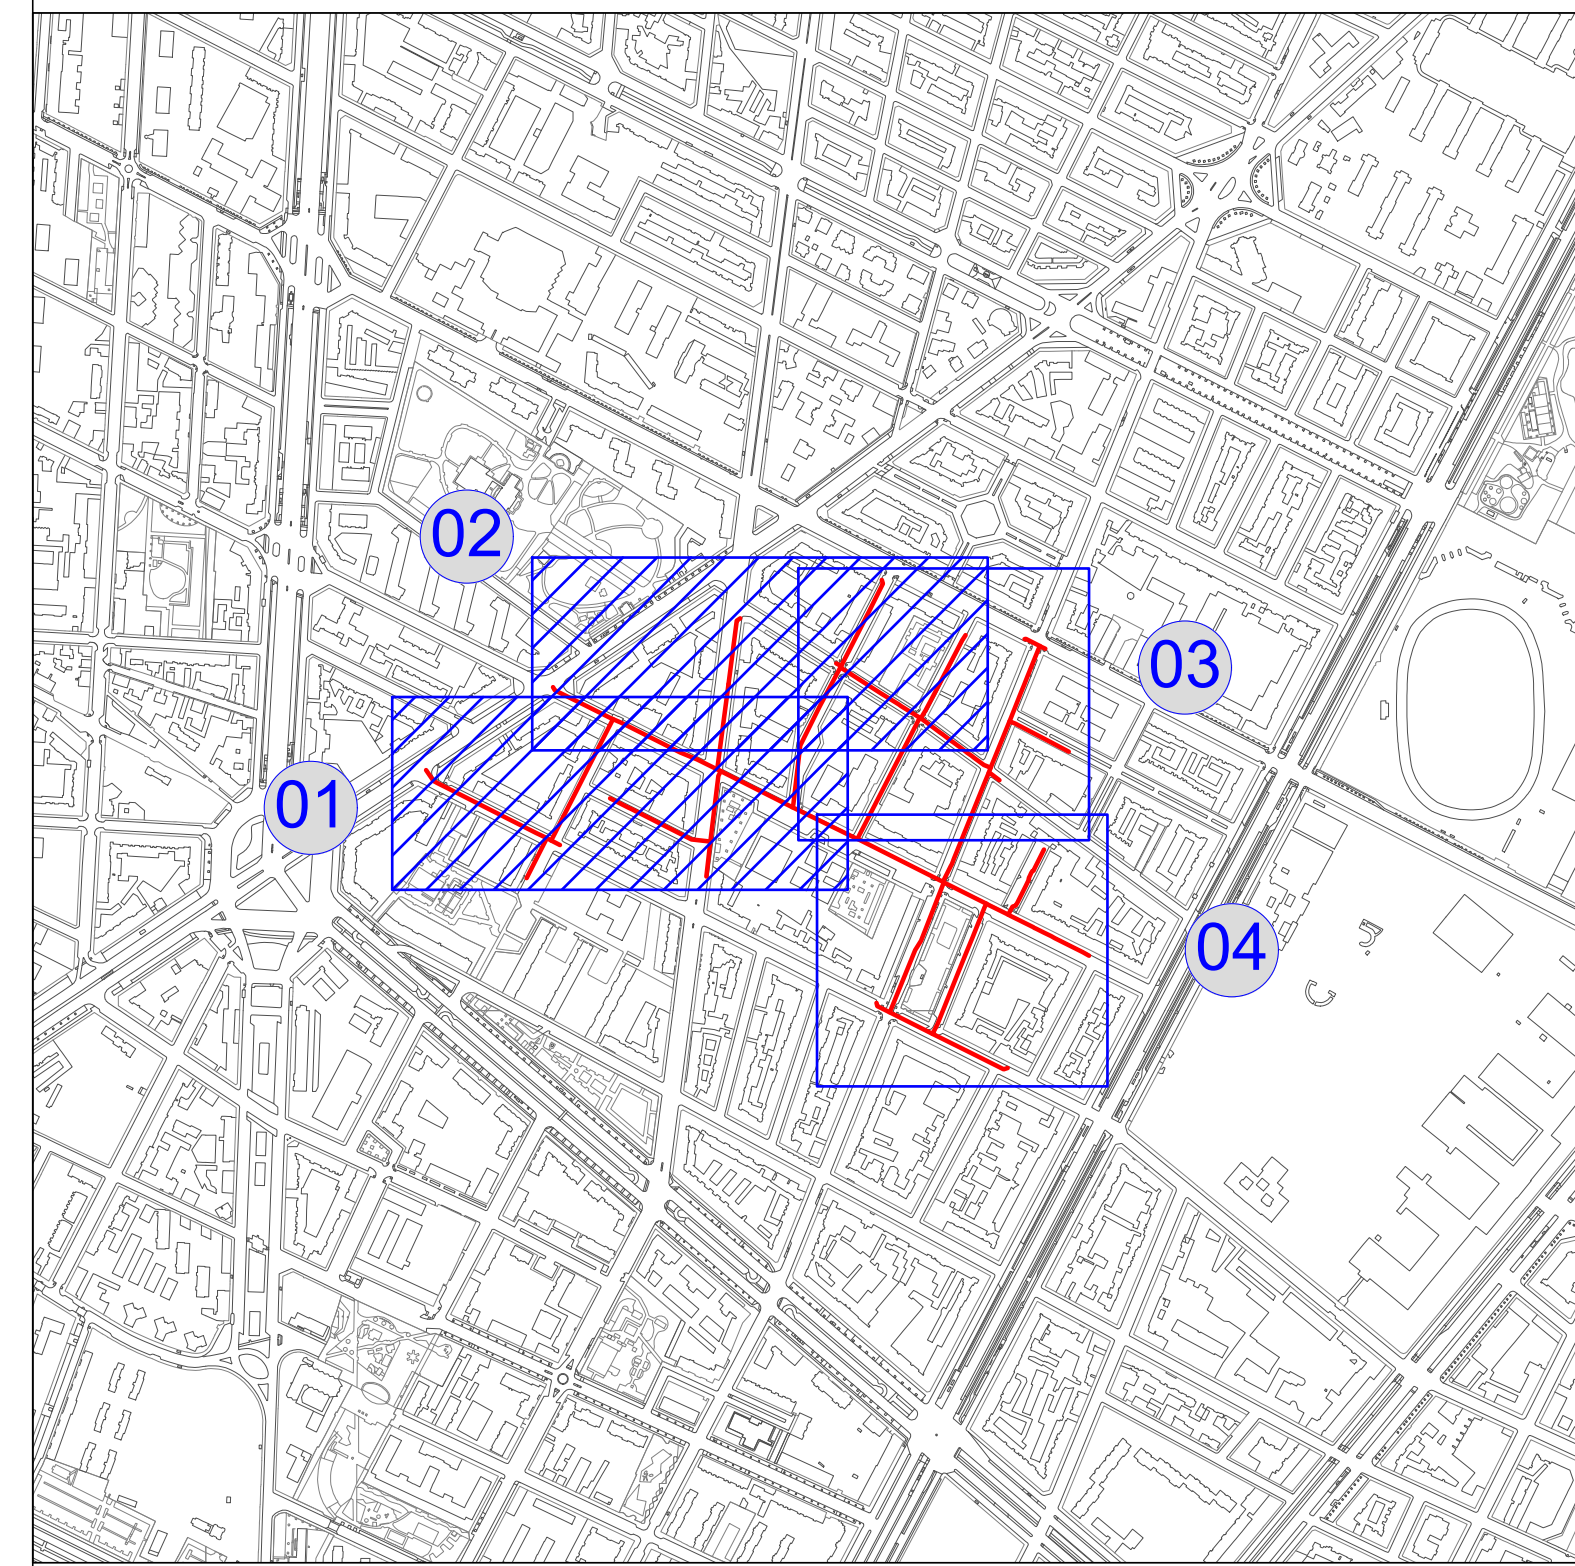


LEGENDA

	Rete in progetto BP		Zona di lavoro
	Rete da rimuovere BP		n° Zona di lavoro

Riquadro 1



Riquadro 2

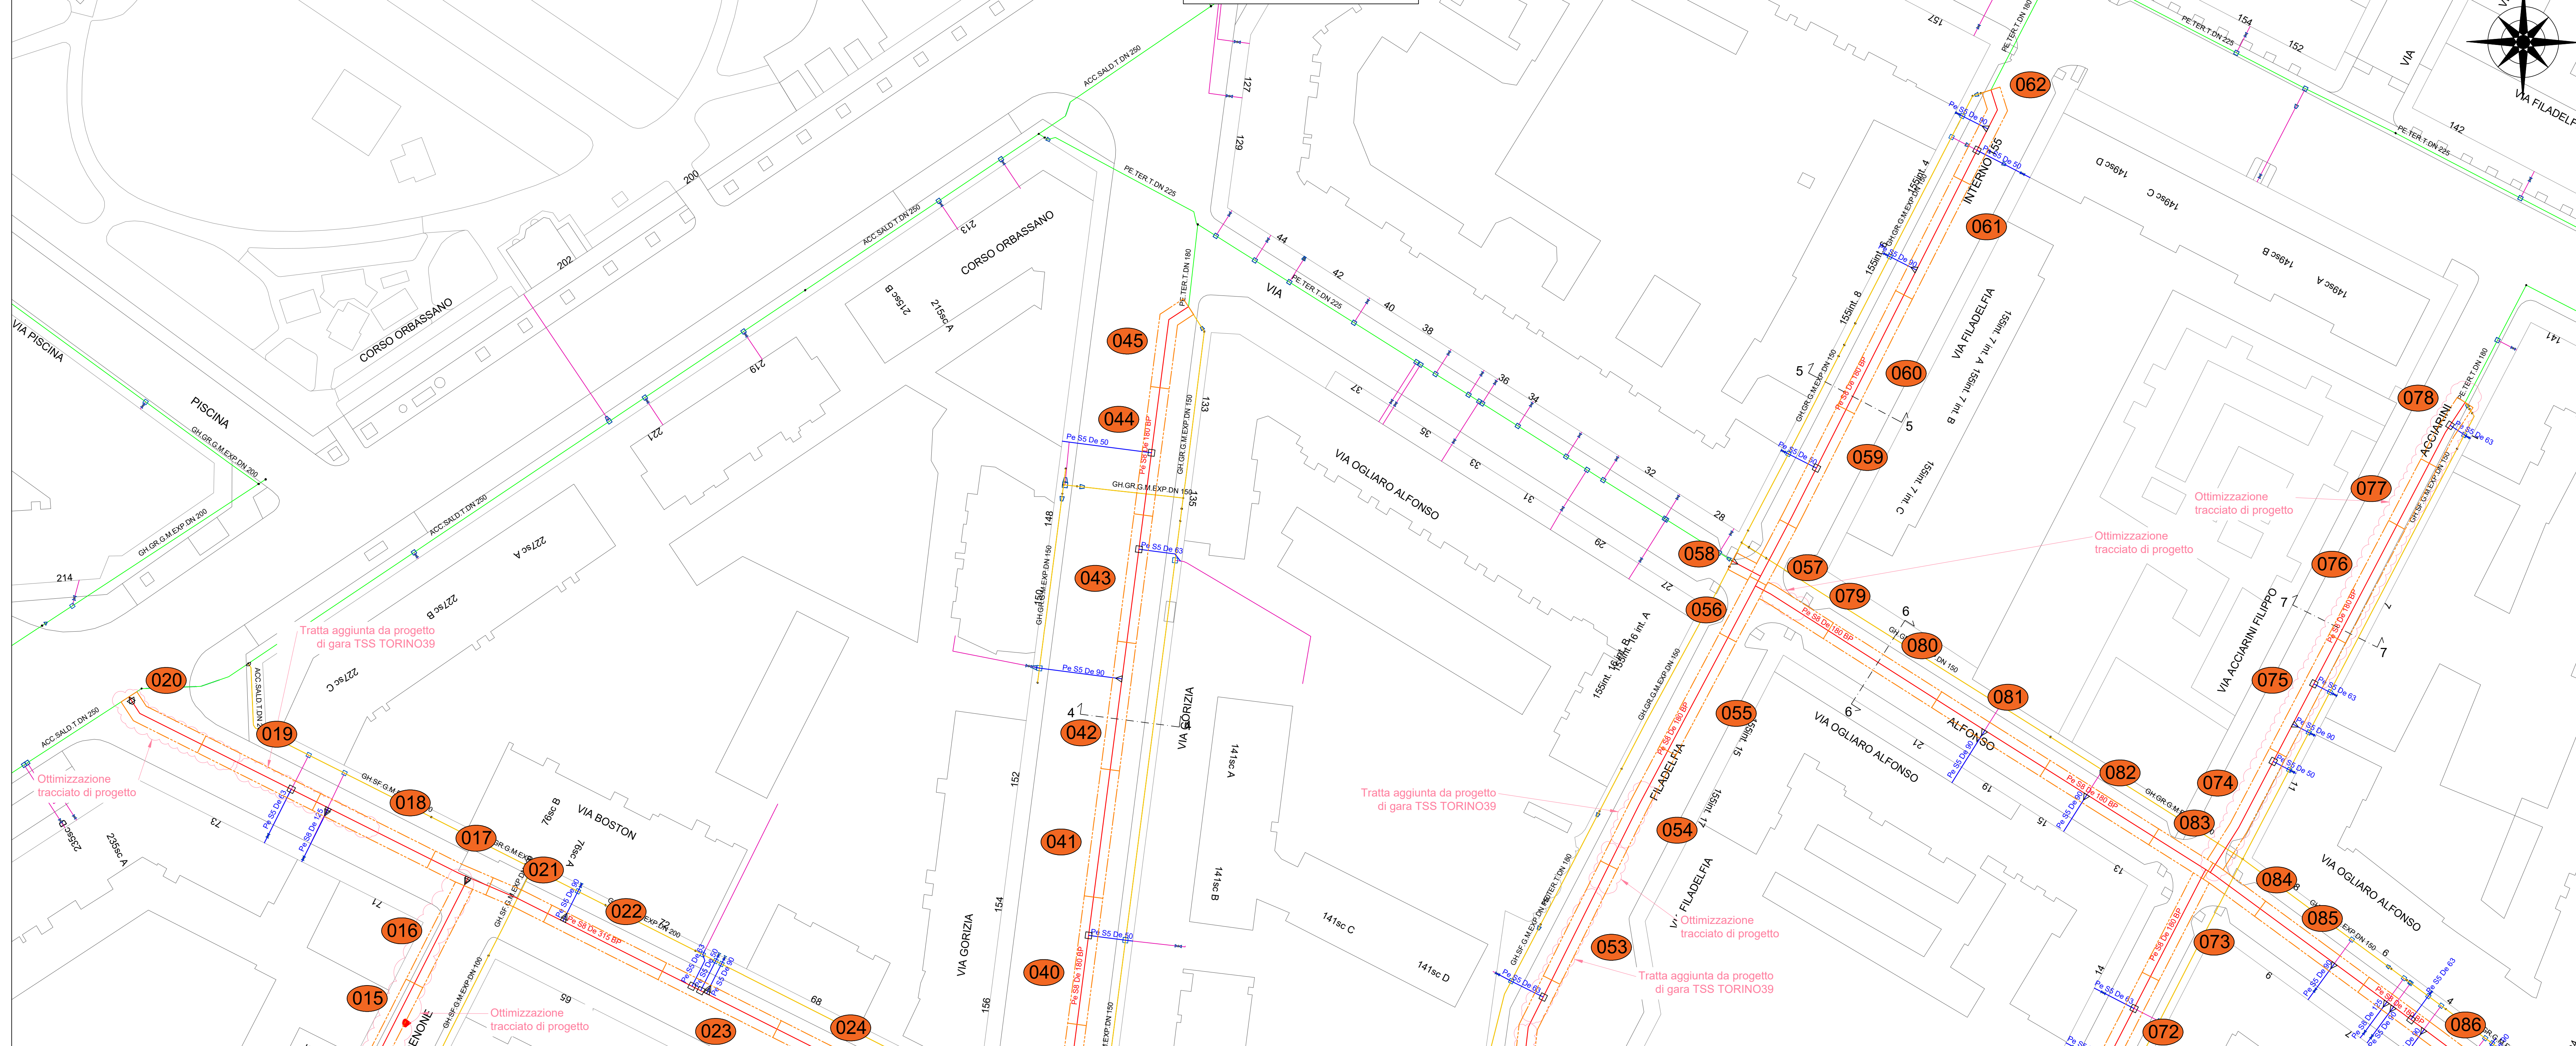



Progetto n°:
22-0320-3E-00-001272
WBS:
SI.20.10300.02.1109
ALLEGATO n°: 10.1
Formato: A0
Scale: 1:500
Comitato: 2484

Progettista:
Ordine degli Ingegneri di Alessandria
m. 22/03/2024

Unità Responsabile della Progettazione:
INGEREAL-INGE-PROGRE



Revisione	0	04	11	22	L. Tassinari	L. Cantagalli	A. Leardi
Elaborazione per commenti							
Redatto							
Controllato							
Approvato							

Comune di TORINO
Via Varesina
Progetto Esecutivo
SOSTITUZIONE RETE IN BP (L=2604,78 m) GARA ATEM T01
Intervento n° SI-036215-001272-TSS-TORINO36
Layout di cantiere - Tavola 1

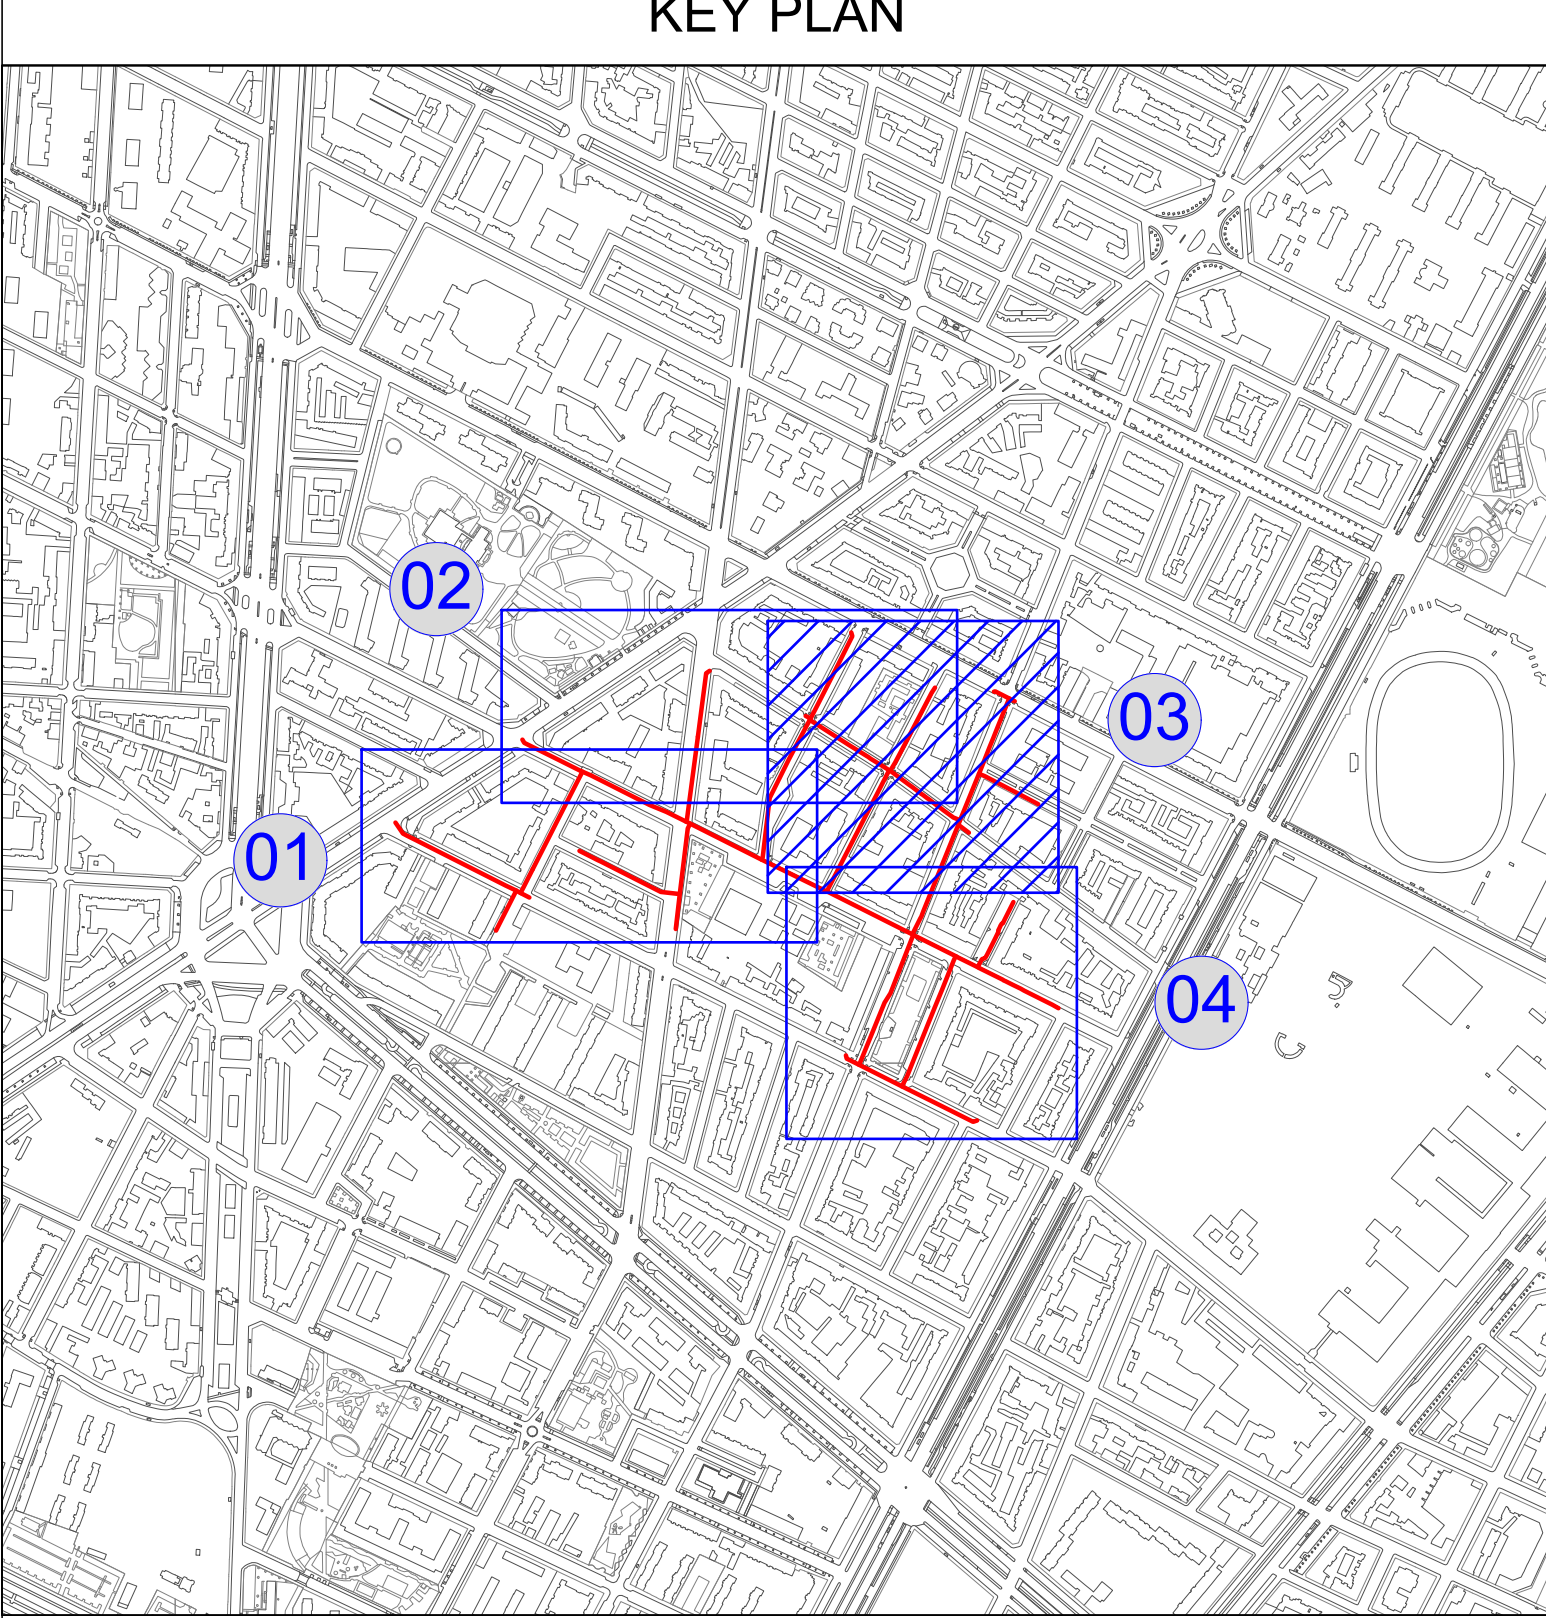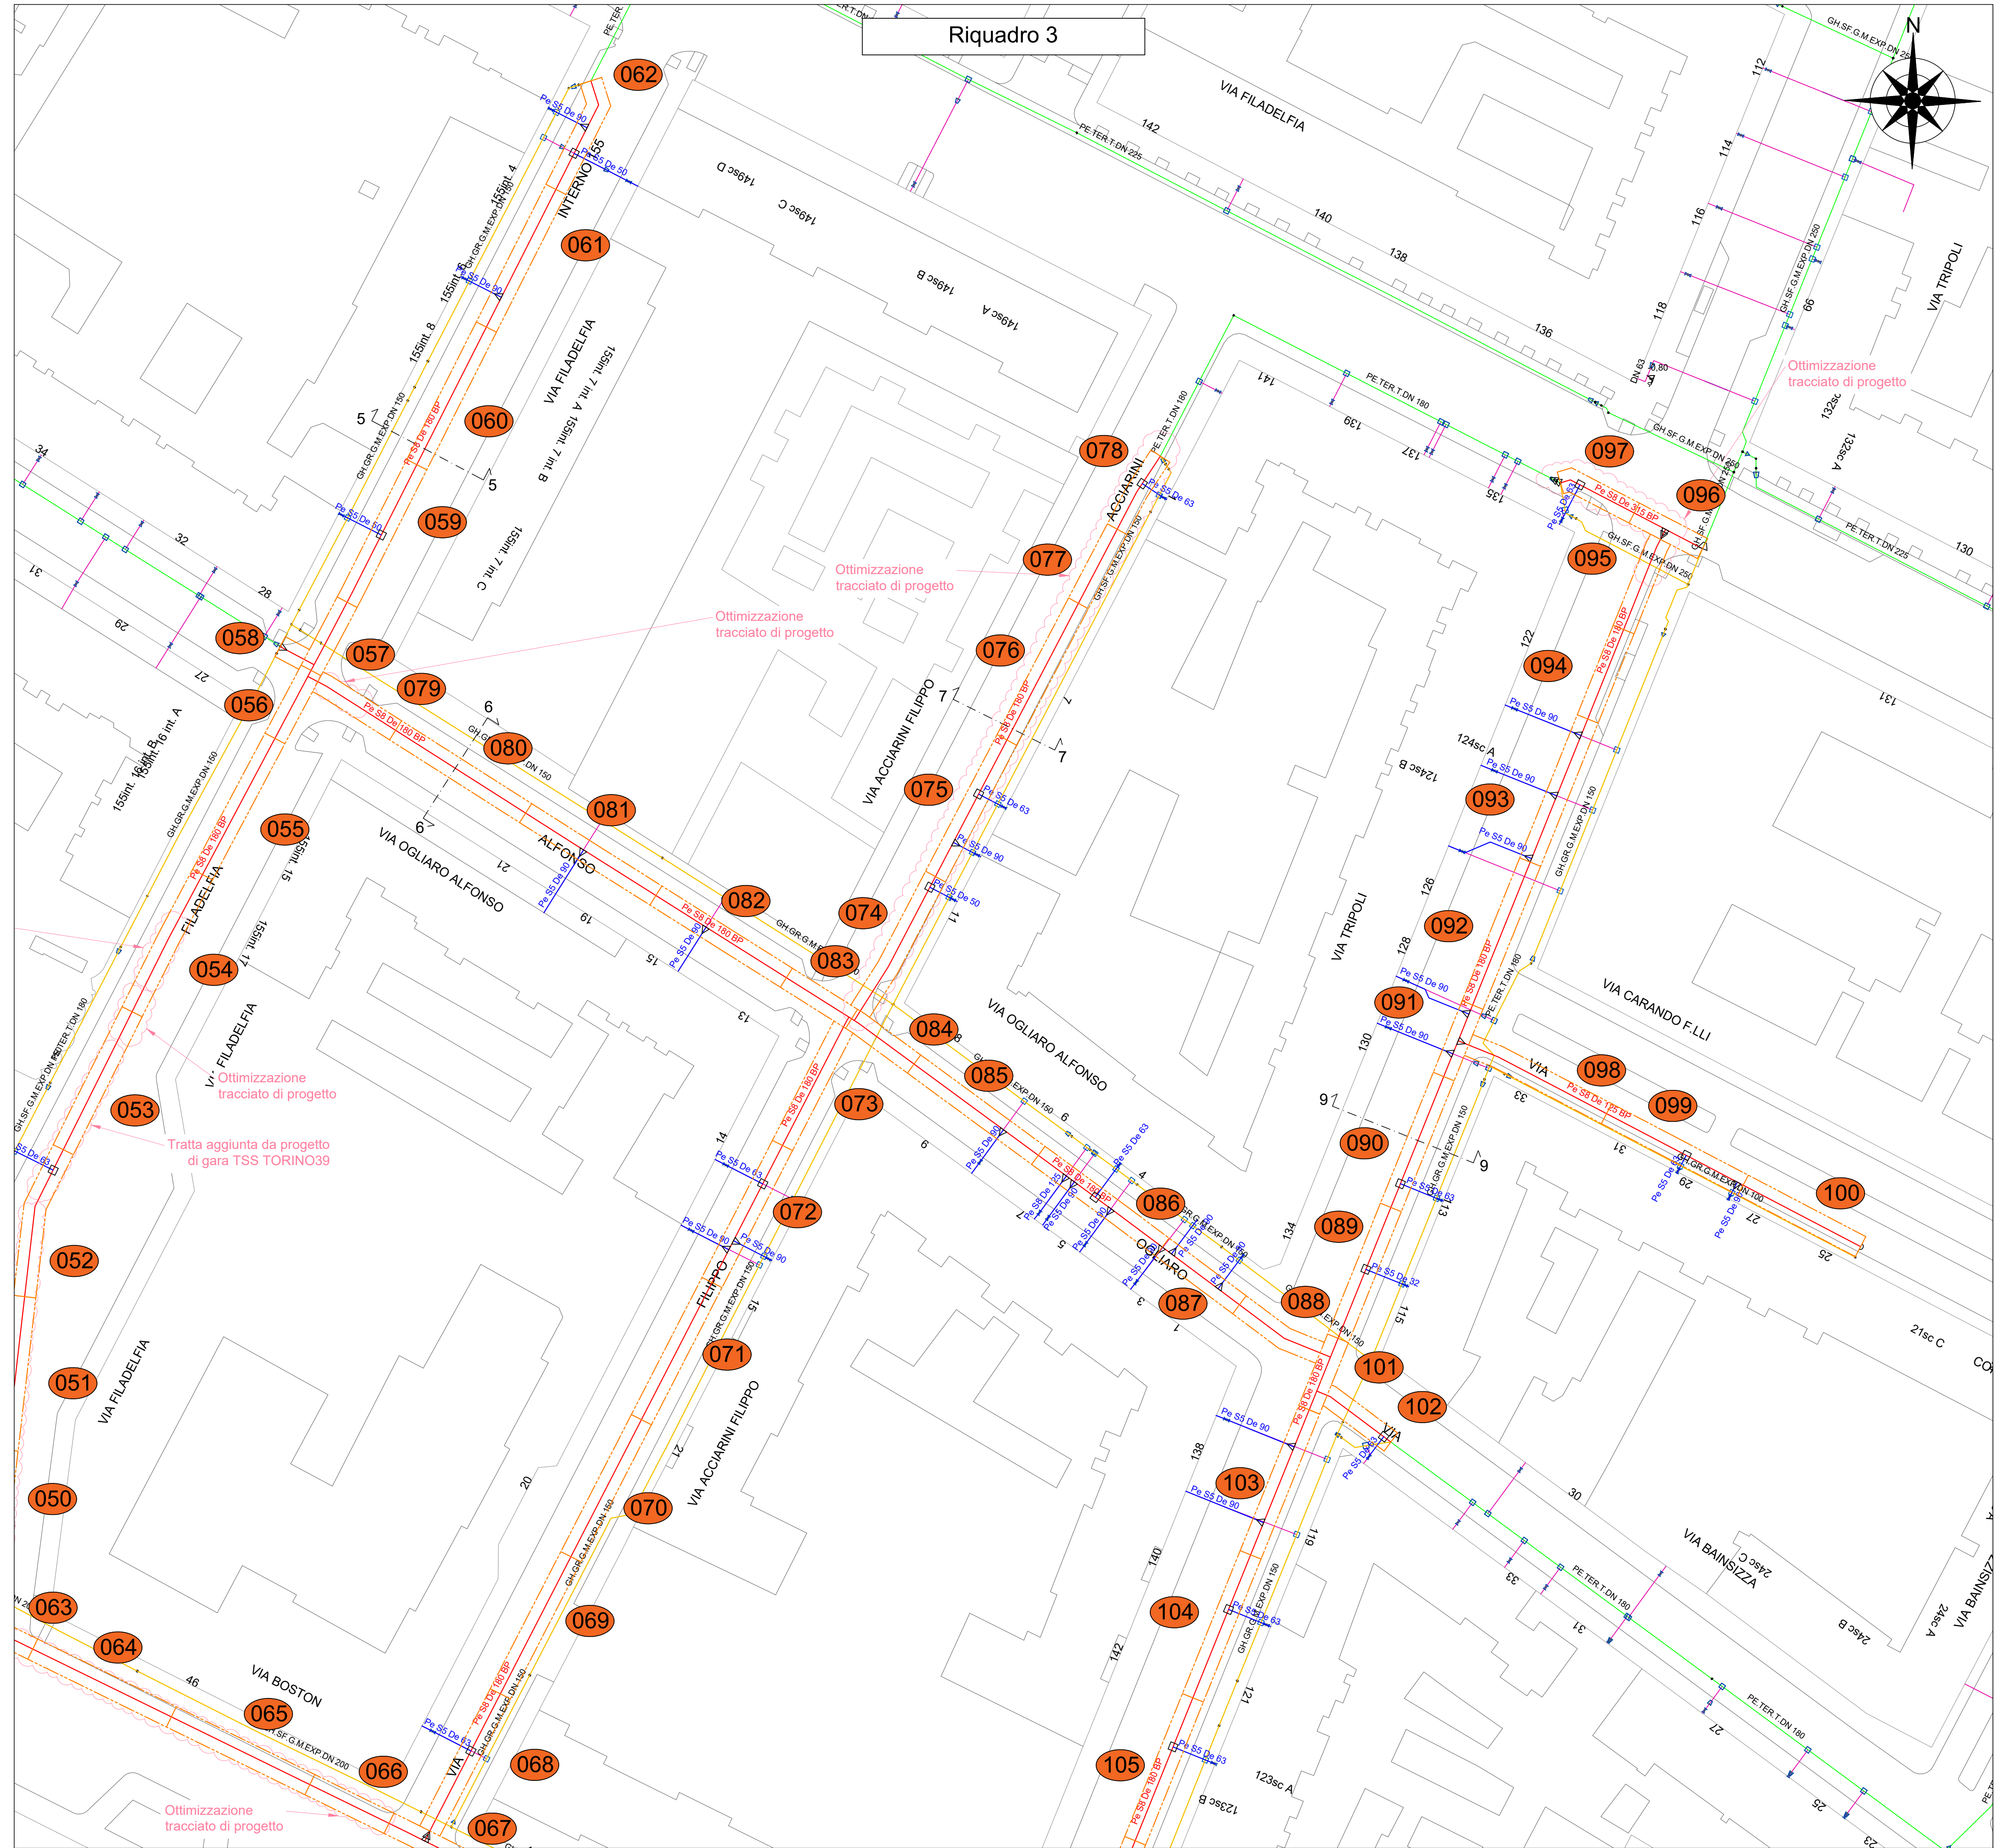

LEGENDA	
Rete in progetto BP	Zona di lavoro
Rete da rimuovere BP	n° Zona di lavoro

		Progettista: Alessandro Leardi Ing. n° 1701		Unità Responsabile della Progettazione INGEREAL-INGE-PROGRE	
Progetto n°: 22-0320-3E-00-001272 WBS: SI.20.10300.02.1109 ALLEGATO n°: 10.2		Descrizione:			
Nome File: 01.13.mxd		Descrizione:			
Formato: A1 Scala 1 : 500		Emissione per commenti			
Comm.: 2464		Rev.			
Comittente:		Comune di TORINO Via Varie			
		Progetto Esecutivo SOSTITUZIONE RETE IN BP (L=2504.78 m) GARA ATEM TO1 Intervento n° SI-036213-001272-TSS-TORIN036 Layout di cantiere - Tavola 2			

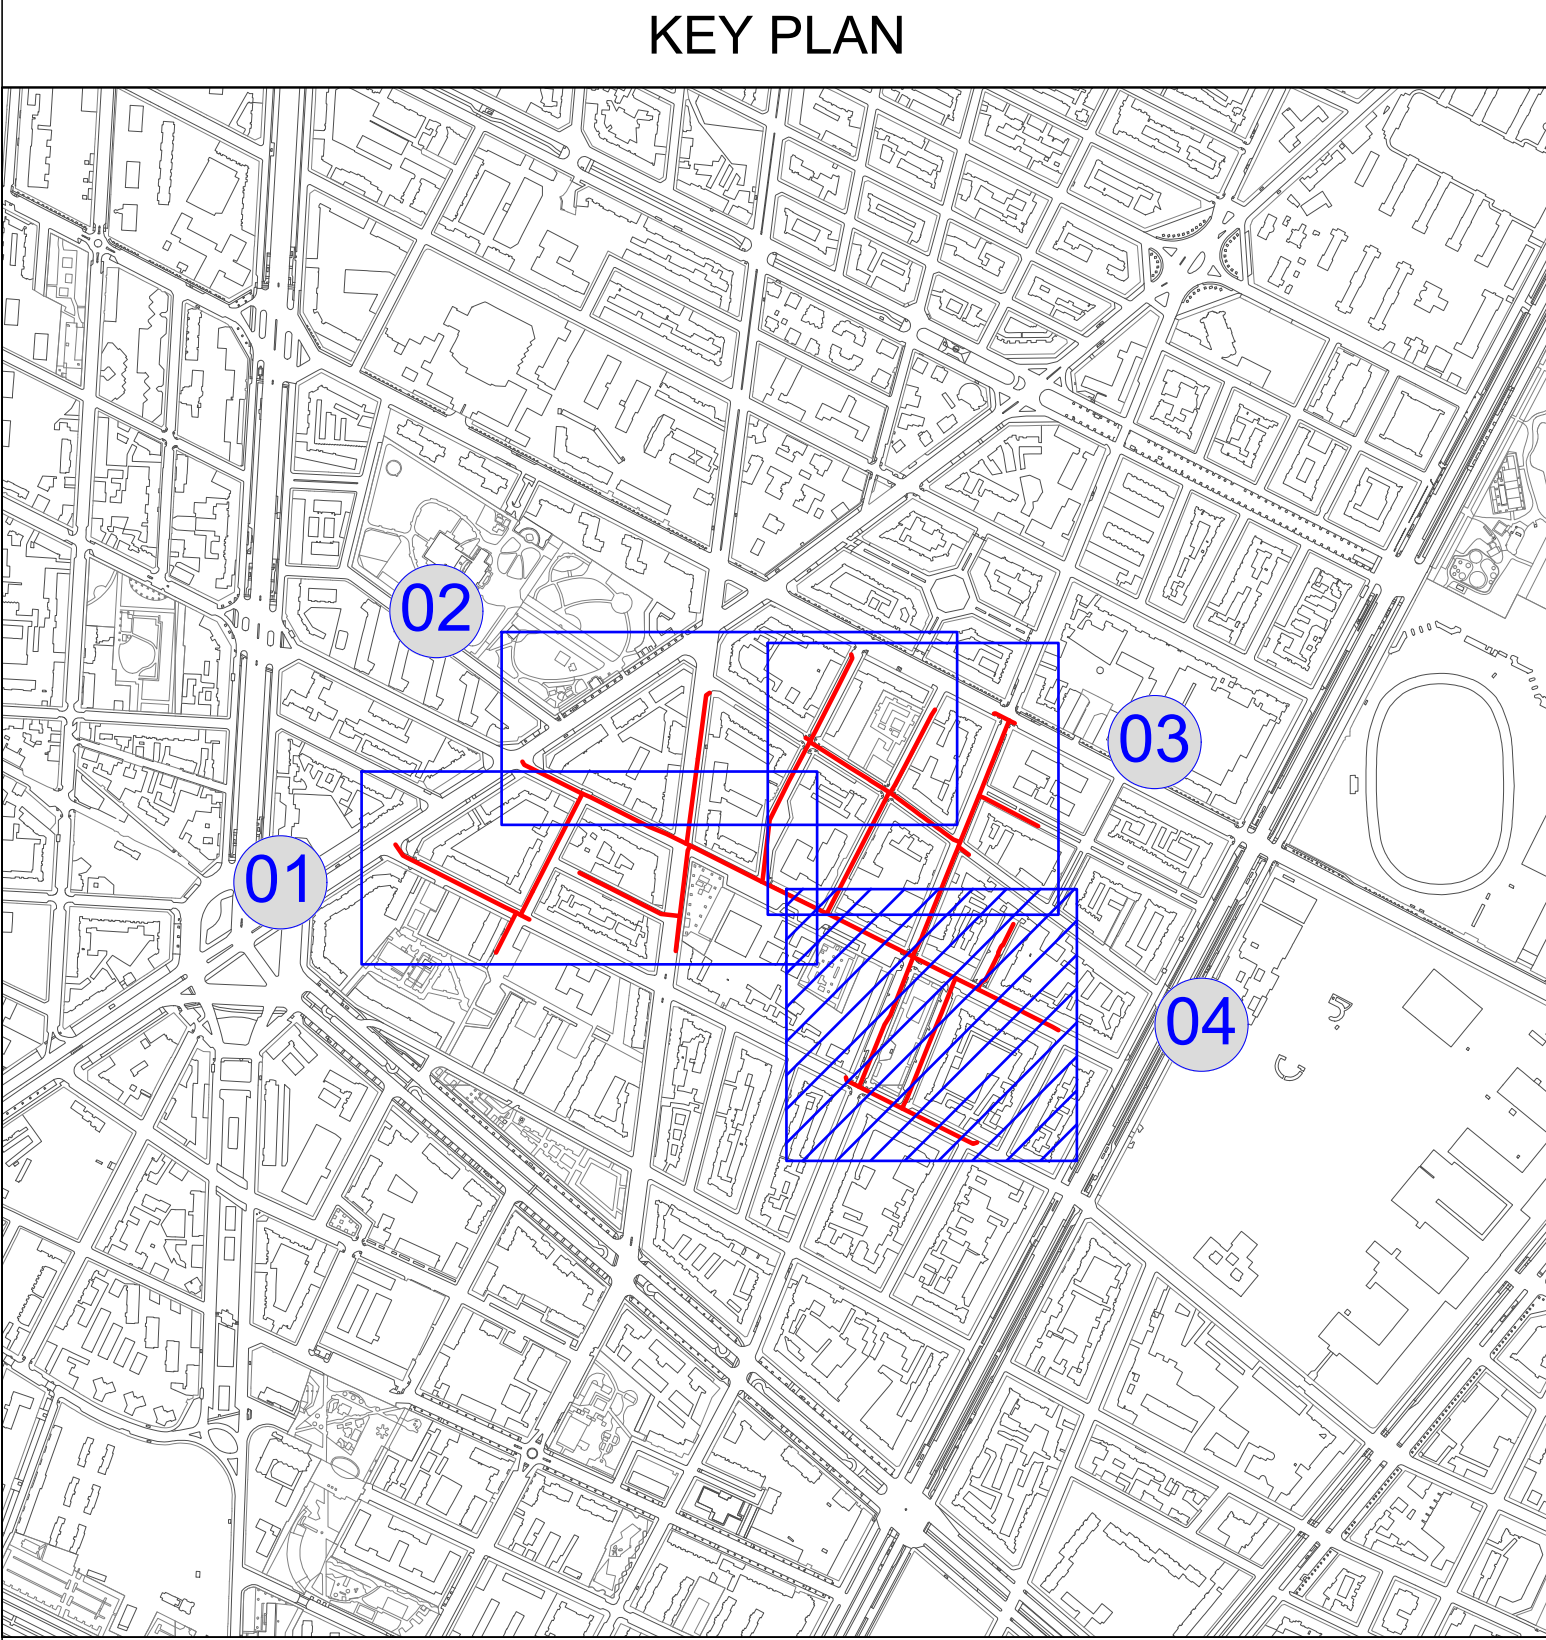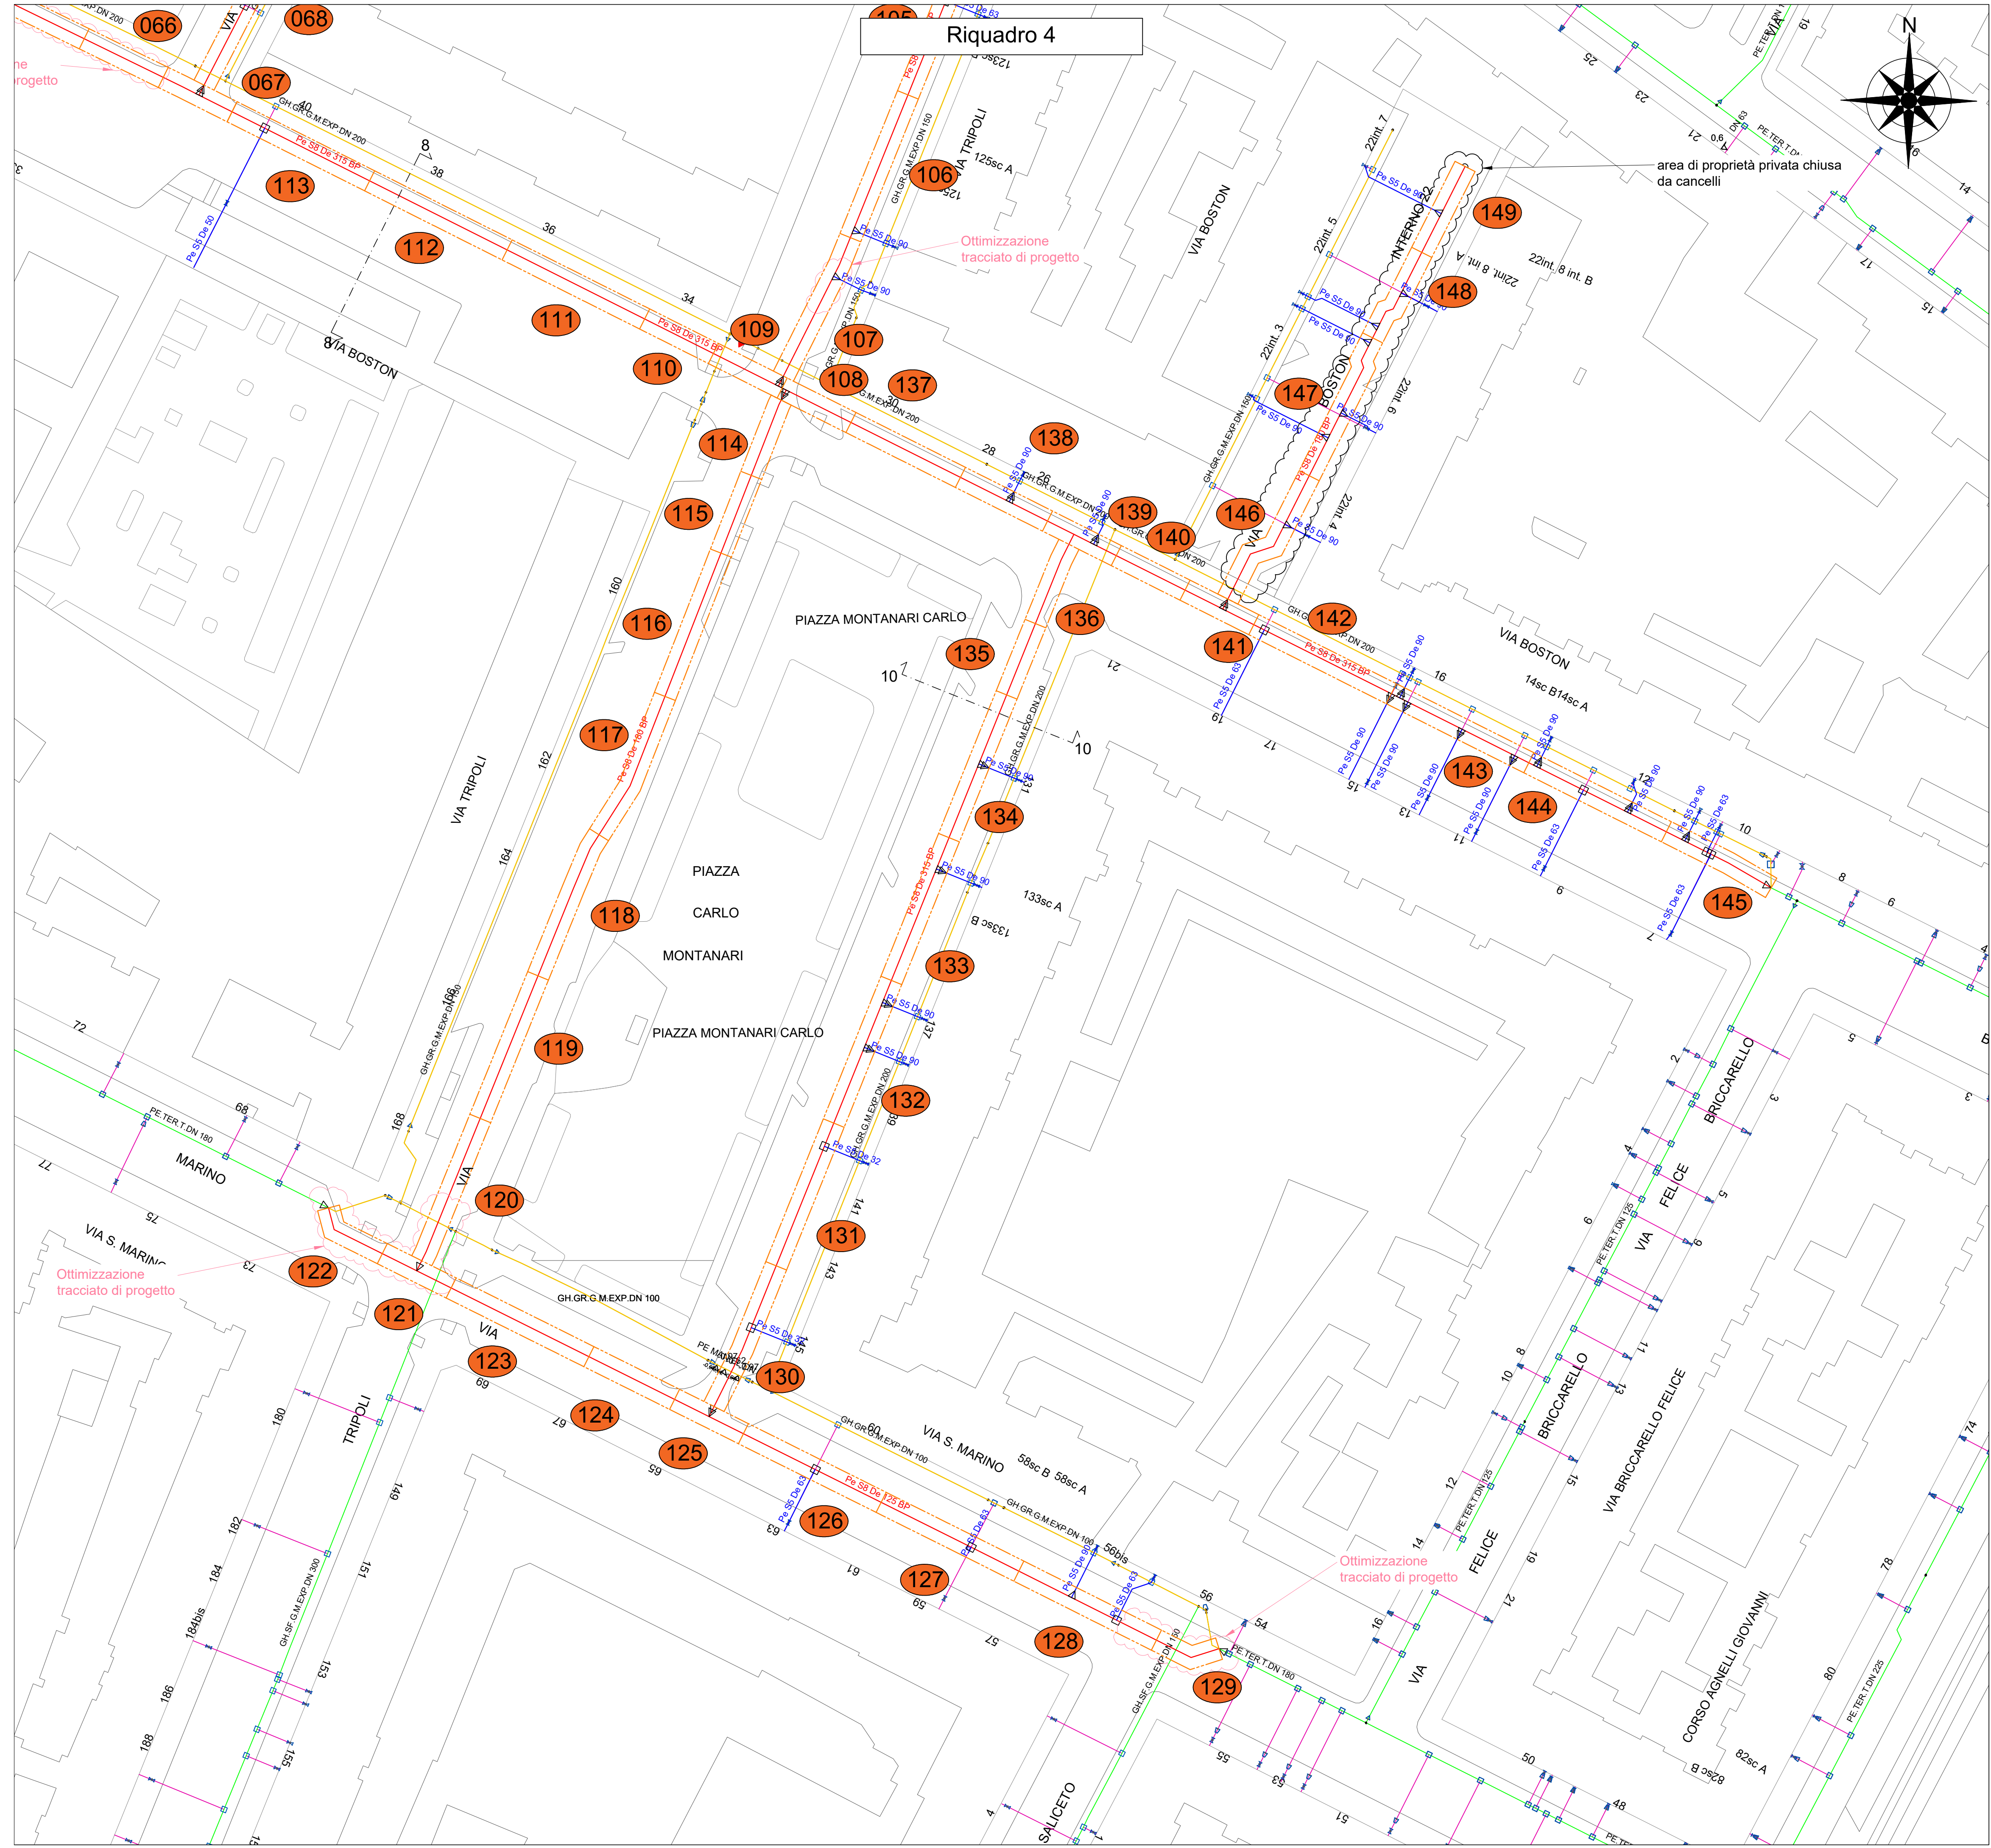

LEGENDA	
— Rete in progetto BP	001 Zona di lavoro
— Rete da rimuovere BP	001 n° Zona di lavoro

Progetto n°:
22-0320-3E-00-001272
WBS:
SI.20.10300.02.1109
ALLEGATO n°: 10.3
Nome File: 20.10.1109
Formato: A1 Scala: 1 : 500
Committente:

Unità Responsabile della Progettazione
INGEREAL-INGE-PROGRE

Descrizione:	0	04	11	22	L.Tosonotti	L.Carlasegna	A.Leardi
Descrizione:	0	04	11	22	L.Tosonotti	L.Carlasegna	A.Leardi
Com.: 2464	Rev.	G.	M.	A.	Redatto	Controllato	Approvato


Comune di
TORINO
Vie Varie
Progetto Esecutivo
SOSTITUZIONE RETE IN BP (L=2504.78 m) GARA ATEM TO1
Intervento n° SI-036213-001272-TSS-TORIN036
Layout di cantiere - Tavola 3

Elenco aree, tipologia layout e lunghezza cantiere		
n. area	n. layout	lunghezza [m]
1	82	20
2	85	24
3	85	24
4	85	24
5	85	24
6	85	24
7	82	14
8	82	14
9	85	24
10	85	21
11	85	24
12	85	24
13	85	24
14	85	24
15	85	24
16	82	20
17	82	14
18	82	24
19	85	24
20	82	17
21	82	12
22	85	24
23	85	24
24	85	24
25	82	24
26	82	14
27	82	14
28	82	24
29	85	24
30	85	24
31	82	14
32	85	14
33	85	13
34	82	24
35	85	24
36	85	24
37	85	24
38	85	19
39	82	24
40	85	24
41	85	24
42	85	24
43	85	24
44	85	24
45	82	17
46	85	24
47	85	24
48	82	24
49	82	13
50	85	13
51	85	24
52	85	24
53	85	24
54	85	24
55	85	24
56	82	14
57	82	14
58	82	4
59	85	24
60	85	24
61	85	24
62	85	19
63	82	14
64	85	24
65	85	24
66	82	14
67	82	14
68	82	24
69	85	24
70	85	24
71	85	24
72	85	24
73	82	21
74	82	24
75	85	24
76	85	24
77	85	13
78	85	14
79	82	14
80	85	24
81	85	24
82	85	24
83	82	14
84	82	14
85	85	24











Elenco aree, tipologia layout e lunghezza cantiere		
n. area	n. layout	lunghezza [m]
86	85	24
87	85	15
88	82	15
89	82	22
90	85	22
91	82	14
92	82	24
93	85	24
94	85	15
95	82	15
96	82	14
97	82	13
98	82	24
99	85	24
100	85	21
101	82	16
102	82	12
103	82	24
104	85	24
105	85	24
106	85	24
107	82	24
108	82	14
109	82	14
110	85	12
111	85	24
112	85	24
113	85	24
114	82	13
115	85	13
116	85	24
117	85	24
118	85	24
119	85	24
120	82	24
121	82	14
122	82	12
123	82	24
124	82	15
125	82	14
126	85	24
127	85	24
128	82	24
129	82	11
130	82	24
131	85	24
132	85	24
133	85	24
134	85	24
135	85	12
136	82	13
137	85	19
138	82	15
139	82	14
140	82	12
141	82	14
142	82	24
143	85	24
144	85	24
145	85	19
146	S1 - proprietà privata	24
147	S1 - proprietà privata	24
148	S1 - proprietà privata	16
149	S1 - proprietà privata	15

	Progettista:	Unità Responsabile della Progettazione								
	Ordine degli Ingegneri di Alessandria	INGEREAL-INGE-PROGRE								
	Progetto n°: 22-0320-3E-00-001272 WBS: SI.20.I0300.02.1109 ALLEGATO n°: 10.4									
	Nome File: AL10.dwg									
Formato: A2	Scala 1 : -	Emissione per commenti		0	04	11	22	L.Tosonotti	L.Cartasegna	A.Leardi
Committente		Comm. : 2464		Rev.	G.	M.	A.	Redatto	Controllato	Approvato
		Comune di TORINO Vie Varie Progetto Esecutivo SOSTITUZIONE RETE IN BP (L=2504,78 m) GARA ATEM TO1 Intervento n° SI-036213-001272-TSS-TORIN036 Layout di Cantiere - Tavola 4								

Il presente elaborato è di proprietà aziendale - La società tutelerà i propri diritti a termini di legge.

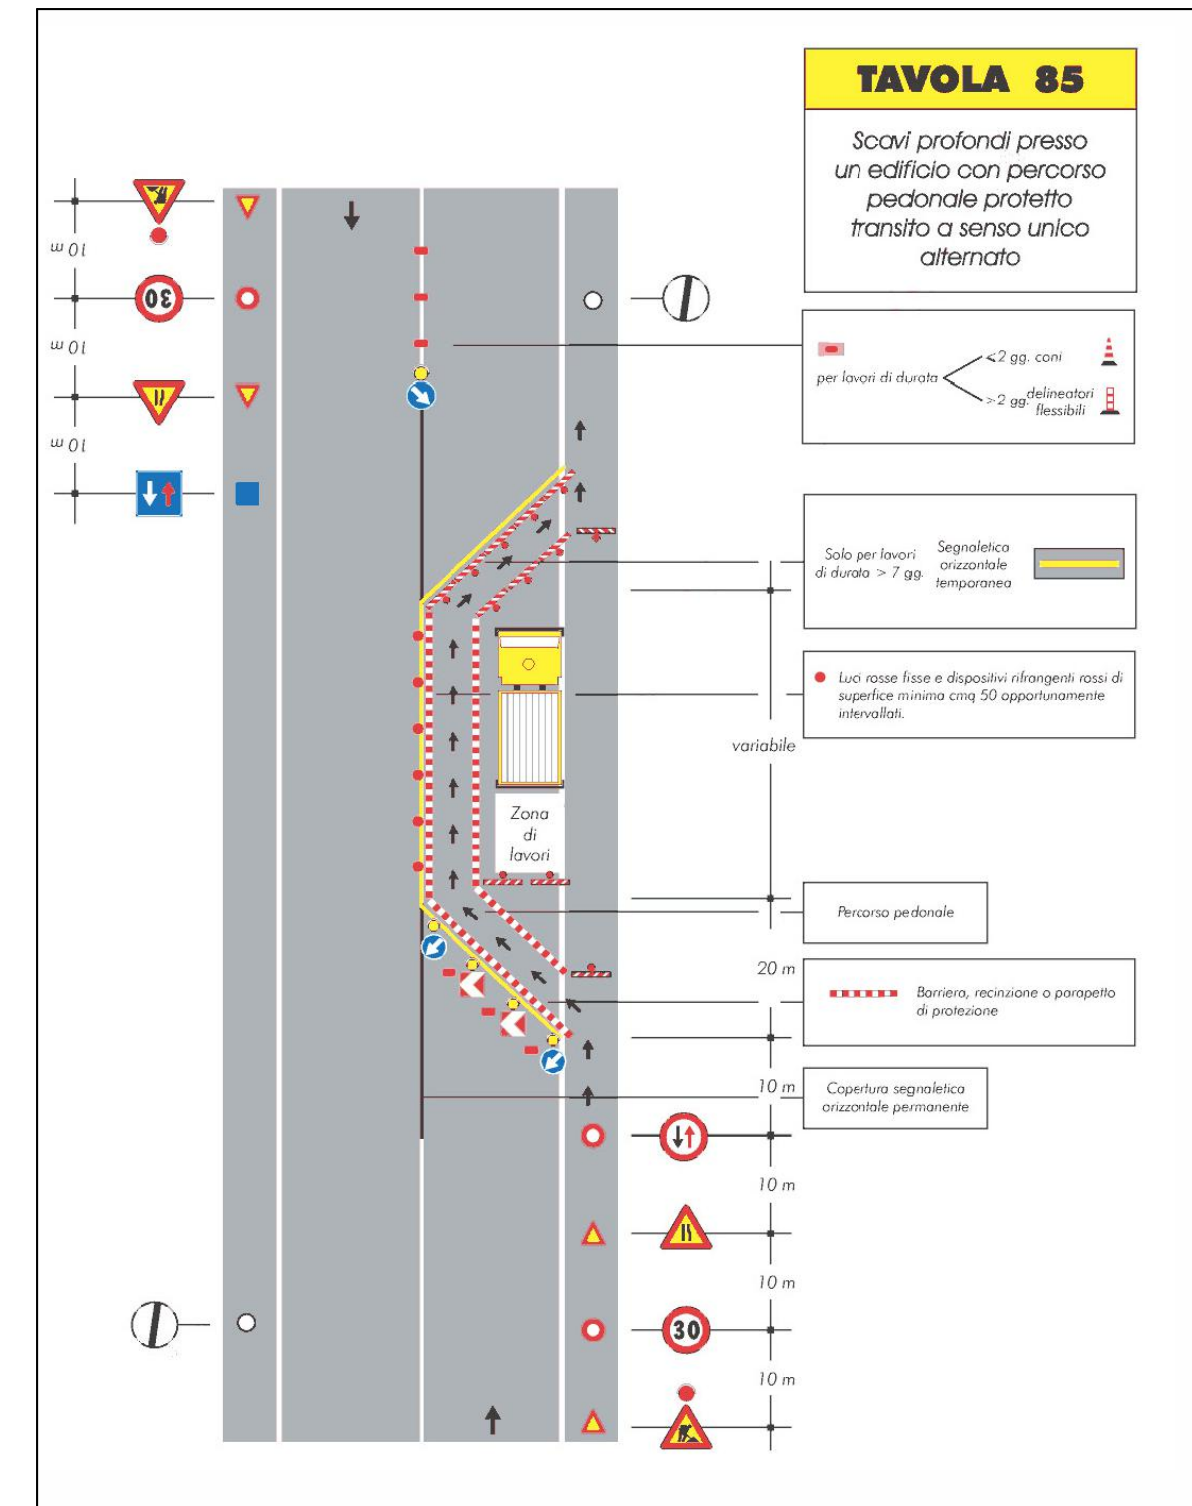

		Progetto: Alessandro Leardi Ordine degli Ingegneri di Alessandria matricola n° 149101		Unità Responsabile della Progettazione INGEGREAL-INGE-PROGRE						
Progetto n°: 22-0320-3E-00-001272 WBS: SI.20.I0300.02.1109 ALLEGATO n°: 10.5		Descrizione: Descrizione: Emissione per commenti		0	04	11	22	L.Tosonotti	L.Cartasegna	A.Leardi
Nome File: All.10.dwg Formato: A2 Scala 1 : -		Comm. : 2464		Rev.	G.	M.	A.	Redatto	Controllato	Approvato
Committente 		Comune di TORINO Vie Varie Progetto Esecutivo SOSTITUZIONE RETE IN BP (L=2504,78 m) GARA ATEM TO1 Intervento n° SI-036213-001272-TSS-TORIN036 Layout di Cantiere - Tavola 5								

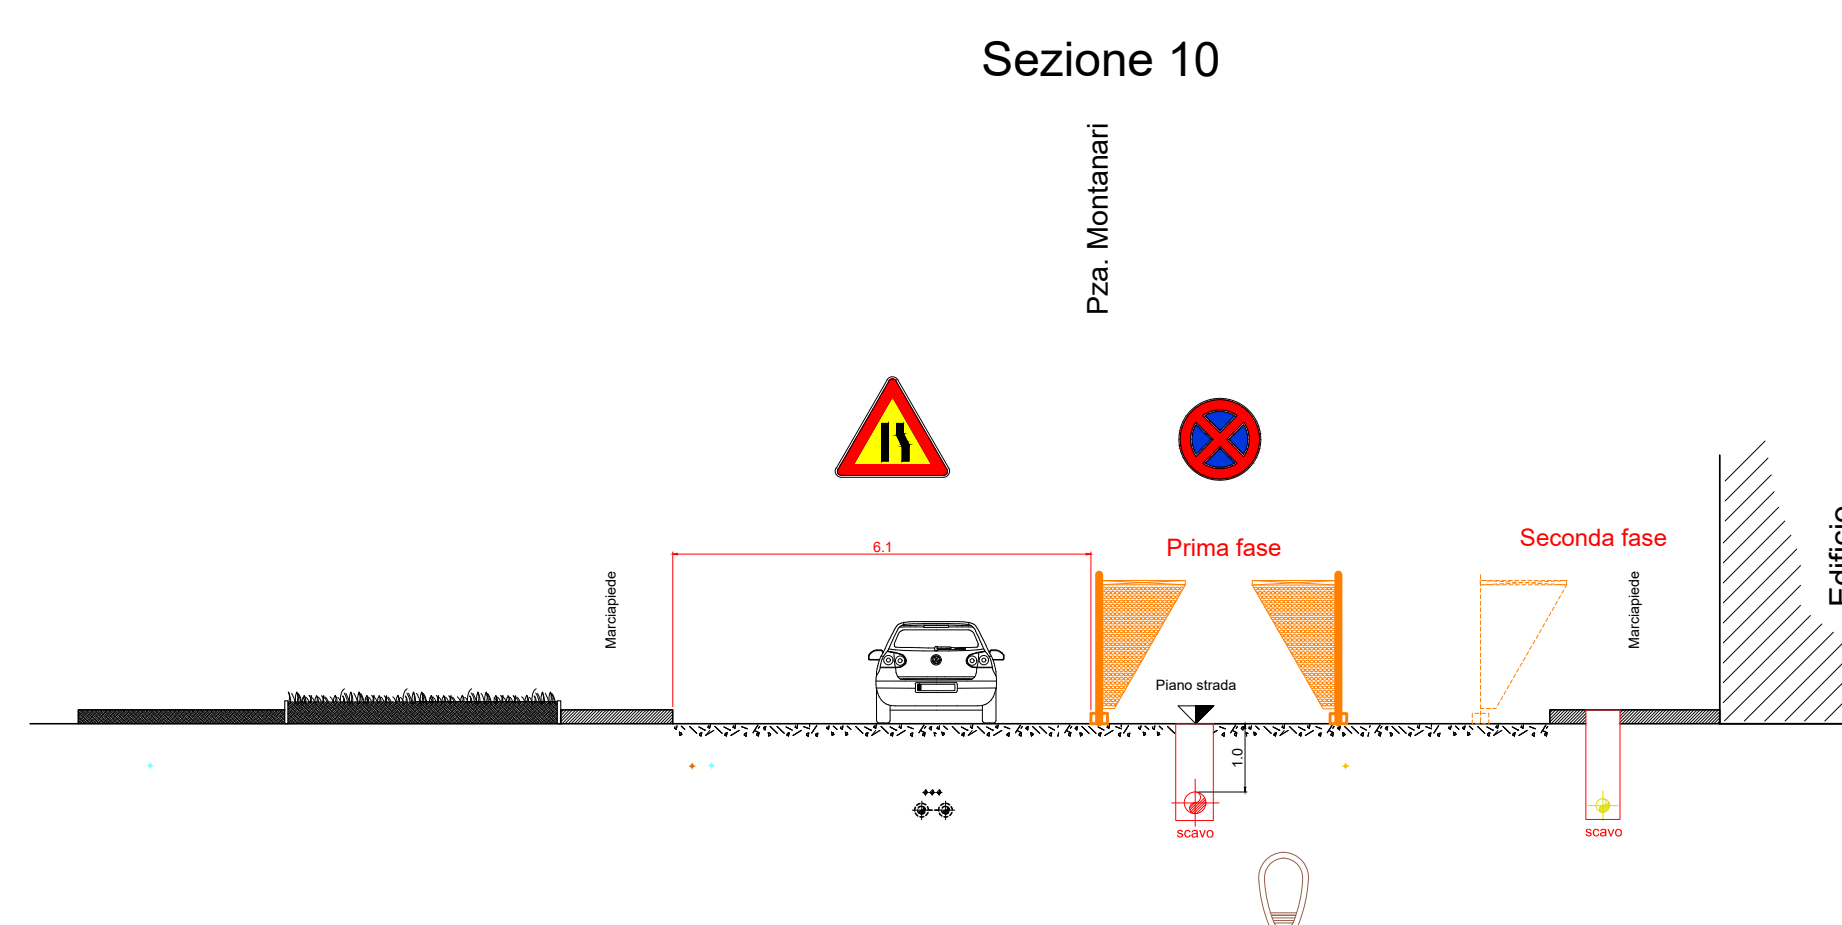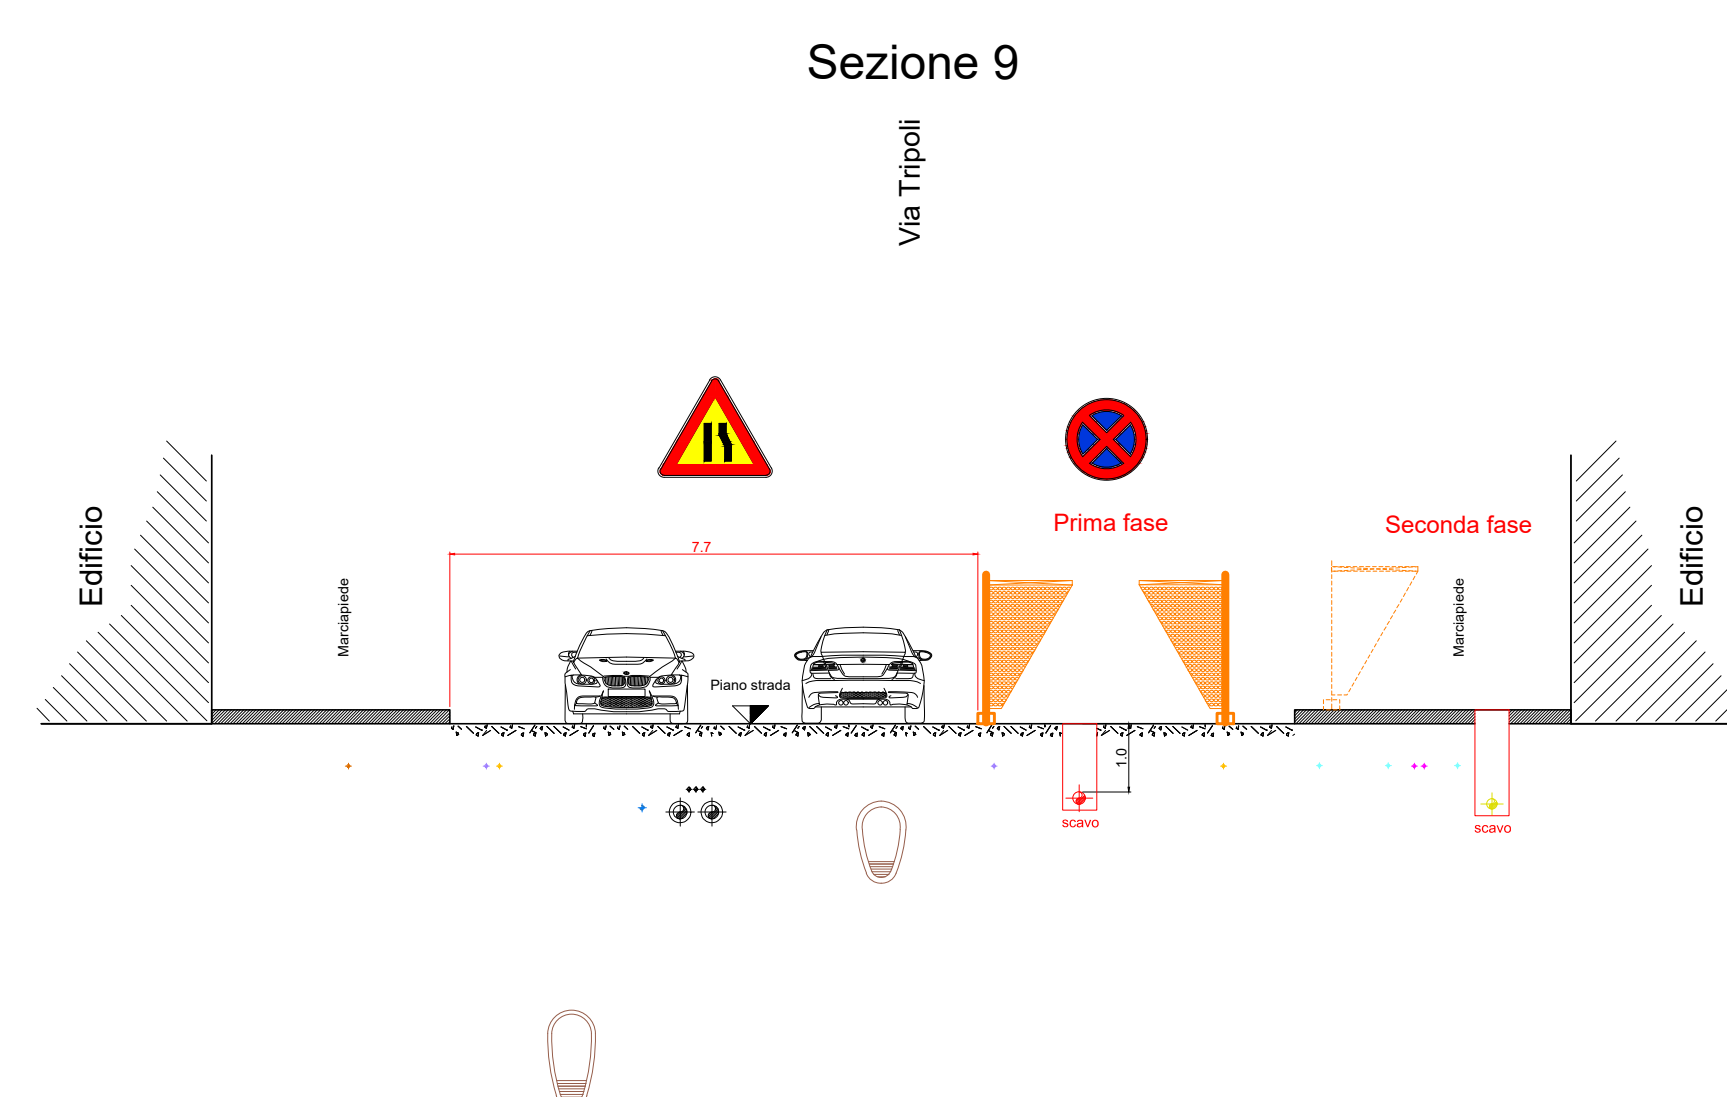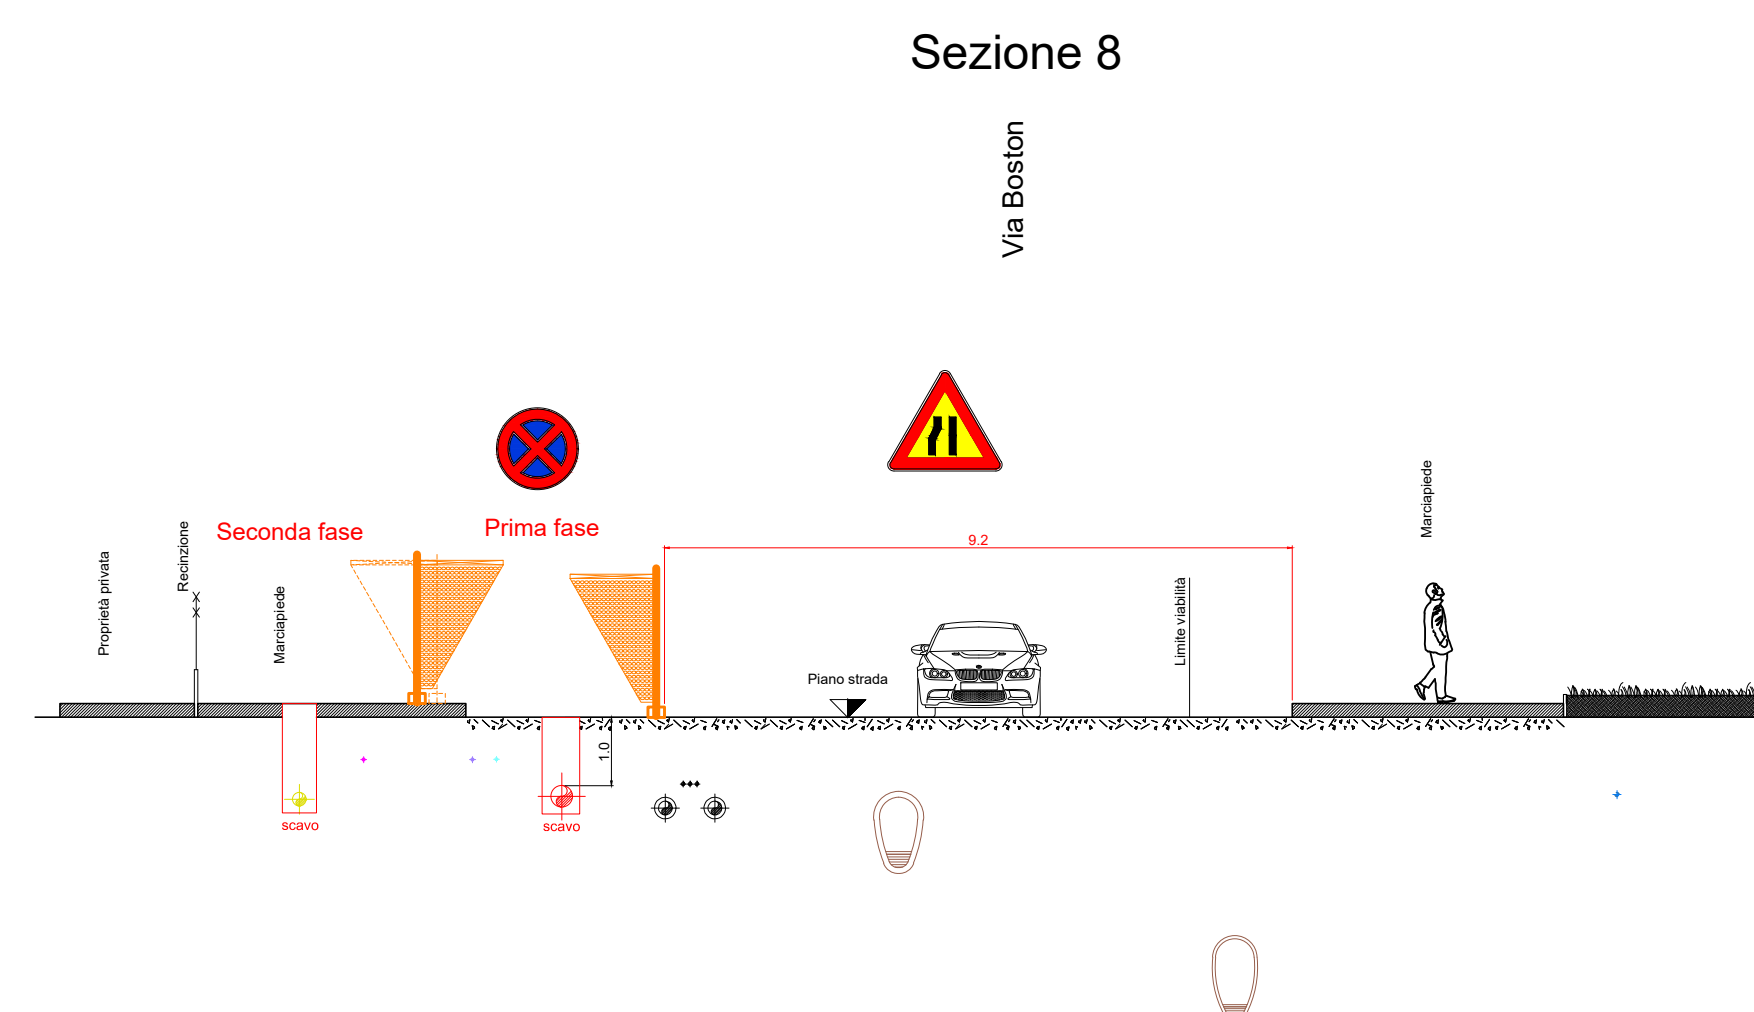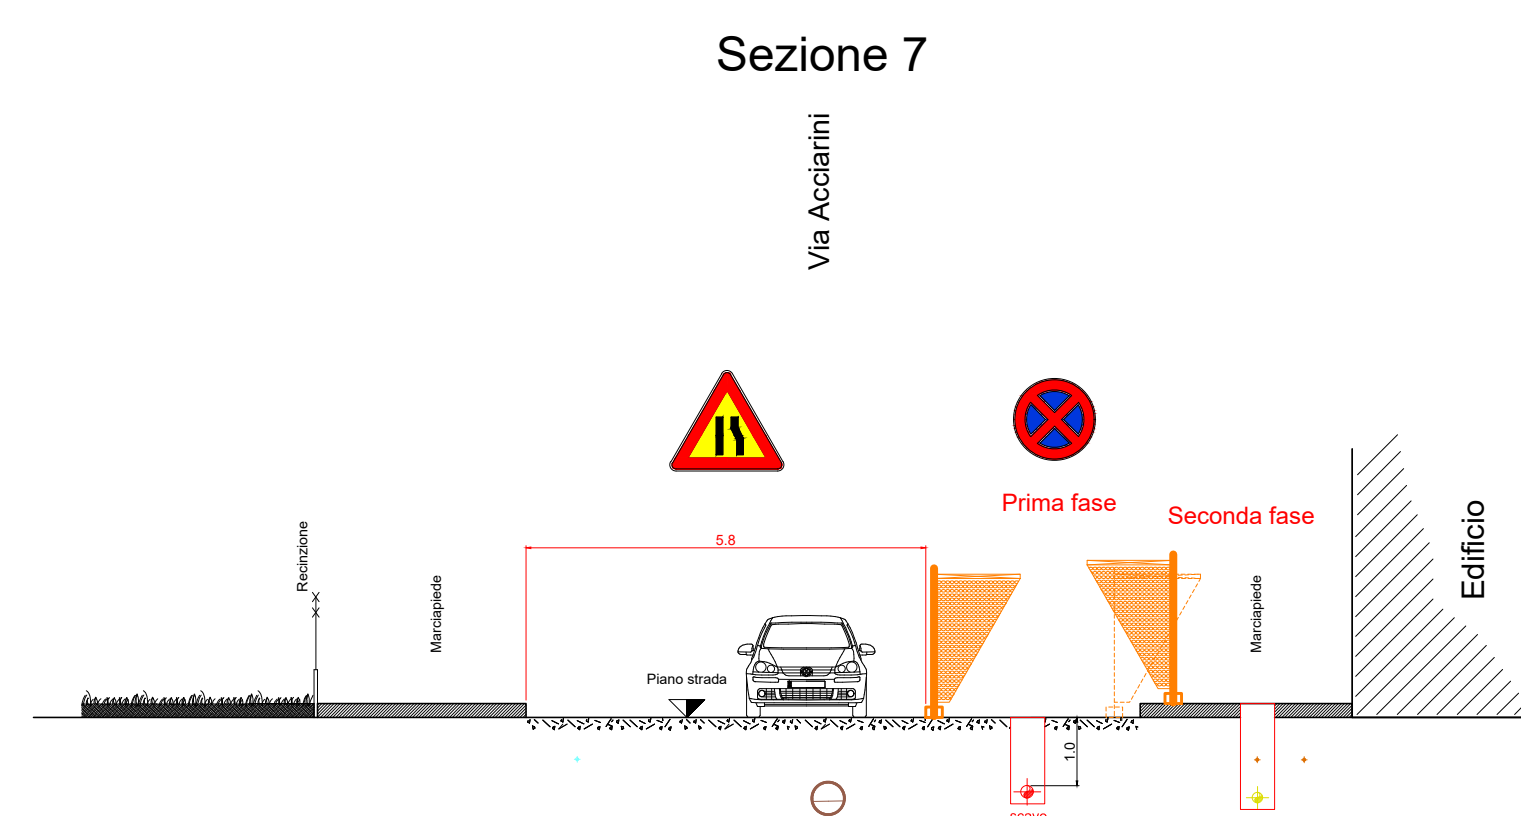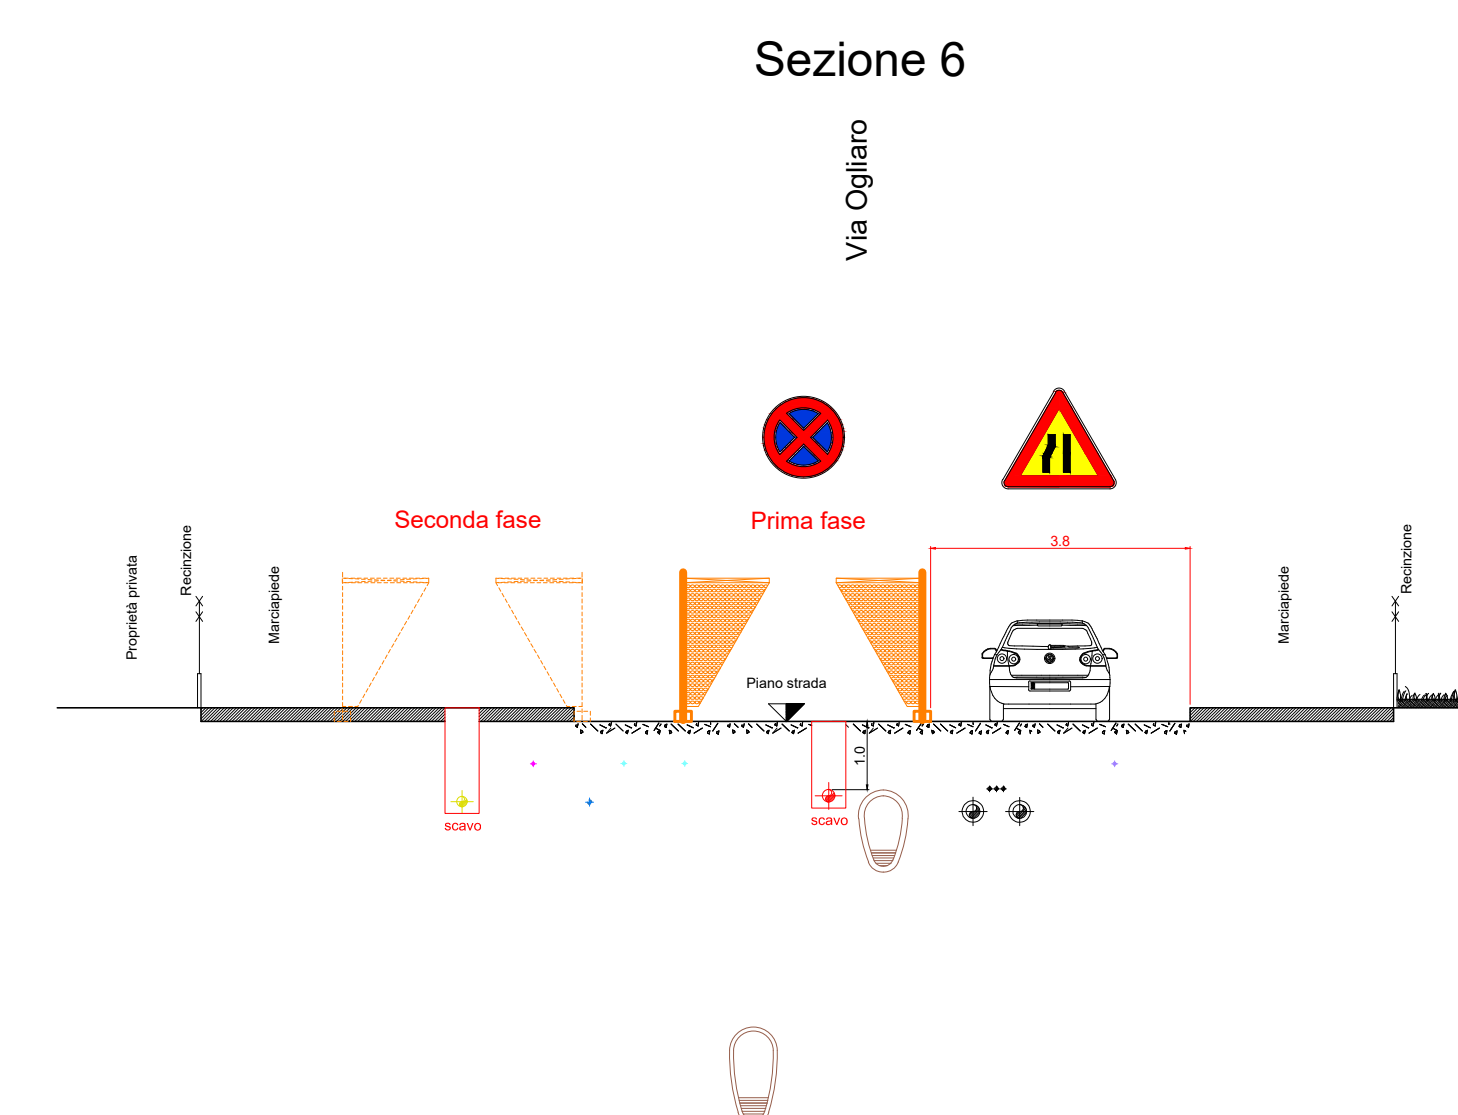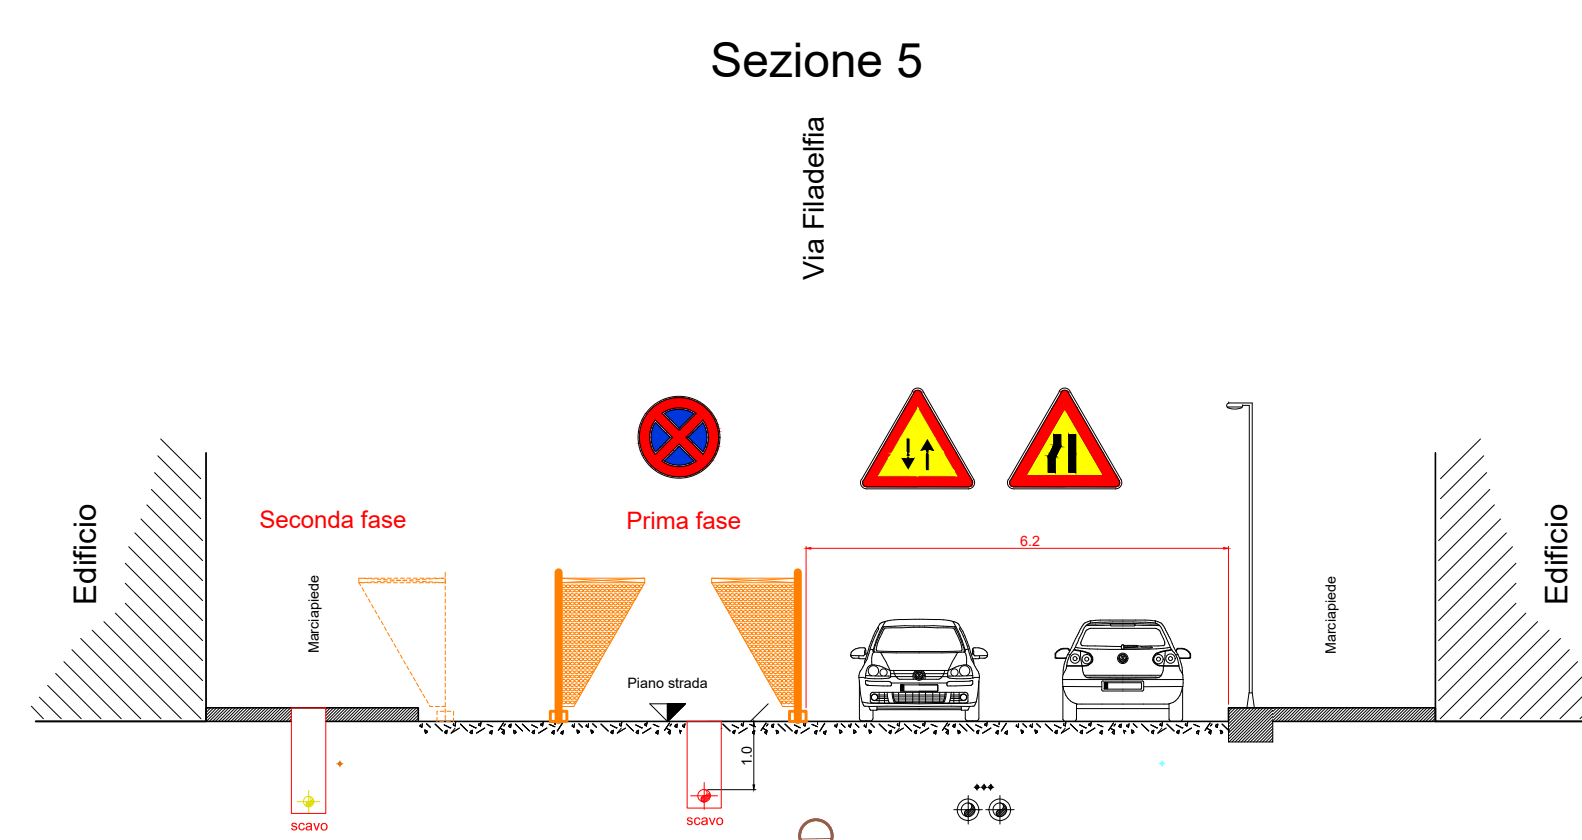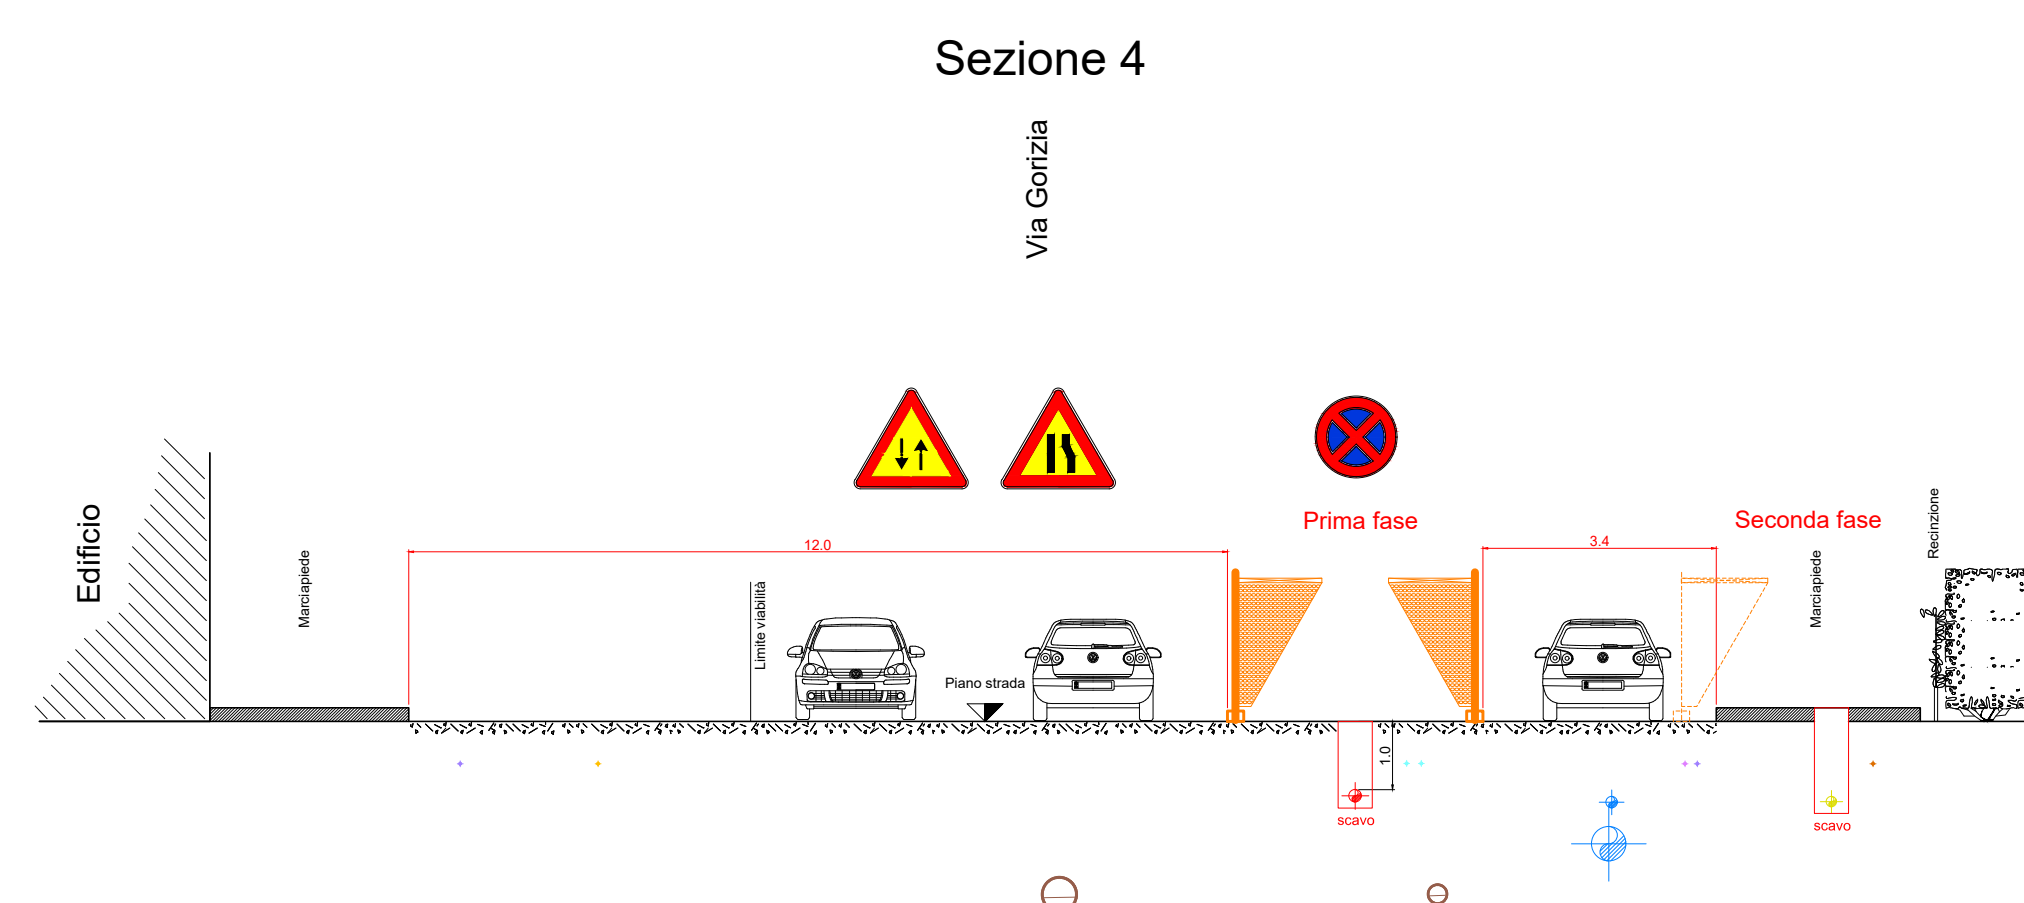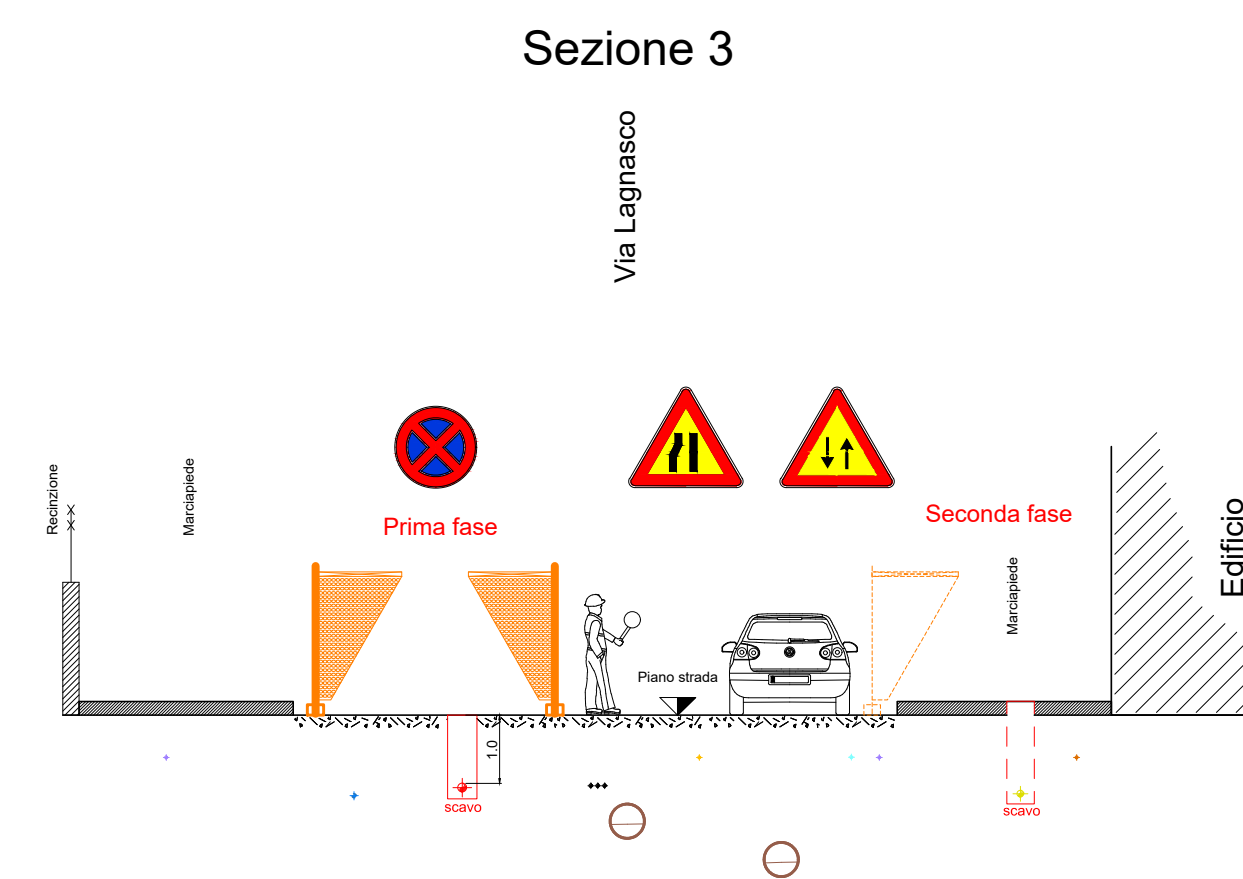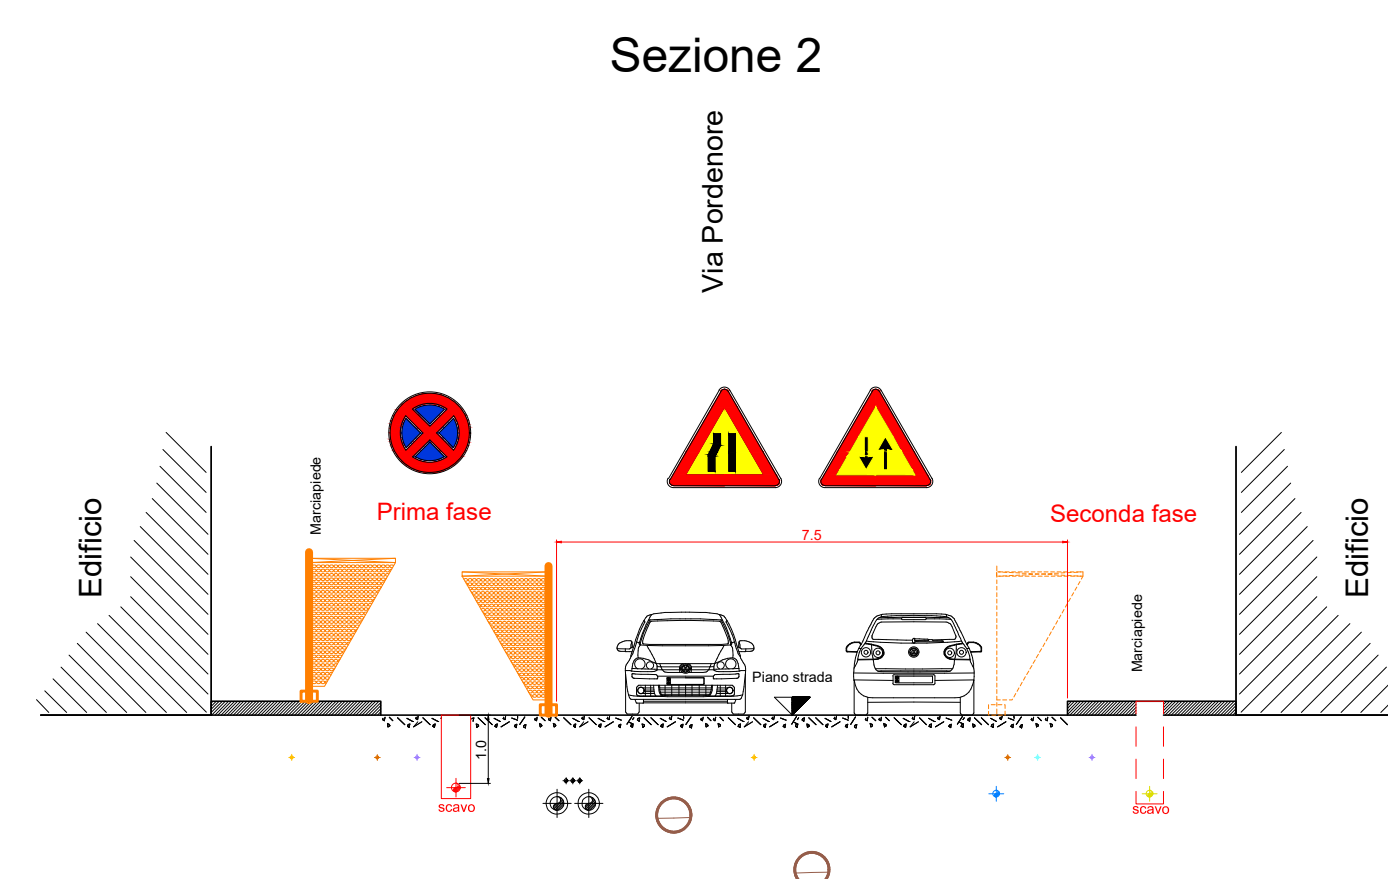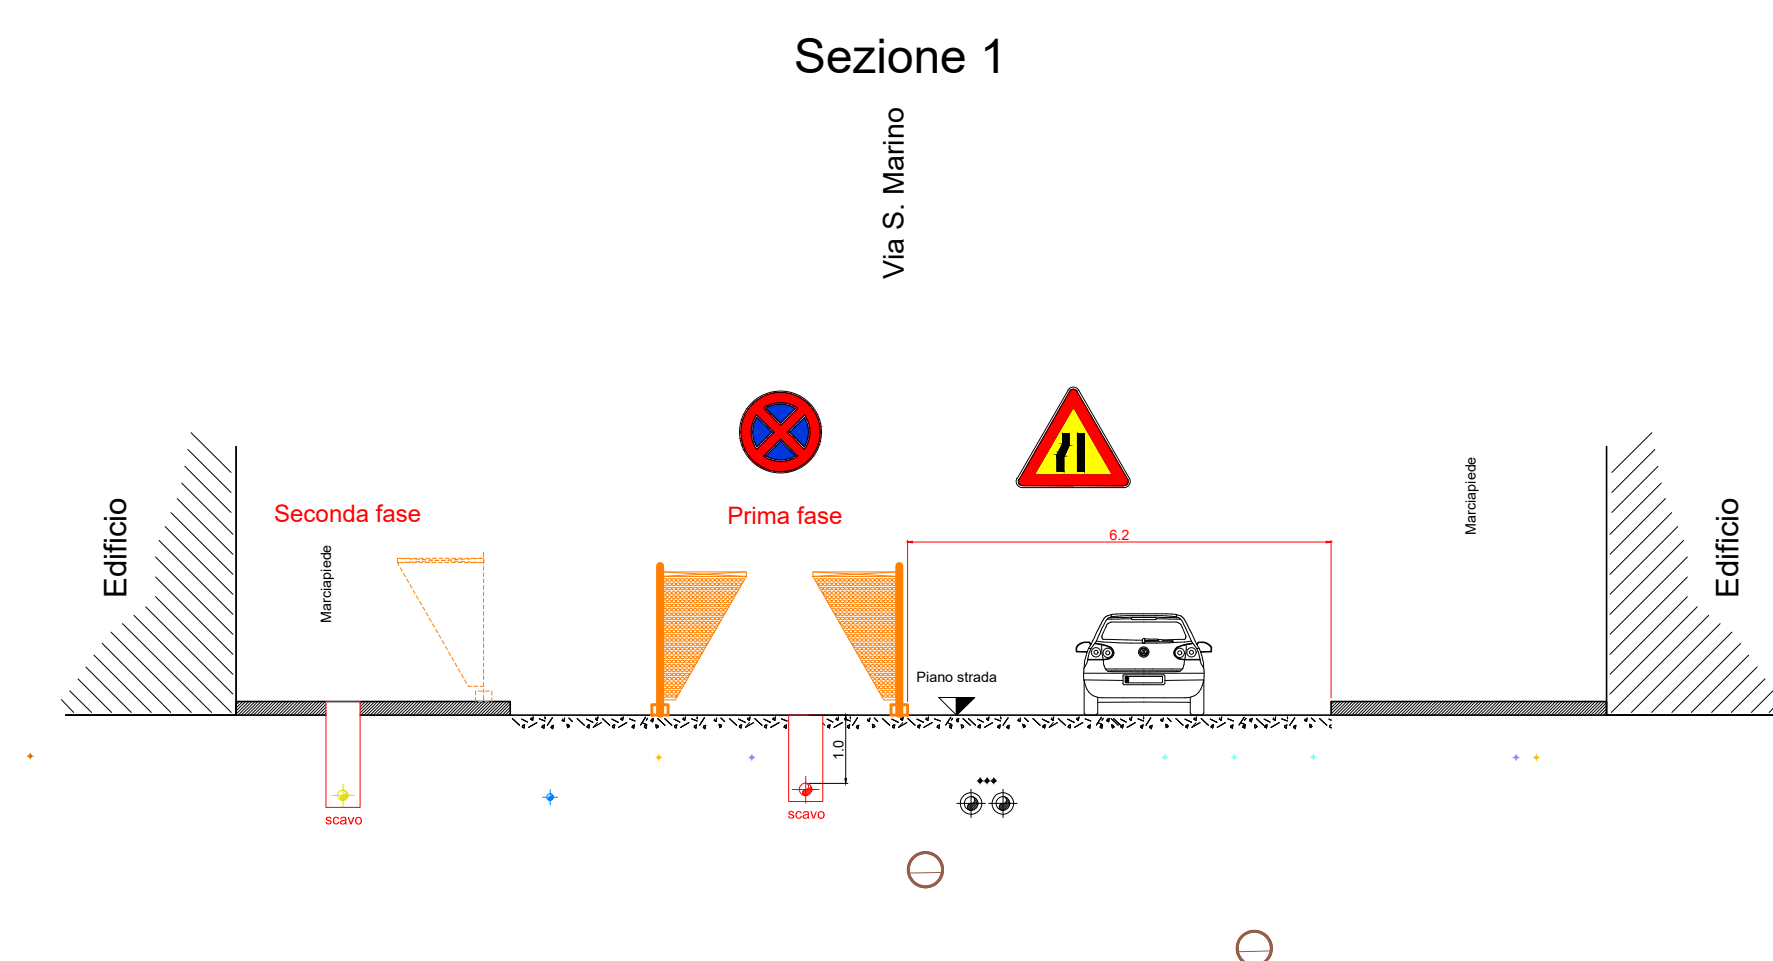

NOTE:

- Prima dell'inizio dei lavori dovranno essere accertati con scavi a mano, alla presenza dei tecnici interessati, natura e posizione dei sottoservizi, che potranno comportare variazioni dello sviluppo piano/altimetrico del tracciato della tubazione gas in progetto.
- Le misure riportate sono in metri.

[illegible]