


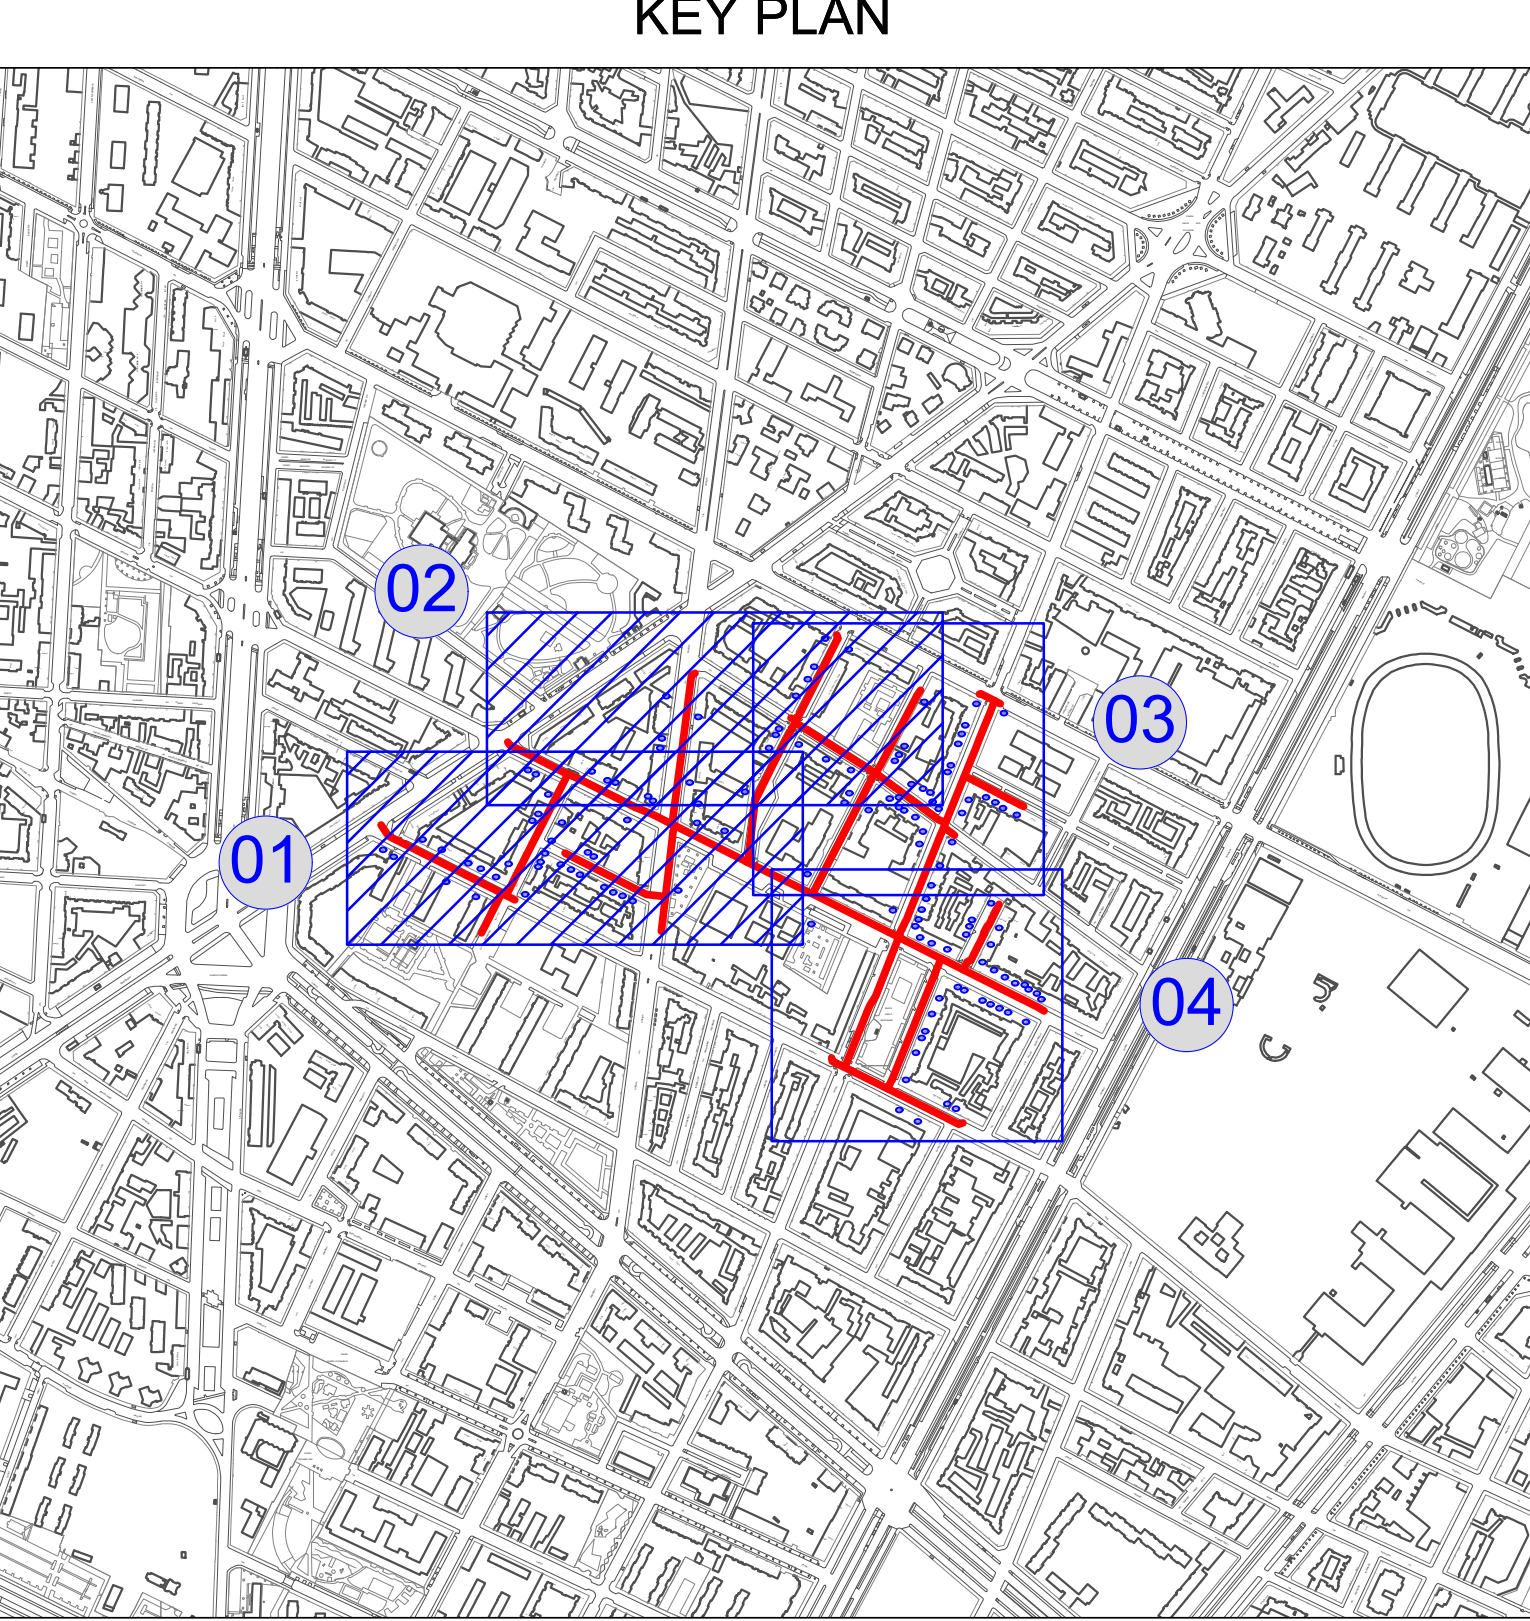

LEGENDA

— Rete in progetto BP
— Tubazione I.D.U. esistente
— Rete da rimuovere
— Tubazione I.D.U. in progetto

□ Organo di presa

001 Numero I.D.U. in progetto

n.	Posizione	Tipologico	diametro esistente Acc DN	Pe De	diametro di progetto Acc DN	Pe De	lunghezza (L) [m]	Δ H [m]	L privata >12m [m]
1	Via San Martino civ. 123						90	12,00	
2	Via San Martino civ. 123						90	12,00	
3	Via San Martino civ. 120						63	8,50	
4	Via San Martino civ. 120						63	8,50	
5	Via San Martino civ. 129						90	12,00	
6	Via San Martino civ. 118						63	8,50	
7	Via San Martino civ. 116						63	8,50	
8	Via San Martino civ. 119						50	12,00	
9	Via San Martino civ. 144						90	8,50	
10	Via Pordenone civ. 13						50	11,00	
11	Via Pordenone civ. 15						90	3,50	
12	Via Pordenone civ. 13						63	12,00	
13	Via Pordenone civ. 13						50	12,00	
14	Via Pordenone civ. 13						50	11,00	
15	Via Pordenone civ. 7						50	11,00	
16	Via Pordenone civ. 8						90	3,50	
17	Via Pordenone civ. 6						63	3,50	
18	Via Pordenone civ. 5						63	11,00	
19	Via Pordenone civ. 6						50	3,50	
20	Via Boston civ. 73	4	100				125	11,00	
21	Via Boston civ. 73	4	50				63	11,00	
22	Via Boston civ. 76	3	75				90	8,00	
23	Via Boston civ. 72	1			63		63	8,00	
24	Via Boston civ. 72	3	40				50	7,00	
25	Via Boston civ. 59						90	12,00	
26	Via Boston civ. 68						90	9,00	
27	Via Boston civ. 68						90	9,00	
28	Via Gorizia civ. 148/A						90	20,50	
29	Via Gorizia civ. 141	3	40				50	8,00	
30	Via Gorizia civ. 152						50	17,00	
31	Via Gorizia civ. 150	1			90		90	17,00	
32	Via Gorizia civ. 141	1			63		63	8,00	
33	Via Gorizia civ. 144	3	40				50	17,00	
34	Via Gorizia inc.	4	40				50	6,00	
35	Via Lagnasco civ. 1	3	50				63	10,00	
36	Via Lagnasco civ. 3	3	25				32	10,00	
37	Via Lagnasco civ. 3	3	80				90	10,00	
38	Via Lagnasco civ. 5	3	40				50	9,00	
39	Via Lagnasco civ. 8	4	80				90	6,00	
40	Via Lagnasco civ. 9	1			63		63	9,00	
41	Via Lagnasco civ. 10	4	80				90	6,00	
42	Via Lagnasco civ. 11	3	25				32	9,00	
43	Via Pordenone civ. 13 sc B da via Lagnasco	3	50				63	9,00	
44	Via Boston civ. 60						90	9,00	
45	Via Boston civ. 60/A						90	25,00	
46	Via Gorizia 141 sc D da via Filadelfia 155	3	50				63	10,00	
47	Via Filadelfia 155						50	7,00	
48	Via Filadelfia 155 int. 15						50	11,00	
49	Via Filadelfia 155						50	7,00	
50	Via Filadelfia 155						50	7,00	
51	Via Filadelfia 155 civ. 10/A	3	40				50	7,00	
52	Via Filadelfia 155 int. 8						90	7,00	
53	Via Filadelfia 155 civ. 6	3	75				90	7,00	
54	Via Filadelfia 155 civ. 3/A	4	40				50	11,00	
55	Via Filadelfia 155 civ. 2/D	3	75				90	7,00	
56	Via Ogliaro civ. 21	4	80				90	12,00	
57	Via Ogliaro civ. 15	4	75				90	8,00	
58	Via Acciarini civ. 11	3	40				50	5,00	
59	Via Acciarini civ. 7	3	80				90	5,00	
60	Via Acciarini civ. 7	3	50				63	5,00	
61	Via Acciarini civ. 1	3	50				63	5,00	



geopavia

Progetto n°: 22-0320-3E-00-001272
Web: SI-20-0300-02-1109
Codice intervento: 25.1


Unità Responsabile della Progettazione
INGEGNERIA-PROGRE

Comune di Torino (TO) - Via Vire
PROGETTO ESECUTIVO
SOSTITUZIONE RETE IN BP (L=2.504,78 m) - GARA ATEM T01
Intervento n° SK-036213-001272-TSS-TORINO36

Planimetria di localizzazione IDU

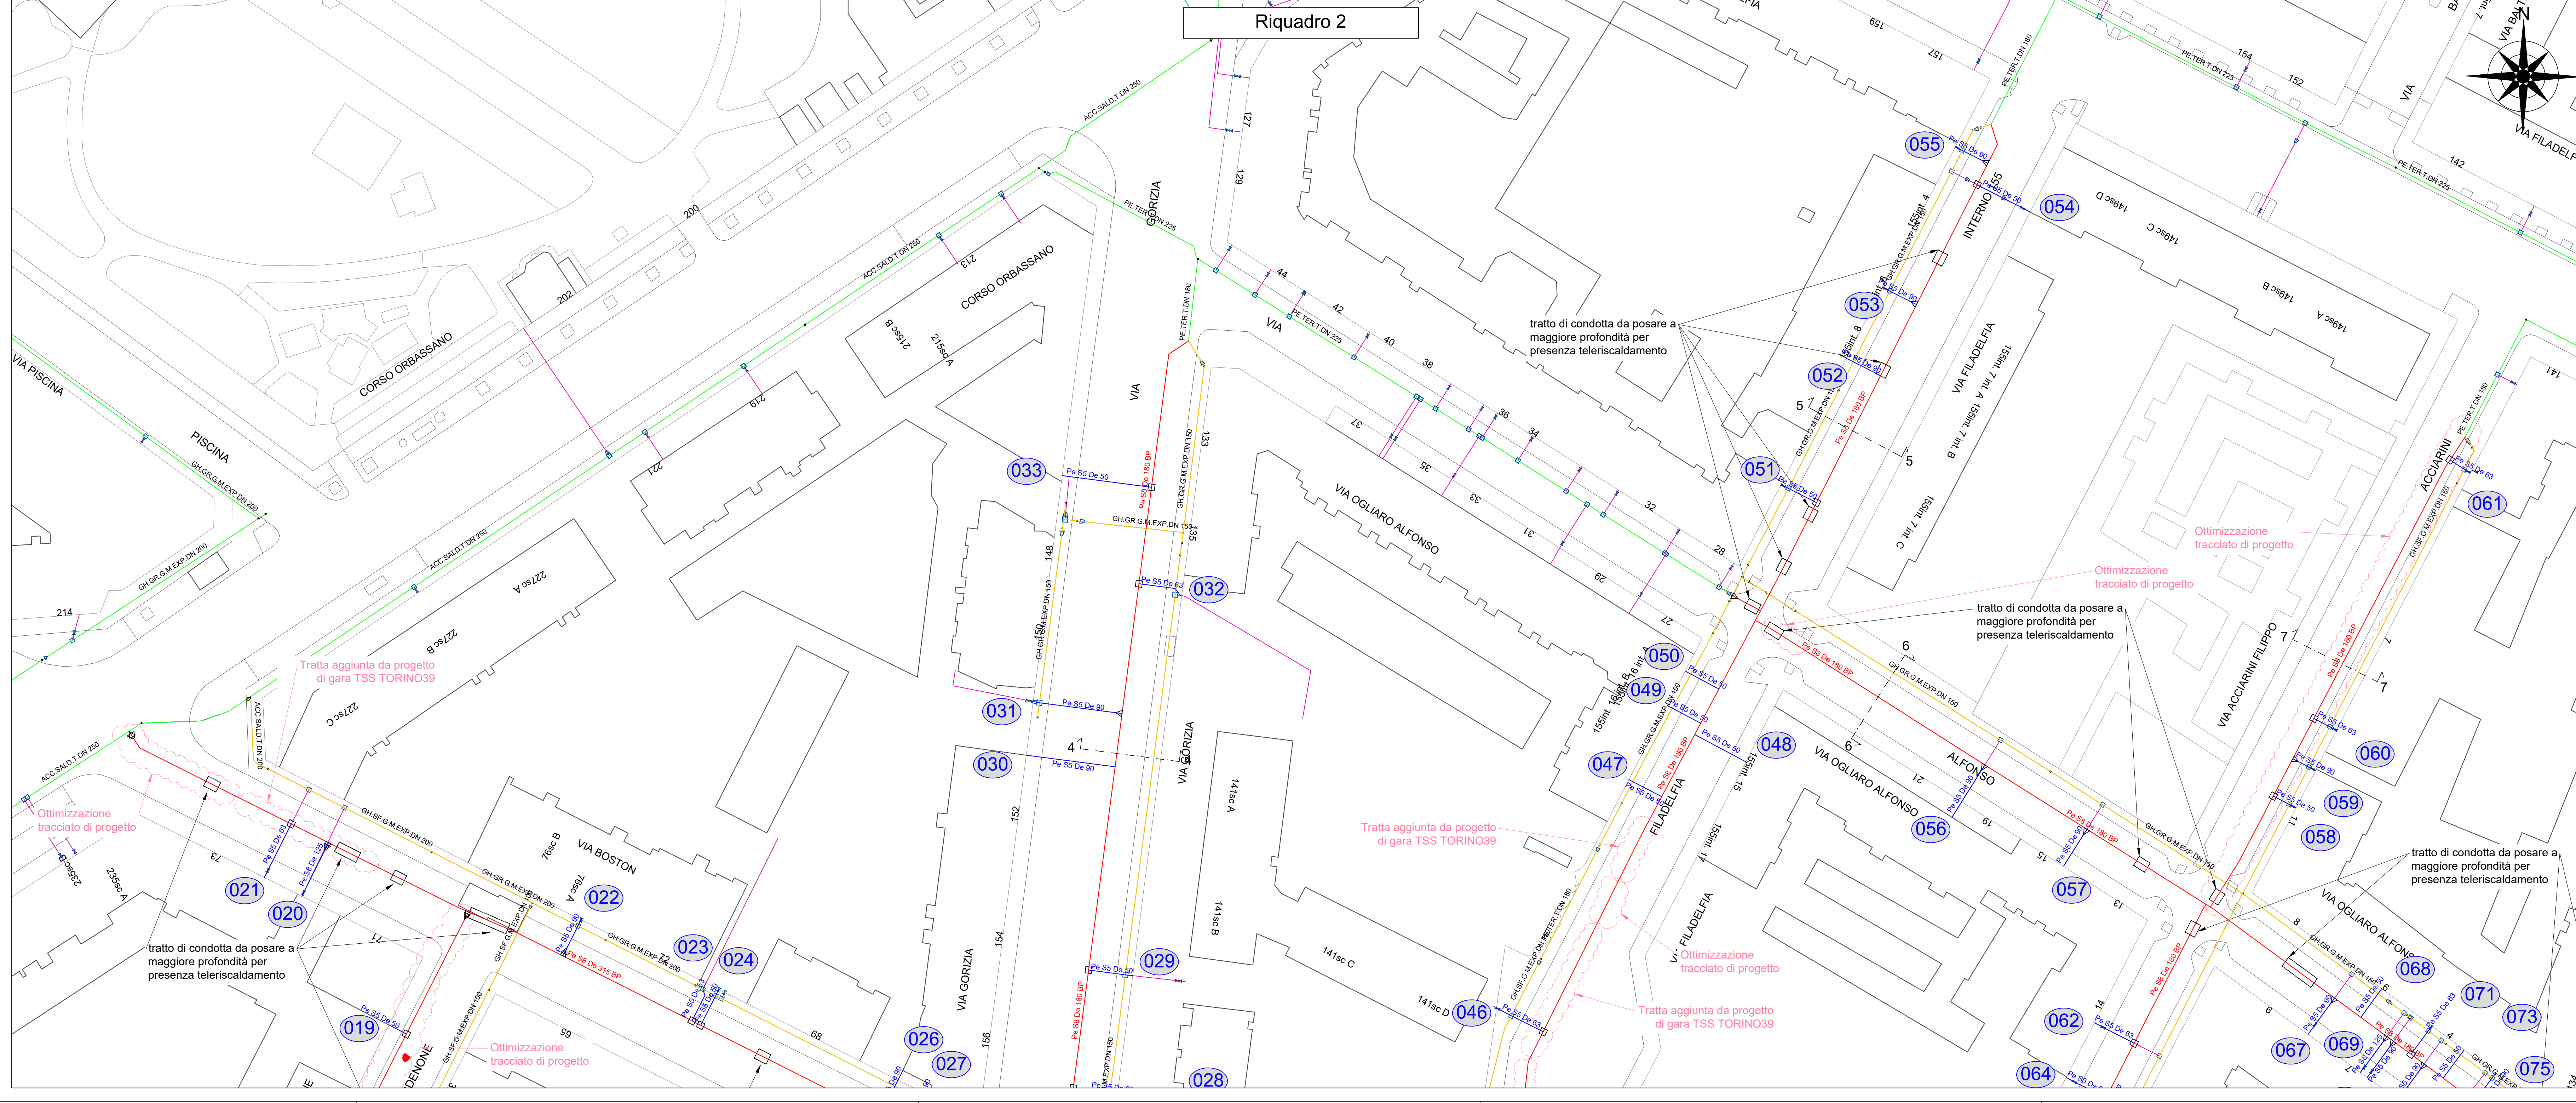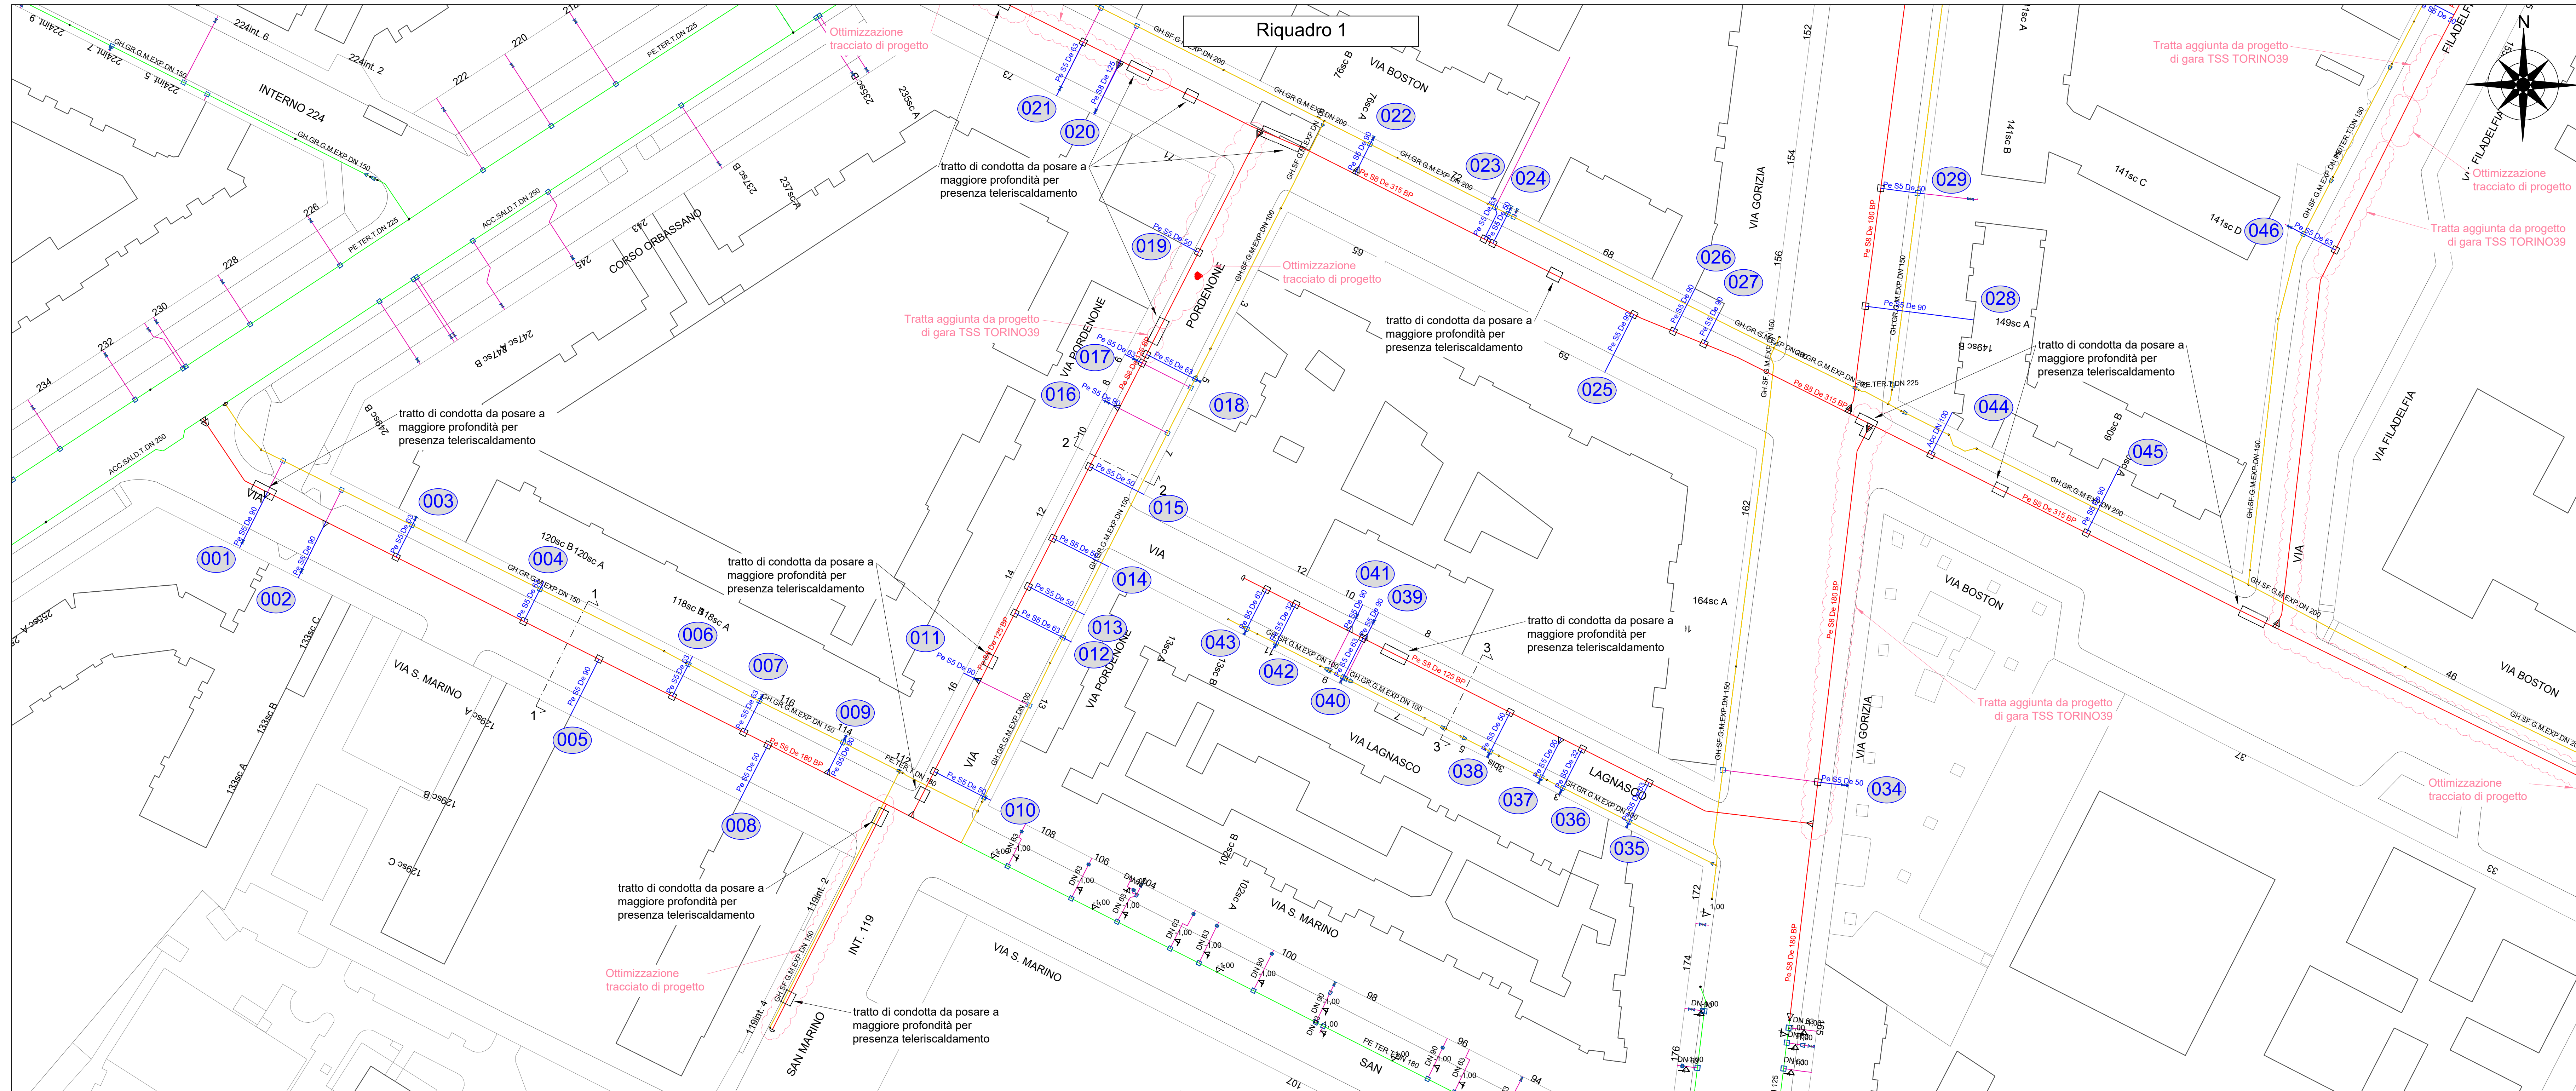

KEY PLAN

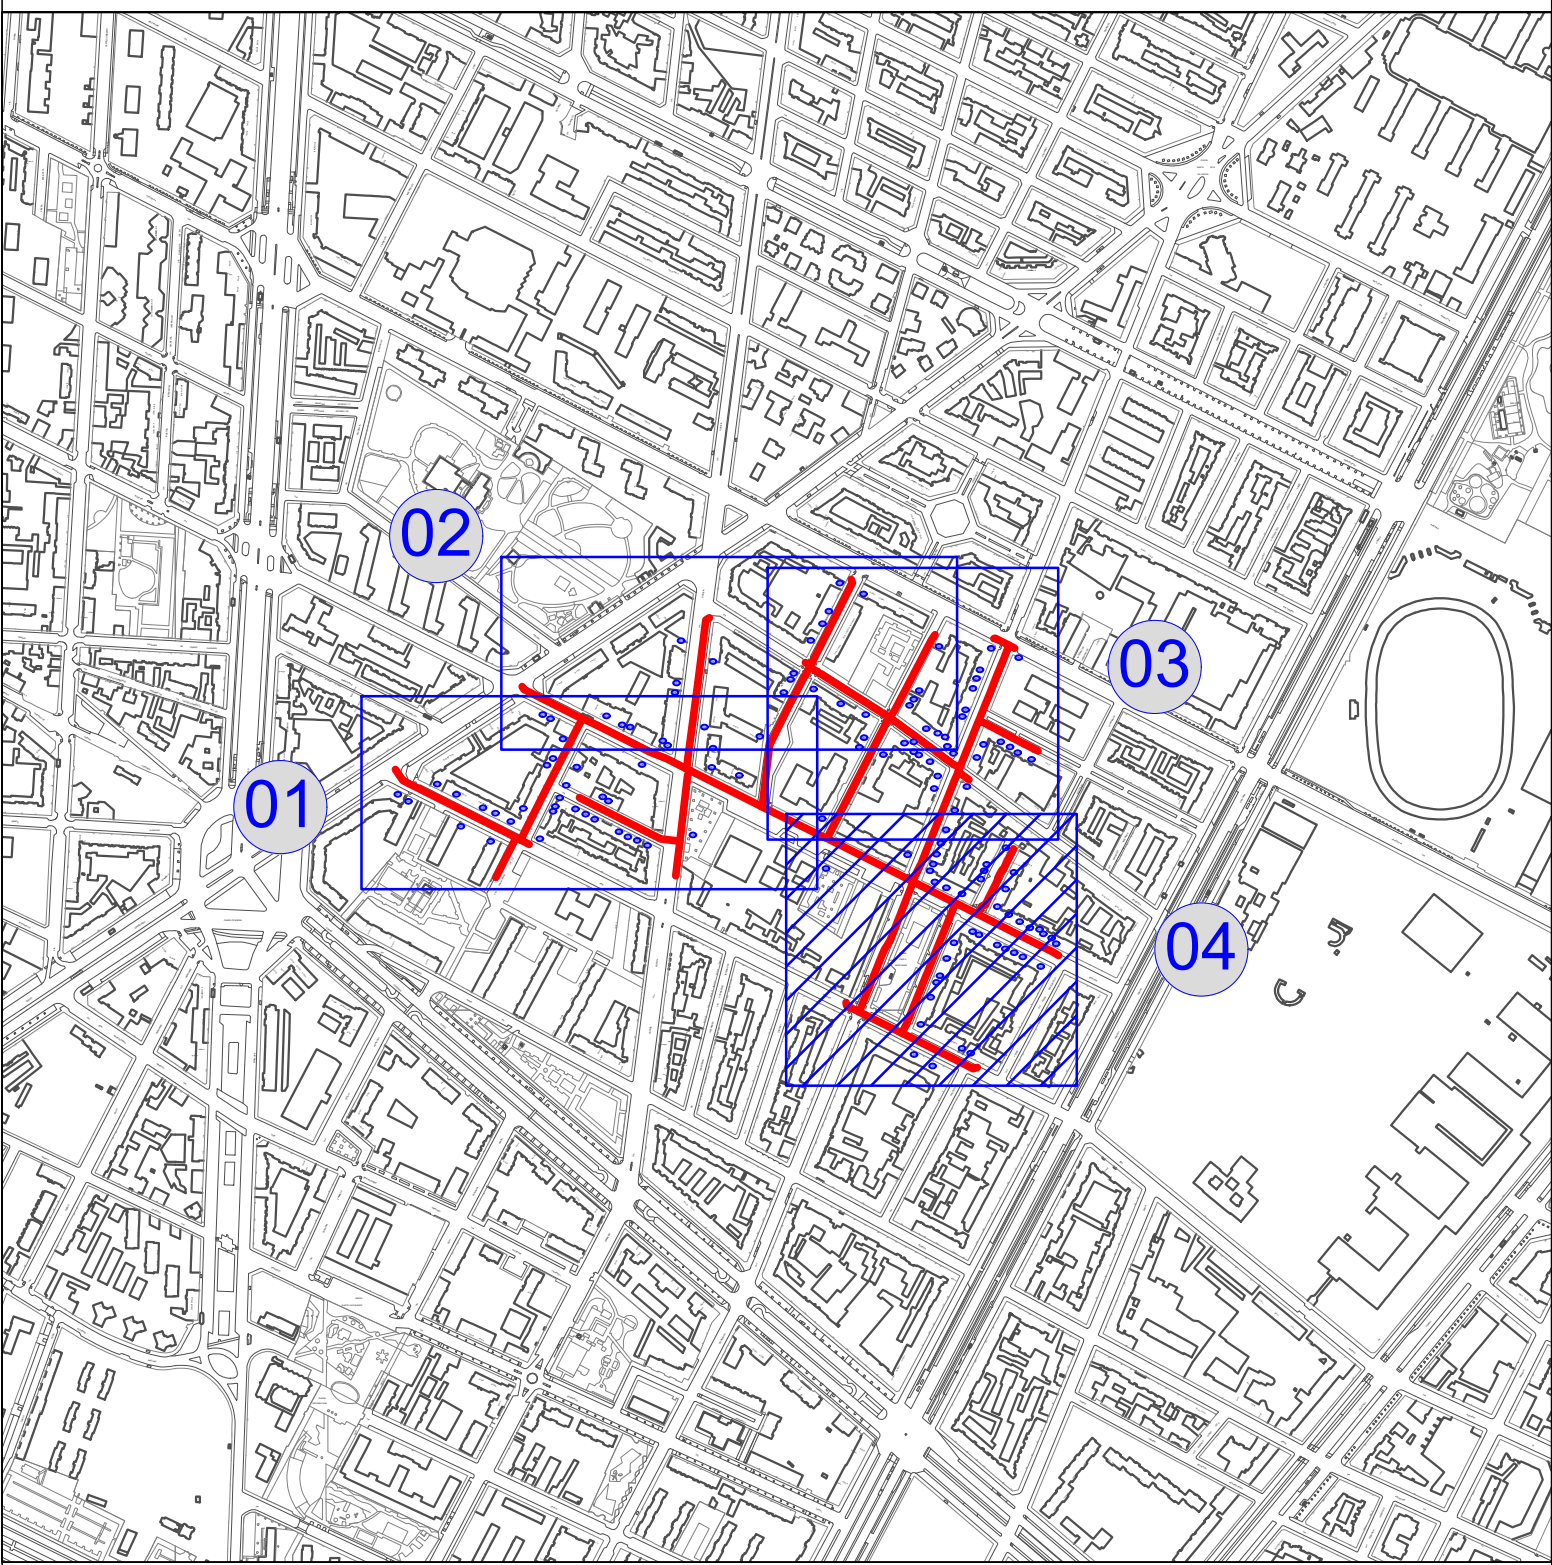

LEGENDA

	Rete in progetto BP		Organo di presa		Numero I.D.U. in progetto
	Tubazione I.D.U. esistente				
	Rete da rimuovere				
	Tubazione I.D.U. in progetto				

n.	Posizione	Tipologico	diametro esistente		diametro di progetto		lunghezza (L) [m]	Δ H[m]	L privata >12m [m]
			Acc DN	Pe De	Acc DN	Pe De			
100	Via Boston civ. 30					90	5,00		
101	Via Boston civ. 26	3	80			90	5,00		
102	Piazza Montanari civ. 131	3	80			90	8,00		
103	Piazza Montanari civ. 133	3	80			90	8,00		
104	Piazza Montanari civ. 137	3	75			90	8,00		
105	Piazza Montanari civ. 137	3	75			90	7,00		
106	Piazza Montanari civ. 139	3	25			32	7,00		
107	Piazza Montanari civ. 145	3	25			32	8,00		
108	Via San Marino civ. 63	4	65			63	11,00		
109	Via San Marino civ. 59	2		63		63	1,00		
110	Via San Marino civ. 58	3	75			90	9,00		
111	Via San Marino civ. 56	3	50			63	10,00		
112	Via Boston civ. 24	3	80			90	5,00		
113	Via Boston 22 int. 4	4	75			90	6,00		
114	Via Boston 22 int. 3	3	75			90	14,00		
115	Via Boston 22 int. 6	4	80			90	6,00		
116	Via Boston 22 int. 5	3	75			90	13,00		
117	Via Boston 22 int. 8	4	80			90	6,00		
118	Via Boston 22 int. 5	3	80			90	13,00		
119	Via Boston 22 int. 7	3	75			90	15,00		
120	Via Boston 19	4	50			63	15,00		
121	Via Boston 17					90	15,00		
122	Via Boston 16	3	75			90	5,00		
123	Via Boston 15	4	80			90	15,00		
124	Via Boston 13	4	75			90	15,00		
125	Via Boston 16					50	5,00		
126	Via Boston 11	4	80			90	15,00		
127	Via Boston 14	3	75			90	5,00		
128	Via Boston 9	4	50			63	15,00		
129	Via Boston 12					50	5,00		
130	Via Boston 12	3	75			90	6,00		
131	Via Boston 10	3	80			90	5,00		
132	Via Boston 10	1		63		63	5,00		
133	Via Boston 7	4	50			63	15,00		

INGEGNERI DELLA PROV. DI PAVIA
DOTT. ING. CLAUDIO GATTI
AUT. MIN. 10/03/2015
ANNO 1978/2015
S. 1147

 geopavia		Progettista: Ing. Claudio Gatti Ordine degli Ingegneri di Pavia Albo n. 3197		Unità Responsabile della Progettazione									
				INGEREAL-INGE-PROGRE									
Progetto n°: 22-0320-3E-00-001272													
WBS: SI.20.0300.02.1109													
Codice elaborato: 25.3				Tavola:									
Nome file: AI.25.dwg				Descrizione: Emissione per progetto esecutivo		00		28		01		26	
Formato: A0				Scale: 1:500		A.		Ingardi		L.		Domingo	
Completato:				Comm.: 2464		Rev.		G.		M.		A.	
						Redatto		Controllato		Approvato			
 Italgas Reti				Comune di Torino (TO) - Vie Varie									
				PROGETTO ESECUTIVO									
				SOSTITUZIONE RETE IN BP (L=2.504,78 m) - GARA ATEM TO1									
				Intervento n° SI-036213-001272-TSS-TORIN036									
				Planimetria di localizzazione IDU									

Il presente elaborato è di proprietà aziendale - La società tutelera i propri diritti a termini di legge.