

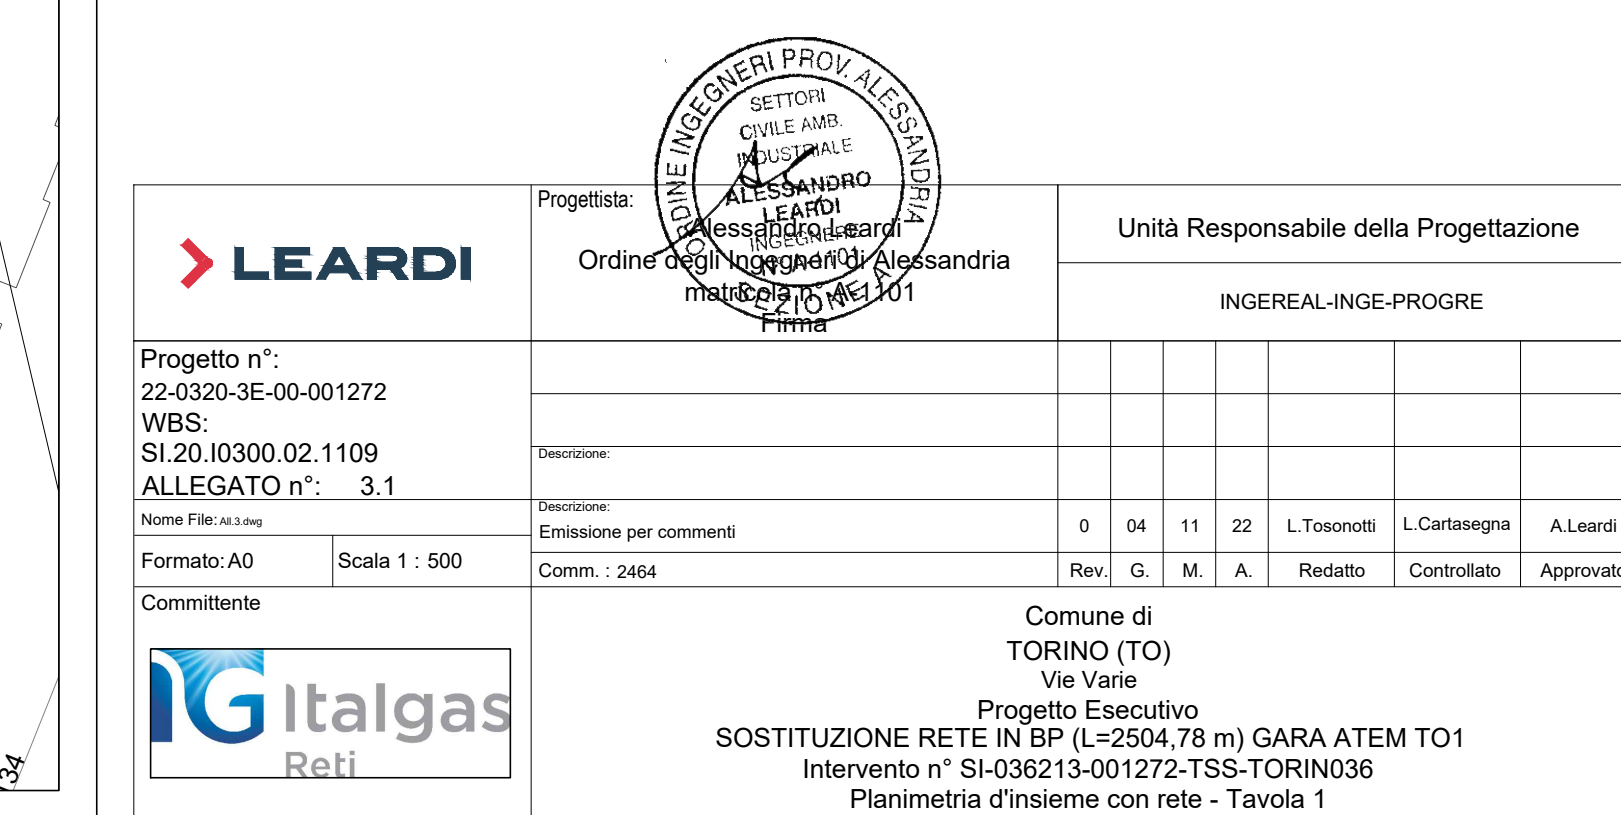
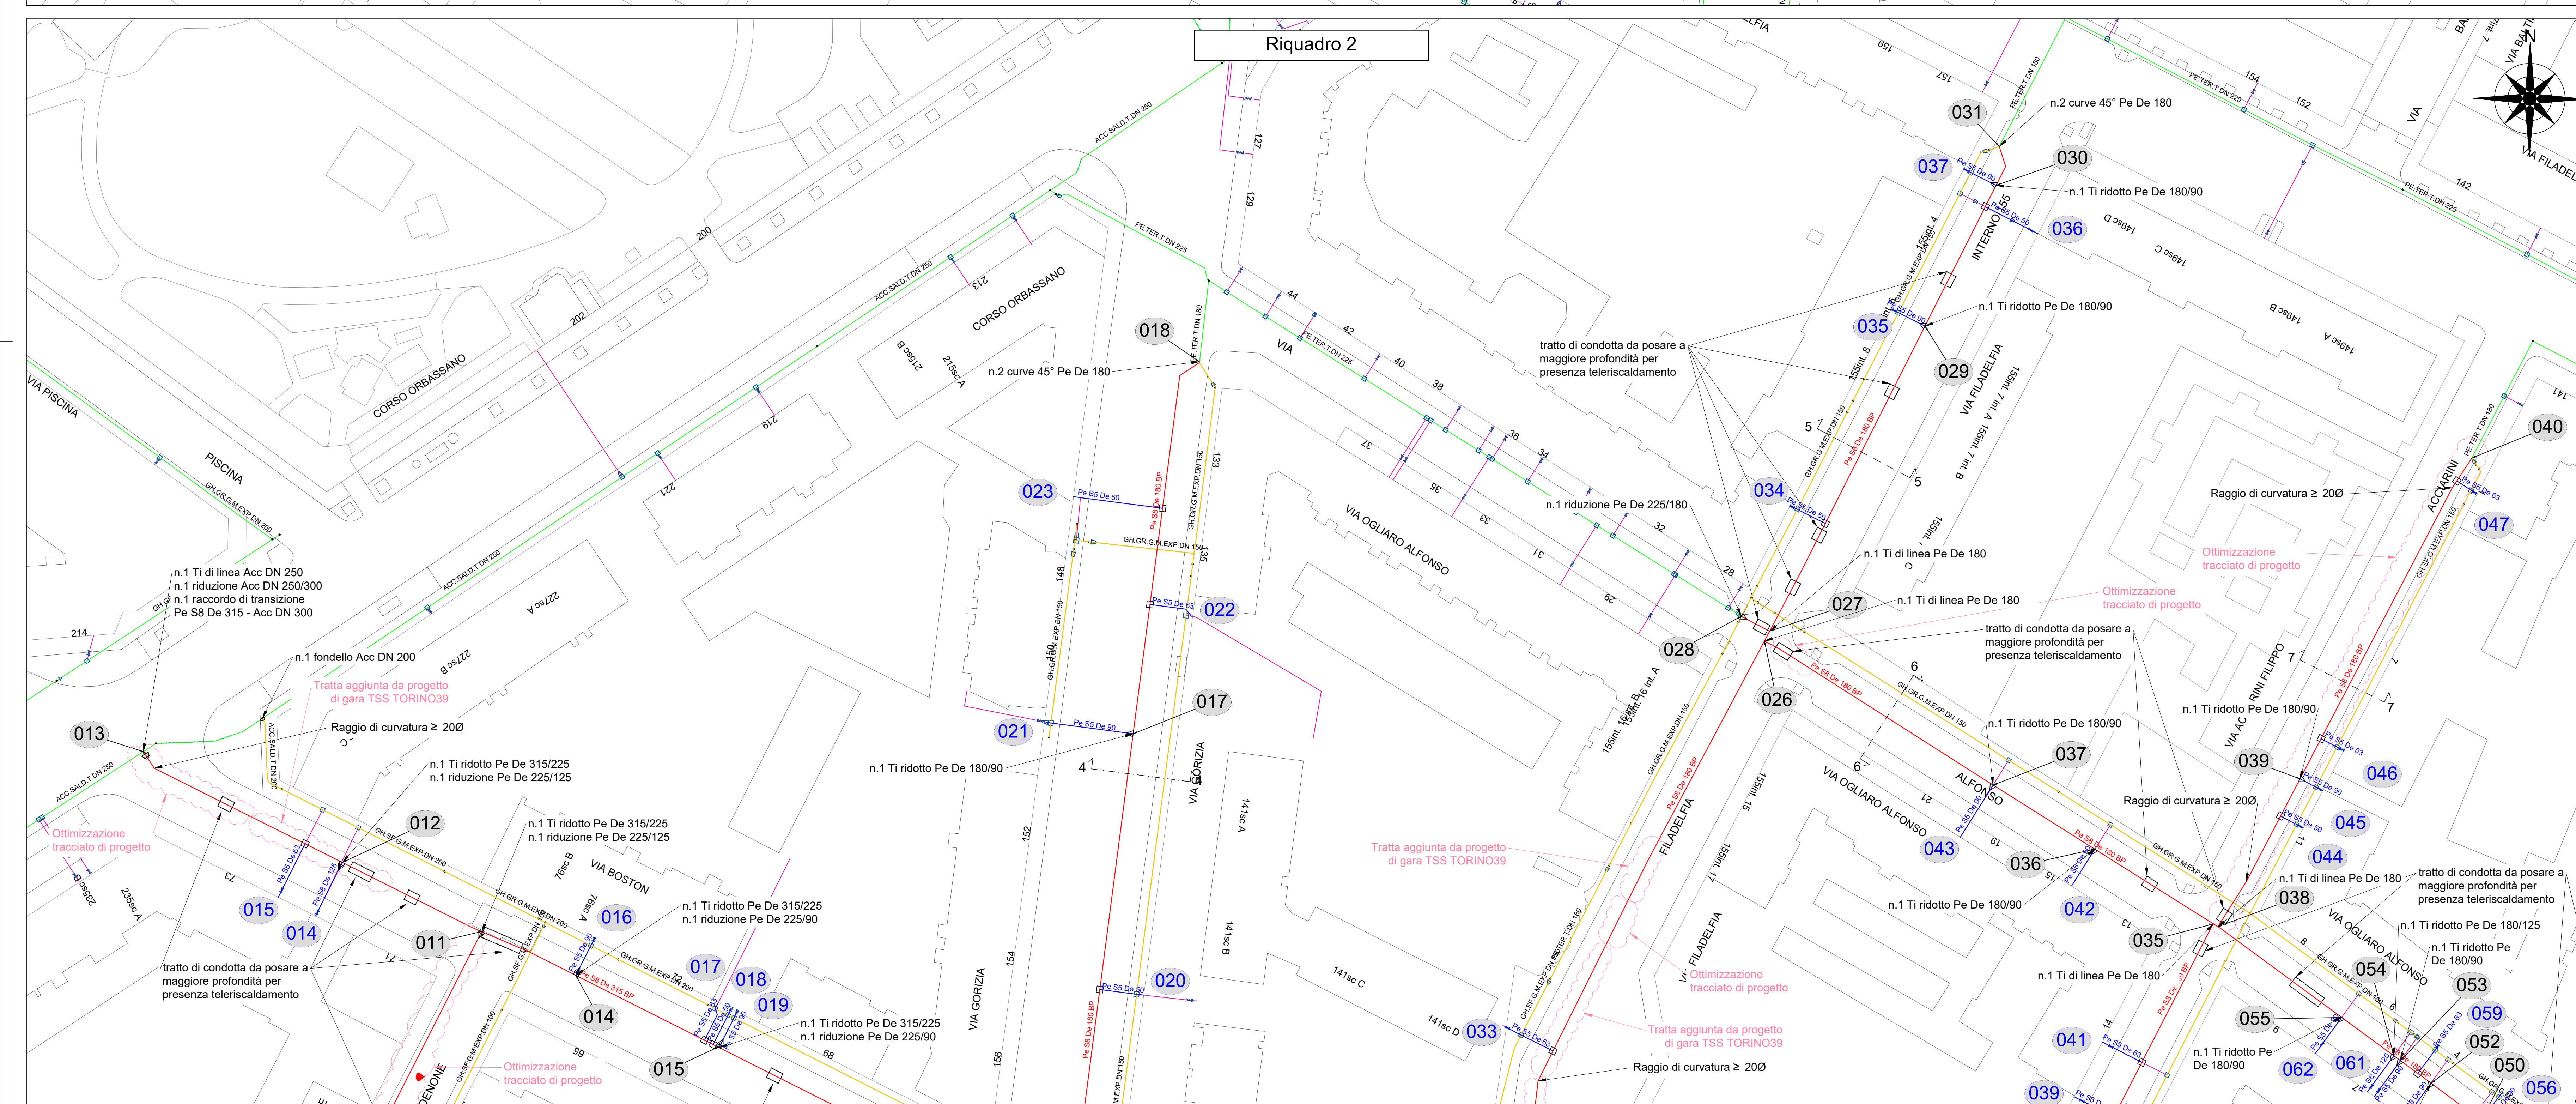
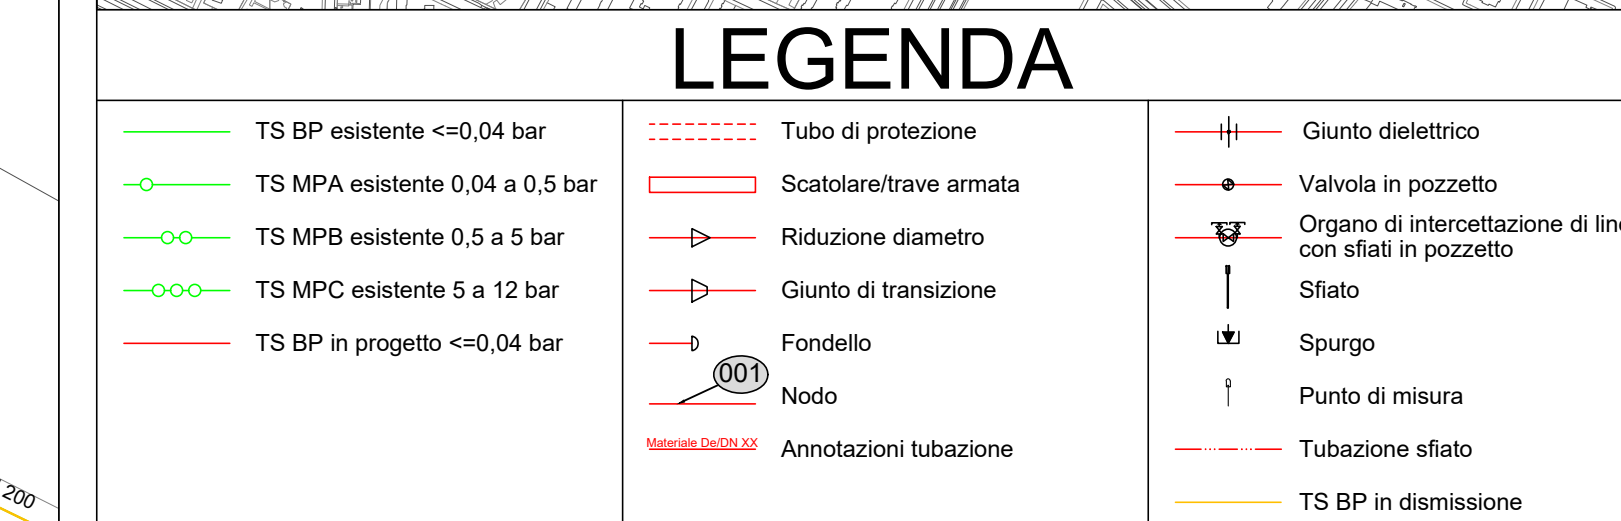
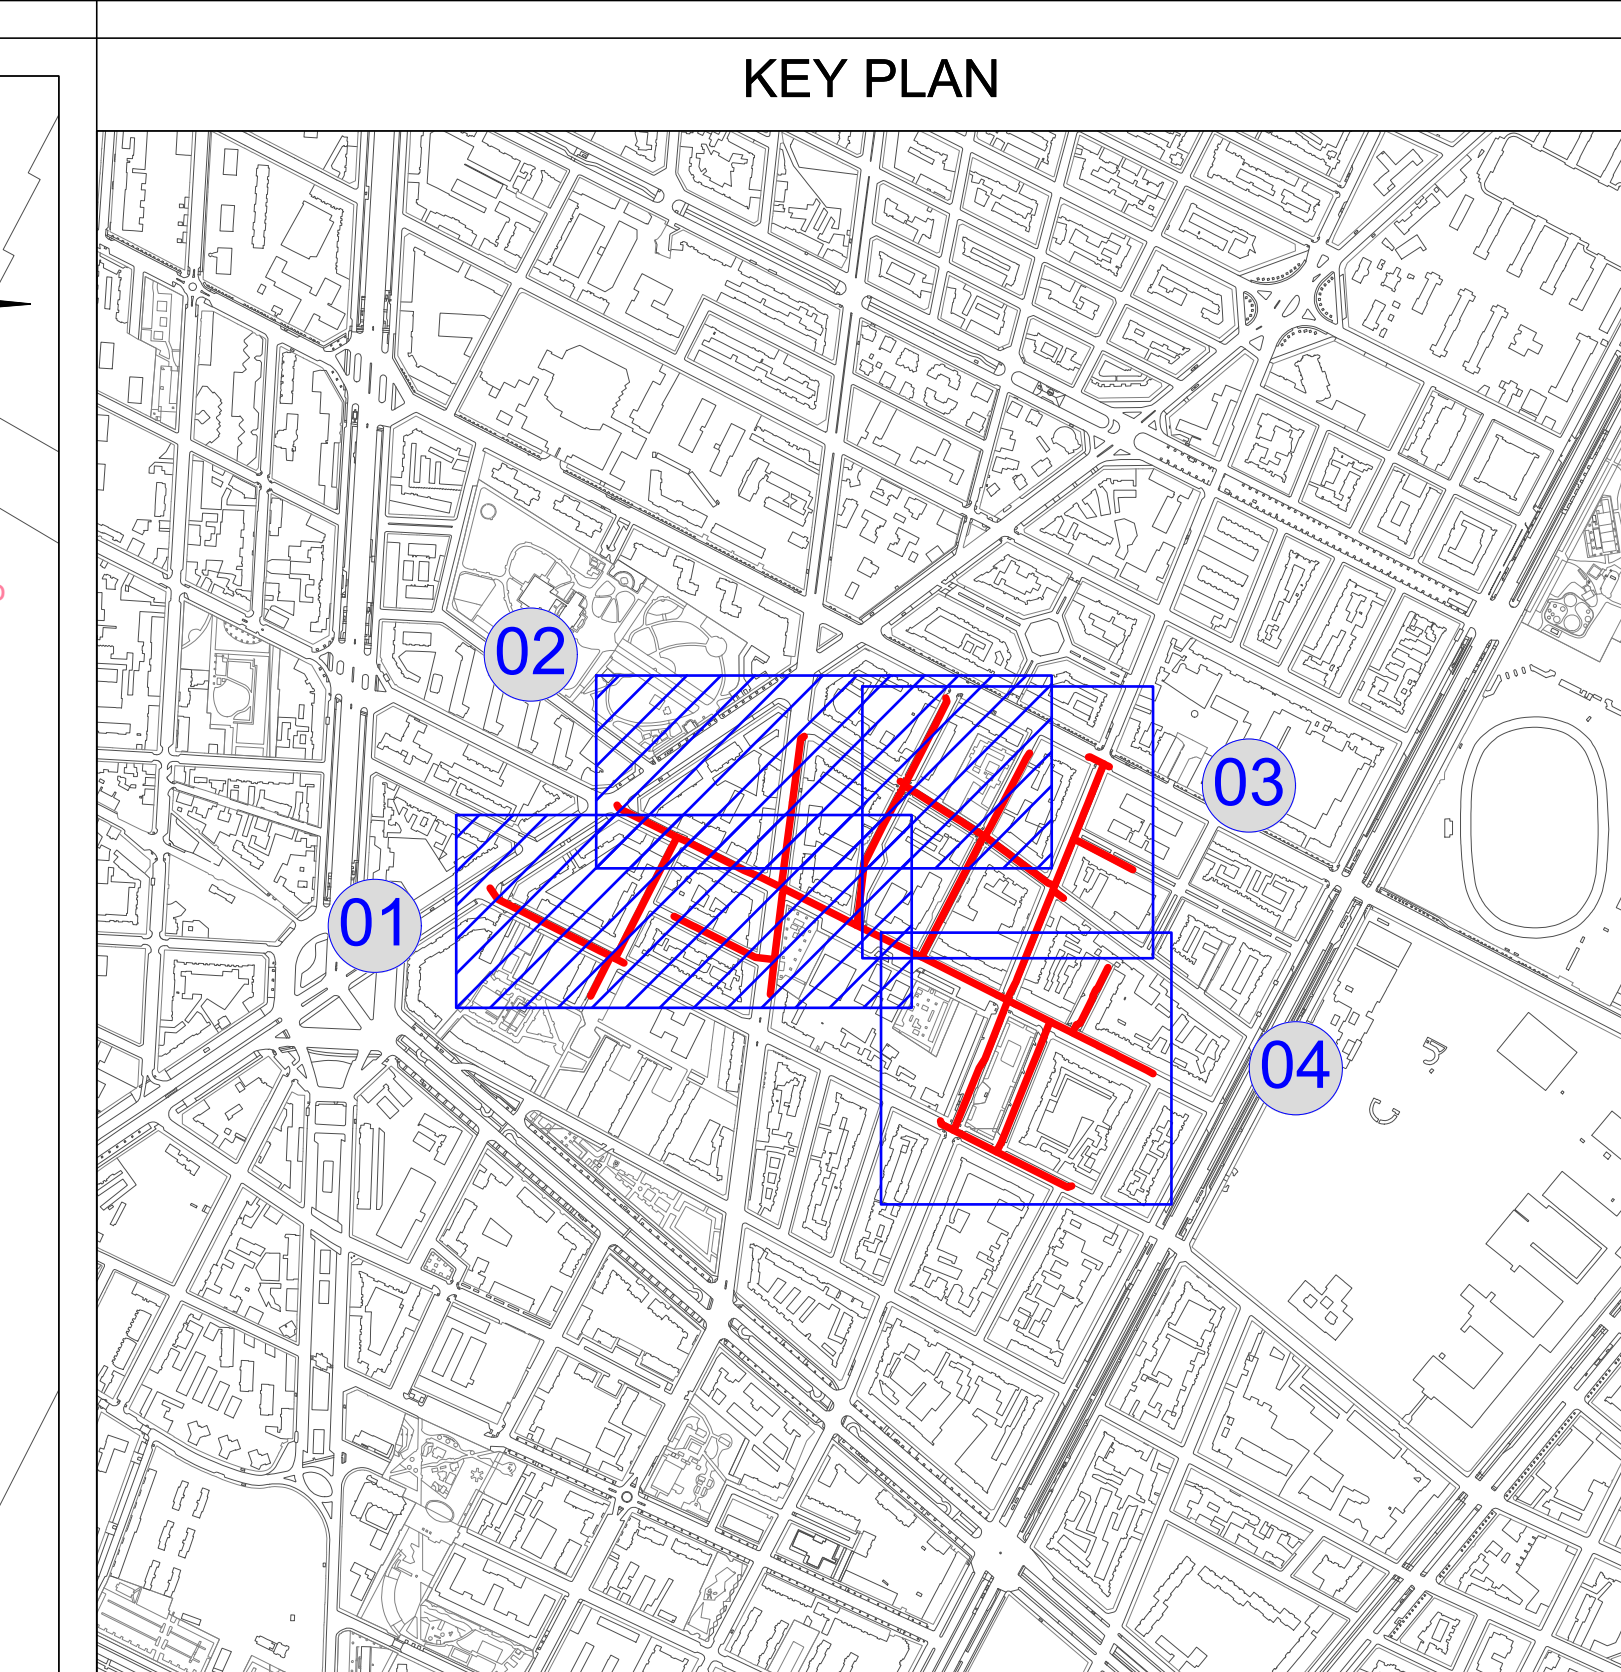


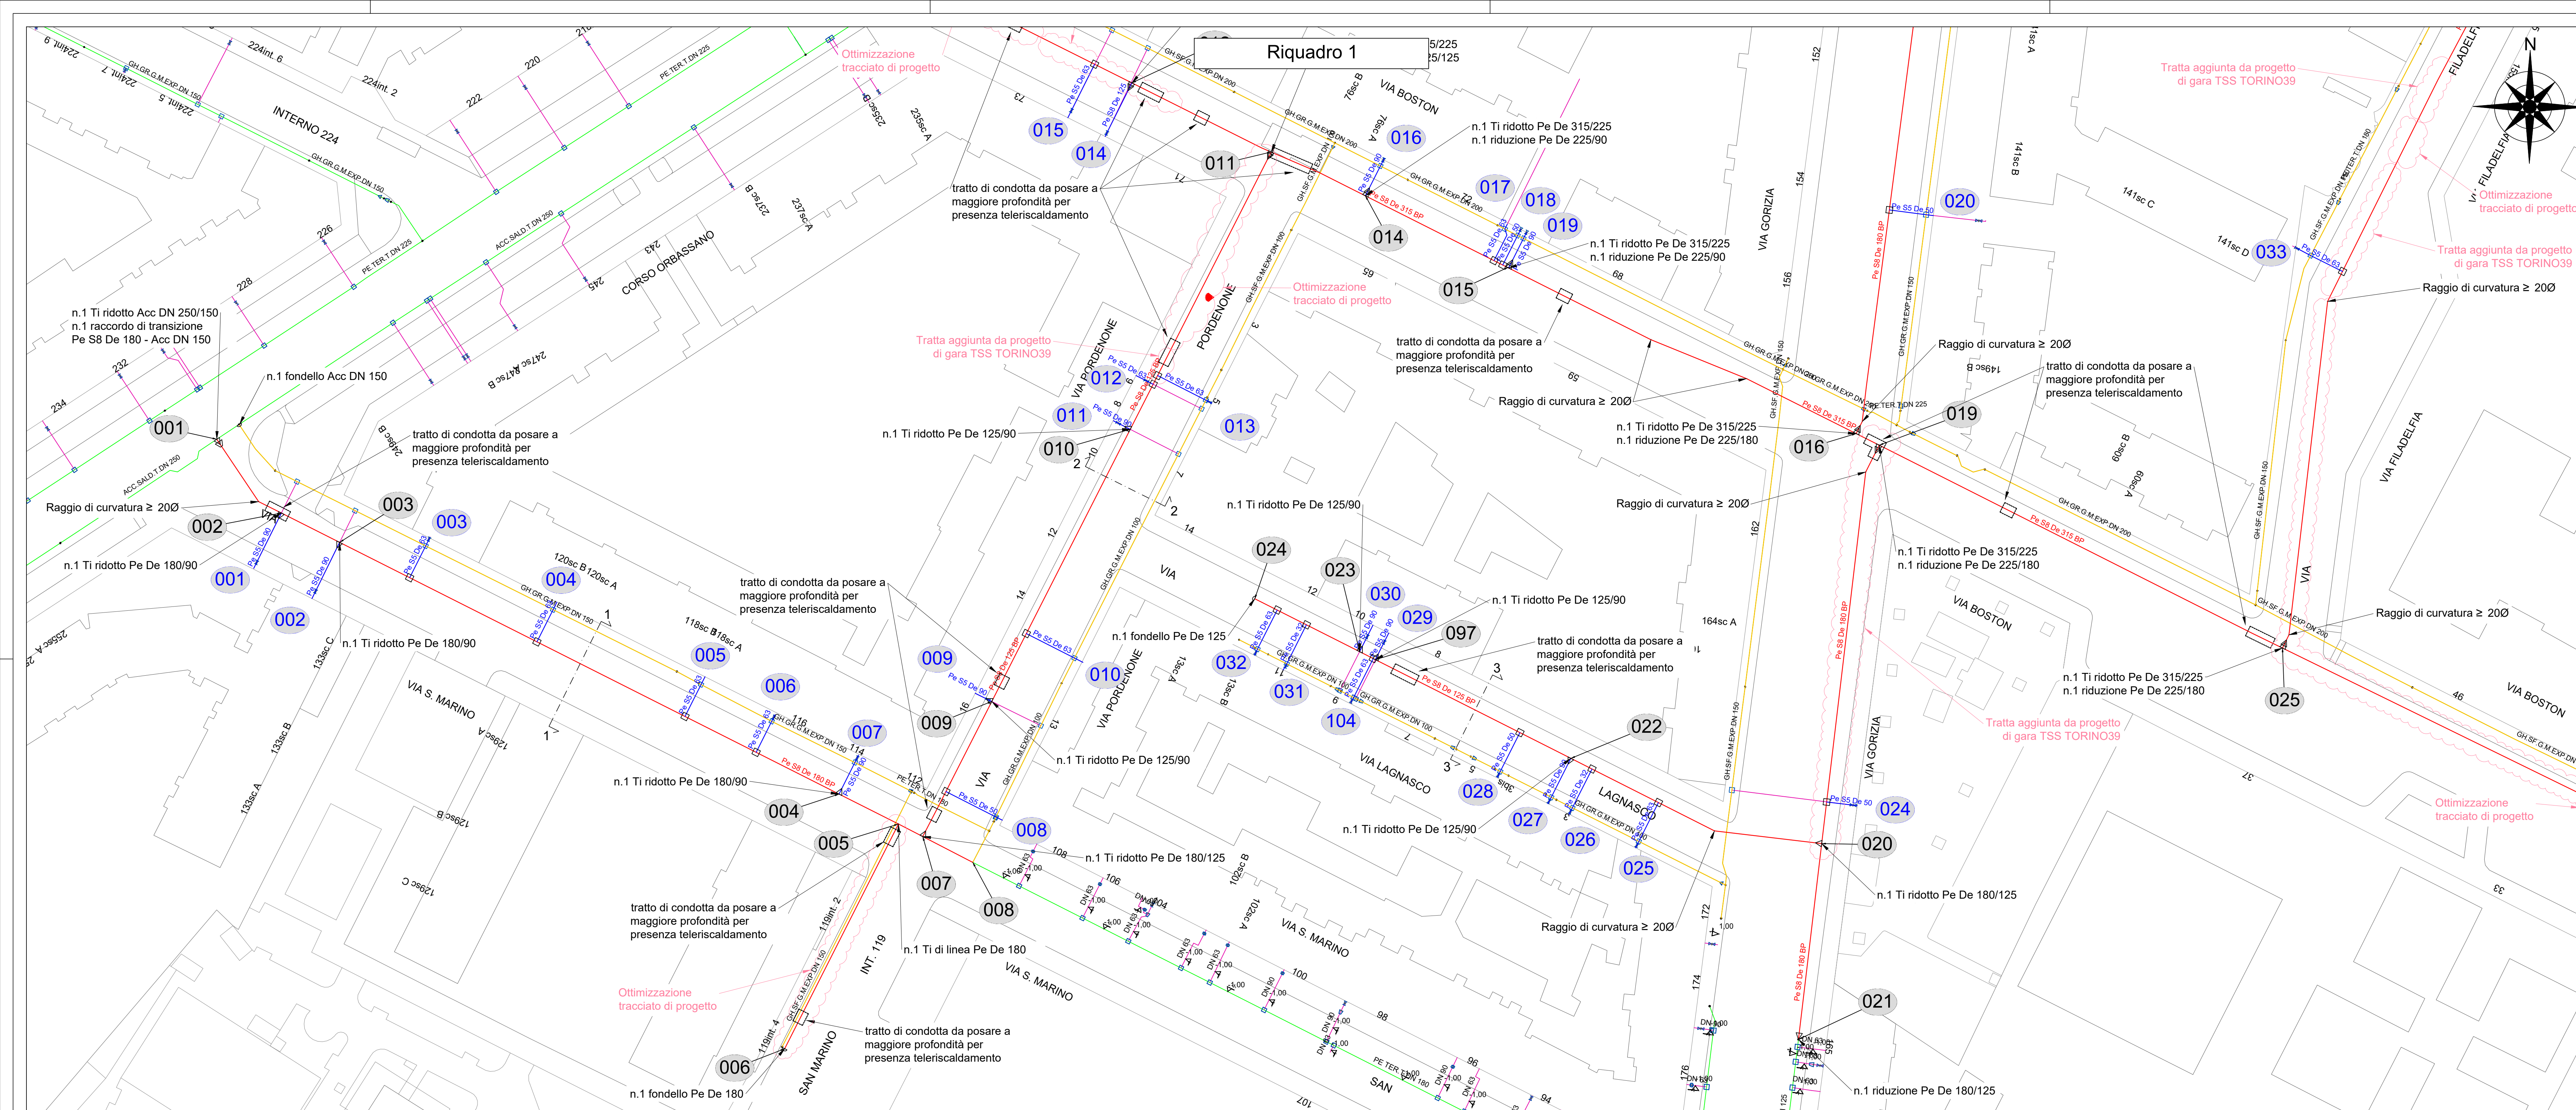


KEY PLAN

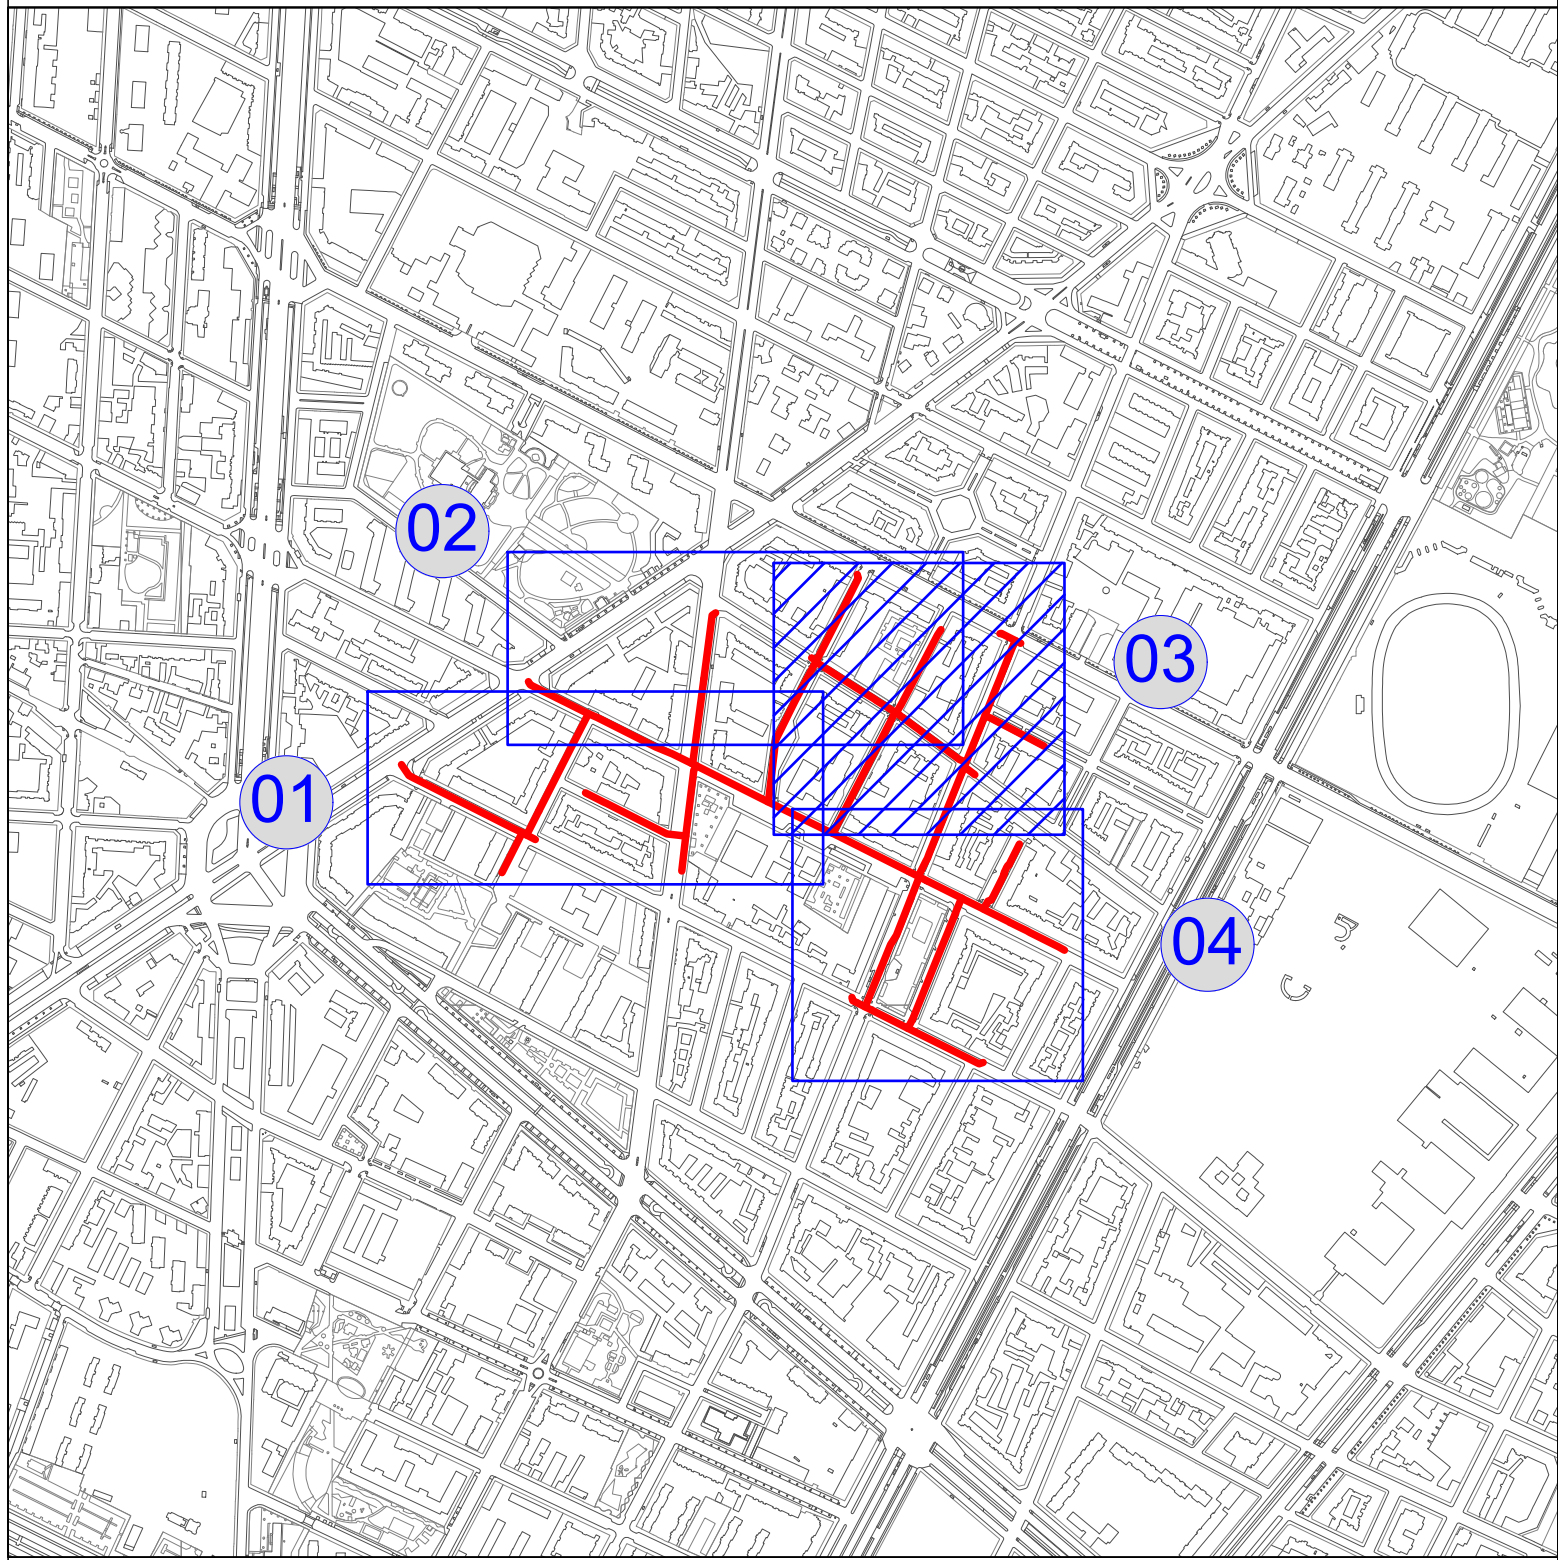


LEGENDA

- TS BP esistente <=0,04 bar - TS MPA esistente 0,04 a 0,5 bar - TS MPB esistente 0,5 a 5 bar - TS MPC esistente 5 a 12 bar - TS BP in progetto <=0,04 bar	- Tubo di protezione - Scatolare/trave armata - Riduzione diametro - Giunto di transizione - Fondello - Nodo - Annotazioni tubazione	- Giunto dielettrico - Valvola in pozzetto - Organo di intercettazione di linea con sfiati in pozzetto - Sfialo - Spurgo - Punto di misura - Tubazione sfiato - TS BP in dismissione
--	--	--

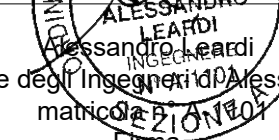
	Progettista:  Alessandro Leardi Ordine degli Ingegneri di Alessandria matricola n. 10101 Firma	Unità Responsabile della Progettazione									
		INGEREAL-INGE-PROGRE									
Progetto n°: 22-0320-3E-00-001272 WBS: SI.20.10300.02.1109 ALLEGATO n°: 3.2											
Nome File: 03.03.03		Descrizione:									
Emissione per commenti		0 04 11 22 L.Tosonotti L.Cartasegna A.Leardi									
Formato: A1	Scala 1 : 500	Comm.: 2464		Rev.	G.	M.	A.	Redatto	Controllato	Approvato	
Committente		Comune di TORINO (TO) Vie Varie Progetto Esecutivo SOSTITUZIONE RETE IN BP (L=2504,78 m) GARA ATEM TO1 Intervento n° SI-036213-001272-TSS-TORINO36 Planimetria d'insieme con rete - Tavola 2									
											

Il presente elaborato è di proprietà aziendale - La società tutelerà i propri diritti a termini di legge.

Riquadro 3

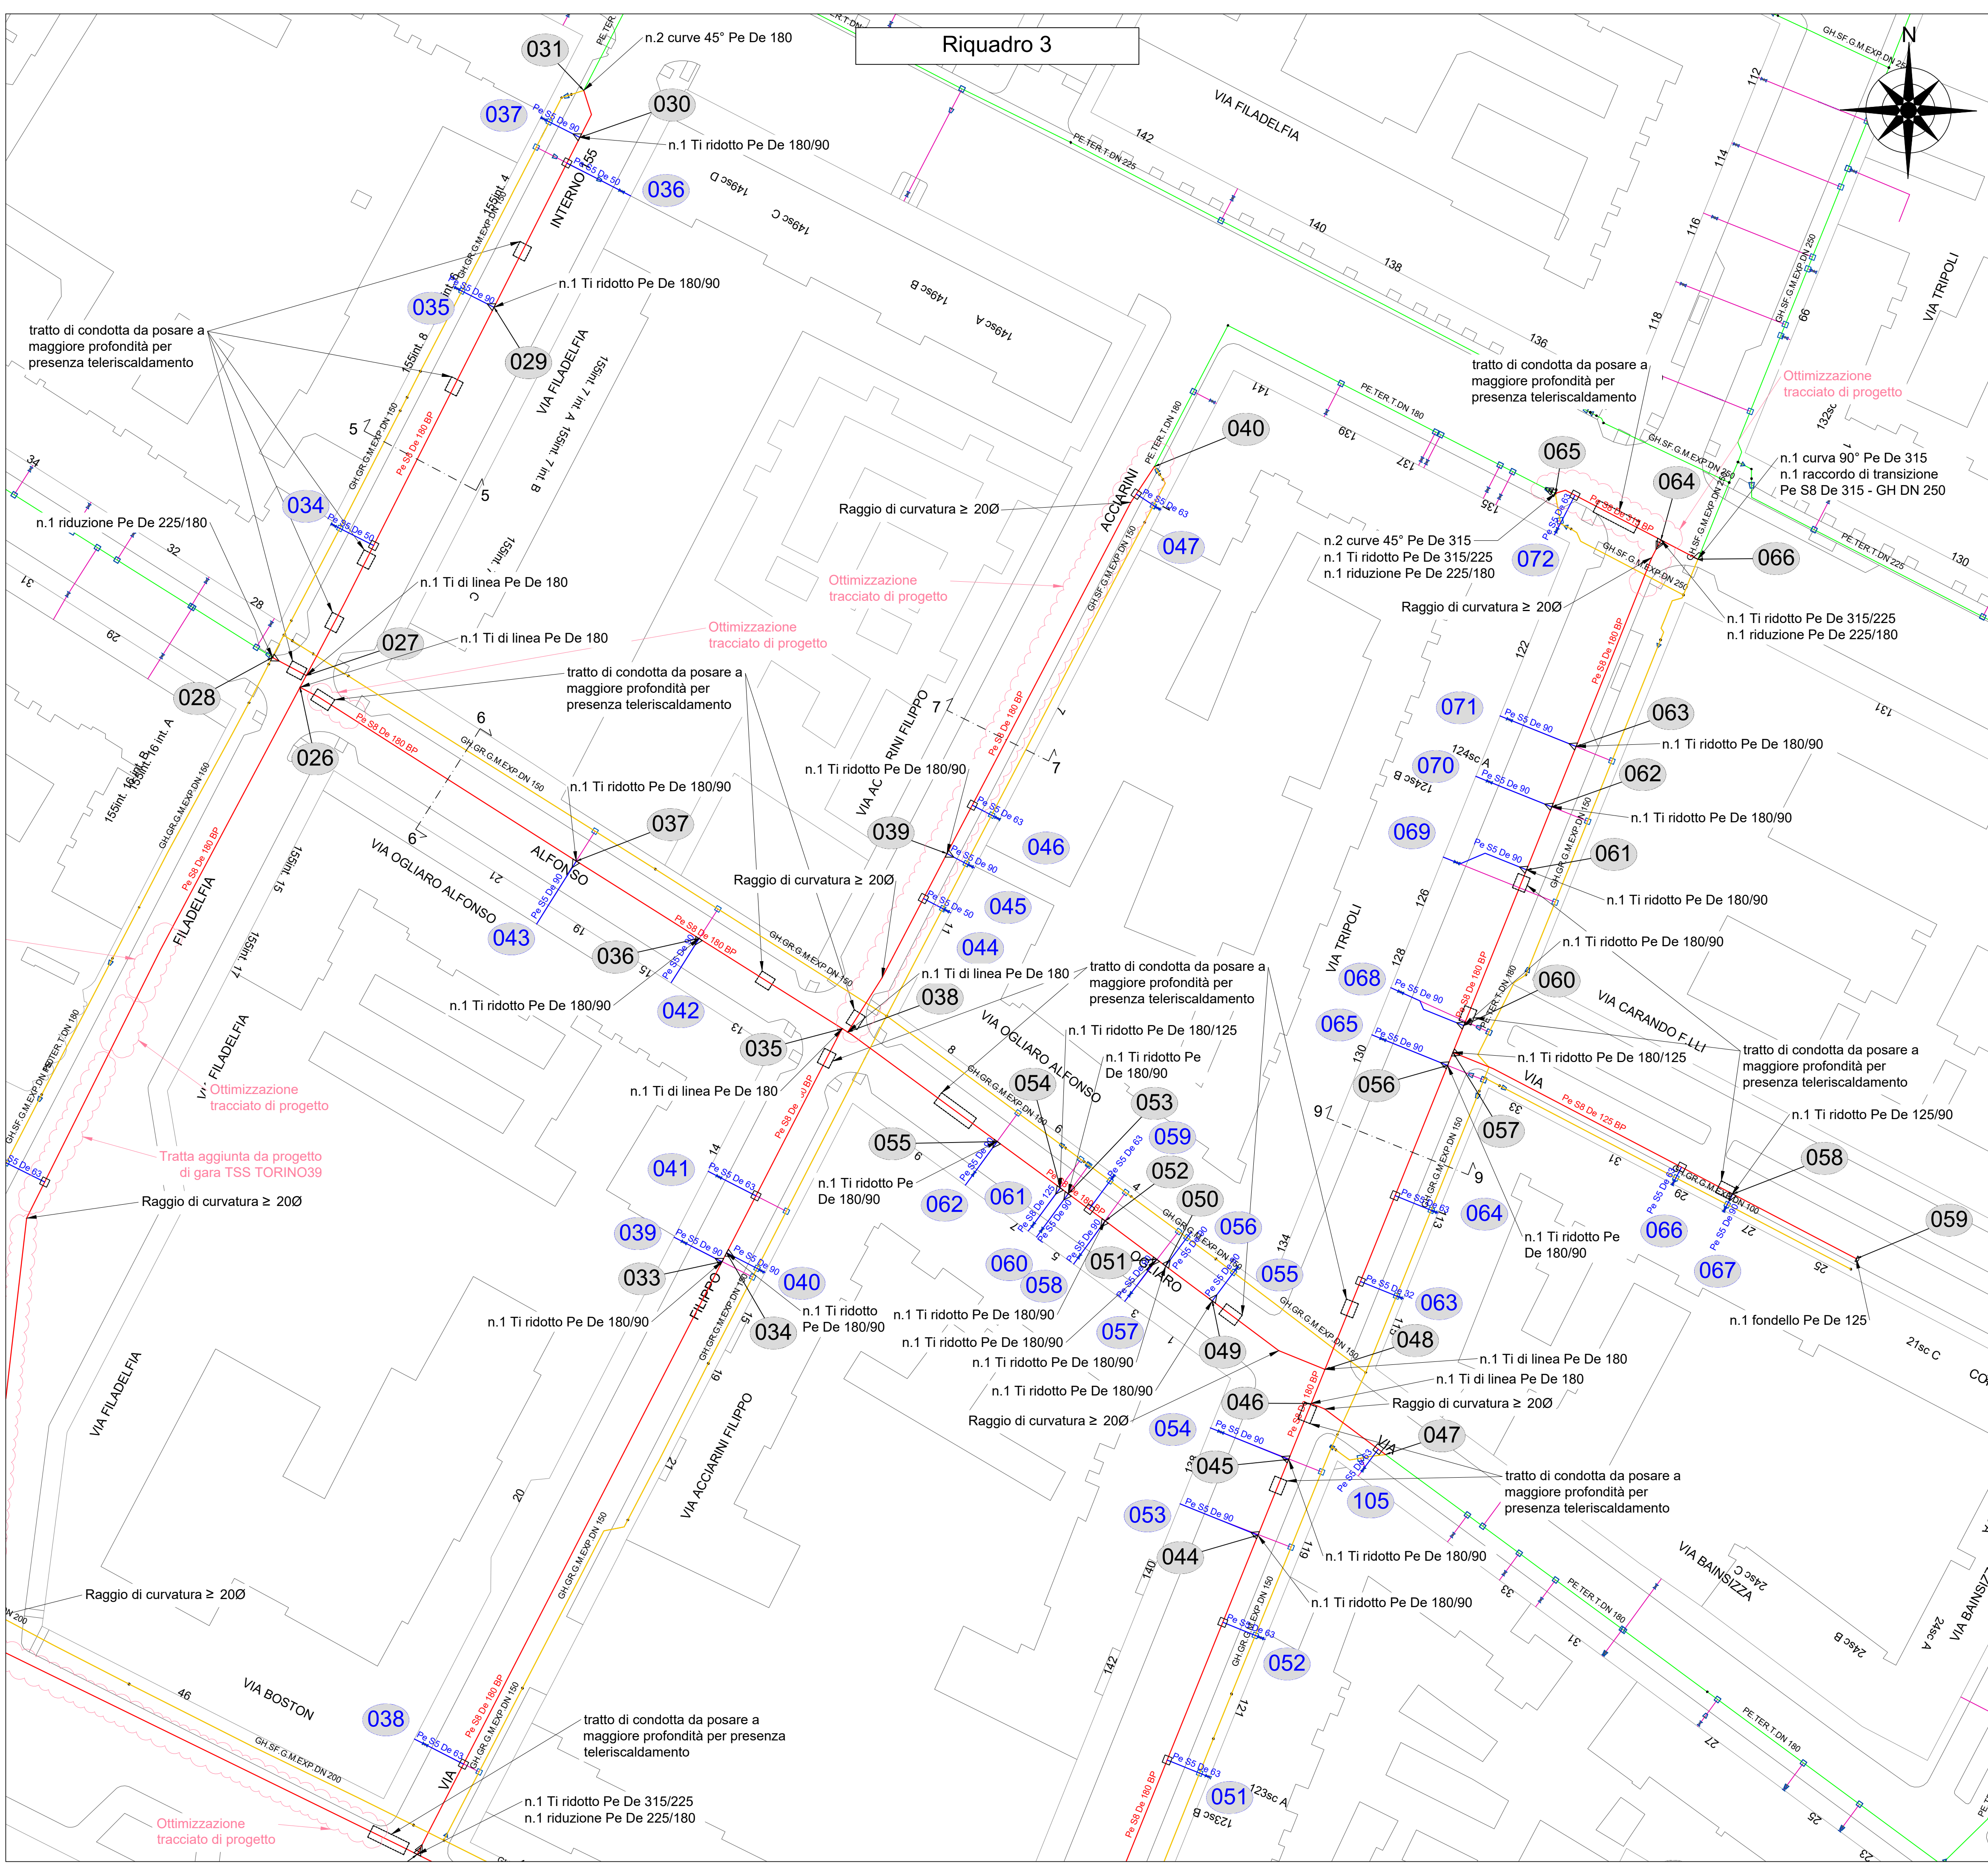

KEY PLAN

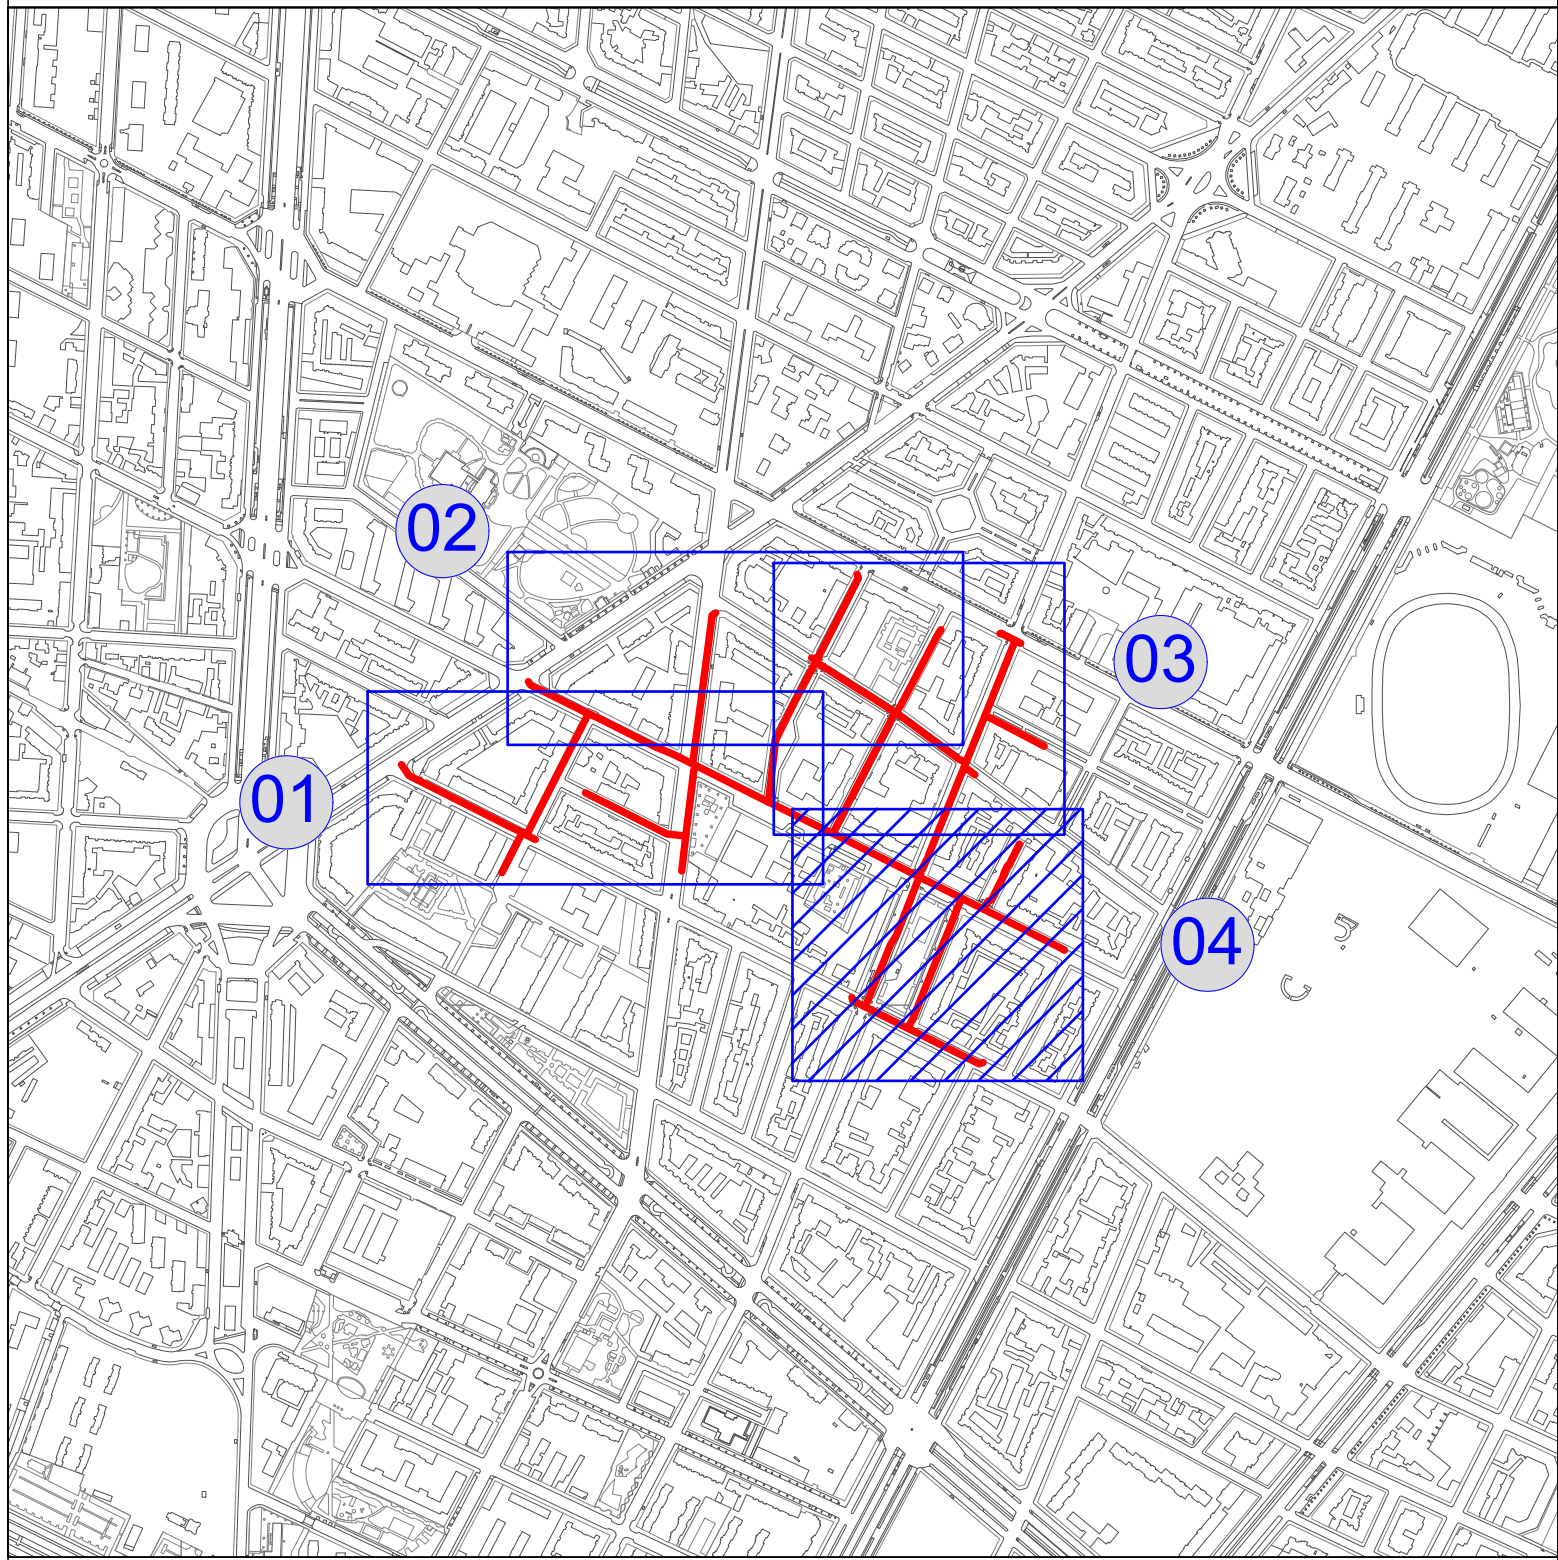

LEGENDA

TS BP esistente <=0,04 bar	Tubo di protezione	Giunto dielettrico
TS MPA esistente 0,04 a 0,5 bar	Scatolare/trave armata	Valvola in pozzetto
TS MPB esistente 0,5 a 5 bar	Riduzione diametro	Organo di intercettazione di linea con sfiati in pozzetto
TS MPC esistente 5 a 12 bar	Giunto di transizione	Sfiato
TS BP in progetto <=0,04 bar	Fondello	Spurgo
	Nodo	Punto di misura
	Annotazioni tubazione	Tubazione sfiato
		TS BP in dismissione



Progetto n°:
22-0320-3E-00-001272
WBS:
SI.20.10300.02.1109
ALLEGATO n°: 3.3

Formato: A1 Scala: 1 : 500

Committente



Progettista:
Alessandro Leardi
Ordine degli Ingegneri di Alessandria
matricola n° 1401

Unità Responsabile della Progettazione

INGEREAL-INGE-PROGRE

Descrizione:									
Emissione per commenti									
Comm. : 2464									

Comune di
TORINO (TO)
Vie Varie
Progetto Esecutivo
SOSTITUZIONE RETE IN BP (L=2504,78 m) GARA ATEM TO1
Intervento n° SI-036213-001272-TSS-TORINO36
Planimetria d'insieme con rete - Tavola 3