



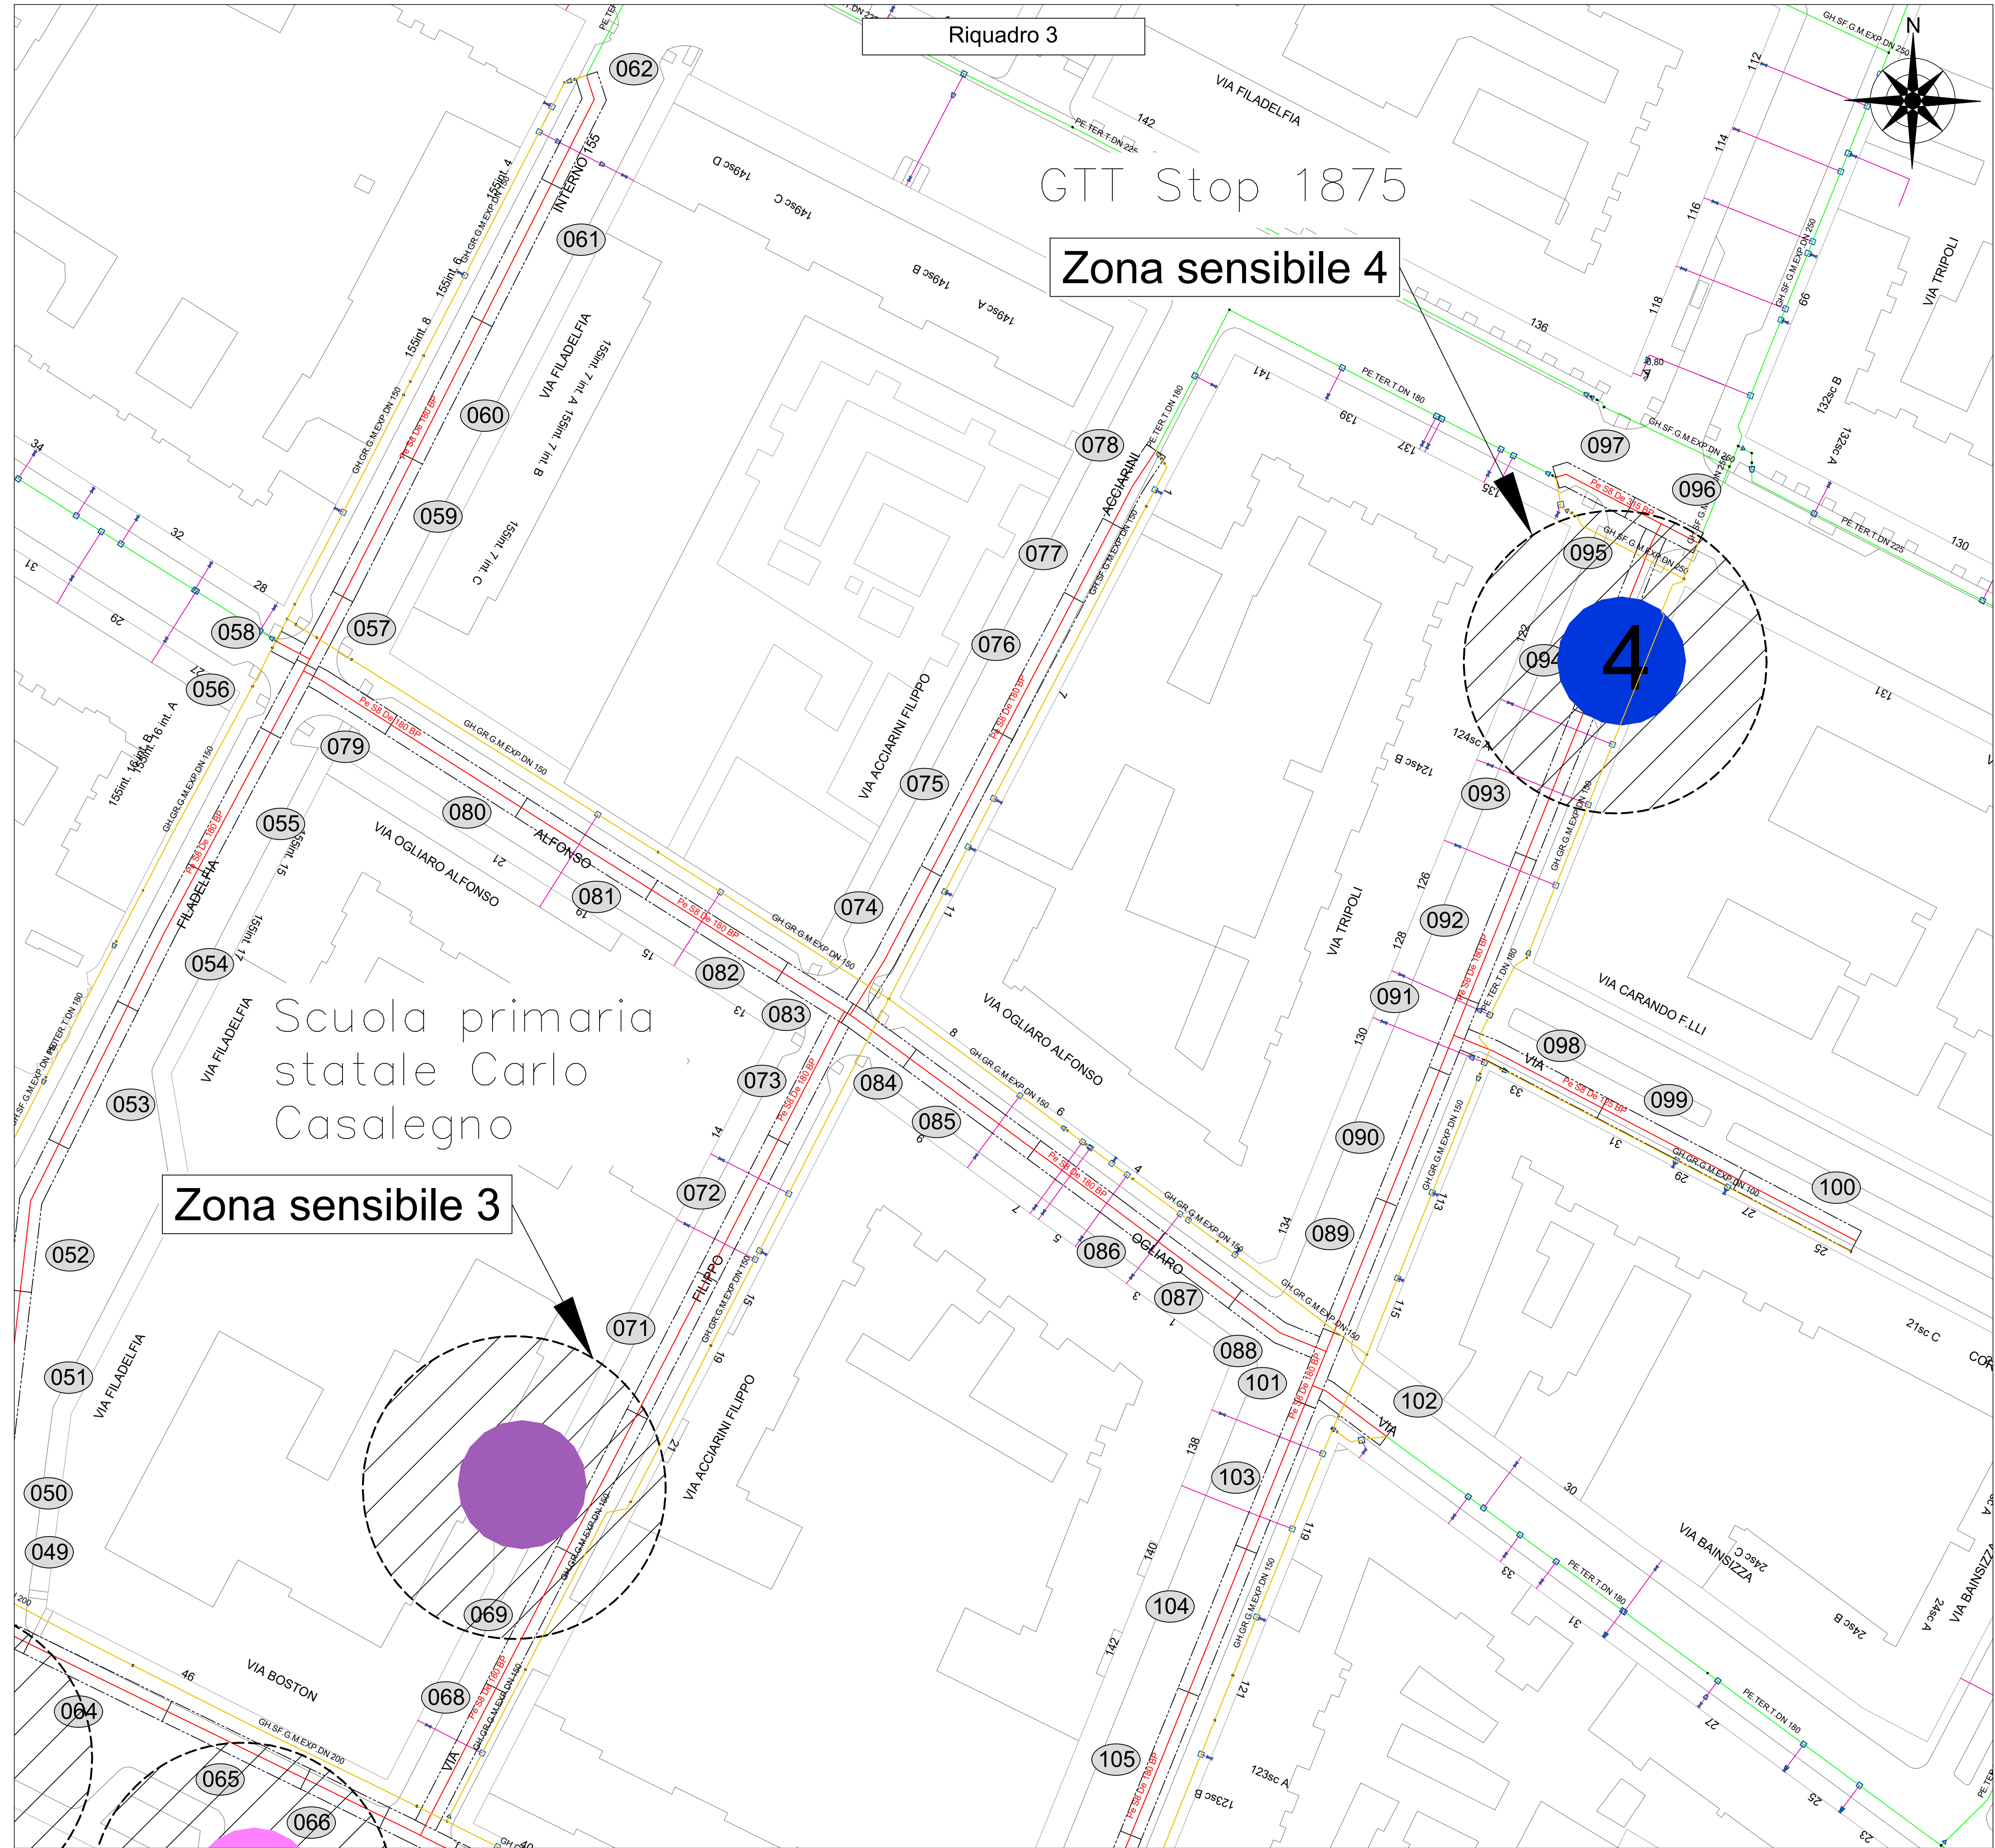

KEY PLAN


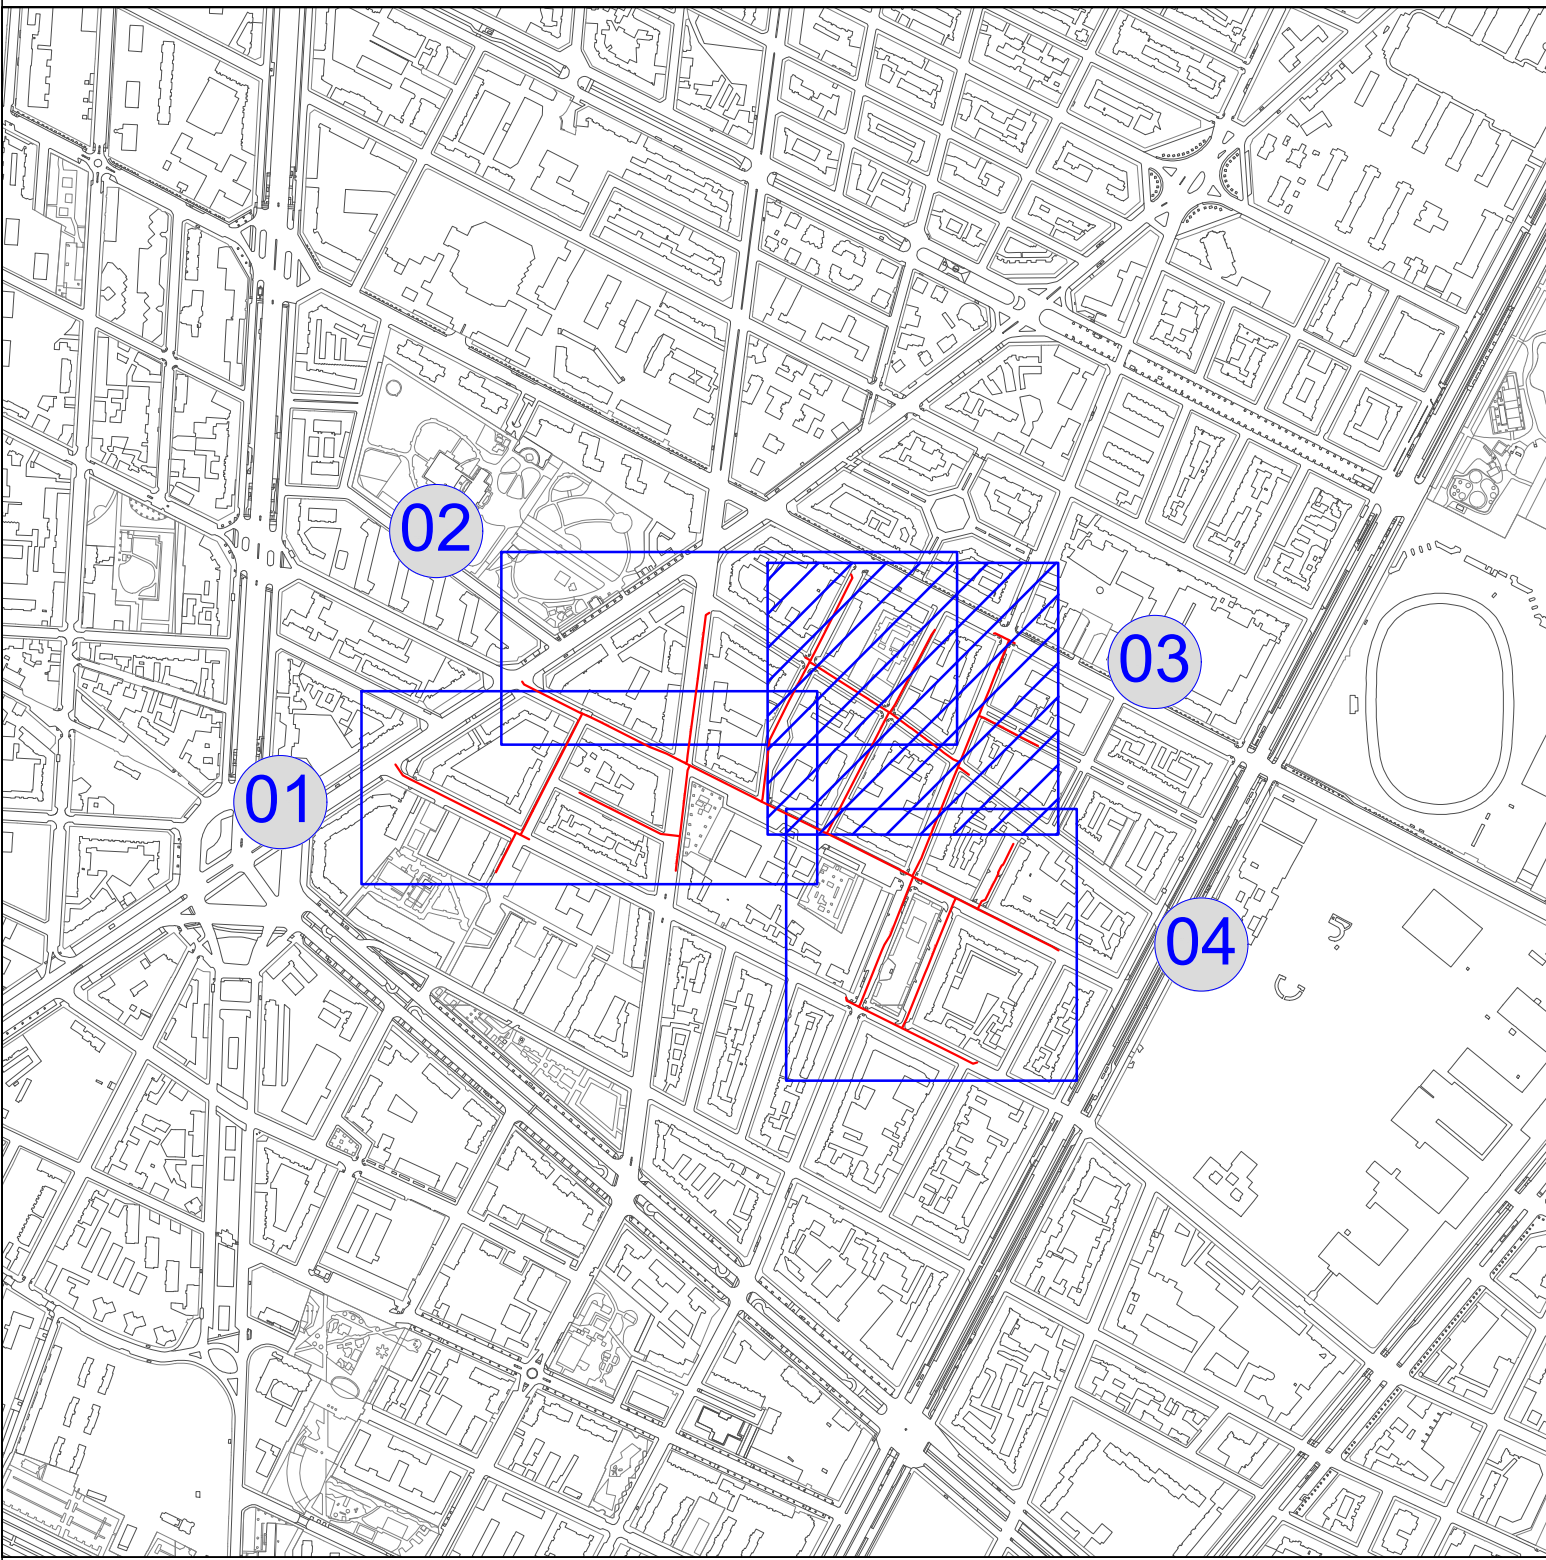


LEGENDA

	Rete nuova		Chiese
	Rete da rimuovere		Carabinieri
	Metro		Vigili del fuoco
	Scuole		Cimiteri
	GTT stop		Polizia municipale
	Musei		Ospedali
	Università		Stazioni ferroviarie
	Biblioteche		Altri luoghi di culto
	Uffici postali		Zona sensibile
	Impianti Sportivi		Aree di lavoro

Zone sensibili				
Zona di lavoro	Zona sensibile	Via/Strada/Piazza	Dettaglio	Nota
069-070	3	Via Acciari Filippo	Scuola Primaria statale Carlo Casalegno	Planificare le attività di cantiere fuori dall'orario scolastico
093-094-095-096	4	Via Tripoli	GTT Stop 1875	Richiedere lo spostamento della fermata prima o dopo il punto di interferenza

LEARDI	Progettista: Alessandro Leardi Ordine degli Ingegneri di Alessandria mat. 61610/01-101 Firma	Unità Responsabile della Progettazione							
		INGEREAL-INGE-PROGRE							
	Progetto n°: 22-0320-3E-00-001272 WBS: SI.20.10300.02.1109 ALLEGATO n°: 30.2								
Nome File: 22-03-20-3E-00-001272-01.dwg	Descrizione: Emissione per modifiche ed integrazioni	1	25	11	22	L.Olmi	L.Cartasegna	A.Leardi	
Formato: A1	Descrizione: Emissione per commenti	0	04	11	22	L.Olmi	L.Cartasegna	A.Leardi	
Scala 1 : 500	Comm. : 2464	Rev.	G.	M.	A.	Redatto	Controllato	Approvato	
Committente	Comune di TORINO Vie Varie Progetto Esecutivo SOSTITUZIONE RETE IN BP (L=2504,78 m) GARA ATEM TO1 Intervento n° SI-036213-001272-TSS-TORIN036								
Italgas Reti									

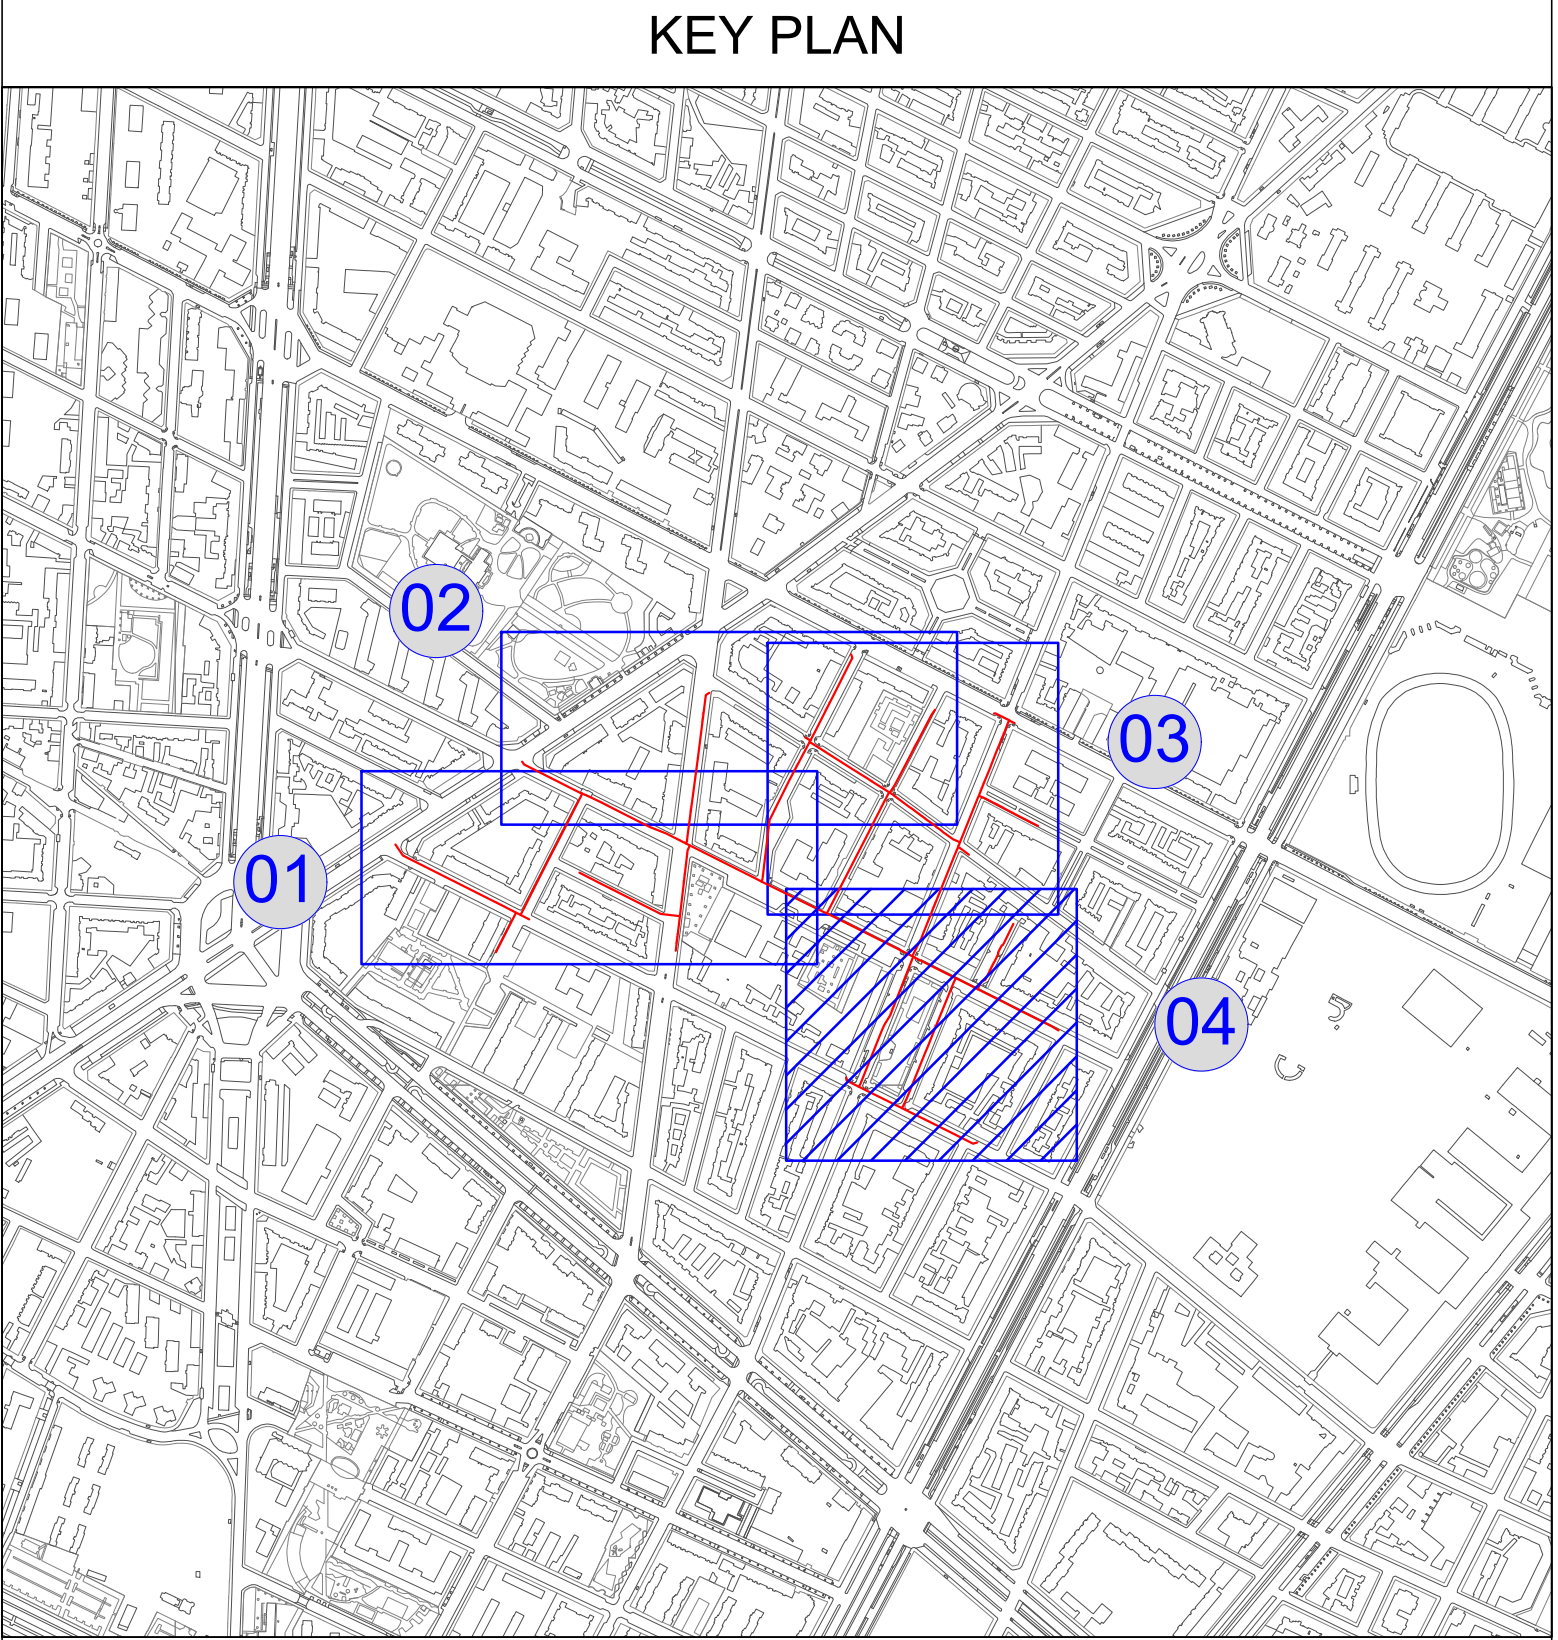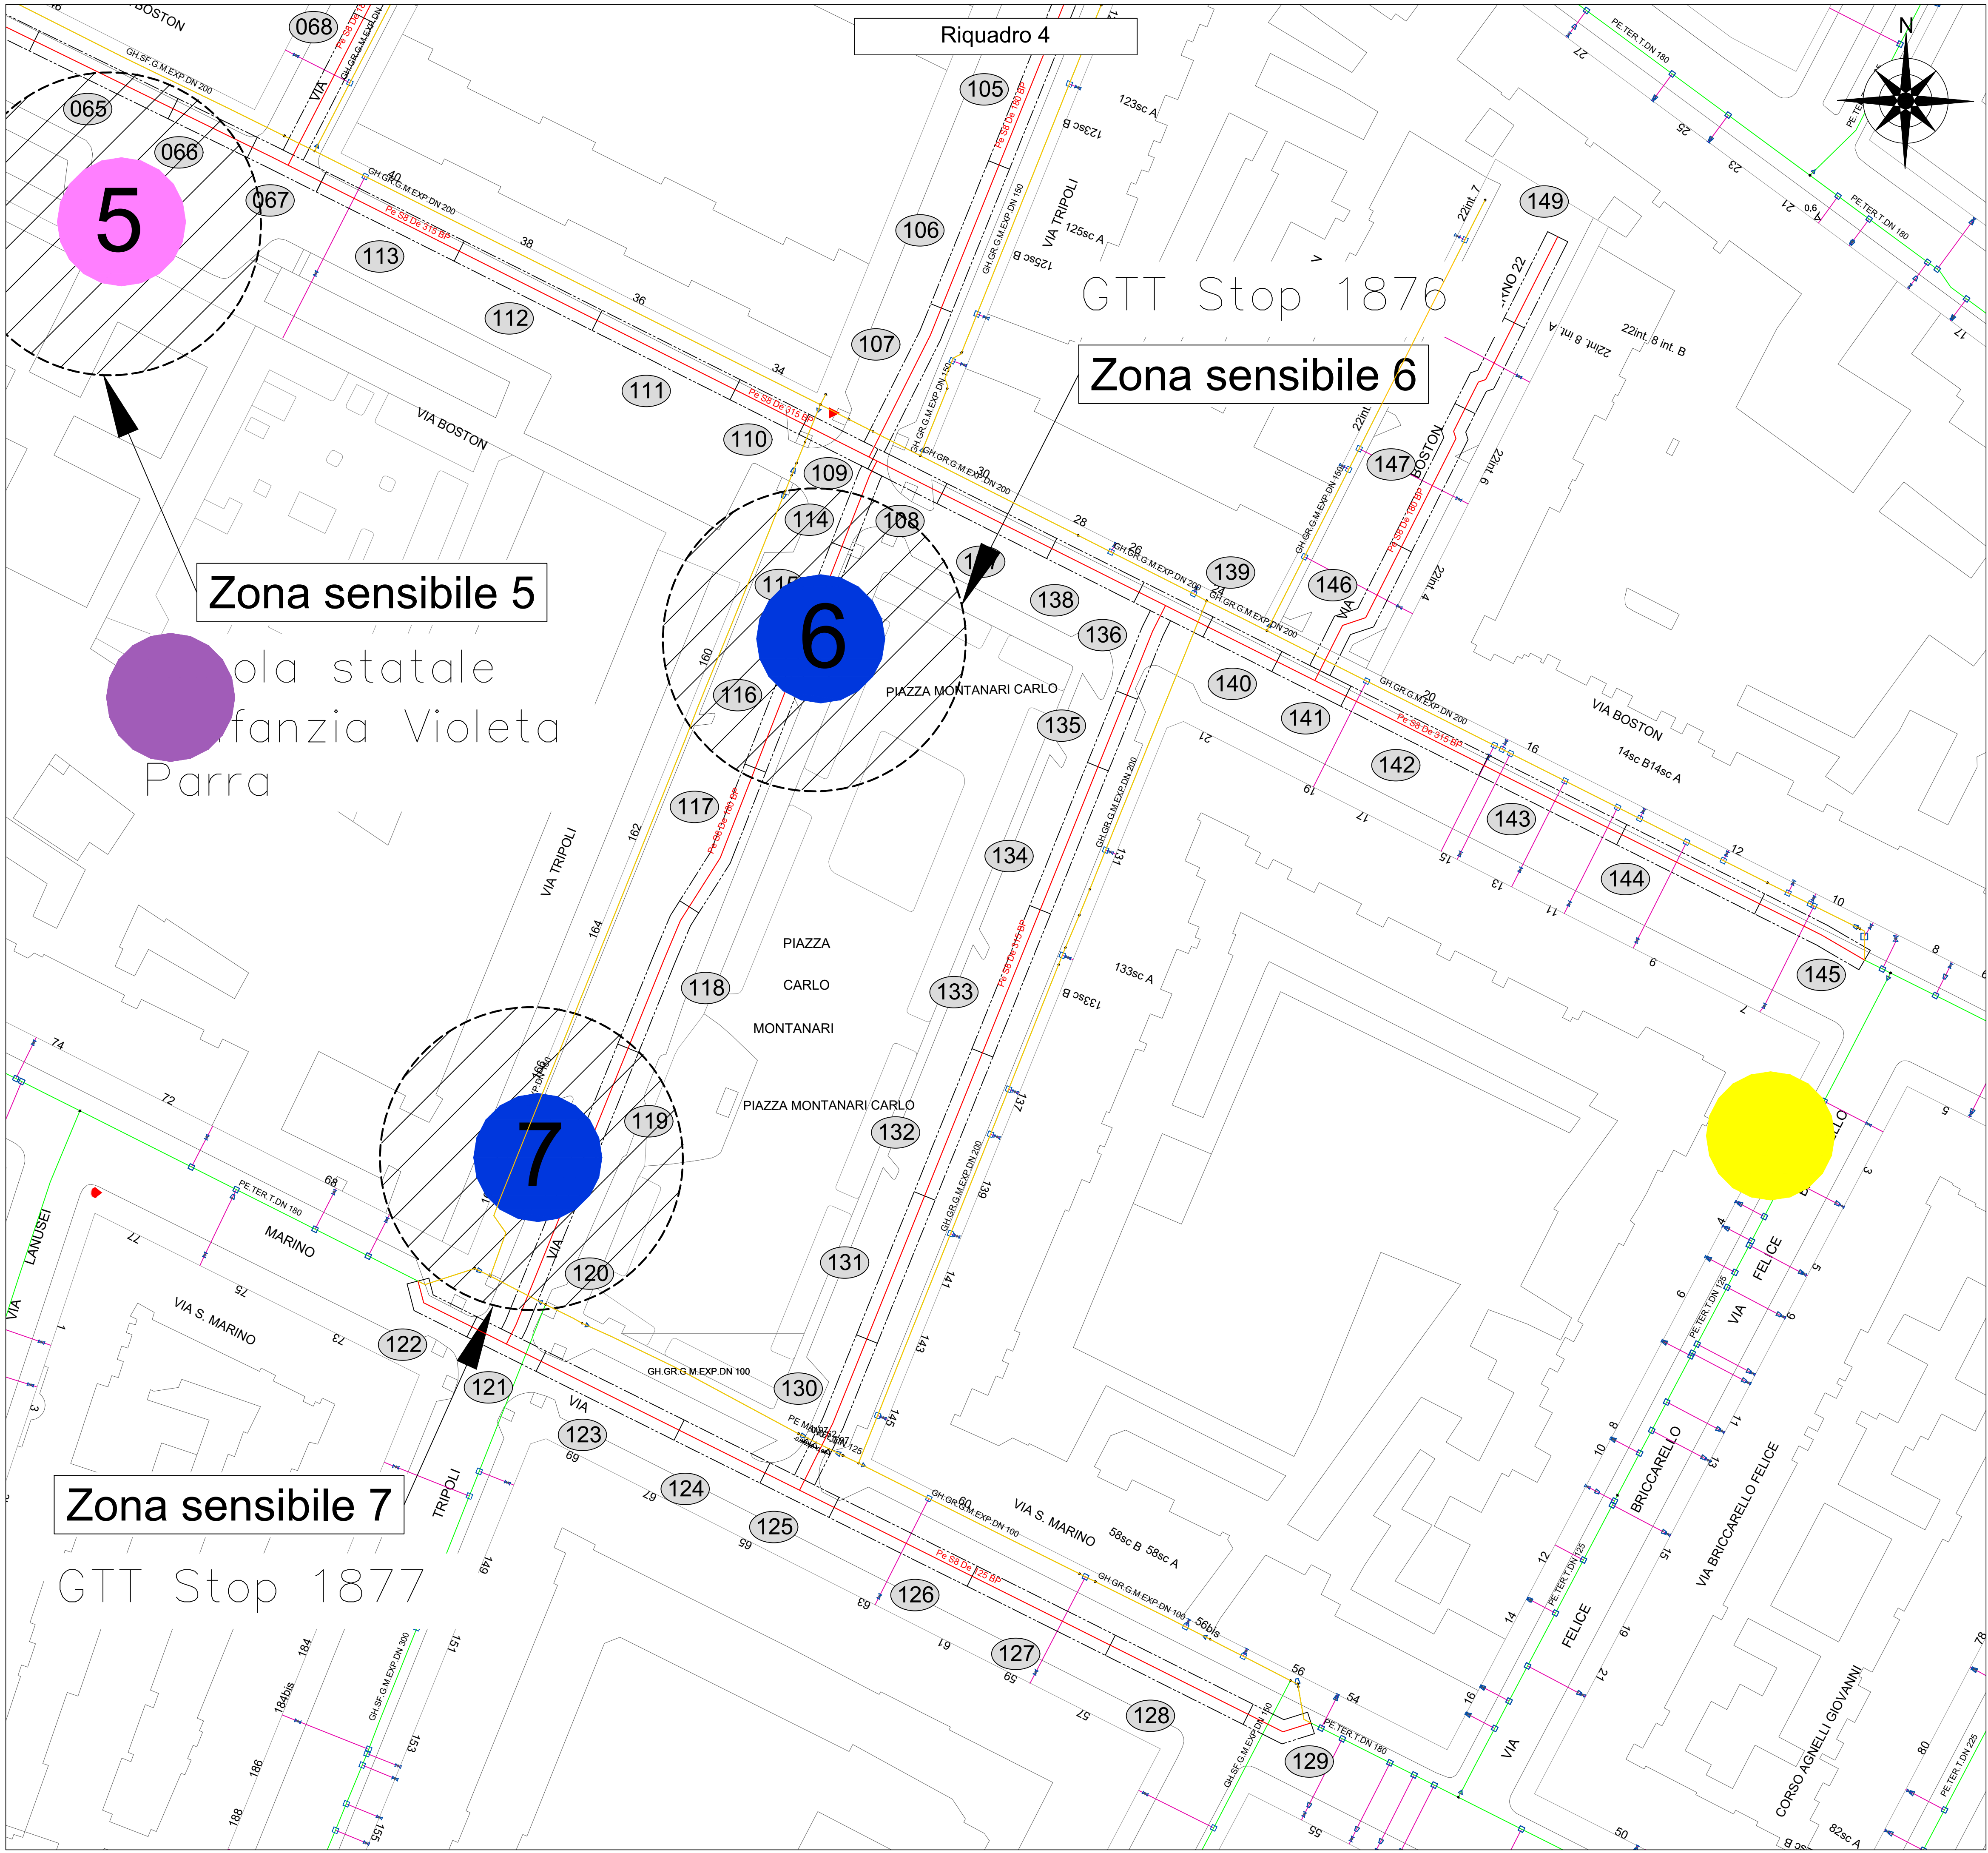

KEY PLAN

LEGENDA

- Rete nuova

Rete da rimuovere

Metro

Scuole

GTT stop

Musei

Università

Biblioteche

Uffici postali

Impianti Sportivi
- Chiese

Carabinieri

Vigili del fuoco

Cimiteri

Polizia municipale

Ospedali

Stazioni ferroviarie

Altri luoghi di culto

Zona sensibile

Arete di lavoro

Zone sensibili				
Zona di lavoro	Zona sensibile	Via/Strada/Piazza	Dettaglio	Nota
065-066	5	Via Boston	Scuola statale d'infanzia Violeta Parra	Planificare le attività di cantiere fuori dall'orario scolastico
114-115-116	6	Via Tripoli	GTT Stop 1876	Richiedere lo spostamento della fermata prima o dopo il punto di interferenza
119-120	7	Via Tripoli	GTT Stop 1877	Richiedere lo spostamento della fermata prima o dopo il punto di interferenza

Zona sensibile 7

Zona sensibile 5

Zona sensibile 6

LEARDI

Progetto n°:
22-0320-3E-00-001272
WBS:
SI.20.10300.02.1109
ALLEGATO n°: 30.3
Formato: A1 Scala 1 : 500
Comittente

Progettista:
Ing. Alessandro Leardi
Ordine degli Ingegneri di Alessandria
matricola n° 41764

Unità Responsabile della Progettazione
INGEREAL-INGE-PROGRE

Descrizione:
Emissione per modifiche ed integrazioni
Descrizione:
Emissione per commenti
Comm.: 2464

1	25	11	22	L.Olm	L.Cartasegna	A.Leardi
0	04	11	22	L.Olm	L.Cartasegna	A.Leardi
Rev.	G. M. A.	Redatto	Controllato	Approvato		

Comune di TORINO
Via Varie
Progetto Esecutivo
SOSTITUZIONE RETE IN BP (L=2504.78 m) GARA ATEM TO1
Intervento n° SI-036213-001272-TSS-TORIN036
Planimetria zone sensibili - Tavola 3

INGEGNERI PROV. ALESSANDRIA
SEZIONE
CIVILE AMB. INDUSTRIALE
ALESSANDRO LEARDI
matricola n° 41764

Il presente elaborato è di proprietà aziendale - La società tutelerà i propri diritti a termini di legge.