
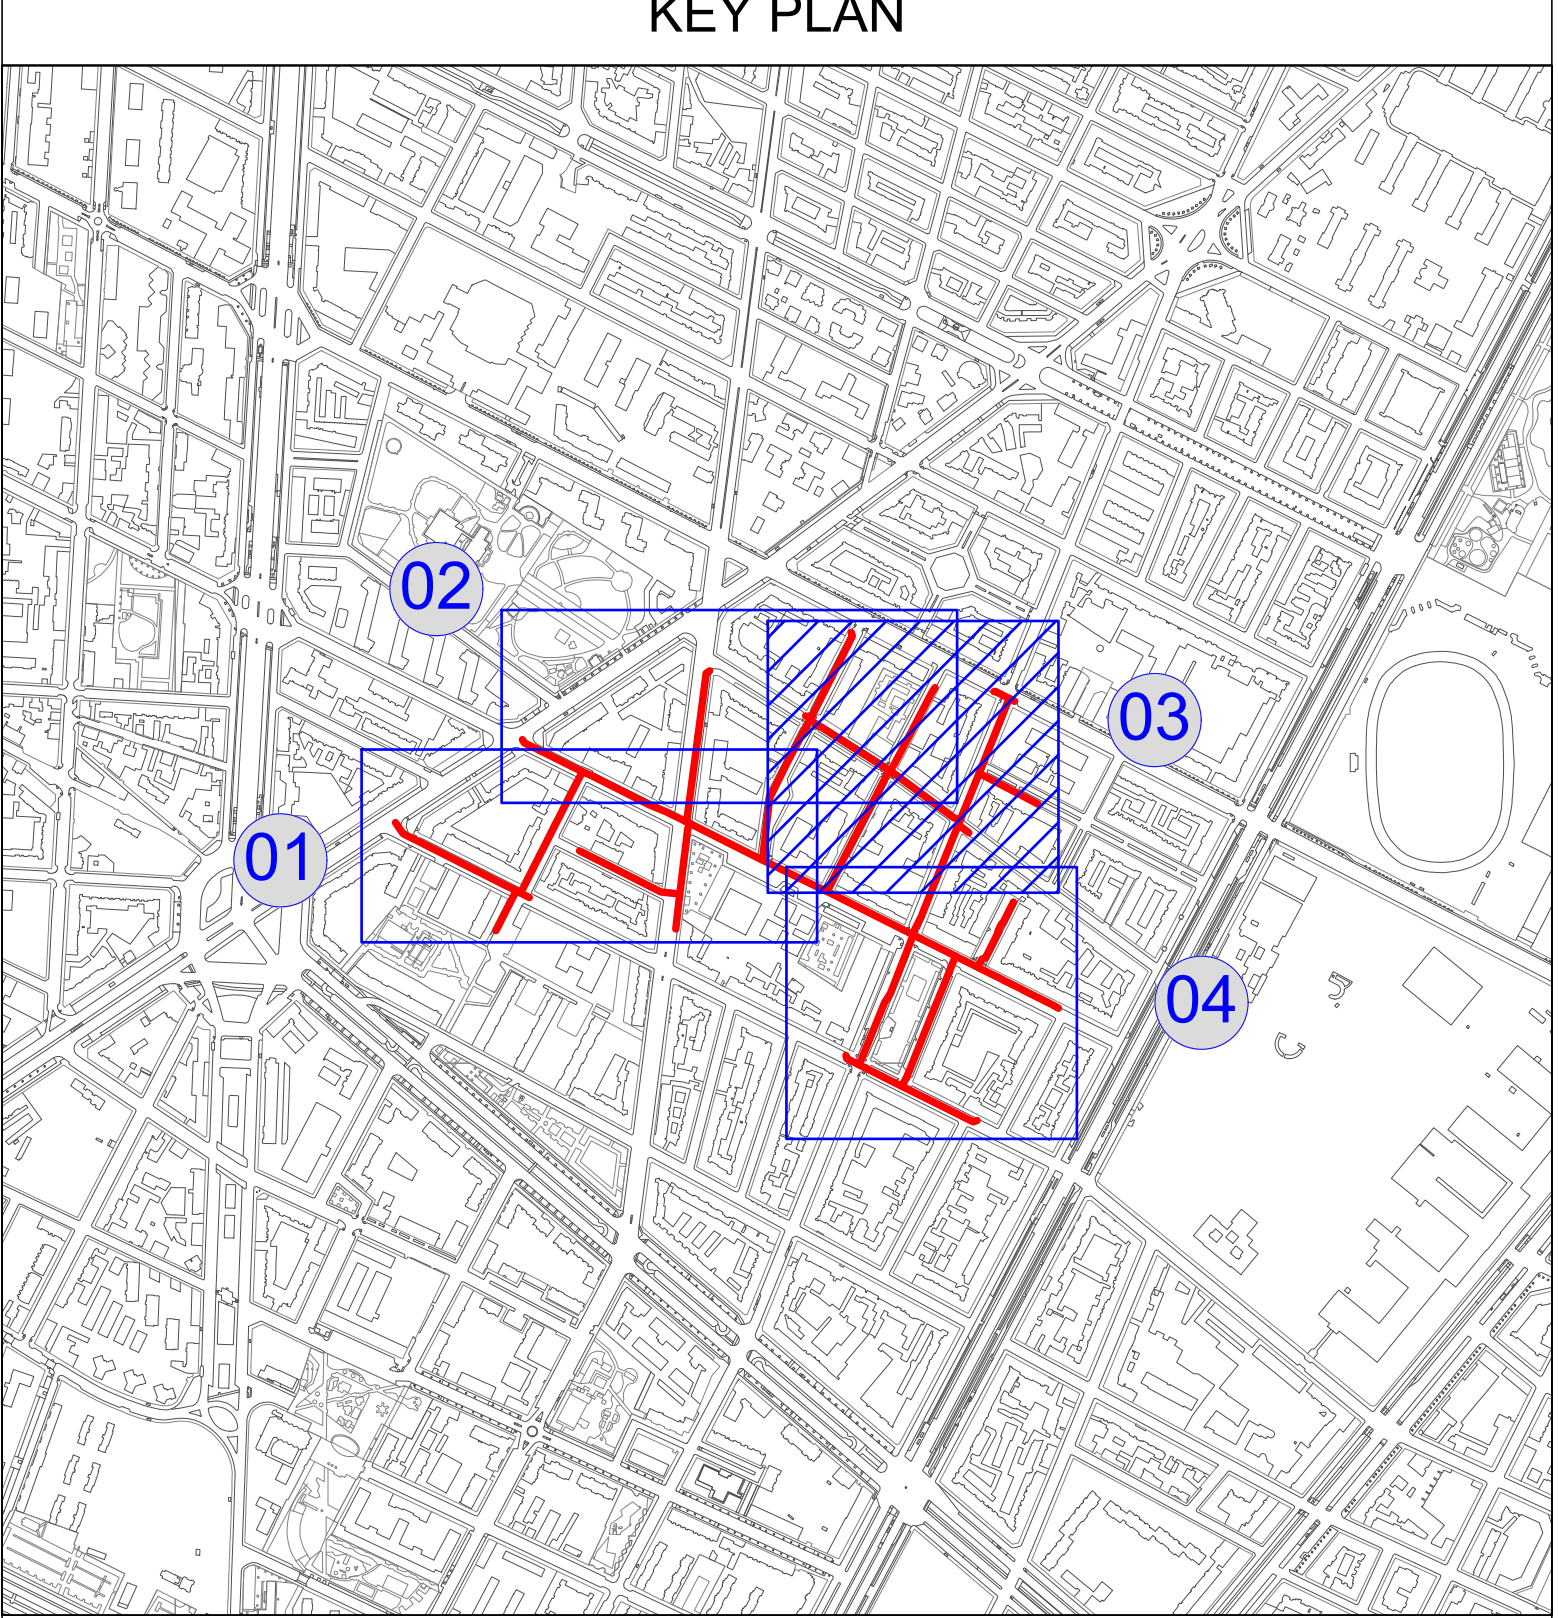



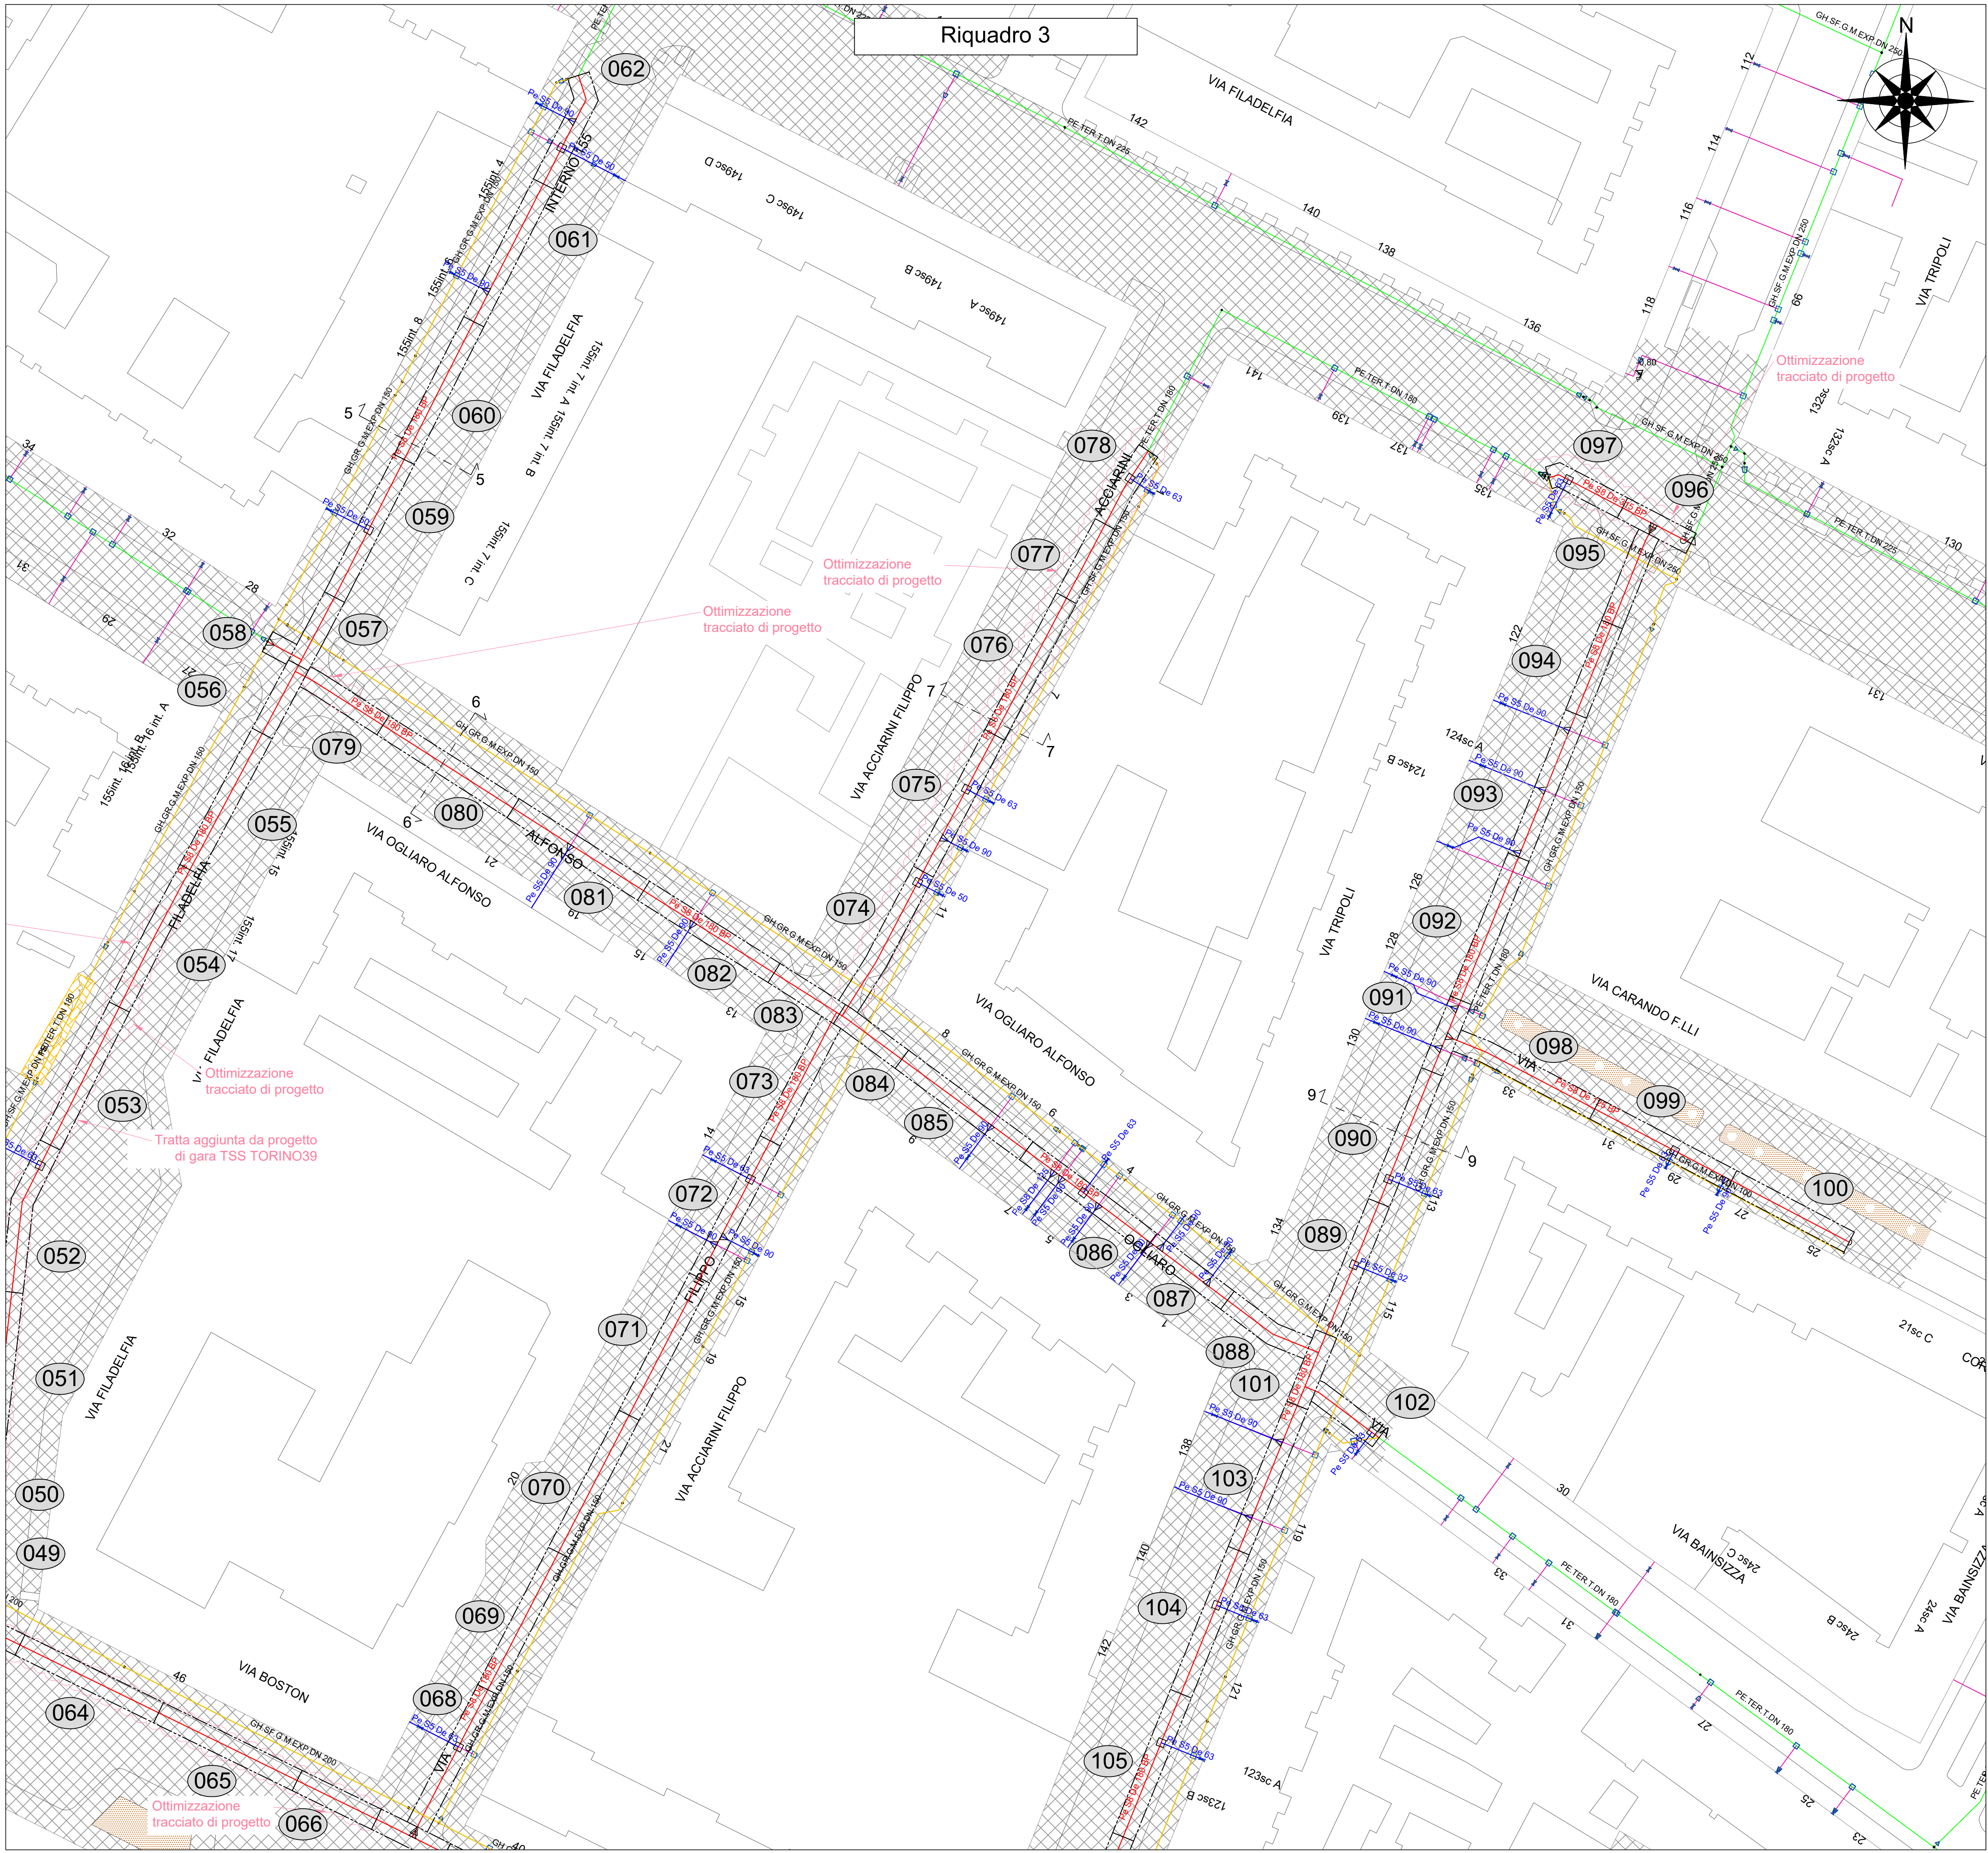


LEGENDA

	Rete in progetto BP		n° Zona di lavoro
	Rete in dismissione BP		Asfalto
	Zona di lavoro		Sterrato/area verde
			Autobloccanti/ammattionato

	Progettista: Alessandro Leardi matricola n° 14941 Firma	Unità Responsabile della Progettazione			
	INGEREAL-INGE-PROGRE				
Progetto n°: 22-0320-3E-00-001272 WBS: SI.20.10300.02.1109 ALLEGATO n°: 4.2					
Nome File: 04.dwg	Descrizione:				
Formato: A1	Emissione per commenti				
Committente	Comm.: 2464				
		Comune di TORINO (TO) Vie Varie Progetto Esecutivo SOSTITUZIONE RETE IN BP (L=2504.78 m) GARA ATEM TO1 Intervento n° SI-036213-001272-TSS-TORIN036 Planimetria pavimentazioni e zone di lavoro - Tavola 2			

Il presente elaborato è di proprietà aziendale - La società tutelerà i propri diritti a termini di legge.

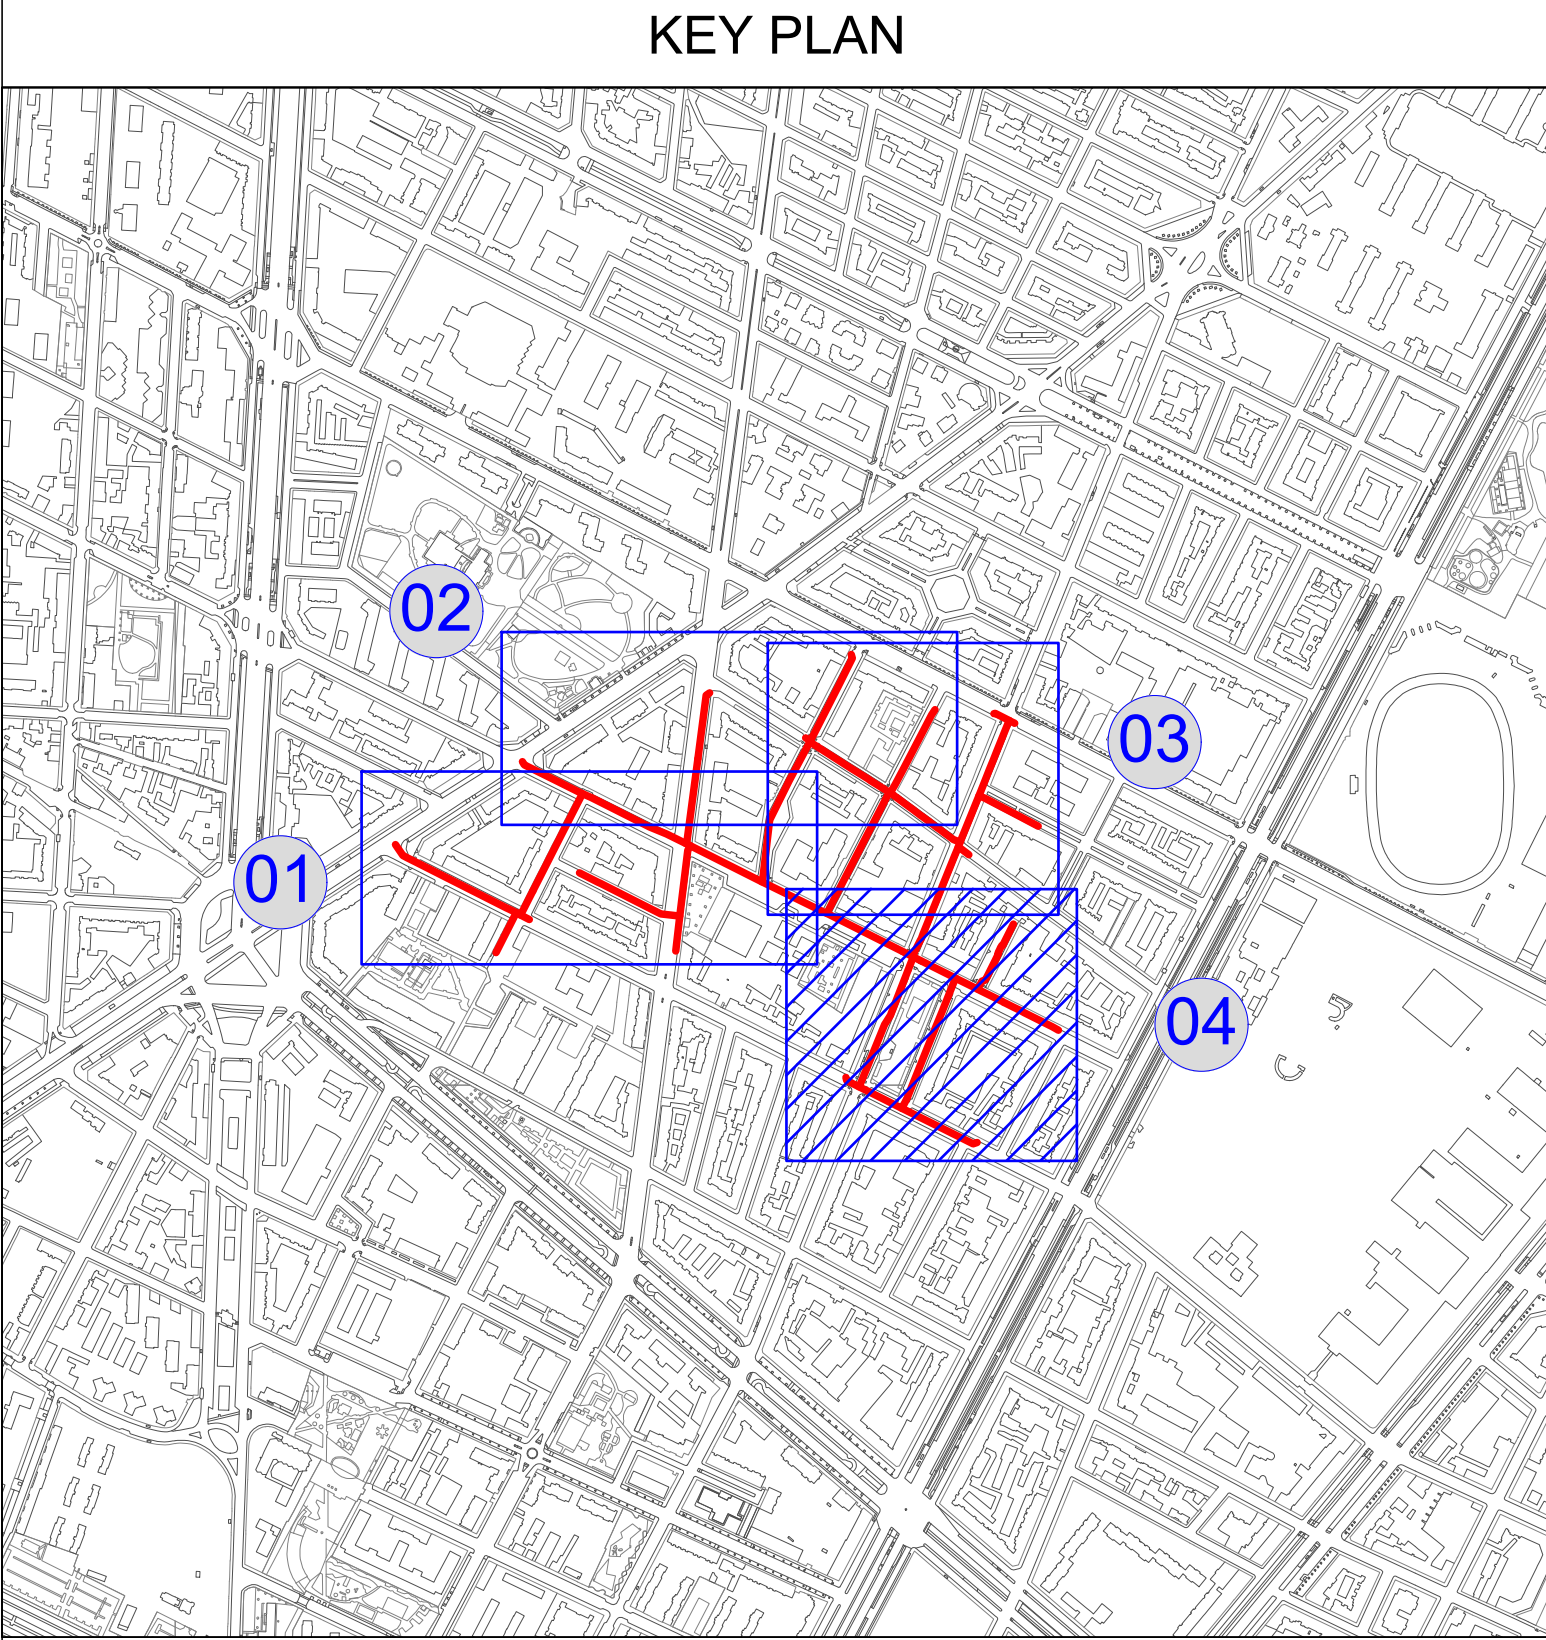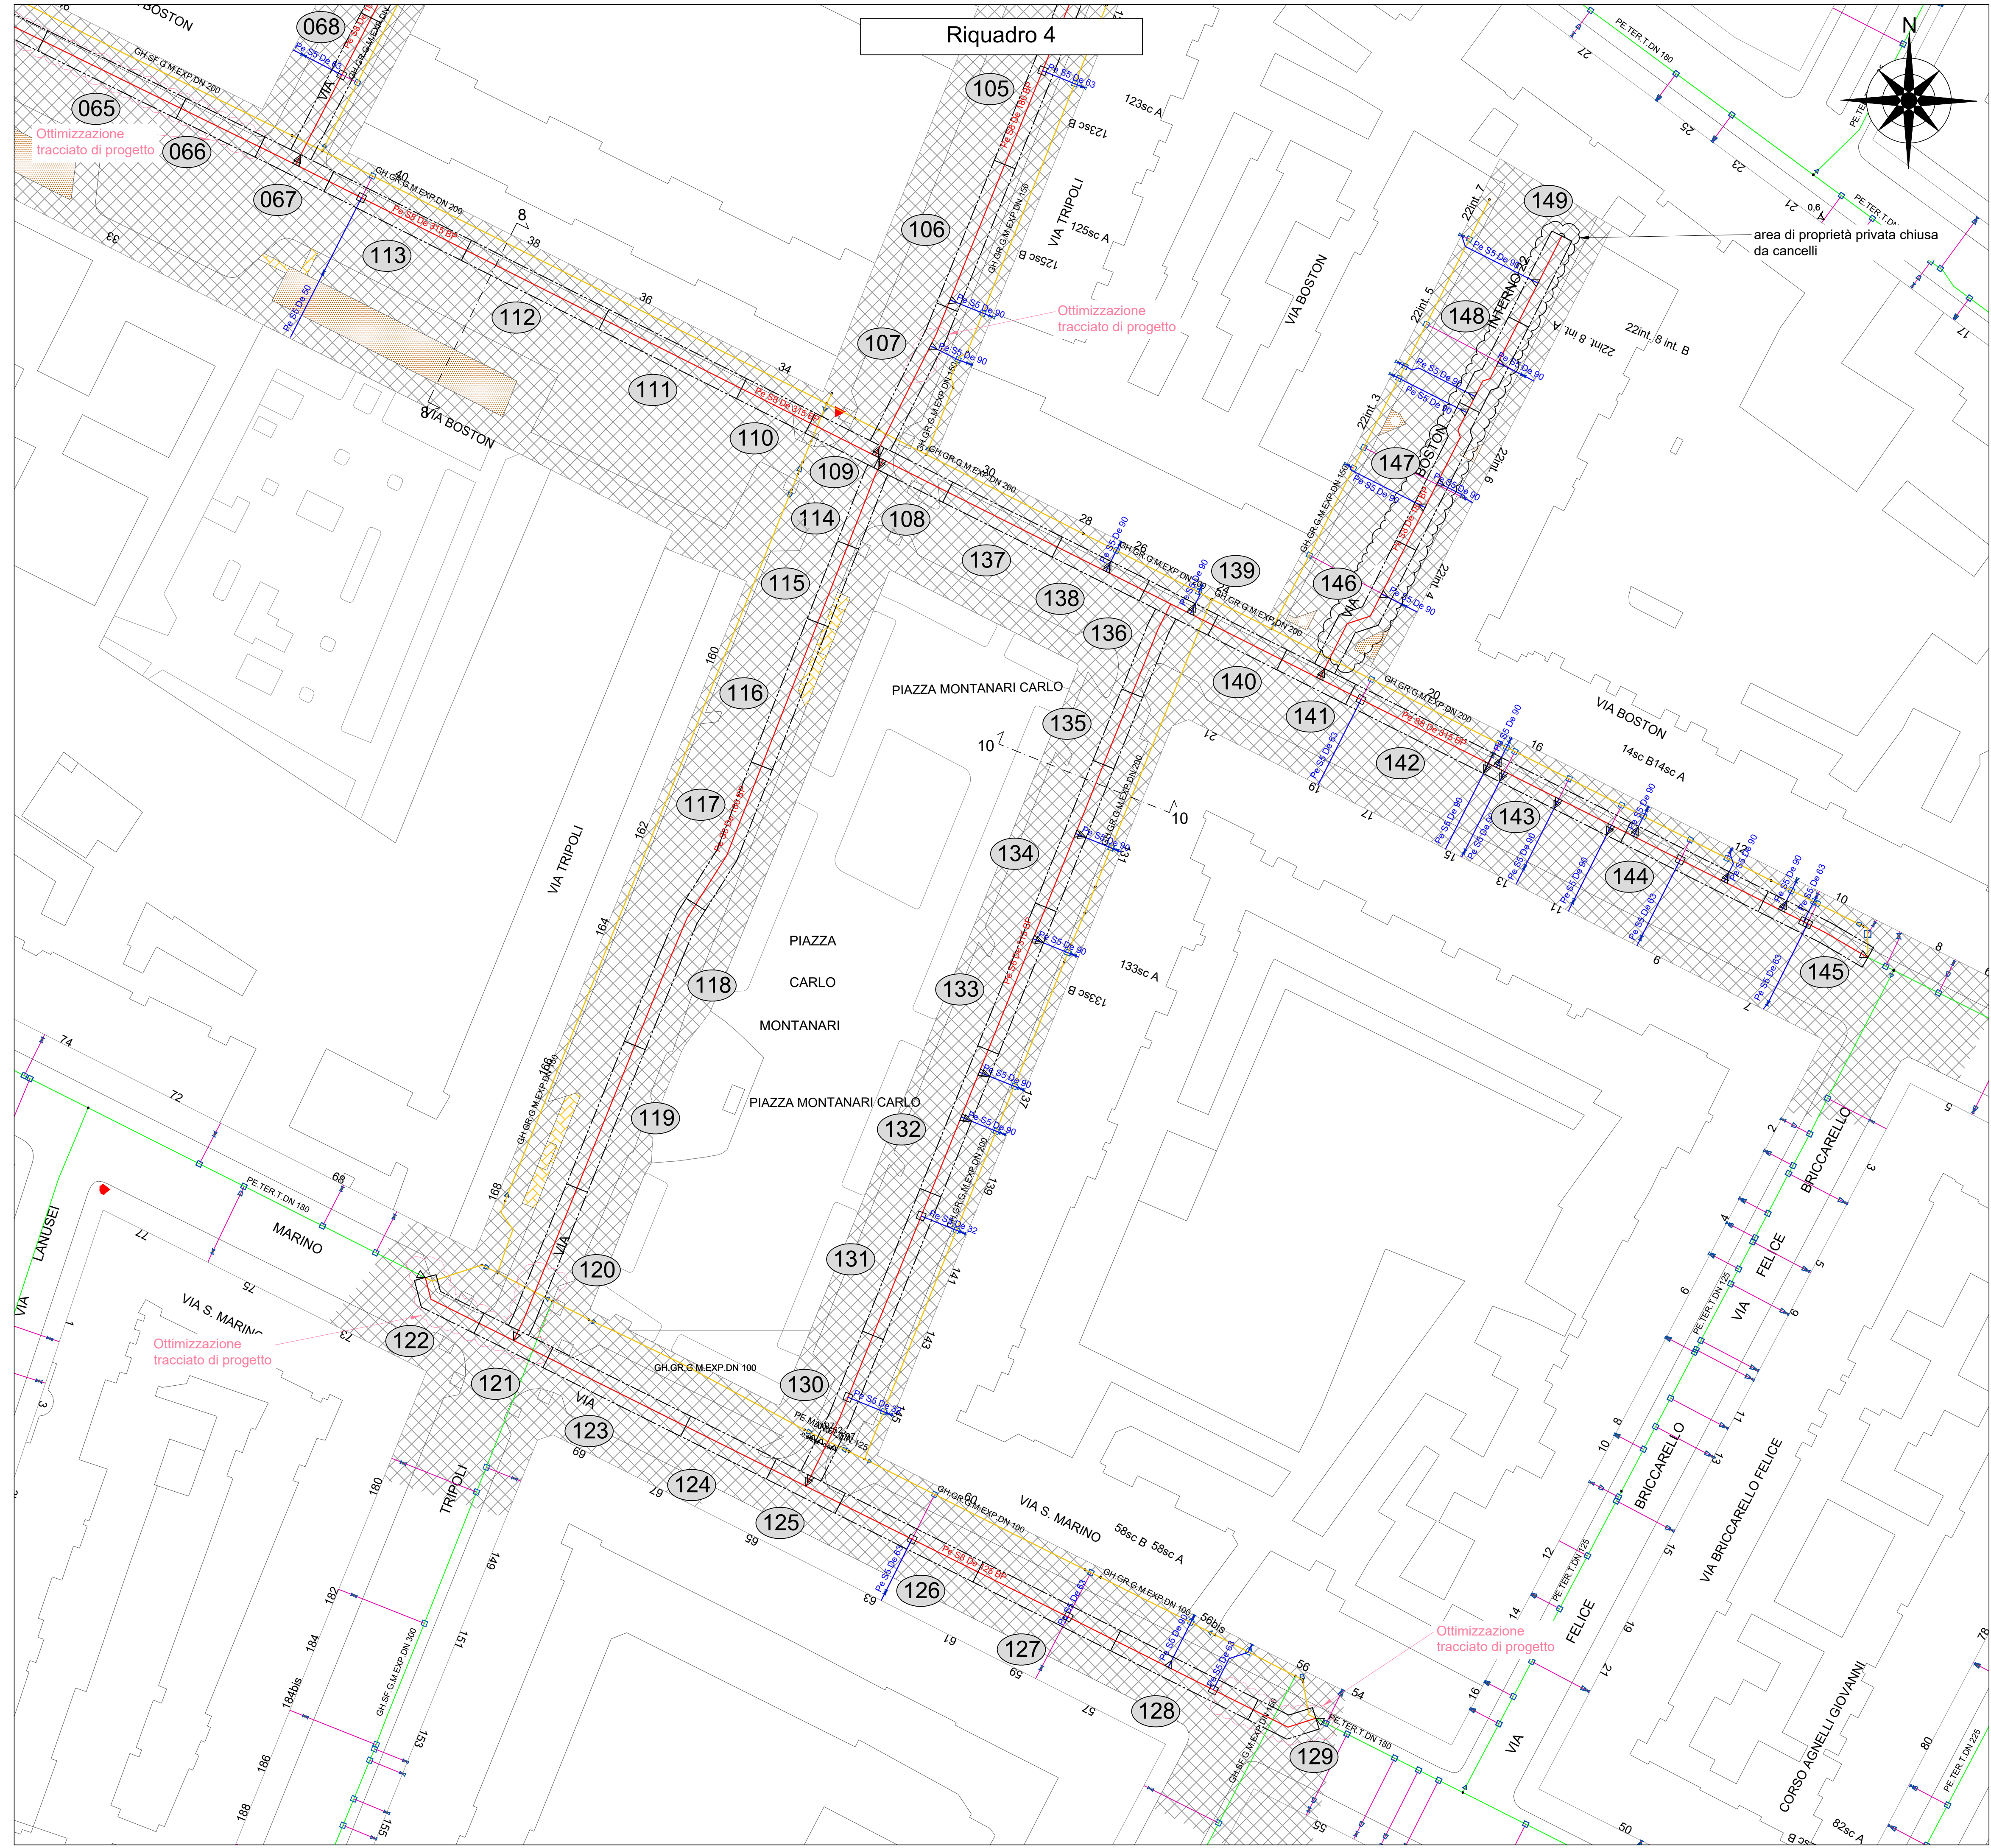

LEGENDA

	Rete in progetto BP		n° Zona di lavoro
	Rete in dismissione BP		Asfalto
	Zona di lavoro		Sterrato/area verde
			Autobloccanti/ammattionato

	Progettista: ALESSANDRO LEARDI Ordine degli Ingegneri di Alessandria matr. n° 101 Firma	Unità Responsabile della Progettazione INGEREAL-INGE-PROGRE	
	Comune di TORINO (TO) Vie Varie Progetto Esecutivo SOSTITUZIONE RETE IN BP (L=2504,78 m) GARA ATEM TO1 Intervento n° SI-036213-001272-TSS-TORIN036 Planimetria pavimentazioni e zone di lavoro - Tavola 3		
Progetto n°: 22-0320-3E-00-001272 WBS: SI-2010300.02.1109 ALLEGATO n°: 4.3	Descrizione: Emissione per commenti Comm.: 2464	0 04 11 22 Rev. G. M. A. Redatto Controllato Approvato	A.Cappelletti L.Carlasegna A.Leardi

Zone di lavoro e pavimentazioni				
n.	dati condotta	quantità [m]	lato strada	tipo di pavimentazione
1	Pe S8 De 180 BP	20	Sinistra	Asfalto
2	Pe S8 De 180 BP	24	Sinistra	Asfalto
3	Pe S8 De 180 BP	24	Sinistra	Asfalto
4	Pe S8 De 180 BP	24	Sinistra	Asfalto
5	Pe S8 De 180 BP	24	Sinistra	Asfalto
6	Pe S8 De 180 BP	24	Sinistra	Asfalto
7	Pe S8 De 180 BP	12	Sinistra	Asfalto
7	Pe S8 De 180 BP	2	Attraversamento	Asfalto
8	Pe S8 De 180 BP	12	Attraversamento	Asfalto
8	Pe S8 De 125 BP	1	Attraversamento	Asfalto
9	Pe S8 De 180 BP	5	Attraversamento	Asfalto
9	Pe S8 De 180 BP	18	Destra	Asfalto
10	Pe S8 De 180 BP	21	Destra	Asfalto
11	Pe S8 De 125 BP	24	Sinistra	Asfalto
12	Pe S8 De 125 BP	24	Sinistra	Asfalto
13	Pe S8 De 125 BP	24	Sinistra	Asfalto
14	Pe S8 De 125 BP	24	Sinistra	Asfalto
15	Pe S8 De 125 BP	24	Sinistra	Asfalto
16	Pe S8 De 125 BP	14	Sinistra	Asfalto
16	Pe S8 De 125 BP	5	Attraversamento	Asfalto
17	Pe S8 De 125 BP	2	Attraversamento	Asfalto
17	Pe S8 De 315 BP	12	Centro	Asfalto
18	Pe S8 De 315 BP	24	Centro	Asfalto
19	Pe S8 De 315 BP	24	Centro	Asfalto
20	Pe S8 De 315 BP	17	Centro	Asfalto
21	Pe S8 De 315 BP	12	Sinistra	Asfalto
22	Pe S8 De 315 BP	24	Sinistra	Asfalto
23	Pe S8 De 315 BP	24	Sinistra	Asfalto
24	Pe S8 De 315 BP	24	Sinistra	Asfalto
25	Pe S8 De 315 BP	20	Sinistra	Asfalto
25	Pe S8 De 315 BP	4	Attraversamento	Asfalto
26	Pe S8 De 315 BP	12	Attraversamento	Asfalto
26	Pe S8 De 180 BP	2	Attraversamento	Asfalto
27	Pe S8 De 315 BP	12	Sinistra	Asfalto
27	Pe S8 De 180 BP	2	Attraversamento	Asfalto
28	Pe S8 De 180 BP	9	Attraversamento	Asfalto
28	Pe S8 De 180 BP	15	Sinistra	Asfalto
29	Pe S8 De 180 BP	24	Sinistra	Asfalto
30	Pe S8 De 180 BP	24	Sinistra	Asfalto
31	Pe S8 De 180 BP	12	Sinistra	Asfalto
31	Pe S8 De 125 BP	1	Attraversamento	Asfalto
32	Pe S8 De 180 BP	14	Sinistra	Asfalto
33	Pe S8 De 180 BP	13	Sinistra	Asfalto
34	Pe S8 De 125 BP	15	Attraversamento	Asfalto
34	Pe S8 De 125 BP	9	Destra	Asfalto
35	Pe S8 De 125 BP	24	Destra	Asfalto
36	Pe S8 De 125 BP	24	Destra	Asfalto
37	Pe S8 De 125 BP	24	Destra	Asfalto
38	Pe S8 De 125 BP	19	Destra	Asfalto
39	Pe S8 De 180 BP	24	Destra	Asfalto
40	Pe S8 De 180 BP	24	Destra	Asfalto
41	Pe S8 De 180 BP	24	Destra	Asfalto
42	Pe S8 De 180 BP	24	Destra	Asfalto
43	Pe S8 De 180 BP	24	Destra	Asfalto
44	Pe S8 De 180 BP	24	Destra	Asfalto
45	Pe S8 De 180 BP	17	Destra	Asfalto
46	Pe S8 De 315 BP	24	Sinistra	Asfalto
47	Pe S8 De 315 BP	24	Sinistra	Asfalto
48	Pe S8 De 315 BP	24	Sinistra	Asfalto
49	Pe S8 De 180 BP	13	Centro	Asfalto
50	Pe S8 De 180 BP	13	Centro	Asfalto
51	Pe S8 De 180 BP	24	Sinistra	Asfalto
52	Pe S8 De 180 BP	24	Sinistra	Asfalto
53	Pe S8 De 180 BP	24	Sinistra	Asfalto
54	Pe S8 De 180 BP	24	Sinistra	Asfalto
55	Pe S8 De 180 BP	24	Sinistra	Asfalto

Zone di lavoro e pavimentazioni				
n.	dati condotta	quantità [m]	lato strada	tipo di pavimentazione
56	Pe S8 De 180 BP	12	Sinistra	Asfalto
56	Pe S8 De 180 BP	2	Attraversamento	Asfalto
57	Pe S8 De 180 BP	12	Sinistra	Asfalto
57	Pe S8 De 180 BP	2	Attraversamento	Asfalto
58	Pe S8 De 180 BP	4	Destra	Asfalto
59	Pe S8 De 180 BP	24	Sinistra	Asfalto
60	Pe S8 De 180 BP	24	Sinistra	Asfalto
61	Pe S8 De 180 BP	24	Sinistra	Asfalto
62	Pe S8 De 180 BP	19	Sinistra	Asfalto
63	Pe S8 De 315 BP	11	Attraversamento	Asfalto
63	Pe S8 De 180 BP	2	Attraversamento	Asfalto
64	Pe S8 De 315 BP	24	Sinistra	Asfalto
65	Pe S8 De 315 BP	24	Sinistra	Asfalto
66	Pe S8 De 315 BP	14	Sinistra	Asfalto
67	Pe S8 De 315 BP	11	Attraversamento	Asfalto
67	Pe S8 De 180 BP	2	Attraversamento	Asfalto
68	Pe S8 De 180 BP	24	Destra	Asfalto
69	Pe S8 De 180 BP	24	Destra	Asfalto
70	Pe S8 De 180 BP	24	Centro	Asfalto
71	Pe S8 De 180 BP	24	Centro	Asfalto
72	Pe S8 De 180 BP	24	Centro	Asfalto
73	Pe S8 De 180 BP	21	Centro	Asfalto
74	Pe S8 De 180 BP	24	Destra	Asfalto
75	Pe S8 De 180 BP	24	Destra	Asfalto
76	Pe S8 De 180 BP	24	Destra	Asfalto
77	Pe S8 De 180 BP	13	Destra	Asfalto
78	Pe S8 De 180 BP	14	Destra	Asfalto
79	Pe S8 De 180 BP	14	Centro	Asfalto
80	Pe S8 De 180 BP	24	Centro	Asfalto
81	Pe S8 De 180 BP	24	Centro	Asfalto
82	Pe S8 De 180 BP	24	Centro	Asfalto
83	Pe S8 De 180 BP	7	Centro	Asfalto
83	Pe S8 De 180 BP	4	Attraversamento	Asfalto
83	Pe S8 De 180 BP	2	Attraversamento	Asfalto
84	Pe S8 De 180 BP	12	Centro	Asfalto
84	Pe S8 De 180 BP	2	Attraversamento	Asfalto
85	Pe S8 De 180 BP	24	Centro	Asfalto
86	Pe S8 De 180 BP	24	Centro	Asfalto
87	Pe S8 De 180 BP	15	Centro	Asfalto
88	Pe S8 De 180 BP	9	Centro	Asfalto
88	Pe S8 De 180 BP	5	Attraversamento	Asfalto
89	Pe S8 De 180 BP	22	Destra	Asfalto
90	Pe S8 De 180 BP	22	Destra	Asfalto
91	Pe S8 De 180 BP	12	Destra	Asfalto
91	Pe S8 De 125 BP	2	Attraversamento	Asfalto
92	Pe S8 De 180 BP	4	Attraversamento	Asfalto
92	Pe S8 De 180 BP	19	Destra	Asfalto
93	Pe S8 De 180 BP	24	Destra	Asfalto
94	Pe S8 De 180 BP	15	Destra	Asfalto
95	Pe S8 De 180 BP	15	Destra	Asfalto
96	Pe S8 De 315 BP	5	Attraversamento	Asfalto
96	Pe S8 De 315 BP	5	Sinistra	Asfalto
96	Pe S8 De 180 BP	2	Attraversamento	Asfalto
97	Pe S8 De 315 BP	13	Sinistra	Asfalto
98	Pe S8 De 125 BP	24	Destra	Asfalto
99	Pe S8 De 125 BP	24	Destra	Asfalto
100	Pe S8 De 125 BP	21	Destra	Asfalto
101	Pe S8 De 180 BP	12	Attraversamento	Asfalto
101	Pe S8 De 180 BP	2	Attraversamento	Asfalto
101	Pe S8 De 180 BP	2	Attraversamento	Asfalto
102	Pe S8 De 180 BP	12	Destra	Asfalto
103	Pe S8 De 180 BP	24	Sinistra	Asfalto
104	Pe S8 De 180 BP	24	Sinistra	Asfalto
105	Pe S8 De 180 BP	24	Sinistra	Asfalto
106	Pe S8 De 180 BP	24	Sinistra	Asfalto
107	Pe S8 De 180 BP	24	Sinistra	Asfalto

Zone di lavoro e pavimentazioni				
n.	dati condotta	quantità [m]	lato strada	tipo di pavimentazione
108	Pe S8 De 315 BP	12	Destra	Asfalto
108	Pe S8 De 180 BP	2	Attraversamento	Asfalto
109	Pe S8 De 315 BP	12	Destra	Asfalto
109	Pe S8 De 180 BP	2	Attraversamento	Asfalto
110	Pe S8 De 315 BP	12	Destra	Asfalto
111	Pe S8 De 315 BP	24	Destra	Asfalto
112	Pe S8 De 315 BP	24	Destra	Asfalto
113	Pe S8 De 315 BP	24	Destra	Asfalto
114	Pe S8 De 180 BP	6	Attraversamento	Asfalto
114	Pe S8 De 180 BP	7	Sinistra	Asfalto
115	Pe S8 De 180 BP	13	Sinistra	Asfalto
116	Pe S8 De 180 BP	24	Sinistra	Asfalto
117	Pe S8 De 180 BP	24	Sinistra	Asfalto
118	Pe S8 De 180 BP	24	Centro	Asfalto
119	Pe S8 De 180 BP	24	Centro	Asfalto
120	Pe S8 De 180 BP	24	Centro	Asfalto
121	Pe S8 De 125 BP	12	Attraversamento	Asfalto
121	Pe S8 De 180 BP	2	Attraversamento	Asfalto
122	Pe S8 De 125 BP	12	Destra	Asfalto
123	Pe S8 De 125 BP	24	Centro	Asfalto
124	Pe S8 De 125 BP	15	Centro	Asfalto
125	Pe S8 De 125 BP	12	Attraversamento	Asfalto
125	Pe S8 De 315 BP	2	Attraversamento	Asfalto
126	Pe S8 De 125 BP	24	Centro	Asfalto
127	Pe S8 De 125 BP	24	Centro	Asfalto
128	Pe S8 De 125 BP	24	Centro	Asfalto
129	Pe S8 De 125 BP	11	Centro	Asfalto
130	Pe S8 De 315 BP	24	Centro	Asfalto
131	Pe S8 De 315 BP	24	Centro	Asfalto
132	Pe S8 De 315 BP	24	Centro	Asfalto
133	Pe S8 De 315 BP	24	Centro	Asfalto
134	Pe S8 De 315 BP	24	Centro	Asfalto
135	Pe S8 De 315 BP	12	Centro	Asfalto
136	Pe S8 De 315 BP	6	Centro	Asfalto
136	Pe S8 De 315 BP	6	Attraversamento	Asfalto
137	Pe S8 De 315 BP	19	Sinistra	Asfalto
138	Pe S8 De 315 BP	15	Sinistra	Asfalto
139	Pe S8 De 315 BP	12	Sinistra	Asfalto
139	Pe S8 De 315 BP	2	Attraversamento	Asfalto
140	Pe S8 De 315 BP	12	Sinistra	Asfalto
141	Pe S8 De 315 BP	12	Attraversamento	Asfalto
141	Pe S8 De 180 BP	2	Attraversamento	Asfalto
142	Pe S8 De 315 BP	24	Sinistra	Asfalto
143	Pe S8 De 315 BP	24	Sinistra	Asfalto
144	Pe S8 De 315 BP	24	Sinistra	Asfalto
145	Pe S8 De 315 BP	19	Sinistra	Asfalto
146	Pe S8 De 180 BP	24	Destra	Asfalto (privato)
147	Pe S8 De 180 BP	24	Destra	Asfalto (privato)
148	Pe S8 De 180 BP	16	Destra	Asfalto (privato)
149	Pe S8 De 180 BP	15	Destra	Asfalto (privato)

	Progettista:	Unità Responsabile della Progettazione					
	Ordine degli Ingegneri di Alessandria						
Progetto n°: 22-0320-3E-00-001272 WBS: SI-20.10300.02.1109 ALLEGATO n°: 4.4	INGEREAL-INGE-PROGRE						
Nome File: 014.png							
Formato: A1	Scala: 1 : -						
Committente							
		Comune di TORINO (TO) Vie Varie Progetto Esecutivo SOSTITUZIONE RETE IN BP (L=2504.78 m) GARA ATEM TO1 Intervento n° SI-036213-001272-TSS-TORIN036 Planimetria pavimentazioni e zone di lavoro - Tavola 4					

0

04

11

22

A.Cappelletti

L.Certasegna

A.Leardi

Rev.

G.

M.

A.

Redatto

Controllato

Approvato