
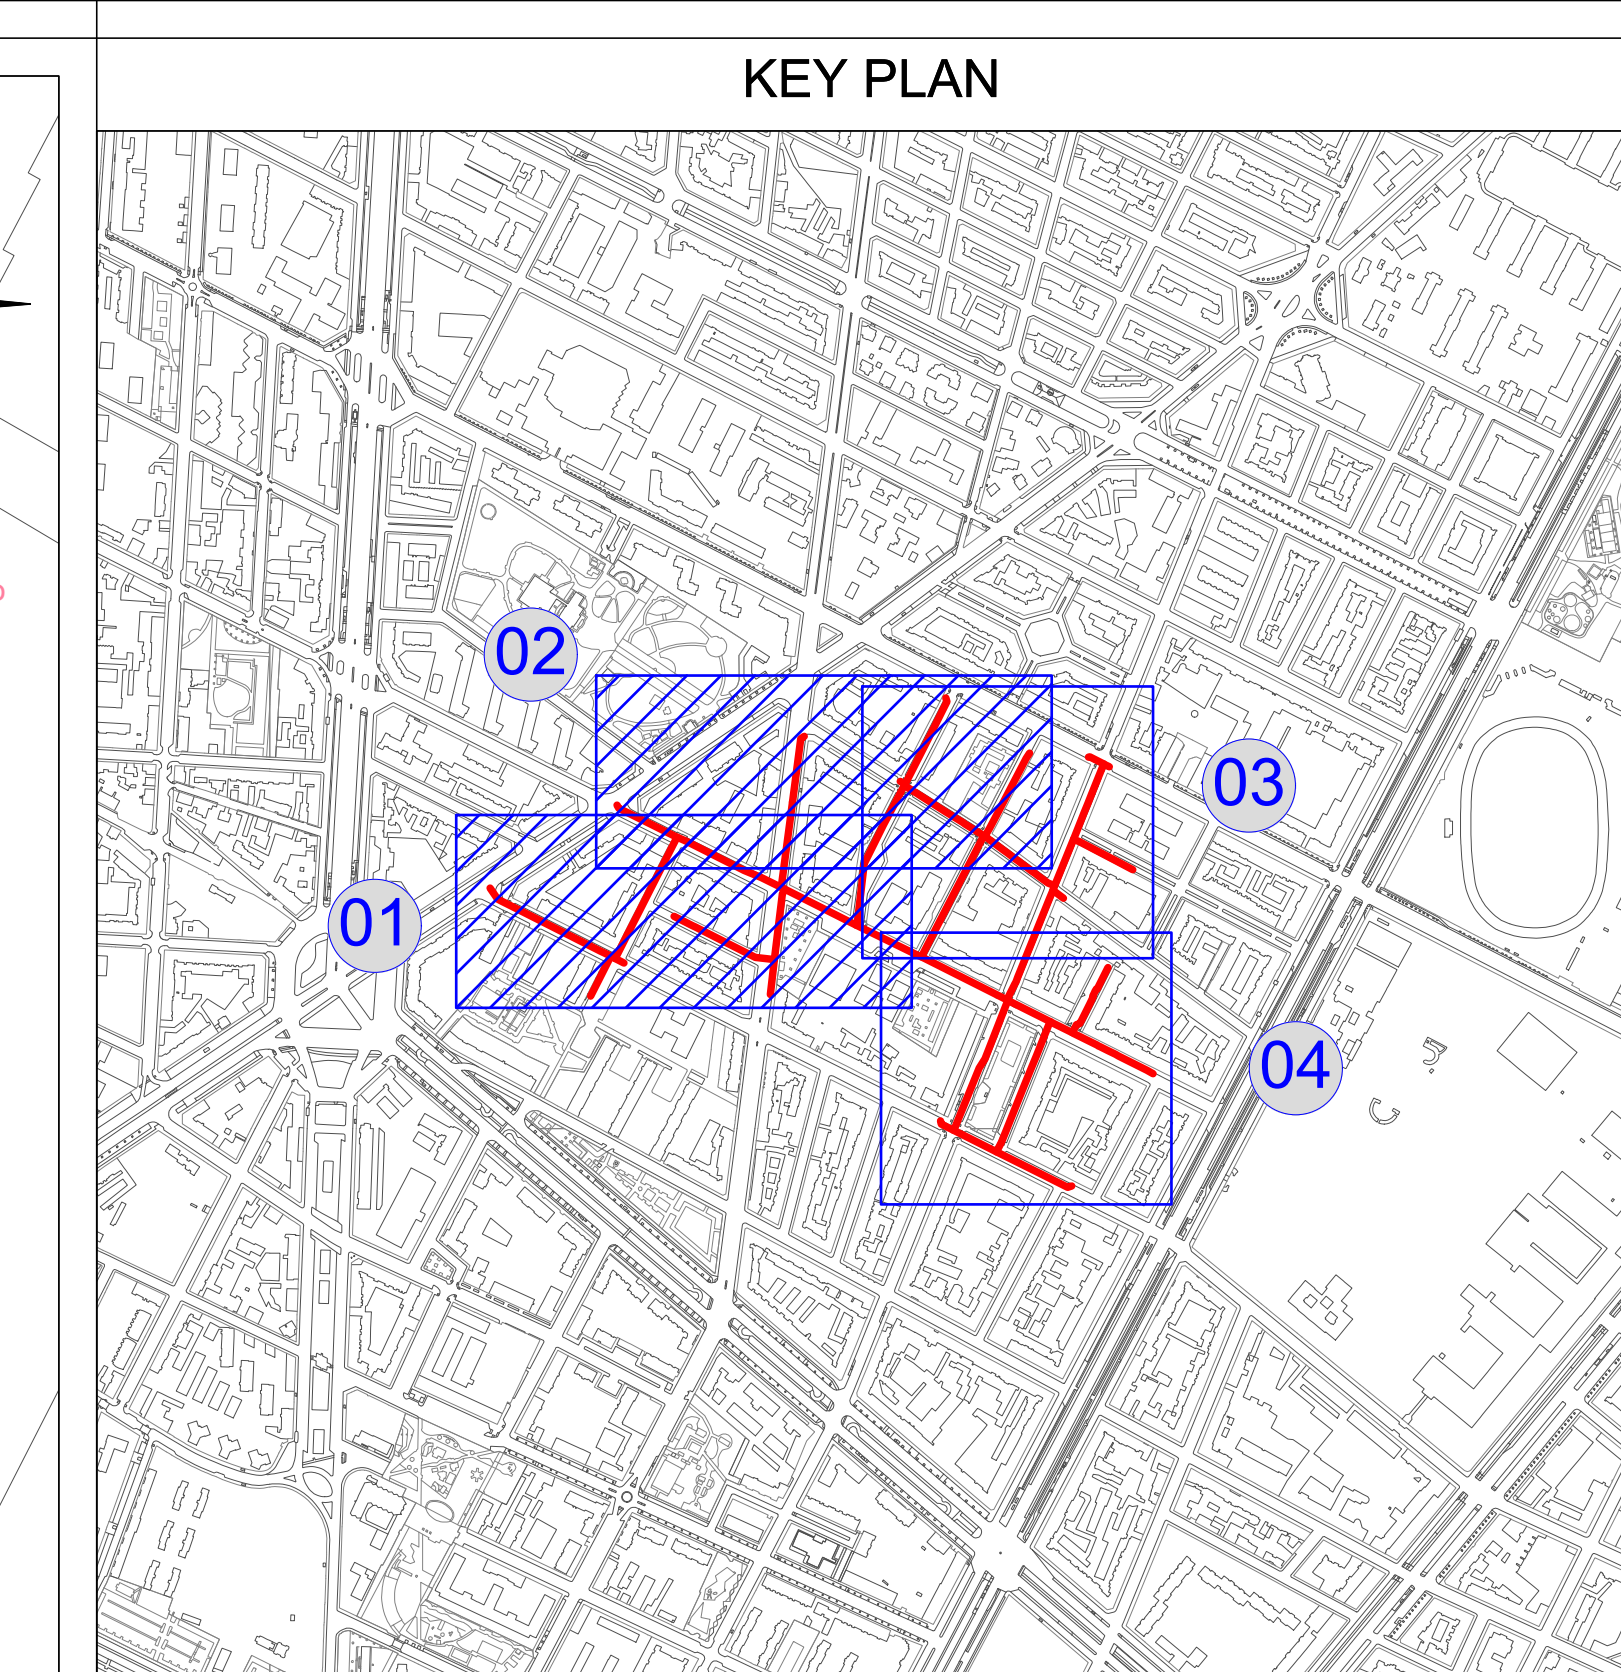


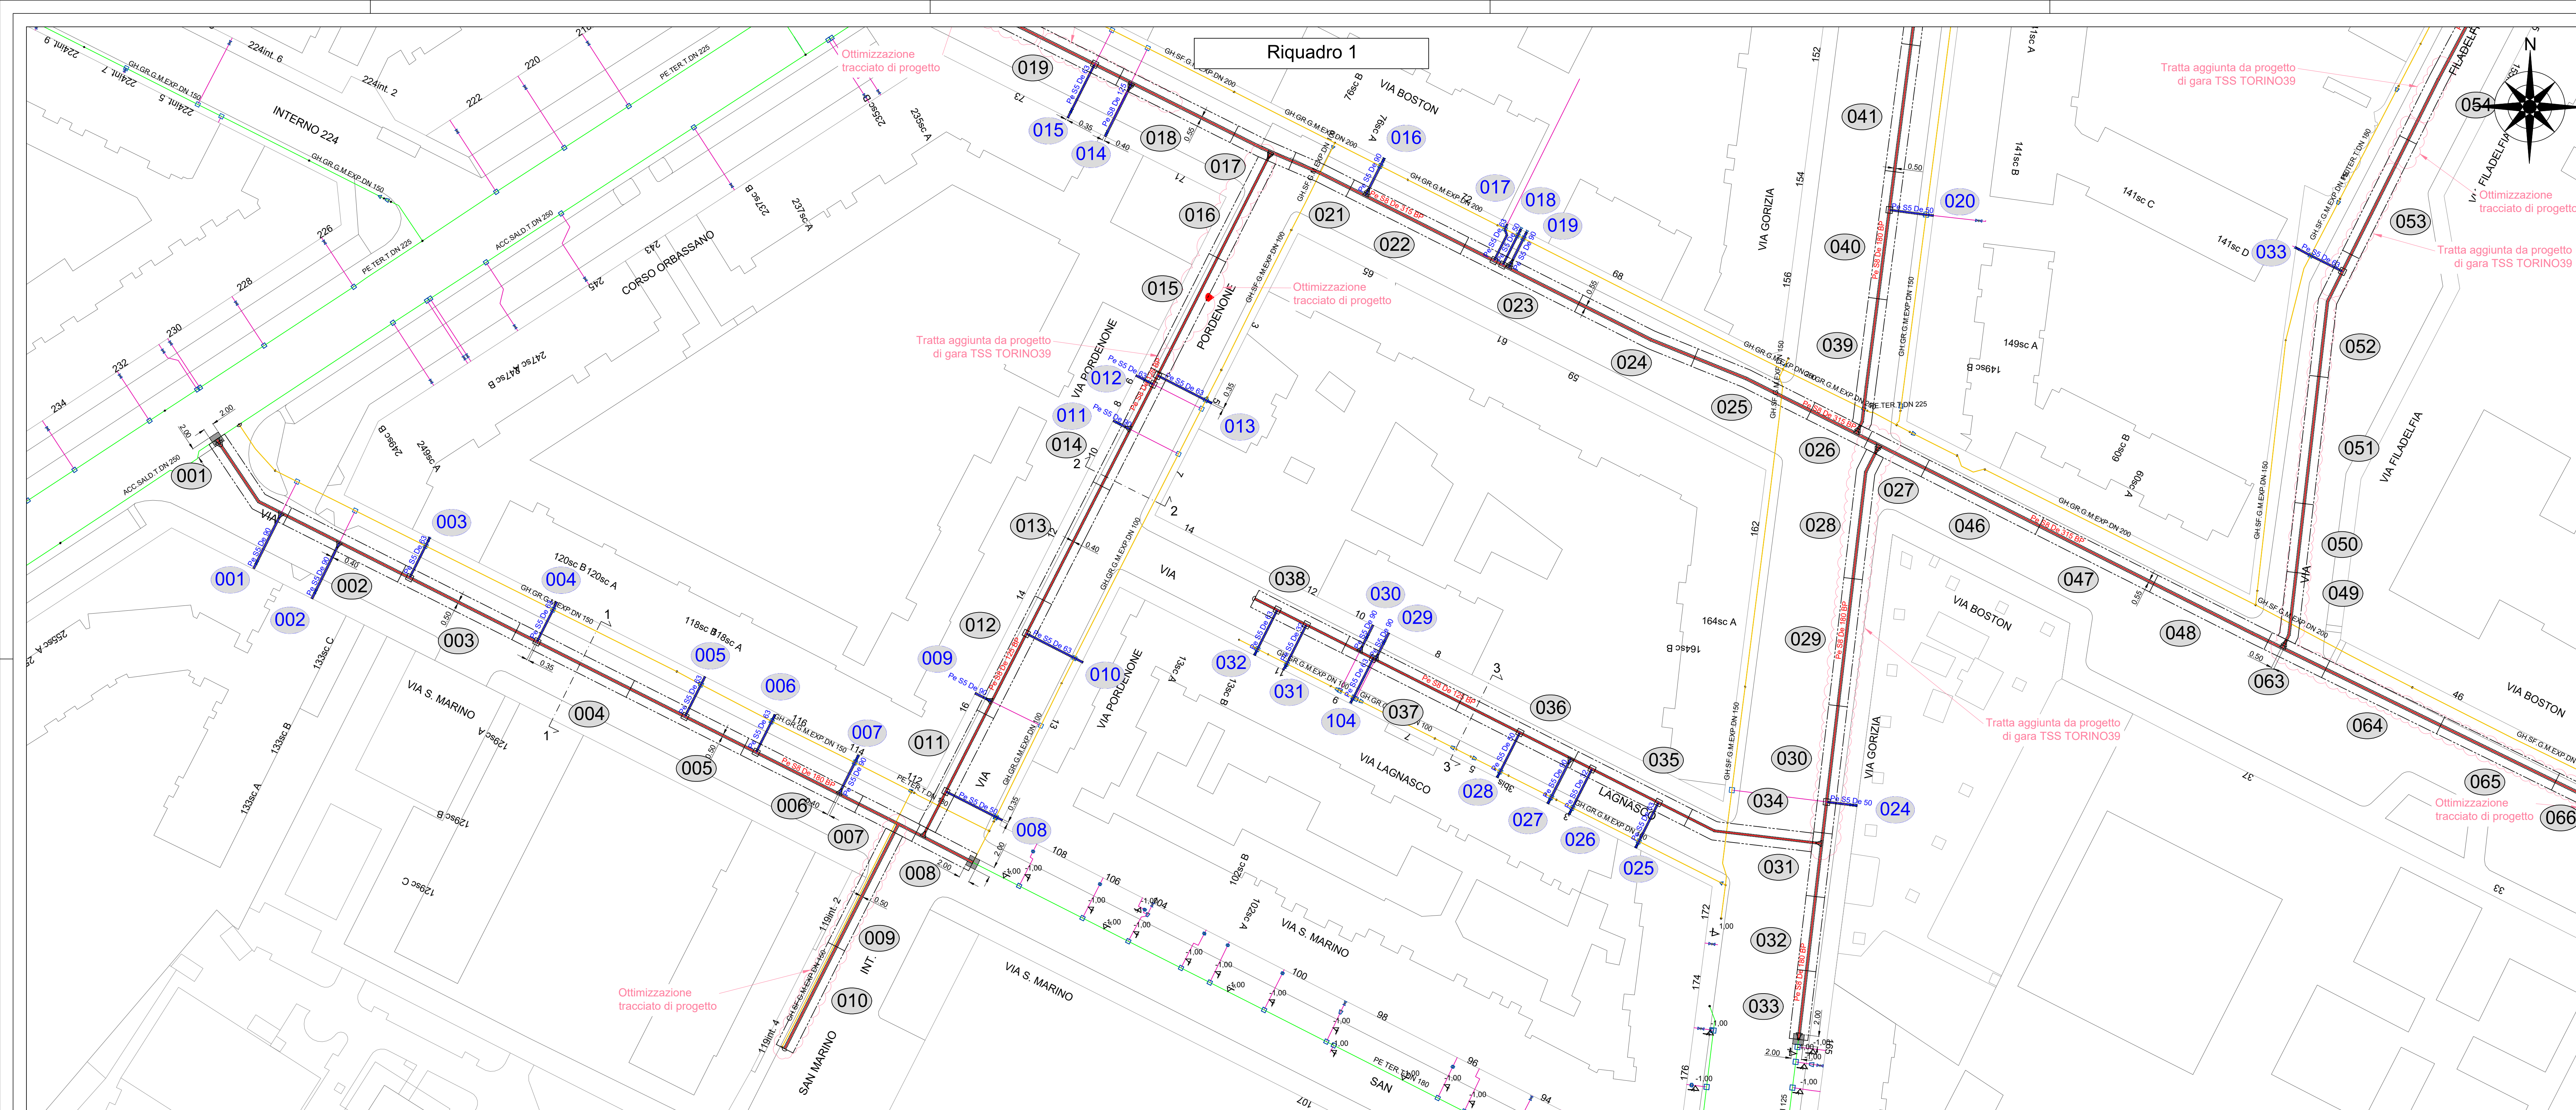

# LEGENDA

Rele in progetto

Rele da rimuovere

Zona di lavoro

I.D.U. in progetto

Tubazione I.D.U. esistente

n° Zona di lavoro

n° I.D.U. in progetto

Area scavi asfaltati

Area scavi sterrati

Area scavi autobloccanti

## Realizzo Scavi

| dati condotta           |      | scavo    |            |           |               | tipo superficie | volume (m³) | tipo di terreno | volume terre smosse (m³) |
|-------------------------|------|----------|------------|-----------|---------------|-----------------|-------------|-----------------|--------------------------|
| caratteristiche         | bar  | lung [m] | largh. [m] | prof. [m] | intr. [m]     |                 |             |                 |                          |
| P.S. DN 315             | BP   | 806      | 0,55       | 0,15      | 1,27          | Asfalto         | 66,41       | di riporto      | 56,08                    |
| P.S. DN 180             | BP   | 1705     | 0,50       | 0,15      | 1,13          | Asfalto         | 127,88      | di riporto      | 983,33                   |
| P.S. DN 125             | BP   | 497      | 0,40       | 0,15      | 1,08          | Asfalto         | 29,22       | di riporto      | 209,41                   |
| GH DN 300 (rimozione)   | 6    | 0,50     | 0,15       | 1,25      | Asfalto       | 0,46            | di riporto  | 3,75            |                          |
| GH DN 250 (rimozione)   | 38   | 0,50     | 0,15       | 1,20      | Asfalto       | 2,70            | di riporto  | 27,63           |                          |
| P.E. De 225 (rimozione) | 14   | 0,50     | 0,15       | 1,18      | Asfalto       | 1,05            | di riporto  | 8,23            |                          |
| Ace. DN 300 (rimozione) | 11   | 0,50     | 0,15       | 1,15      | Asfalto       | 0,93            | di riporto  | 6,33            |                          |
| GH DN 200 (rimozione)   | 771  | 0,50     | 0,15       | 1,15      | Asfalto       | 57,85           | di riporto  | 443,33          |                          |
| P.E. De 180 (rimozione) | 102  | 0,50     | 0,15       | 1,13      | Asfalto       | 7,68            | di riporto  | 57,63           |                          |
| P.E. De 160 (rimozione) | 20   | 0,50     | 0,10       | 1,10      | Autobloccanti | 1,00            | di riporto  | 11,00           |                          |
| Ace. De 125 (rimozione) | 14   | 0,40     | 0,15       | 1,08      | Asfalto       | 0,94            | di riporto  | 8,02            |                          |
| GH DN 150 (rimozione)   | 1642 | 0,50     | 0,15       | 1,10      | Asfalto       | 123,15          | di riporto  | 980,10          |                          |
| GH De 125 (rimozione)   | 14   | 0,40     | 0,15       | 1,08      | Asfalto       | 0,94            | di riporto  | 8,02            |                          |
| GH DN 100 (rimozione)   | 401  | 0,40     | 0,15       | 1,05      | Asfalto       | 24,06           | di riporto  | 186,42          |                          |
| Totale                  |      |          |            |           |               | Totale          | 444,12      | di riporto      | 3371,94                  |

Scarifica approntata

Scarifica OD

Buche di inserimento

Totale

Scarifica

Scarifica

Buche

Totale

Scarifica

Scarifica

Buche

Totale

Scarifica

Scarifica

Buche

Totale

Scarifica

Scarifica

Buche

Totale

Scarifica

Scarifica

Buche

Totale

Scarifica

Scarifica

Buche

Totale

Scarifica

Scarifica

Buche

Totale

Scarifica

Scarifica

Buche

Totale

Scarifica

Scarifica

Buche



Totale



Scarifica

Scarifica

Buche

Totale

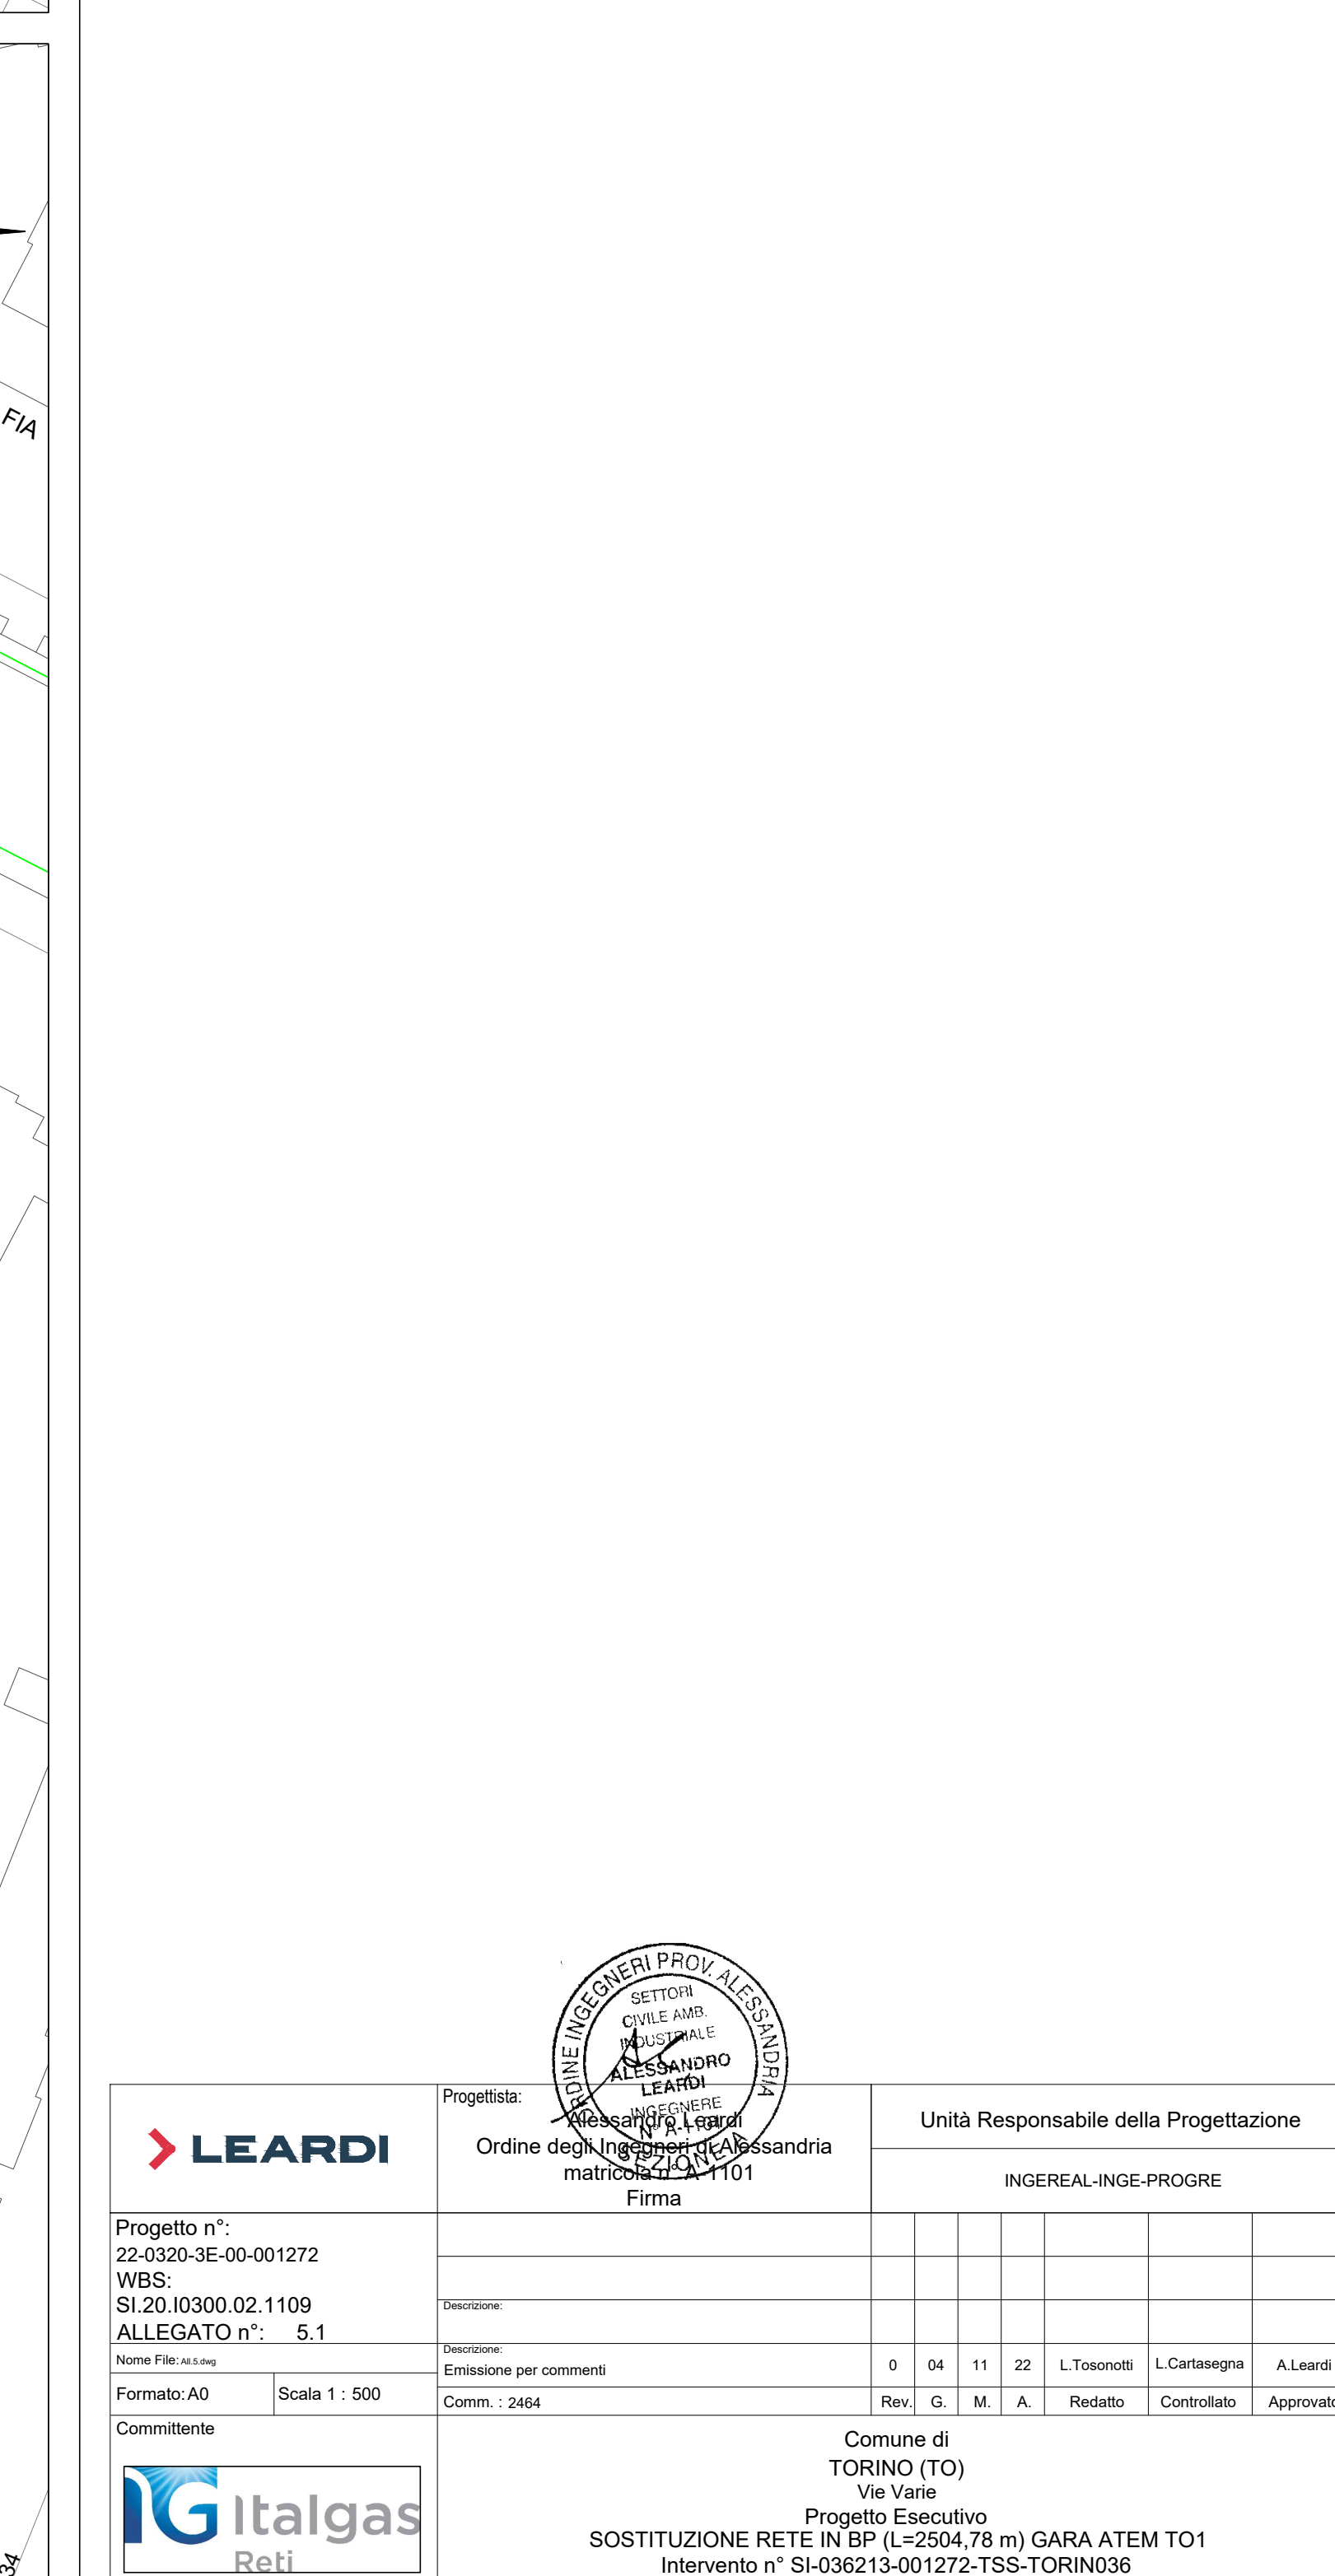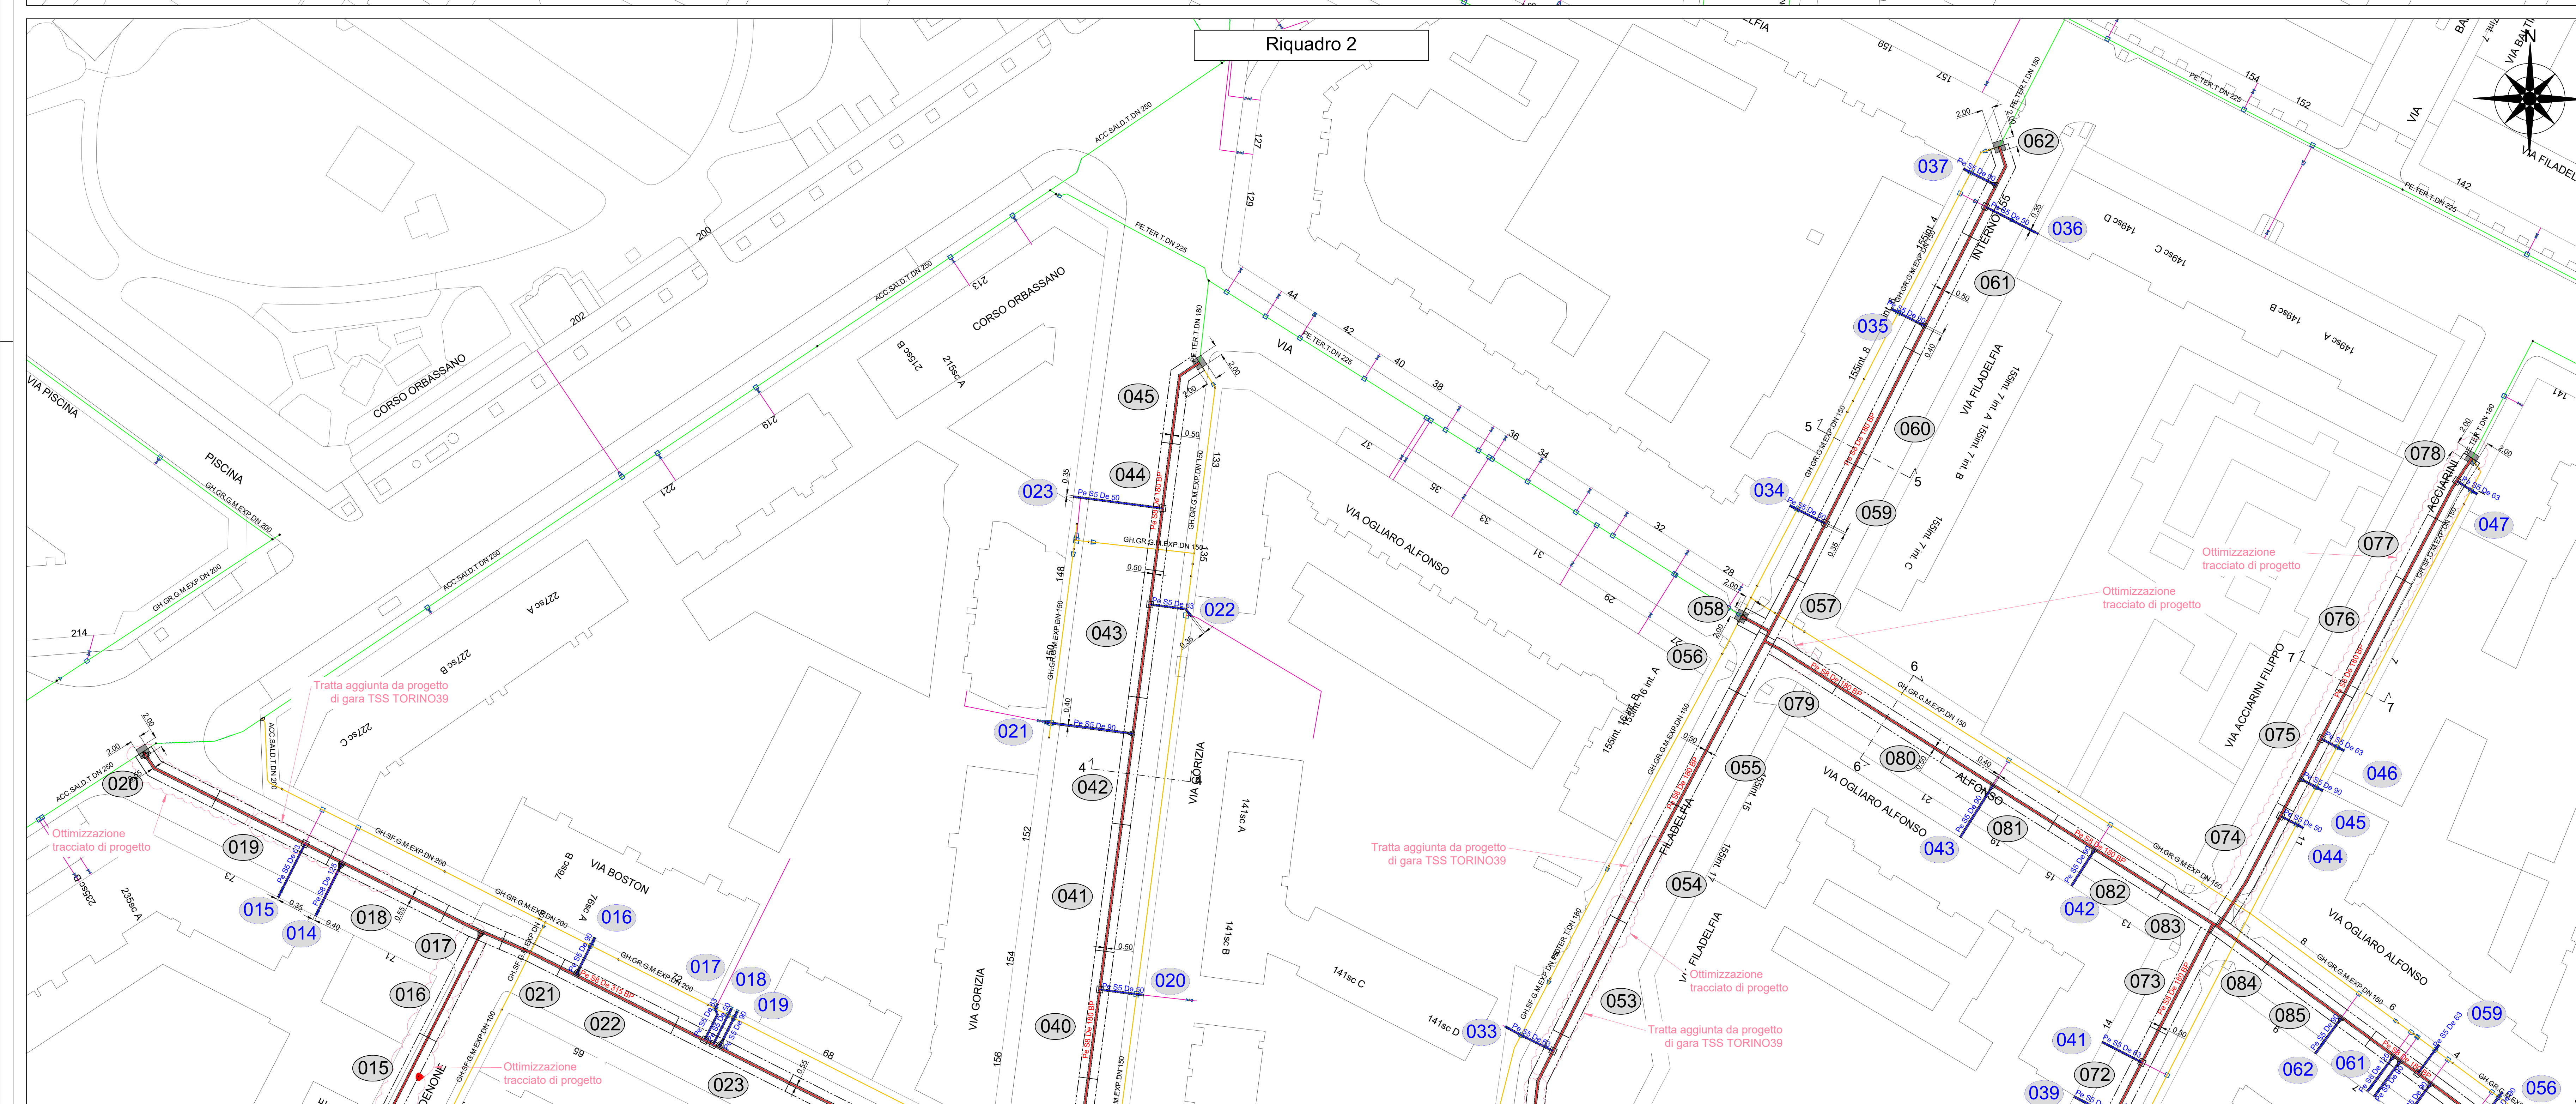

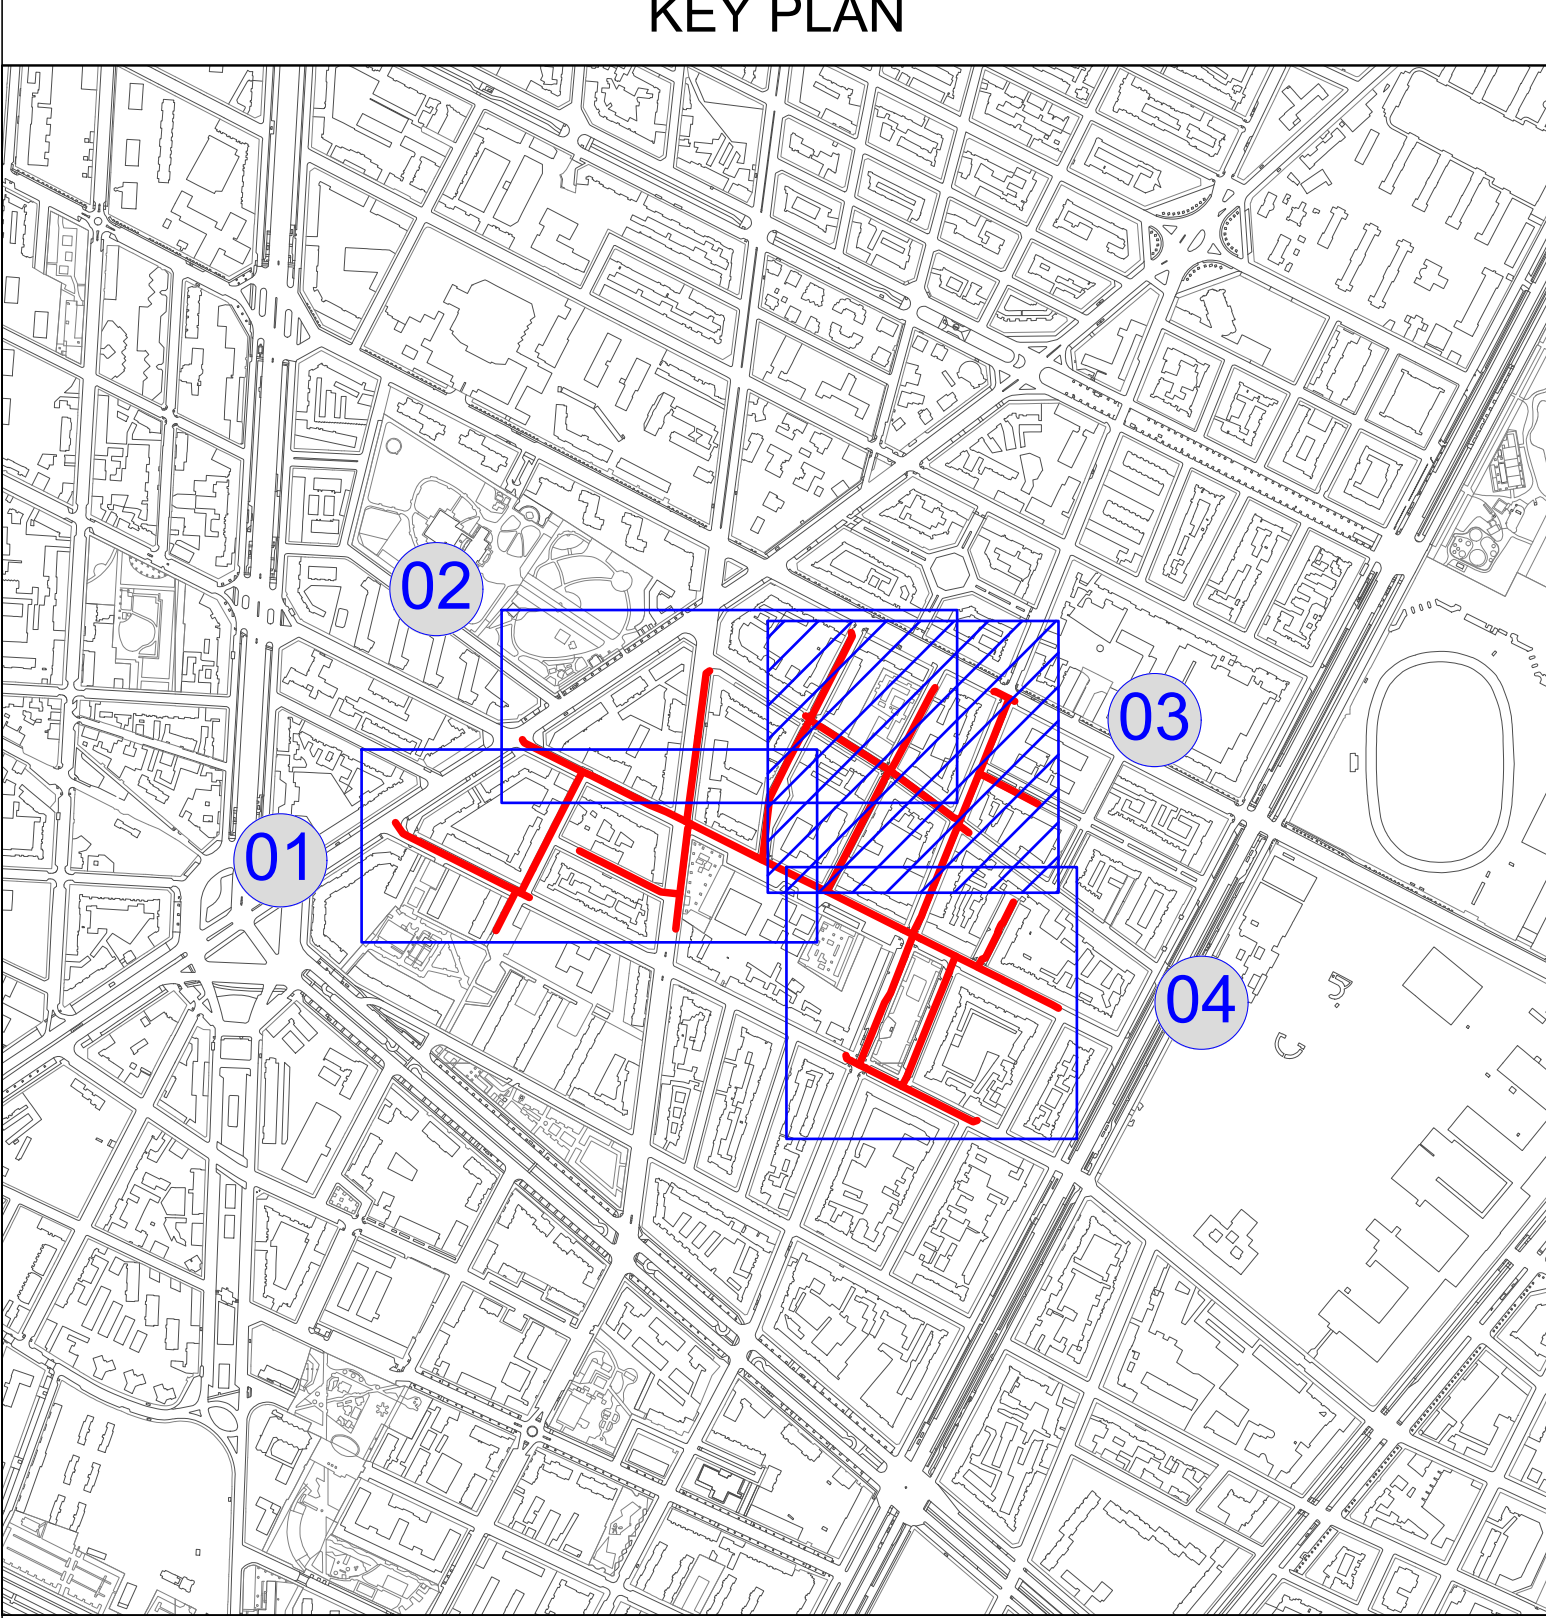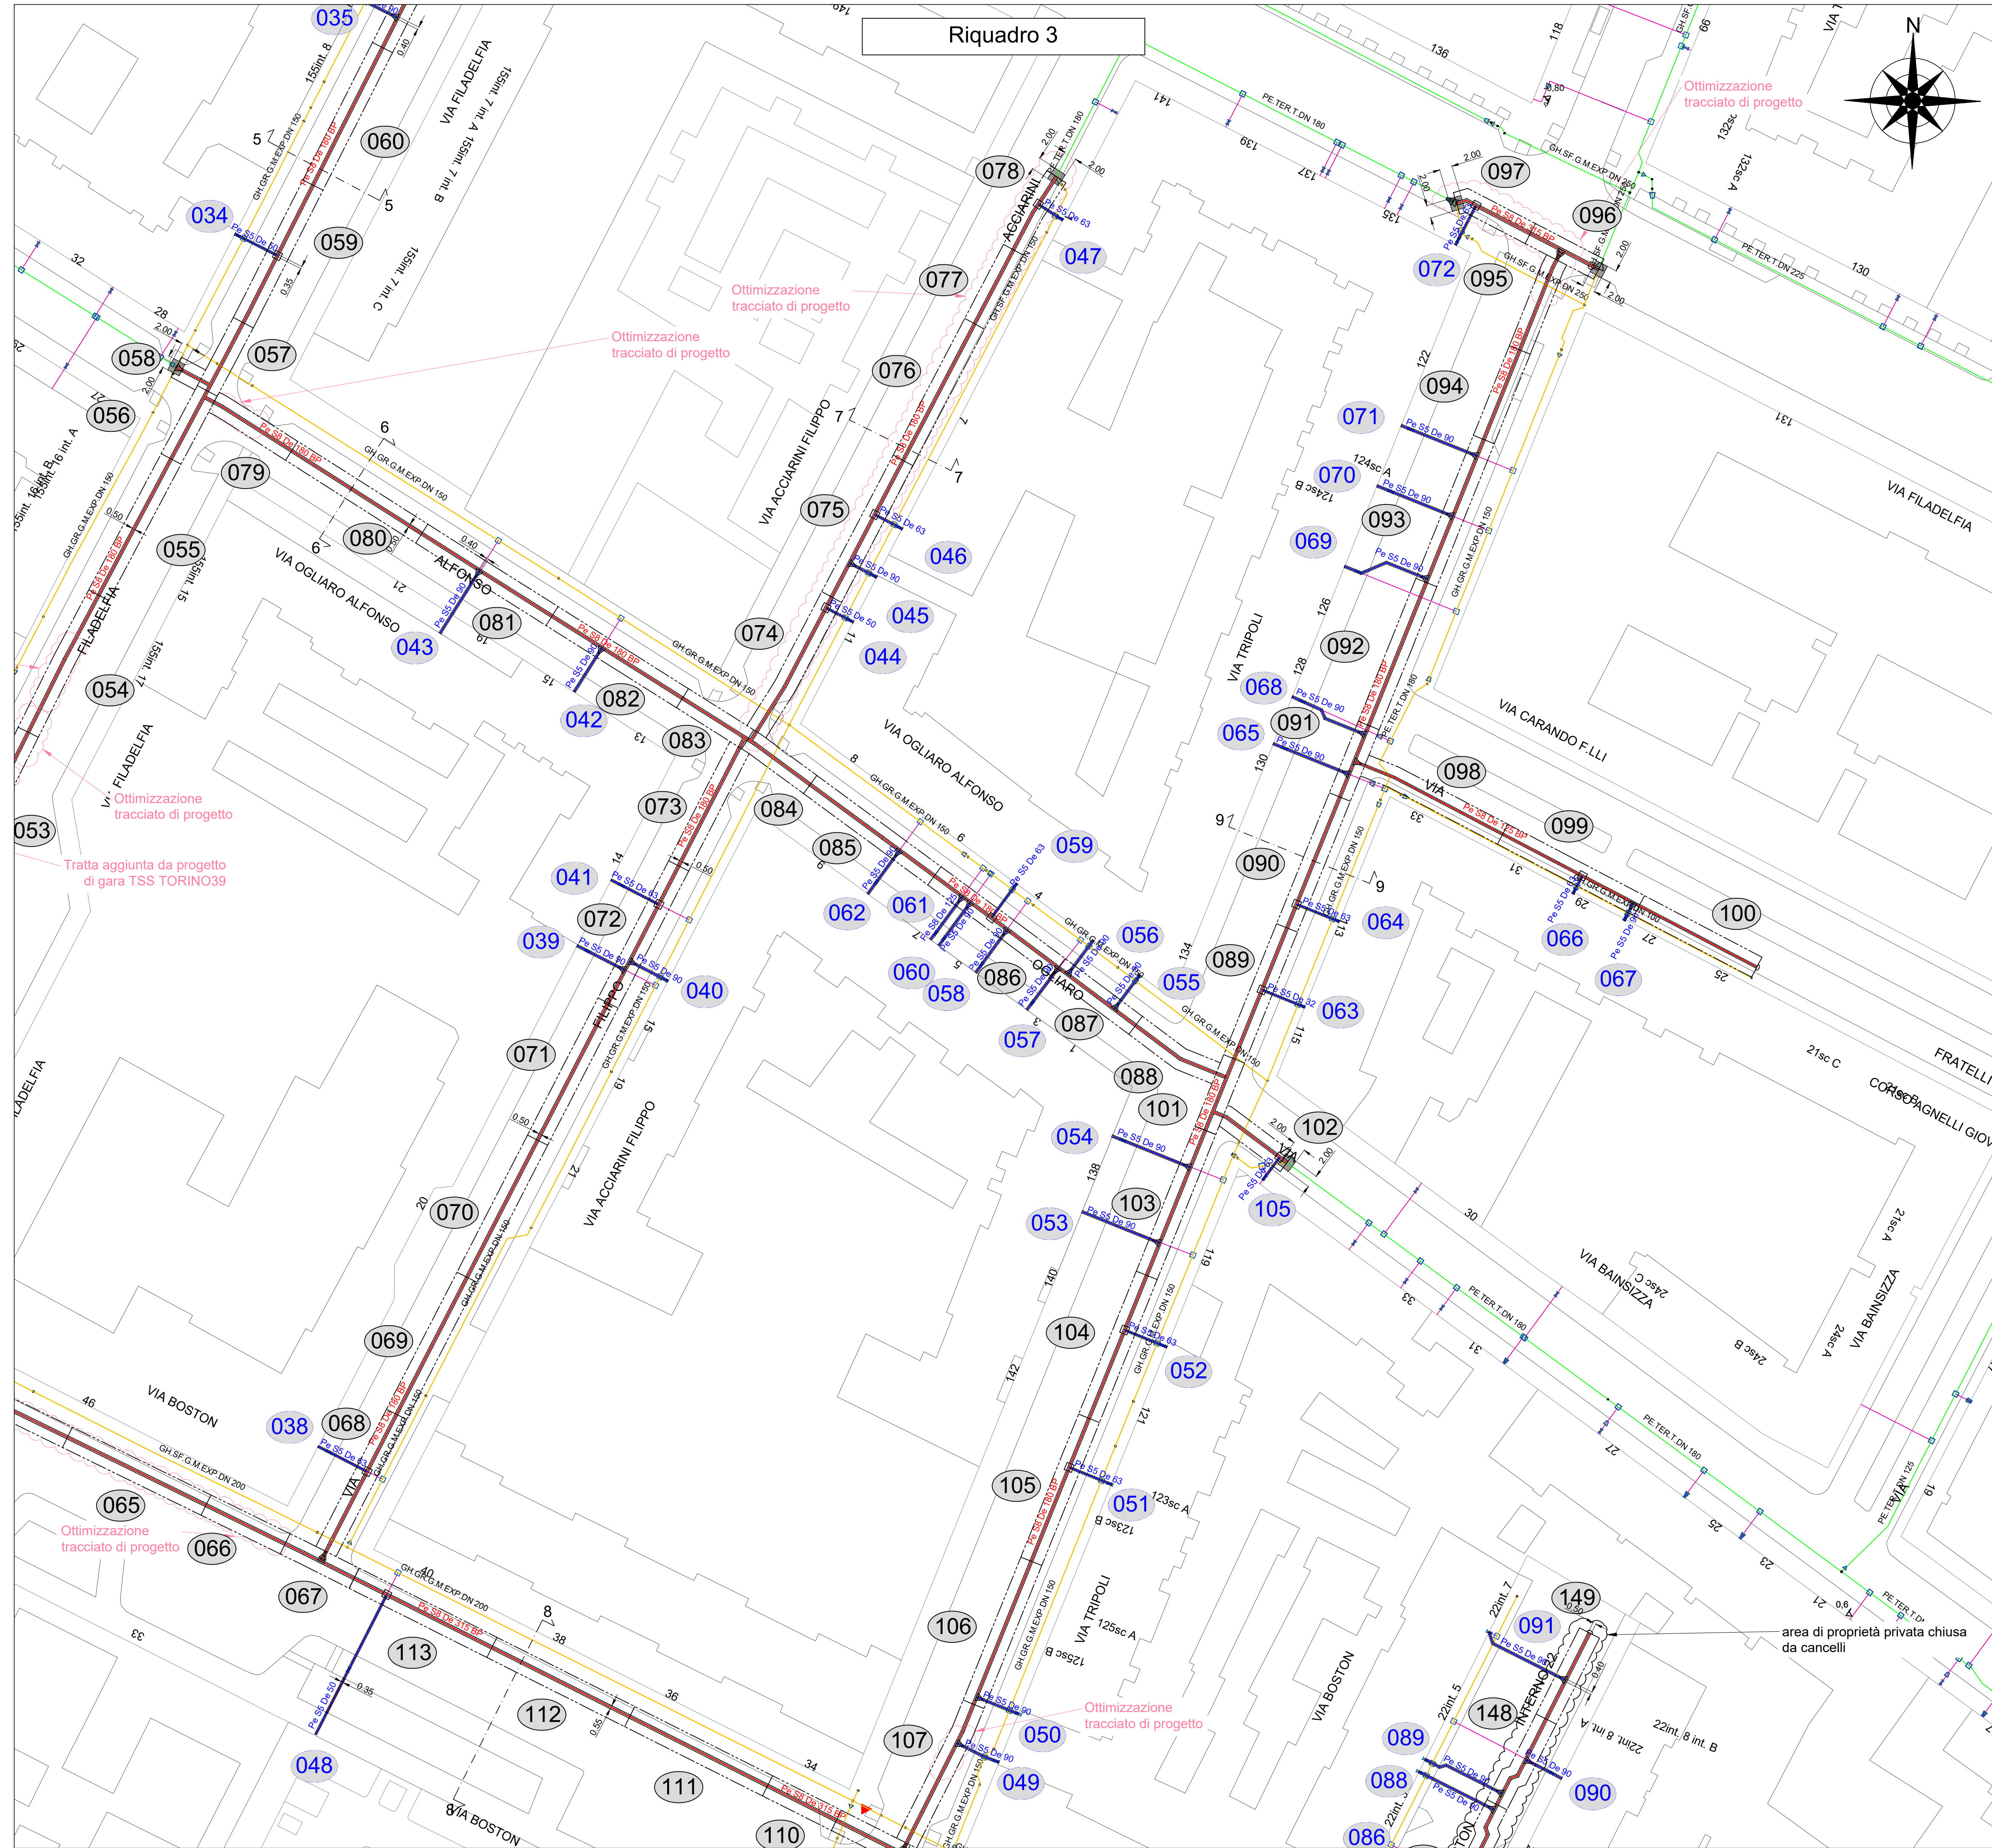

Rete in progetto

Rete da rimuovere

Zona di lavoro

I.D.U. in progetto

Tubazione I.D.U. esistente

001

n° Zona di lavoro

001

n° I.D.U. in progetto

Area scavi asfalto

Area scavi sterrato

Area scavi autobloccanti

Riepilogo Scavi

| dati condotta          |      | scavo     |            |               |             | tipo superficie | volume rifiuti [mc] | tipo di terreno | volume terre e rocce [mc] |
|------------------------|------|-----------|------------|---------------|-------------|-----------------|---------------------|-----------------|---------------------------|
| caratteristiche        | bar  | lung. [m] | largh. [m] | h superf. [m] | h terr. [m] |                 |                     |                 |                           |
| Pe S8 DN 315           | BP   | 805       | 0,55       | 0,15          | 1,27        | Asfalto         | 66,41               | di riporto      | 560,08                    |
| Pe S8 DN 180           | BP   | 1705      | 0,50       | 0,15          | 1,13        | Asfalto         | 127,86              | di riporto      | 963,33                    |
| Pe S8 DN 125           | BP   | 487       | 0,40       | 0,15          | 1,08        | Asfalto         | 29,22               | di riporto      | 209,41                    |
| GH DN 300 (rimozione)  | 6    | 0,50      | 0,15       | 1,25          |             | Asfalto         | 0,45                | di riporto      | 3,75                      |
| GH DN 250 (rimozione)  | 36   | 0,50      | 0,15       | 1,20          |             | Asfalto         | 2,70                | di riporto      | 21,60                     |
| Pe De 225 (rimozione)  | 14   | 0,50      | 0,15       | 1,18          |             | Asfalto         | 1,05                | di riporto      | 8,23                      |
| Acc DN 200 (rimozione) | 11   | 0,50      | 0,15       | 1,15          |             | Asfalto         | 0,83                | di riporto      | 6,33                      |
| GH DN 200 (rimozione)  | 771  | 0,50      | 0,15       | 1,15          |             | Asfalto         | 57,83               | di riporto      | 443,33                    |
| Pe De 180 (rimozione)  | 102  | 0,50      | 0,15       | 1,13          |             | Asfalto         | 7,65                | di riporto      | 57,63                     |
| Pe De 180 (rimozione)  | 20   | 0,50      | 0,10       | 1,18          |             | Autobloccanti   | 1,00                | di riporto      | 11,80                     |
| Acc DN 150 (rimozione) | 10   | 0,50      | 0,15       | 1,10          |             | Asfalto         | 0,75                | di riporto      | 5,50                      |
| GH DN 150 (rimozione)  | 1642 | 0,50      | 0,15       | 1,10          |             | Asfalto         | 123,15              | di riporto      | 903,10                    |
| Pe De 125 (rimozione)  | 14   | 0,40      | 0,15       | 1,08          |             | Asfalto         | 0,84                | di riporto      | 6,02                      |
| GH DN 100 (rimozione)  | 401  | 0,40      | 0,15       | 1,05          |             | Asfalto         | 24,06               | di riporto      | 168,42                    |
| Parziale               |      |           |            |               |             |                 | 444,12              |                 | 3371,04                   |
| Scarifica aggiuntiva   |      |           |            |               |             |                 | 1498,78             |                 | 0,00                      |
| Scarifica IDU          |      |           |            |               |             |                 | 198,71              |                 | 356,47                    |
| Buche di inserimento   |      |           |            |               |             |                 | 8,40                |                 | 64,96                     |
| Totale                 |      |           |            |               |             |                 | 2150,01             |                 | 3792,47                   |

Progettista: **LEARDI**

Progetto n°: 22-0320-3E-00-001272  
WBS: SI.20.10300.02.1109  
ALLEGATO n°: 5.2

Formato: A1  
Scala: 1 : 500

Comune di TORINO (TO)  
Via Varie  
Progetto Esecutivo  
SOSTITUZIONE RETE IN BP (L=2504,78 m) GARA ATEM TO1  
Intervento n° SI-036213-001272-TSS-TORINO36  
Planimetria scavi - Tavola 2

Unità Responsabile della Progettazione  
INGEREAL-INGE-PROGRE

Descrizione: Emissione per commenti  
Comm.: 2464

Rev. G. M. A. Redatto Controllato Approvato

