

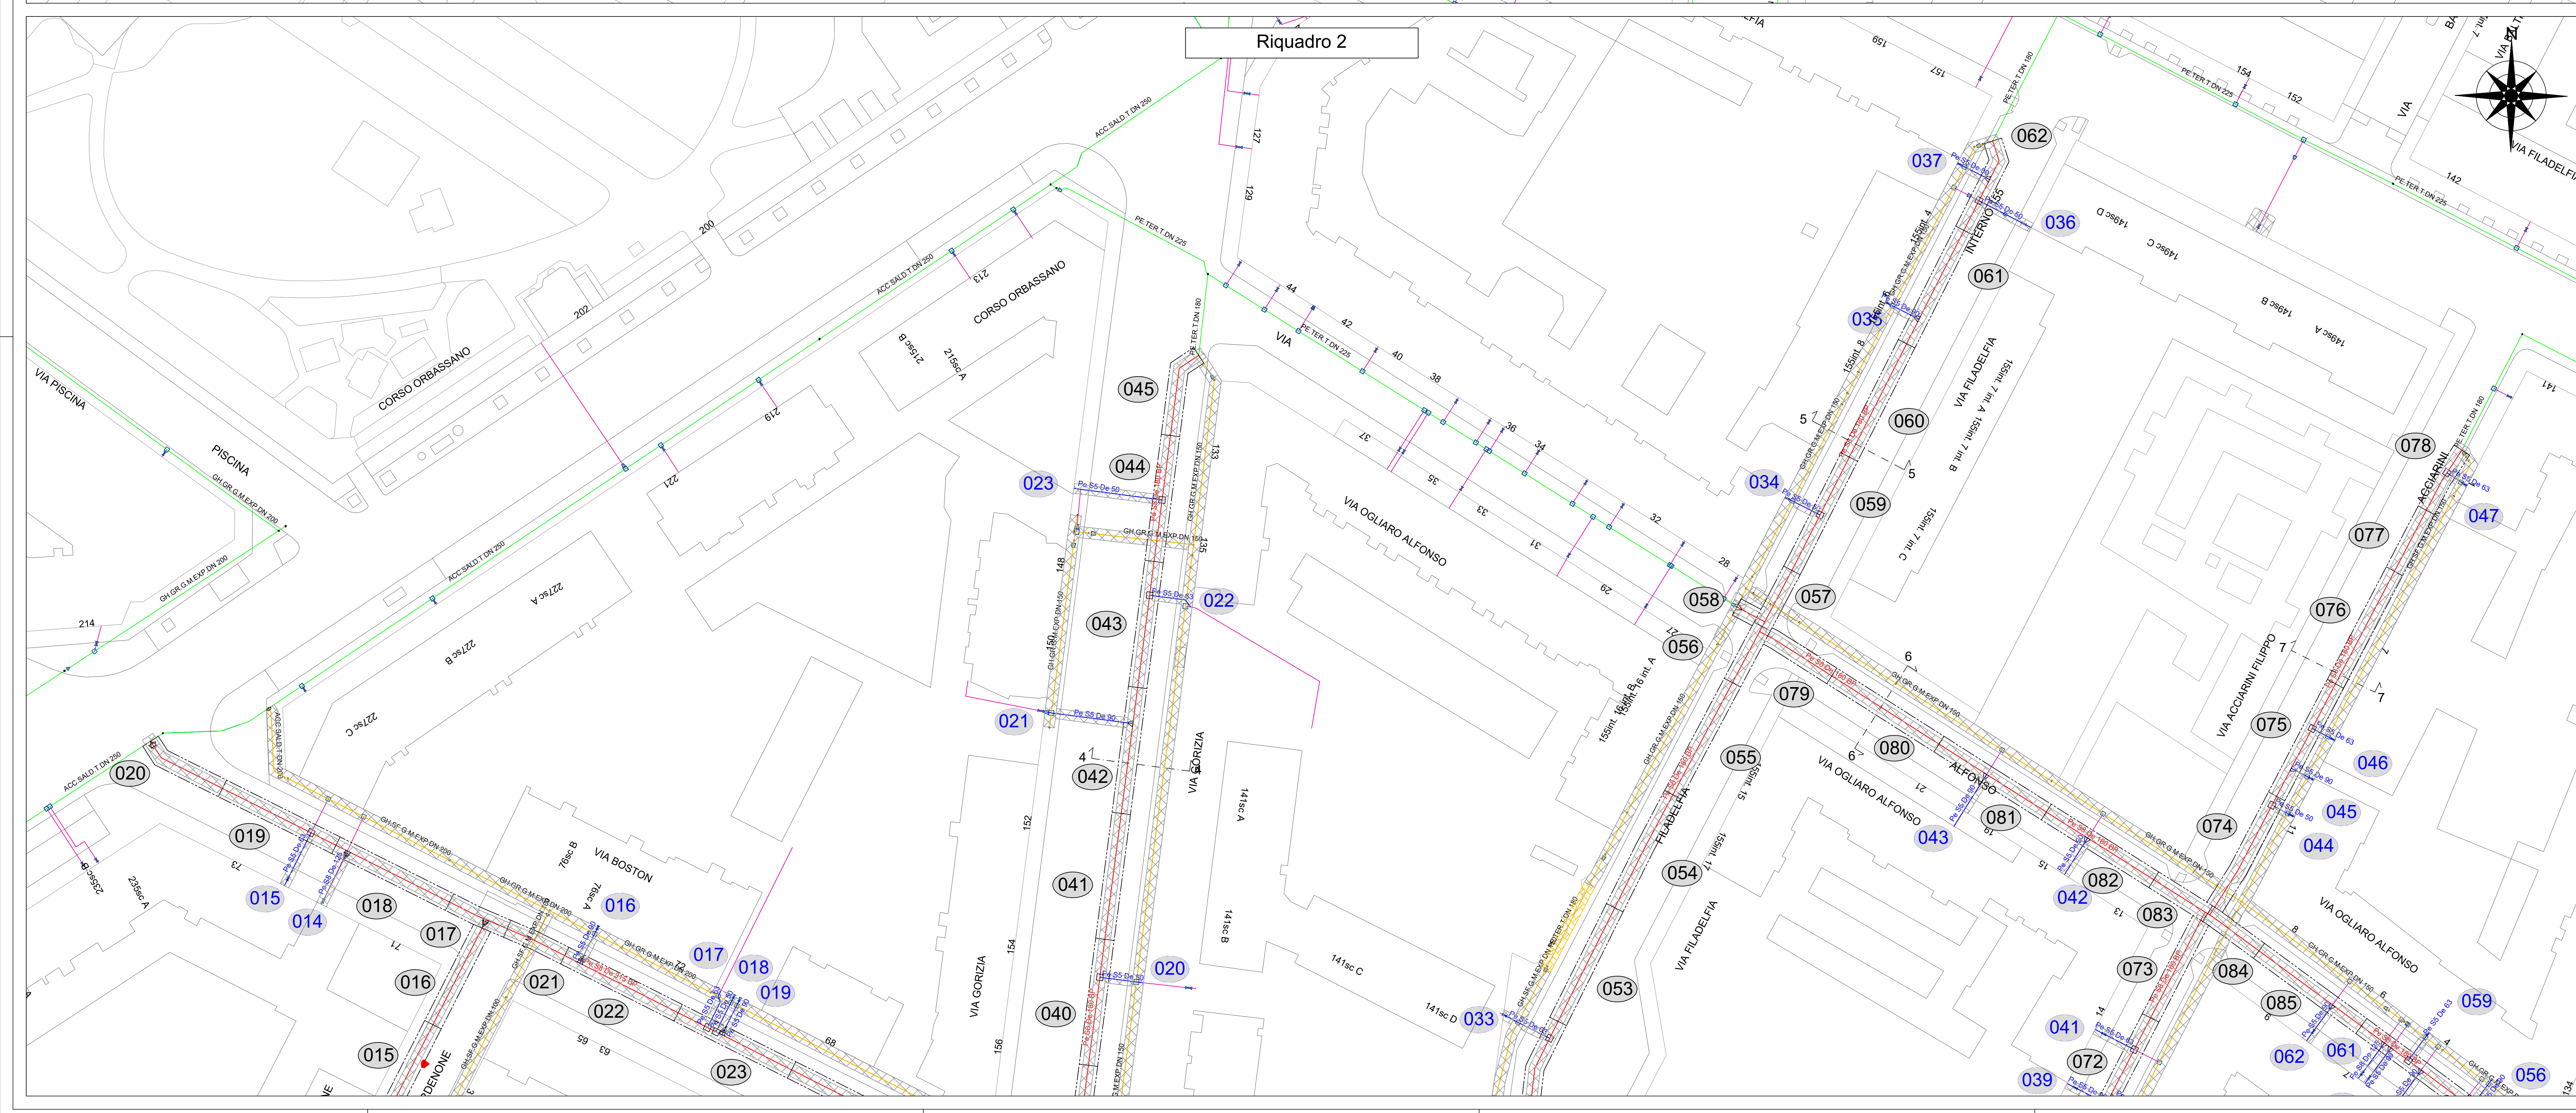
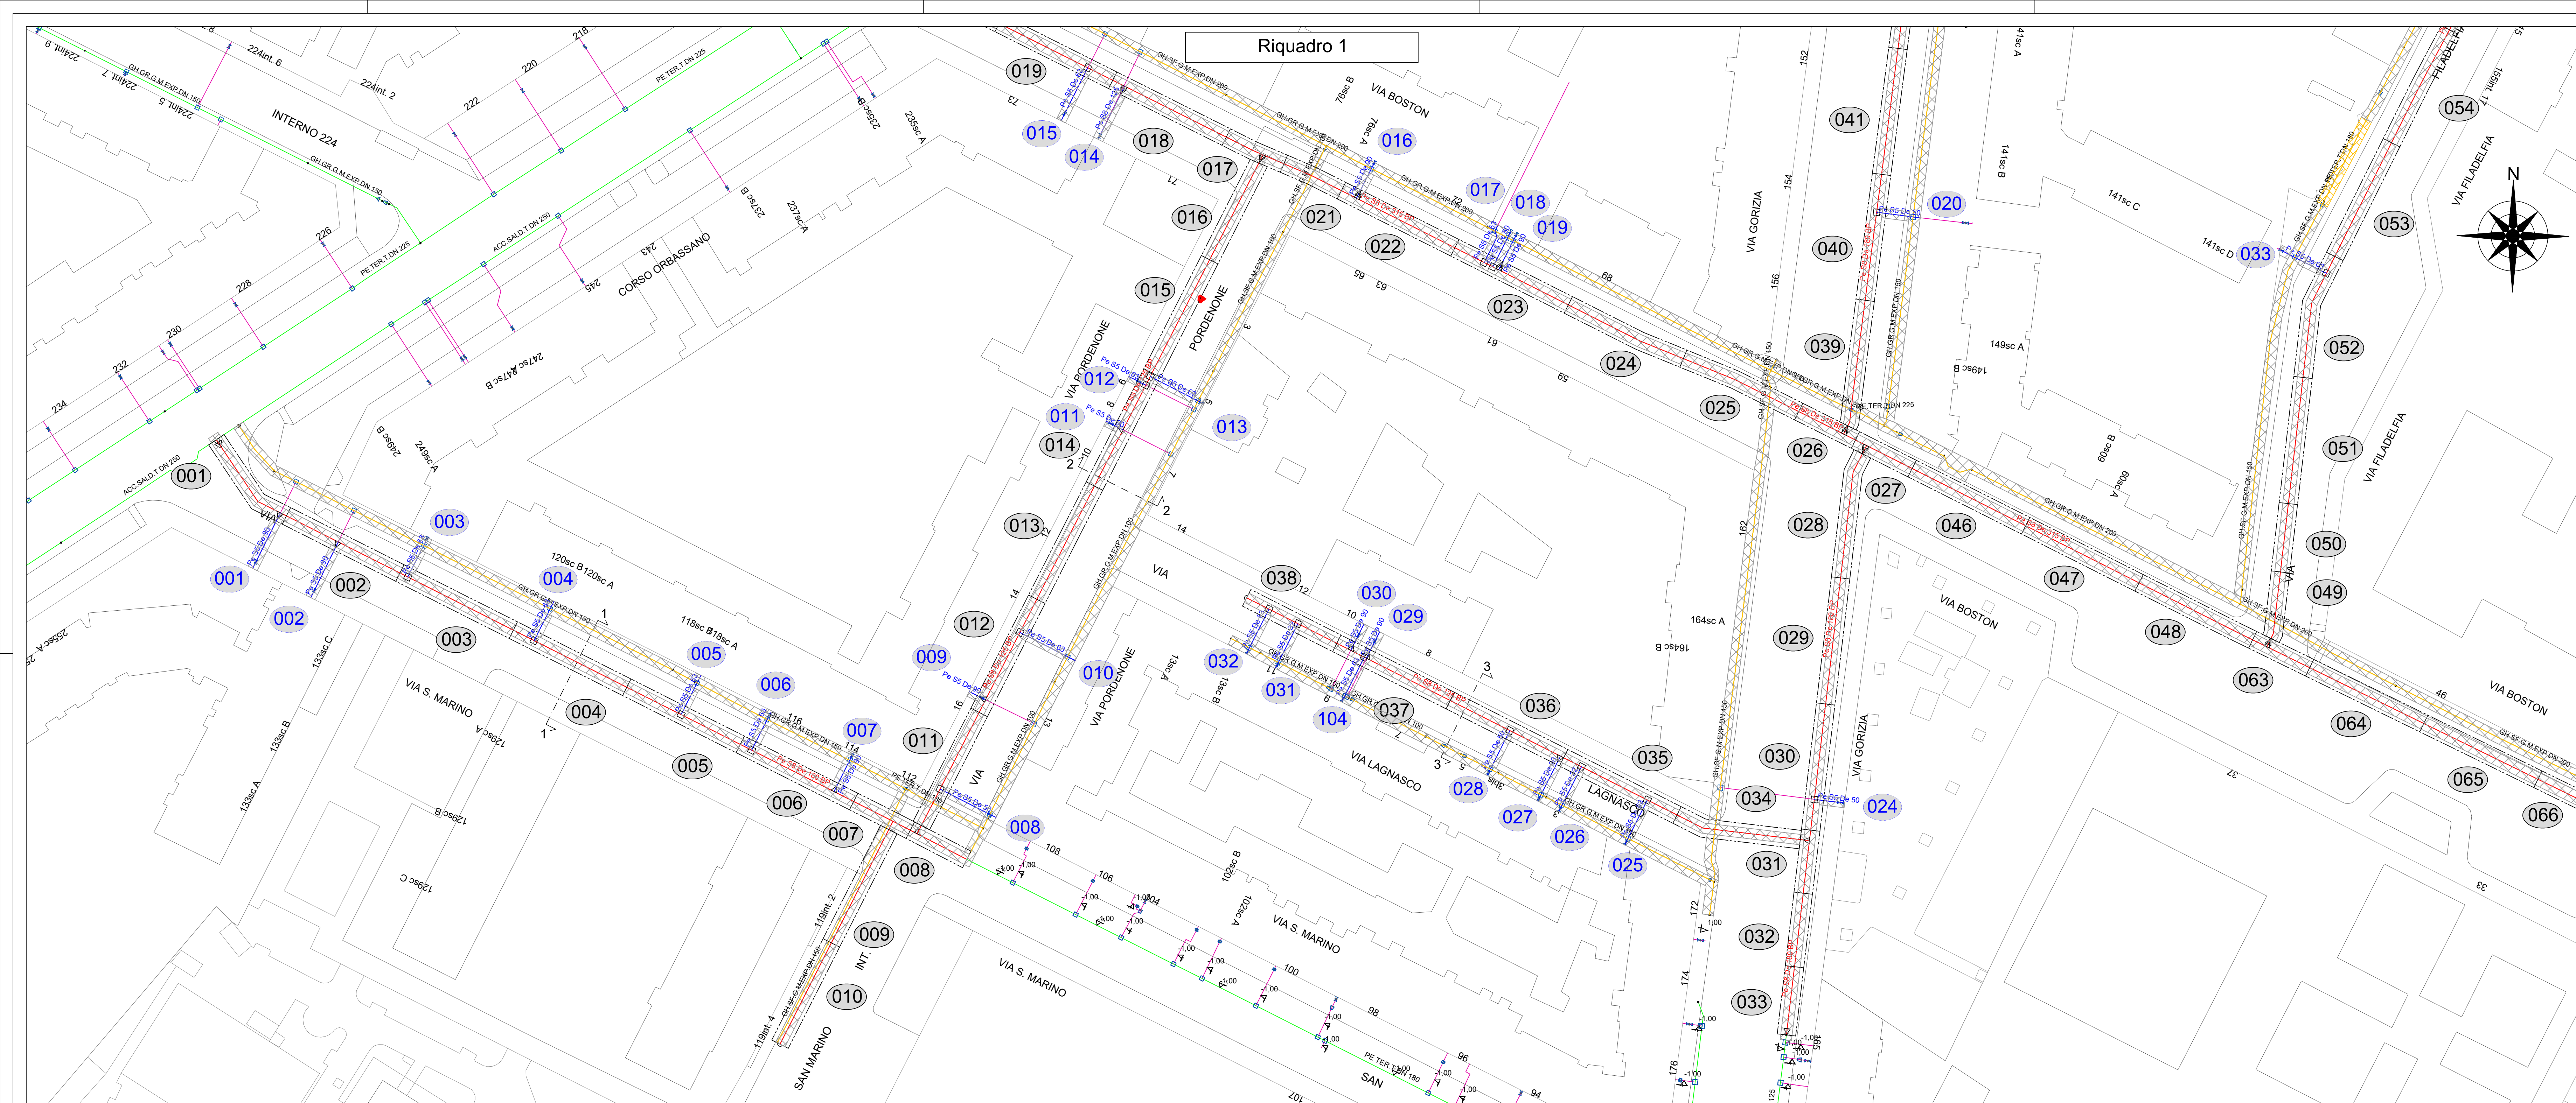
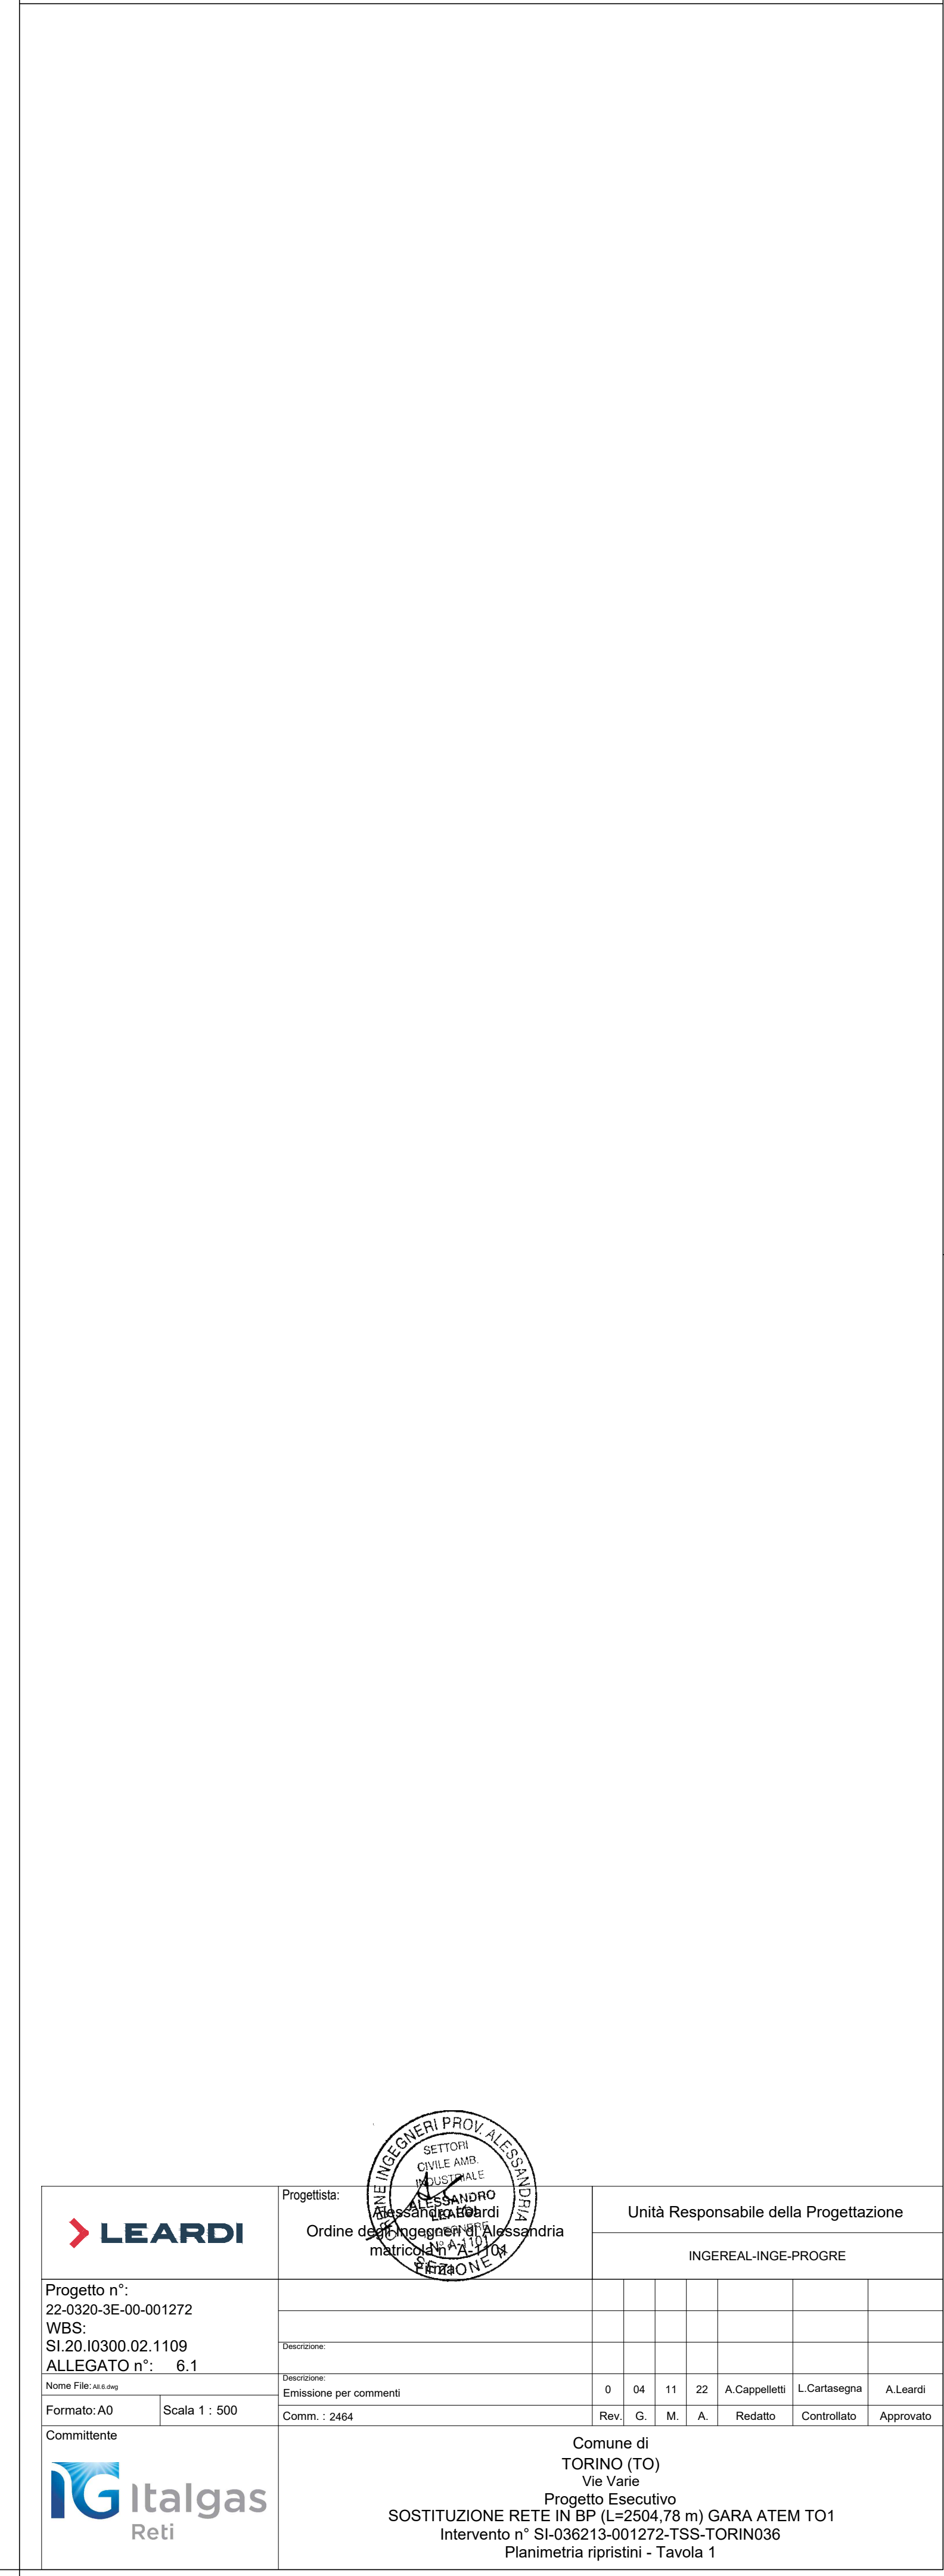
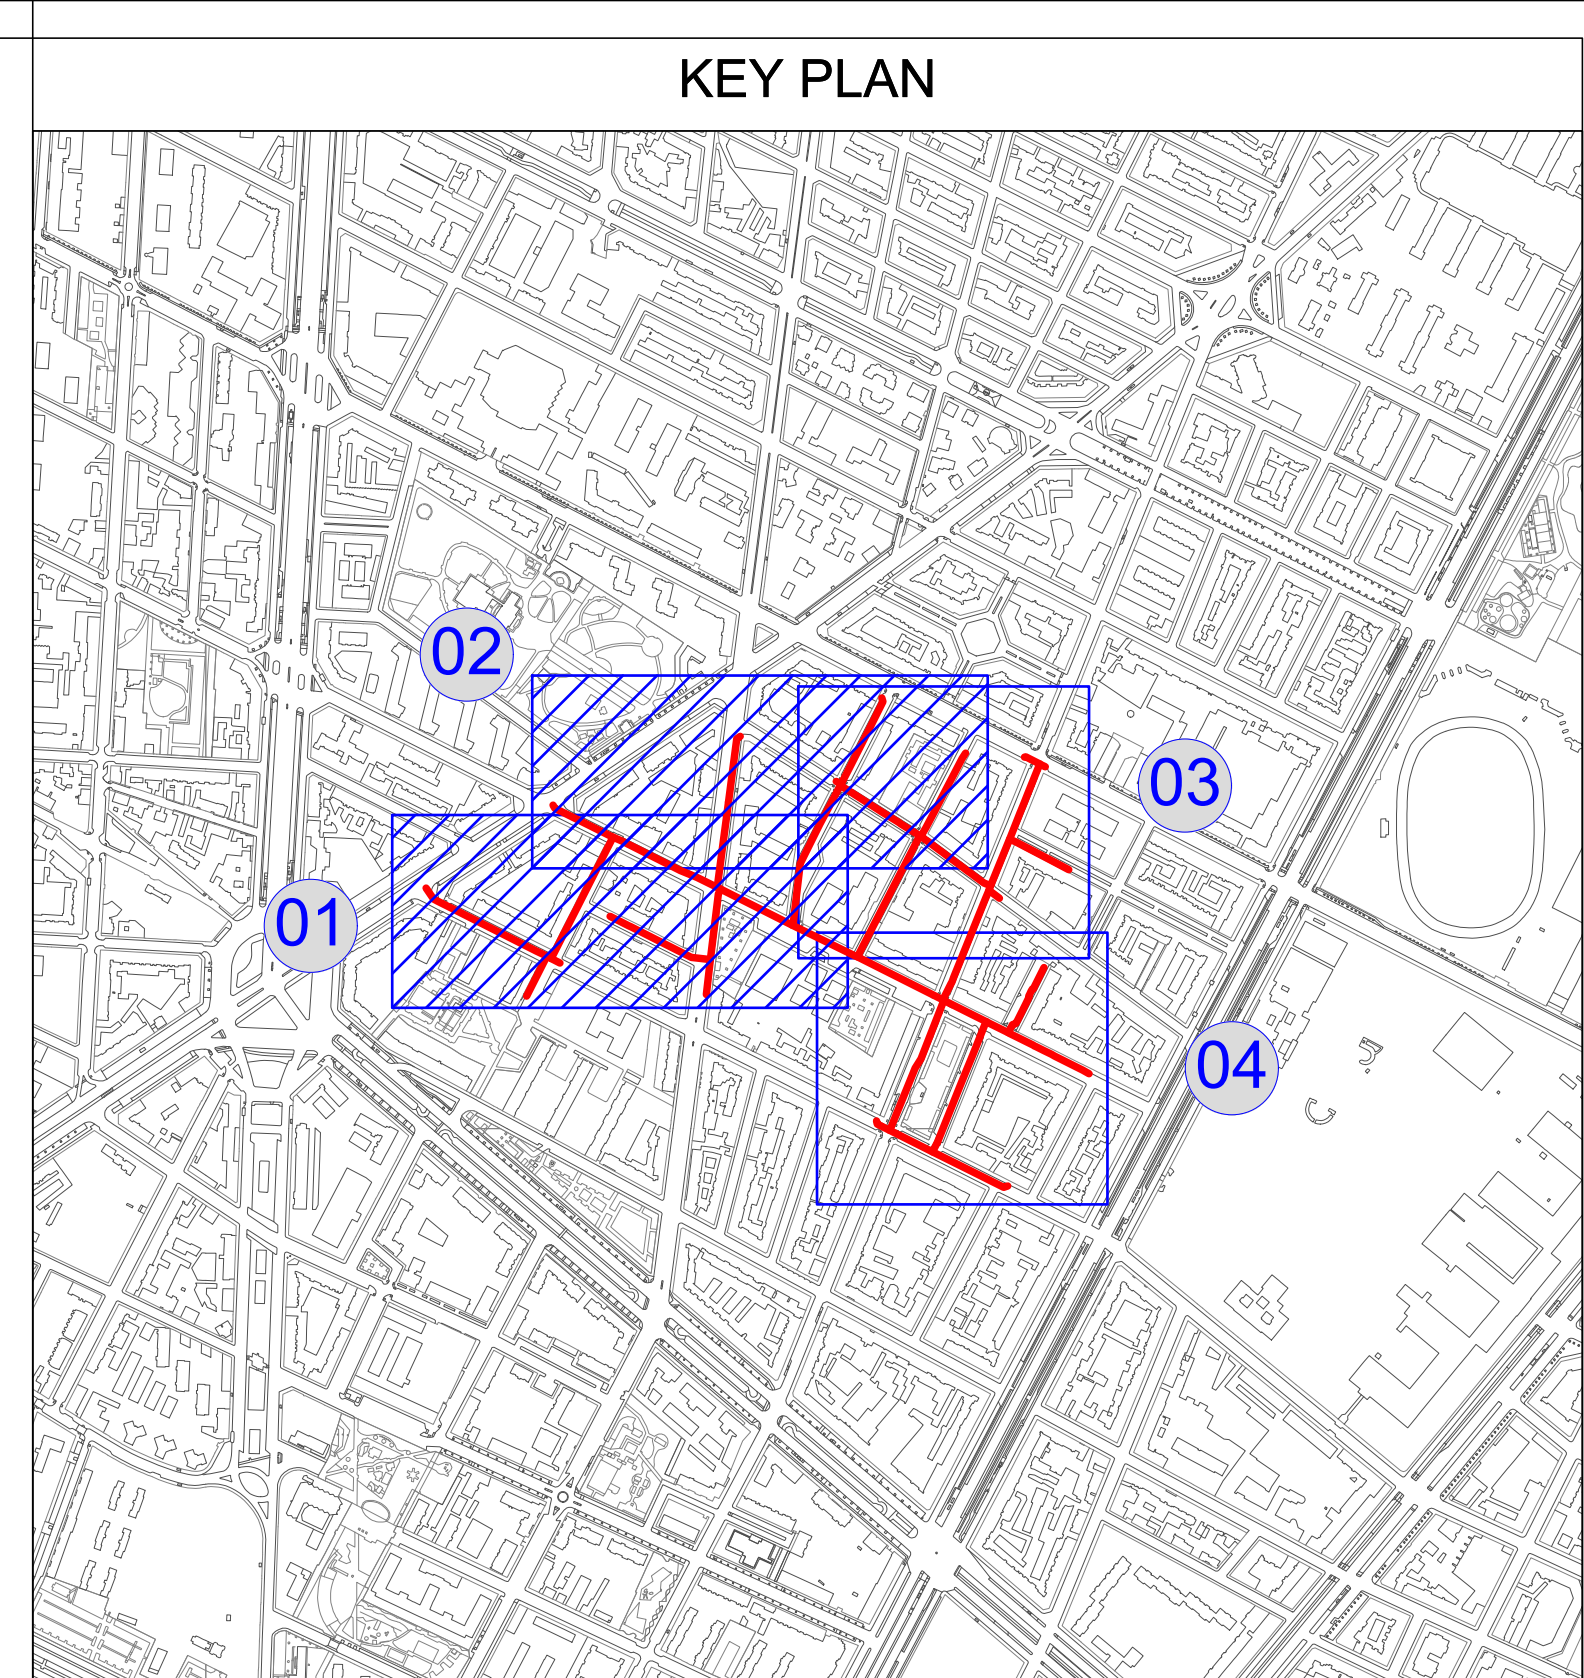


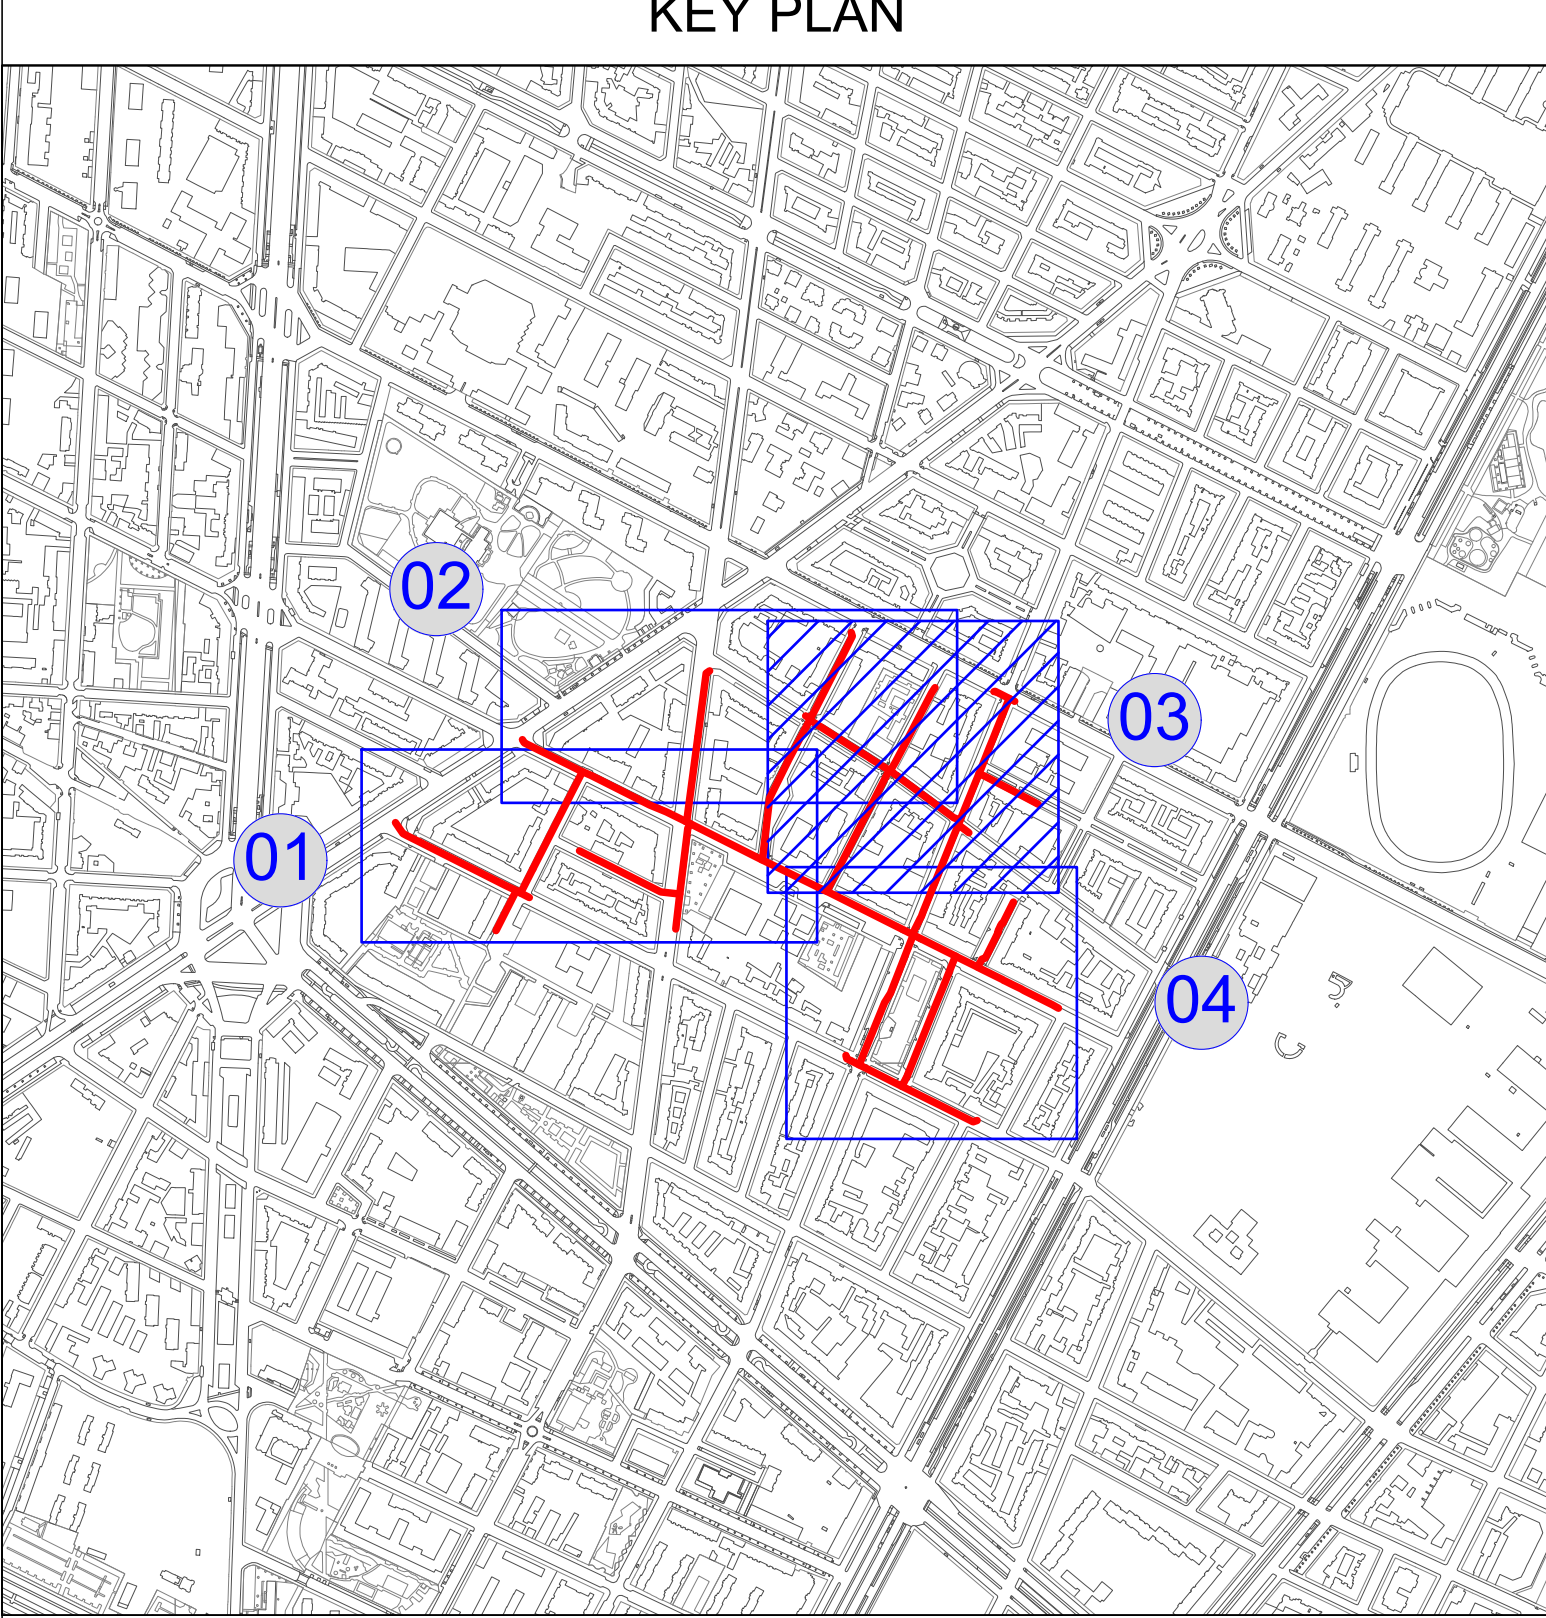

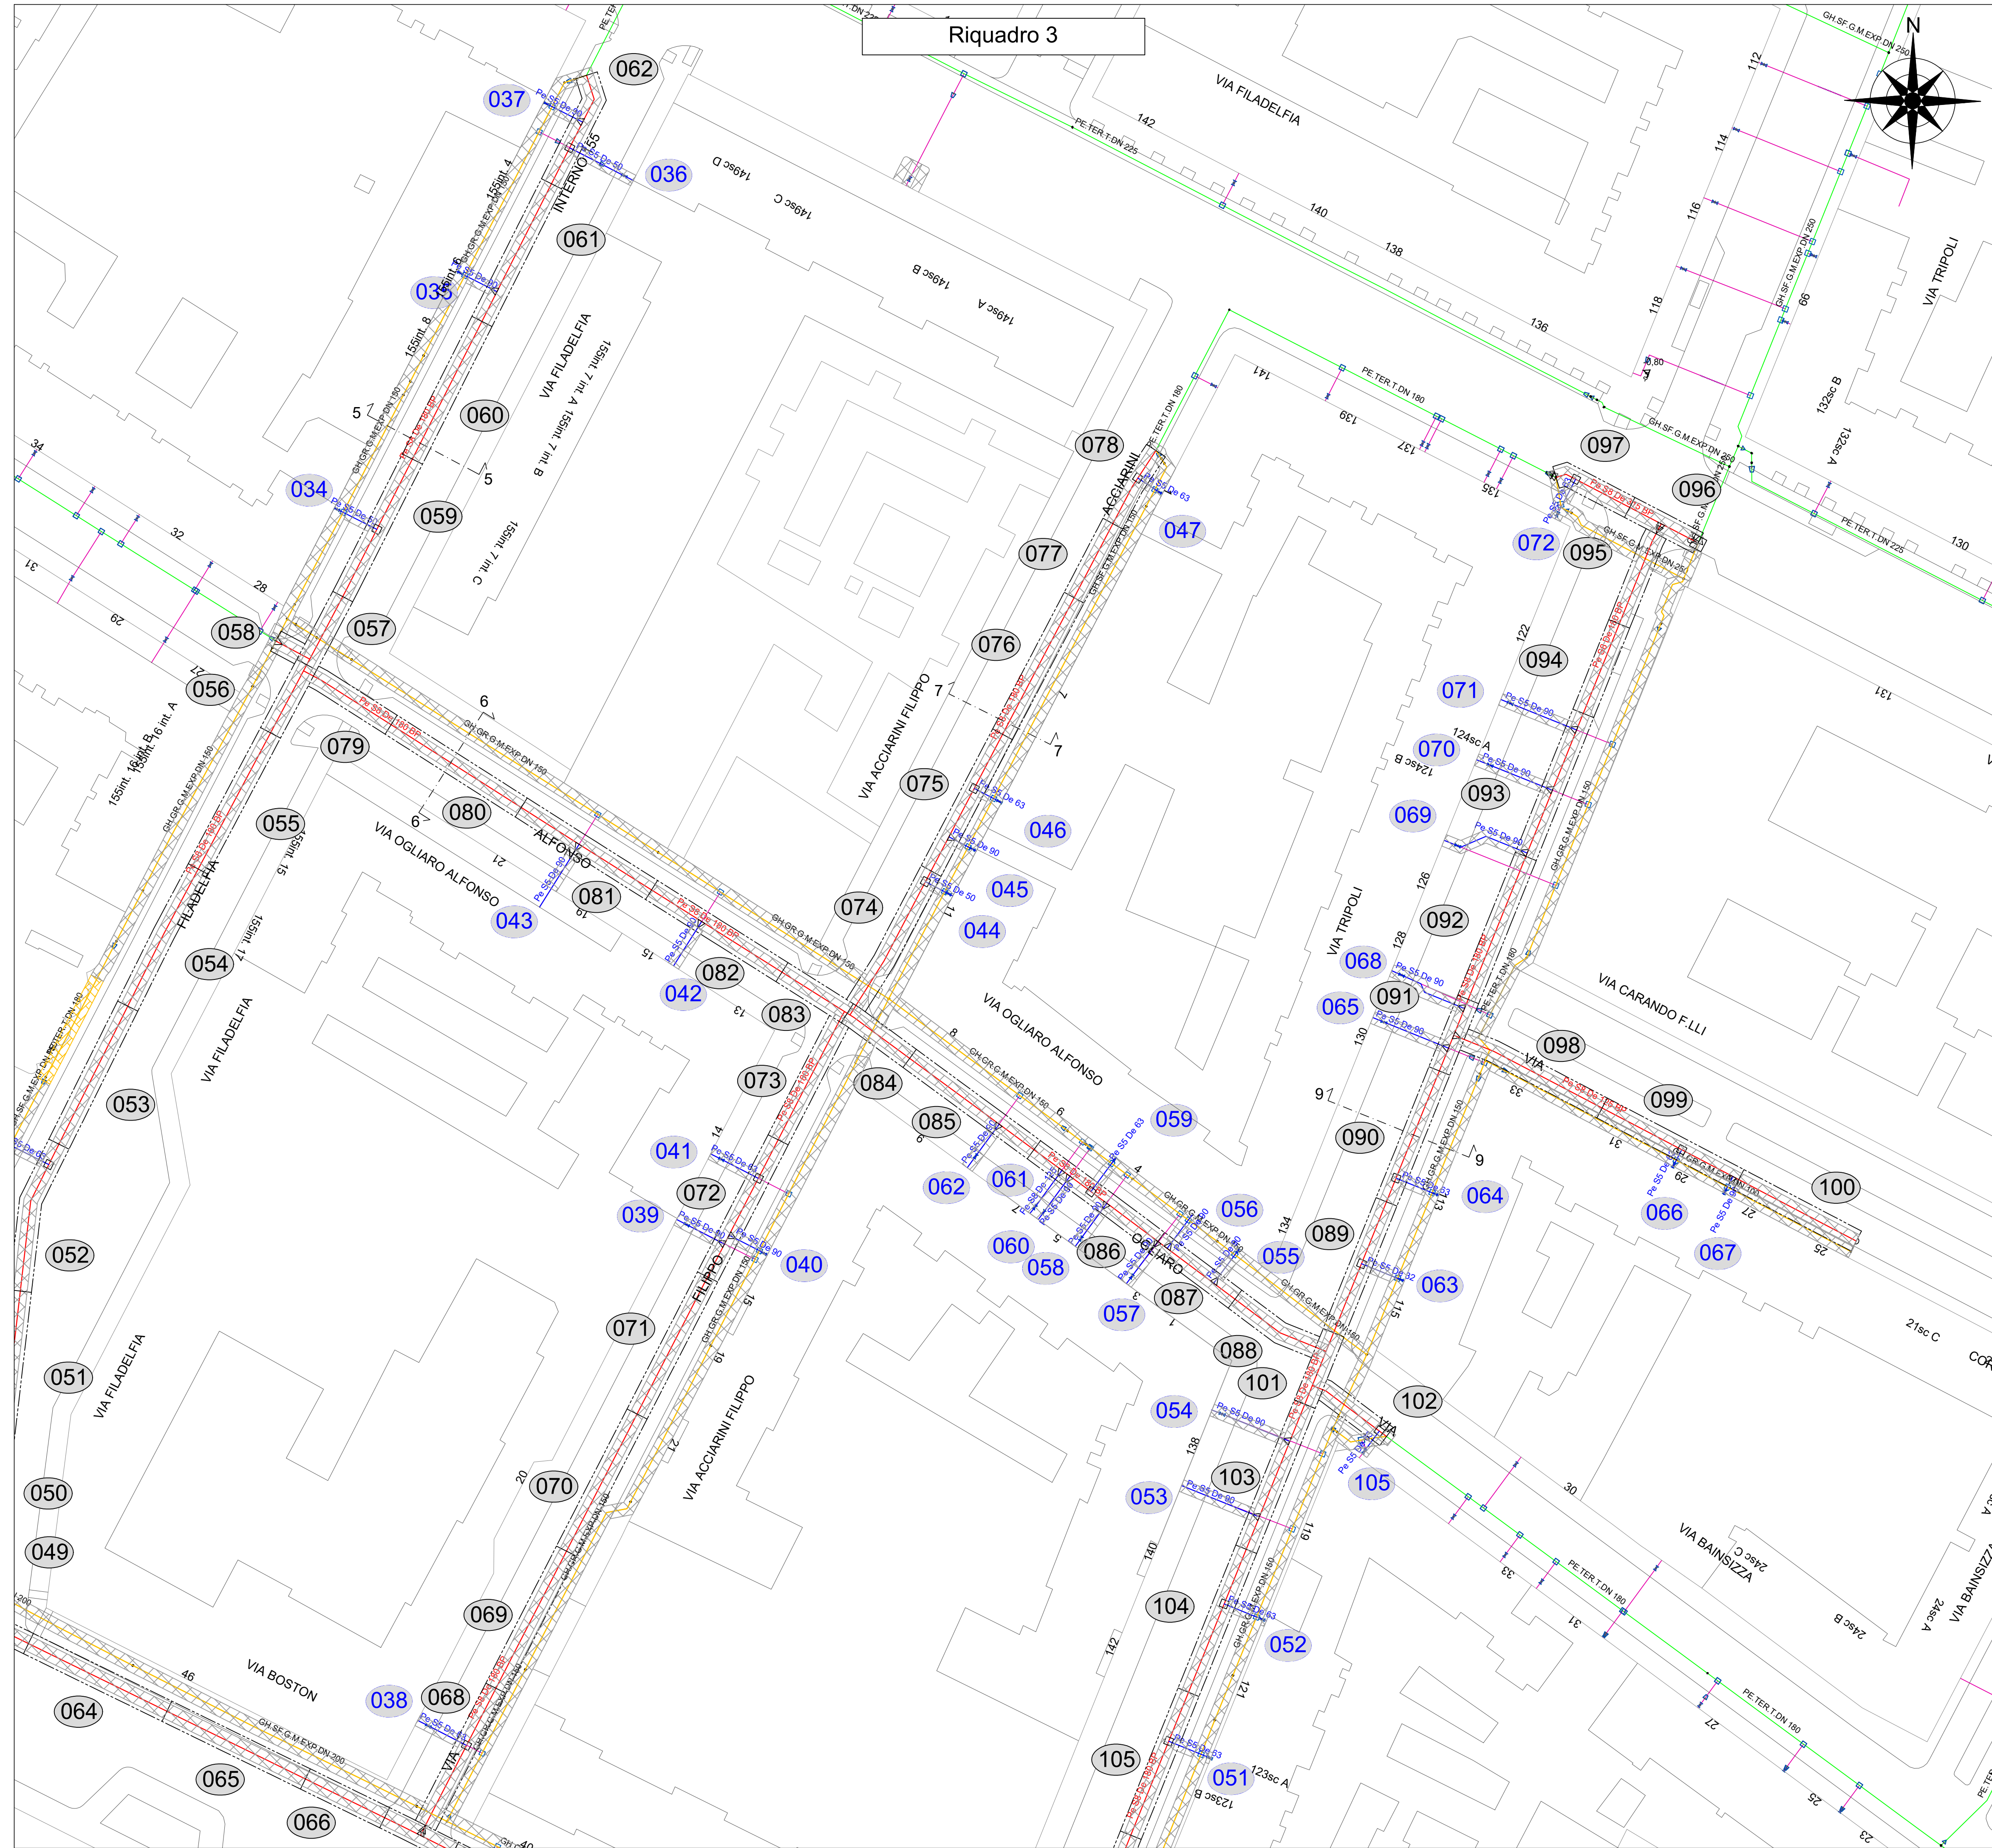

LEGENDA

Rete in progetto BP

Rete in dismissione BP

Zona di lavoro

001

n° Zona di lavoro



Asfalto

Sterrato/area verde

Autobloccanti/ammattionato

|   |   |                                                      |          |         |             |
|---|---|------------------------------------------------------|----------|---------|-------------|
| <div><div><div></div><div>LEARDI</div></div><div>Progetto n°:<br/>22-0320-3E-00-001272<br/>WBS:<br/>SI.20.10300.02.1109<br/>ALLEGATO n°: 6.2</div><div>Formato: A0    Scala 1 : 500</div><div>Committente</div></div> | <div><div><div><div></div><div>INGEGNERI PROV. ALESSANDRIA</div><div>SETTORIO CIVILE AMB. INDUSTRIALE</div><div>ALESSANDRO</div><div>Ordine degli Ingegneri di Alessandria</div><div>matricola n° 1161</div></div></div></div> | Unità Responsabile della Progettazione               |          |         |             |
|   |   | INGEREAL-INGE-PROGRE                                 |          |         |             |
| Descrizione:   | Emissione per commenti   | 0                                                    | 04       | 11      | 22          |
|   |   | Rev.                                                 | G. M. A. | Redatto | Controllato |
| Comune di TORINO (TO)<br>Vie Varie<br>Progetto Esecutivo<br>SOSTITUZIONE RETE IN BP (L=2504.78 m) GARA ATEM TO1<br>Intervento n° SI-036213-001272-TSS-TORIN036<br>Planimetria ripristini - Tavola 2                   | Comune di TORINO (TO)<br>Vie Varie<br>Progetto Esecutivo<br>SOSTITUZIONE RETE IN BP (L=2504.78 m) GARA ATEM TO1<br>Intervento n° SI-036213-001272-TSS-TORIN036<br>Planimetria ripristini - Tavola 2                            | A.Cappelletti    L.Carlasegna    A.Leardi            |          |         |             |
|   |   | Rev. G. M. A.    Redatto    Controllato    Approvato |          |         |             |

Il presente elaborato è di proprietà aziendale - La società tutelerà i propri diritti a termini di legge.

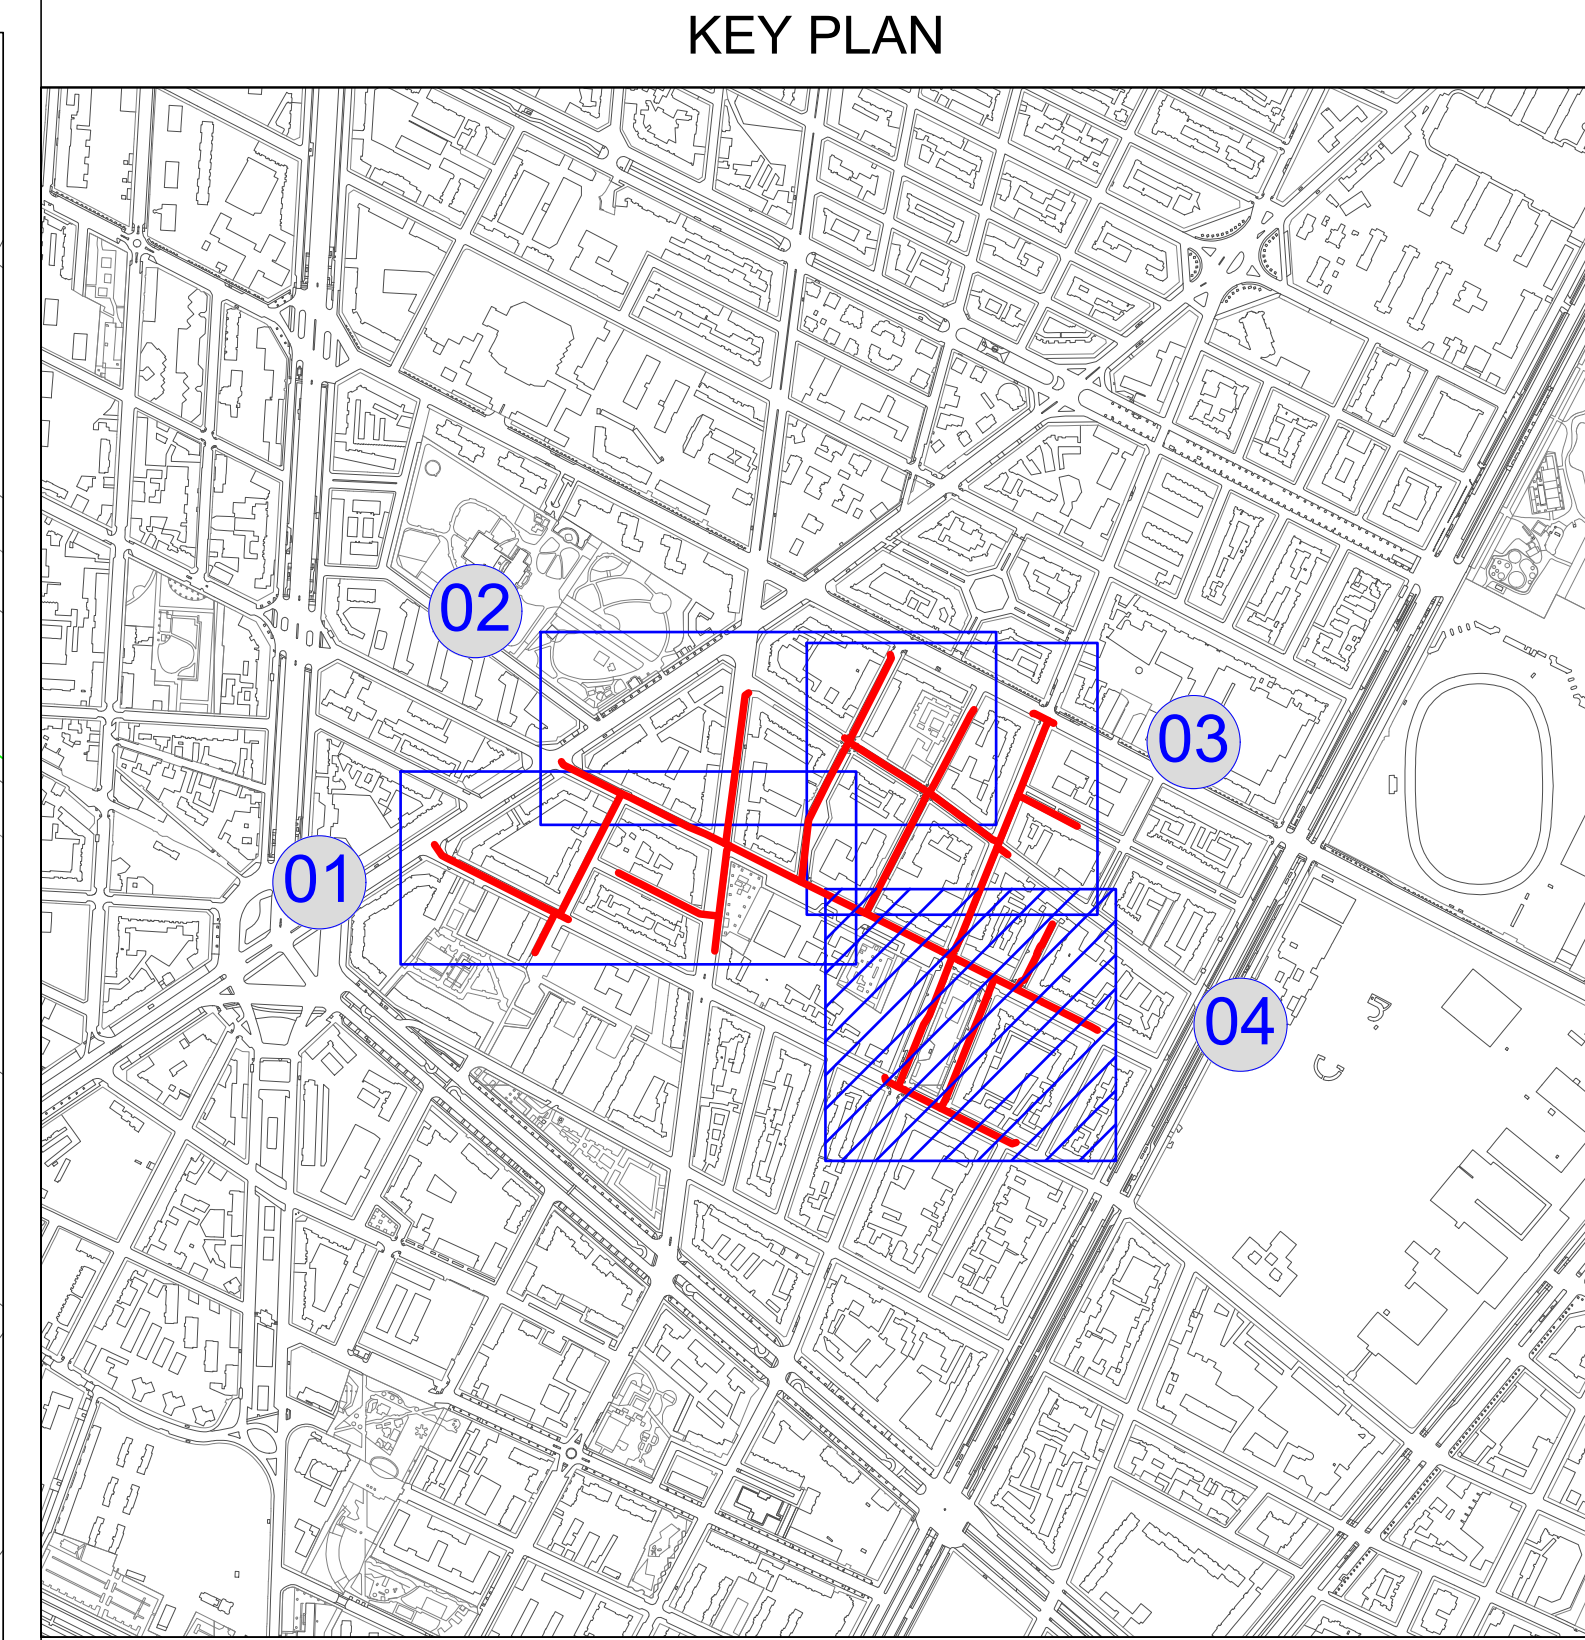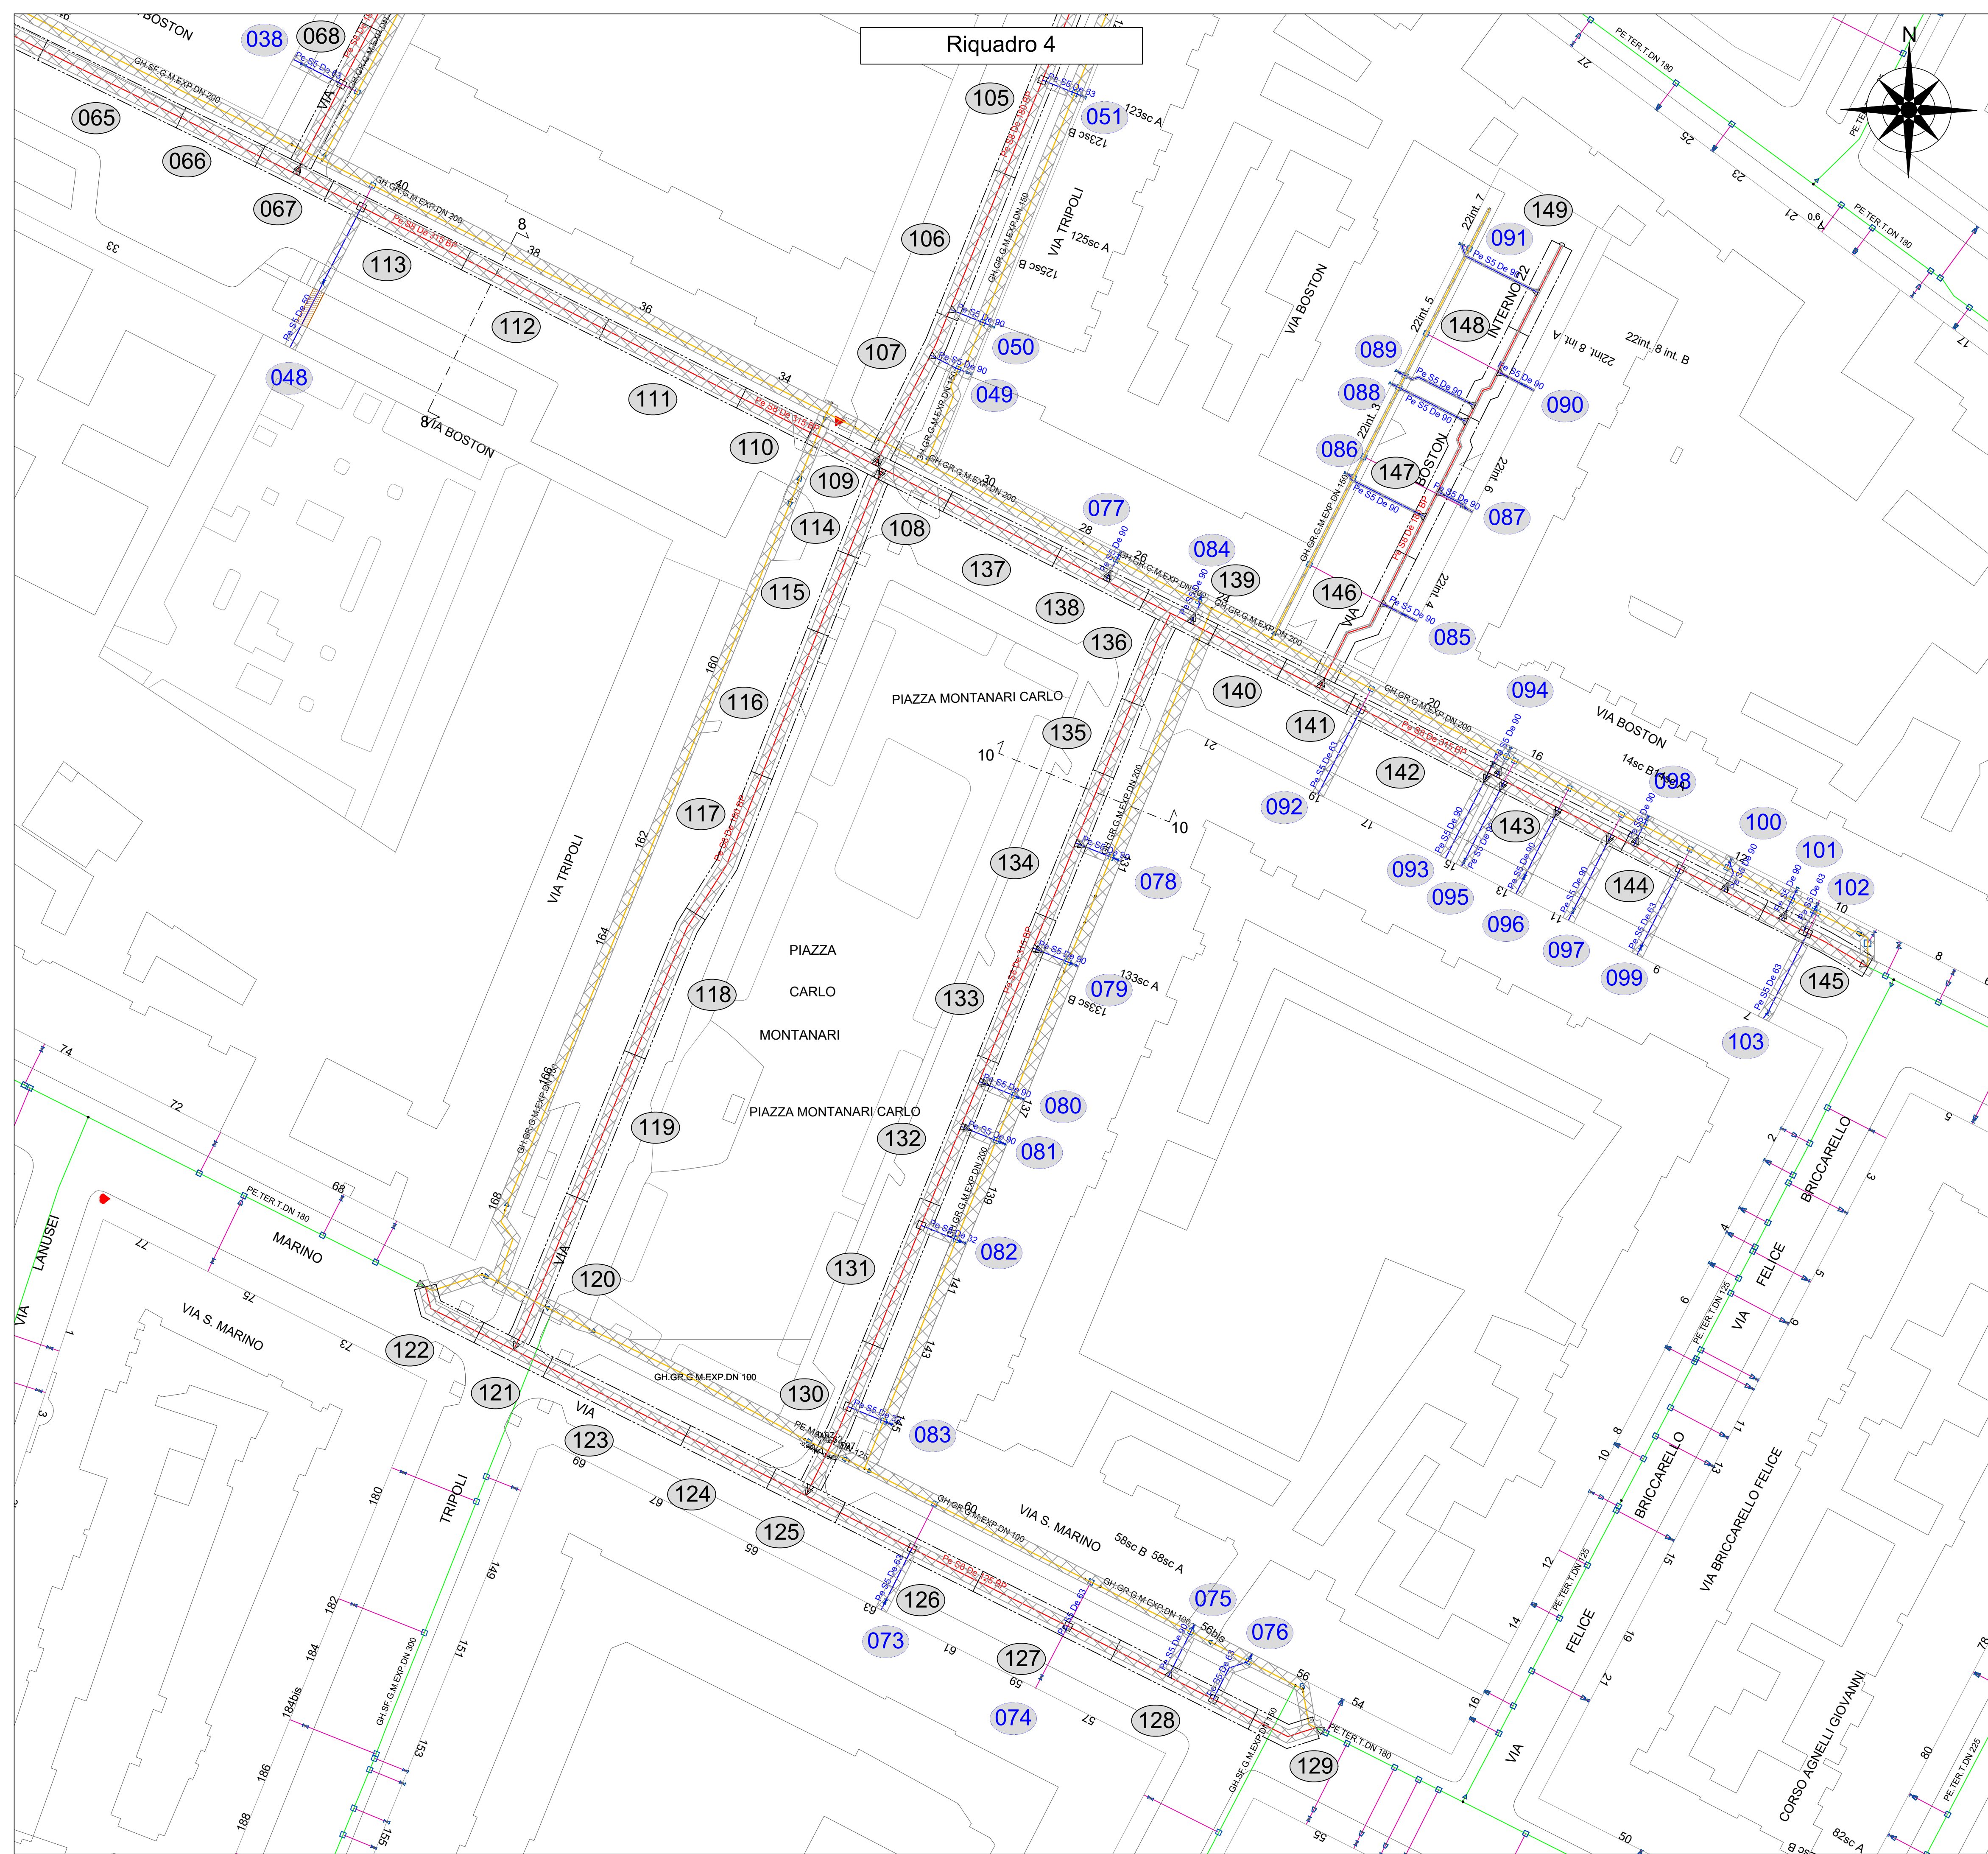

LEGENDA

|  |                        |  |                            |
|--|------------------------|--|----------------------------|
|  | Rete in progetto BP    |  | n° Zona di lavoro          |
|  | Rete in dismissione BP |  | Asfalto                    |
|  | Zona di lavoro         |  | Sterrato/area verde        |
|  |                        |  | Autobloccanti/ammattionato |

|                                                                                         |  |   |  |                                                                    |  |
|-----------------------------------------------------------------------------------------|--|---|--|--------------------------------------------------------------------|--|
|                                                                                         |  | Progettista:<br><br>Ordine degli Ingegneri di Alessandria<br>mat. 6121041-101<br>Firma   |  | Unità Responsabile della Progettazione<br><br>INGEREAL-INGE-PROGRE |  |
| Progetto n°:<br>22-0320-3E-00-001272<br>WBS:<br>SI.20.10300.02.1109<br>ALLEGATO n°: 6.3 |  | Descrizione:   |  |                                                                    |  |
| Nome File: 01.03.03                                                                     |  | Descrizione:   |  |                                                                    |  |
| Formato: A0                                                                             |  | Emissione per commenti   |  |                                                                    |  |
| Committente:                                                                            |  | Comm.: 2464   |  |                                                                    |  |
| Scala 1 : 500                                                                           |  | Rev.   |  | 0 04 11 22<br>G. M. A. A. Cappelletti L. Carisegna A. Leardi       |  |
|                                                                                         |  | Comune di TORINO (TO)<br>Vie Varie<br>Progetto Esecutivo<br>SOSTITUZIONE RETE IN BP (L=2504.78 m) GARA ATEM TO1<br>Intervento n° SI-036213-001272-TSS-TORIN036<br>Planimetria ripristini - Tavola 3 |  |                                                                    |  |

Il presente elaborato è di proprietà aziendale - La società tutelerà i propri diritti a termini di legge.

| Zone di lavoro e pavimentazioni |                 |     |                 |                 |             |
|---------------------------------|-----------------|-----|-----------------|-----------------|-------------|
| n.                              | dati condotta   |     | tipo superficie | lato strada     |             |
|                                 | caratteristiche | bar |                 | lato strada     | Segnaletica |
| 1                               | Pe De 180       | BP  | Asfalto         | Sinistra        | Comunale    |
| 2                               | Pe De 180       | BP  | Asfalto         | Sinistra        | Comunale    |
| 3                               | Pe De 180       | BP  | Asfalto         | Sinistra        | Comunale    |
| 4                               | Pe De 180       | BP  | Asfalto         | Sinistra        | Comunale    |
| 5                               | Pe De 180       | BP  | Asfalto         | Sinistra        | Comunale    |
| 6                               | Pe De 180       | BP  | Asfalto         | Sinistra        | Comunale    |
| 7                               | Pe De 180       | BP  | Asfalto         | Sinistra        | Comunale    |
| 7                               | Pe De 180       | BP  | Asfalto         | Attraversamento | Comunale    |
| 8                               | Pe De 180       | BP  | Asfalto         | Attraversamento | Comunale    |
| 8                               | Pe De 125       | BP  | Asfalto         | Attraversamento | Comunale    |
| 9                               | Pe De 180       | BP  | Asfalto         | Attraversamento | Comunale    |
| 9                               | Pe De 180       | BP  | Asfalto         | Destra          | Comunale    |
| 10                              | Pe De 180       | BP  | Asfalto         | Destra          | Comunale    |
| 11                              | Pe De 125       | BP  | Asfalto         | Sinistra        | Comunale    |
| 12                              | Pe De 125       | BP  | Asfalto         | Sinistra        | Comunale    |
| 13                              | Pe De 125       | BP  | Asfalto         | Sinistra        | Comunale    |
| 14                              | Pe De 125       | BP  | Asfalto         | Sinistra        | Comunale    |
| 15                              | Pe De 125       | BP  | Asfalto         | Sinistra        | Comunale    |
| 16                              | Pe De 125       | BP  | Asfalto         | Sinistra        | Comunale    |
| 16                              | Pe De 125       | BP  | Asfalto         | Attraversamento |             |
| 17                              | Pe De 125       | BP  | Asfalto         | Attraversamento | Comunale    |
| 17                              | Pe De 315       | BP  | Asfalto         | Centro          | Comunale    |
| 18                              | Pe De 315       | BP  | Asfalto         | Centro          | Comunale    |
| 19                              | Pe De 315       | BP  | Asfalto         | Centro          | Comunale    |
| 20                              | Pe De 315       | BP  | Asfalto         | Centro          | Comunale    |
| 21                              | Pe De 315       | BP  | Asfalto         | Sinistra        | Comunale    |
| 22                              | Pe De 315       | BP  | Asfalto         | Sinistra        | Comunale    |
| 23                              | Pe De 315       | BP  | Asfalto         | Sinistra        | Comunale    |
| 24                              | Pe De 315       | BP  | Asfalto         | Sinistra        | Comunale    |
| 25                              | Pe De 315       | BP  | Asfalto         | Sinistra        | Comunale    |
| 25                              | Pe De 315       | BP  | Asfalto         | Attraversamento | Comunale    |
| 26                              | Pe De 315       | BP  | Asfalto         | Attraversamento | Comunale    |
| 26                              | Pe De 180       | BP  | Asfalto         | Attraversamento | Comunale    |
| 27                              | Pe De 315       | BP  | Asfalto         | Sinistra        | Comunale    |
| 27                              | Pe De 180       | BP  | Asfalto         | Attraversamento | Comunale    |
| 28                              | Pe De 180       | BP  | Asfalto         | Attraversamento | Comunale    |
| 28                              | Pe De 180       | BP  | Asfalto         | Sinistra        | Comunale    |
| 29                              | Pe De 180       | BP  | Asfalto         | Sinistra        | Comunale    |
| 30                              | Pe De 180       | BP  | Asfalto         | Sinistra        | Comunale    |
| 31                              | Pe De 180       | BP  | Asfalto         | Sinistra        | Comunale    |
| 31                              | Pe De 125       | BP  | Asfalto         | Attraversamento | Comunale    |
| 32                              | Pe De 180       | BP  | Asfalto         | Sinistra        | Comunale    |
| 33                              | Pe De 180       | BP  | Asfalto         | Sinistra        | Comunale    |
| 34                              | Pe De 125       | BP  | Asfalto         | Attraversamento | Comunale    |
| 34                              | Pe De 125       | BP  | Asfalto         | Destra          | Comunale    |
| 35                              | Pe De 125       | BP  | Asfalto         | Destra          | Comunale    |
| 36                              | Pe De 125       | BP  | Asfalto         | Destra          | Comunale    |
| 37                              | Pe De 125       | BP  | Asfalto         | Destra          | Comunale    |
| 38                              | Pe De 125       | BP  | Asfalto         | Destra          | Comunale    |
| 39                              | Pe De 180       | BP  | Asfalto         | Destra          | Comunale    |
| 40                              | Pe De 180       | BP  | Asfalto         | Destra          | Comunale    |
| 41                              | Pe De 180       | BP  | Asfalto         | Destra          | Comunale    |
| 42                              | Pe De 180       | BP  | Asfalto         | Destra          | Comunale    |
| 43                              | Pe De 180       | BP  | Asfalto         | Destra          | Comunale    |
| 44                              | Pe De 180       | BP  | Asfalto         | Destra          | Comunale    |
| 45                              | Pe De 180       | BP  | Asfalto         | Destra          | Comunale    |
| 46                              | Pe De 315       | BP  | Asfalto         | Sinistra        | Comunale    |
| 47                              | Pe De 315       | BP  | Asfalto         | Sinistra        | Comunale    |
| 48                              | Pe De 315       | BP  | Asfalto         | Sinistra        | Comunale    |
| 49                              | Pe De 180       | BP  | Asfalto         | Centro          | Comunale    |
| 50                              | Pe De 180       | BP  | Asfalto         | Centro          | Comunale    |
| 51                              | Pe De 180       | BP  | Asfalto         | Sinistra        | Comunale    |
| 52                              | Pe De 180       | BP  | Asfalto         | Sinistra        | Comunale    |
| 53                              | Pe De 180       | BP  | Asfalto         | Sinistra        | Comunale    |
| 54                              | Pe De 180       | BP  | Asfalto         | Sinistra        | Comunale    |
| 55                              | Pe De 180       | BP  | Asfalto         | Sinistra        | Comunale    |
| 56                              | Pe De 180       | BP  | Asfalto         | Sinistra        | Comunale    |
| 56                              | Pe De 180       | BP  | Asfalto         | Attraversamento | Comunale    |
| 57                              | Pe De 180       | BP  | Asfalto         | Sinistra        | Comunale    |
| 57                              | Pe De 180       | BP  | Asfalto         | Attraversamento | Comunale    |
| 58                              | Pe De 180       | BP  | Asfalto         | Destra          | Comunale    |
| 59                              | Pe De 180       | BP  | Asfalto         | Sinistra        | Comunale    |
| 60                              | Pe De 180       | BP  | Asfalto         | Sinistra        | Comunale    |
| 61                              | Pe De 180       | BP  | Asfalto         | Sinistra        | Comunale    |
| 62                              | Pe De 180       | BP  | Asfalto         | Sinistra        | Comunale    |
| 63                              | Pe De 315       | BP  | Asfalto         | Attraversamento | Comunale    |
| 63                              | Pe De 180       | BP  | Asfalto         | Attraversamento | Comunale    |
| 64                              | Pe De 315       | BP  | Asfalto         | Sinistra        | Comunale    |
| 65                              | Pe De 315       | BP  | Asfalto         | Sinistra        | Comunale    |
| 66                              | Pe De 315       | BP  | Asfalto         | Sinistra        | Comunale    |
| 67                              | Pe De 315       | BP  | Asfalto         | Attraversamento | Comunale    |
| 67                              | Pe De 180       | BP  | Asfalto         | Attraversamento | Comunale    |
| 68                              | Pe De 180       | BP  | Asfalto         | Destra          | Comunale    |
| 69                              | Pe De 180       | BP  | Asfalto         | Destra          | Comunale    |
| 70                              | Pe De 180       | BP  | Asfalto         | Centro          | Comunale    |
| 71                              | Pe De 180       | BP  | Asfalto         | Centro          | Comunale    |
| 72                              | Pe De 180       | BP  | Asfalto         | Centro          | Comunale    |
| 73                              | Pe De 180       | BP  | Asfalto         | Centro          | Comunale    |
| 74                              | Pe De 180       | BP  | Asfalto         | Destra          | Comunale    |

| Zone di lavoro e pavimentazioni |                 |     |                          |                 |             |
|---------------------------------|-----------------|-----|--------------------------|-----------------|-------------|
| n.                              | dati condotta   |     | tipo superficie          | lato strada     |             |
|                                 | caratteristiche | bar |                          | lato strada     | Segnaletica |
| 75                              | Pe De 180       | BP  | Asfalto                  | Destra          | Comunale    |
| 76                              | Pe De 180       | BP  | Asfalto                  | Destra          | Comunale    |
| 77                              | Pe De 180       | BP  | Asfalto                  | Destra          | Comunale    |
| 78                              | Pe De 180       | BP  | Asfalto                  | Destra          | Comunale    |
| 79                              | Pe De 180       | BP  | Asfalto                  | Centro          | Comunale    |
| 80                              | Pe De 180       | BP  | Asfalto                  | Centro          | Comunale    |
| 81                              | Pe De 180       | BP  | Asfalto                  | Centro          | Comunale    |
| 82                              | Pe De 180       | BP  | Asfalto                  | Centro          | Comunale    |
| 83                              | Pe De 180       | BP  | Asfalto                  | Centro          | Comunale    |
| 83                              | Pe De 180       | BP  | Asfalto                  | Attraversamento | Comunale    |
| 83                              | Pe De 180       | BP  | Asfalto                  | Attraversamento | Comunale    |
| 84                              | Pe De 180       | BP  | Asfalto                  | Centro          | Comunale    |
| 84                              | Pe De 180       | BP  | Asfalto                  | Attraversamento | Comunale    |
| 85                              | Pe De 180       | BP  | Asfalto                  | Centro          | Comunale    |
| 86                              | Pe De 180       | BP  | Asfalto                  | Centro          | Comunale    |
| 87                              | Pe De 180       | BP  | Asfalto                  | Centro          | Comunale    |
| 88                              | Pe De 180       | BP  | Asfalto                  | Centro          | Comunale    |
| 88                              | Pe De 180       | BP  | Asfalto                  | Attraversamento | Comunale    |
| 89                              | Pe De 180       | BP  | Asfalto                  | Destra          | Comunale    |
| 90                              | Pe De 180       | BP  | Asfalto                  | Destra          | Comunale    |
| 91                              | Pe De 180       | BP  | Asfalto                  | Destra          | Comunale    |
| 91                              | Pe De 125       | BP  | Asfalto                  | Attraversamento | Comunale    |
| 92                              | Pe De 180       | BP  | Asfalto                  | Attraversamento | Comunale    |
| 92                              | Pe De 180       | BP  | Asfalto                  | Destra          | Comunale    |
| 93                              | Pe De 180       | BP  | Asfalto                  | Destra          | Comunale    |
| 94                              | Pe De 180       | BP  | Asfalto                  | Destra          | Comunale    |
| 95                              | Pe De 180       | BP  | Asfalto                  | Destra          | Comunale    |
| 96                              | Pe De 315       | BP  | Asfalto                  | Attraversamento | Comunale    |
| 96                              | Pe De 315       | BP  | Asfalto                  | Sinistra        | Comunale    |
| 96                              | Pe De 180       | BP  | Asfalto                  | Attraversamento | Comunale    |
| 97                              | Pe De 315       | BP  | Asfalto                  | Sinistra        | Comunale    |
| 98                              | Pe De 125       | BP  | Asfalto                  | Destra          | Comunale    |
| 99                              | Pe De 125       | BP  | Asfalto                  | Destra          | Comunale    |
| 100                             | Pe De 125       | BP  | Asfalto                  | Destra          | Comunale    |
| 101                             | Pe De 180       | BP  | Asfalto                  | Attraversamento | Comunale    |
| 101                             | Pe De 180       | BP  | Asfalto                  | Attraversamento | Comunale    |
| 101                             | Pe De 180       | BP  | Asfalto                  | Attraversamento | Comunale    |
| 102                             | Pe De 180       | BP  | Asfalto                  | Destra          | Comunale    |
| 103                             | Pe De 180       | BP  | Asfalto                  | Sinistra        | Comunale    |
| 104                             | Pe De 180       | BP  | Asfalto                  | Sinistra        | Comunale    |
| 105                             | Pe De 180       | BP  | Asfalto                  | Sinistra        | Comunale    |
| 106                             | Pe De 180       | BP  | Asfalto                  | Sinistra        | Comunale    |
| 107                             | Pe De 180       | BP  | Asfalto                  | Sinistra        | Comunale    |
| 108                             | Pe De 315       | BP  | Asfalto                  | Destra          | Comunale    |
| 108                             | Pe De 180       | BP  | Asfalto                  | Attraversamento | Comunale    |
| 109                             | Pe De 315       | BP  | Asfalto                  | Destra          | Comunale    |
| 109                             | Pe De 180       | BP  | Asfalto                  | Attraversamento | Comunale    |
| 110                             | Pe De 315       | BP  | Asfalto                  | Destra          | Comunale    |
| 111                             | Pe De 315       | BP  | Asfalto                  | Destra          | Comunale    |
| 112                             | Pe De 315       | BP  | Asfalto                  | Destra          | Comunale    |
| 113                             | Pe De 315       | BP  | Asfalto                  | Destra          | Comunale    |
| 114                             | Pe De 180       | BP  | Asfalto                  | Attraversamento | Comunale    |
| 114                             | Pe De 180       | BP  | Asfalto                  | Sinistra        | Comunale    |
| 115                             | Pe De 180       | BP  | Asfalto                  | Sinistra        | Comunale    |
| 116                             | Pe De 180       | BP  | Asfalto                  | Sinistra        | Comunale    |
| 117                             | Pe De 180       | BP  | Asfalto                  | Sinistra        | Comunale    |
| 118                             | Pe De 180       | BP  | Asfalto                  | Centro          | Comunale    |
| 119                             | Pe De 180       | BP  | Asfalto                  | Centro          | Comunale    |
| 120                             | Pe De 180       | BP  | Asfalto                  | Centro          | Comunale    |
| 121                             | Pe De 125       | BP  | Asfalto                  | Attraversamento | Comunale    |
| 121                             | Pe De 180       | BP  | Asfalto                  | Attraversamento | Comunale    |
| 122                             | Pe De 125       | BP  | Asfalto                  | Destra          | Comunale    |
| 123                             | Pe De 125       | BP  | Asfalto                  | Centro          | Comunale    |
| 124                             | Pe De 125       | BP  | Asfalto                  | Centro          | Comunale    |
| 125                             | Pe De 125       | BP  | Asfalto                  | Attraversamento | Comunale    |
| 125                             | Pe De 315       | BP  | Asfalto                  | Attraversamento | Comunale    |
| 126                             | Pe De 125       | BP  | Asfalto                  | Centro          | Comunale    |
| 127                             | Pe De 125       | BP  | Asfalto                  | Centro          | Comunale    |
| 128                             | Pe De 125       | BP  | Asfalto                  | Centro          | Comunale    |
| 129                             | Pe De 125       | BP  | Asfalto                  | Centro          | Comunale    |
| 130                             | Pe De 315       | BP  | Asfalto                  | Centro          | Comunale    |
| 131                             | Pe De 315       | BP  | Asfalto                  | Centro          | Comunale    |
| 132                             | Pe De 315       | BP  | Asfalto                  | Centro          | Comunale    |
| 133                             | Pe De 315       | BP  | Asfalto                  | Centro          | Comunale    |
| 134                             | Pe De 315       | BP  | Asfalto                  | Centro          | Comunale    |
| 135                             | Pe De 315       | BP  | Asfalto                  | Centro          | Comunale    |
| 136                             | Pe De 315       | BP  | Asfalto                  | Centro          | Comunale    |
| 136                             | Pe De 315       | BP  | Asfalto                  | Attraversamento | Comunale    |
| 137                             | Pe De 315       | BP  | Asfalto                  | Sinistra        | Comunale    |
| 138                             | Pe De 315       | BP  | Asfalto                  | Sinistra        | Comunale    |
| 139                             | Pe De 315       | BP  | Asfalto                  | Sinistra        | Comunale    |
| 139                             | Pe De 315       | BP  | Asfalto                  | Attraversamento | Comunale    |
| 140                             | Pe De 315       | BP  | Asfalto                  | Sinistra        | Comunale    |
| 141                             | Pe De 315       | BP  | Asfalto                  | Attraversamento | Comunale    |
| 141                             | Pe De 180       | BP  | Asfalto                  | Attraversamento | Comunale    |
| 142                             | Pe De 315       | BP  | Asfalto                  | Sinistra        | Comunale    |
| 143                             | Pe De 315       | BP  | Asfalto                  | Sinistra        | Comunale    |
| 144                             | Pe De 315       | BP  | Asfalto                  | Sinistra        | Comunale    |
| 145                             | Pe De 315       | BP  | Asfalto                  | Sinistra        | Comunale    |
| 146                             | Pe De 180       | BP  | Asfalto (Strada privata) | Destra          | Privato     |
| 147                             | Pe De 180       | BP  | Asfalto (Strada privata) | Destra          | Privato     |
| 148                             | Pe De 180       | BP  | Asfalto (Strada privata) | Destra          | Privato     |
| 149                             | Pe De 180       | BP  | Asfalto (Strada privata) | Destra          | Privato     |

|                                                                                         |   |                                                         |
|-----------------------------------------------------------------------------------------|---|---------------------------------------------------------|
|    | Progettista:<br><br>Alessandro Leardi<br>Ing. Civile                                                           | Unità Responsabile della Progettazione                  |
| Progetto n°:<br>22-0320-3E-00-001272<br>WBS:<br>SI.20.10300.02.1109<br>ALLEGATO n°: 6.4 | Descrizione:   | INGEREAL-INGE-PROGRE                                    |
| Nome File: 01.0.png                                                                     | Descrizione:<br>Emissione per commenti   | 0 04 11 22 L.Tosonotti L.Cartasegna A.Leardi            |
| Formato: A1                                                                             | Scala: 1 : -   | Comm.: 2464 Rev. G. M. A. Redatto Controllato Approvato |
| Committente                                                                             | Comune di TORINO (TO)<br>Vie Varie<br>Progetto Esecutivo<br>SOSTITUZIONE RETE IN BP (L=2504.78 m) GARA ATEM TO1<br>Intervento n° SI-036213-001272-TSS-TORIN036<br>Planimetria ripristini - Tavola 4 |                                                         |