




Sezione tipo
percorrenza/attraversamento marciapiede strada comunale
asfaltata
Condotta gas in progetto/dismissione Pe De 180/
ACC-GH DN 150/GH DN 200/Pe De 225/ ACC DN 200

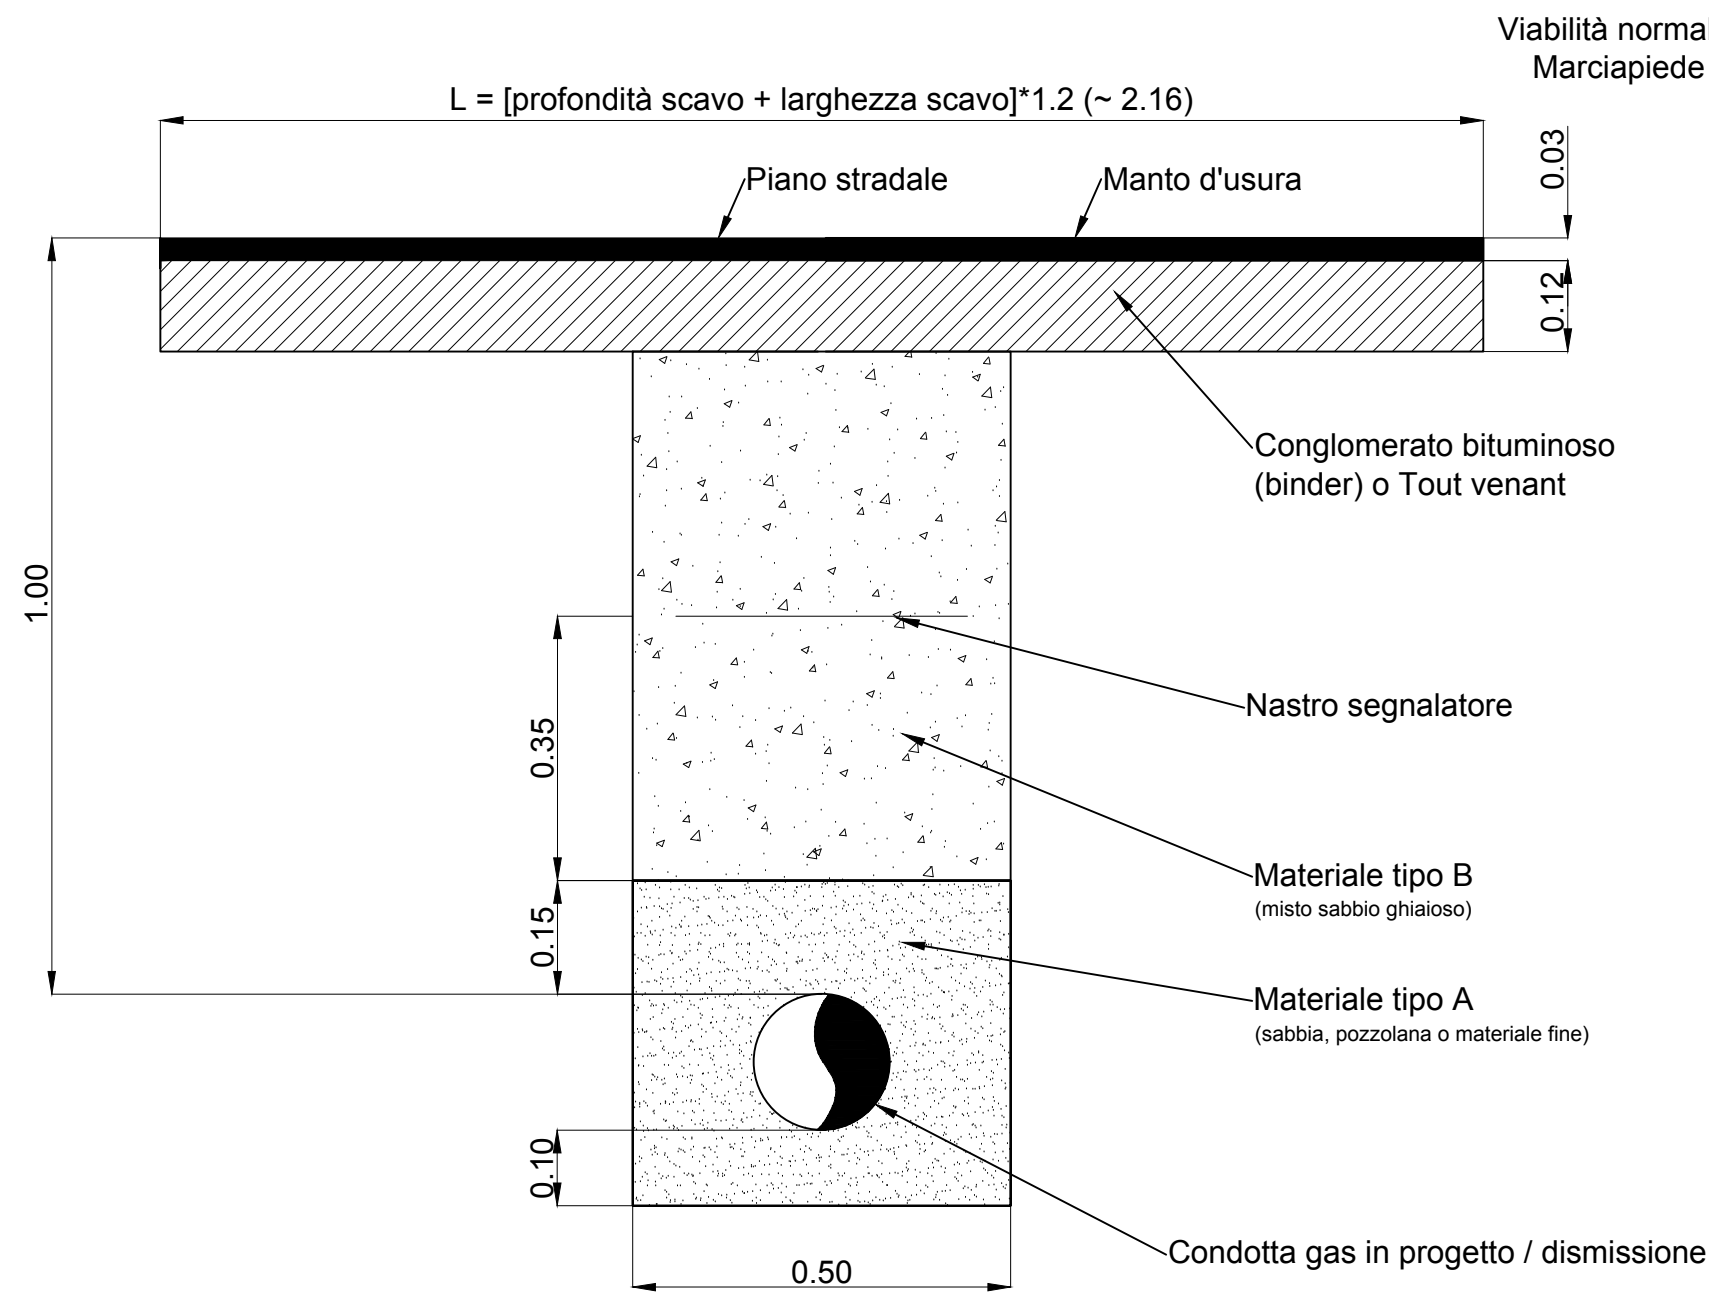

Sezione tipo
percorrenza/attraversamento marciapiede strada comunale
asfaltata
Condotta gas in progetto/dismissioni Pe De 315/ GH
DN 300/GH DN 250

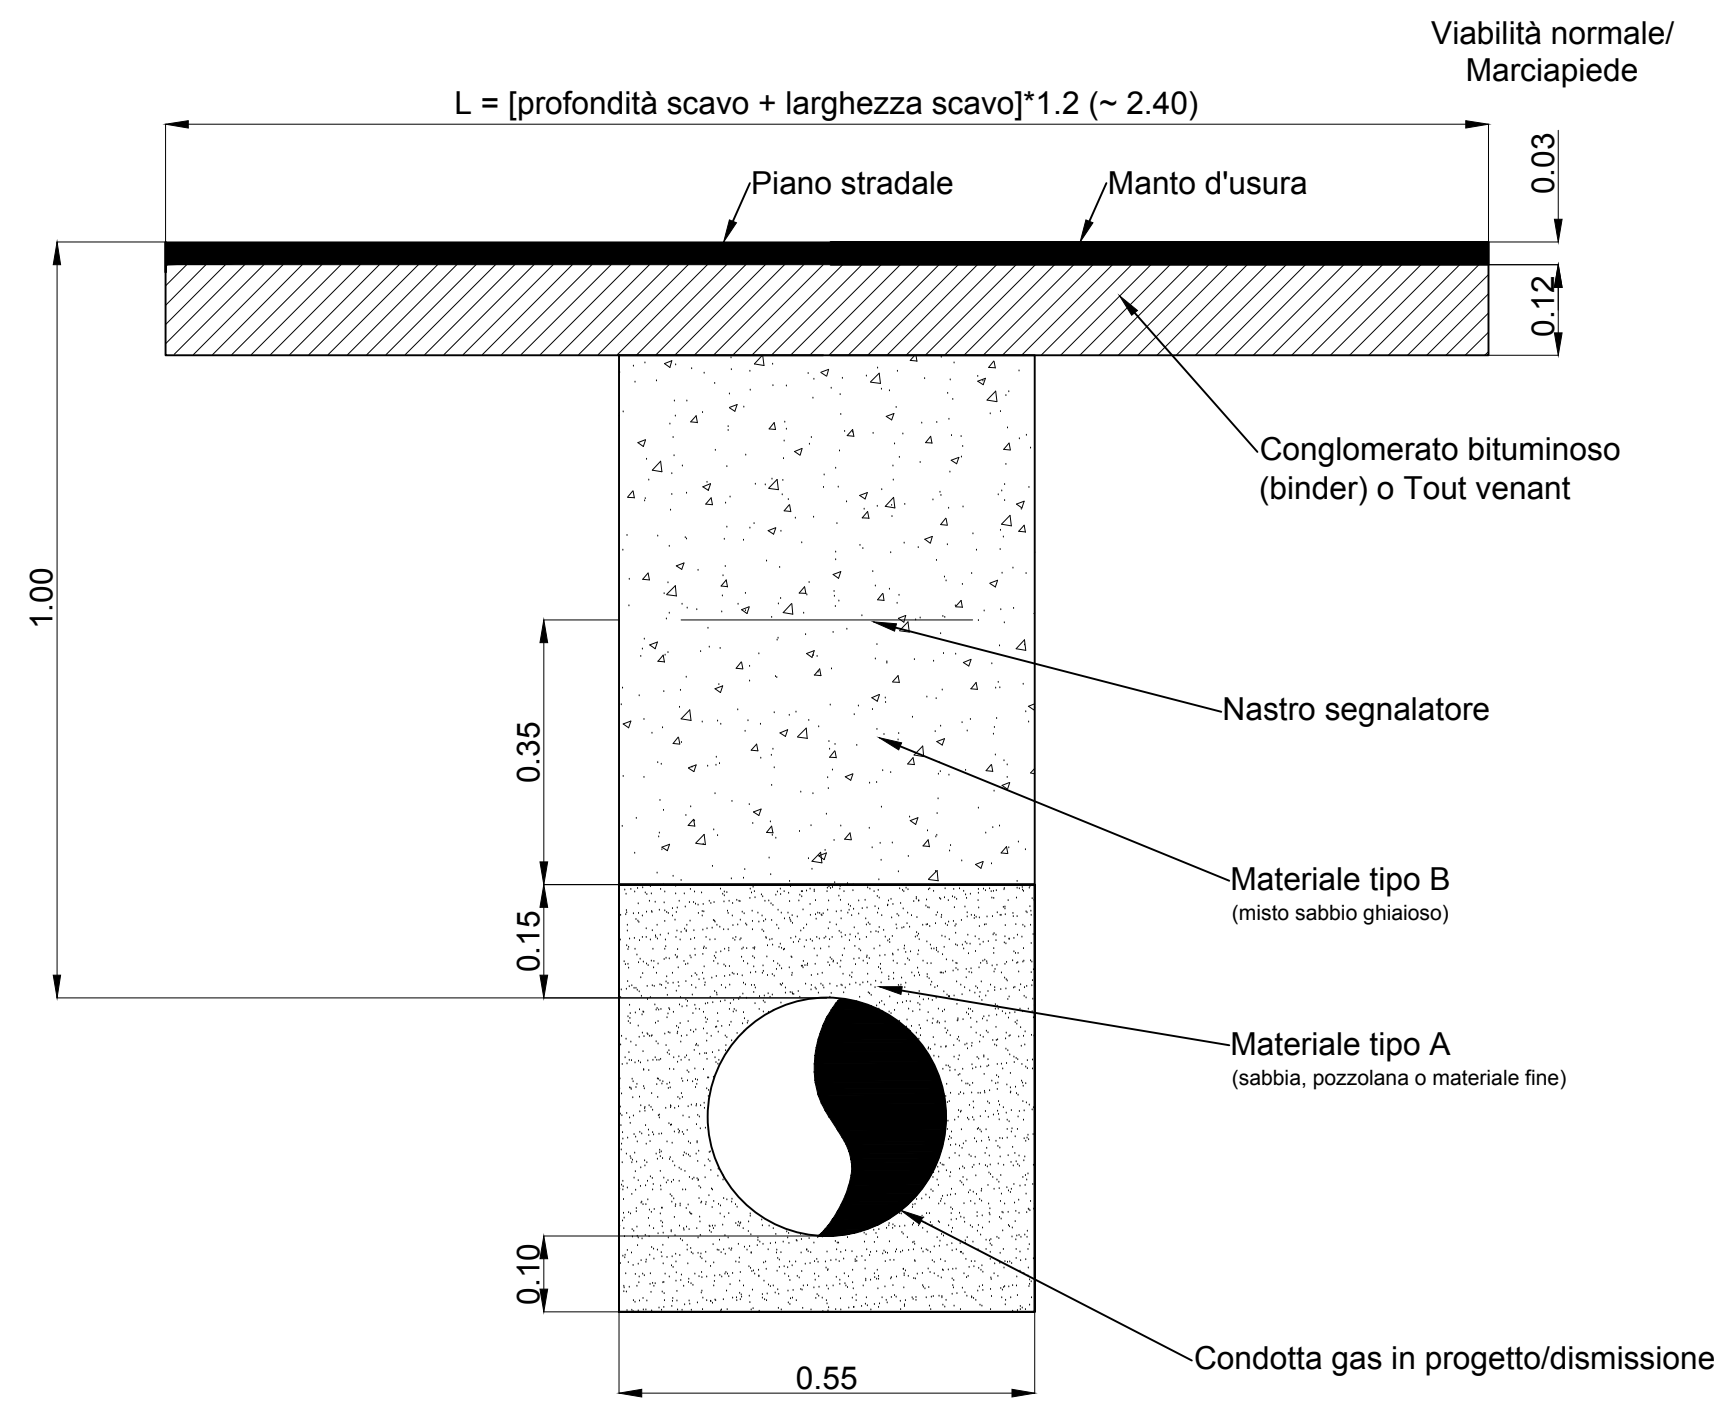

Sezione tipo
pavimentazione autobloccanti
Condotta gas in dismissione Pe De 180

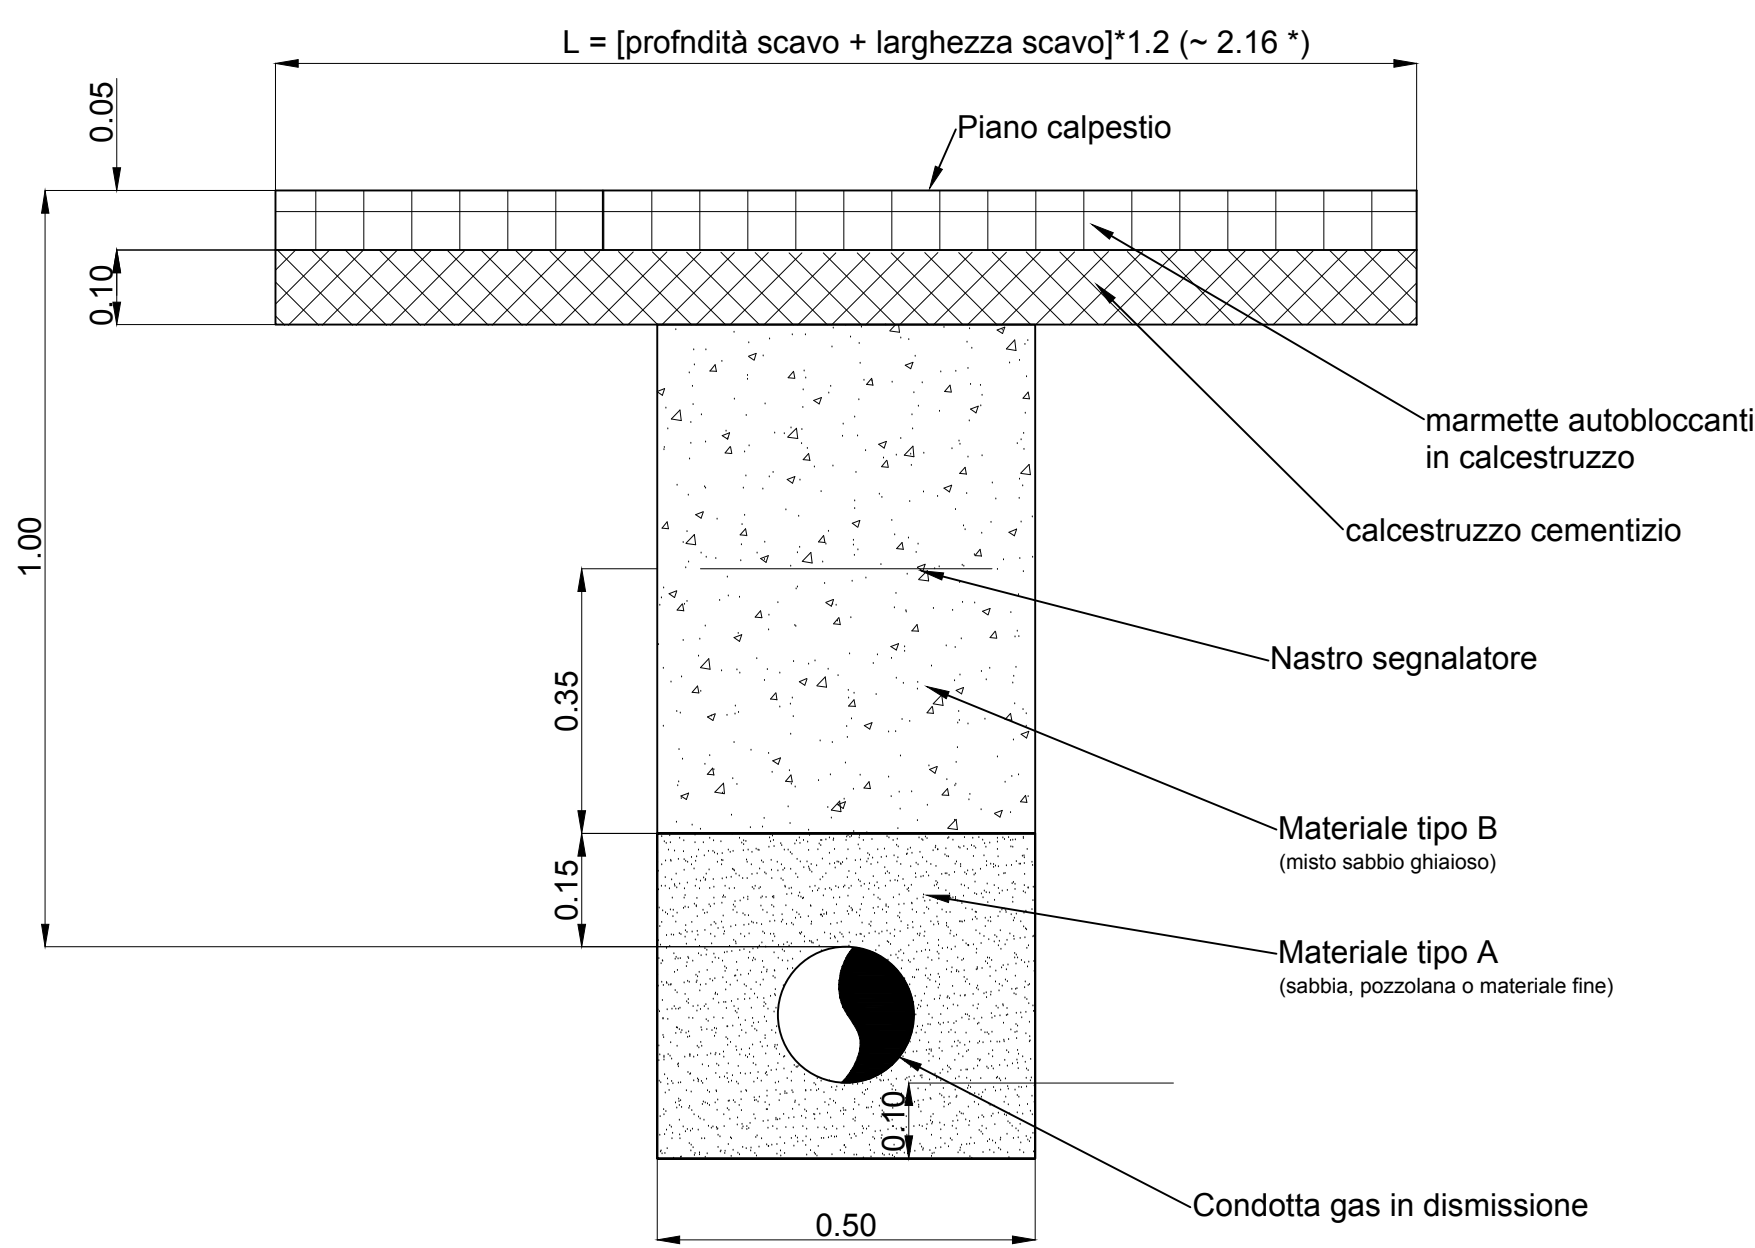

Sezione tipo
percorrenza/attraversamento marciapiede strada comunale
asfaltata
Condotta gas in progetto/dismissione Pe De 125/ GH DN 100

