




Tipologico 1
Collegamento a Ti ridotto Acc DN 250/150
Nodo 1

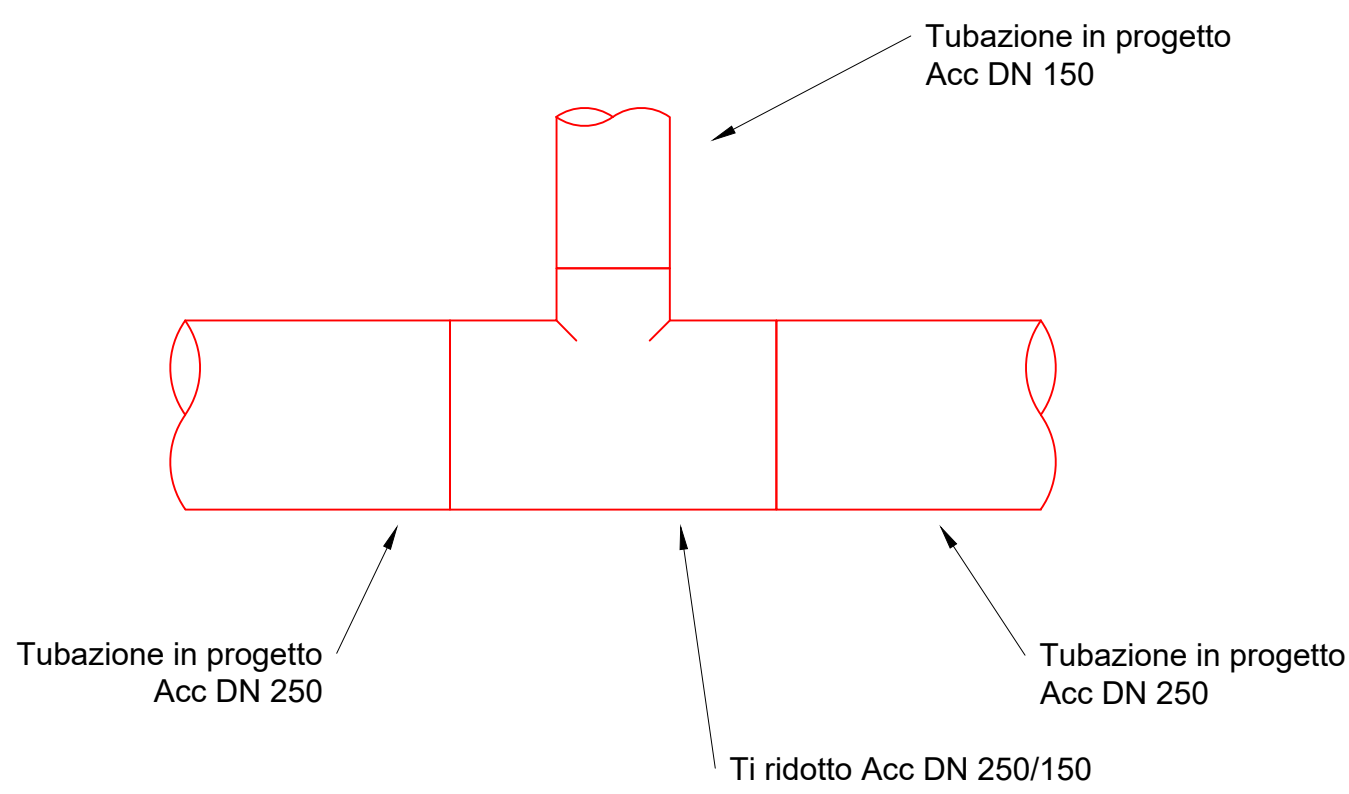


Tipologico 2
Collegamento a Ti ridotto Pe De 180/90
Nodi 2-3-4-17-29-30-33-34-36-37-39-42-43-44-45
49-50-51-52-53-55-56-60-61-62-63-80-81-82-83-84-85-86

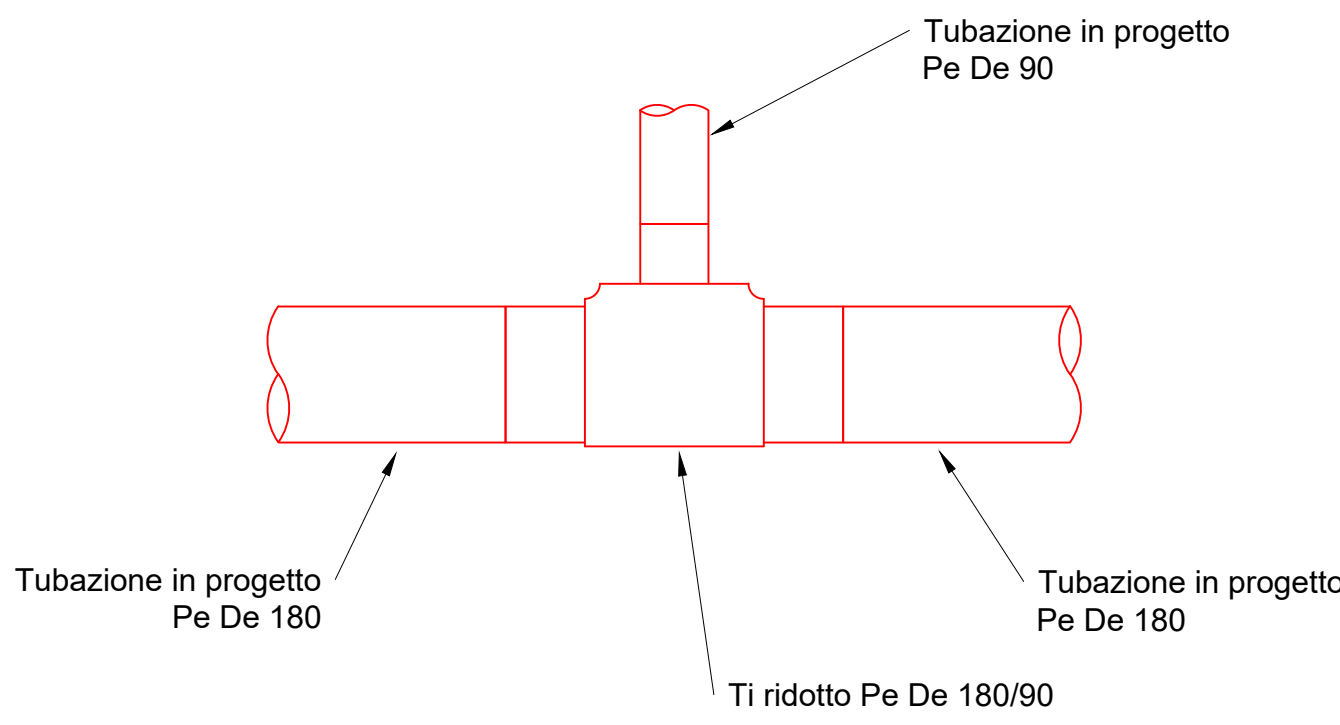


Tipologico 3
Collegamento a Ti di linea Pe De 180
Nodi 5-26-27-35-38-46-48

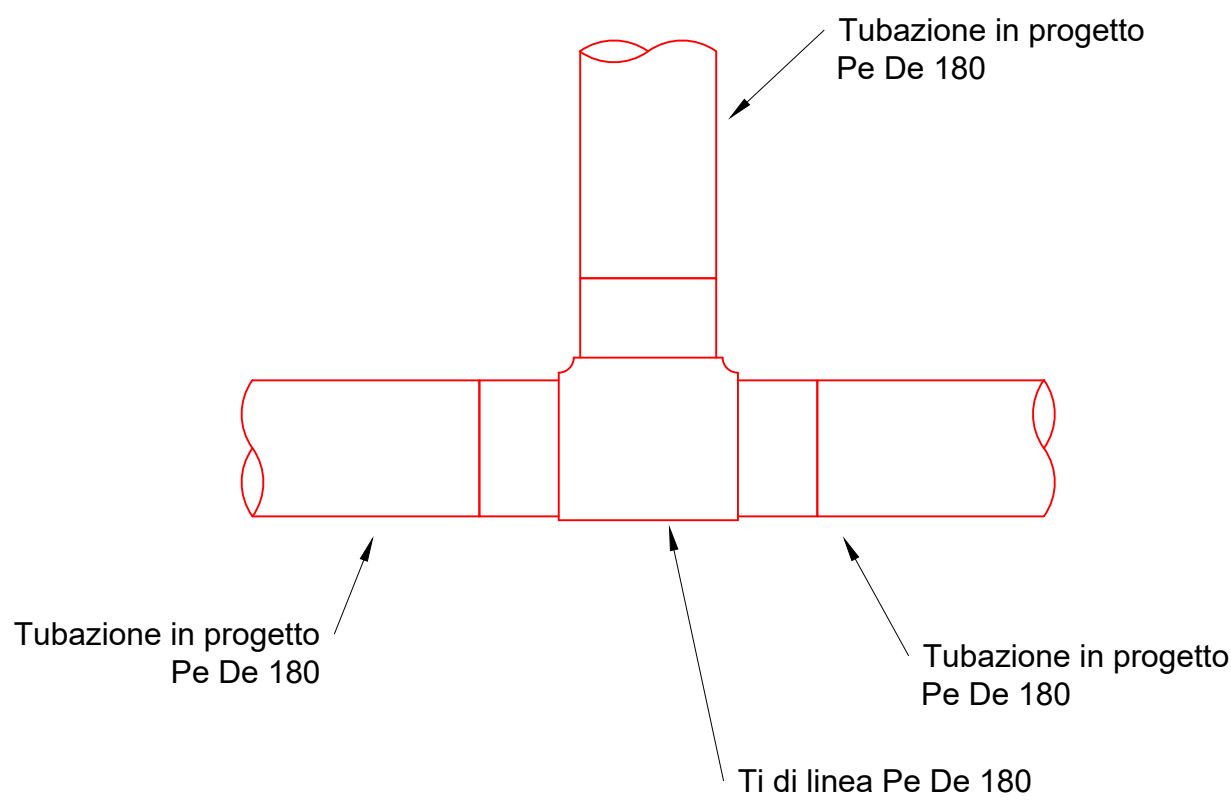


Tipologico 4
Fondello Pe De 180
Nodi 6-87

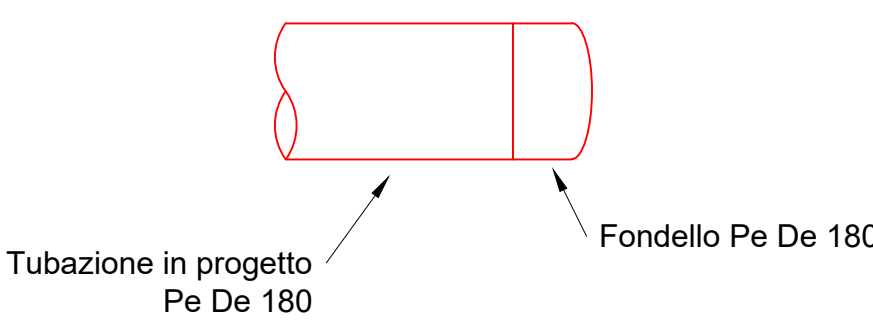


Tipologico 5
Collegamento a Ti ridotto Pe De 180/125
Nodi 7-20-54-57

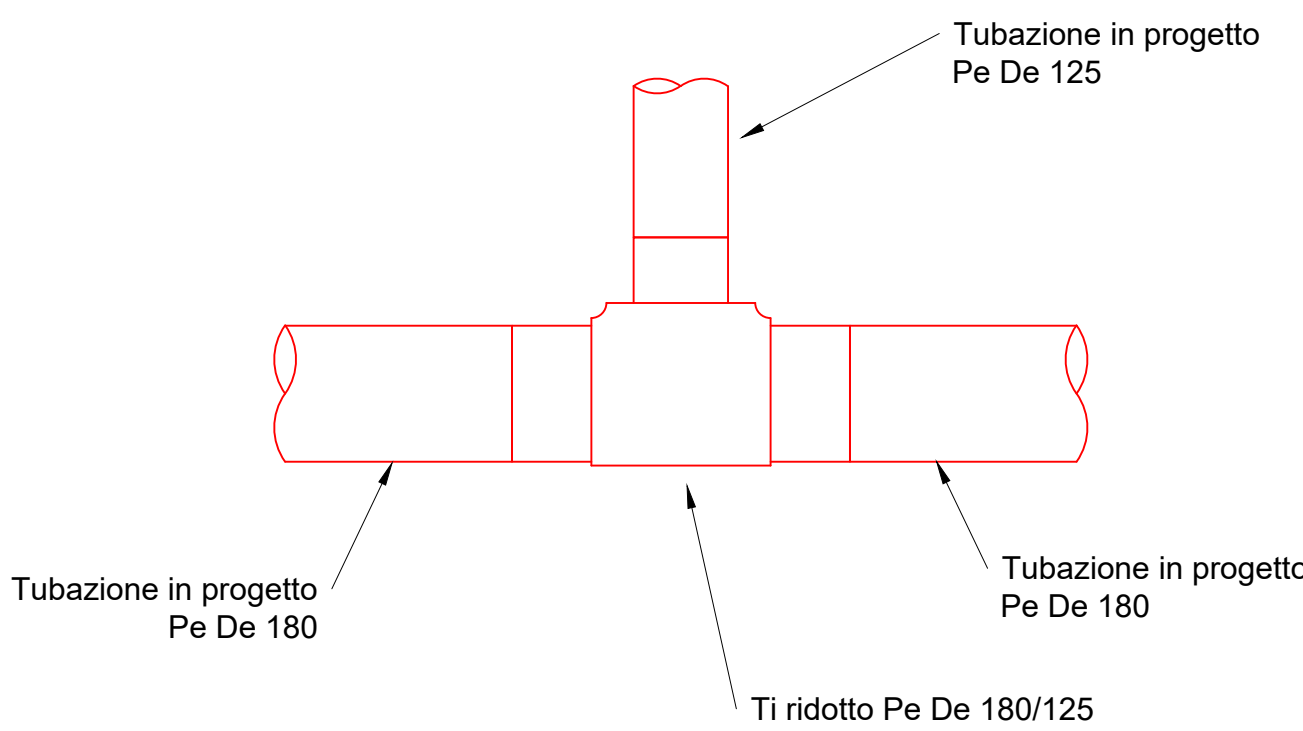


Tipologico 6
Collegamento in linea Pe De 180
Nodi 8-40-47

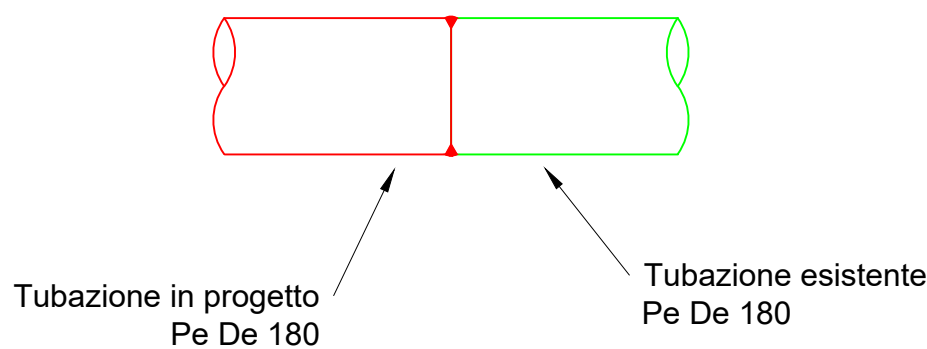


Tipologico 7
Collegamento a Ti ridotto Pe De 125/90
Nodi 9-10-22-23-58-71-97

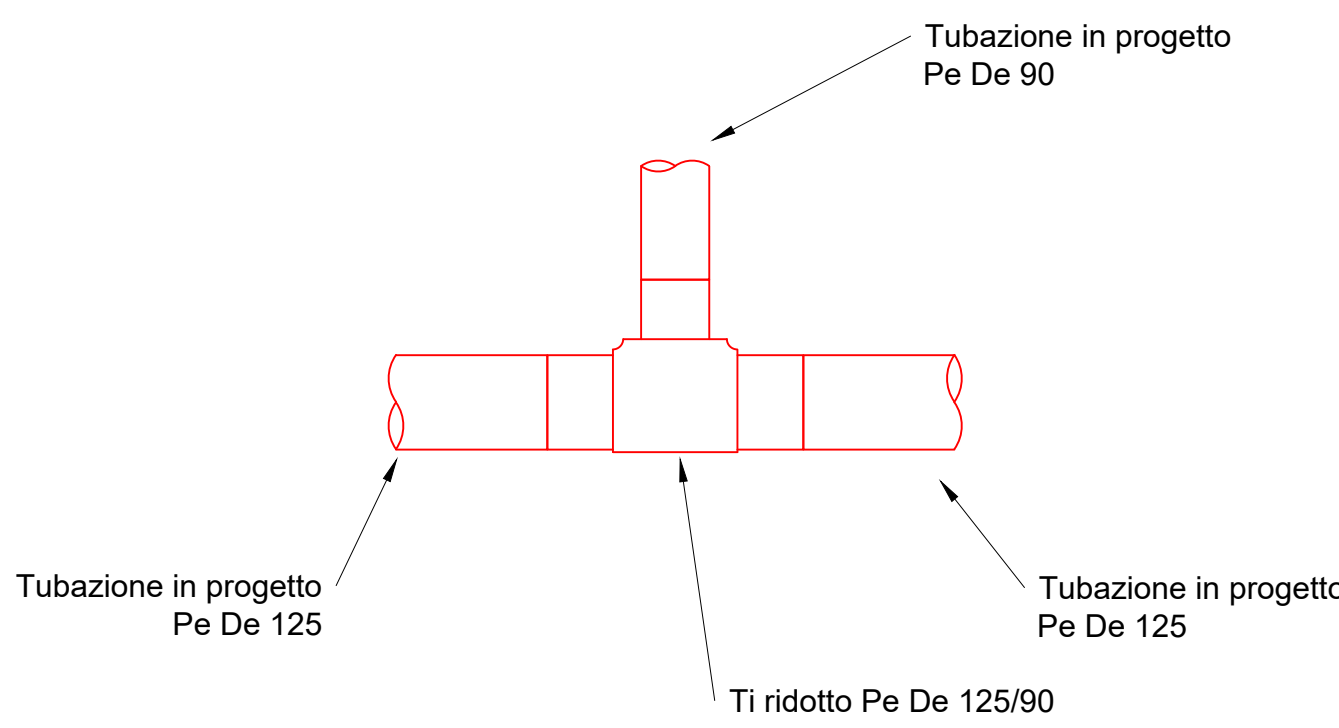


Tipologico 8
Collegamento a Ti ridotto Pe De 315/225
Nodi 11-12-14-15-16-19-25
32-41-64-67-73-74-75-76-77
78-79-88-89-90-91-92-93-94-95

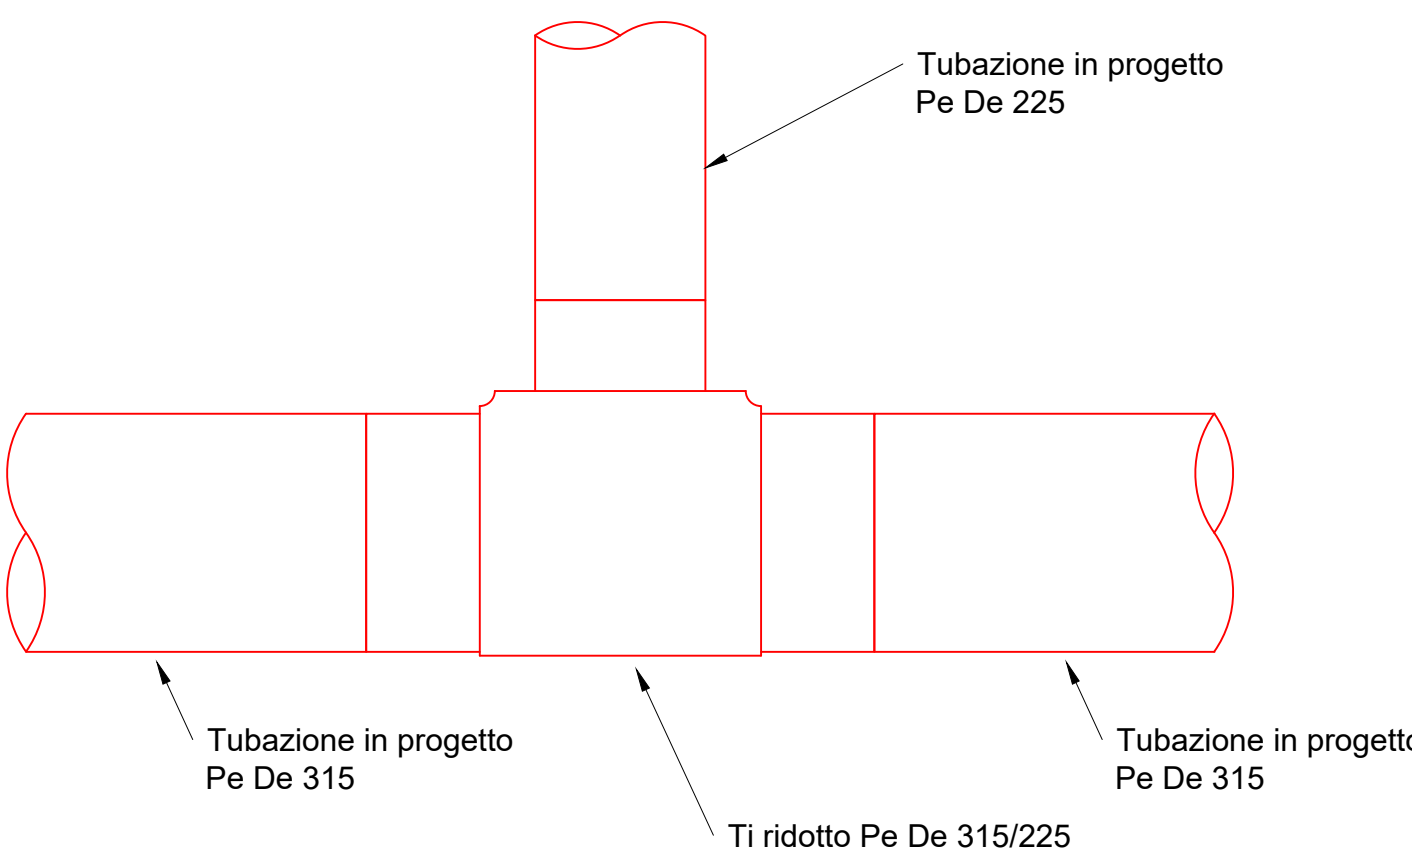


Tipologico 9
Collegamento a Ti di linea Acc DN 250
Nodo 13

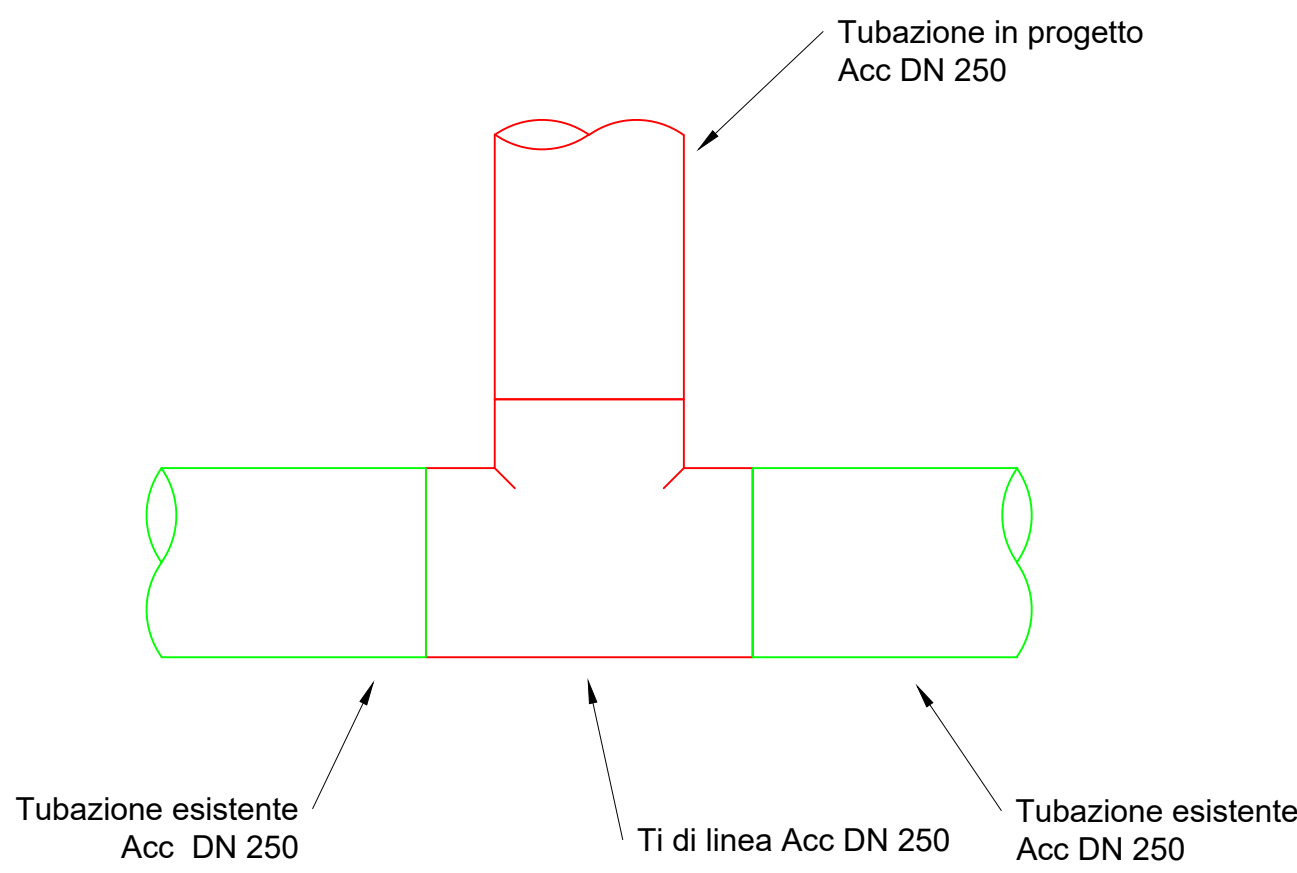


Tipologico 10
Collegamento in linea curva 45° Pe De 180
Nodi 18-31

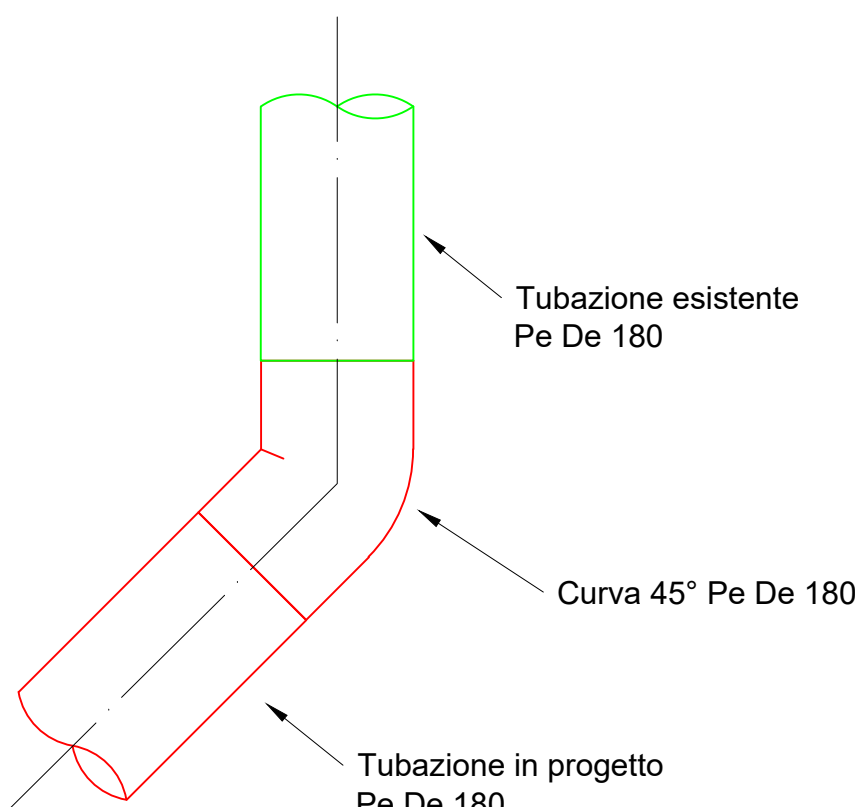


Tipologico 11
Riduzione in linea Pe De 180/125
Nodo 21

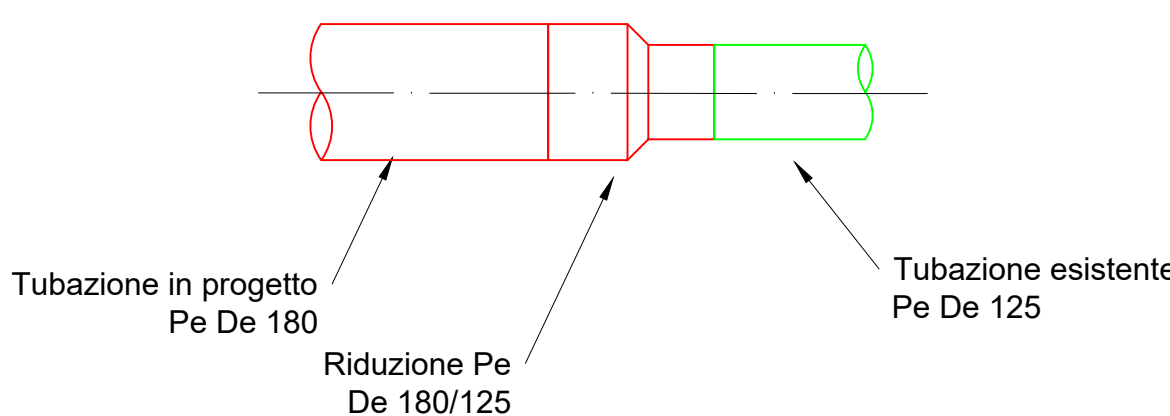


Tipologico 12
Fondello Pe De 125
Nodi 24-59

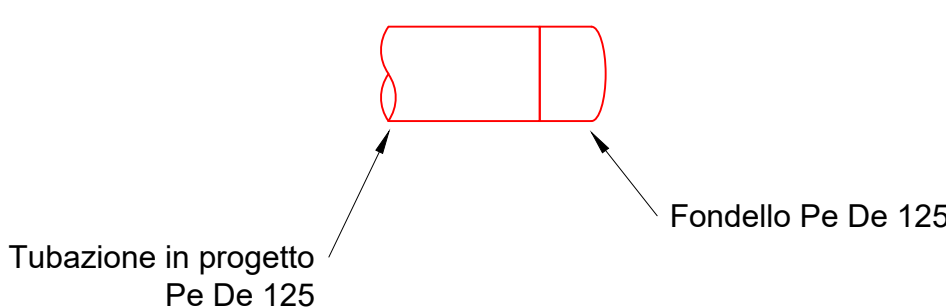


Tipologico 13
Riduzione in linea Pe De 225/180
Nodi 28-65

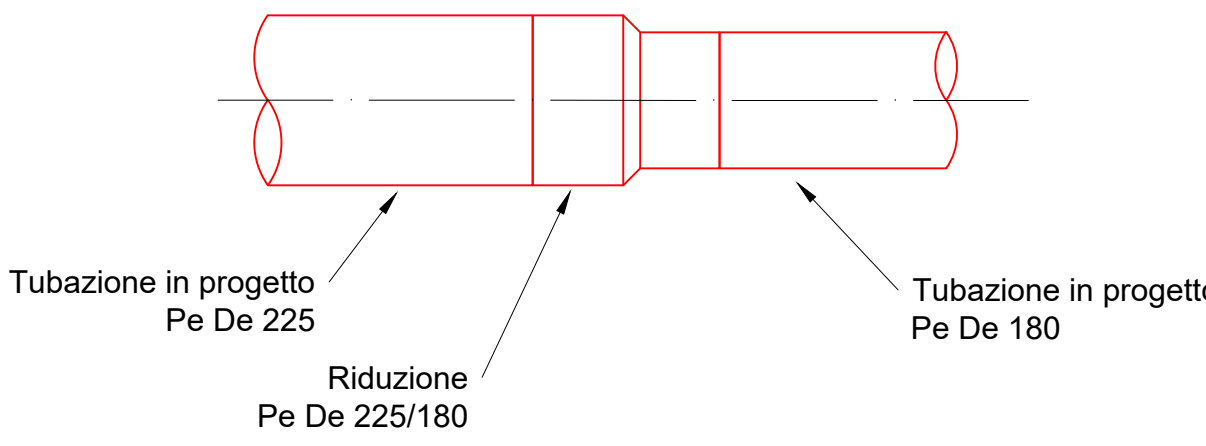


Tipologico 14
Collegamento in linea curva 90° Pe De 315
Nodo 66

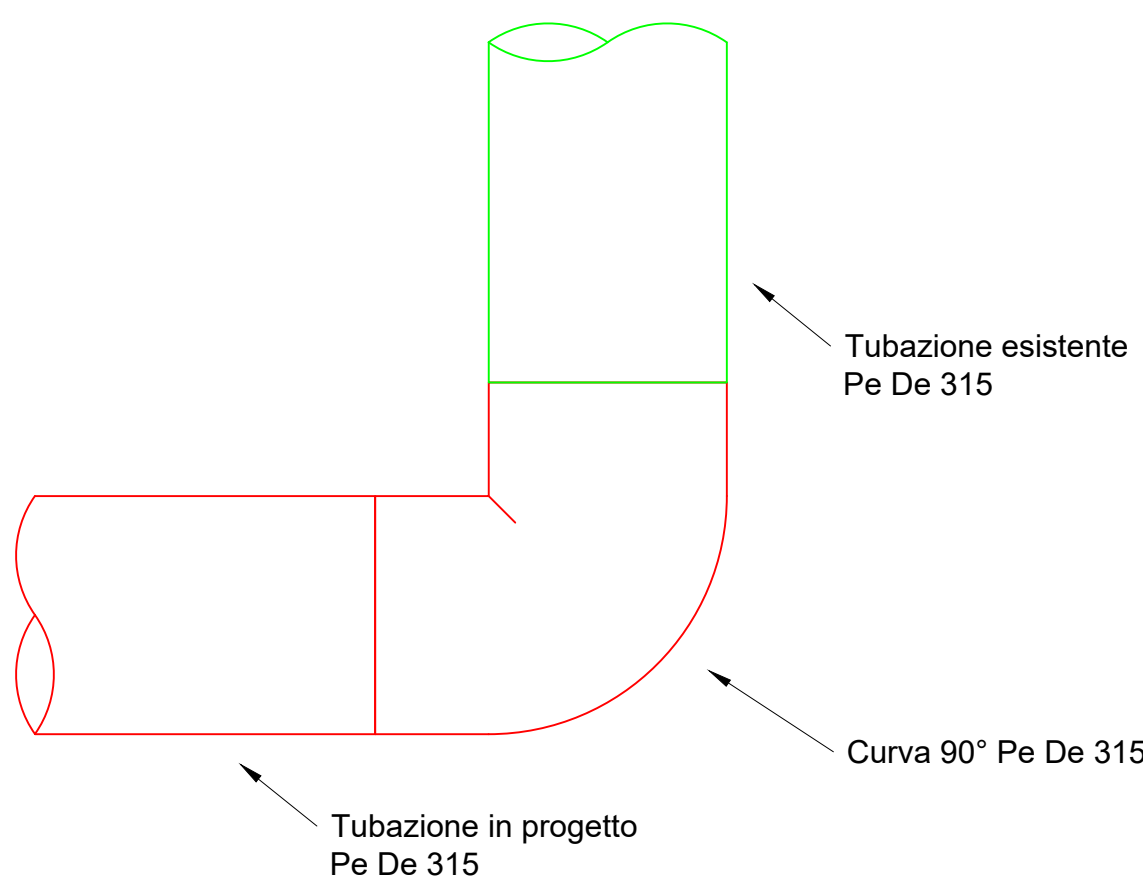


Tipologico 15
Collegamento a Ti di linea Pe De 125
Nodi 68-70

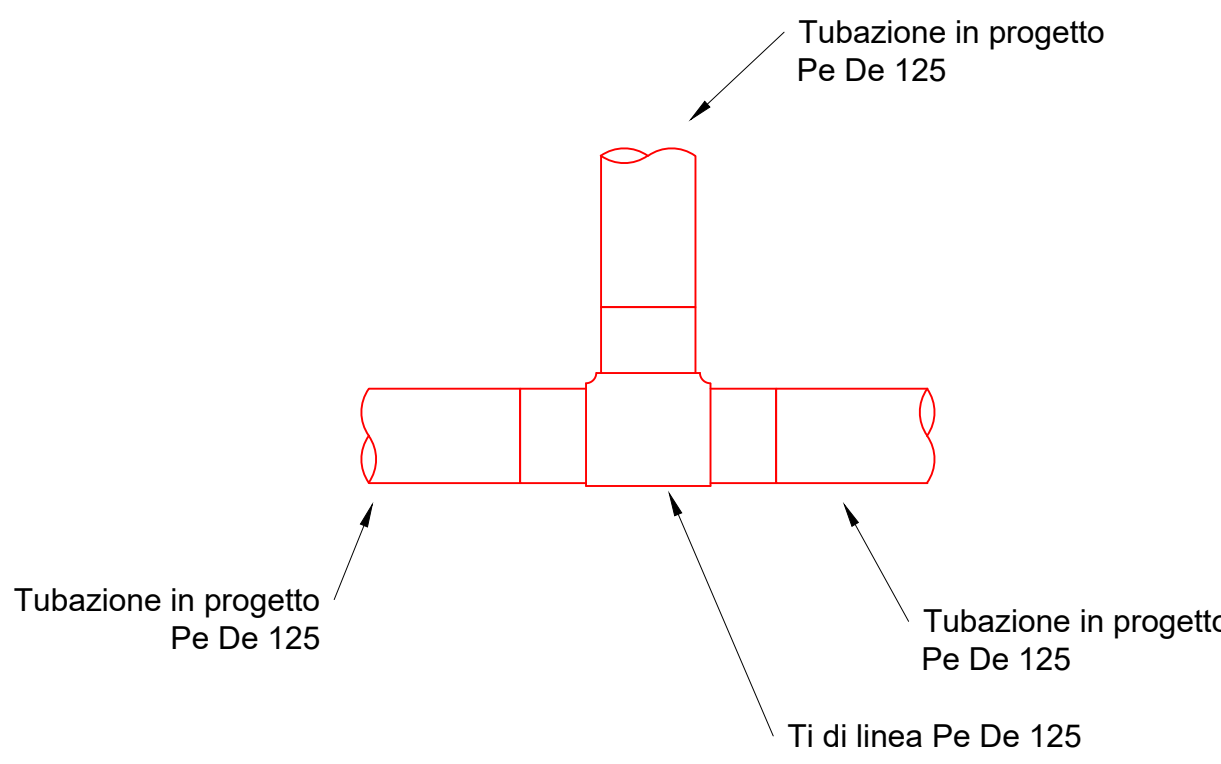

Tipologico 16
Collegamento in linea curva 45° Pe De 125
Nodi 69-72

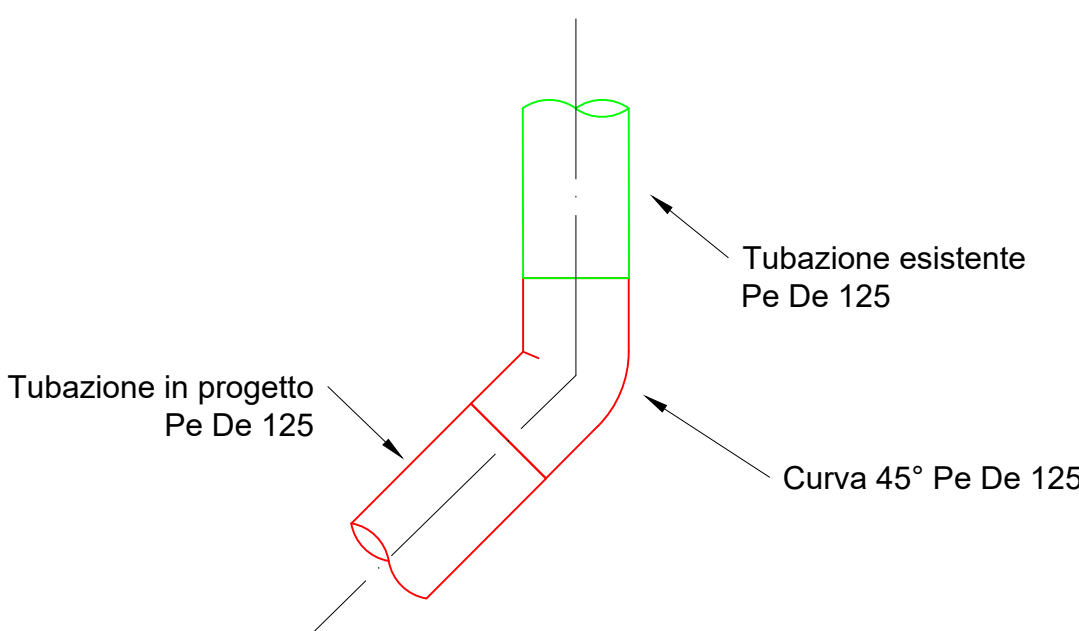

Tipologico 17
Riduzione in linea Pe De 315/225
Nodo 96

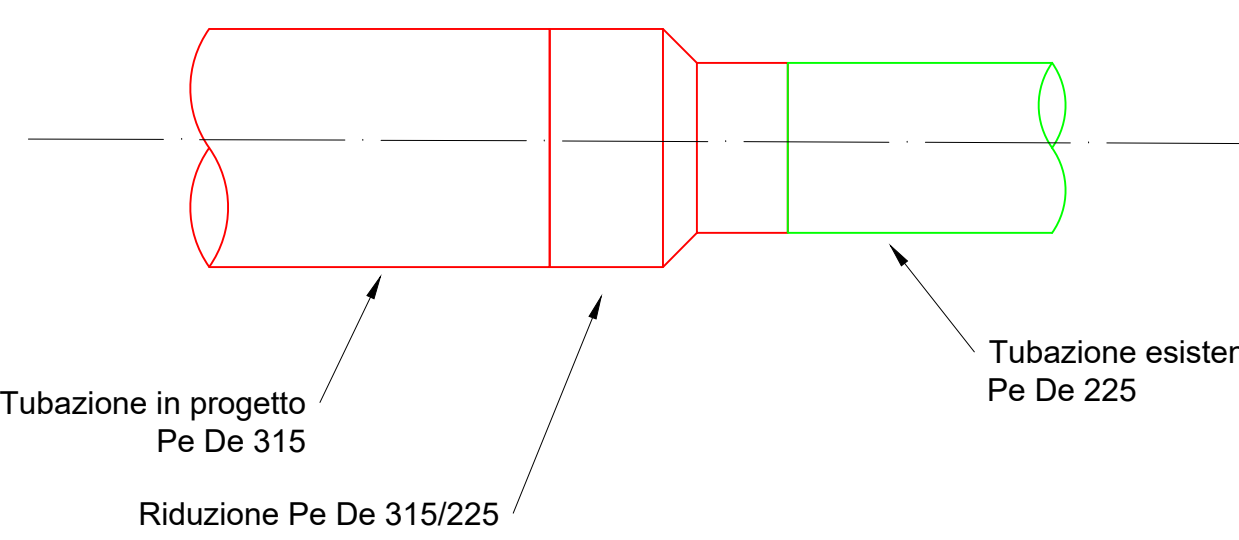

		Progettista:		Unità Responsabile della Progettazione	
Progetto n°: 22-0320-3E-00-001272 WBS: SI.20.10300.02.1109 ALLEGATO n°: 8		Revisione:		INGEREAL-INGE-PROGRE	
Formato: A0 Scale: 1:10		Elaborazione per commenti:		Rev. G. M. A. Redatto Controllato Approvato	
Committente:		Comune di TORINO (TO) Via Vane Progetto Esecutivo SOSTITUZIONE RETE IN BP (L=2504,78 m) GARA ATEM TO1 Intervento n° SI-036213-001272-TSS-TORINO36 Particolari costruttivi			