


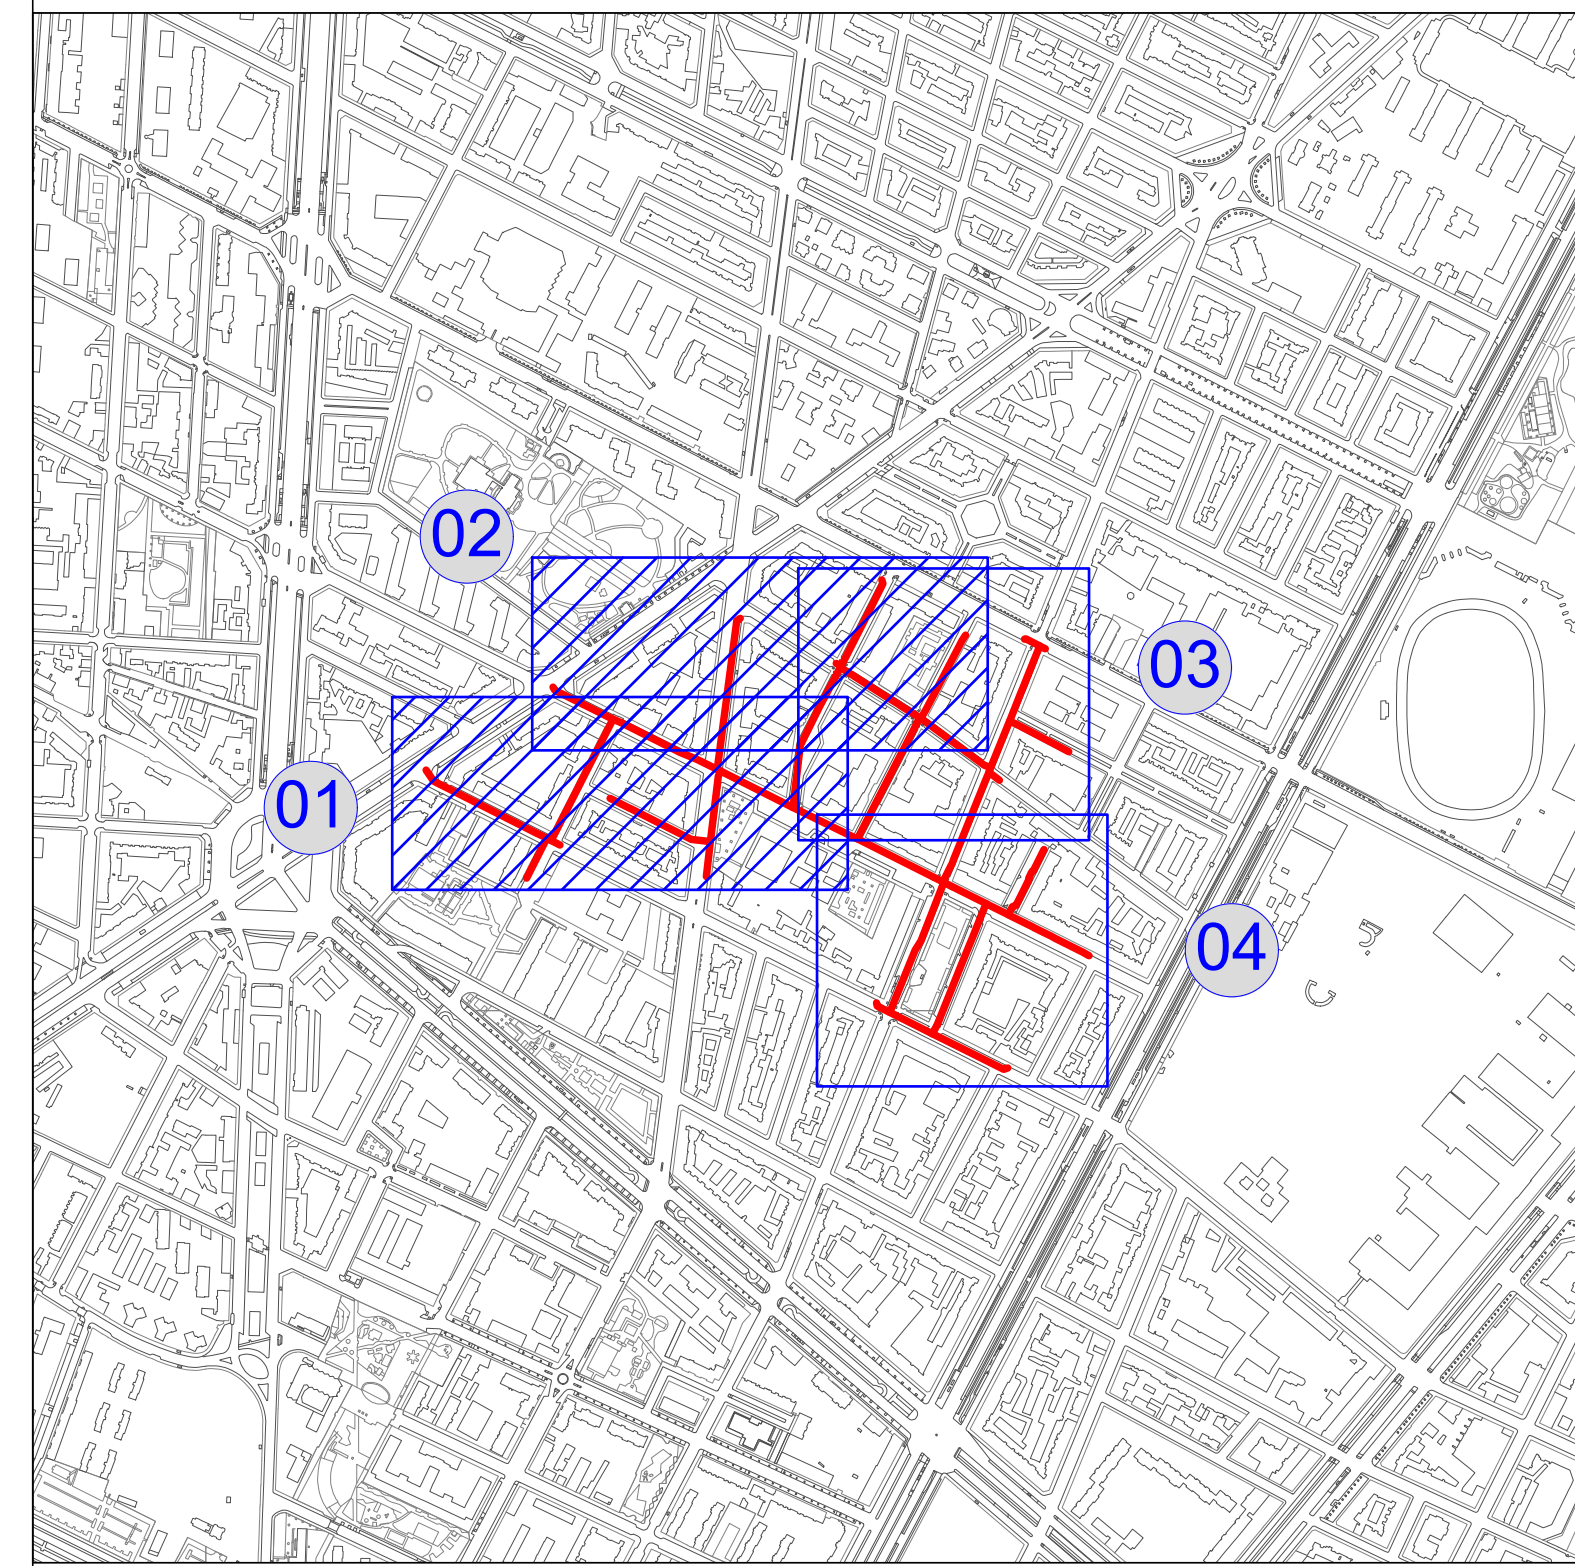


LEGENDA


— Rete in progetto BP	— Cavidotti energia elettrica (MT)	□ Tombino quadrato
— Rete in dismissione BP	— Cavidotti energia elettrica (AT)	⊙ Tombino tondo
— Condotta acquedotto	— Linee aeree energia elettrica	⊙ Caditoia
— Condotta fognatura	— Cavidotti Terna (AT)	⊙ Palo
— Condotti teleriscaldamento	— Cavidotti TelecomWind	⊙ Armadietto tecnico
— Cavidotti Telecom	— Illuminazione pubblica	
— Cavidotti Fastweb	— Canale intubato	
— Cavidotti energia elettrica (BT)	— Aggiornamento rilievo	
	— Sottoservizi rilevati non identificati	
	— Condotta SNAAM Rete Gas	

N	Tipo sottoservizio	Modalità di risoluzione	Quantità interferenze
1	Fognatura	sovrappasso	36
2	Acquedotto	sottopasso	18
4	Teleriscaldamento	sottopasso	67
5	Illuminazione pub.	sottopasso	61
6	Energia elettrica	sottopasso	65
7	Telecom	sottopasso	31
8	Fastweb	sottopasso	14
9	Wind	sottopasso	3
11	Terna (AT)	sovrappasso	0
TOTALE			295

Riquadro 1

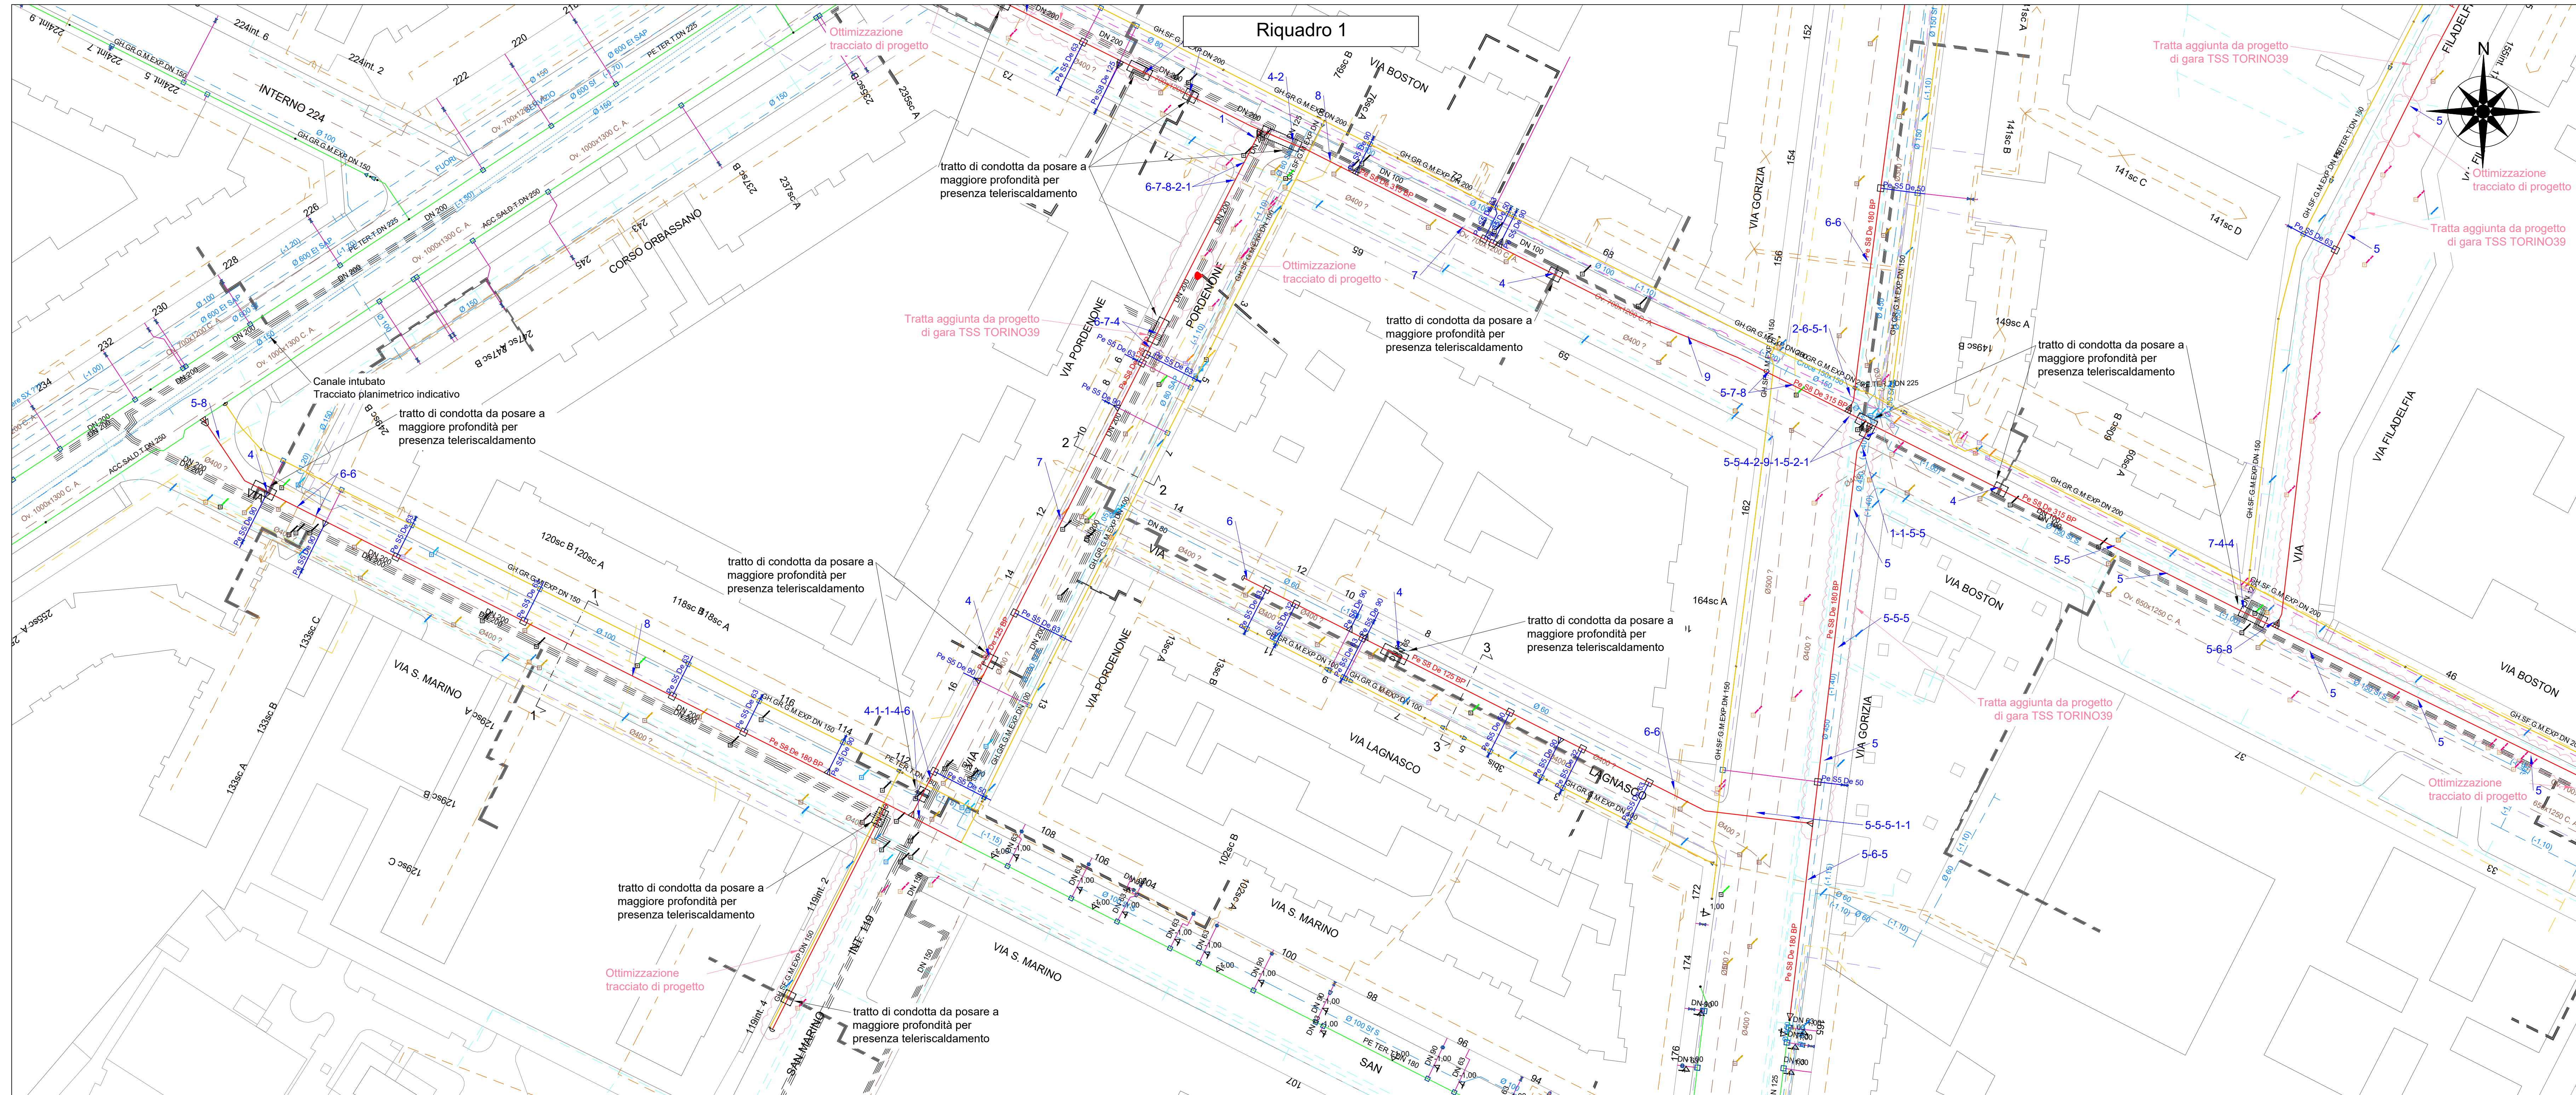

Riquadro 2

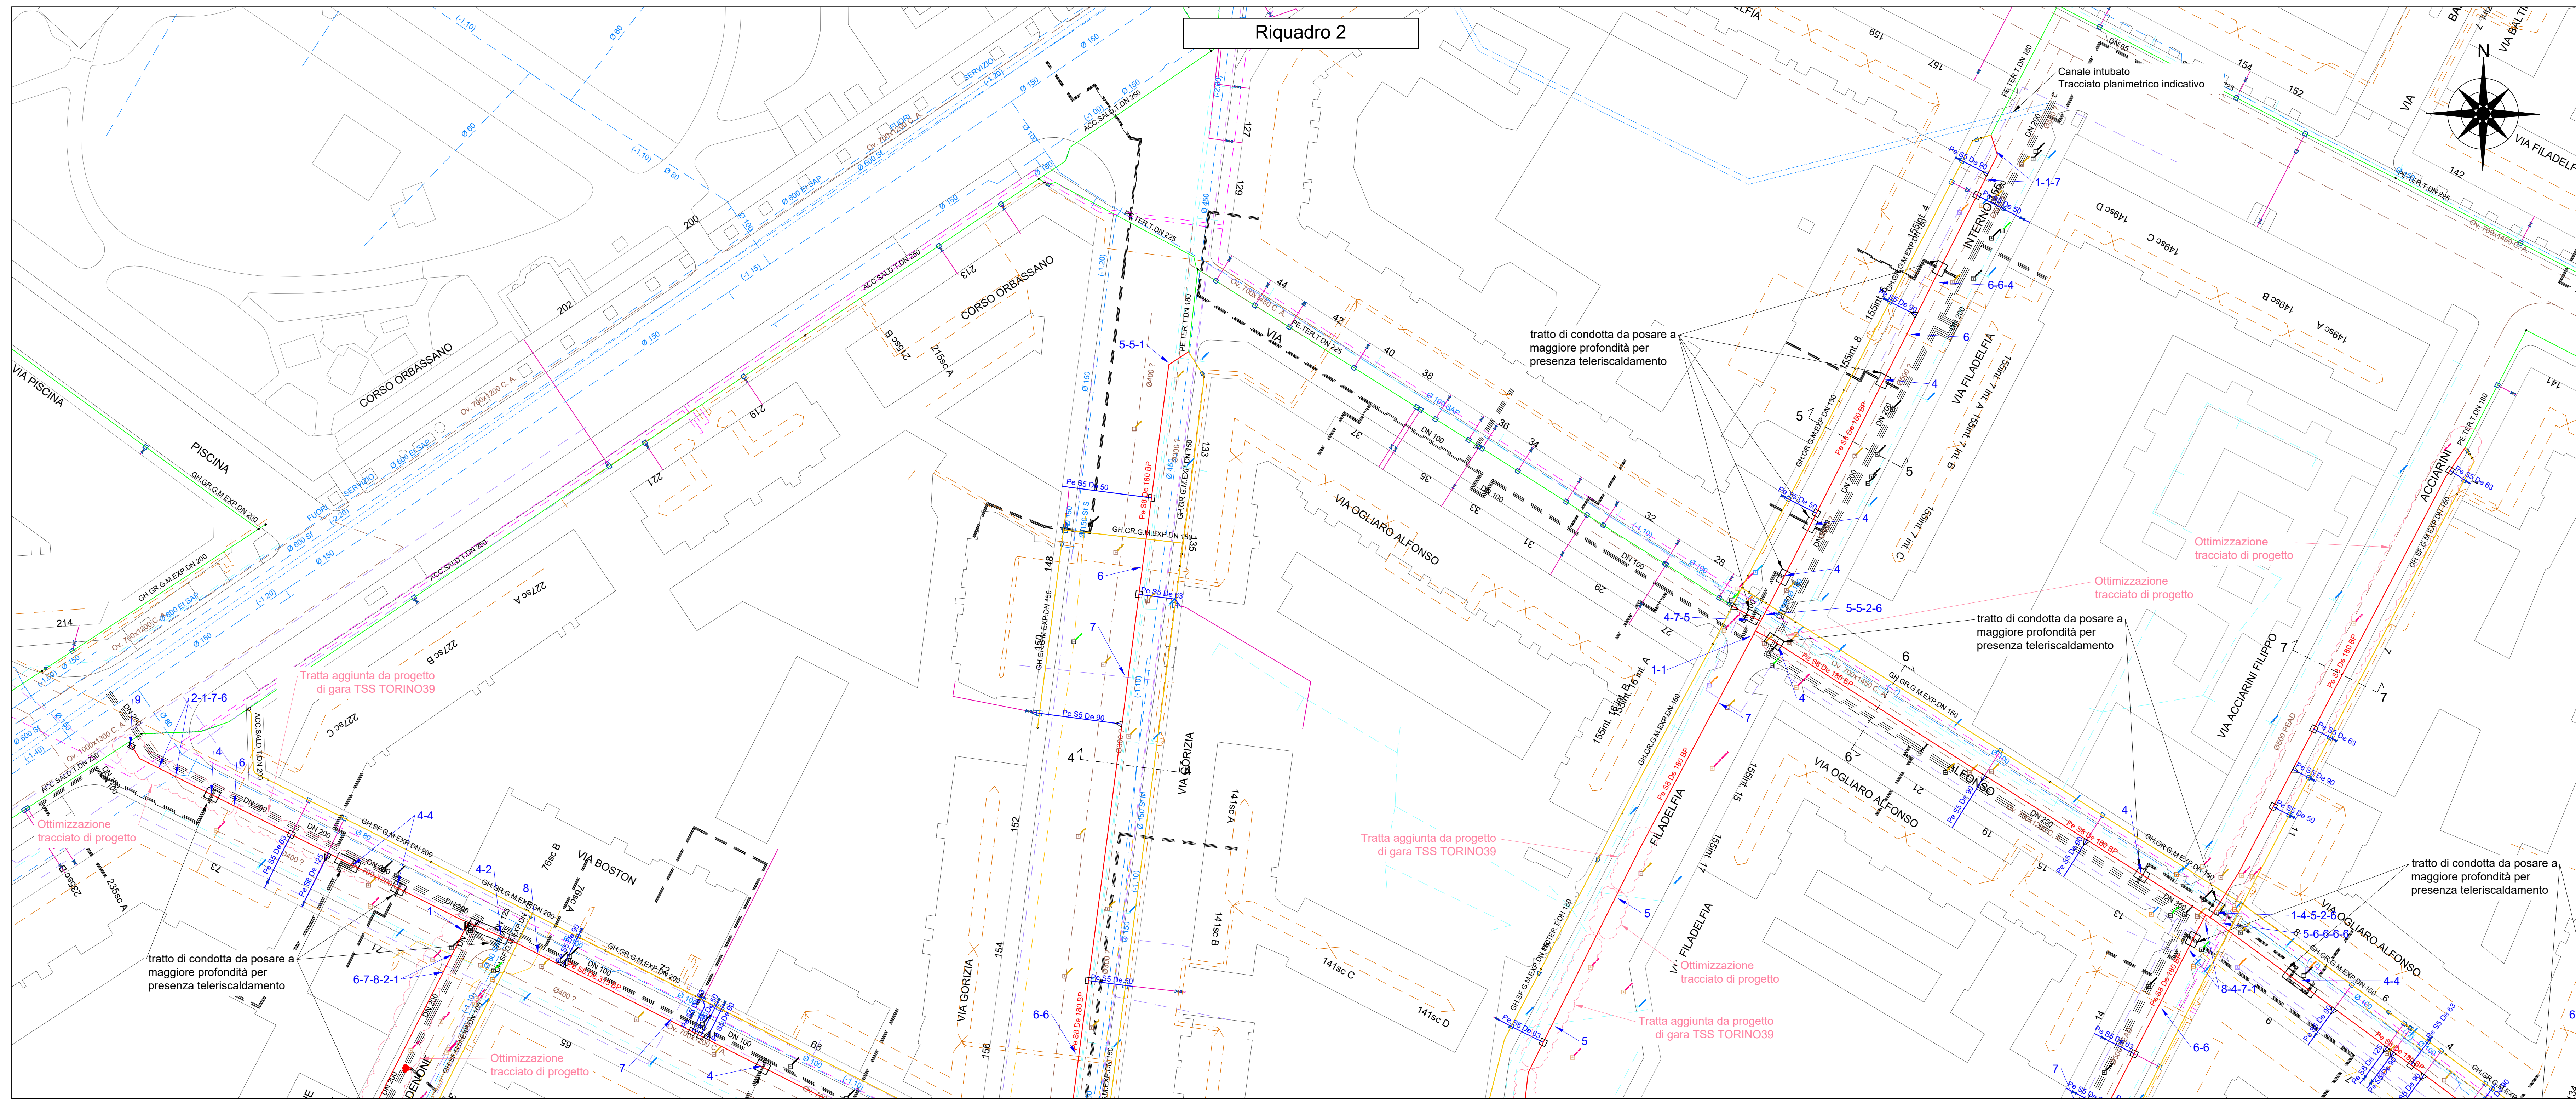


Progetto n°:
22-0320-3E-00-001272
WBS:
SI.20.10300.02.1109
ALLEGATO n°: 9.1
Formato: A0
Scale: 1:500
Com: 2484

Progettista:
Ordine n°:
Ing. G. M. A.
Ing. G. M. A.
Ing. G. M. A.

Unità Responsabile della Progettazione
INGENER-INGE-PROGRE
Comune di TORINO (TO)
Via Vane
Progetto Esecutivo
SOSTITUZIONE RETE IN BP (L=2604,78 m) GARA ATEM TO1
Intervento n° SI-036213-001272-TSS-TORINO36
Planimetria con sottoservizi e risoluzione delle interferenze - Tavola 1



Riquadro 3

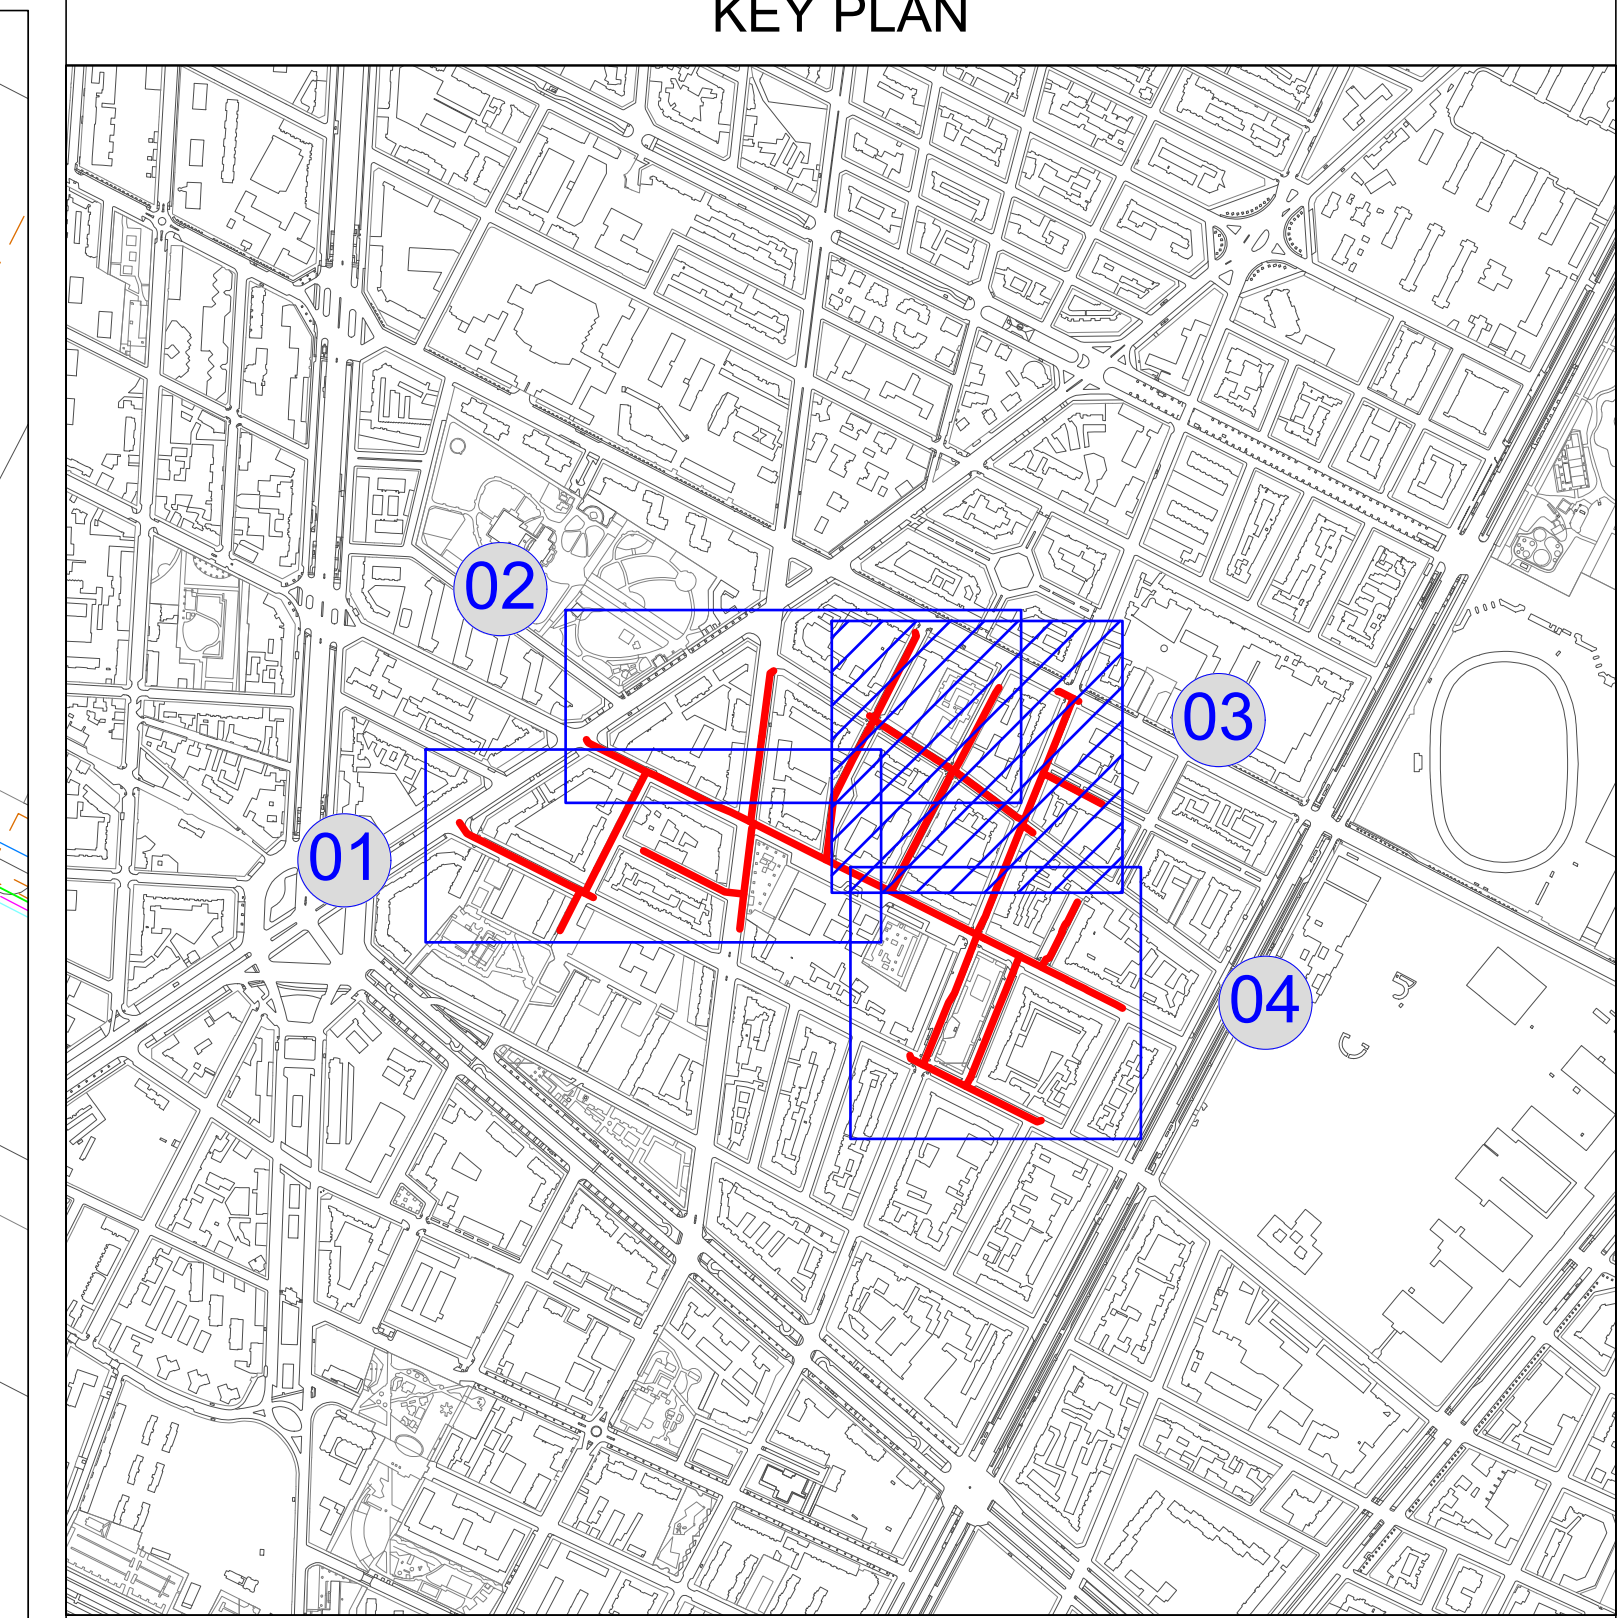

	Rete in progetto BP		Cavidotti energia elettrica (MT)		Tombino quadrato
	Rete in dismissione BP		Cavidotti energia elettrica (AT)		Tombino tondo
	Condotte acquedotto		Linee aeree energia elettrica		Caditoia
	Condotte fognatura		Cavidotti Terna (AT)		Palo
	Condotte teleriscaldamento		Cavidotti Telecom/Wind		Armadietto tecnico
	Cavidotti Telecom		Illuminazione pubblica		
	Cavidotti Fastweb		Canale intubato		
	Cavidotti energia elettrica (BT)		Aggiornamento rilievo		
			Sottoservizi rilevati non identificati		
			Condotta SNAM Rete Gas		

	Progettista:  Ordine degli Ingegneri di Alessandria matricola n° 404		Unità Responsabile della Progettazione						
			INGEGRALE-INGE-PROGRE						
Progetto n°: 22-0320-3E-00-001272 WBS: SI.20.I0300.02.1109 ALLEGATO n°: 9.2									
Norme File: 441-0-000									
Descrizione:									
Emissione per commenti			0	04	11	22	R. Mancinelli	L. Cartasegna	A. Leardi
Formato: A1	Scala 1 : 500		Rev.	G.	M.	A.	Redatto	Controllato	Approvato
Committente			Comune di TORINO (TO) Vie Varie Progetto Esecutivo SOSTITUZIONE RETE IN BP (L=2504,78 m) GARA ATEM TO1 Intervento n° SI-036213-001272-TSS-TORIN036 Planimetria con sottoservizi e risoluzione delle interferenze - Tavola 2						
									

Il presente elaborato è di proprietà aziendale - La società tutelerà i propri diritti a termini di legge.

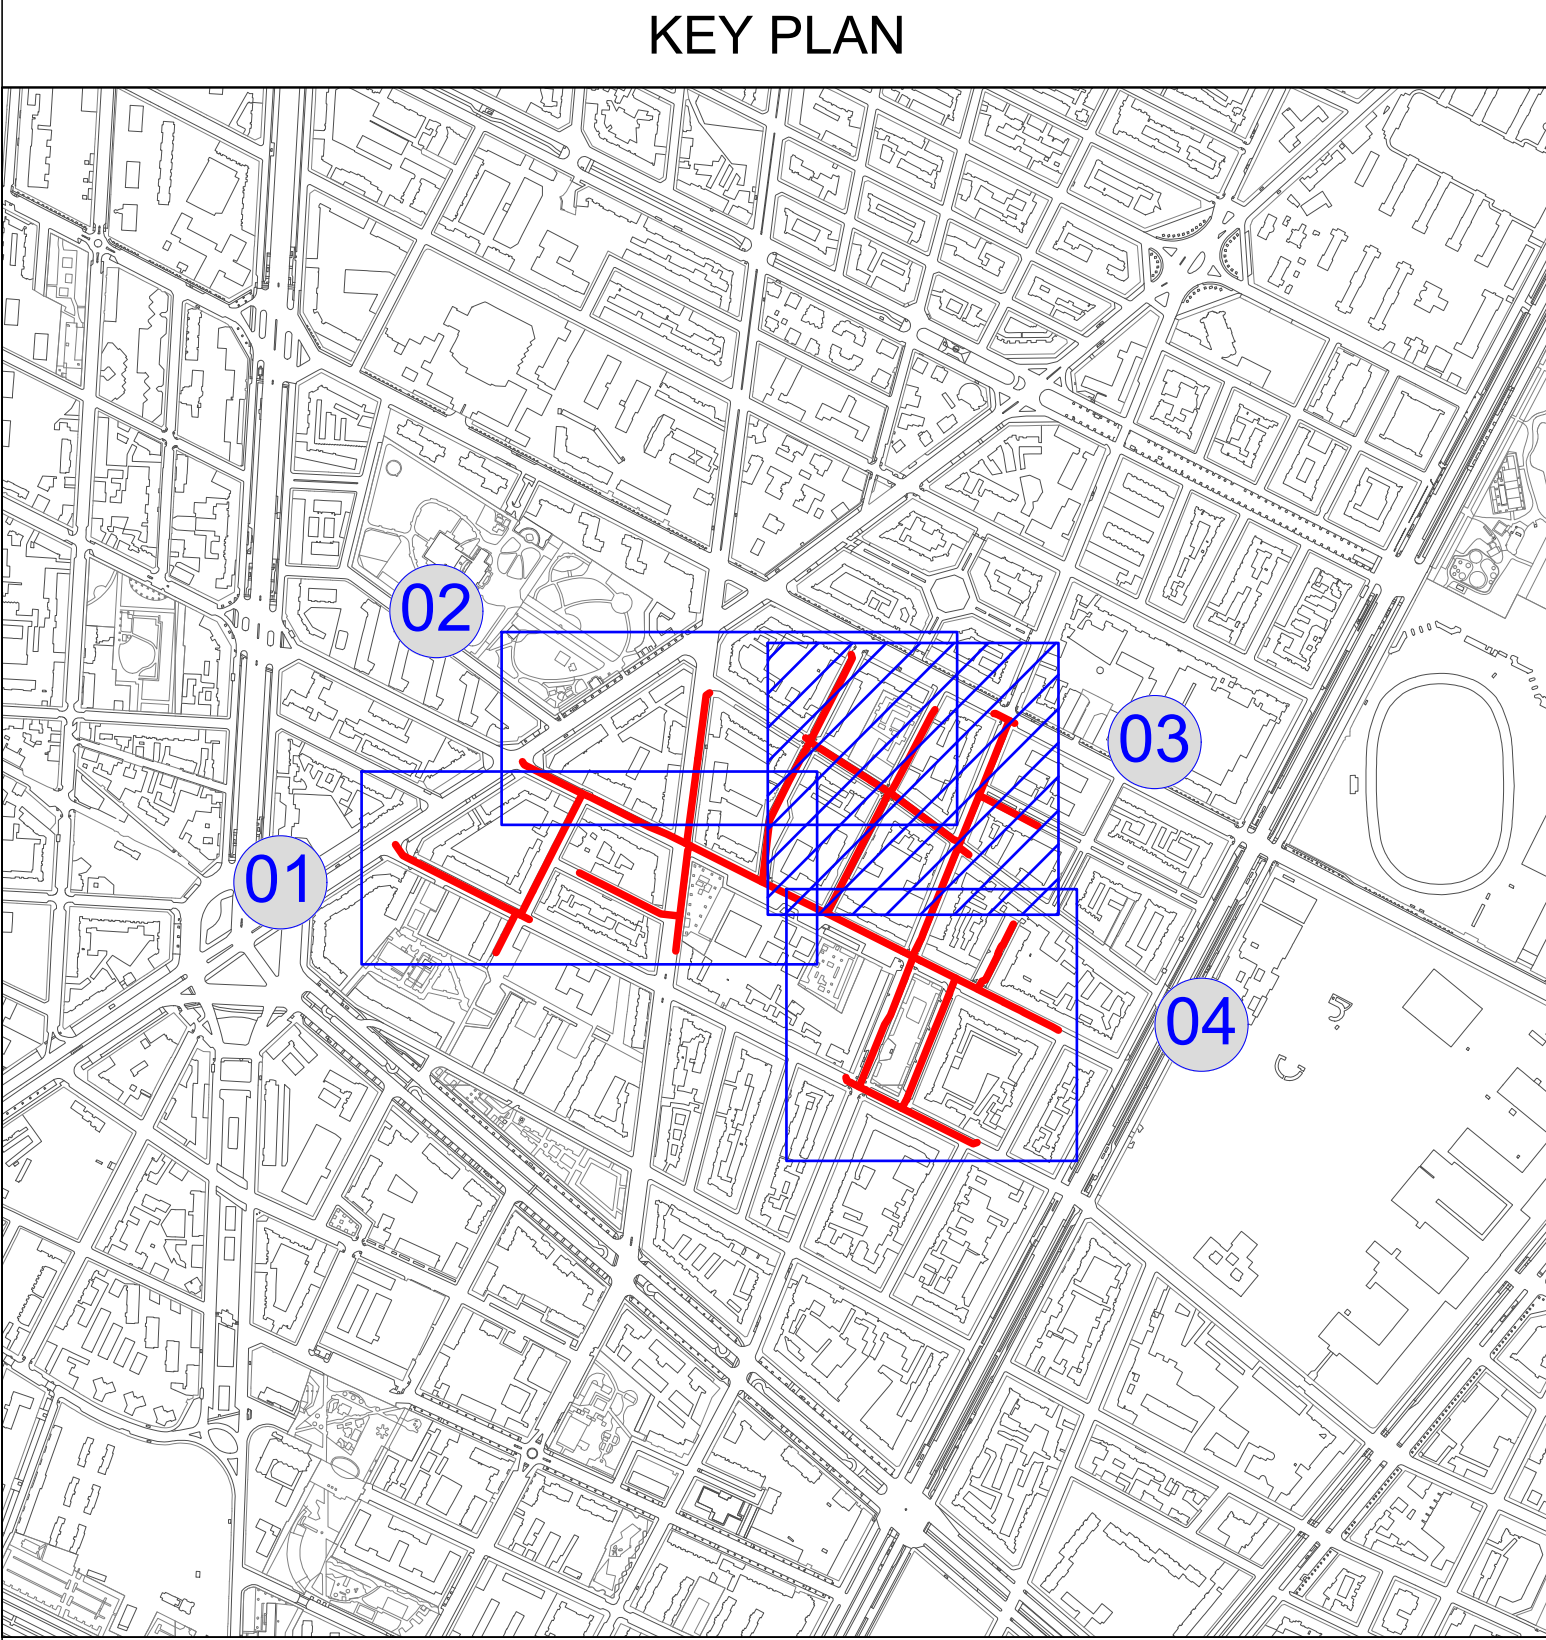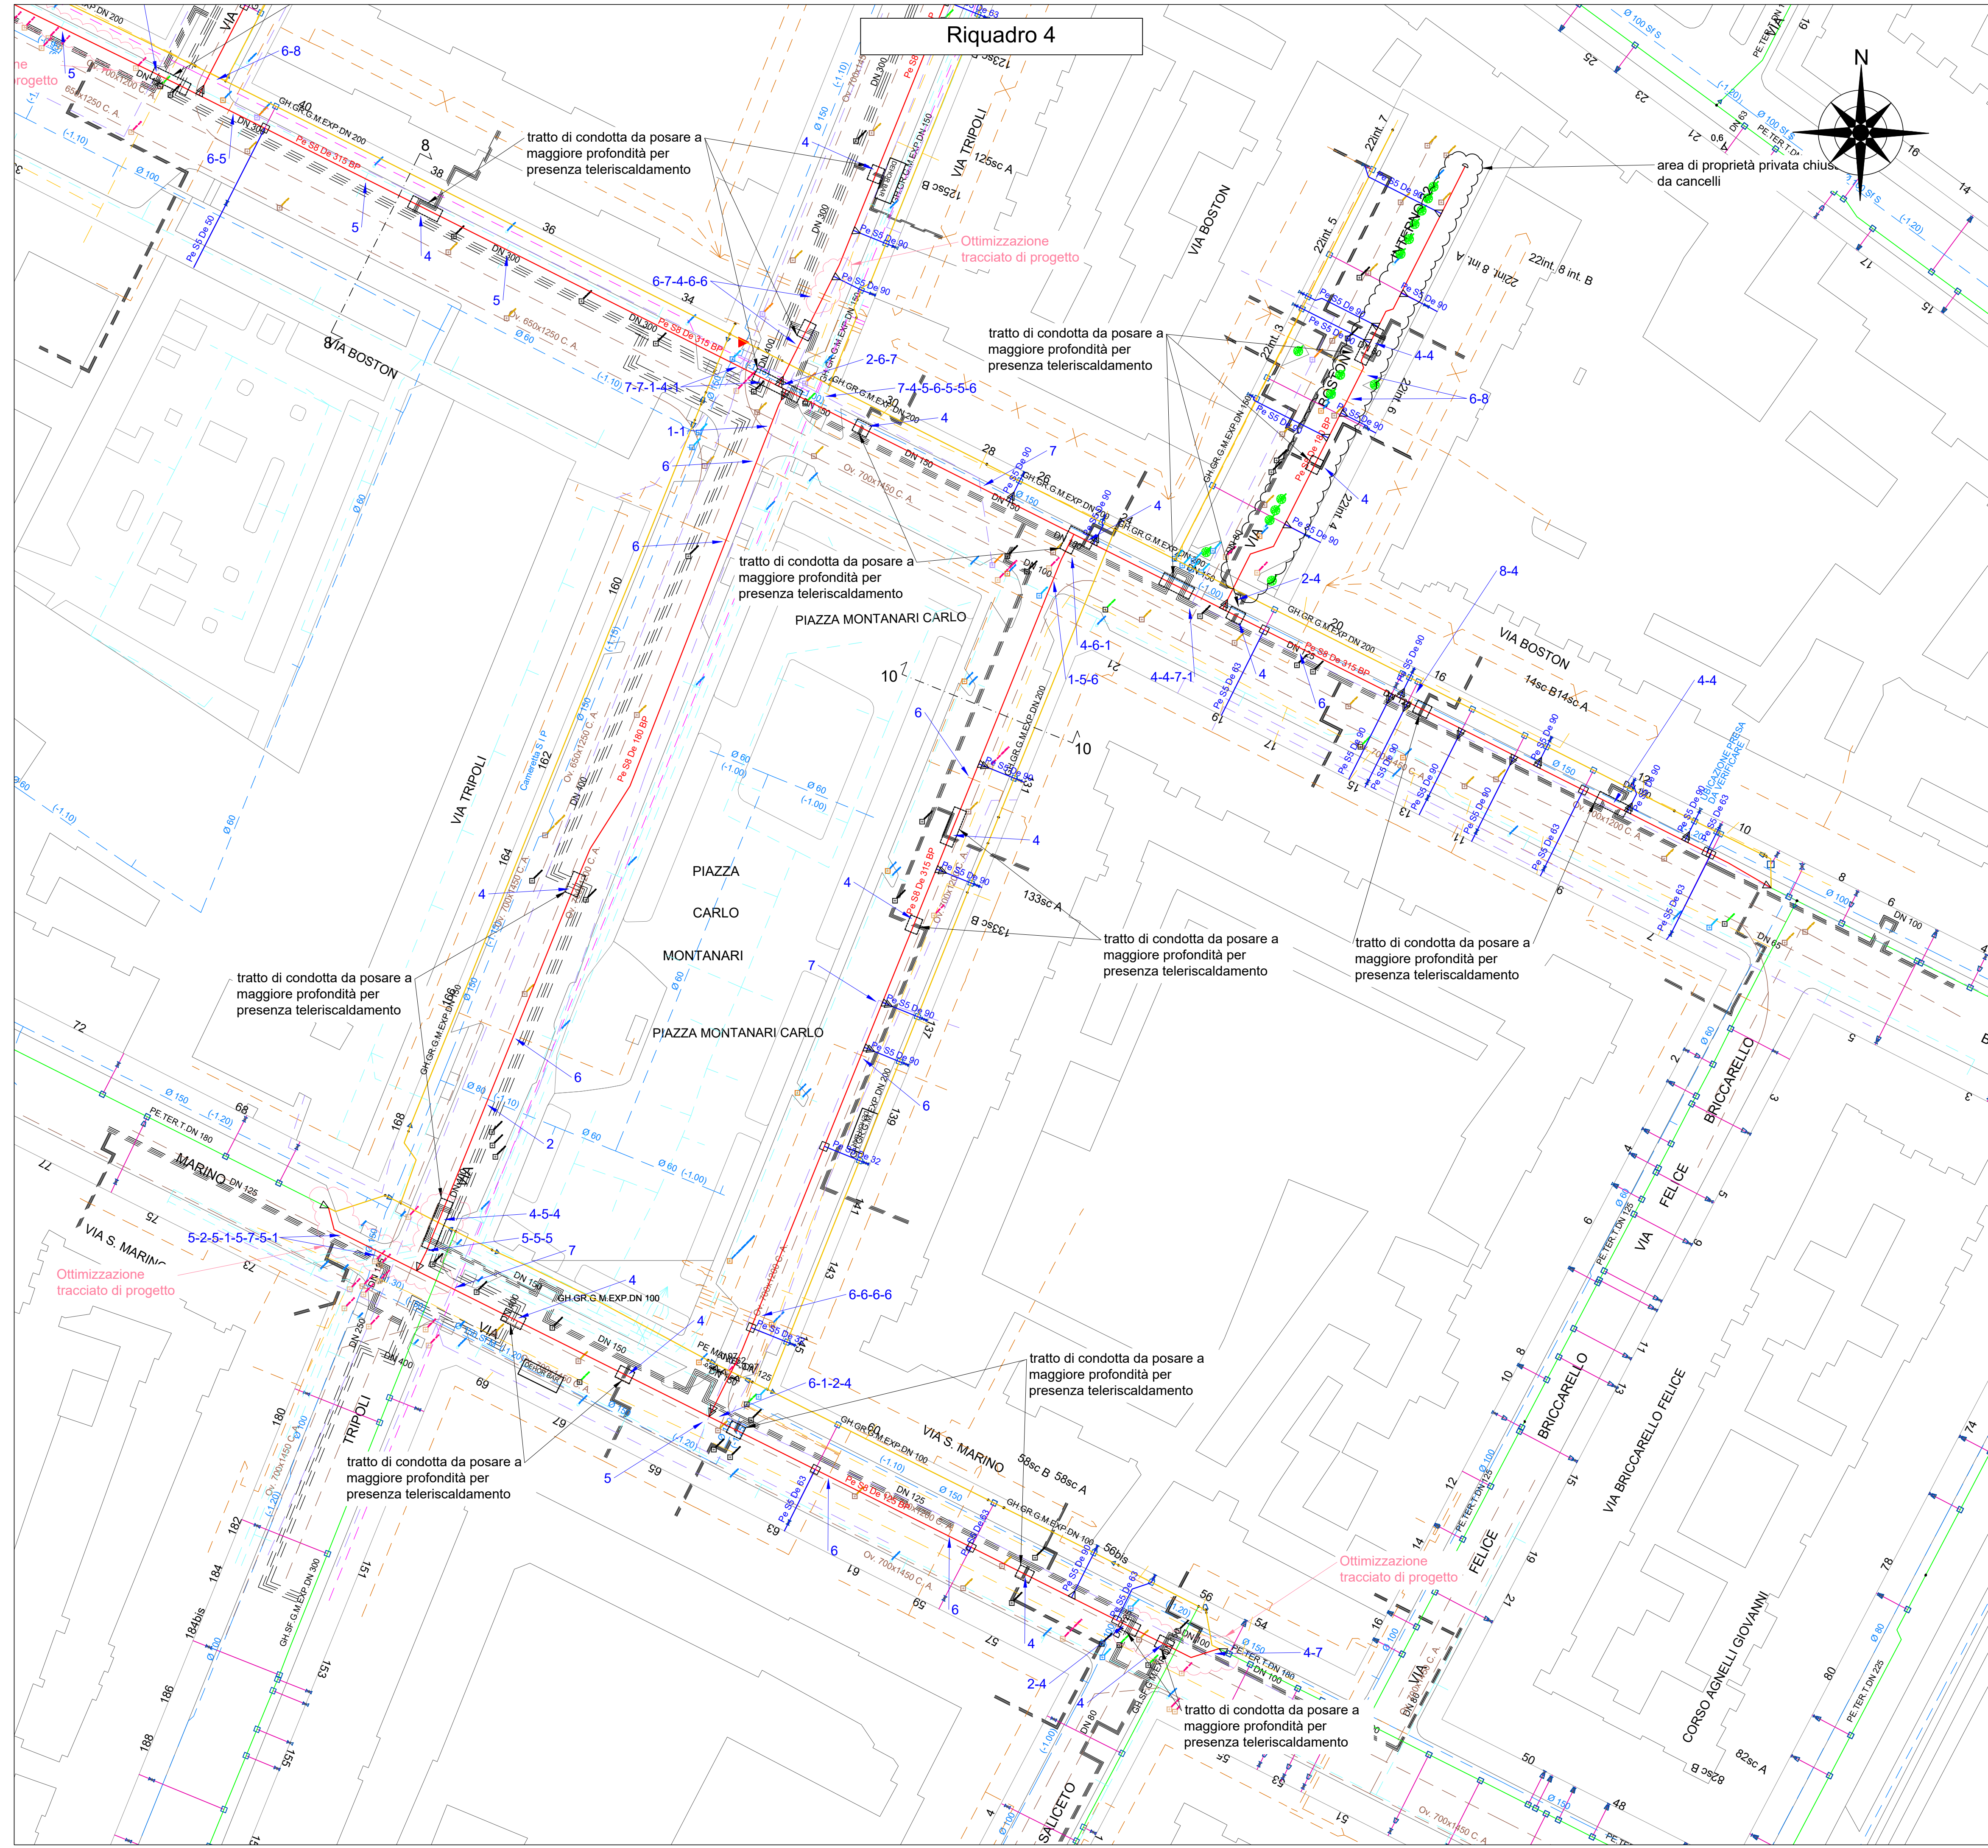

LEGENDA			
	Rete in progetto BP		Cavidotti energia elettrica (MT)
	Rete in dismissione BP		Cavidotti energia elettrica (AT)
	Condotte acquedotto		Linee aeree energia elettrica
	Condotte fognatura		Cavidotti Terna (AT)
	Condotte teleriscaldamento		Cavidotti Telecom/Wind
	Cavidotti Telecom		Illuminazione pubblica
	Cavidotti Fastweb		Canale intubato
	Cavidotti energia elettrica (BT)		Aggiornamento rilievo
	Sottoservizi rilevati non identificati		Sottoservizi rilevati non identificati
	Condotta SNAM Rete Gas		Condotta SNAM Rete Gas
	Tombino quadrato		Tombino tondo
	Caditoia		Paio
	Armadietto tecnico		

N.	Tipo sottoservizio	Modalità di risoluzione	Quantità interferenze
1	Fognatura	sovrappasso	36
2	Acquedotto	sottopasso	18
4	Teleriscaldamento	sottopasso	67
5	Illuminazione pub.	sottopasso	61
6	Energia elettrica	sottopasso	65
7	Telecom	sottopasso	31
8	Fastweb	sottopasso	14
9	Wind	sottopasso	3
11	Terna (AT)	sovrappasso	0
TOTALE			295

Progettista:
Ordine degli Ingegneri di Alessandria
matr. n. 1014
Ing. Alessandro Leardi

Unità Responsabile della Progettazione
INGEREAL-INGE-PROGRE

Progetto n°:
22-0320-3E-00-001272
WBS:
SI.20.10300.02.1109
ALLEGATO n°: 9.3

Descrizione:
SOSTITUZIONE RETE IN BP (L=2504.78 m) GARA ATEM TO1
Intervento n° SI-036213-001272-TSS-TORIN036
Planimetria con sottoservizi e risoluzione delle interferenze - Tavola 3


Descrizione:
Emissione per commenti
Comm.: 2464

0 04 11 22
R. Mancinelli L. Cartasegna A. Leardi
Rev. G. M. A. Redatto Controllato Approvato

Comune di
TORINO (TO)
Vie Varie
Progetto Esecutivo
SOSTITUZIONE RETE IN BP (L=2504.78 m) GARA ATEM TO1
Intervento n° SI-036213-001272-TSS-TORIN036
Planimetria con sottoservizi e risoluzione delle interferenze - Tavola 3


Sezione 1

Via S. Maino

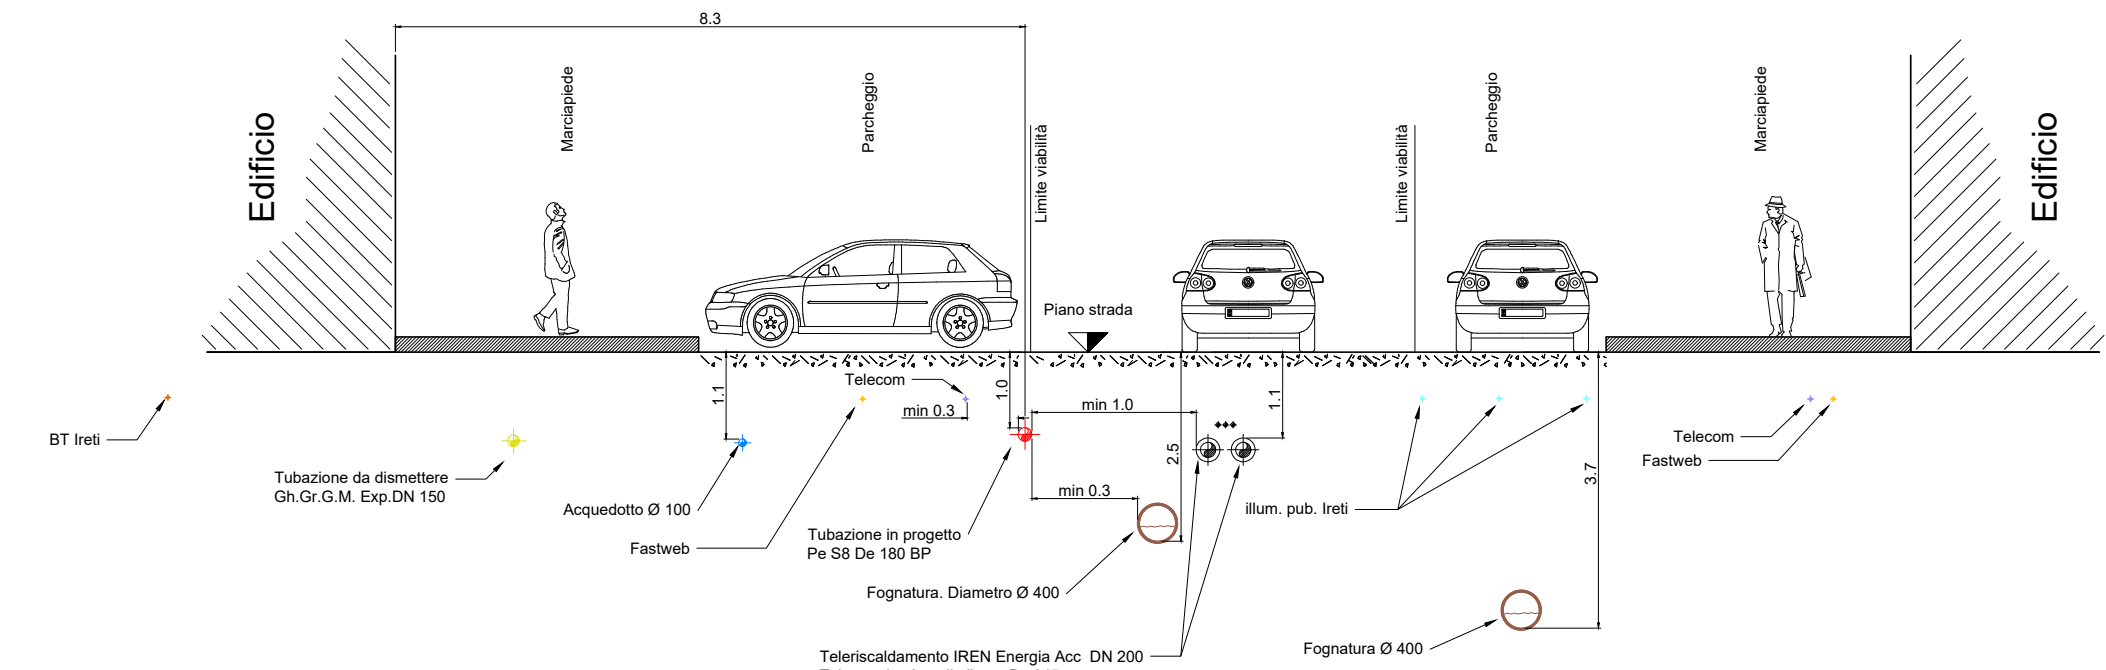


Sezione 2

Via Pordenone

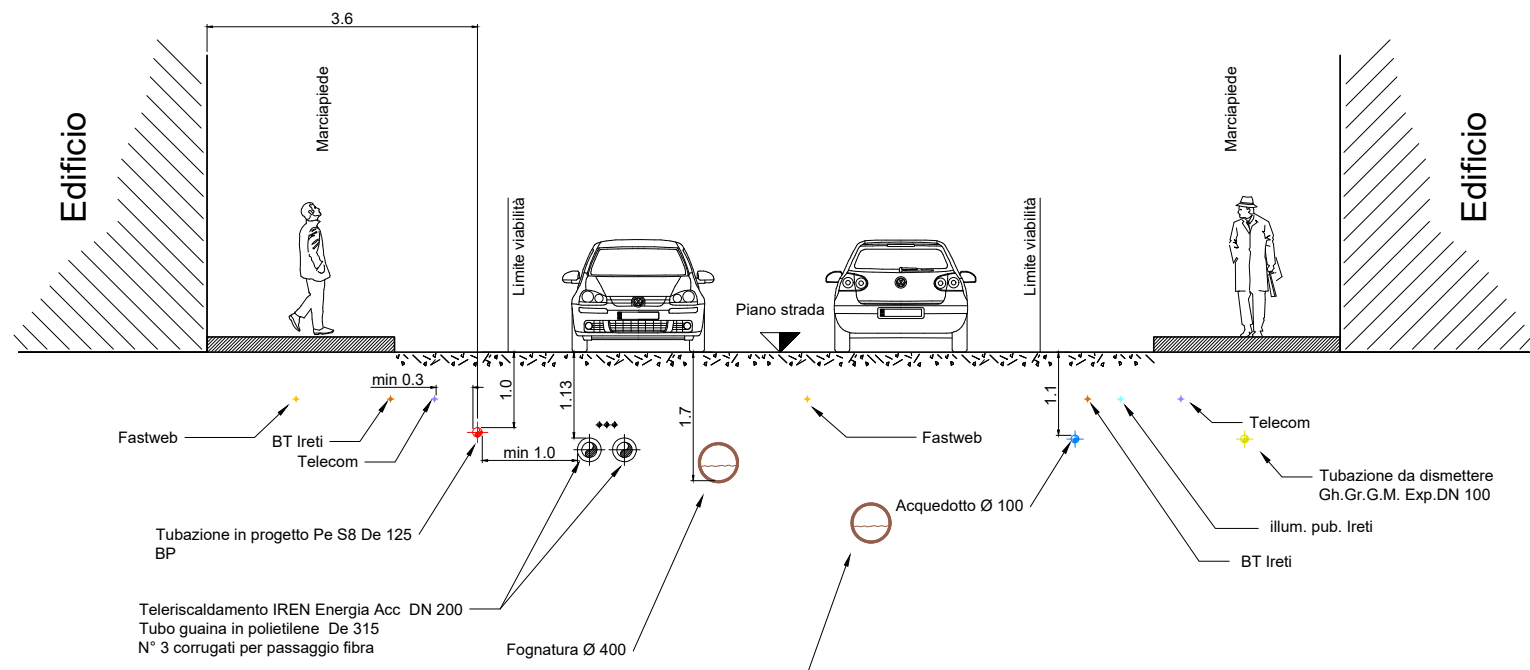


Sezione 3

Via Lagnasco

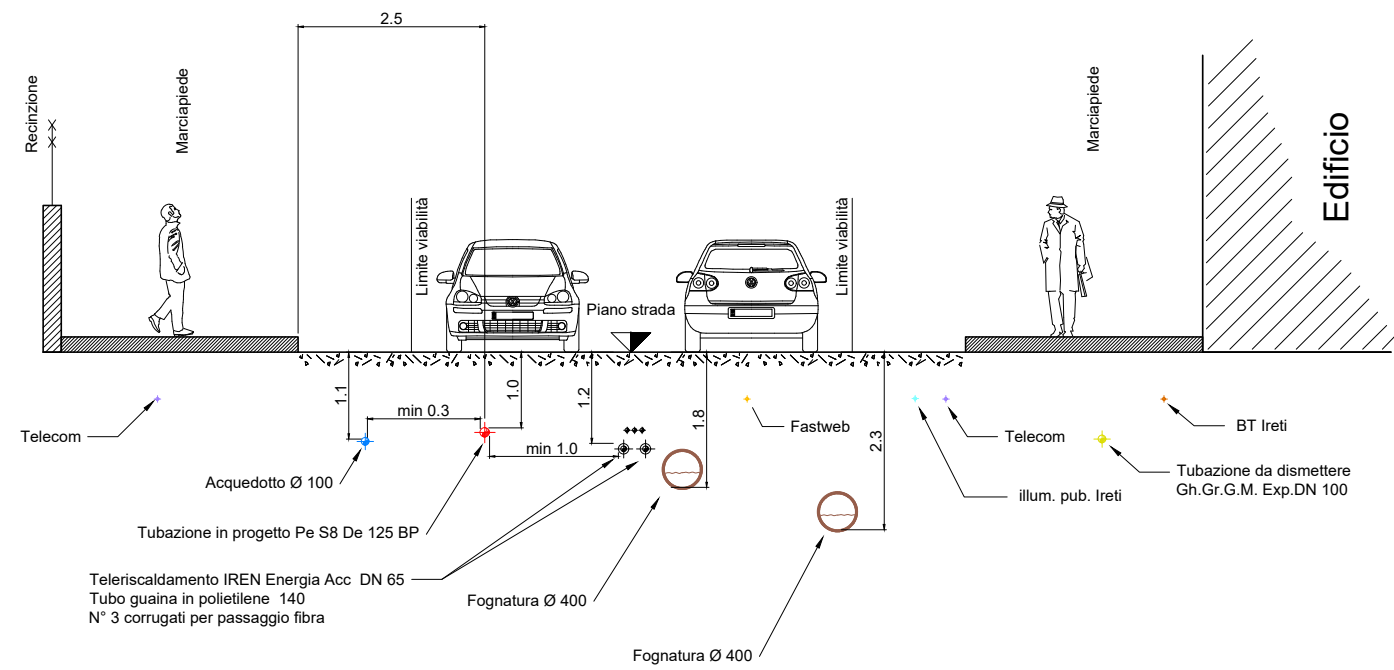


Sezione 4

Via Gonzia

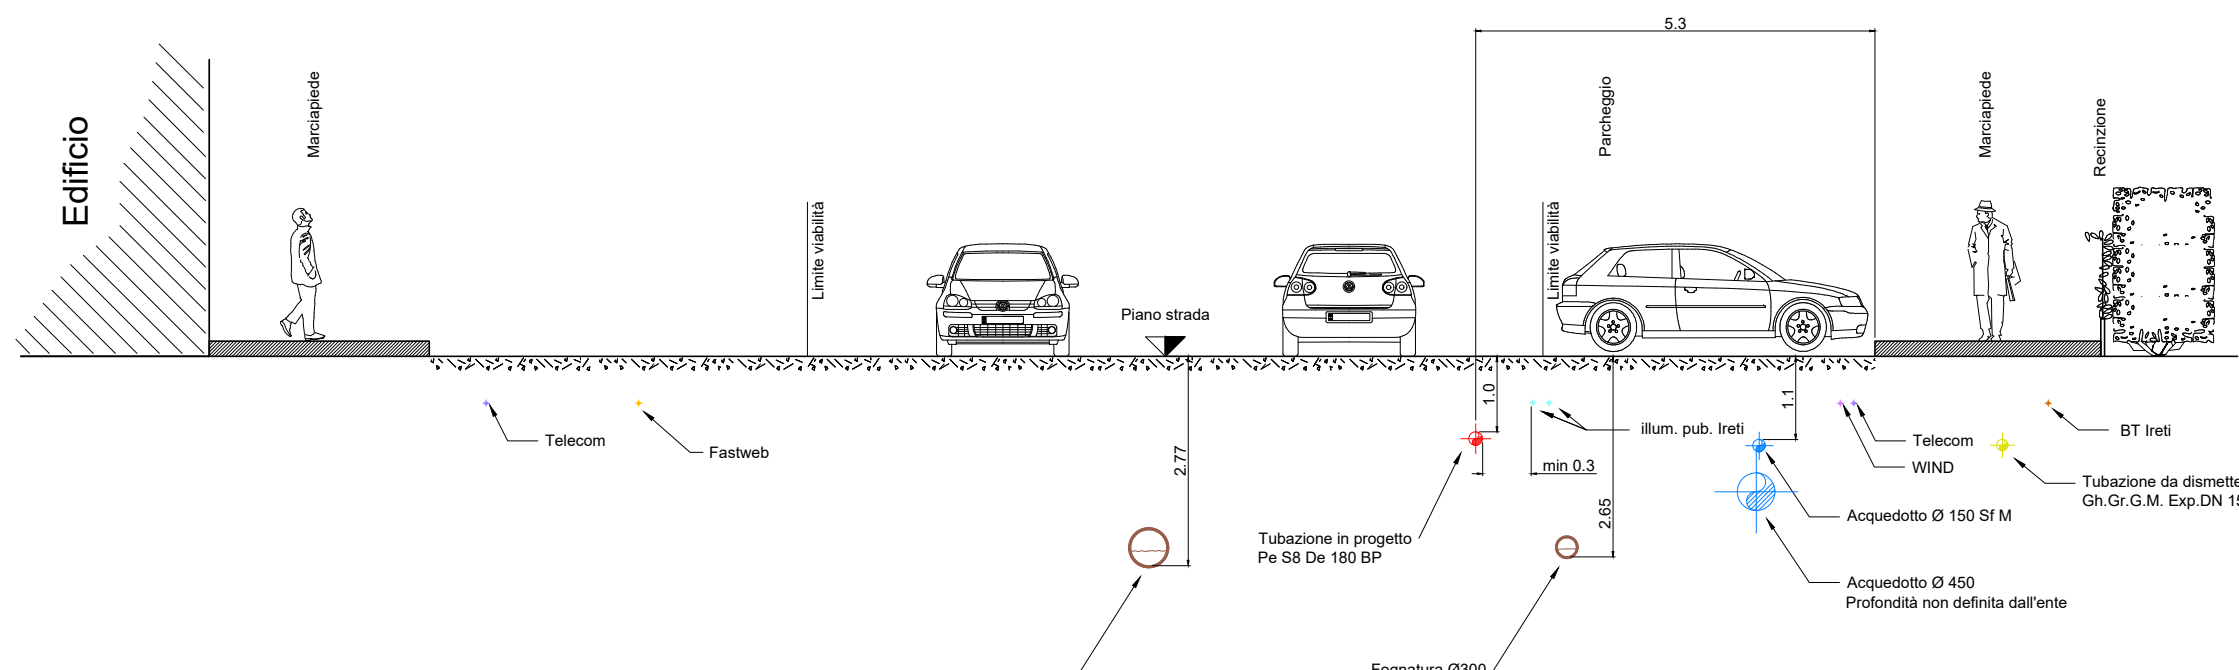


Sezione 5

Via Fiadellia

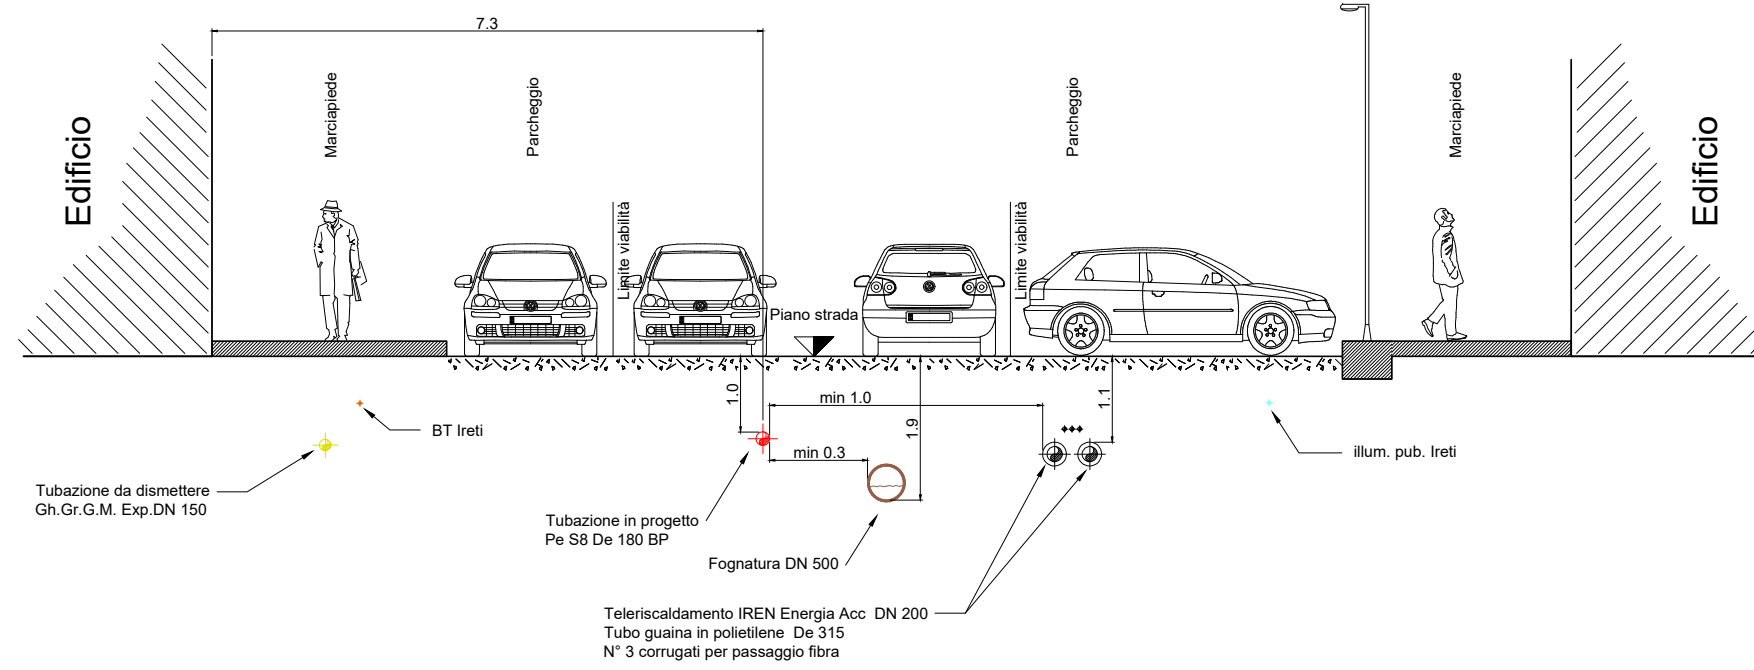


Sezione 6

Via Ogliaro

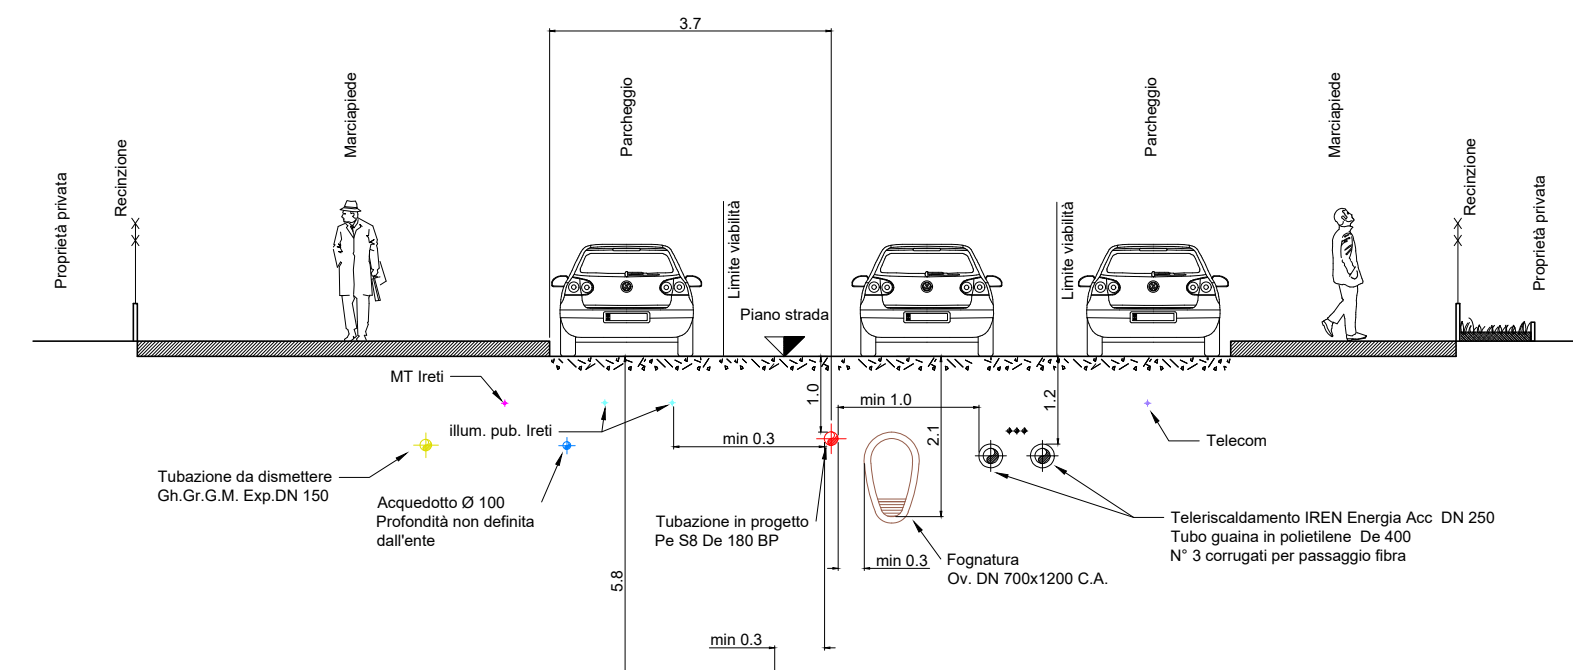


Sezione 7

Via Acciaini

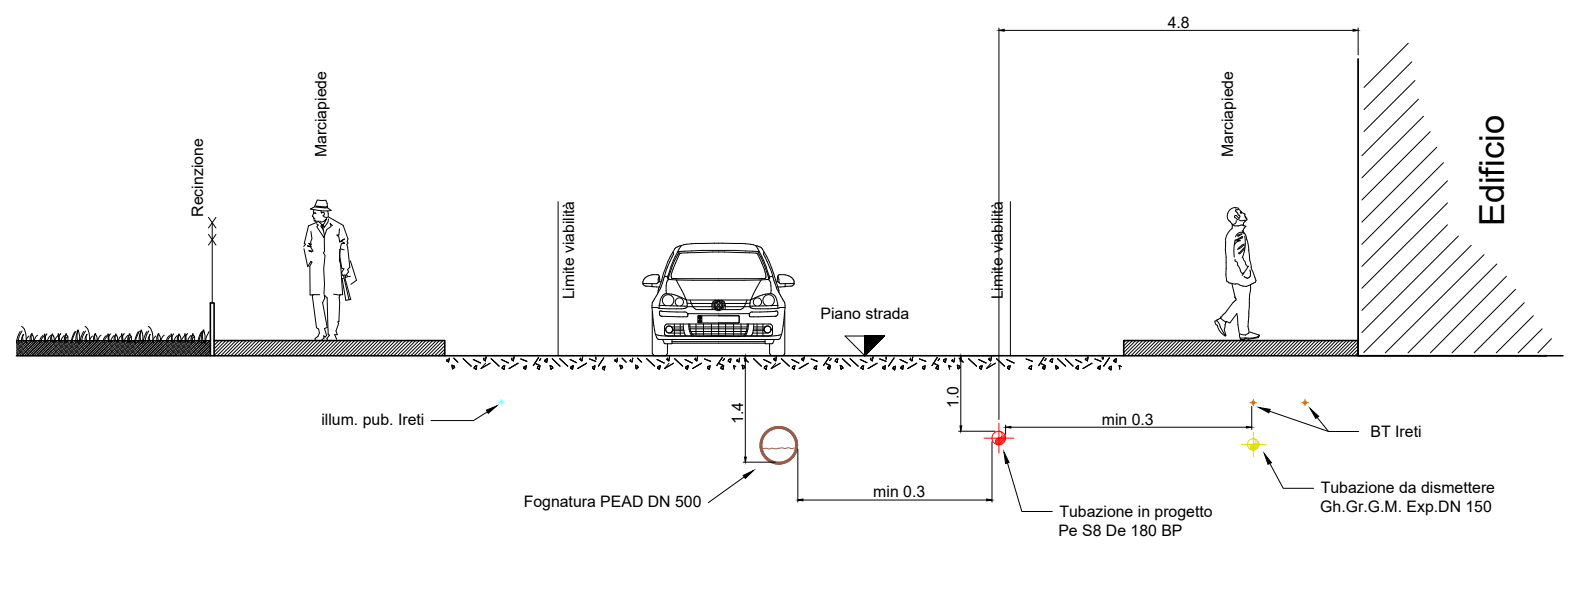


Sezione 8

Via Boston

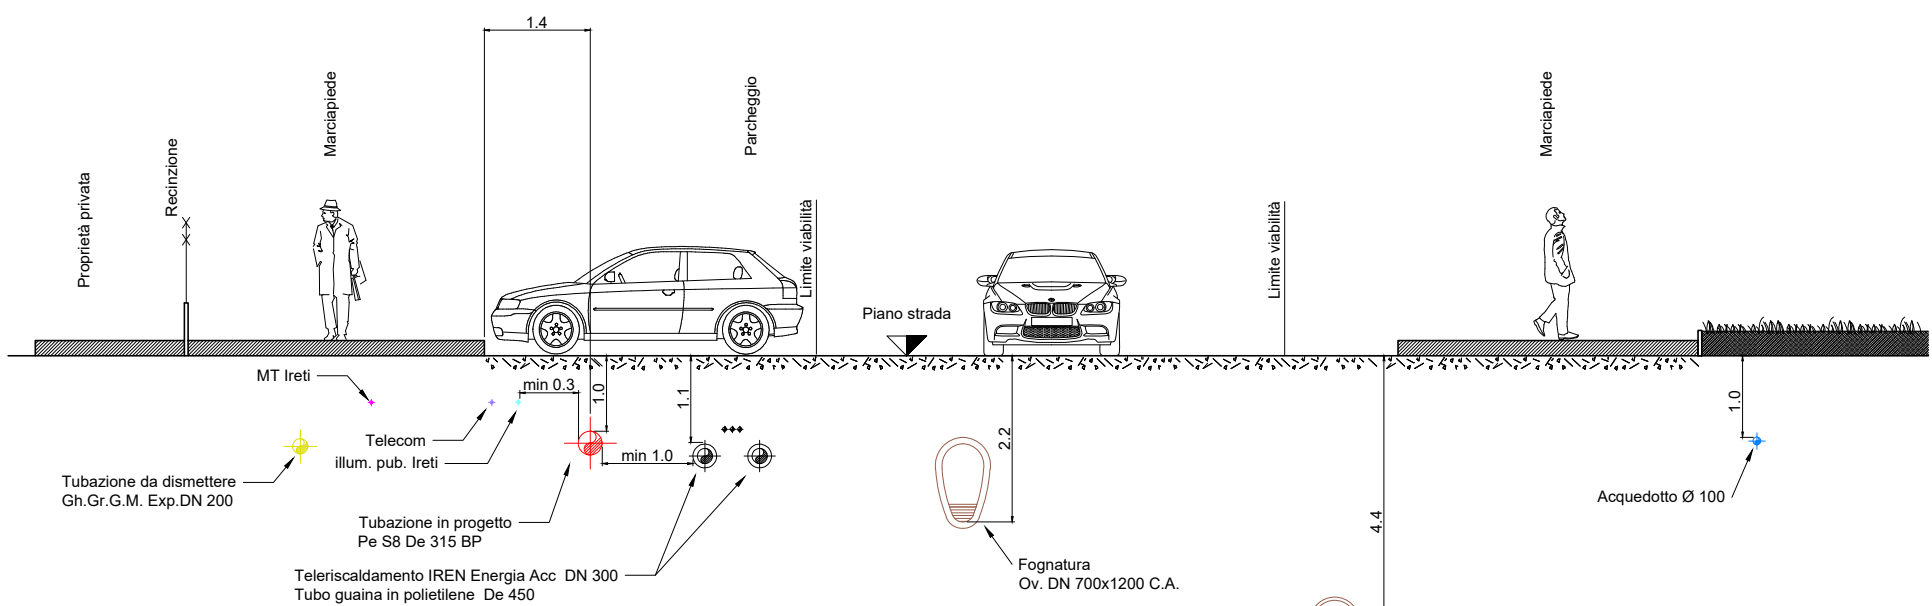


Sezione 9

Via Tripoli

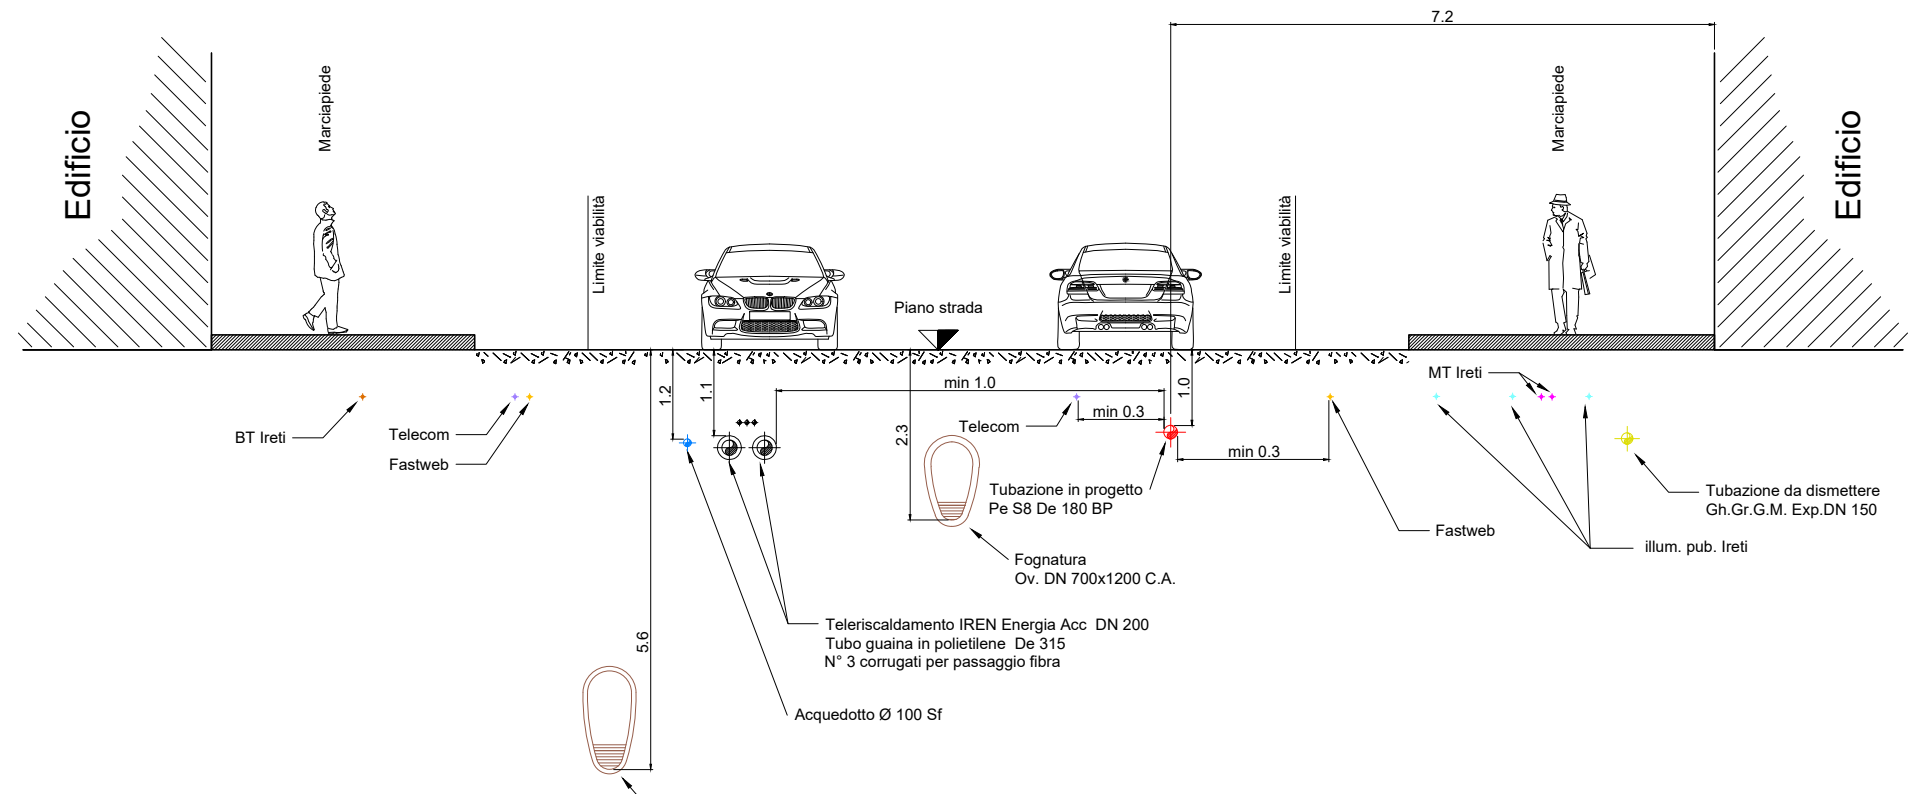

Sezione 10

Pza. Montanari

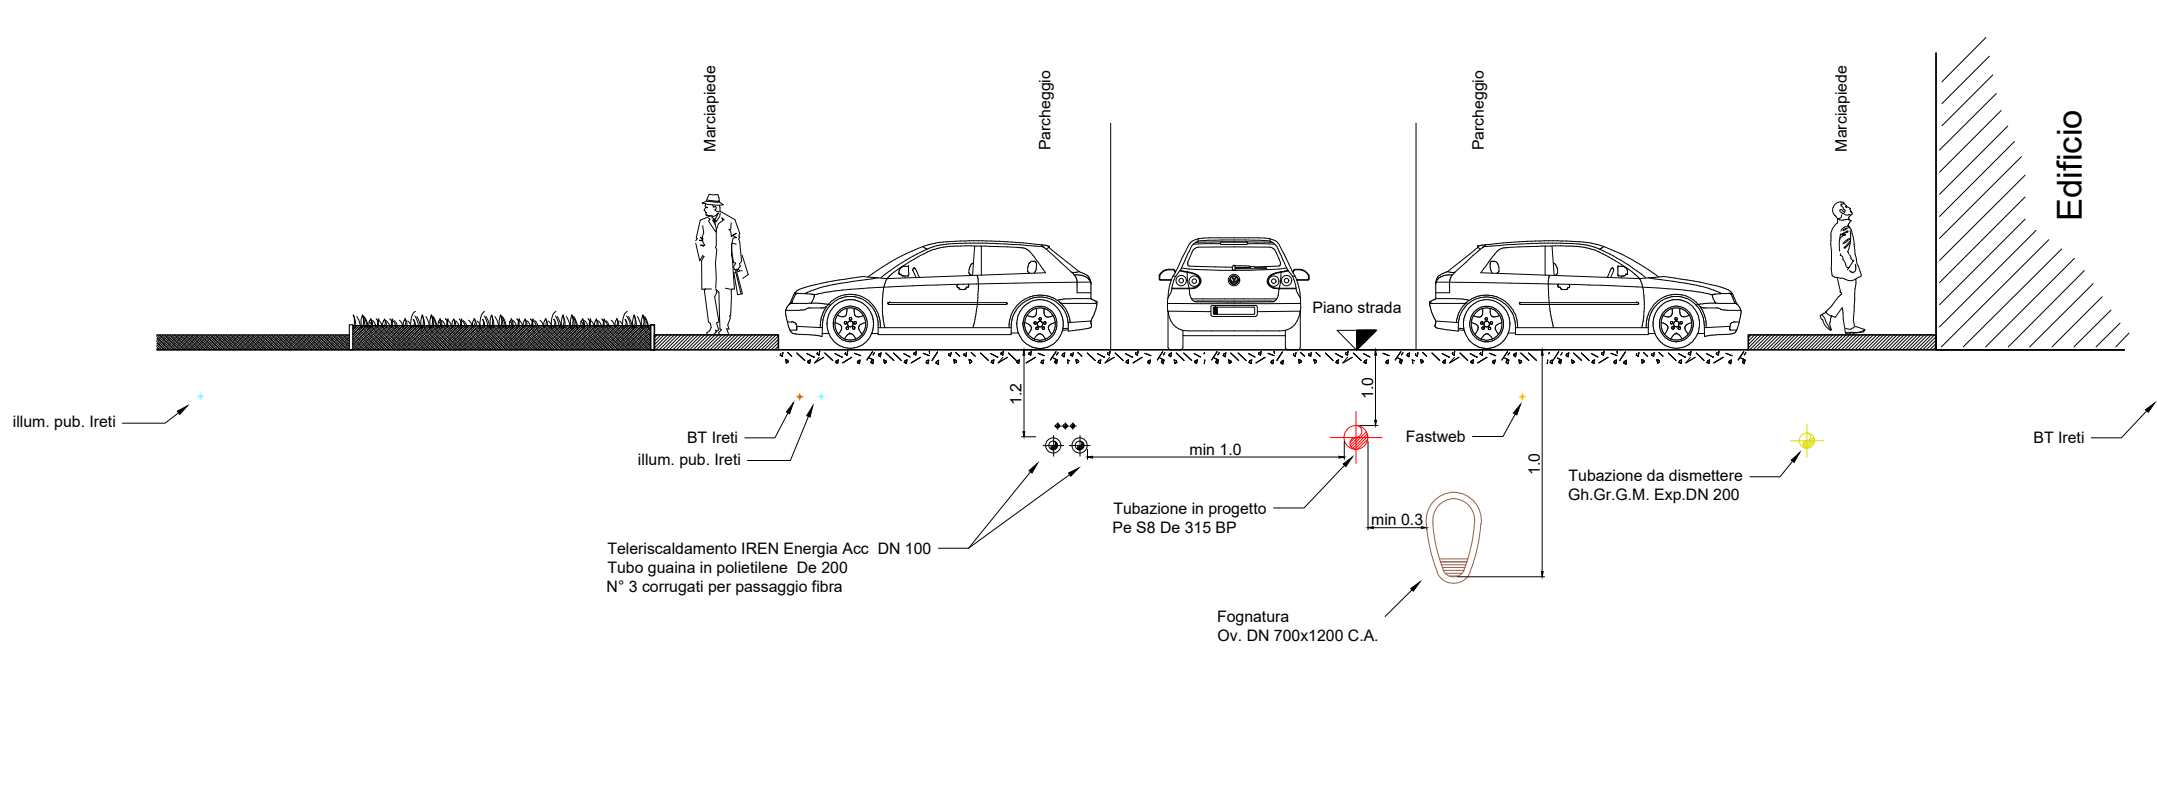

NOTE:
• Prima dell'inizio dei lavori dovranno essere accertati con scavi a mano, alla presenza dei tecnici interessati, natura e posizione dei sottoservizi, che potranno comportare variazioni dello sviluppo plano/altimetrico del tracciato della tubazione gas in progetto.
• Le misure riportate sono in metri.

LEARDI	Progettista: Ordine degli Ingegneri della Provincia di Alessandria Ingegnere ALBERTO G. G. G. G. G.	Unità Responsabile della Progettazione INGEREAL-INGE-PROGRE
Progetto n°: 22-0320-3E-00-001272 WBS: SI 20.10300.02.1109 ALLEGATO n°: 9.4		
Revisione: Emissione per commenti		
Formato: A0 Scale: 1: 100		
Committente: IG Italgas Reh		
Comune di: TORINO (TO) Via Vares Progetto Esecutivo SOSTITUZIONE RETE IN BP (L=2604,78 m) GARA ATEM T01 Intervento n° SI-0362.13-001272-TSS-TORINO06 Planimetria con sottoservizi e risoluzione delle interferenze - Tavola 4		