

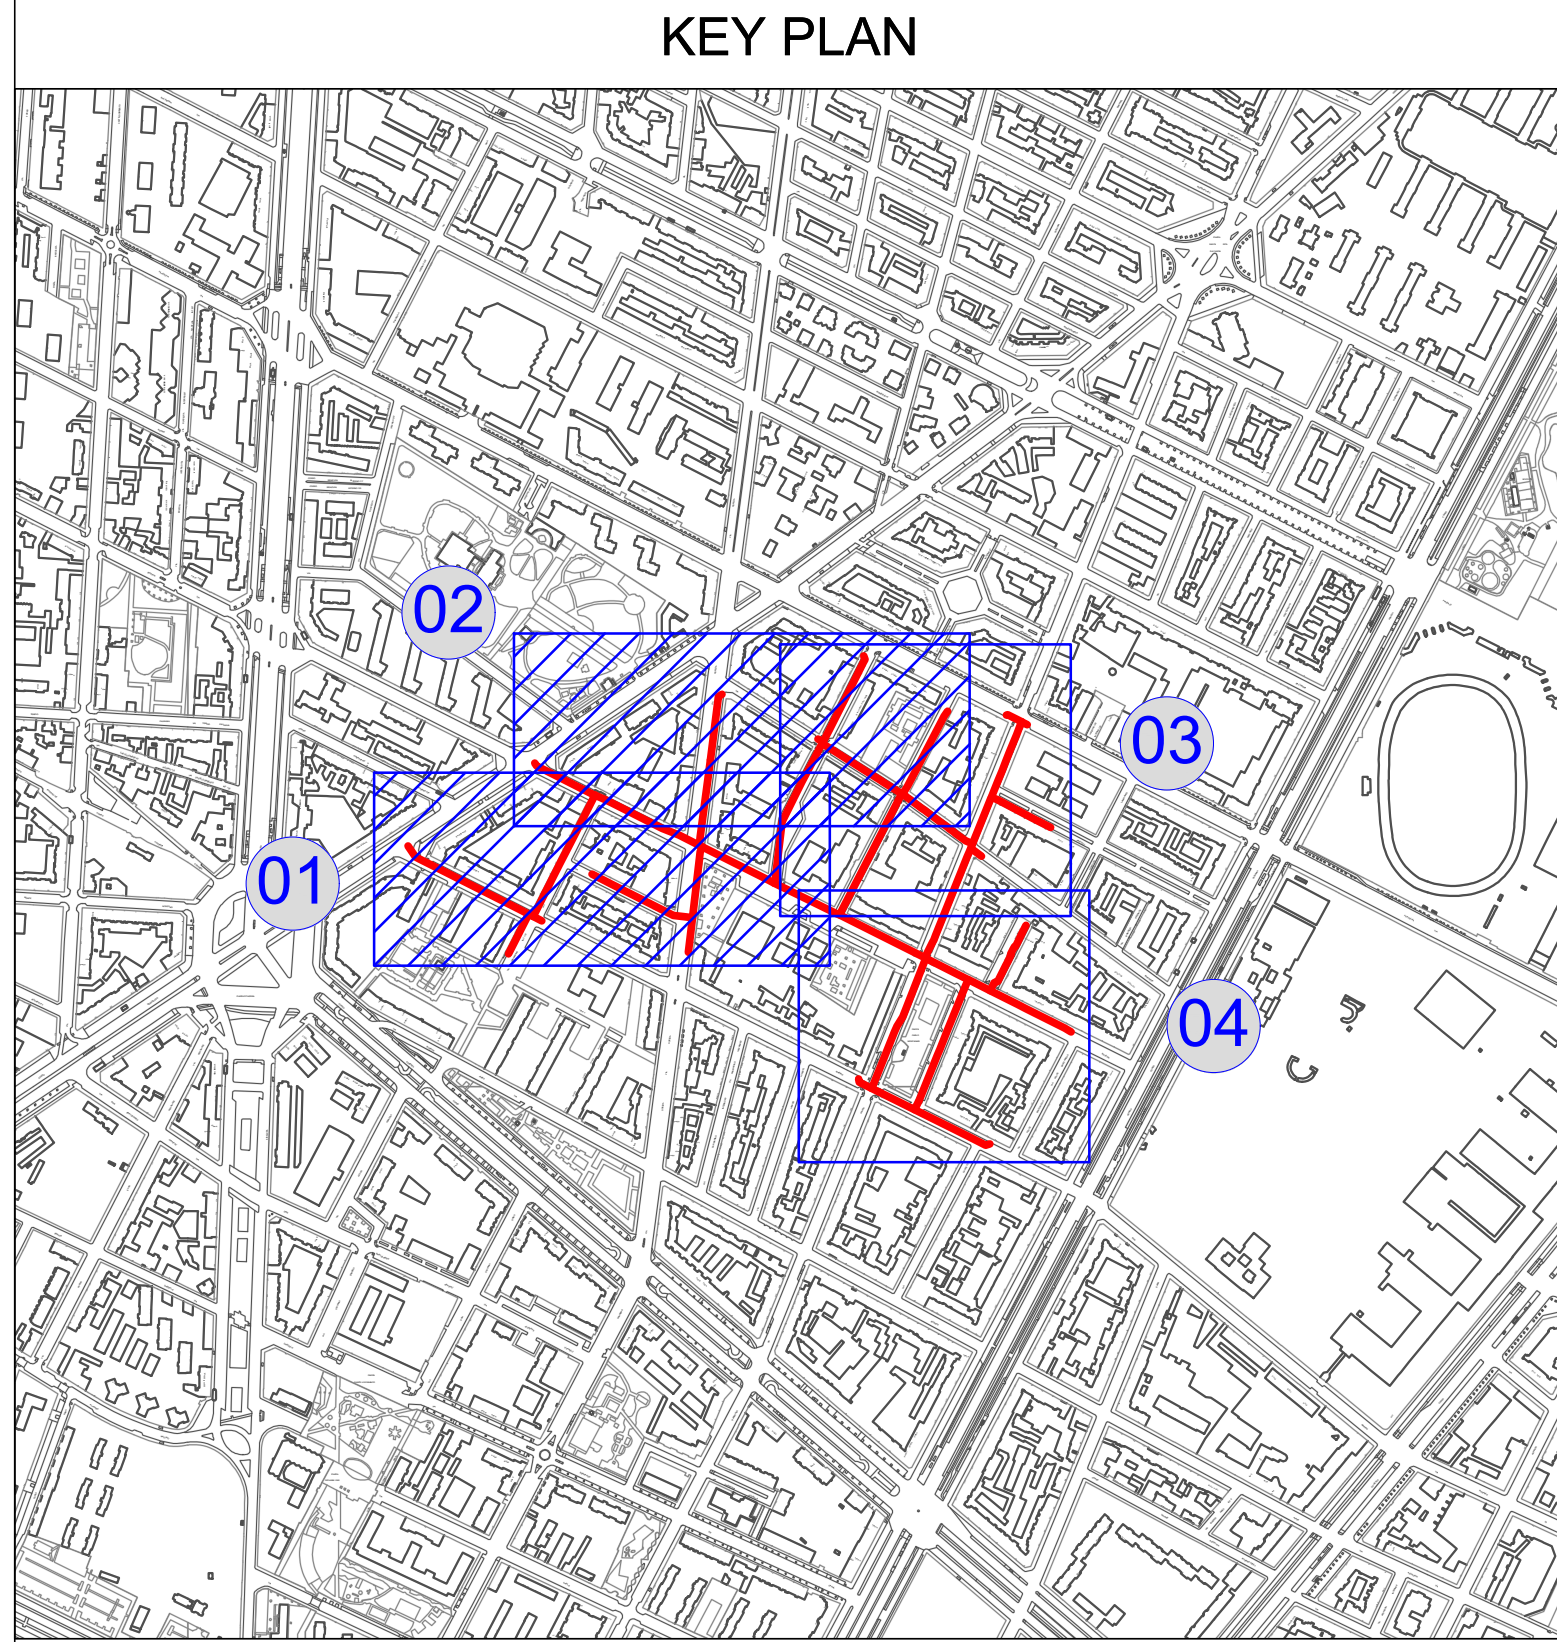


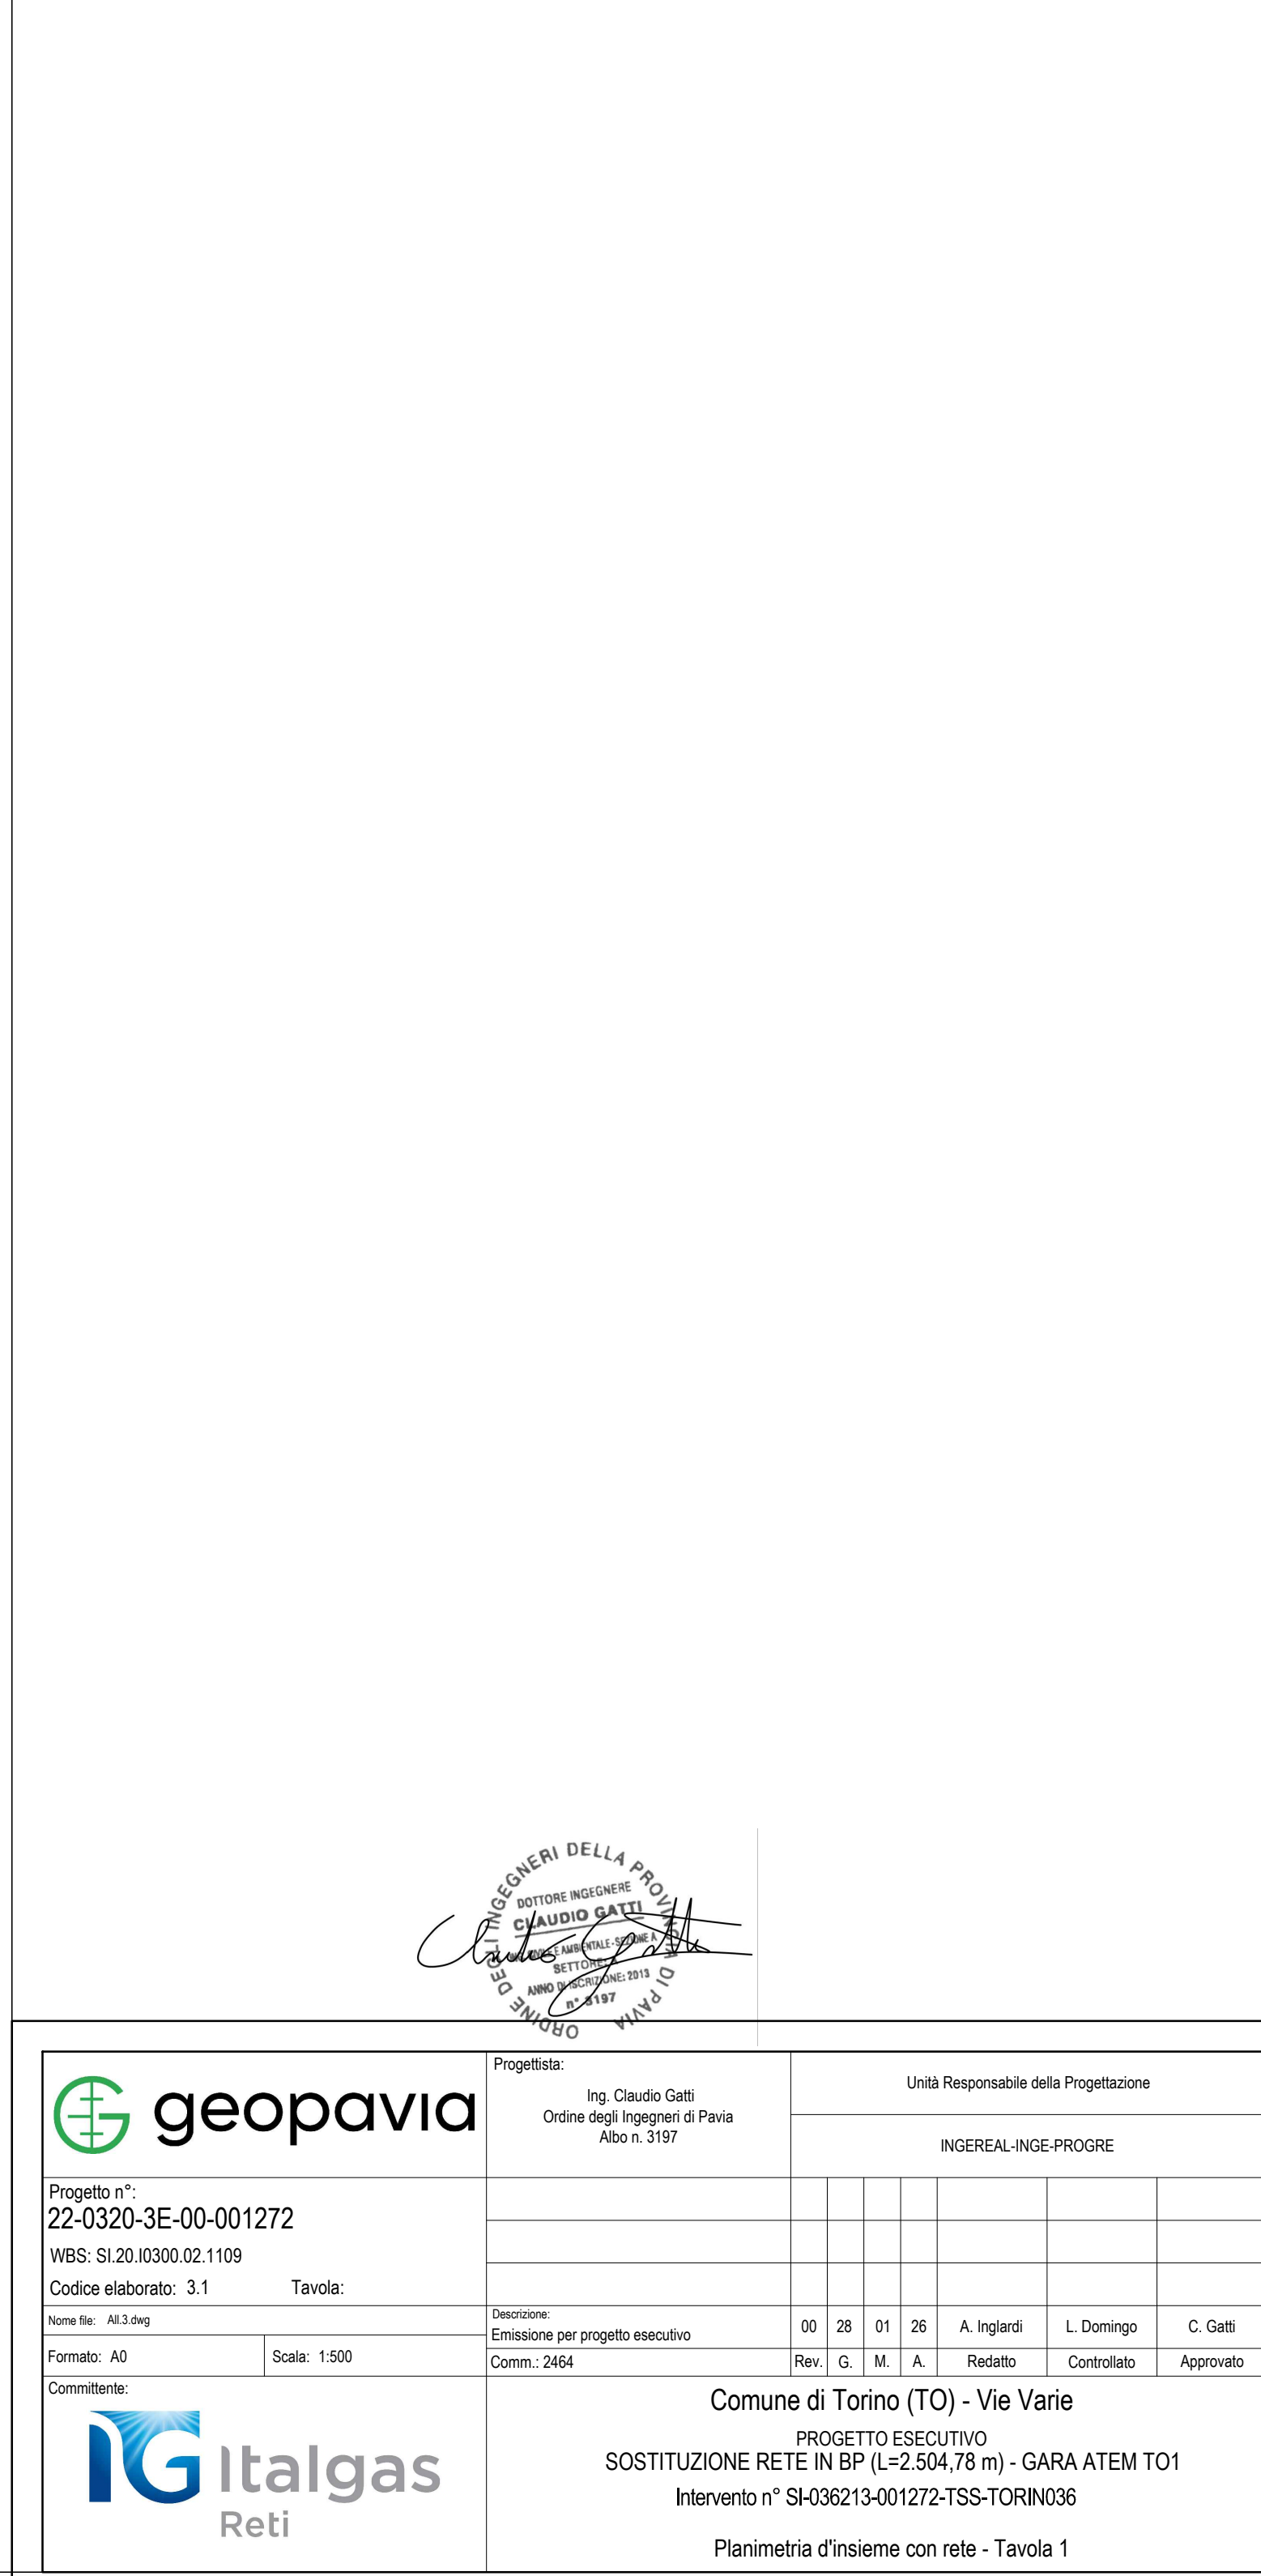

LEGENDA

TS BP esistente <=0,04 bar	TS MPA esistente 0,04 a 0,5 bar	TS MPB esistente 0,5 a 5 bar	TS MPC esistente 5 a 12 bar	TS BP in progetto <=0,04 bar
Tubo di protezione	Scala/trave armata	Riduzione diametro	Giunto di transizione	Fondello
Giunto dielettrico	Valvola in pozzetto	Organo di intercettazione di linea con sfili in pozzetto	Sfizio	Spurgo
			Punto di misura	Tubazione sfizio
				TS BP in dismissione

 


geopavia

Progetto n°: 22-0320-3E-00-001272
VRS: 51/20/0300/0/1109
Codice cliente: 3.1

Unità Responsabile della Progettazione
INGEGNERIA-PROGRIE

Comune di Torino (TO) - Vie Varie
SOSTITUZIONE RETE IN BP (L=2.504,78 m) - GARA ATEM T01
Intervento n° SK036213-001272-TSS-TORINO36
Planimetria d'insieme con rete - Tavola 1

KEY PLAN

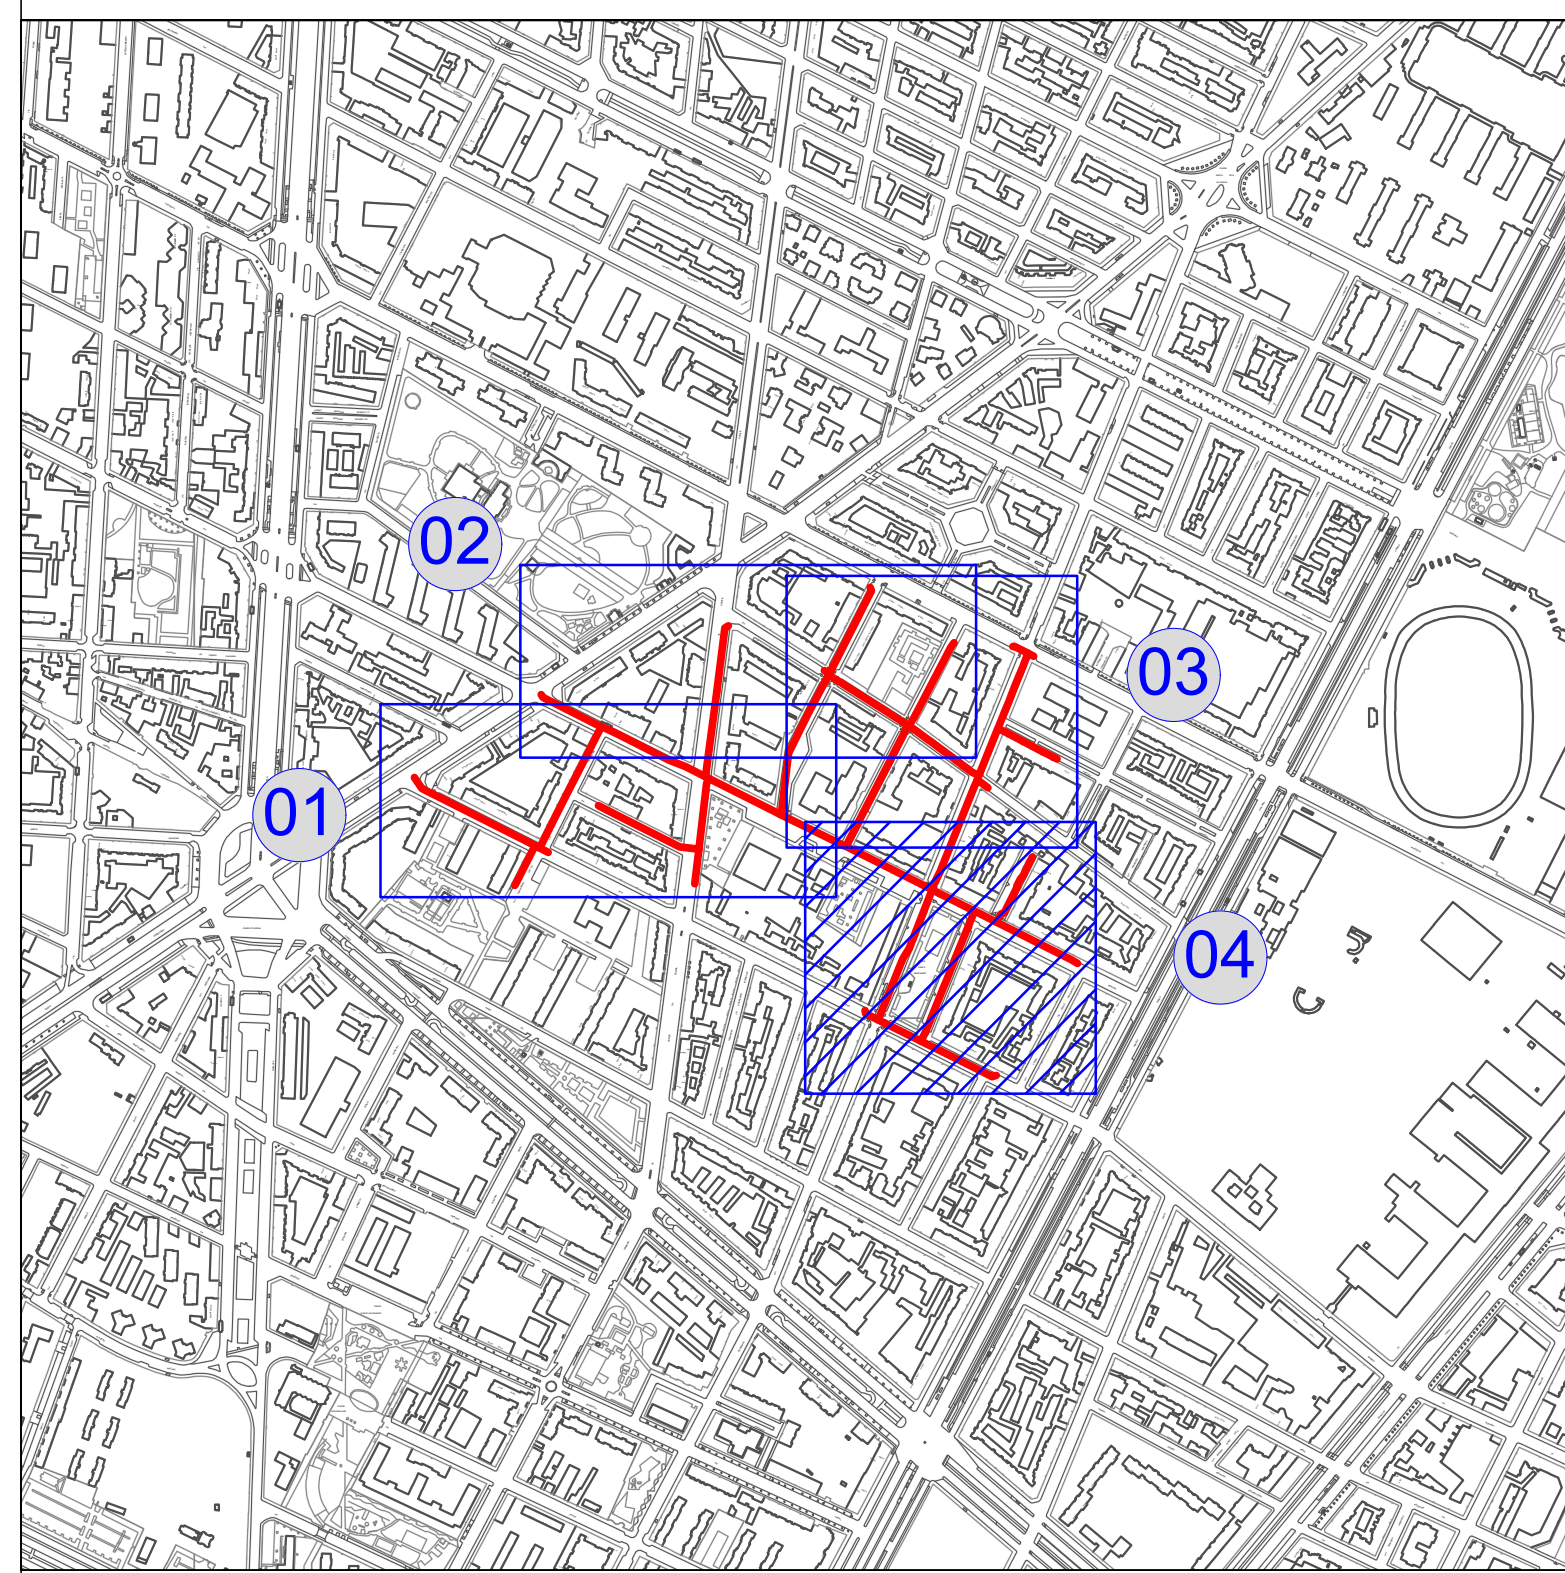

LEGENDA

 Progetto n°: 22-0320-3E-00-001272 WBS: SI.20.0300.02.1109 Codice elaborato: 3.3 Nome file: Al.3.dwg Formato: A0 Scale: 1:500 Comittente:	Progettista: Ing. Claudio Gatti Ordine degli Ingegneri di Pavia Albo n. 3197	Unità Responsabile della Progettazione INGEAL-INGE-PROGRE
	Decisione: Emissione per progetto esecutivo Comm.: 2464	00 28 01 26 Rev. G. M. A. A. Ingardi L. Domingo C. Gatti