

ITALGAS - ESERCIZIO DI TORINO

Località lavoro:

P.zza Montanari 160-168 > Via S. Martino 70

SCHIZZO: 30905

Cat. lavoro
2

Commessa
3880

Lavoro richiesto:

nuovo impianto

Esecutore
905

Conto
01

S/C
09

Esecuzione Imp.: Artig.

Salp

Ass.

Tavella

Data

27/4/67

Esecuzione att.: Sq.

Salp (1/2)

Ass.

Tavella

Data

6/9/67

Preso

N. 102

Cal. 20

Rosso 16/5/66

Q	Spese	Preso
3"	34.50	4.60
2 1/2"	60.40	1.60
2"	44.20	
1 1/2"	227.40	
1"	123.45	
1"	149.40	
Totale	633.35	6.20
A.I.E. P.b. X		F.b.


mp. 45.00

mp. 45.00

mp. 45.00

Colonne incassate
autorizzate dalla
Direzioni

Via San Martino

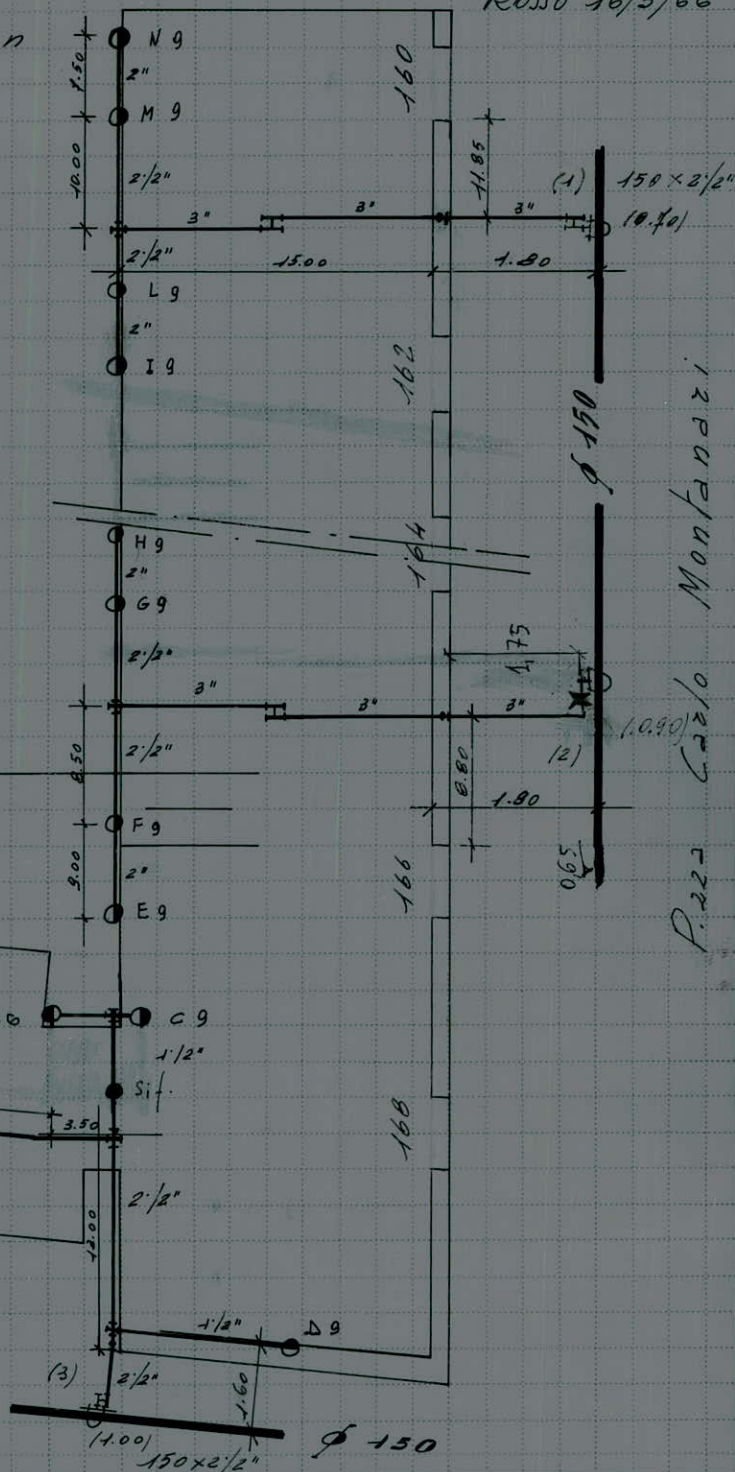

Sgombri totali

Sgombri parziali

Modifiche e riparazioni in genere



14

Italgas

Rifatto attacco collare Italgas
Comm. N° 4867 An. Appendini - Ip. Luchelli
il 28-4-68-