italgas
Esercizio di Torino

esecutore commerciale

data esecuzione

località lavoro VIA GORIZIA 1/4

richiedente VECCHIA EUROPA S.R.L.

unità esecutrice 3089/40

Descrizione lavoro NUOVO IMPIANTO

Destinazione contabile

Centro Operativo	Categ.	Specie	Centro di costo	Commessa
1109	21	53	TE43	59/4

Esecutore impianto: Ditta FISCHETTI Ass. [signature] Data 5-6-96

Esecutore attacco: Sq. MASTROMARTINO Ass. [signature] Data 6-6-96

P.G. N° 1 cal. G10

Schizzo n°

rif. mappa n°

SCHEMA IMPIANTO

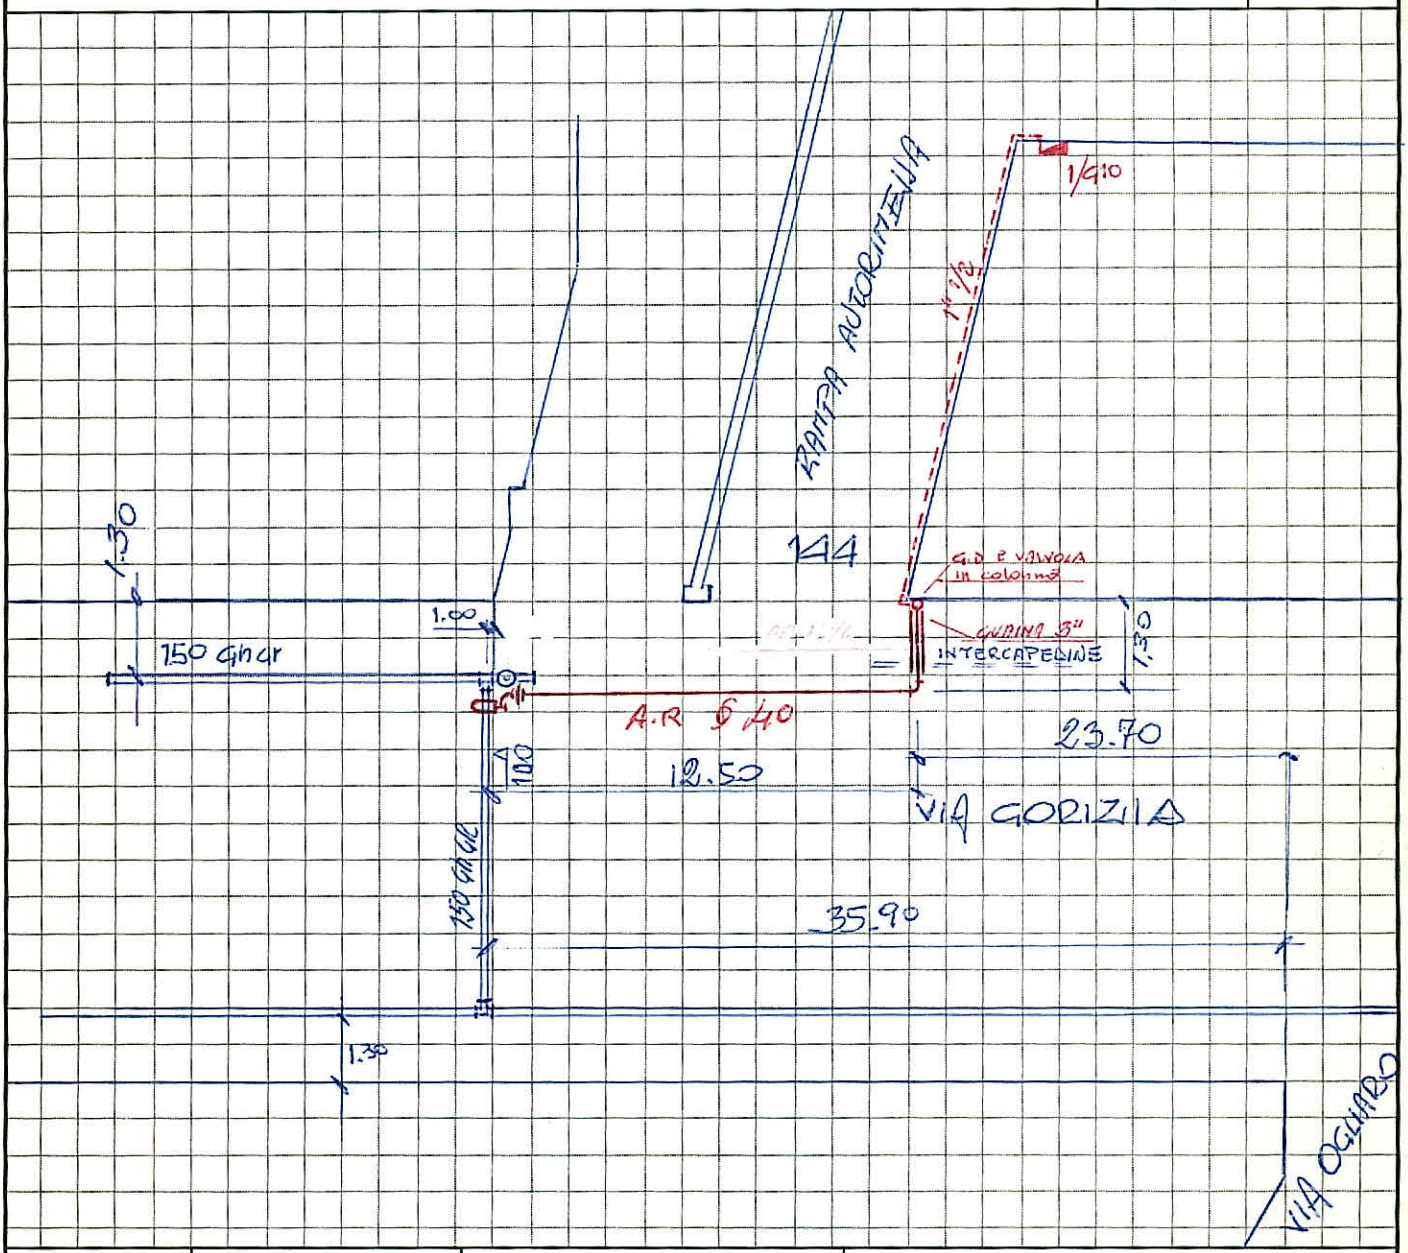

PROVA DI TENUTA
Eseguita a 10.000 mm. c.d.a.

N° REG.

Data 6-6-96

controllata da MASTROMARTINO

V. Resp.

NOTE

SVILUPPO

Ø	Sviluppo allac. interr.	Sviluppo allac. aereo	Sviluppo sottocol. colonne diramaz.	Sviluppo Guaina
¾				
1"				
1¼'				
1½	15.40	36.50		
2				
2½'				
3"				1.90
4"				
Tot.	15.40	36.50		1.90

NOTE PER ESECUZIONE

- ☐ occorre scala aerea
- ☐ occorre torre telescopica
- ☐ occorre scala italiana
- ☐ eseguire foro lastra pietra
- ☐ consegnato prospetto misure nicchia
- ☐ nicchia { esistente ☐ / da eseguire ☐ }
- ☐ taglio colonna Ø
- ☐ manicotto da saldare
- ☐ creazione aereazione secondo norme

riport. su mappa N.° 765
data 1/4/98
disegnatore [signature]

765

Cod. 0043072 - Tipografia Sosso