


GORIZIA 124666

		Unità PI 1	SCHEDA RIPARAZIONE DISPERSIONE DA TUBAZIONE STRADALE			N. 31679 2 del 28/3/12	Ubicazione TOPIDA 3 Via GORIZIA 148A				
Richiesta intervento N. 31679 4 Del 28/3/12		Riparazione Dispersione N. 31679 5 Del 3/4/12		Origine Intervento ☐ 1 ☒ 2 ☐ 3		Causa/Natura Dispersione ☒ 09		Riparazione Dispersioni Precedenti ☐ SI ☒ NO ☐ ?		Gas Distribuito Naturale ☒ Manifatt. ☐	
Pressione di Esercizio ☒ 1 BP (0,04) ☐ 2 MPA (0,5) ☐ 3 MPB (1,5) ☐ 4 MPB (5)		Materiale ☒ 5 AP (12) ☐ 6 AP (24) ☐ 7 AP (>24) ☒ 02 Ghisa grigia ☐ 05 Ghisa sferoid. ☐ 06 Acciaio nudo ☐ 07 Acciaio rivestito ☐ 08 Acciaio C 56 ☐ 09 Acciaio API ☐ 14 Fibron ☐ Altri		Materiali Impiegati Descrizione U.M. Quantità Tipo Interv.				Varie Distanza Fabbricato Profondità Anno Posa Giunto % Ostruzione N. reticolo			
Imputazione Contabile Codice Centro Operativo Categoria Specie C. Costo/O.L. Fornit. Commessa		O.L. Ricerca Dispers. N. Commessa		Tipo Traffico Isola Pedonale ☐ Tr. pesante ☐ Tr. leggero ☐		Patrol Survey Segnale N. ☐ SI ☒ NO					

ACCERTAMENTO																			
Apparecchio GRASCOPE		Intensità 25		Esecutore 14000		Data 28/3/12		Compilatore DEIDA		Dimens. Scavi 600x120x160 280x130x120		Sottosuolo ☒		Sede posa 3		Paviment. 2		Punti Dispersione 1	
RIPIRISTINI TIPO METRI QUADRI		PROPRIETÀ ☐ P ☐ C		Entità Dispersione Modesta ☐ Media ☐ Elevata ☐		Numero Mappa		Codice Nodo		Fine ☐ Inizio ☐									

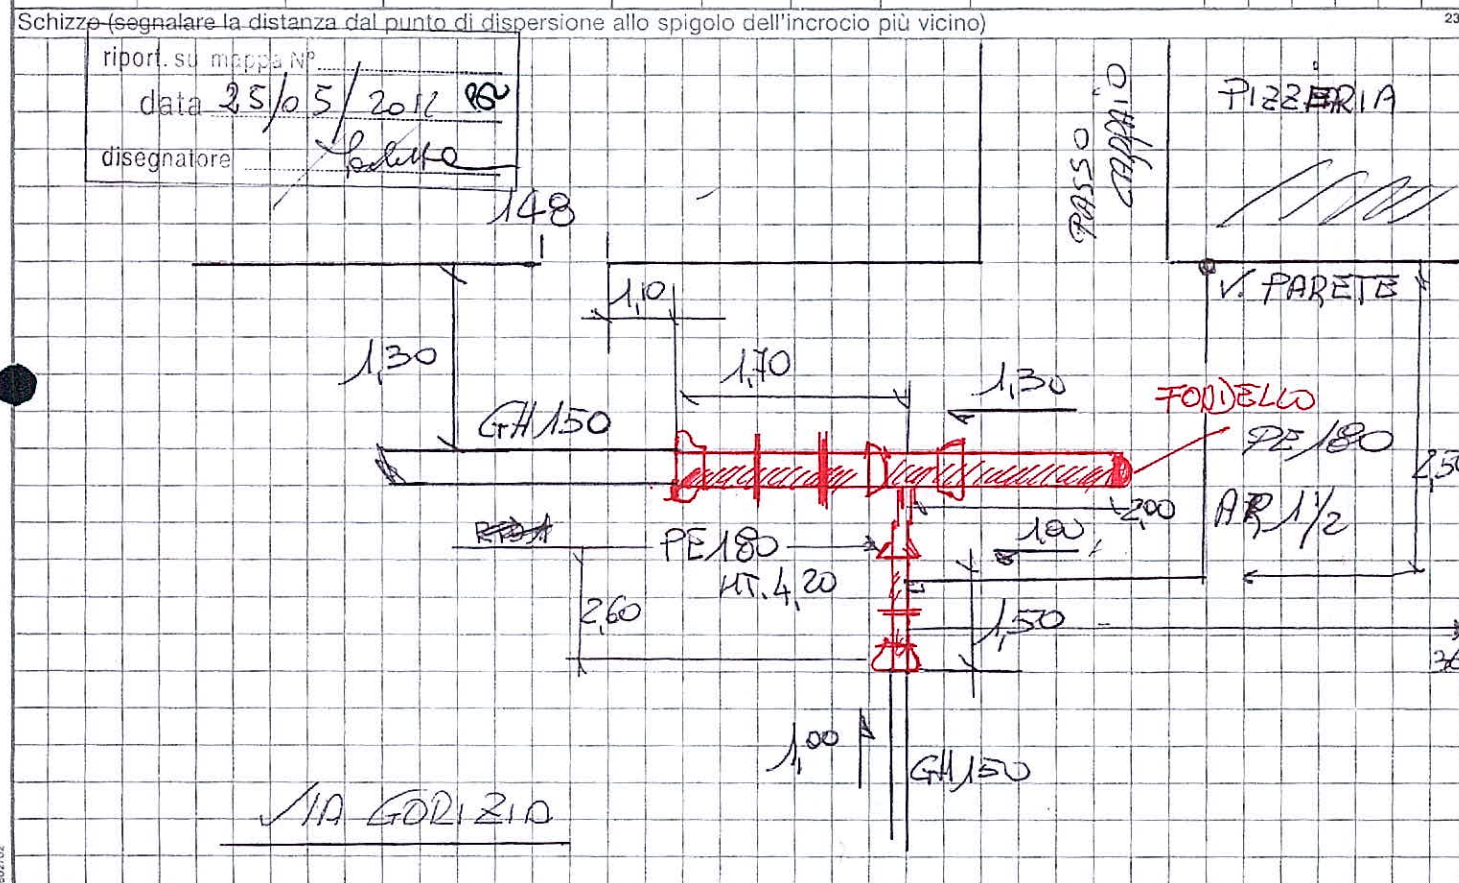

NOTE ES. DIP. TROPHEWO DA GH 150 A PE 180 + ALL. ALLA PIZZERIA		
SQUADRA	ASSISTENTE	RESPONSABILE
D'ARCAUNGO <i>[Signature]</i> <i>[Signature]</i>		

TABELLE

ORIGINE INTERVENTO

- 01 Disp. da ricerca preventiva
- 02 Disp. segnalata
- 03 Manutenzione preventiva programmata
- 04 Mancanza gas
- 05 Esigenza rete
- 06 Esigenza utenza
- 07 Modifica per sost. tubazione stradale
- 08 Modifica impianto derivazione utenza
- 09 Per danni arrecati da terzi

CAUSA/NATURA DISPERSIONE

- 01 Disp. per rottura trasversale del tubo
- 02 Disp. per fessurazione longit. del tubo
- 03 Disp. per fessur. longit. su bicchiere
- 04 Disp. da guarn. di collare o sport. a T
- 05 Disp. da guarn. di giunto a bicchiere
- 06 Disp. da guarn. di giunto meccanico
- 07 Dips. da code lisce + Gibault o Viking o Express
- 08 Disp. su giunto filettato
- 09 Disp. su giunto flangiato di tubazione
- 10 Disp. su giunto saldato
- 11 Disp. da guarnizione di morsa mecc.
- 12 Disp. da manicotto a 2 o 3 pezzi
- 13 Disp. su tappo filettato
- 14 Disp. per corrosione localizzata
- 15 Disp. per corrosione diffusa
- 16 Disp. su saldatura di giunzione (difetto di saldatura di posa)
- 17 Disp. per sfogliatura
- 18 Disp. su sald. longitud. (difetto di mat.)
- 19 Disp. su organo di presa
- 20 Disp. su sifone
- 21 Disp. da cannetta sifone
- 22 Disp. su bocca di sgombero o tenca (sportello di ispezione)
- 23 Disp. su valvola di linea
- 24 Disp. su valvola di sfianto
- 25 Disp. su collegamento valvola di sfianto
- 26 Disp. su giunto dielettrico

MATERIALI

- 01 Piombo
- 02 Rame
- 03 Ghisa grigia
- 04 Ghisa grigia - Gregorino
- 05 Ghisa Sferoidale
- 06 Acciaio Fe 00 nudo o acciaio Fe 00 rivestito (Pb)
- 07 Acciaio Fe 00 rivestito
- 08 Acciaio (DM del 24/1/1964)
- 09 API 5L gr. B
- 10 API 5LX 42
- 11 API 5LX 48
- 12 API 5LX 52
- 13 API 5LX 60
- 14 Fibronit
- 15 Eternit
- 16 P.V.C.
- 17 Polietilene P.A.D. poliestere alta densità
- 18 Delrin
- 19 Acciaio Fe 37 rivestito P.V.C.

TIPO INTERVENTO

- 01 Applic. manicotto mecc. o collare INOX
- 02 Sostituzione manicotto meccanico
- 03 Applic. manicotto incapsulante (BTR)
- 04 Applic. manicotto termorestring. (RAIKEM)
- 05 Inser. tronchetto ($\leq 1,5$ m) con giunti mecc.
- 06 Inserimento morsa meccanica
- 07 Sostituzione morsa meccanica
- 08 Aggiustaggio morsa meccanica
- 09 Sostituzione Gibault o Viking
- 10 Inser. e aggiustaggio Gibault o Viking
- 11 Applic. collare cieco per annullam. presa
- 12 Sost. collare cieco per annullam. presa
- 13 Sostituzioni guarnizioni
- 14 Serraggio e/o sostituzione bulloni
- 15 Saldatura
- 16 Ripresa saldatura
- 17 Applicazione lembo
- 18 Inscatolamento
- 19 Inserimento tronchetto saldato ($\leq 1,5$ m.)
- 20 Inser. acciaio ($> 1,5$ m e ≤ 10 m) su tubo acc.
- 21 Inser. acc. ($> 1,5$ m e ≤ 10 m) su tubo ghisa
- 22 Inserimento ghisa sferoidale ($> 1,5$ m e ≤ 6 m)
- 23 Ostruzione rilevata
- 24 Disostruzione meccanica
- 25 Disostruzione idrodinamica
- 26 Disostruzione pneumatica
- 27 Trattamento con Con Seal
- 28 Trattamento con Key-Hole
- 29 Trattamento con Joint Interne
- 30 Inserimento nuova presa
- 31 Annul. presa esistente (non con col. cieco)
- 32 Rifacimento presa
- 33 Potenziamento presa
- 34 Inserimento sifone nuovo
- 35 Annullamento sifone esistente
- 36 Sostituzione sifone
- 37 Intervento su cannetta sifone
- 38 Bocca di sgombero esist. (scheda creaz. arch.)
- 39 Annul. bocca sgombero o tenca (sport. isp.)
- 40 Inserimento valvola di linea
- 41 Annullamento valvola di linea
- 42 Sostituzione valvola di linea
- 43 Riparazione valvola di linea
- 44 Inserimento valvola di sfianto (spurgo)
- 45 Annullamento valvola di sfianto
- 46 Sostituzione valvola di sfianto
- 47 Riparazione valvola di sfianto
- 48 Intervento su collegamento valvola di sfianto
- 49 Inserimento giunto dielettrico
- 50 Annullamento giunto dielettrico
- 51 Sostituzione giunto dielettrico
- 52 Inserimento cunicolo SNAM
- 53 Riparazione cunicolo SNAM
- 54 Inserimento tubo guaina PVC
- 55 Inserimento tubo guaina acciaio
- 56 Sostituzione tubo guaina acciaio
- 57 Inserimento tubo guaina ghisa
- 58 Inserimento soffione
- 59 Sostituzione soffione
- 60 Annullamento soffione
- 61 Inserimento cavalletto
- 62 Sostituzione cavalletto
- 63 Annullamento cavalletto
- 64 Battitura giunto
- 65 Sella di rinforzo
- 66 Ready-seal
- 67 Inserimento tubo guaina fibronit
- 68 Inserimento tubo fibronit su ghisa
- 69 Inserimento tubo acciaio su fibronit
- 70 Piastra acciaio
- 71 Soletta CLS
- 72 Inserimento presa su M.P.A.
- 73 Annullamento presa su M.P.A.

- 74 Rifacimento presa su M.P.A.
- 75 Potenziamento presa su M.P.A.
- 76 Inserimento presa su M.P.B.
- 77 Annullamento presa su M.P.B.
- 78 Rifacimento presa su M.P.B.
- 79 Potenziamento presa su M.P.B.
- 80 Inser. chiusino immissione "IMMUNOL"
- 81 Annul. chiusino immissione "IMMUNOL"
- 82 Inserimento lastra gretata
- 83 Inserimento valvola LINDQUIST
- 84 Annullamento valvola LINDQUIST
- 85 Sostituzione valvola LINDQUIST
- 86 Riparazione valvola LINDQUIST
- 87 Inserimento acciaio rivestito su ghisa sferoidale
- 88 Inserimento acciaio rivestito su ghisa grigia giunti mecc.
- 89 Inserimento ghisa sferoidale su ghisa grigia giunti meccanici
- 90 Inserimento ghisa su Fibronit

TIPO GIUNTO

- 01 Bicchiere con canapa e Pb
- 02 Bicchiere con para, canapa e Pb (Büdde & Göhde)
- 03 Bicchiere con gomma di Fibronit
- 04 Meccanico Express
- 05 Meccanico Ilva
- 06 Meccanico generico
- 07 Code lisce + Gibault o Viking o Express
- 08 Filettato
- 09 Flangiato
- 10 Saldato di testa
- 11 Saldato a Bicchiere cilindrico o sferico
- 12 Bicchiere incollato

SOTTOSUOLO

- 01 Normale - Agricolo
- 02 Roccoso
- 03 Sabbioso
- 04 Ghiaioso
- 05 Di riporto
- 06 Misto a macerie
- 07 Argilloso

SEDE POSA

- 01 Carreggiata
- 02 Carreggiata su strada alberata
- 03 Marciapiedi
- 04 Marciapiedi su strada alberata
- 05 Spartitraffico
- 06 Spartitraffico su strada alberata
- 07 Non in sede stradale (terreno agr. giard.)
- 08 Su area di rispetto
- 09 Su opera d'arte (viadotti, sopraelevate)

PAVIMENTAZIONE

- 01 Sterrato (non impovertito)
- 02 Bitumato
- 03 Lastriato
- 04 Calcestruzzo
- 05 Porfido
- 06 Marmo, Quarzite, cc.
- 07 Terreno agricolo
- 08 Acciottolato
- 09 Mattonato o piastrellato