


	SCHIZZO TECNICO	Unità	Anno	N. L.M.
		100	2007	1000023464
Proposta lavoro/anno	N. lavoro	W.B.S.	O. L.	Comune
2007	1263213	98405367 530219AJ	/	TORINO

Descrizione lavoro Nuovo impianto Ubicazione Via San Marino 118

Impresa Polono s.r.l. Codice / Data compilazione 14/9/07

Data inizio lavori 14/09/07 Data fine lavori 14/9/07 Compilatore 

Classe pressione		Prese eseguite N.	Prese annullate N.	Punti gas eseguiti N.	Punti gas annullati N.	GRF DN	GRI / GRU Tipo	Materiale	Posato		Rimosso/abbandonato	
									DN	m	DN	m
☒ 1	BP (0,04)							TUBO PEGH	63	2.80		
☐ 2	MPA (0,5)							TUBO DEC-2 NC	2 1/2	1.10	GUSANA	
☐ 3	MPB (1,5)							TUBO DEC 3 1/2	2"	1.00		
☐ 4	MPB (5)											
☐ 5	MPC (12)											
☐ 6	AP (24)											
☐ 7	AP (>24)											

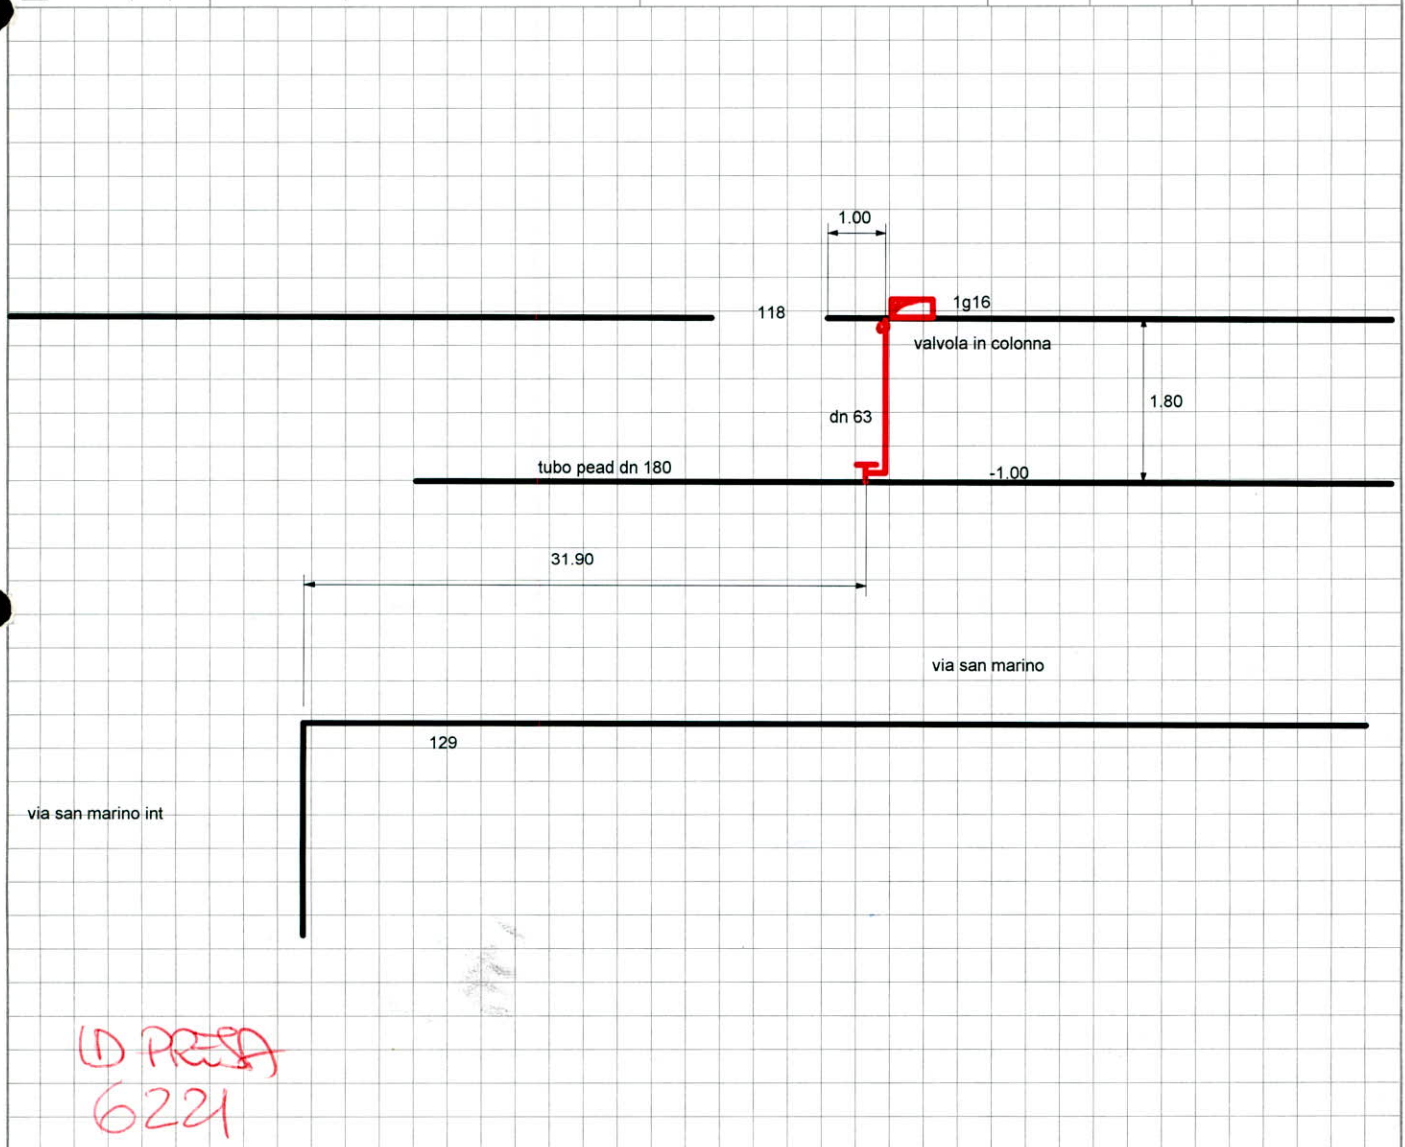

10 PRESA
6221

Prova di tenuta <u>allegata alla Perizia</u>	Pressione collaudo <u>1.30 bar</u>	Data <u>14/9/07</u>
Durata <u>30 mn.</u>	Esito <u>Es.</u>	Capo squadra 
Riportato su mappa n. <u>/</u>	Data <u>8/10/08</u>	Disegnatore 
	Assistente 	Visto Responsabile 

POSIZIONE TUBAZIONE

Riportare in codice:

- ☐ 1 Tubazione interrata _____
- ☐ 2 Tubazione aerea _____
- ☐ 3 Tubazione subacquea _____
- ☒ 4 Tubazione "sub-alveo" _____
- ☐ 5 Allacc. interrato _____

CLASSE DI POSA

Riportare in codice:

- ☒ 1 0,04 bar (BP) _____
- ☐ 2 0,5 bar (MPA) _____
- ☐ 3 1,5 bar (MPB) _____
- ☐ 4 5 bar (MPB) _____
- ☐ 5 12 bar (MPC) _____
- ☐ 6 24 bar (AP) _____
- ☐ 7 >24 bar (AP) _____

ENTITÀ TRAFFICO

Riportare in codice:

- ☒ 1 Leggero _____
- ☐ 2 Pesante _____
- ☐ 3 Scarso _____
- ☐ 4 Intenso _____

TIPO DEL SOTTOSUOLO

Riportare in codice:

- ☒ 1 Normale - agricolo _____
- ☐ 2 Roccioso _____
- ☐ 3 Sabbioso _____
- ☐ 4 Ghiaioso _____
- ☐ 5 Di riporto _____
- ☐ 6 Misto a macerie _____
- ☐ 7 Argilloso _____
- ☐ 9 Non identificato _____

CAUSALI SOSTITUZIONI

- ☐ Sost. per rifacimento pavimentazione stradale _____
- ☐ Sost. causa lavori altri enti _____
- ☐ Annullamento o sostituzione per obsolescenza _____
- ☐ Annullamento o sostituzione per potenziamento _____
- ☐ Annullamento o sostituzione per altri motivi _____

SEDE DI POSA

Riportare in codice:

- ☒ 1 Carreggiata _____
- ☐ 2 Carreggiata su strada alberata _____
- ☐ 3 Marciapiedi _____
- ☒ 4 Marciapiedi su strada alberata _____
- ☐ 5 Spartitraffico _____
- ☐ 6 Spartitraffico su strada alberata _____
- ☐ 7 Fuori sede stradale _____
- ☐ 8 Su area di rispetto _____
- ☐ 9 Su opera d'arte (ponti, ecc.) _____

TIPO DI PAVIMENTAZIONE

Riportare in codice:

- ☒ 1 Sterrato _____
- ☐ 2 Bitumato _____
- ☐ 3 Lastricato _____
- ☐ 4 Calcestruzzo _____
- ☐ 5 Porfido _____
- ☐ 6 Marmo, quarzite, ecc. _____
- ☐ 7 Terreno agricolo _____
- ☐ 8 Acciottolato _____
- ☐ 9 Mattonato o piastrellato _____

ATTRAVERSAMENTI E PERCORRENZE

Riportare in codice:

- ☐ 1 Attraversamento strada ANAS _____
- ☐ 2 Percorrenza strada ANAS _____
- ☐ 3 Attraversamento strada provinciale _____
- ☐ 4 Percorrenza su strada provinciale _____
- ☒ 5 Attraversamento su strada comunale _____
- ☐ 6 Percorrenza su strada comunale _____
- ☐ 7 Attraversamento su strada privata _____
- ☐ 8 Percorrenza su strada privata _____
- ☐ 9 Attraversamento fisico galleria _____
- ☐ 10 Attraversamento sotto galleria _____
- ☐ 11 Percorrenza galleria _____
- ☐ 12 Percorrenza su terreno comunale _____
- ☐ 13 Percorrenza su terreno demaniale _____
- ☐ 14 Percorrenza su terreno privato _____
- ☐ 15 Percorrenza su terreno sociale _____
- ☐ 16 Attraversamento autostradale _____
- ☐ 17 Percorrenza autostradale _____
- ☐ 18 Attraversamento strada vicinale _____
- ☐ 19 Percorrenza strada vicinale _____
- ☐ 20 Attravers./Percorr. opera d'arte _____